

内 部 仕 上 表 （壁下地:石膏ボード12.5mm/天井下地:9.5mm）※脱衣室:床合板特類 下地									
階		床	巾木	壁	品番	廻 縁	天 井	品番	特記事項
1F	ポーチ	LIXILパセオ300/PSO-BR 2							
	玄関	LIXILパセオ300/PSO-BR 2	ライン巾木(W)	ビニルクロス	SLP-252	突付	ビニルクロス	SLP-252	
	ホール①	イタ銘木フロアーラステックt12 ウォールナット3P	ライン巾木(W)	ビニルクロス	SLP-252	突付	ビニルクロス	SLP-252	
	LDK	イタ銘木フロアーラステックt12 ウォールナット3P	ライン巾木(W)	ビニルクロス	SLP-252	突付	ビニルクロス	SLP-252	アクセントクロス BA7237
	畳コーナー	ダイケン 健やかおもて 14 灰桜色	畳寄せ	ビニルクロス	SLP-252	突付	ビニルクロス	SLP-252	畳縁:高田織物 浮No.13
	洗面	イタ銘木フロアーラステックt12 ウォールナット3P	ライン巾木(W)	ビニルクロス	SLP-252	突付	ビニルクロス	SLP-252	
	脱衣ラントリー	フロアタイルt2.3 サンゲツIS-2073	H40ソフト巾木W97	ビニルクロス	SLP-252	突付	ビニルクロス	SLP-252	
	WIC	フロアタイルt2.3 サンゲツIS-2073	H40ソフト巾木W97	ビニルクロス	SLP-252	突付	ビニルクロス	SLP-252	
2F	WC①	フロアタイルt2.3 サンゲツIS-2073	H40ソフト巾木W97	ビニルクロス	SLP-252	突付	ビニルクロス	SLP-252	
	ホール②	イタ銘木フロアーラステックt12 ウォールナット3P	ライン巾木(W)	ビニルクロス	SLP-252	突付	ビニルクロス	SLP-252	
	洋室①	イタ銘木フロアーラステックt12 ウォールナット3P	ライン巾木(W)	ビニルクロス	SLP-252	突付	ビニルクロス	SLP-252	
	洋室②	イタ銘木フロアーラステックt12 ウォールナット3P	ライン巾木(W)	ビニルクロス	SLP-252	突付	ビニルクロス	SLP-252	
	洋室③	イタ銘木フロアーラステックt12 ウォールナット3P	ライン巾木(W)	ビニルクロス	SLP-252	突付	ビニルクロス	SLP-252	
	洋室④	イタ銘木フロアーラステックt12 ウォールナット3P	ライン巾木(W)	ビニルクロス	SLP-252	突付	ビニルクロス	SLP-252	
	CL②	イタ銘木フロアーラステックt12 ウォールナット3P	ライン巾木(W)	ビニルクロス	SLP-252	突付	ビニルクロス	SLP-252	
	WC②	フロアタイルt2.3 サンゲツIS-2073	H40ソフト巾木W97	ビニルクロス	SLP-252	突付	ビニルクロス	SLP-252	
物入・収納・CL etc		※接続する部屋と同仕様とする							

上 框 ※	■ LIXILラシッサS 上框のみ30×150 色: クリエモカ
階 段	■ LIXIL KA 階段 ササラ: プレシャスホワイト
KA階段で対応できない場合、オプション	段 板 : クリエモカ 蹴込板: プレシャスホワイト
ラウンド手摺: ブラック	手摺金物 ブラック
にてラシッサS階段	上段框: クリエモカ 長尺笠木156: LIXIL プレシャスホワイト
窓 枠	■ LIXIL スマート10 色 プレシャスホワイト
	※浴室ドア枠 フクビ3方枠 [ホワイト]
キッチン笠木	■ ゴム集成カウンター(オスモカラー) 色 ウォールナット色合わせ
カウンター	形状 L型(ジョイント加工)
天井点検口	■ 天井アルミ点検口枠 450角 TAN45BW フクビ化学工業
	ミルキーホワイト
床下収納庫	■ 高気密型床下点検口断熱型 SPF-R6060 城東テクノ 収納付
	(脱衣室) ライトグレー(LG)
トイレ棚	■ 1,2階トイレ D250 アートランバー棚(シェルホワイト)
室内物干し金物	■ 川口技研SPC型2セット
洗面所	■ ゴム集成カウンター(オスモカラ 色 ウォールナット色合わせ
下足入	■ なし 色
プッシュタイプ	サイズ: 形状:


支給品	■ 無し
備考	■ 付框は30×150 プレシャスホワイト ■ 可動棚アートランバー色:シェルホワイト ■ 棚受金物類色:ホワイト 集成カウンターは出荷前塗装

内 部 建 具 表								
LIXIL		建具色：プレシャスホワイト		枠色 ： 扉同色		※その他、下記特記による		
ラフィス		把手 ： スクエアL（シャインニッケル） 丁番 固定枠（156） 外付戸当り ガイトピン床色合せ 引戸のみ上吊Wソフトモーション						
階	No	室名	形式	枠外W サイズ	デザイン	枠色	特記事項	
				枠外H サイズ	建具色	把手		
1	1	LDK	片開き戸	—	RAA	—		
	WD			2400	—	—		
	2	LDK	片引き戸	—	RAA			
	WD			2400	-			
	3	WC①	片引き戸	—	RAA	—	明り窓・表示錠	
	WD			2400	—	—		
	4	脱衣ラントリー	片引き戸	—	RAA	—	明り窓・表示錠	
	WD			2400	—	—	アウトセット	
	5	脱衣ラントリー	片開き戸	—	RAA	—	明り窓・表示錠	
	WD			2400	—	—		
2	6	洋室③	片引き戸	—	RAA	—		
	WD			2400	—	—		
	7	洋室②	片開き戸	—	RAA	—		
	WD			2400	—	—		
	8	洋室①	片開き戸	—	RAA	—		
	WD			2400	—	—		
	9	洋室④	片開き戸	—	RAA	--		
	WD			2400	—	--		
	10	CL②	折れ戸	—	RAA	--		
	WD			2400	—	--		
	11	WC②	片引き戸	—	RAA	—	明り窓・表示錠	
	WD			2400	—	—		


		浜 岡 一 級 総 合 設 計 事 務 所			株式会社 LIFEFUND InDesign office 一級建築士事務所		年 月 日	件名				
		一級建築士事務所 静岡県知事登録第 (10)2441 号			事務所登録 (2) 第7595号 一級建築士登録 第179770号 鈴木 達男		2025.9.5	清水裕也様・穂菜実 様邸 新築工事				
		一級建築士 大臣登録第 365879 号 西原利昌			〒432-8023 静岡県浜松市中央区鴨江3丁目70番23号		縮尺	図面	仕上表 2			
									酒井		青島	1-2

磐田市平松地内


G2

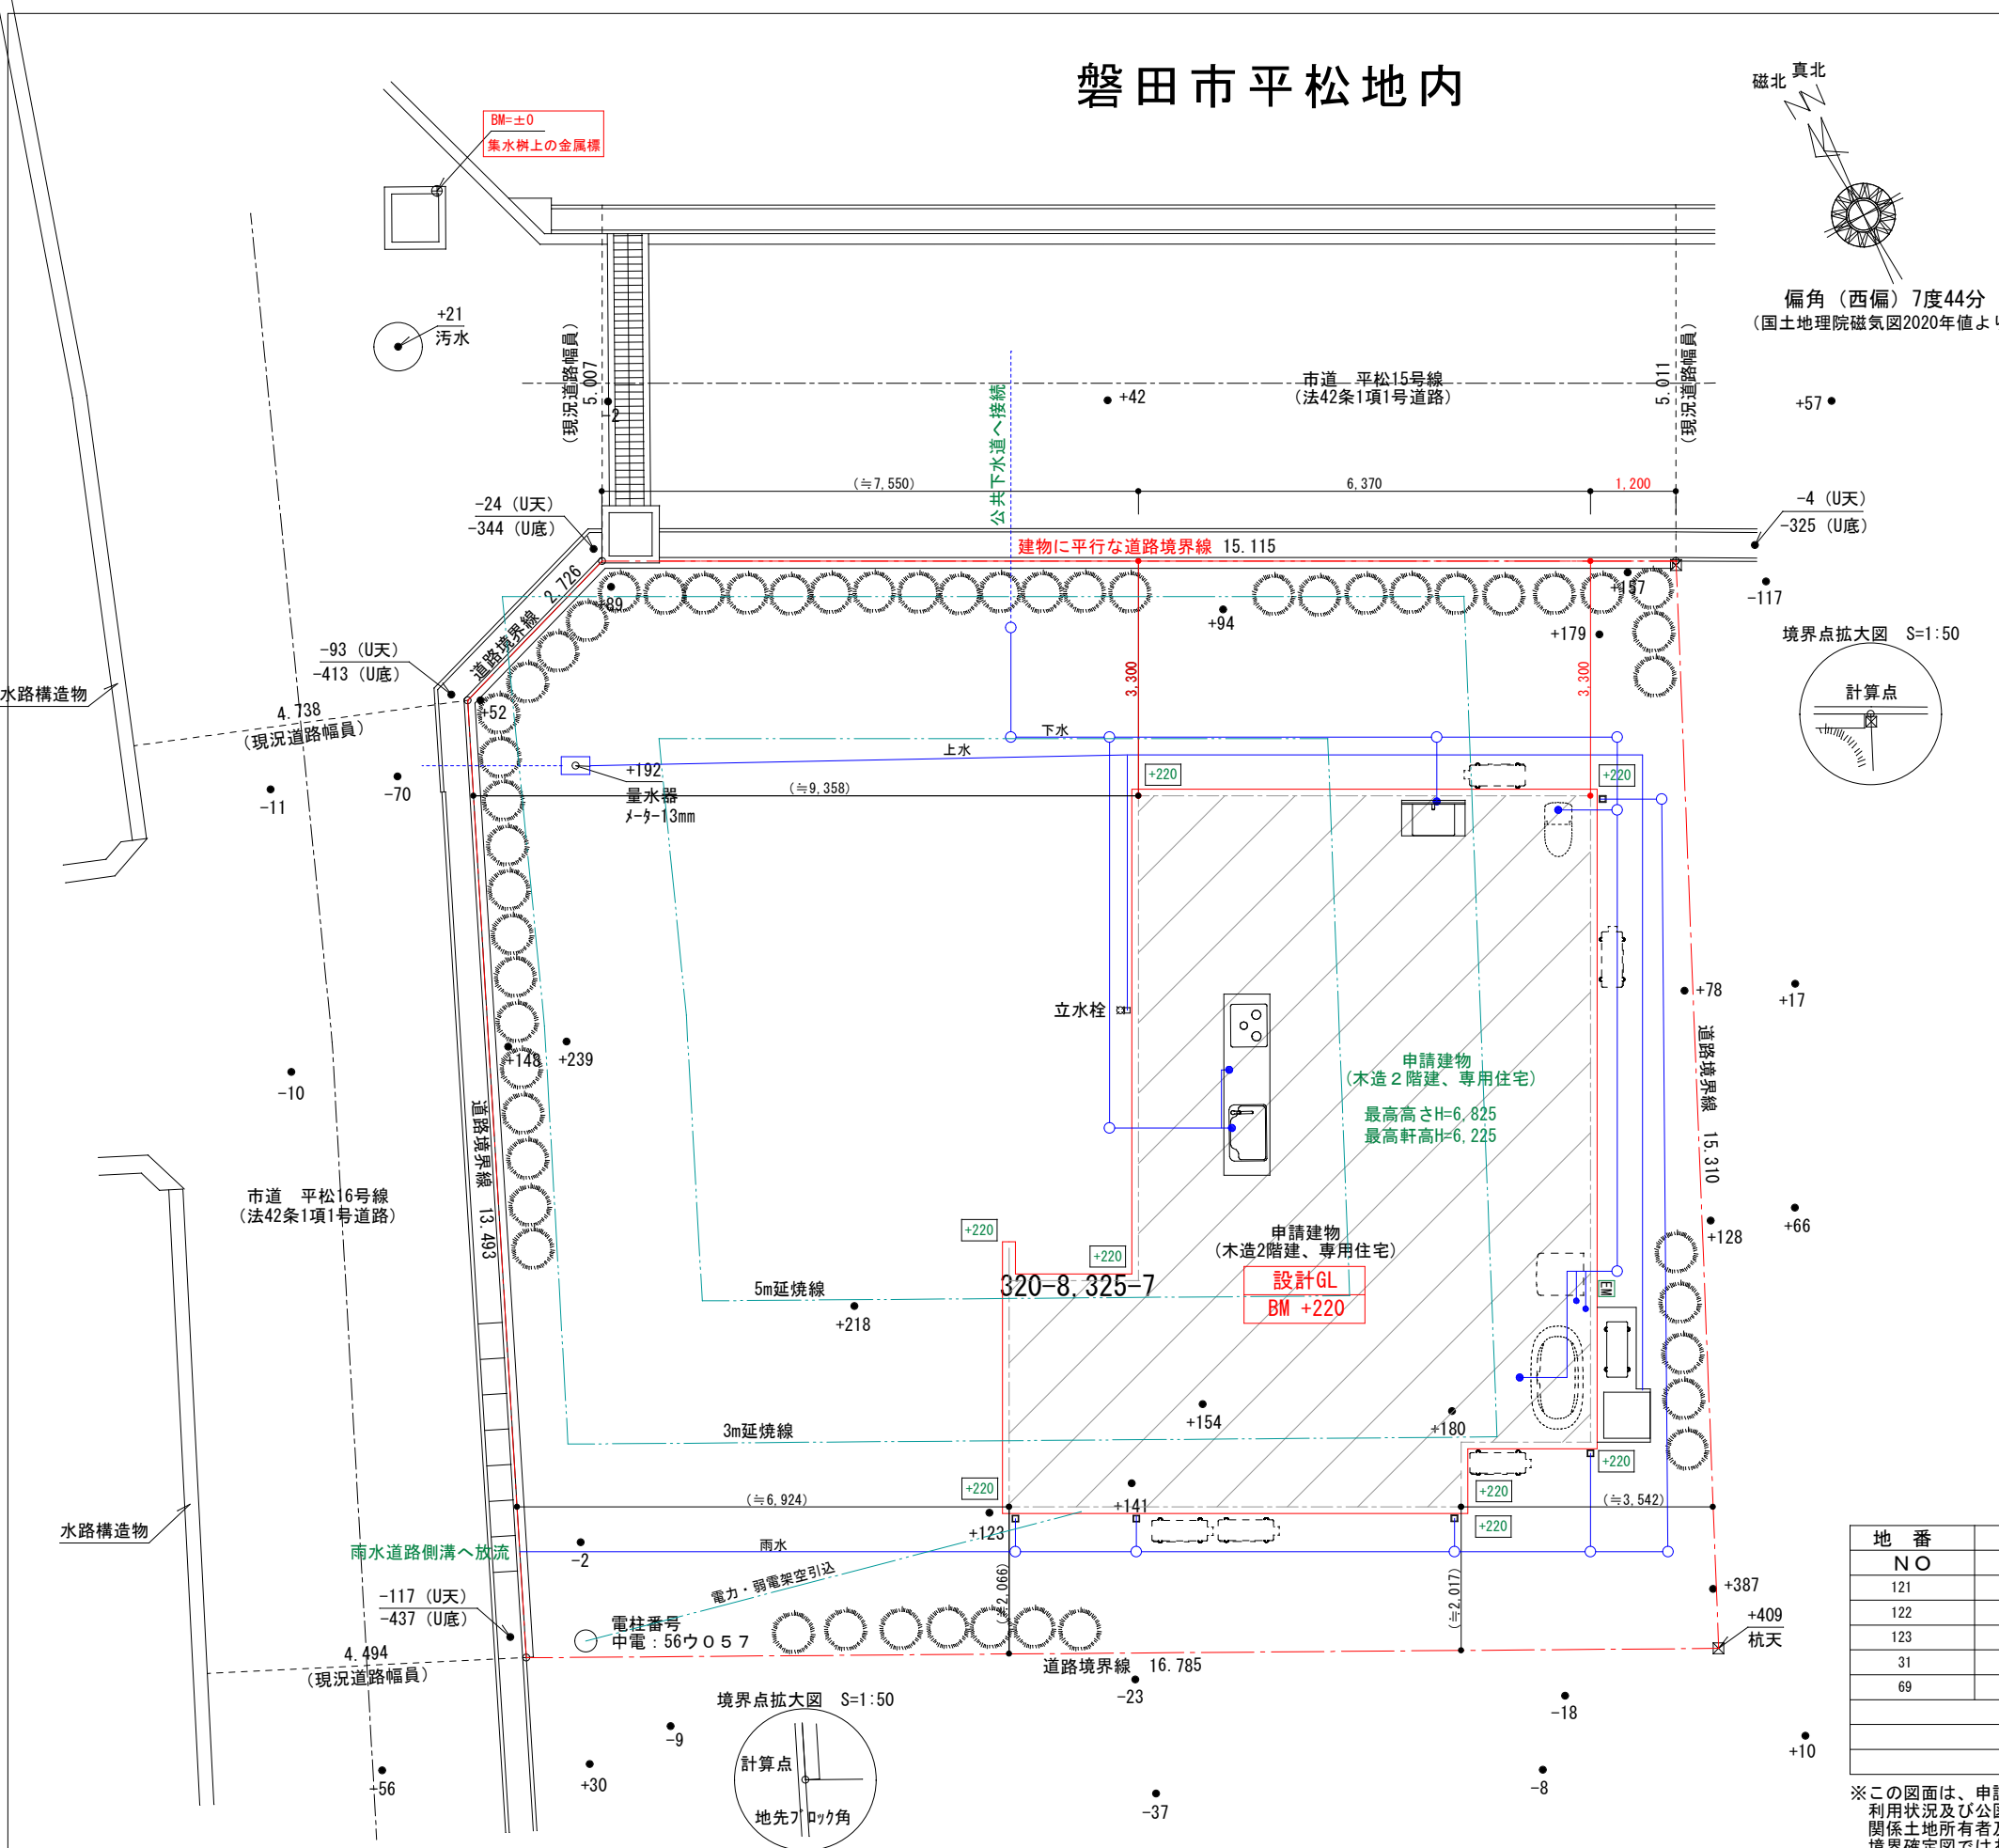

求積図 S=1 : 250

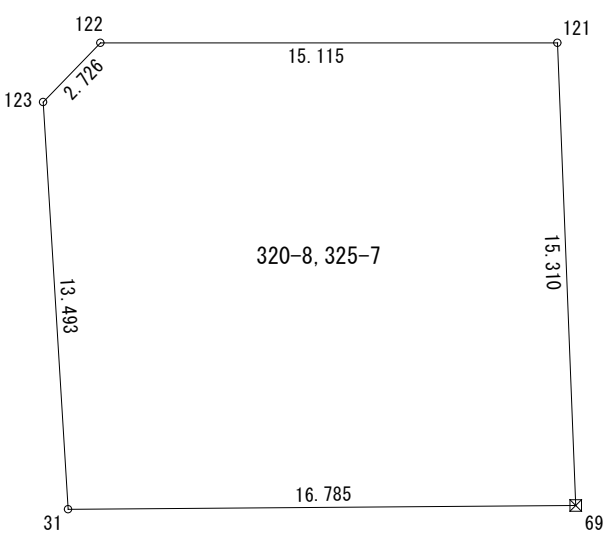

境界点拡大図 S=1:50

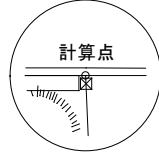

トータル面積表 (㎡)	
敷地面積	258.60
建築面積	68.73
床面積 1階	66.24
2階	50.51
延床面積	116.76
建蔽率	(68.73/258.60) × 100
容積率	(116.76/258.60) × 100


道路斜線制限については、明らかに適合する。
北側斜線制限については、明らかに適合する。
平均地盤面について
申請建物の周囲の平均地盤面高さをBM+220とする。
盛土規制法の許可対象となる工事無し

決定図

求積表

地番	320-8, 325-7			
NO	X _n	Y _n	Y _{n+1} - Y _{n-1}	X _n × (Y _{n+1} - Y _{n-1})
121	86.940	117.408	-5.524	-480.256560
122	94.766	104.477	-15.567	-1475.222322
123	94.070	101.841	-8.903	-837.505210
31	82.121	95.574	8.160	670.107360
69	73.540	110.001	21.834	1605.672360
合計				-517.204372
合計面積				258.6021860
地積				258.60 m ²


※この図面は、申請地及び周囲の現況を簡易測量し、
利用状況及び公図形状から仮で求積した図面です。
関係土地所有者及び道路管理者による境界立会・確認のもと作成された
境界確定図ではありません。

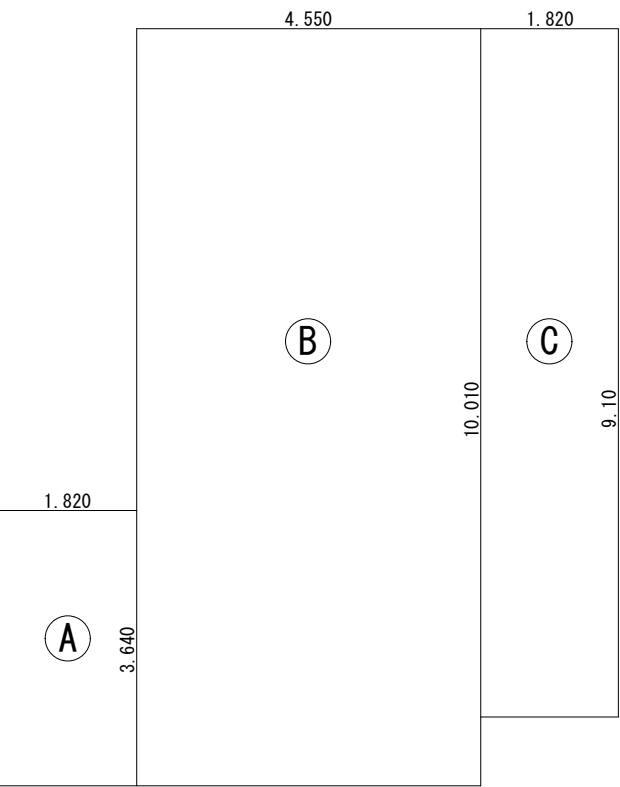

建築面積求積図 S=1/100

建築面積求積表


番号	計算式	(m)	面積 (㎡)
Ⓐ	1.820 × 3.640		6.6248
Ⓑ	4.550 × 10.010		45.5455
Ⓒ	1.820 × 9.10		16.5620
合計			68.7323 68.73 (20.7坪)

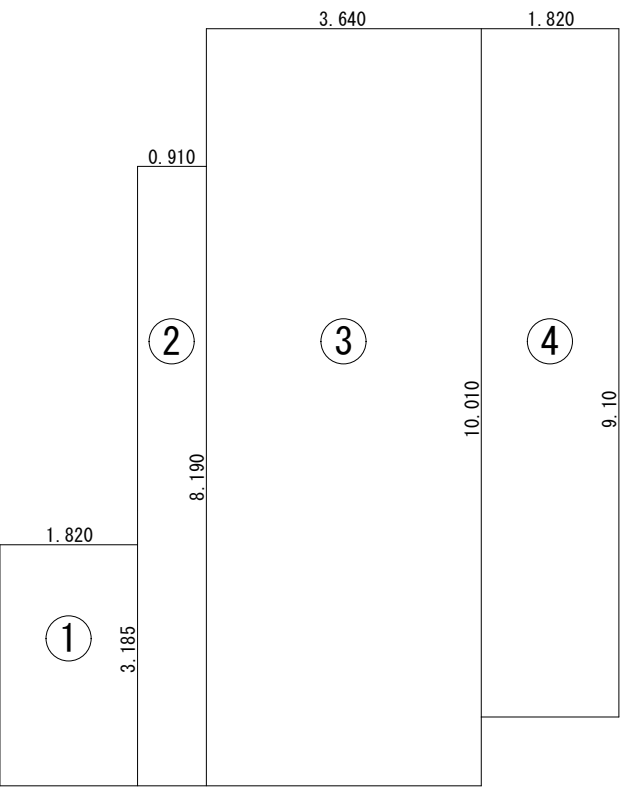

1階床面積図 S=1/100

1階床面積求積表

番号	計算式	(m)	面積 (㎡)
①	1.820 × 3.185		5.7967
②	0.910 × 8.190		7.4529
③	3.640 × 10.010		36.4364
④	1.820 × 9.10		16.5620
合計			66.2480 66.24 (20.0坪)

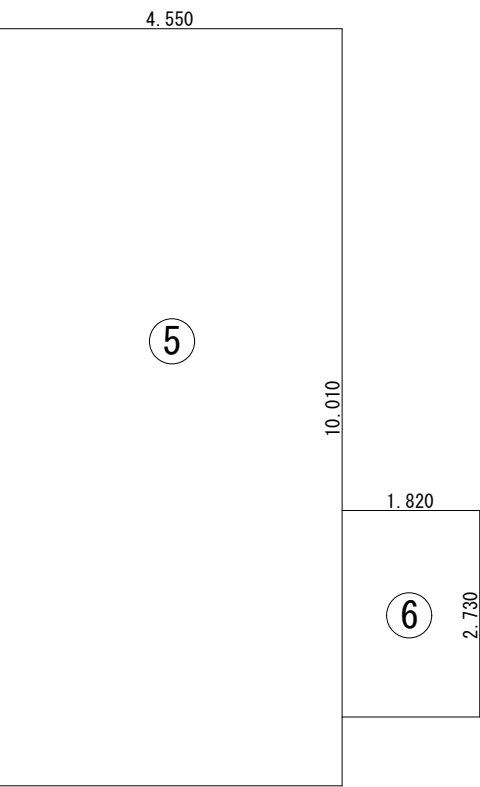

2階床面積図 S=1/100

2階床面積求積表

番号	計算式	(m)	面積 (㎡)
⑤	4.550 × 10.010		45.5455
⑥	1.820 × 2.730		4.9686
合計			50.5141 50.51 (15.2坪)

延べ床面積表

	番号	(m)	面積 (㎡)
1階床面積	① ② ③ ④		66.24
2階床面積	⑤ ⑥		50.51
合計			116.76 (35.3坪)

決定図

G2

壁付け 住宅用火災報知器			数量
H	熱感知器	電池式(単独型)	1
	熱感知器	露出型	
壁付け 住宅用火災報知器			数量
S	煙感知器	電池式(単独型)	
	煙感知器	露出型	

※ 煙感知器は壁・梁より600mm以上離す
壁に取付ける場合、
天井から150mm以上500mm以内離す
換気扇・エアコン吹出口から1500mm以上離す
※ 全室LED照明とする。
※ 標準天井高さ2,400
※ 特記無きガラスは型ガラス

* 凡例

管柱 (105×105)

Kタツバ
(3.30倍 FRM-0641)

片筋違い
(2.00倍 45×90)
(例 左:柱脚 右:柱頭)

たすき掛筋違い
(4.00倍 45×90)

構造用合板 (2.70倍)
(t=9 タイプ-EXハイパー)

床点検口

天井点検口

換気扇


熱交換換気扇VLR-70

※ 全室LED照明とし、調光制御を採用する。
※ 非居室の照明は人感センサーを採用する。

※ 階段寸法

蹴上: 207.14 (2900÷14段)
路面: 227.5
有効幅: 780
手摺出幅100mm以下

決定図

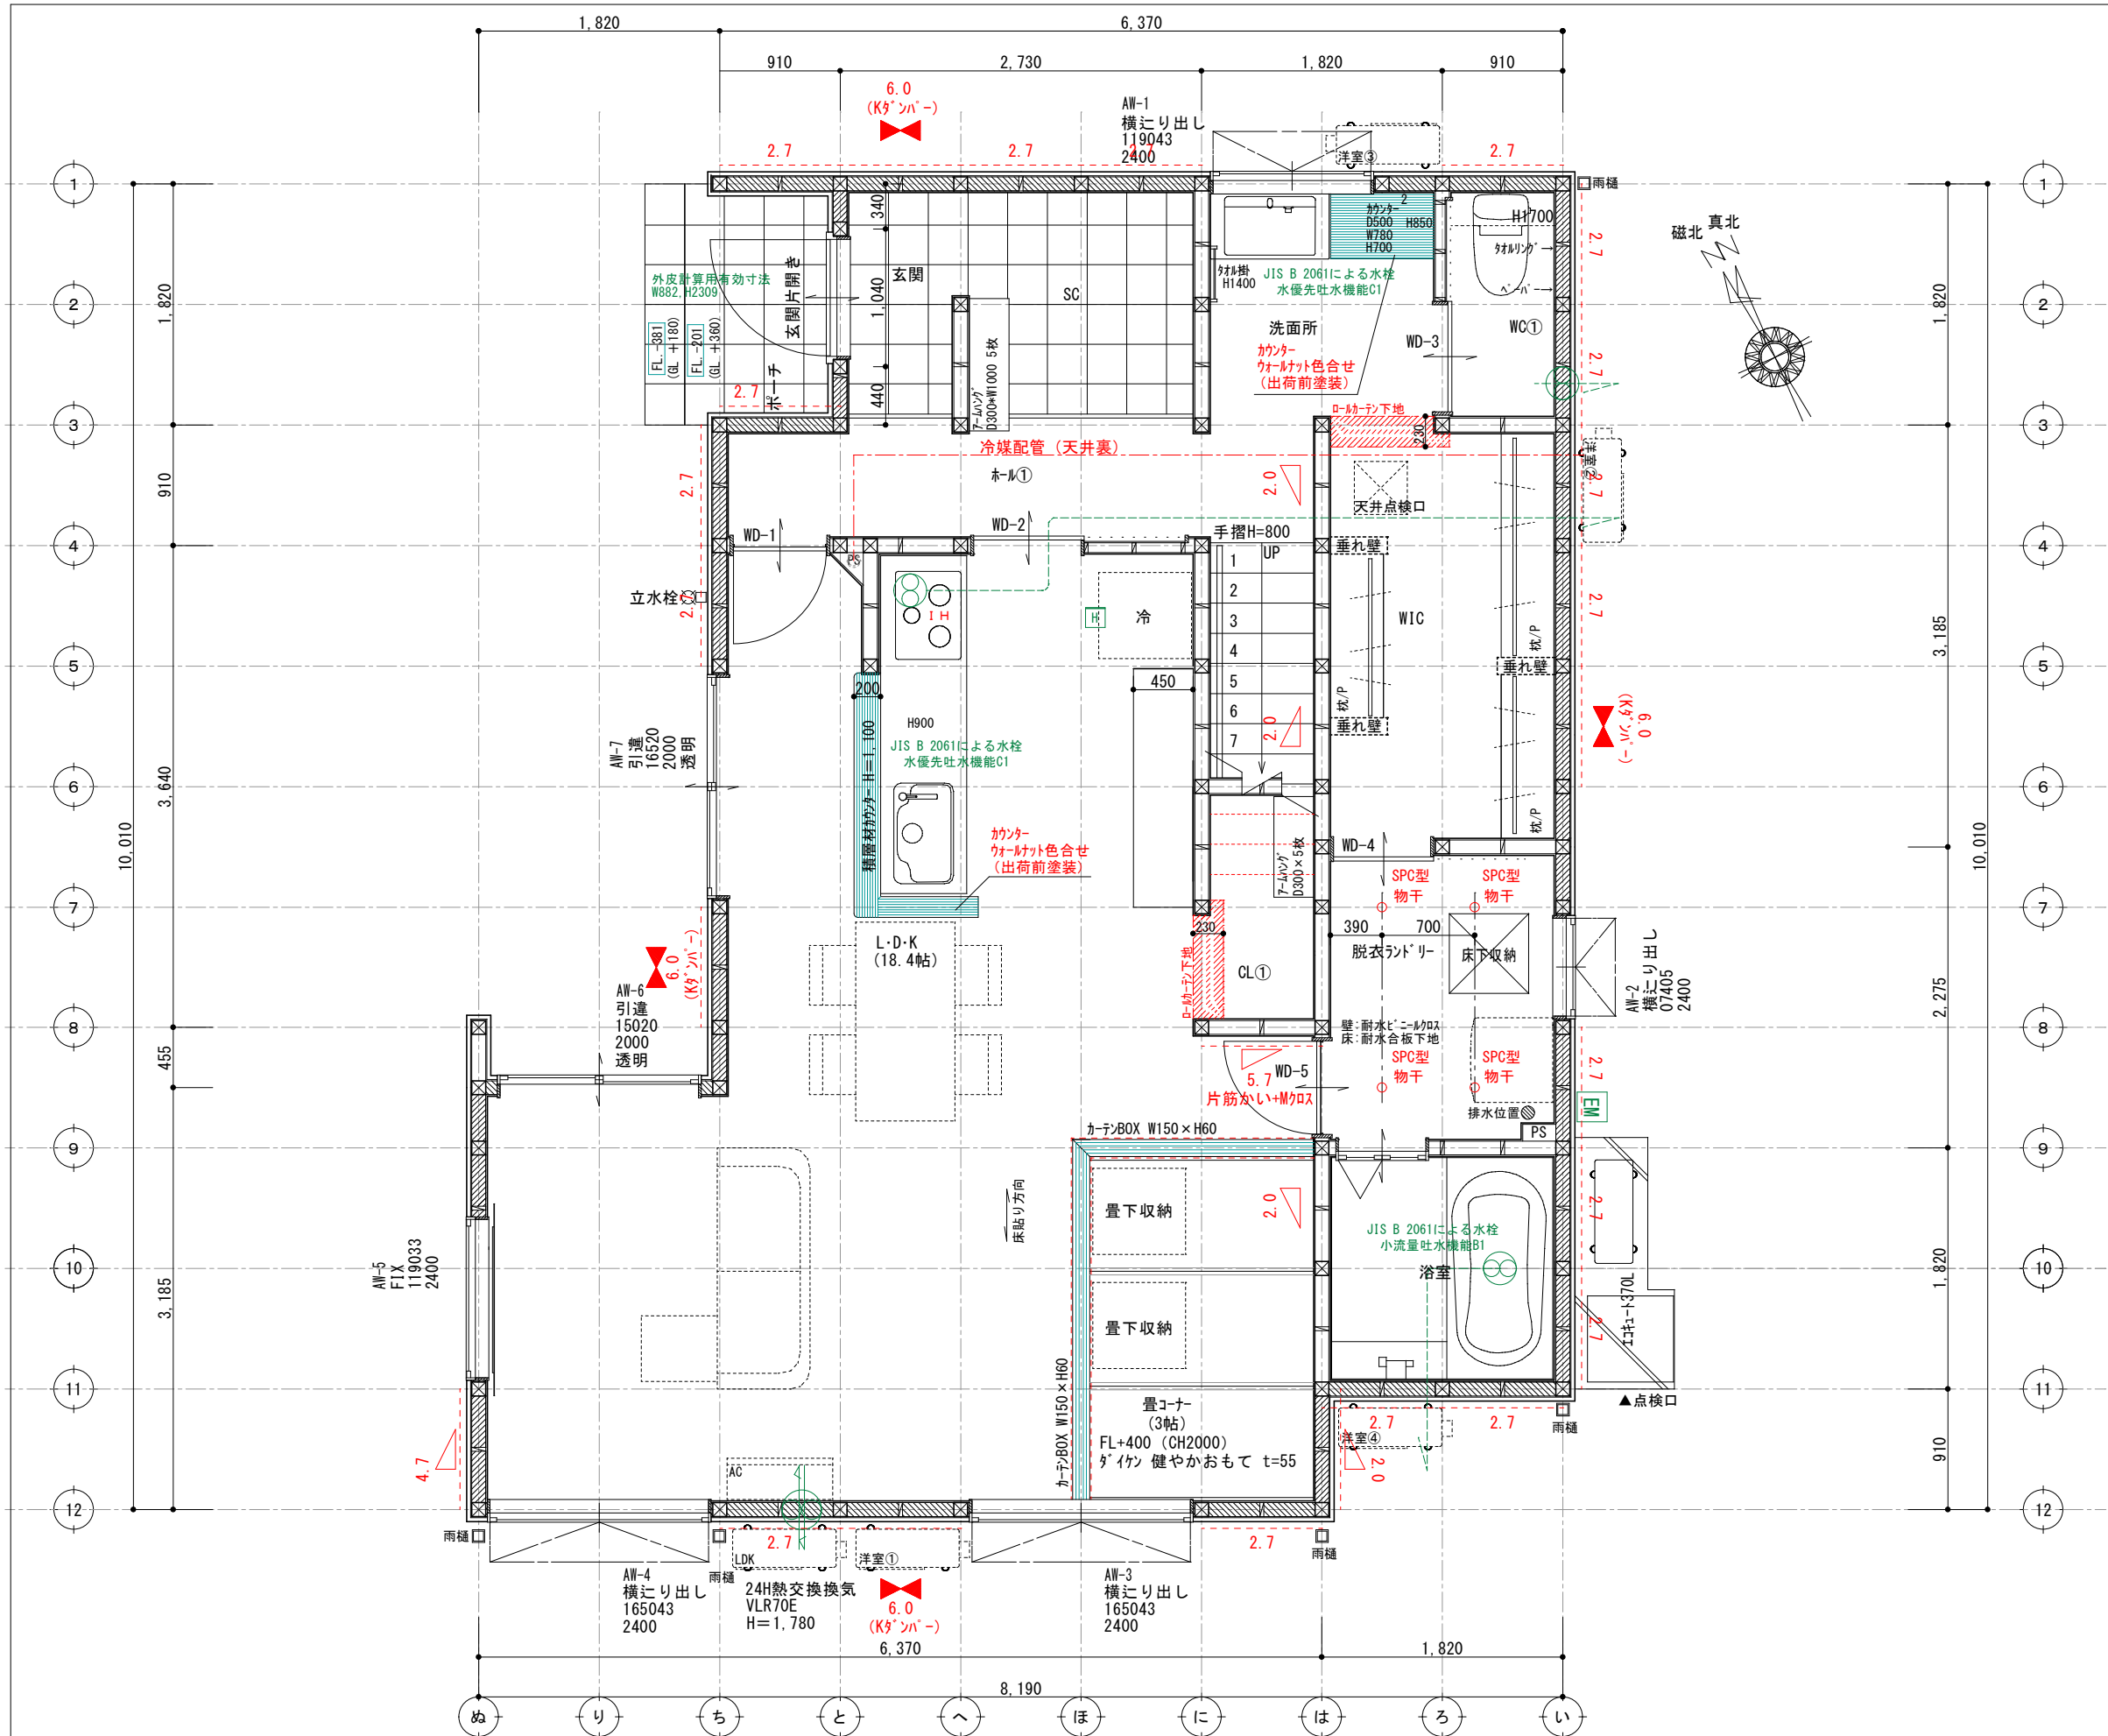

訂正	浜岡一級総合設計事務所 一級建築士事務所 静岡県知事登録第 (10)2441 号 一級建築士 大臣登録第 365879 号 西原利昌	PG HOUSE ピージーハウス	株式会社 LIFEFUND InDesign office 一級建築士事務所 事務所登録 (2) 第7595号 一級建築士登録 第179770号 鈴木 達男 〒432-8023 静岡県浜松市中央区鴨江3丁目70番23号	年月日 2025. 9. 5	件名 清水裕也様・穂菜実様邸 新築工事	設計 IC	工事 青島	図番 3-1
				縮尺 1/50	図名 1階平面図	酒井		

G2

壁付け 住宅用火災報知器			数量
H 熱感知	電池式(単独型)		
	露出型		
壁付け 住宅用火災報知器			数量
S 煙感知	電池式(単独型)		4
	露出型		

※ 煙感知器は壁・梁より600mm以上離す
壁に取付ける場合、
天井から150mm以上500mm以内離す
換気扇・エアコン吹出口から1500mm以上離す
※ 全室LED照明とする。
※ 標準天井高さ2,400
※ 特記無きガラスは型ガラス

* 凡例


- ☒ 管柱 (105×105)
- ◀▶ Kダクト (3.30倍 FRM-0641)
- △ 片筋違い (2.00倍 45×90)
(例 左:柱脚 右:柱頭)
- ◊ たすき掛筋違い (4.00倍 45×90)
- 構造用合板 (2.70倍)
(t=9 材種-EXハイパー)
- ◻ 床点検口
- ◻ 天井点検口
- ↻ 換気扇
- ↻ 熱交換換気扇VLR-70

※ 全室LED照明とし、調光制御を採用する。
※ 非居室の照明は人感センサーを採用する。



アドバンスシリーズ		
スマートデザイン (外部)		
凡例	1	コンセント 1ヶ所
①	2	コンセント 2ヶ所
②	3	コンセント 3ヶ所
①ET	コンセント1ヶ所接地ターミナル付	
②ET	コンセント2ヶ所接地ターミナル付	
WP	コンセント 防水型	
Ⓜ	エアコン用コンセント	
Ⓜ	200V用コンセント	
WP	防雨入線プレート	
スイッチ		
●	3路スイッチ	
●	4路スイッチ	
Ⓜ	直結電源	
TV	テレビ取出口	
TEL	電話取出口 (テレホンガイド)	
LAN	LAN取出口 (テレホンガイド)	
壁照明		
リモコン (給湯関係・ルフロ)		
メーター		
分電盤		
チャイム		

※ACコンセント天井付け
※TVアンテナ工事
※スイッチはFL+1100、コンセントはFL+200

決定図

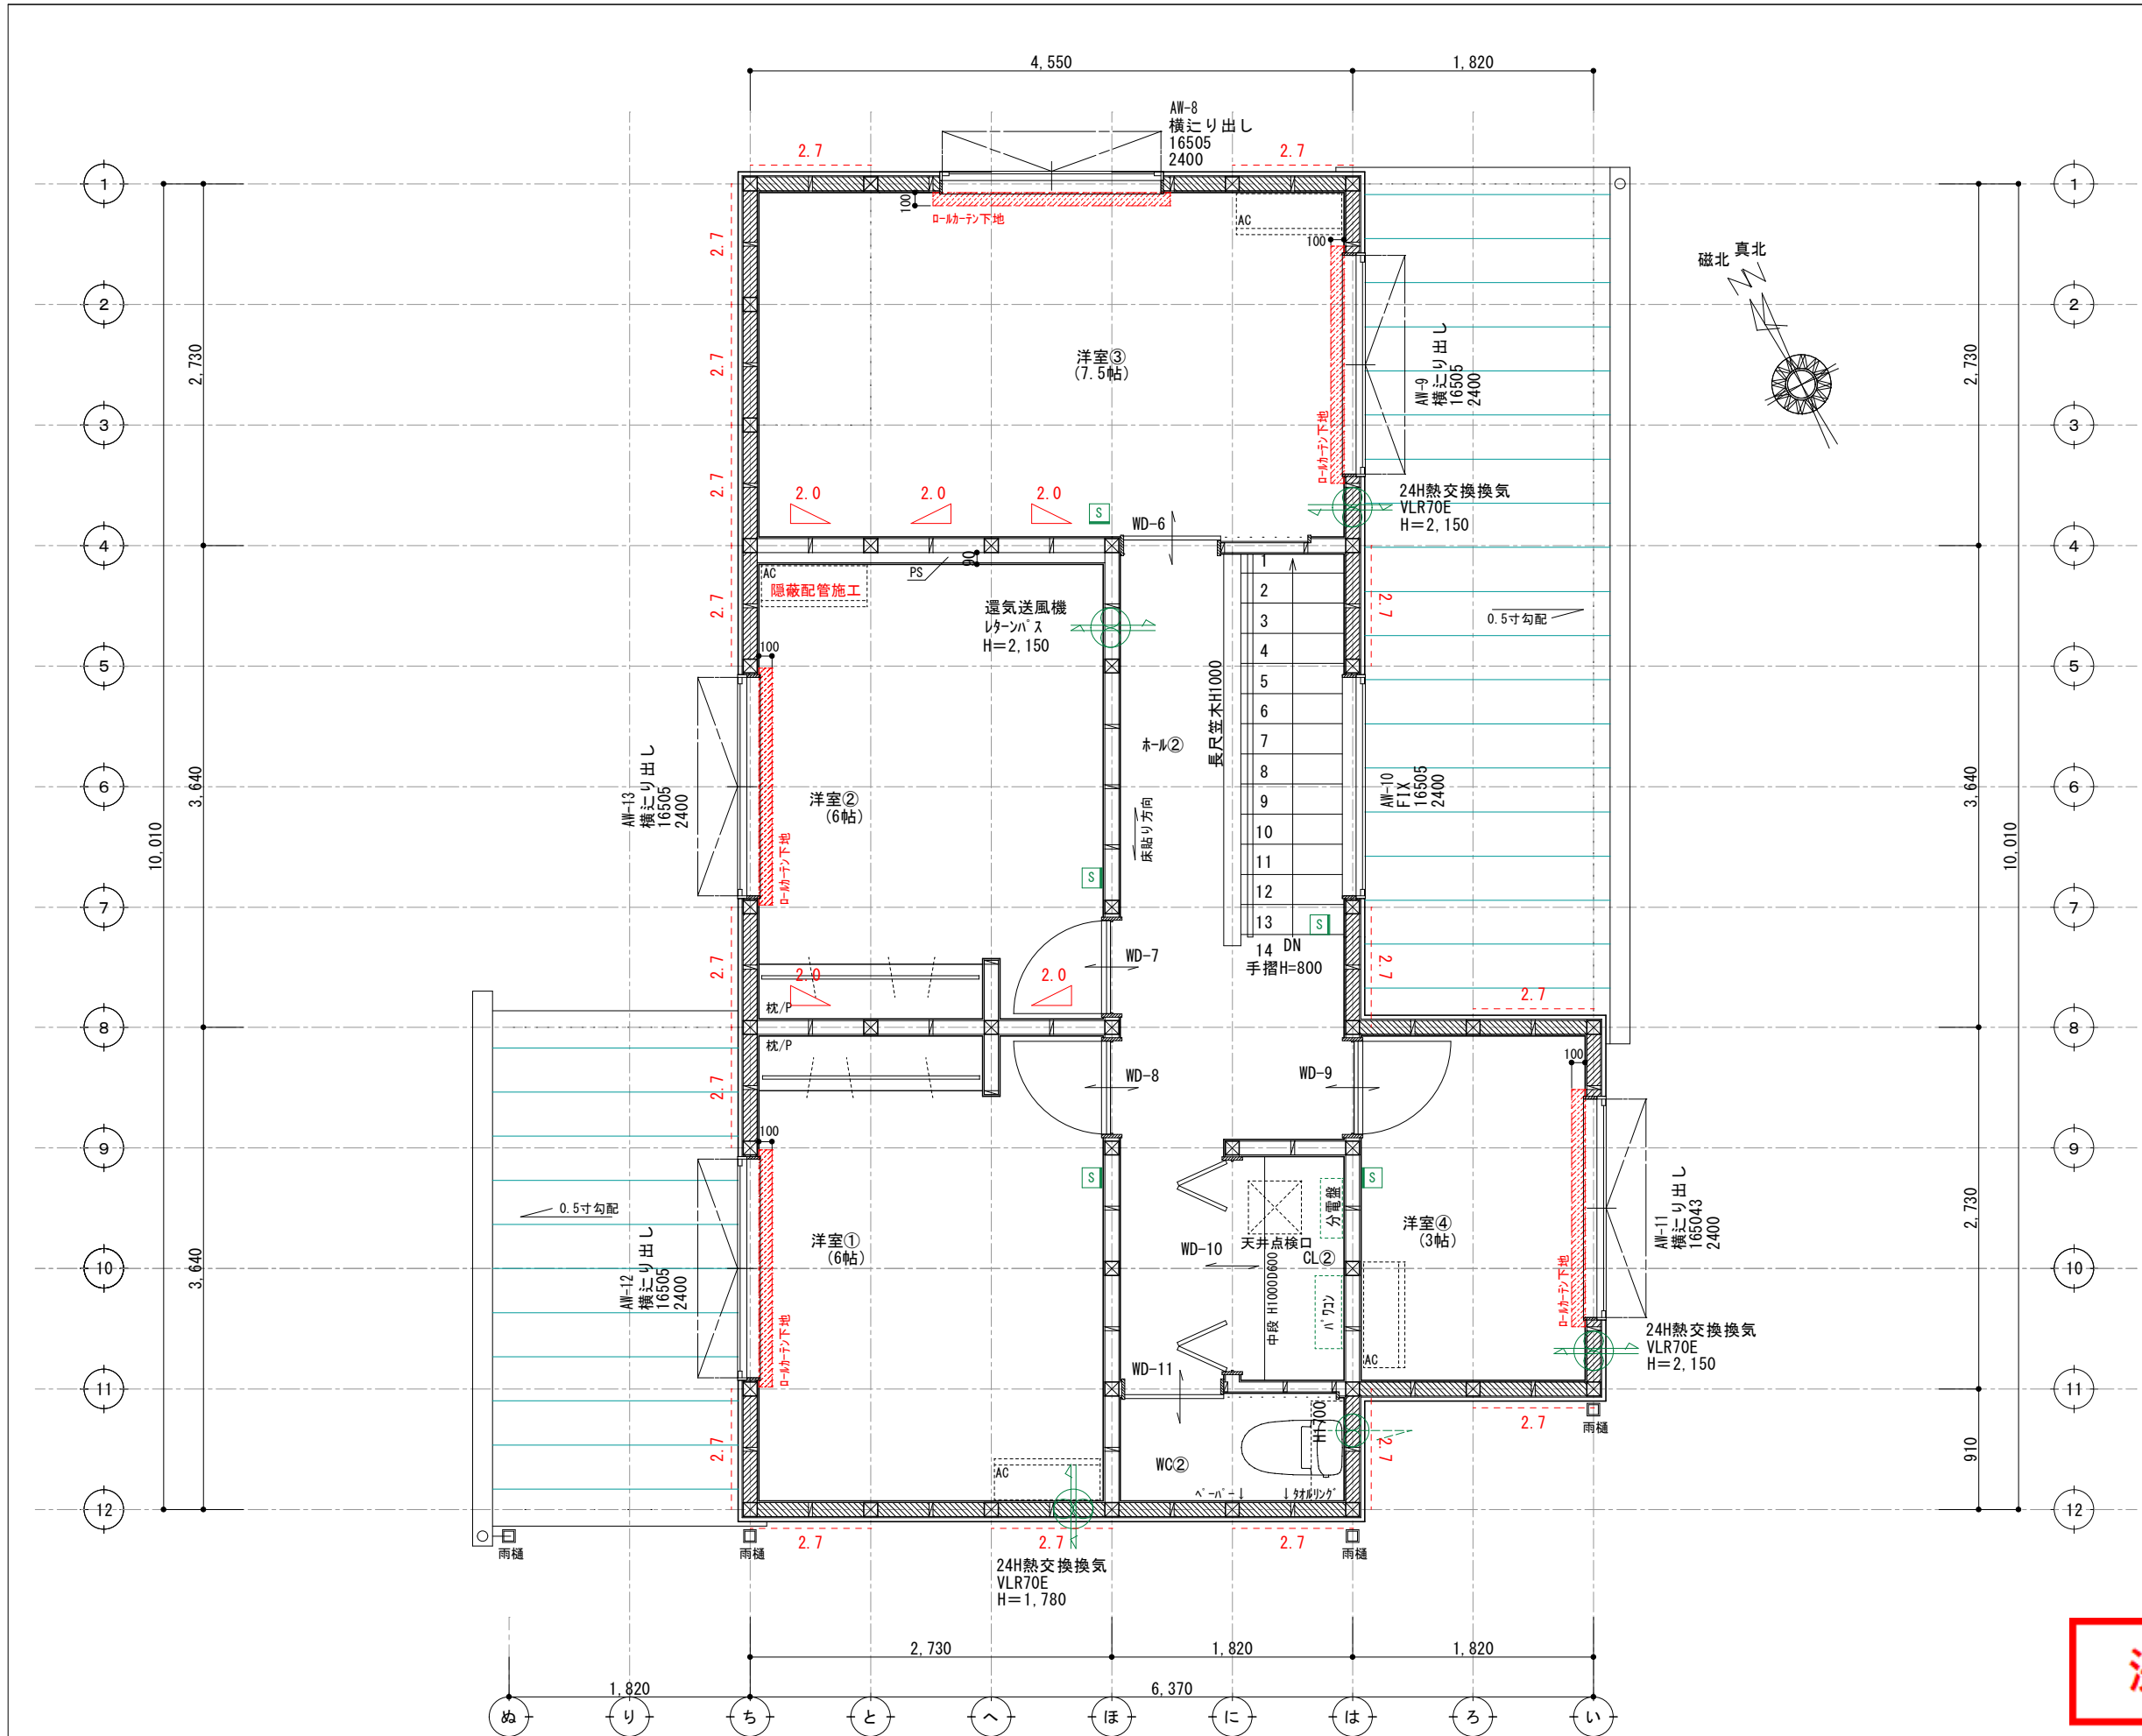


G2

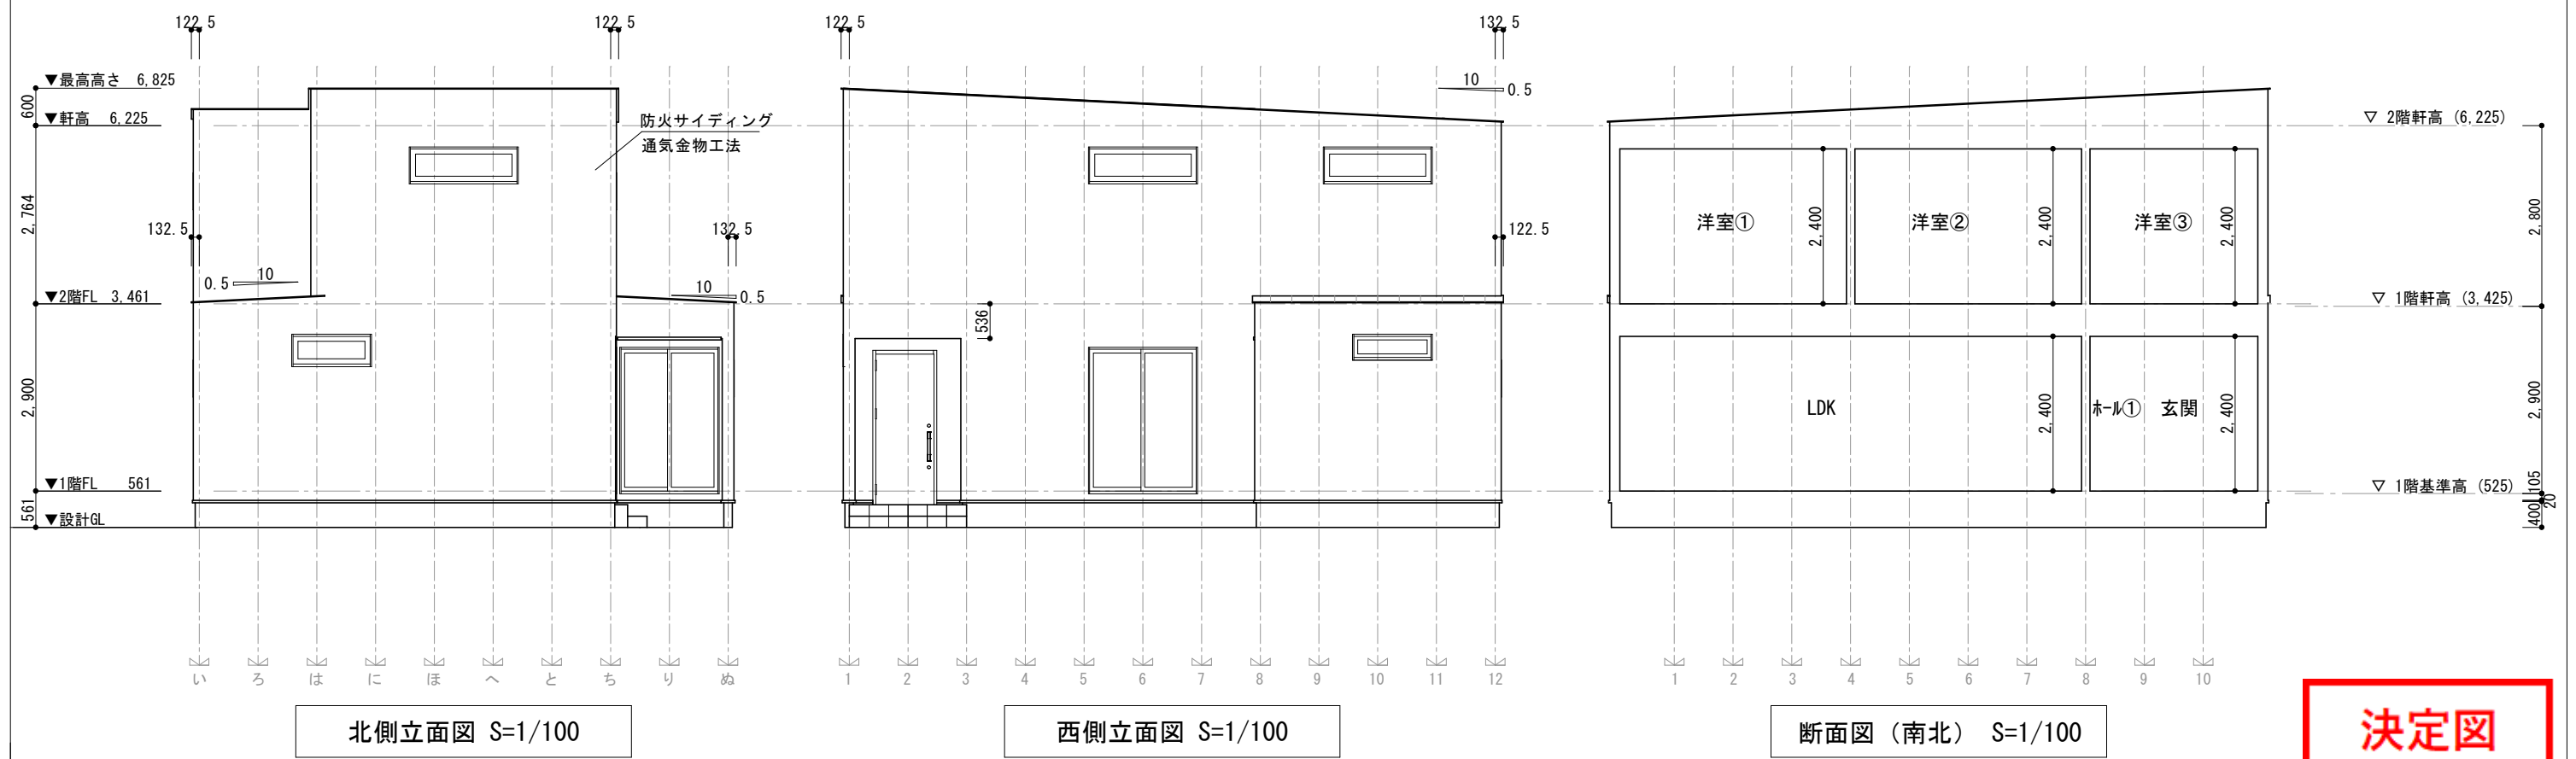
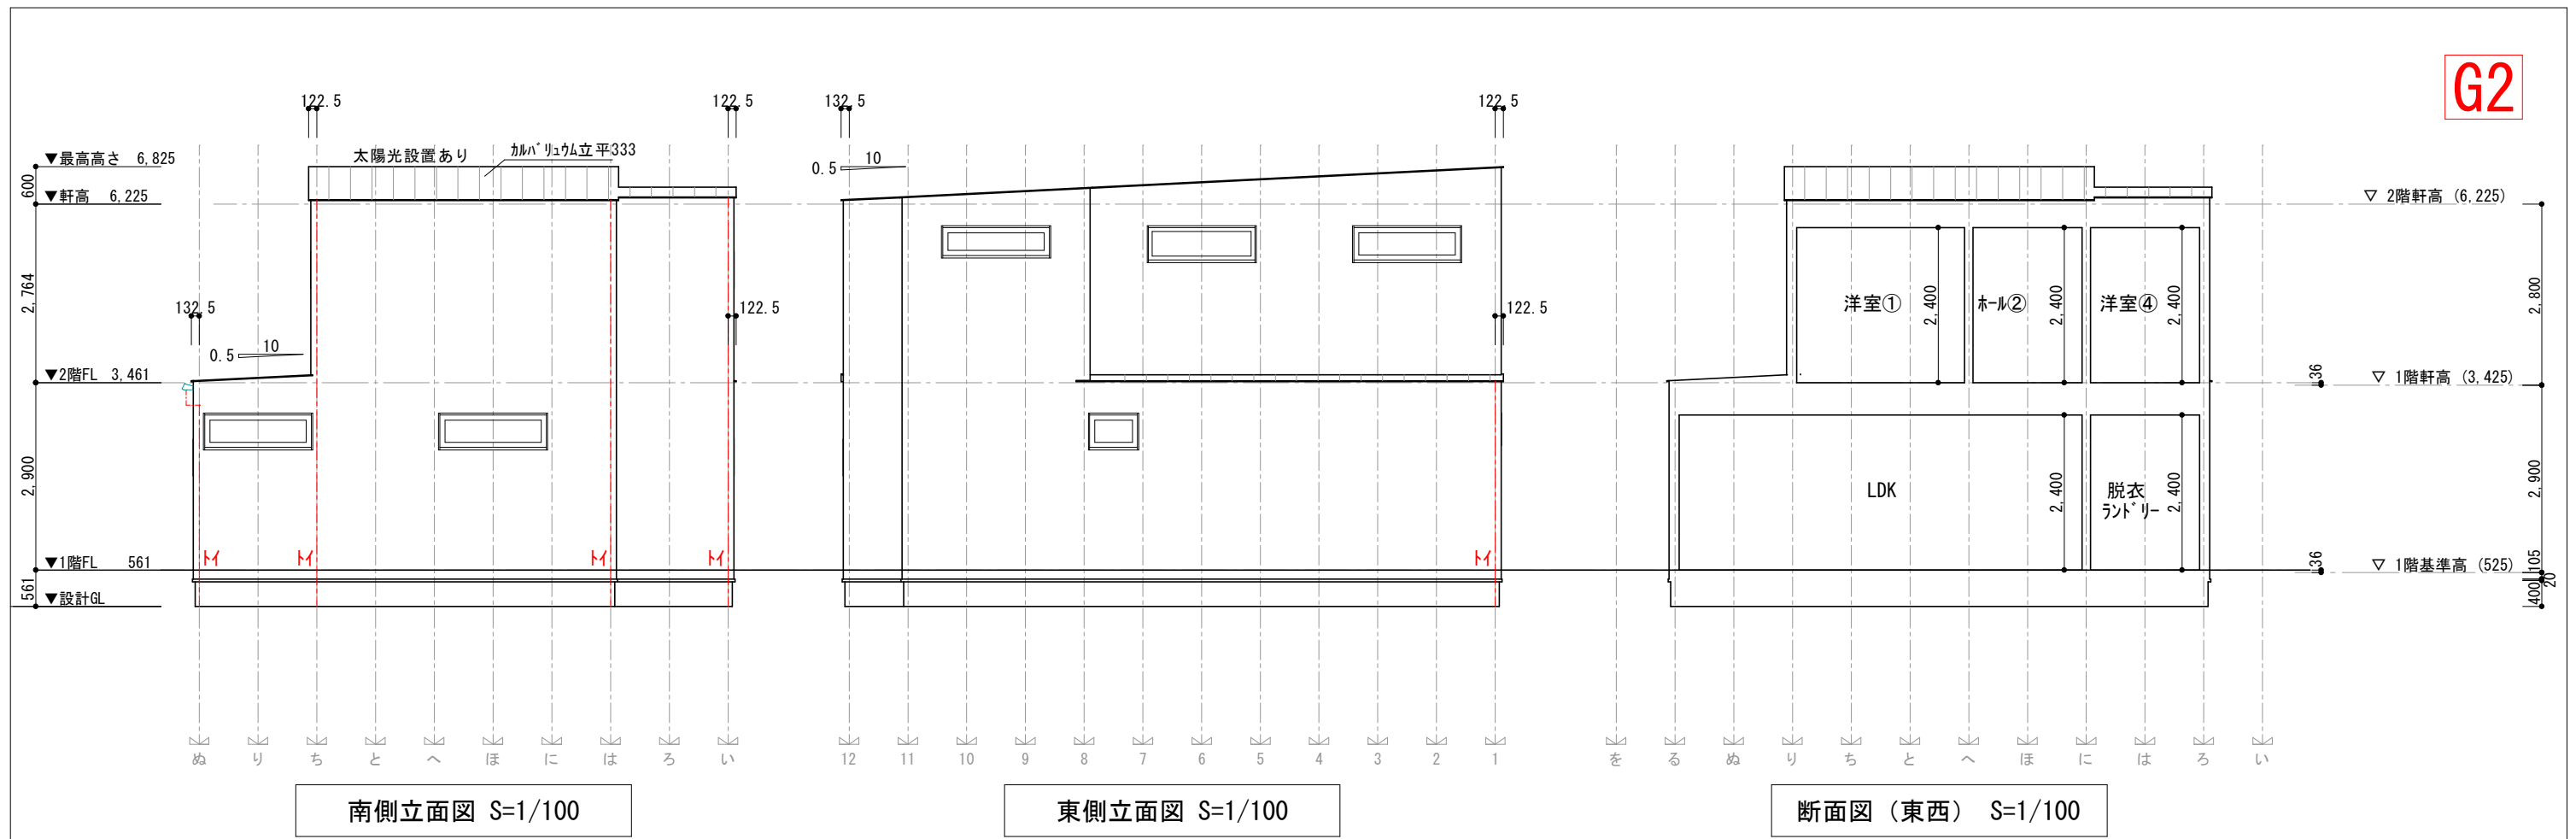


決定図


訂 正	浜 岡 一 級 総 合 設 計 事 務 所 一級建築士事務所 静岡県知事登録第 (10)2441 号 一級建築士 大臣登録第 365879 号 西原利昌		株式会社 LIFEFUND InDesign office 一級建築士事務所 事務所登録 (2) 第7595号 一級建築士登録 第179770号 鈴木 達男 〒432-8023 静岡県浜松市中央区鴨江3丁目70番23号	年 月 日	件 名			設計	IC	工事	図 番
				2025. 9. 5	清水裕也様・穂菜実様邸 新築工事						
				縮 尺	図 名						
				1/100	立面図			酒井		青 島	4

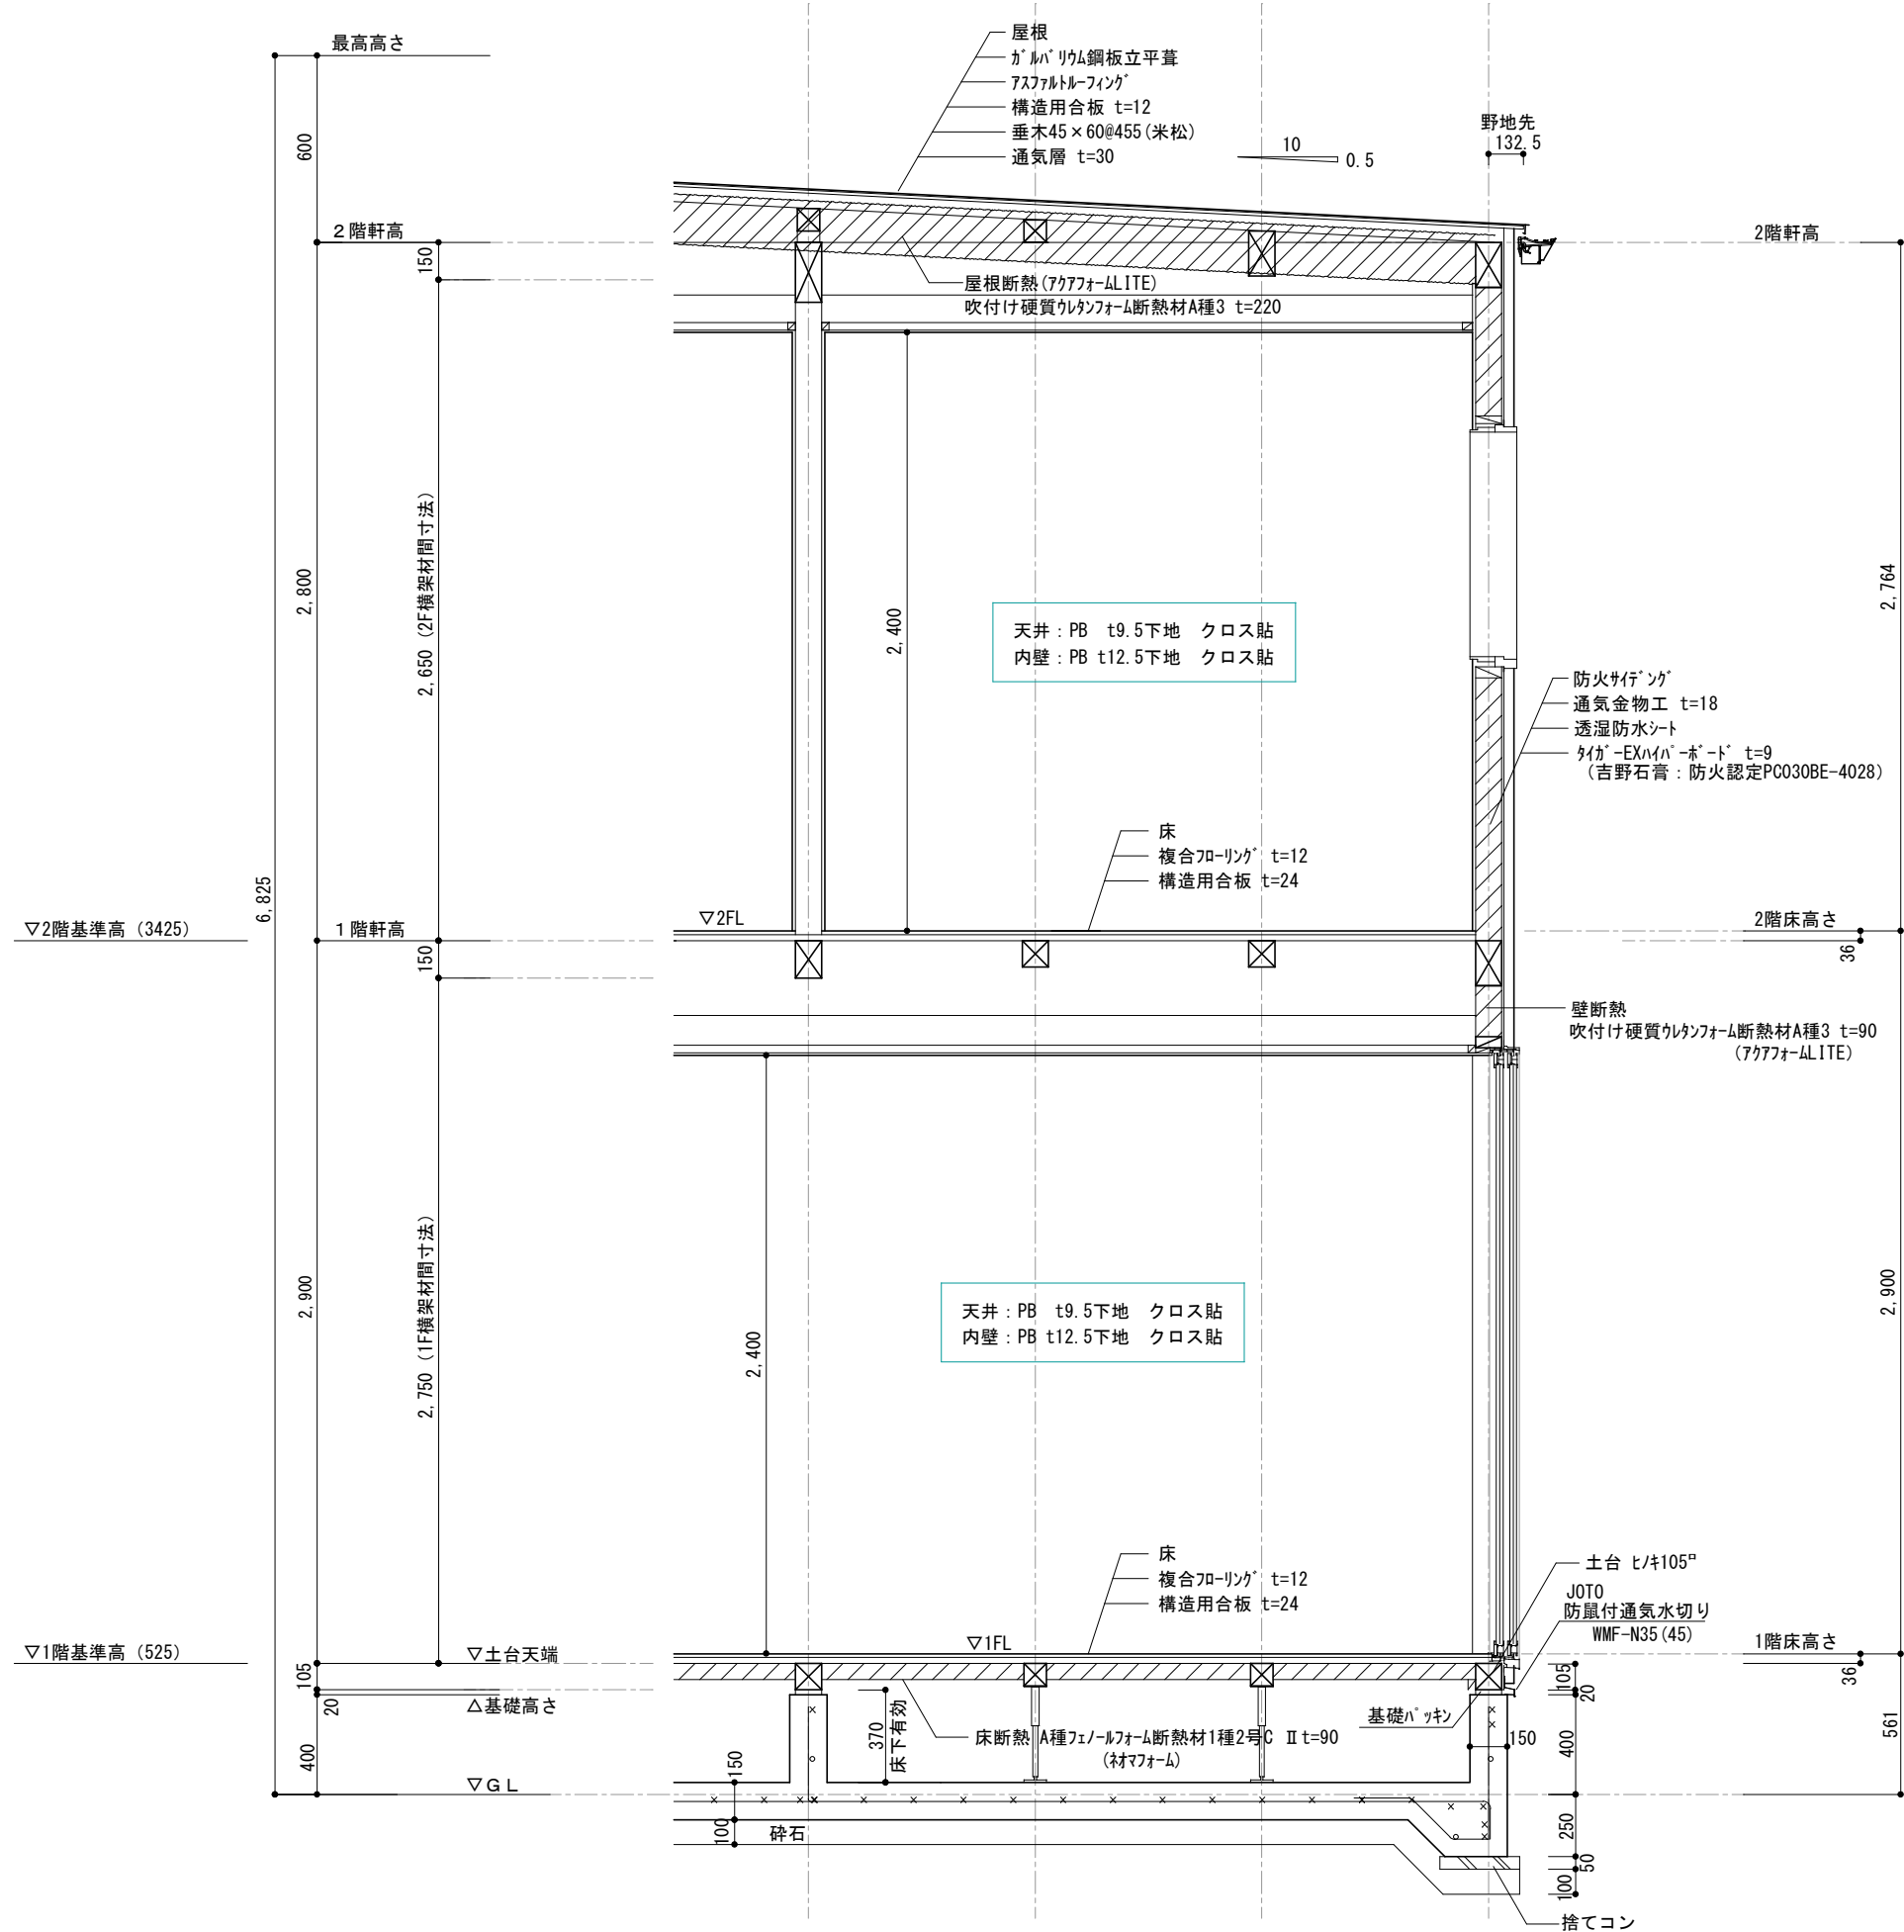


決定図

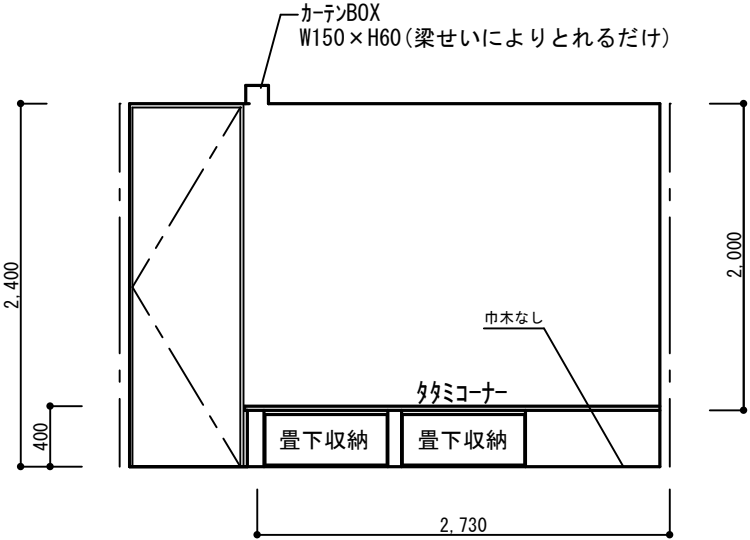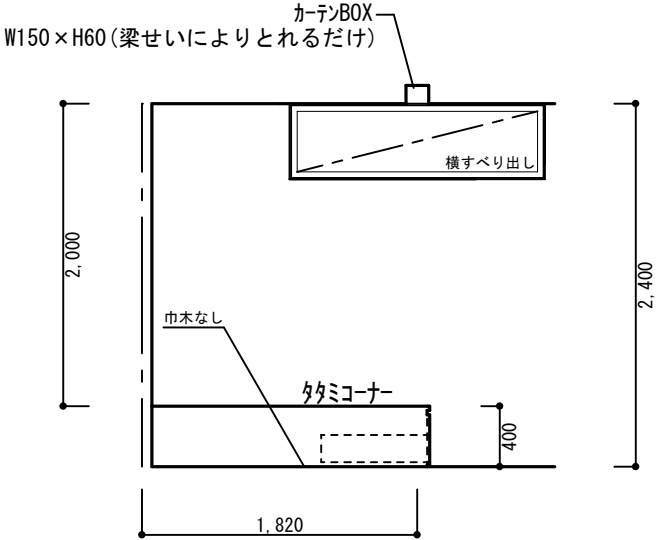


タタミコーナー 東面

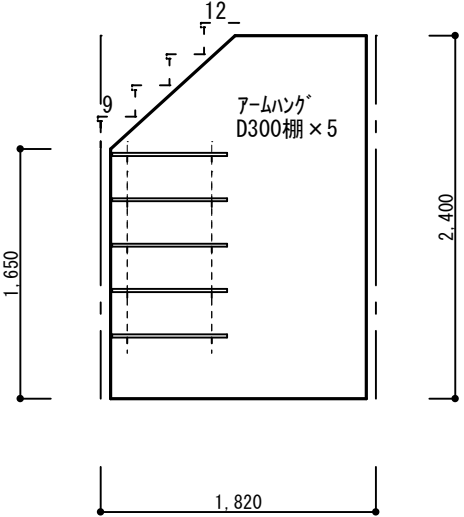

CL① 東面

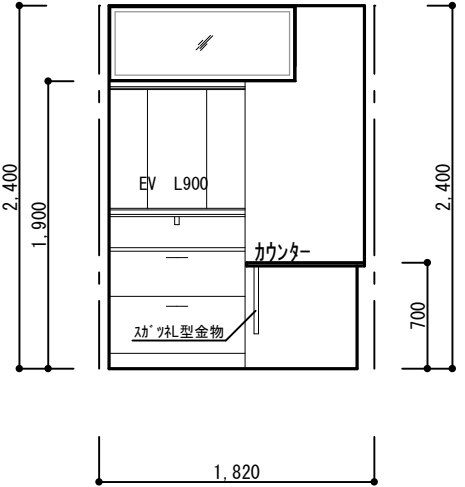


洗面所 北面

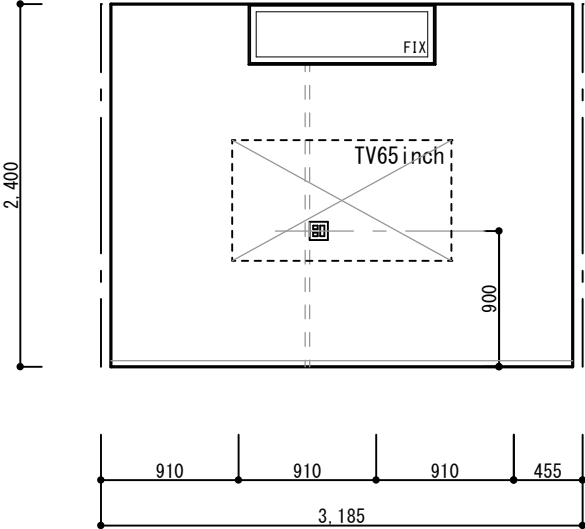


LDK 西面

決定図


訂正	浜岡一級総合設計事務所 一級建築士事務所 静岡県知事登録第 (10)2441 号 一級建築士 大臣登録第 365879 号 西原利昌	LIFEFUND PG HOUSE	株式会社 LIFEFUND InDesign office 一級建築士事務所 事務所登録 (2) 第7595号 一級建築士登録 第179770号 鈴木 達男 〒432-8023 静岡県浜松市中央区鴨江3丁目70番23号	年月日 2025.9.5 縮尺 1/50	件名 清水裕也様・穂菜実様邸 新築工事 図名 展開図-1		設計 酒井	IC	工事 青島	図番 6-1
----	--	----------------------	---	-------------------------------	---------------------------------------	--	----------	----	----------	-----------

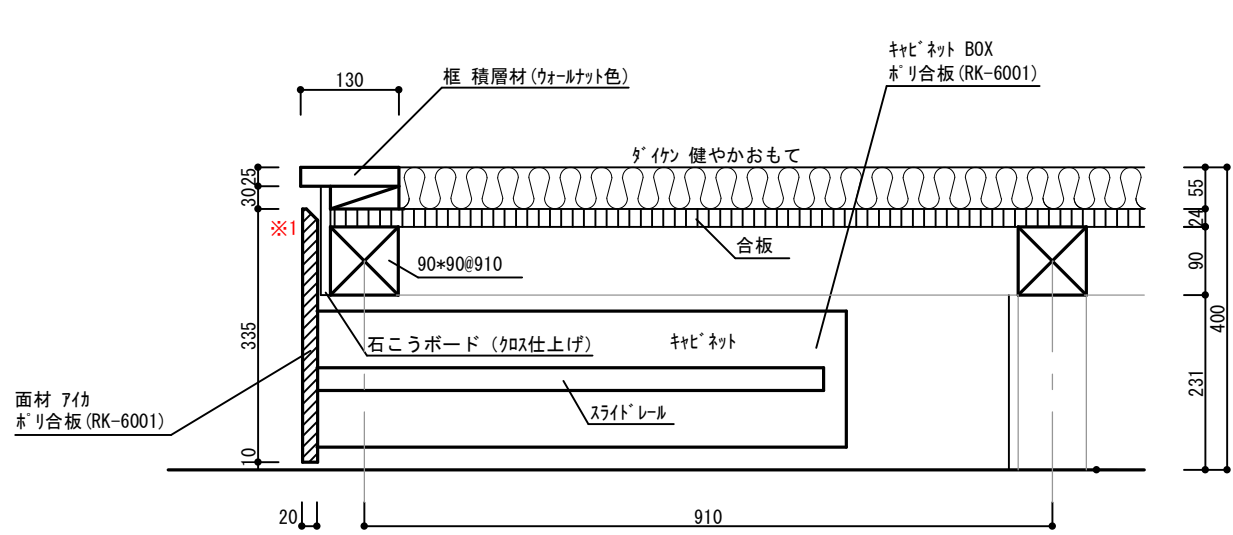


置下収納 断面詳細図 1/10

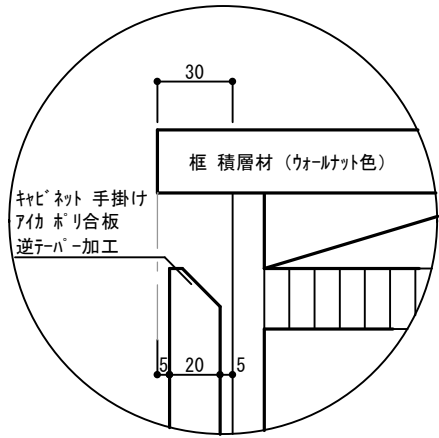


※1 キャベネット 手掛け部分詳細図

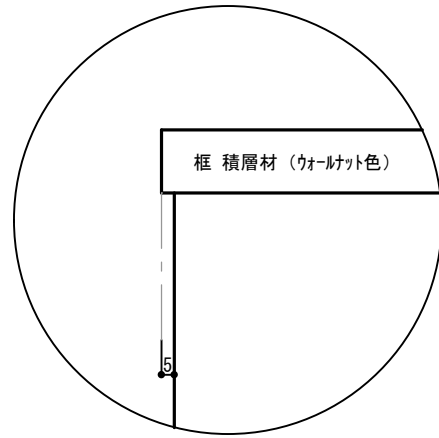

※2 框 取合い詳細図

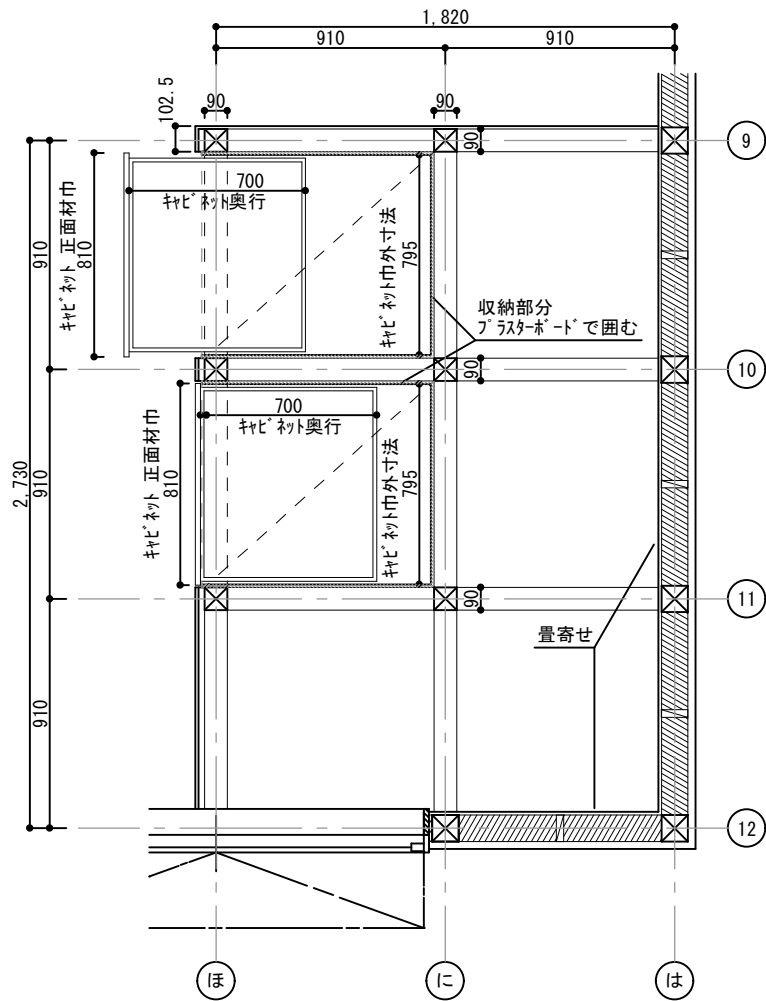


置コーナー 平面詳細図 1/30

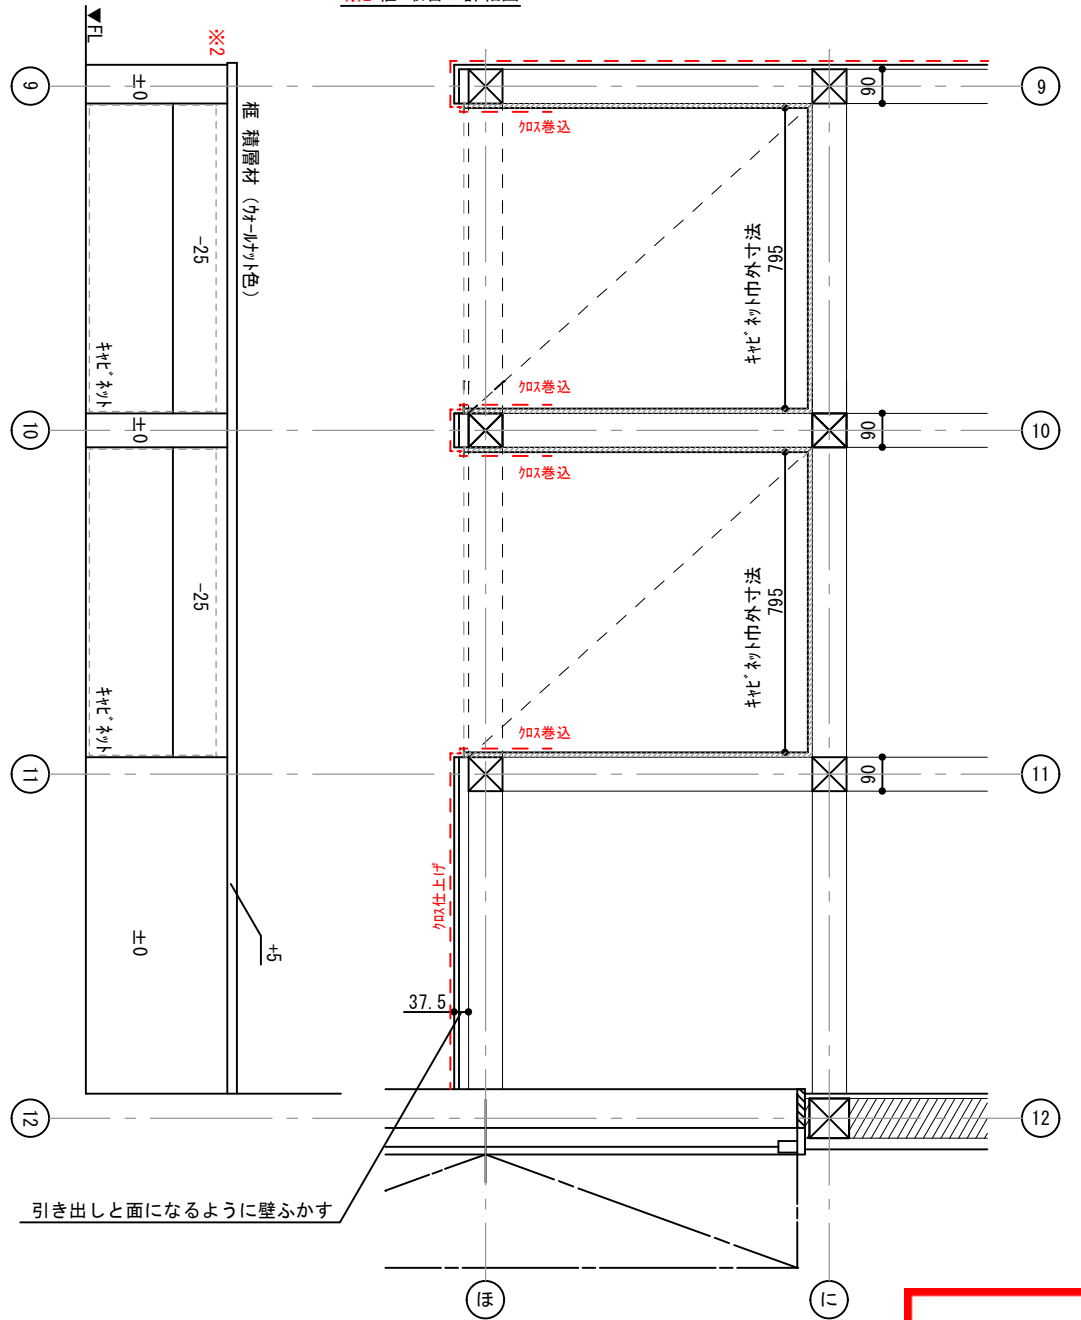

置コーナー 平面詳細図 1/20

決定図

訂 正	浜 岡 一 級 総 合 設 計 事 務 所 一級建築士事務所 静岡県知事登録第 (10)2441 号 一級建築士 大庄登録第 365879 号 西原利昌	LIFEFUND PG HOUSE	株式会社 LIFEFUND InDesign office 一級建築士事務所 事務所登録 (2) 第7595号 一級建築士登録 第179770号 鈴木 達男 〒432-8023 静岡県浜松市中央区鶴江3丁目70番23号	年 月 日	件 名		設計	IC	工事	図 番
				2025.9.5	清水裕也様・穂菜実様邸 新築工事					
				縮 尺	図 名					
				1/50	展開図-2		酒井		青島	6-1

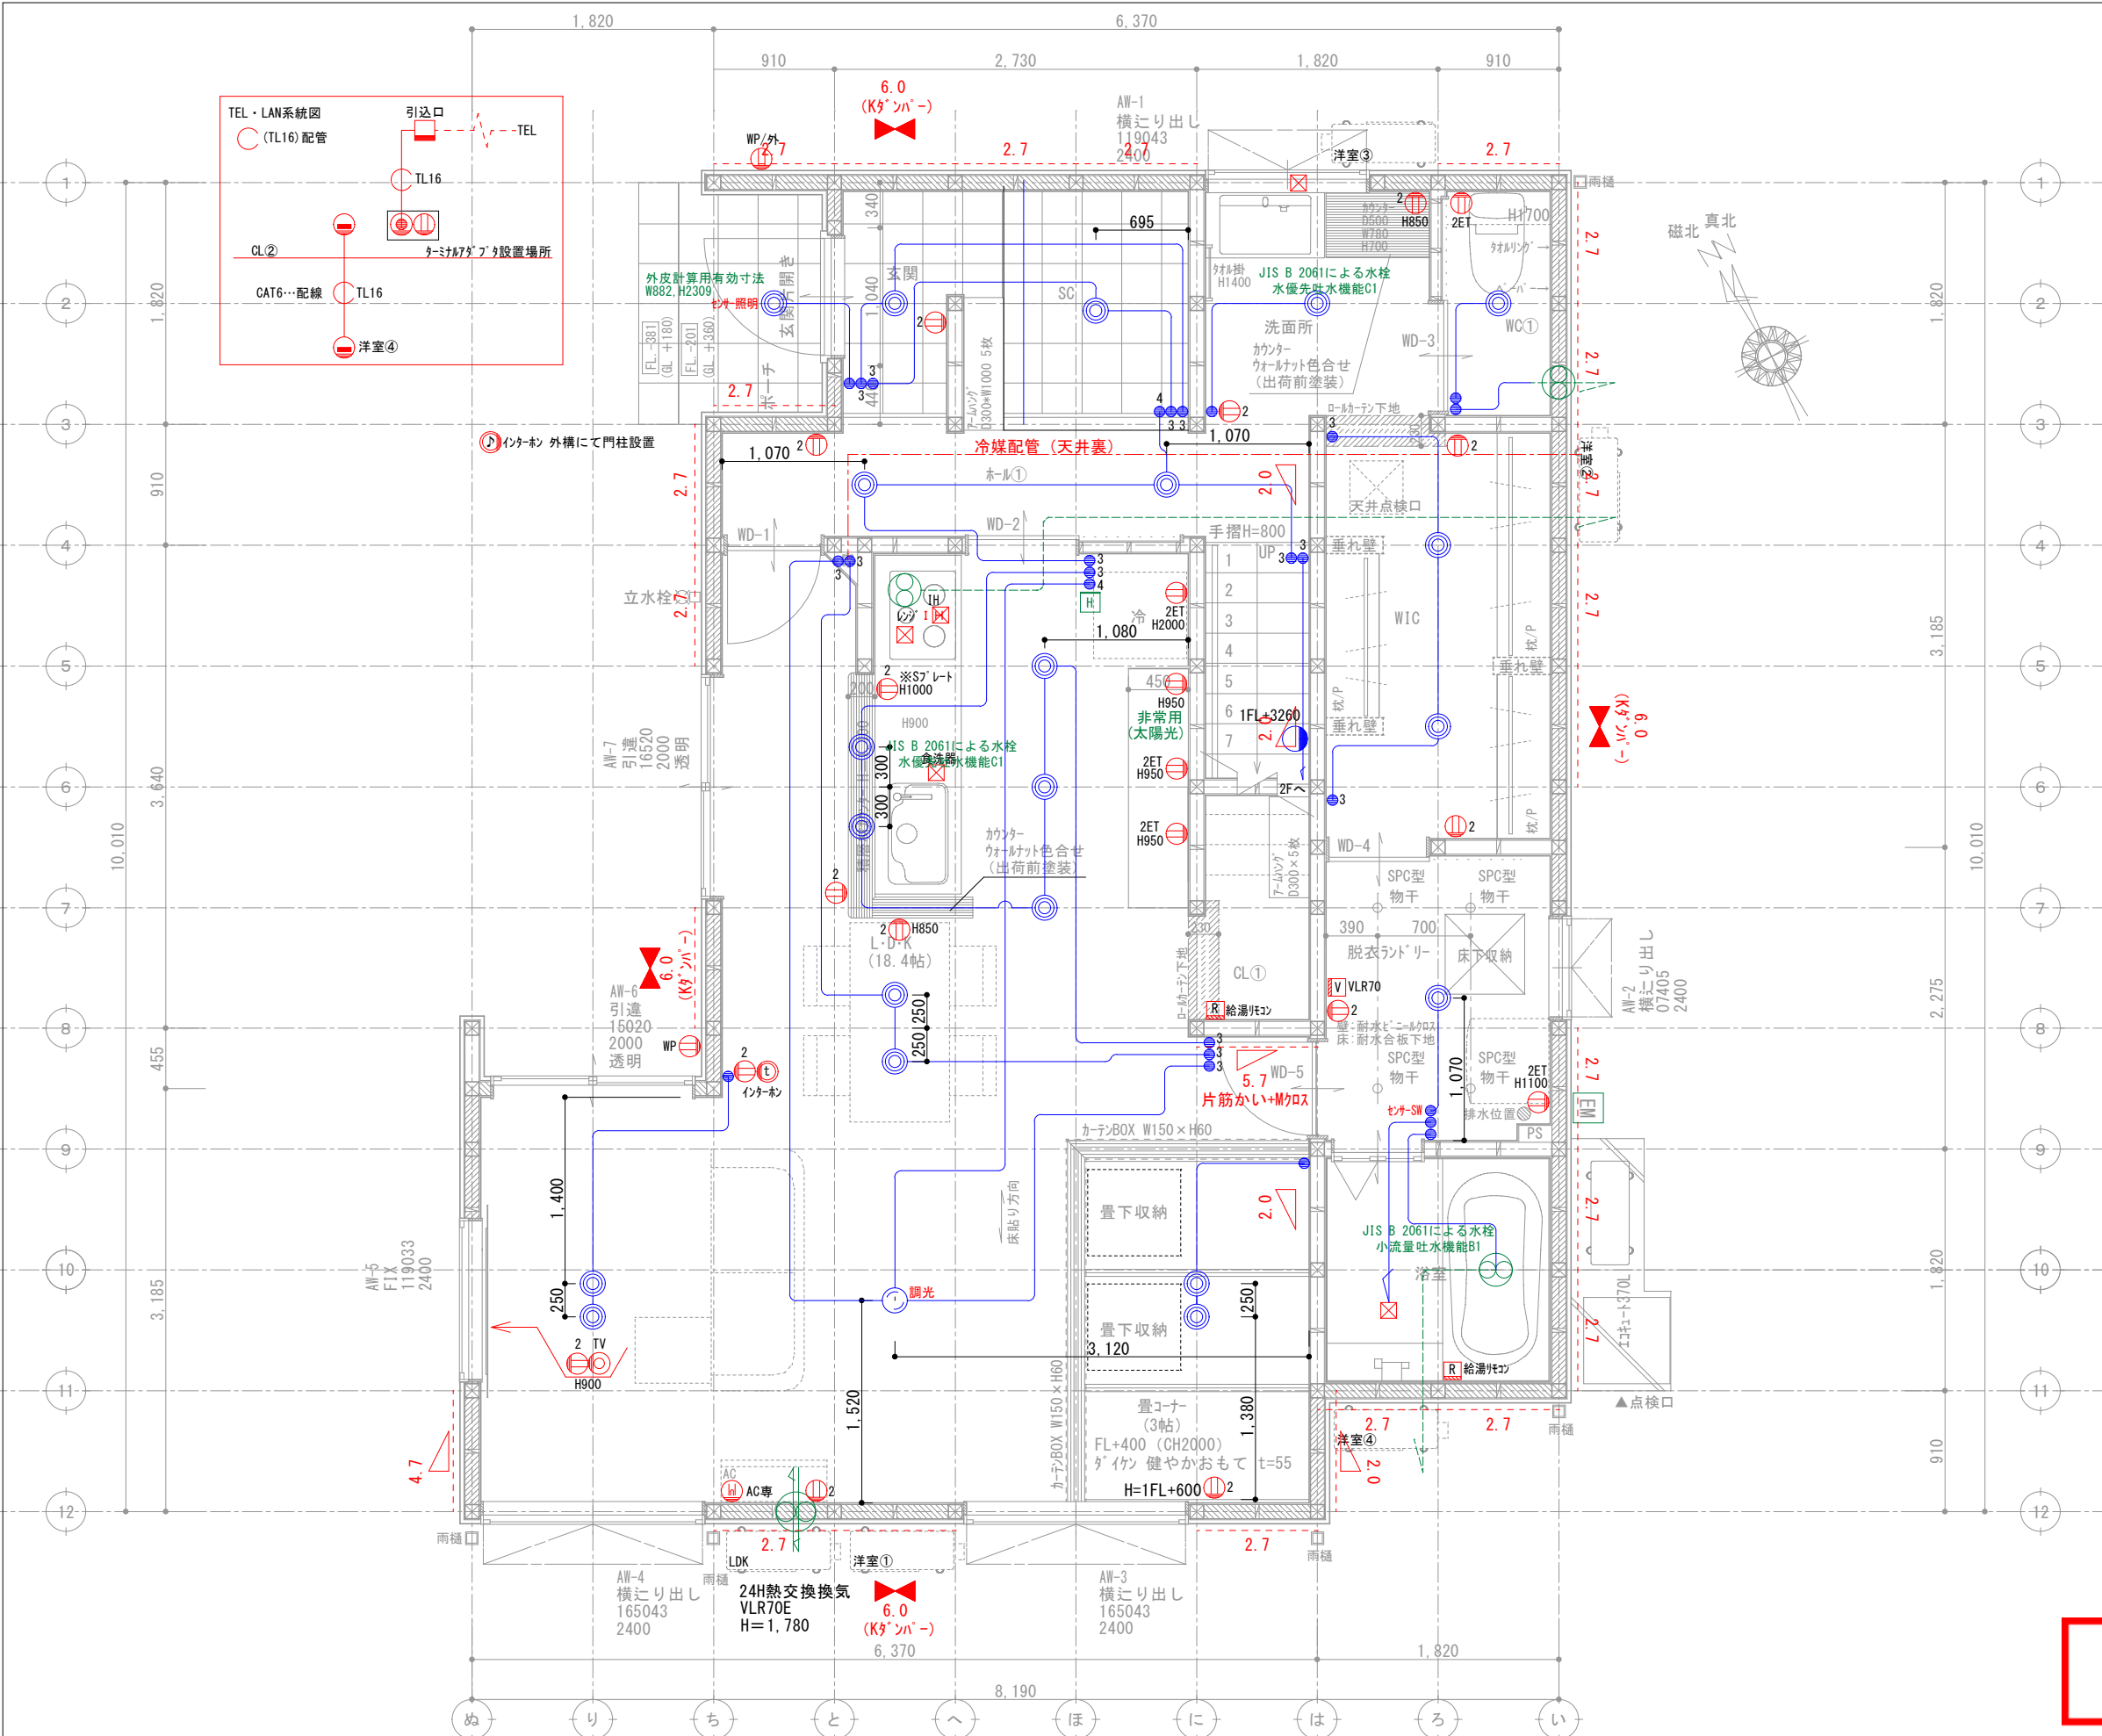

G2

壁付け 住宅用火災報知器			数量
H 熱感知	熱感知器	電池式(単独型)	1
		露出型	
壁付け 住宅用火災報知器			数量
S 煙感知	煙感知器	電池式(単独型)	
		露出型	

※ 煙感知器は壁・梁より600mm以上離す
壁に取付ける場合、
天井から150mm以上500mm以内離す
換気扇・エアコン吹出口から1500mm以上離す
※ 全室LED照明とする。
※ 標準天井高さ2,400
※ 特記無きガラスは型ガラス

* 凡例

管柱 (105×105)

Kダクト (3.30倍 FRM-0641)

片筋違い (2.00倍 45×90)
(例 左:柱脚 右:柱頭)

たすき掛筋違い (4.00倍 45×90)

構造用合板 (2.70倍)
(t=9 材質:EXハイバ)

床点検口

天井点検口

換気扇

熱交換換気扇VLR-70

※ 全室LED照明とし、調光制御を採用する。
※ 非居室の照明は人感センサーを採用する。

アドバンスシリーズ		
スマートデザイン (外部)		
凡例	1	コンセント 1ヶ所
2	コンセント 2ヶ所	
3	コンセント 3ヶ所	
1ET	コンセント1ヶ所接地ターミナル付	
2ET	コンセント2ヶ所接地ターミナル付	
WP	コンセント 防水型	
エ	エアコン用コンセント	
200V	200V用コンセント	
WP	防雨入線プレート	
スイッチ	スイッチ	
3	3路スイッチ	
4	4路スイッチ	
直結電源	直結電源	
TV	テレビ取出口	
TEL	電話取出口 (テレホンガイド)	
LAN	LAN取出口 (テレホンガイド)	
壁照明	壁照明	
リモコン	リモコン(給湯関係・ルフロ)	
メーター	メーター	
分電盤	分電盤	
チャイム	チャイム	

※ACコンセント天井付け
※スイッチはFL+1100、コンセントはFL+200

決定図

G2

壁付け 住宅用火災報知器			数量
H 熱感知	電池式(単独型)		
	露出型		
壁付け 住宅用火災報知器			数量
S 煙感知	電池式(単独型)		4
	露出型		

- ※ 煙感知器は壁・梁より600mm以上離す
壁に取付ける場合、
天井から150mm以上500mm以内離す
換気扇・エアコン吹出口から1500mm以上離す
- ※ 全室LED照明とする。
- ※ 標準天井高さ2,400
- ※ 特記無きガラスは型ガラス

* 凡例

- ☒ 管柱 (105×105)
- ◀▶ Kダクト (3.30倍 FRM-0641)
- △ 片筋違い (2.00倍 45×90)
(例 左:柱脚 右:柱頭)
- ◻ たすき掛筋違い (4.00倍 45×90)
- 構造用合板 (2.70倍)
(t=9 3枚 -EXハイパー)
- ◻ 床点検口
- ◻ 天井点検口
- ↻ 換気扇
- ↻ 熱交換換気扇VLR-70


- ※ 全室LED照明とし、調光制御を採用する。
- ※ 非居室の照明は人感センサーを採用する。

アドバンスシリーズ		
スマートデザイン (外部)		
凡例		
1	コンセント	1ヶ所
2	コンセント	2ヶ所
3	コンセント	3ヶ所
1ET	コンセント1ヶ所接地ターミナル付	
2ET	コンセント2ヶ所接地ターミナル付	
WP	コンセント 防水型	
	エアコン用コンセント	
	200V用コンセント	
WP	防雨入線プレート	
	スイッチ	
3	3路スイッチ	
4	4路スイッチ	
	直結電源	
TV	テレビ取出口	
TEL	電話取出口 (テレホンガイド)	
LAN	LAN取出口 (テレホンガイド)	
	壁照明	
R	リモコン (給湯関係・ルフロ)	
WH	メーター	
t	分電盤	
	チャイム	

- ※ACコンセント天井付け
- ※TVアンテナ工事
- ※スイッチはFL+1100、コンセントはFL+200

決定図



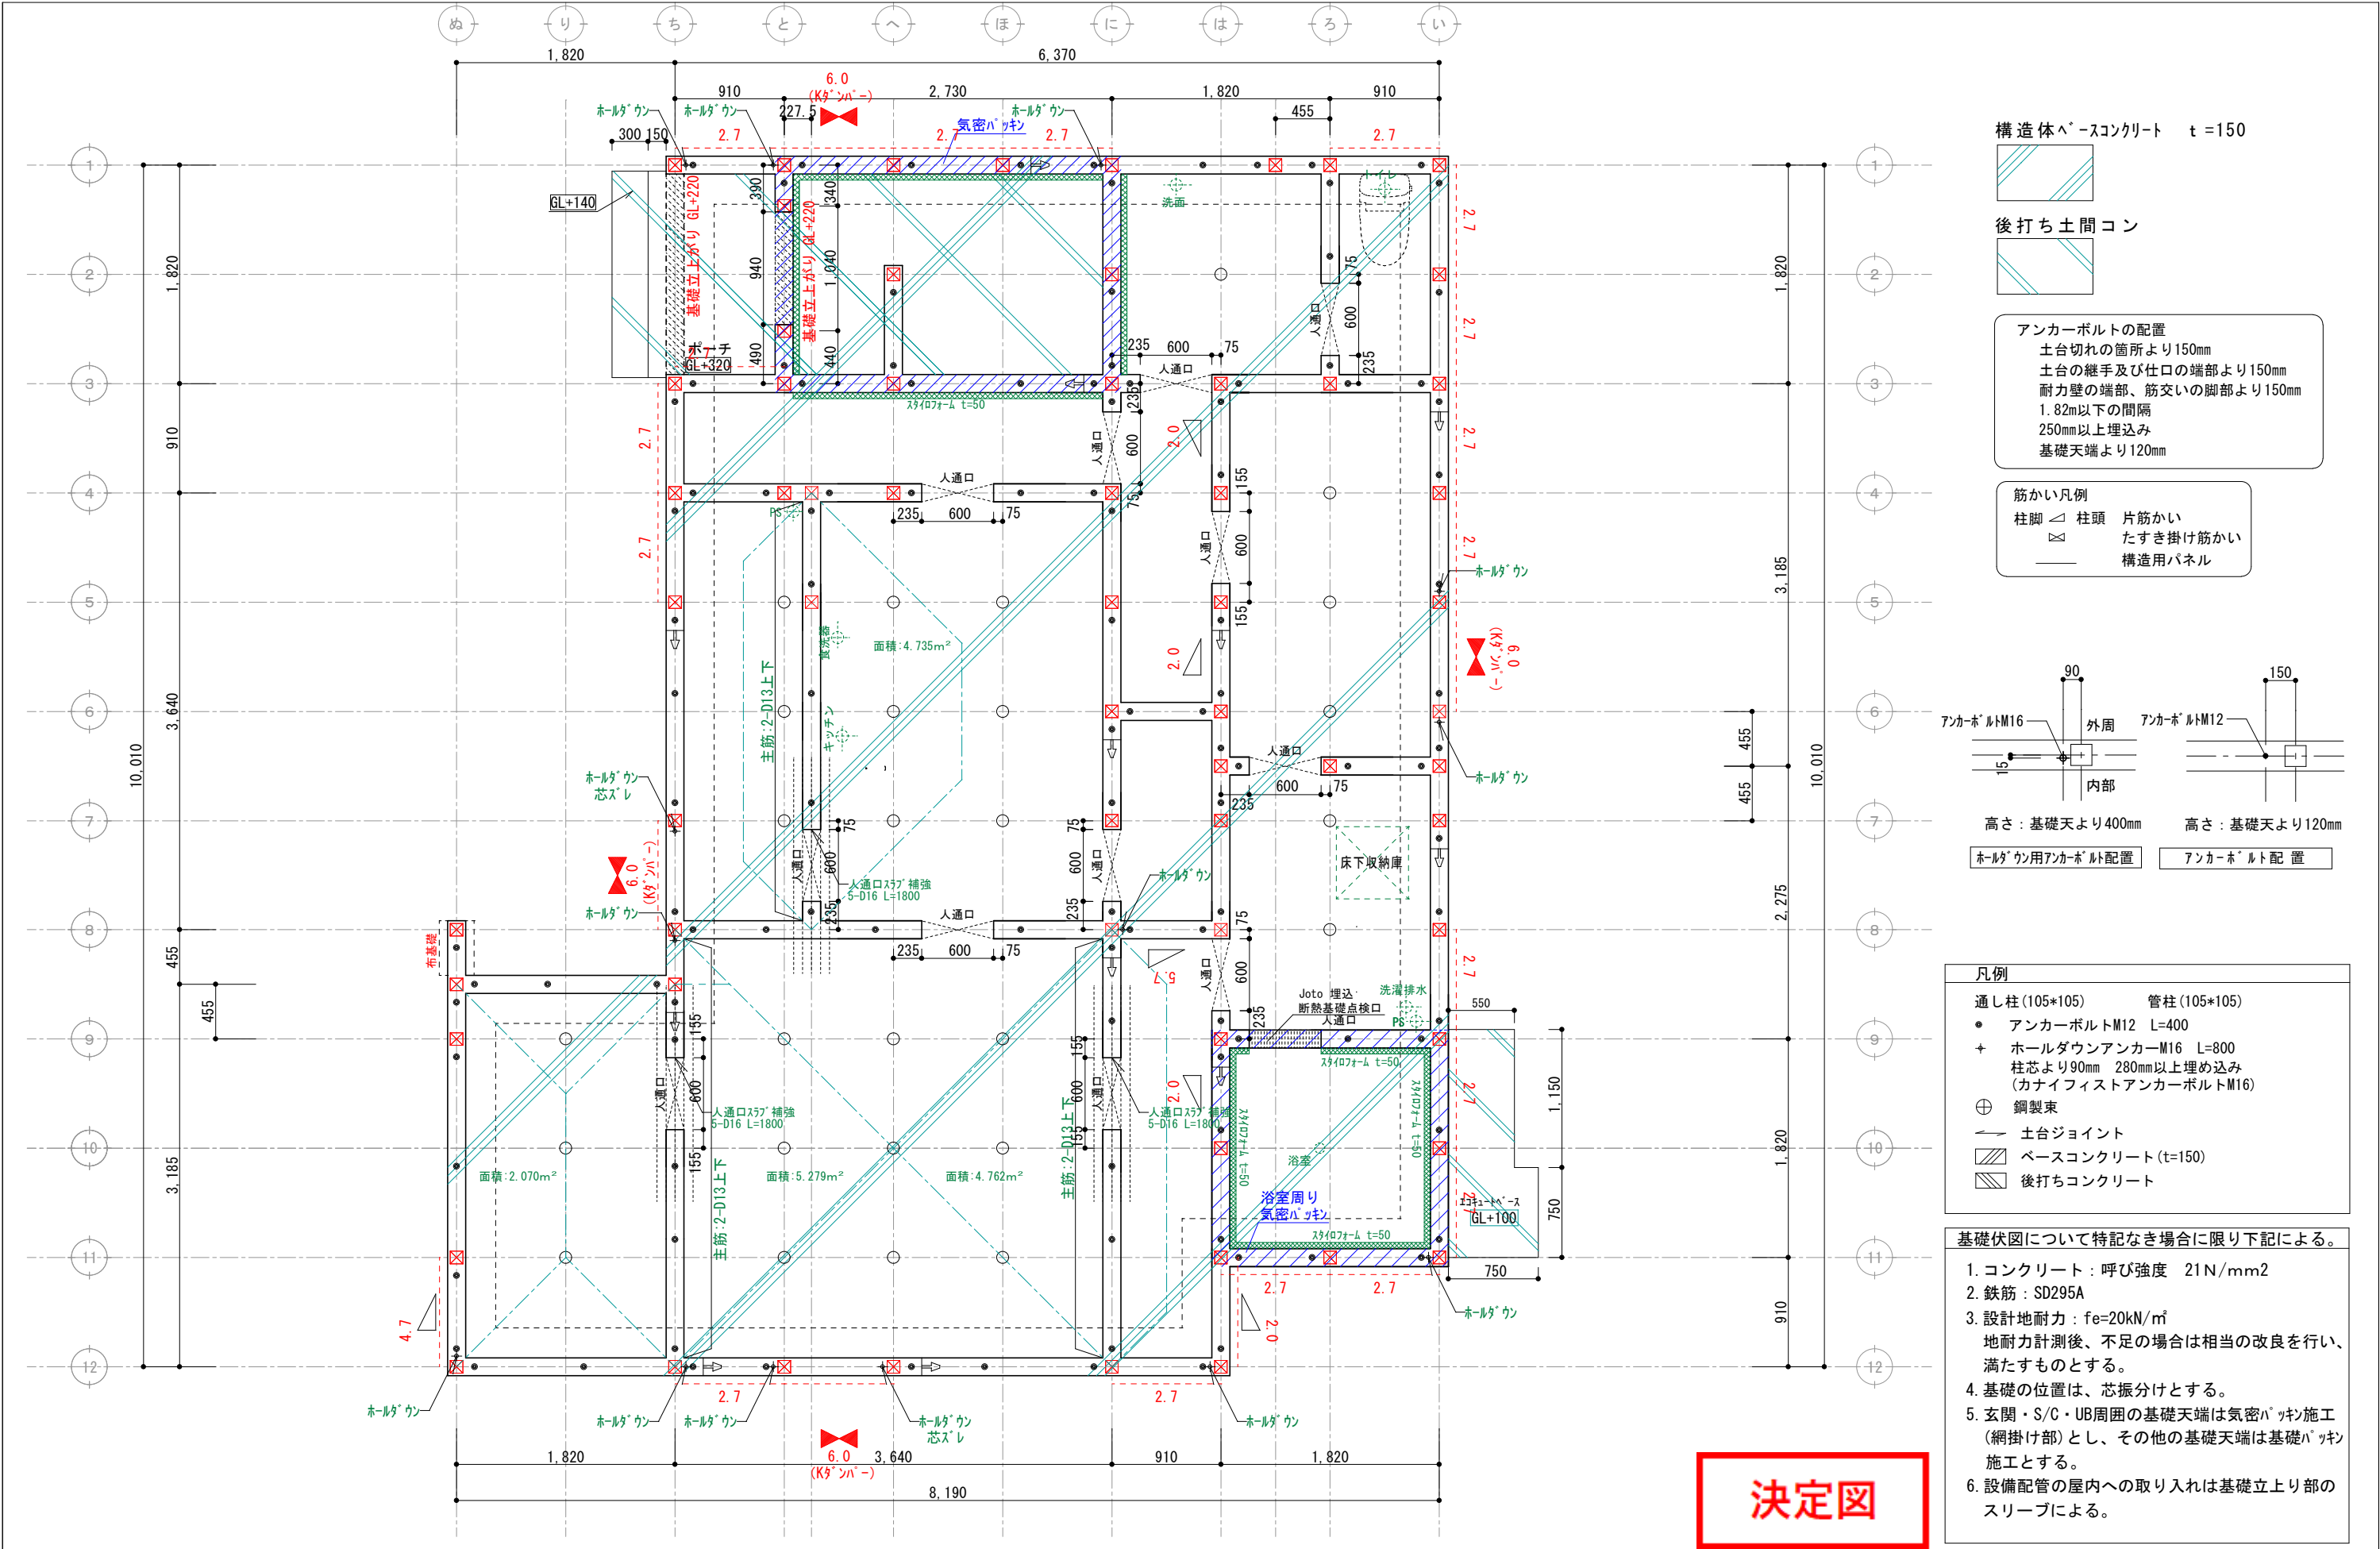


構造体ベースコンクリート t=150

後打ち土間コン

- アンカーボルトの配置
- 土台切れの箇所より150mm
 - 土台の継手及び仕口の端部より150mm
 - 耐力壁の端部、筋交いの脚部より150mm
 - 1.82m以下の間隔
 - 250mm以上埋込み
 - 基礎天端より120mm

- 筋かい凡例
- 柱脚 柱頭 片筋かい
 - たすき掛け筋かい
 - 構造用パネル

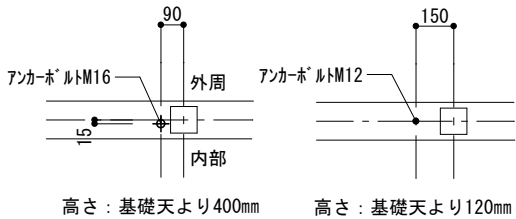

高さ：基礎天より400mm 高さ：基礎天より120mm

ホールダウン用アンカーボルト配置












アンカーボルト配置


- 凡例
- 通し柱(105*105) 管柱(105*105)
 - アンカーボルトM12 L=400
 - + ホールダウンアンカーM16 L=800
 - 柱芯より90mm 280mm以上埋め込み (カナイフリストアンカーボルトM16)
 - ⊕ 鋼製束
 - 土台ジョイント
 - ベースコンクリート(t=150)
 - 後打ちコンクリート

基礎伏図について特記なき場合に限り下記による。


1. コンクリート：呼び強度 21N/mm2
2. 鉄筋：SD295A
3. 設計地耐力：fe=20kN/m²
地耐力計測後、不足の場合は相当の改良を行い、満たすものとする。
4. 基礎の位置は、芯振分けとする。
5. 玄関・S/C・UB周囲の基礎天端は気密パッキン施工（網掛け部）とし、その他の基礎天端は基礎パッキン施工とする。
6. 設備配管の屋内への取り入れは基礎立上り部のスリーブによる。

決定図

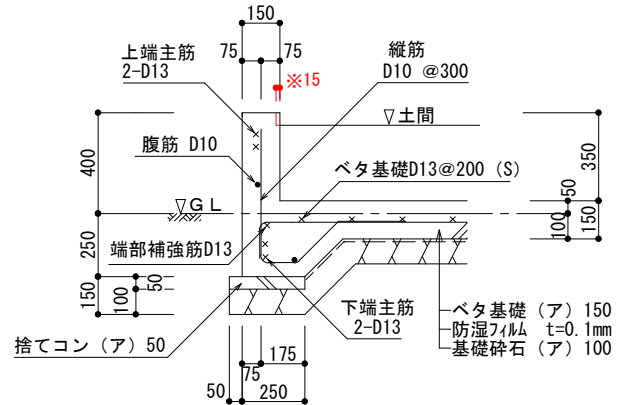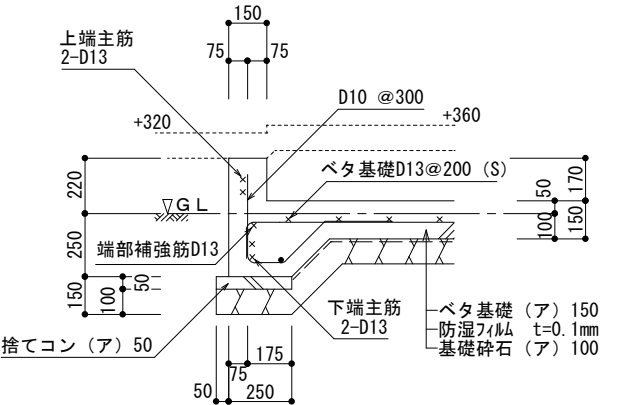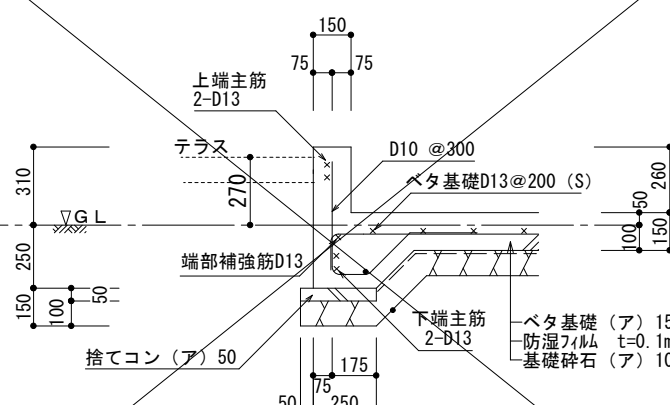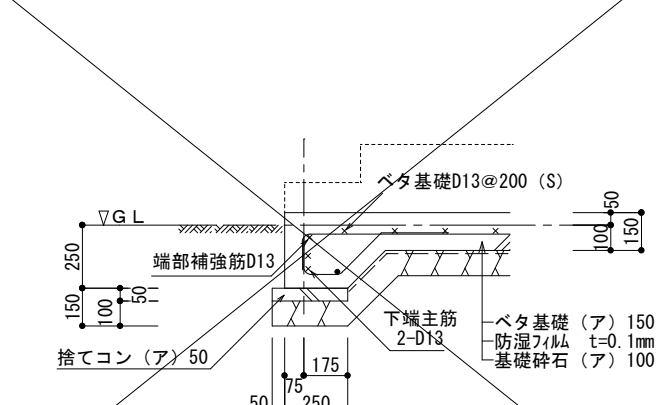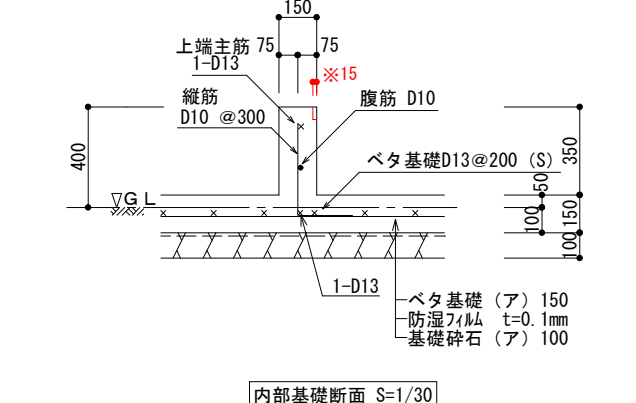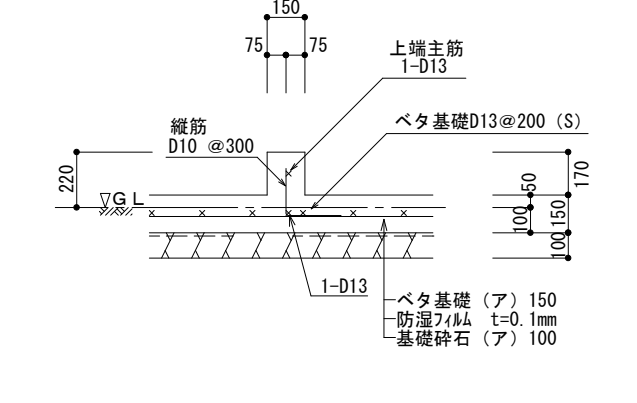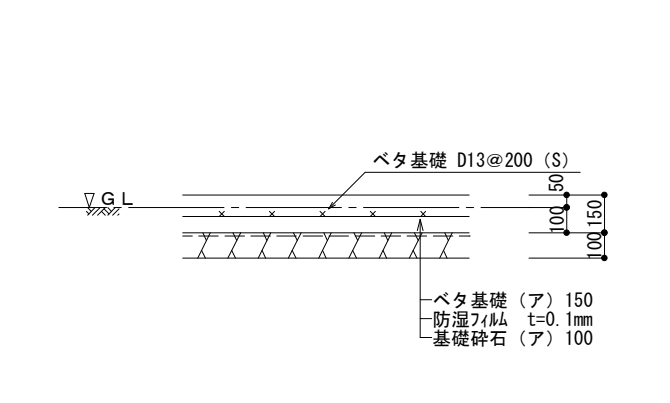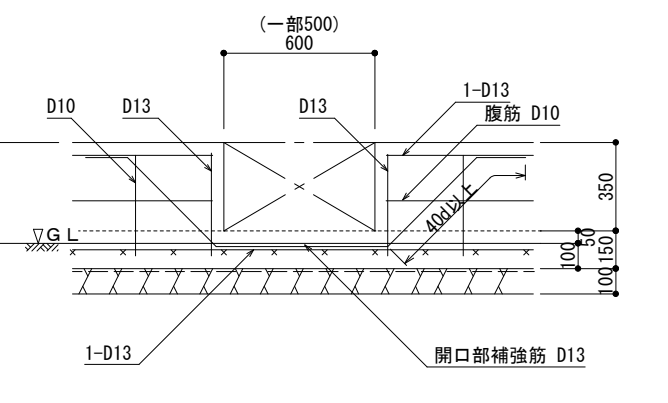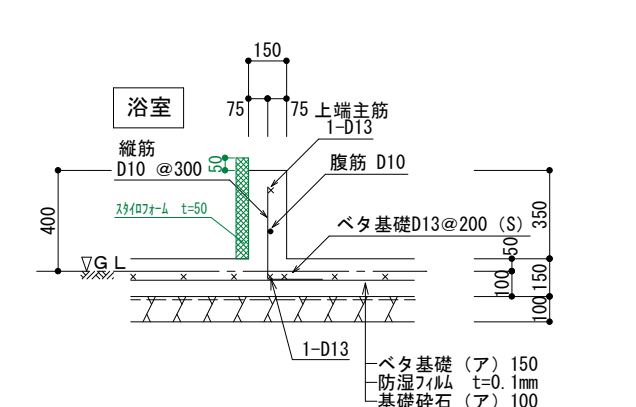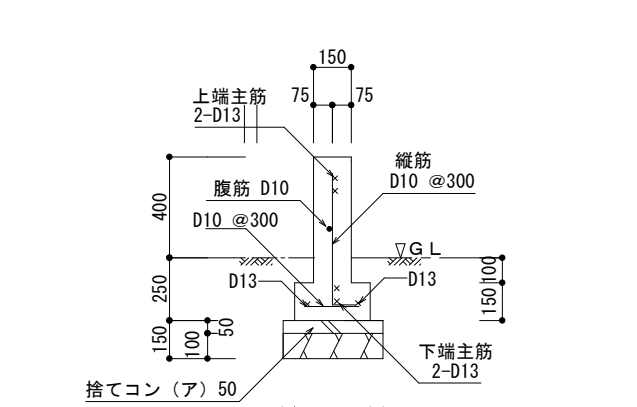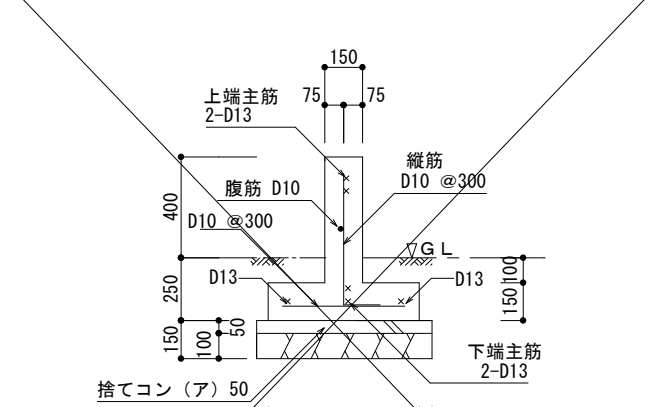 外周基礎断面 S=1/30 ※玄関内土間部分のみ15mm欠き込み	 ポーチ下 外周部基礎断面 S=1/30 倉庫ドア下 外周部基礎断面 S=1/30	 土間納め勝手口ドア下 外周部基礎断面 S=1/30	 ポーチ外周部の基礎断面 S=1/30 立上り無しの基礎断面 S=1/30						
 内部基礎断面 S=1/30 ※玄関内土間部分のみ15mm欠き込み ※注意：基礎伏図に特記のない内部基礎の場合	 ポーチ下 内周部基礎断面 S=1/30 玄関ドア下 内周部基礎断面 S=1/30 玄関＝SC布基礎断面 S=1/30	 ベタ基礎断面 S=1/30	 人通口補強 S=1/30						
 浴室内部基礎断面 S=1/30 ※注意：基礎伏図に特記のない内部基礎の場合	 布基礎A：袖壁用 基礎断面 S=1/30	 布基礎B：応用独立 基礎断面 S=1/30	<table><tr><td>基礎の寸法 及び 配筋の検証方法</td><td>基礎立上り配筋は、 (財)日本住宅・木材技術 センター発行のスパン表 (増補版)による。 ベタ基礎スラブ配筋は、 まもりすまい保険設計施工 基準同解説のベタ基礎配筋表 による。具体的な寸法・配 筋は基礎詳細図参照。</td></tr><tr><td colspan="2">鉄筋断面表記 ●・・・D10を示す。 ×・・・D13を示す。</td></tr><tr><td colspan="2">※使用しない断面は 決定図</td></tr></table>	基礎の寸法 及び 配筋の検証方法	基礎立上り配筋は、 (財)日本住宅・木材技術 センター発行のスパン表 (増補版)による。 ベタ基礎スラブ配筋は、 まもりすまい保険設計施工 基準同解説のベタ基礎配筋表 による。具体的な寸法・配 筋は基礎詳細図参照。	鉄筋断面表記 ●・・・D10を示す。 ×・・・D13を示す。		※使用しない断面は 決定図	
基礎の寸法 及び 配筋の検証方法	基礎立上り配筋は、 (財)日本住宅・木材技術 センター発行のスパン表 (増補版)による。 ベタ基礎スラブ配筋は、 まもりすまい保険設計施工 基準同解説のベタ基礎配筋表 による。具体的な寸法・配 筋は基礎詳細図参照。								
鉄筋断面表記 ●・・・D10を示す。 ×・・・D13を示す。									
※使用しない断面は 決定図									
訂正	浜岡一級総合設計事務所 一級建築士事務所 静岡県知事登録第(10)2441号 一級建築士 大臣登録第 365879 号 西原利昌		株式会社 LIFEFUND InDesign office 一級建築士事務所 事務所登録 (2) 第7595号 一級建築士登録 第179770号 鈴木 達男 〒432-8023 静岡県浜松市中央区鴨江3丁目70番23号	年月日 2025.9.5 縮尺 1/30	件名 清水裕也様・穂菜実様 邸新築工事 図名 基礎断面リスト	設計 酒井	I C	工務 青島	図番 B-2

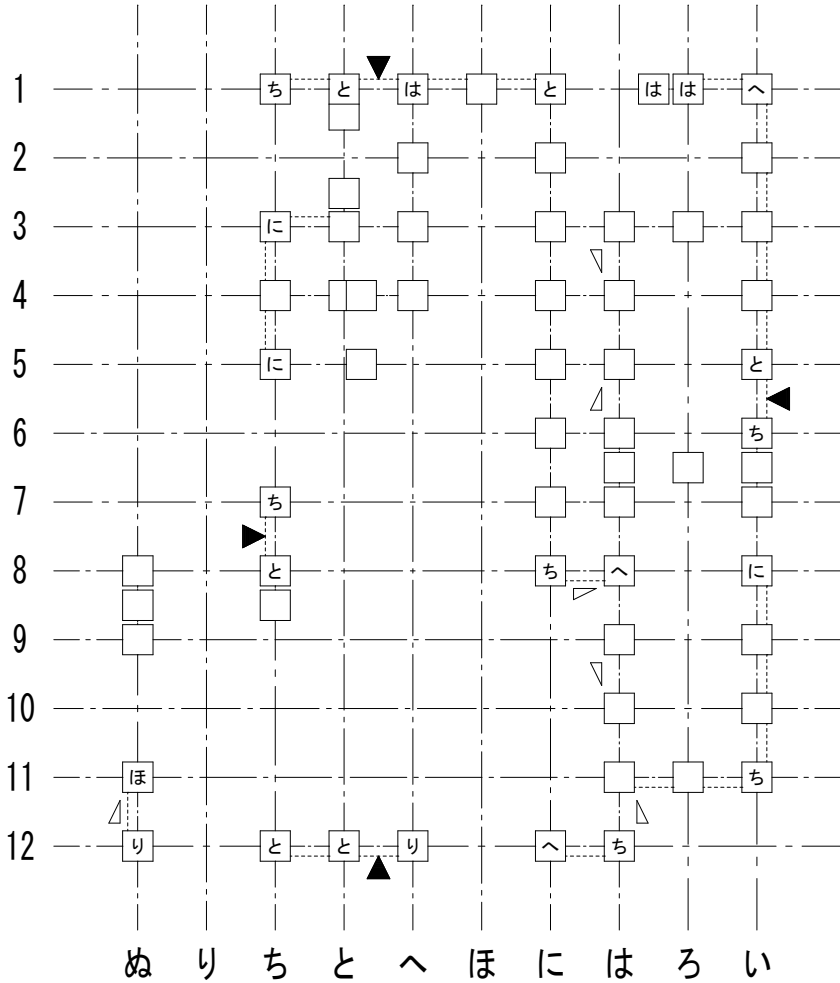

1 階柱壁伏図

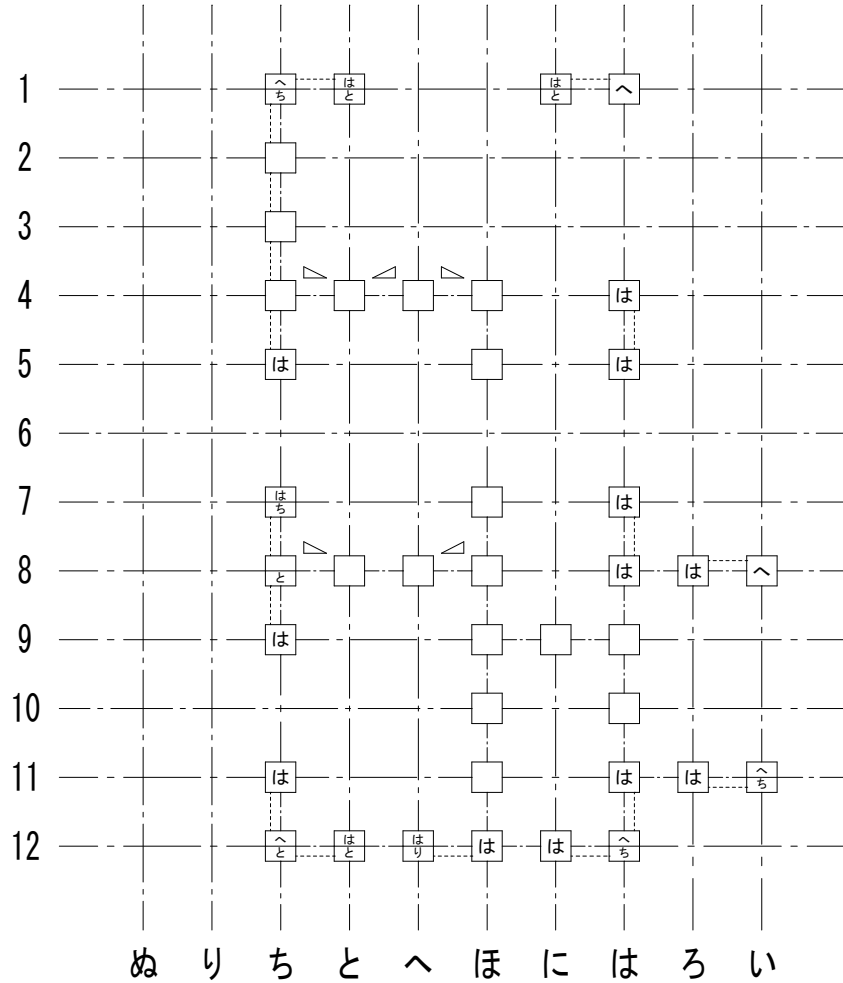

2 階柱壁伏図

接合部凡例		*接合部凡例はユーザ設定されたものです。	
記号	仕様（カナイ金物）	N	倍率
SBCP	スリムビルドコーナー75, チビクリCK(化粧柱の場合)	0.00	1.00
SBCP	スリムビルドコーナー75, チビクリCK(化粧柱の場合)	0.65	1.00
SBCP	は スリムビルドコーナー75	1.00	1.00
ARCG	に アレントコーナー合板用	1.40	2.20
ARCG	ほ アレントコーナー合板用	1.60	2.20
ARCG	へ アレントコーナー合板用	1.80	2.20
HD15	と ブレイブホールダウン B-HD15	2.80	3.60
HD20	ち ブレイブホールダウン B-HD20	3.70	4.70
HD25	り ブレイブホールダウン B-HD25	4.70	4.80
HD30	ぬ ブレイブホールダウン B-HD30	5.60	7.20
J1	る 腰掛け蟻若しくは大入れ蟻掛け+羽子板 [※] ルト, 短冊金物		1.90
J2	を 腰掛け蟻若しくは大入れ蟻掛け+羽子板 [※] ルト, 短冊金物×2		3.00

※表示なき金物は「は」とする。

梁継手・仕口用
梁継手・仕口用

接合部凡例		*接合部凡例はユーザ設定されたものです。	
記号	仕様（タナカ金物）	N	倍率
FCP	フックコーナー, チビクリCK(化粧柱の場合)	0.00	1.00
FCP	フックコーナー, チビクリCK(化粧柱の場合)	0.65	1.00
FCP	は フックコーナー	1.00	1.00
CCP	に シナコーナー	1.40	2.20
CCP	ほ シナコーナー	1.60	2.20
CCP	へ シナコーナー	1.80	2.20
HD15	と ビス止めホールダウンU HD15	2.80	3.60
HD20	ち ビス止めホールダウンU HD20	3.70	4.70
HD25	り ビス止めホールダウンU HD25	4.70	4.80
HD30	ぬ ビス止めホールダウンU HD15×2 (HD35)	5.60	7.20
J1	る 腰掛け蟻若しくは大入れ蟻掛け+羽子板 [※] ルト, 短冊金物		1.90
J2	を 腰掛け蟻若しくは大入れ蟻掛け+羽子板 [※] ルト, 短冊金物×2		3.00

※表示なき金物は「は」とする。

梁継手・仕口用
梁継手・仕口用

筋かいの種類に応じた筋かいの端部の接合部の仕様		
	筋かいの種類	接合部の仕様（構造方法）
イ	鉄筋 φ9	柱又は横架材を貫通し、三角座金を介してナット締め、又は鋼板添え板を用い鋼板を柱及び横架材にCN90, 8本平打ち
ロ	筋かい:15×90	柱・横架材を欠き込み、柱・横架材双方に対してN65, 5本平打ち
ハ	筋かい:30×90	鋼板添え板t=1.6mmを筋かいに対してボルトφ12及びCN65, 3本平打ち、柱に対してCN65, 3本平打ち、横架材に対してCN65, 4本平打ち。筋かいプレートBP同等品
ニ	筋かい:45×90	鋼板添え板t=2.3mmを筋かいに対してボルトφ12及びスクリュー釘φ4.5L50, 7本平打ち、柱及び横架材に対してスクリュー釘φ4.5L50, 5本平打ち。筋かいプレートBP-2同等品
ホ	筋かい:90×90	柱又は横架材にボルトφ12mmを用いて一面剪断接合

胴差と通し柱の接合部の仕様		
	胴差と通し柱の条件	仕口
T1	通し柱の片側に胴差が来る場合	胴差を柱にかたぎ大入れ短ほぞ差しの上、羽子板ボルト、かね折り金物又は同等以上の仕口
T2	通し柱の両側に胴差が来る場合	胴差を柱にかたぎ大入れ短ほぞ差しの上、短冊金物又は、同等以上の仕口で胴差相互を緊結
T3	通し柱と胴差の接合部の近くに90×90以上の筋かいが来る場合(通し柱が建物の出隅にあるか、筋かい壁が外壁と直交して接する場合)	胴差を通し柱に、15KN用引き寄せ金物を水平に用いて緊結

決定図

アクセントクロス 指示書

G2

壁付け 住宅用火災報知器	数量
[H] 熱感知器	電池式(単独型) 1
壁付け 住宅用火災報知器	数量
[S] 煙感知器	電池式(単独型) 1

- ※ 煙感知器は壁・梁より600mm以上離す壁に取付ける場合、天井から150mm以上500mm以内離す換気扇・770吹出口から1500mm以上離す
- ※ 全室LED照明とする。
- ※ 標準天井高さ2,400
- ※ 特記無きガラスは型ガラス

* 凡例


- ☒ 管柱 (105×105)
- ◀▶ K'ン' (3.30倍 FRM-0641)
- △ 片筋違い (2.00倍 45×90) (例 左:柱脚 右:柱頭)
- ⊠ たすき掛筋違い (4.00倍 45×90)
- 構造用合板 (2.70倍) (t=9 945-EXN(N)-)
- 床点検口
- ⊠ 天井点検口
- ⊕ 換気扇
- ⊕ 熱交換換気扇VLR-70

- ※ 全室LED照明とし、調光制御を採用する。
- ※ 非居室の照明は人感センサーを採用する。

- ※ 階段寸法
蹴上: 207.14 (2900÷14段)
踏面: 227.5
有効幅: 780
手摺出幅100mm以下

決定図

アクセントクロス範囲→
シンコール: BA7237

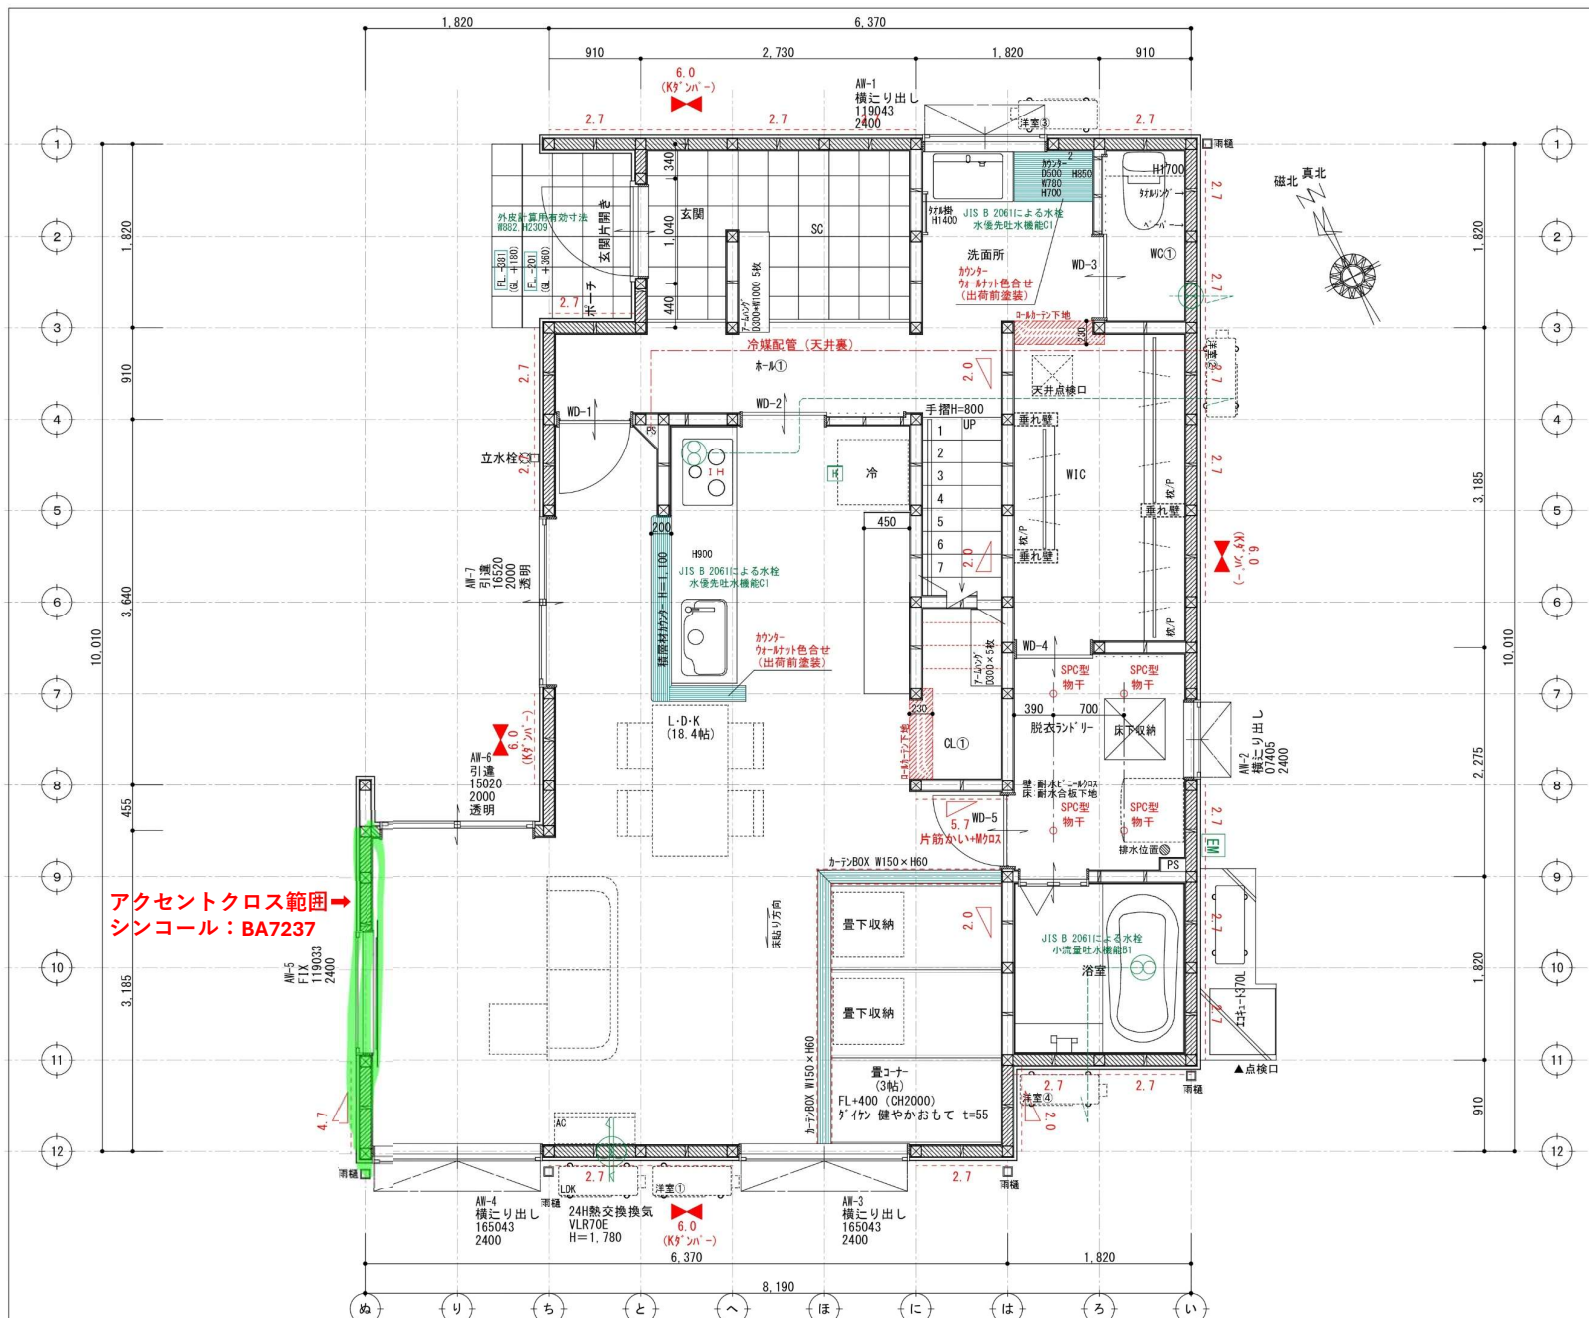

訂正

浜岡一級総合設計事務所
一級建築士事務所 静岡県知事登録第 (10)2441 号
一級建築士 大田登輝 365679 号 西澤利昌

PG HOUSE

株式会社 LIFEFUND InDesign office 一級建築士事務所
事務所登録 (2)第7595号 一級建築士登録 第179770号 鈴木 達男
〒432-8023 静岡県浜松市中央区鶴江3丁目70番23号

年月日
2025.9.5
前尺
1/50

件名 清水裕也様・穂菜実様邸 新築工事
図名 1階平面図

設計	IC	工事	図番
酒井		青島	3-1