


アクセントクロス 指示書

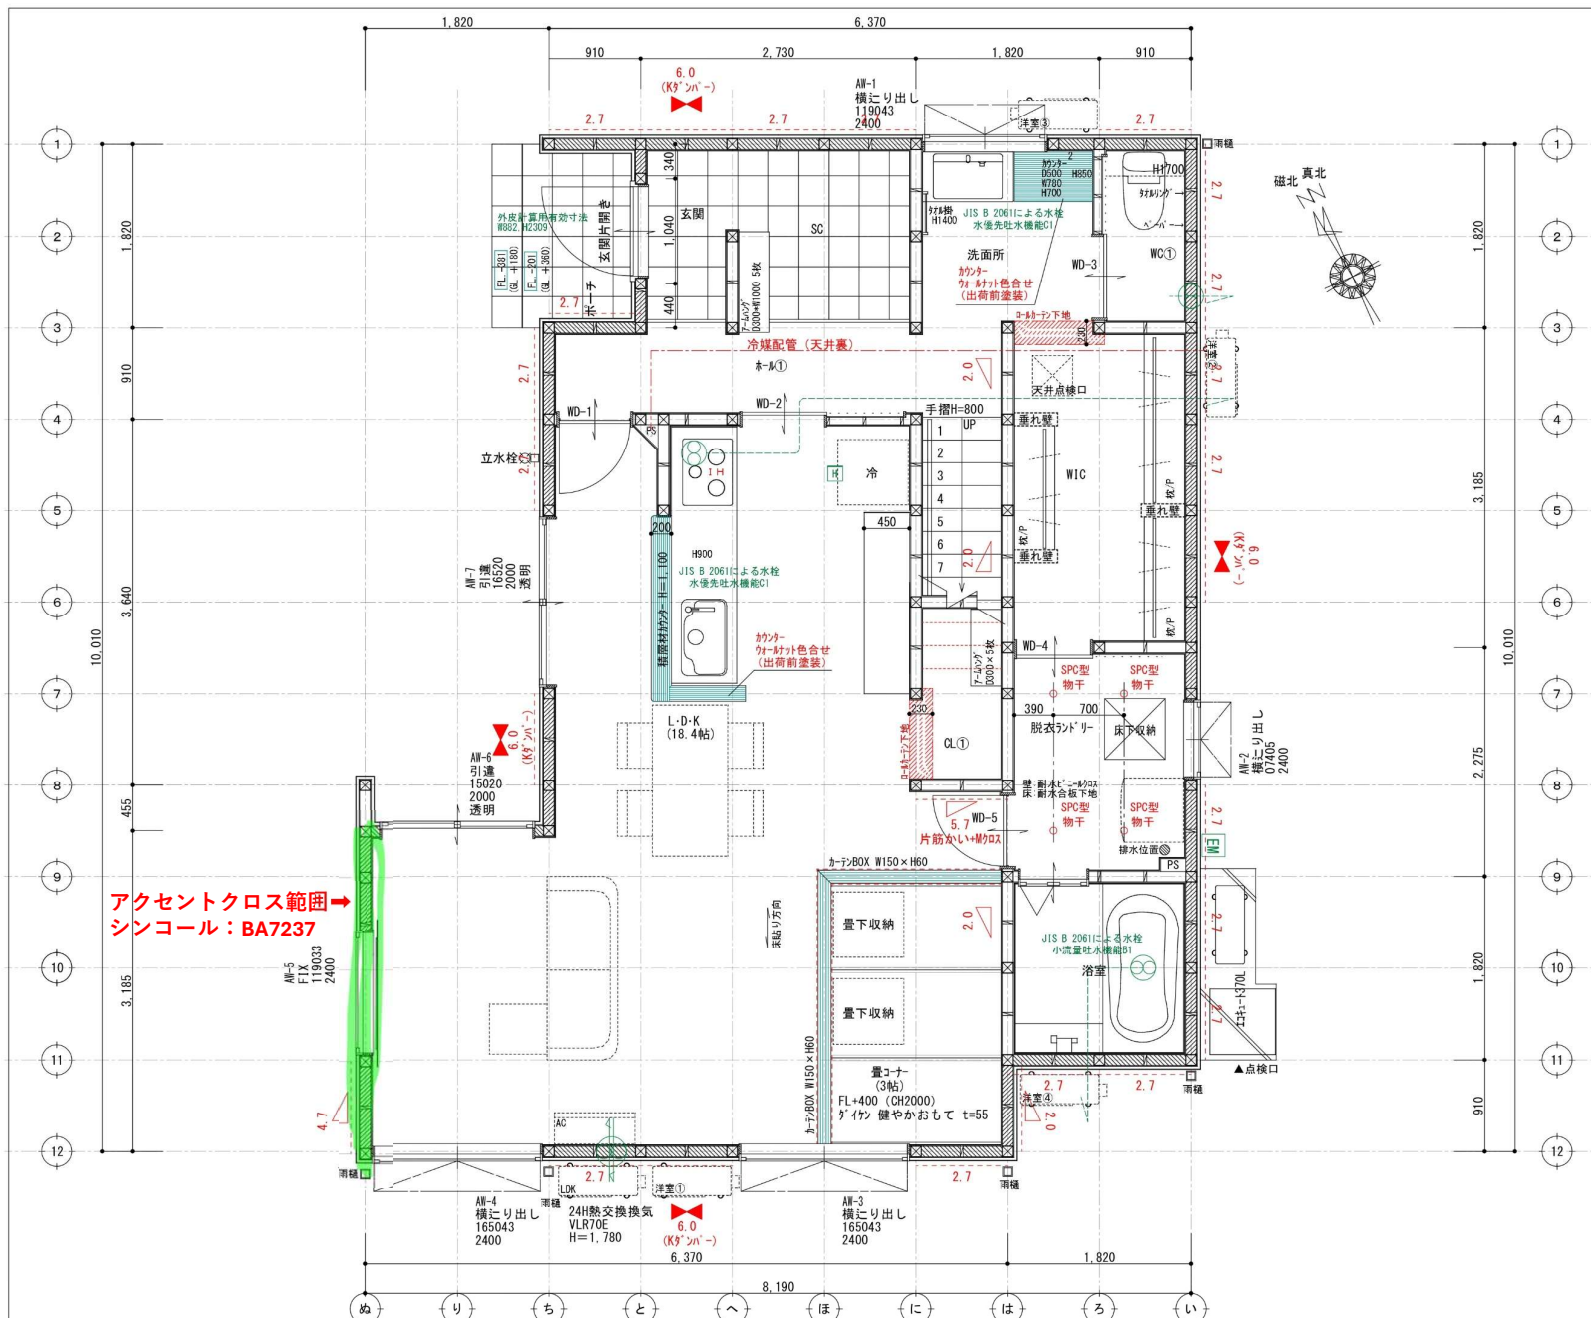

G2

壁付け 住宅用火災警報器	数量
[H] 熱感知器	電池式(単独型) 1
壁付け 住宅用火災警報器	数量
[S] 煙感知器	電池式(単独型) 1

- ※ 煙感知器は壁・梁より600mm以上離す壁に取付ける場合、天井から150mm以上500mm以内離す換気扇・770吹出口から1500mm以上離す
- ※ 全室LED照明とする。
- ※ 標準天井高さ2,400
- ※ 特記無きガラスは型ガラス

* 凡例

- 管柱 (105×105)
- K'ン' (3.30倍 FRM-0641)
- 片筋違い (2.00倍 45×90) (例 左:柱脚 右:柱頭)
- たすき掛筋違い (4.00倍 45×90)
- 構造用合板 (2.70倍) (t=9 945-EXN(N)-)
- 床点検口
- 天井点検口
- 換気扇
- 熱交換換気扇VLR-70

- ※ 全室LED照明とし、調光制御を採用する。
- ※ 非居室の照明は人感センサーを採用する。
- ※ 階段寸法
蹴上: 207.14 (2900÷14段)
踏面: 227.5
有効幅: 780
手摺出幅100mm以下

決定図

訂正	浜岡一級総合設計事務所 一級建築士事務所 静岡県知事登録第 (10)2441 号 一級建築士 大田登輝 365679 号 西澤利昌	PG HOUSE	株式会社 LIFEFUND InDesign office 一級建築士事務所 事務所登録 (2)第7595号 一級建築士登録 第179770号 鈴木 達男 〒432-8023 静岡県浜松市中央区鶴江3丁目70番23号	年月日 2025.9.5 前尺 1/50	件名 清水裕也様・穂菜実様邸 新築工事 図名 1階平面図	設計 酒井	IC	工事 青島	図番 3-1
----	---	----------	--	-------------------------------	---------------------------------------	----------	----	----------	-----------