




面

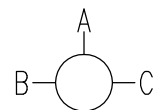

A面

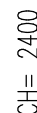

C面

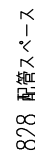[illegible]


【 ご注意 】

- 壁面仕上材（キッチンパネル・タイルなど）の貼付下端位置が変わります。 [機能図参照]
- 記載のキャビネット寸法は扉前面での呼び寸法です。キャビネット本体の寸法・扉厚み等は商品ガイドの巻末資料をご確認ください。
- 記載のワークトップ、カウンター、エンドパネル、サイドパネルの寸法は呼び寸法です。詳細寸法は商品ガイドの巻末資料をご確認ください。
- レンジフード電源プラグ仕様：3芯電源プラグ（アース工が必要です。）

特記事項
扉色 WL2:ホワイトスタッコ
取手 [R]スリム取手R(シャインニッケル)
ワークトップカラー 【DW】ソルティホワイト

物件名	中村悦久・裕子 様邸
仕様	ND23

案件No.	図面名	担当	図面	図番 : 株式会社 LIXIL
A2509DDDD0EUWCN	レイアウト図	栗野 友仁		
見積No.	縮尺	日付		
M25098825370-010-2	1/30	2025.12.22		

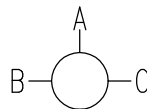

【ご注意】

- 壁面仕上材（キッチンパネル・タイルなど）の貼付下端位置が変わります。〔機能図参照〕
- 記載のキャビネット寸法は扉前面までの呼び寸法です。キャビネット本体の寸法・扉厚み等は商品ガイドの巻末資料をご確認ください。
- 記載のワークトップ、カウンター、エンドパネル、サイドパネルの寸法は呼び寸法です。詳細寸法は商品ガイドの巻末資料をご確認ください。
- 電気・ガス・給排水・換気等は法令・規定に従って有資格者が行ってください。
- 水道工事は排水配管工事となります。
- 取付・設置に際し、各製品の取付・設置説明書や図面の機能図を必ずお読み下さい。
- 内線規程上、各機器のプラグ仕様に関わらず建築側には接地極付コンセントを推奨しています。
- レンジフード電源プラグ仕様：3芯電源プラグ（アース工事が必要です。）
- 食洗機内配管の詳細については必ず別添の機能図をご確認ください。

A3 20251222NCVX-01


A面

注1) 250V・15A 2極接地極付コンセント【専用】(側板取付)

注2) 125V・15A 2極接地極付コンセント (側板取付)

注3) 250V・30A 2極接地極付コンセント 【専用】

注4) レンジフード総高さ(600~900)の時 ダクトカバー範囲(25~325)


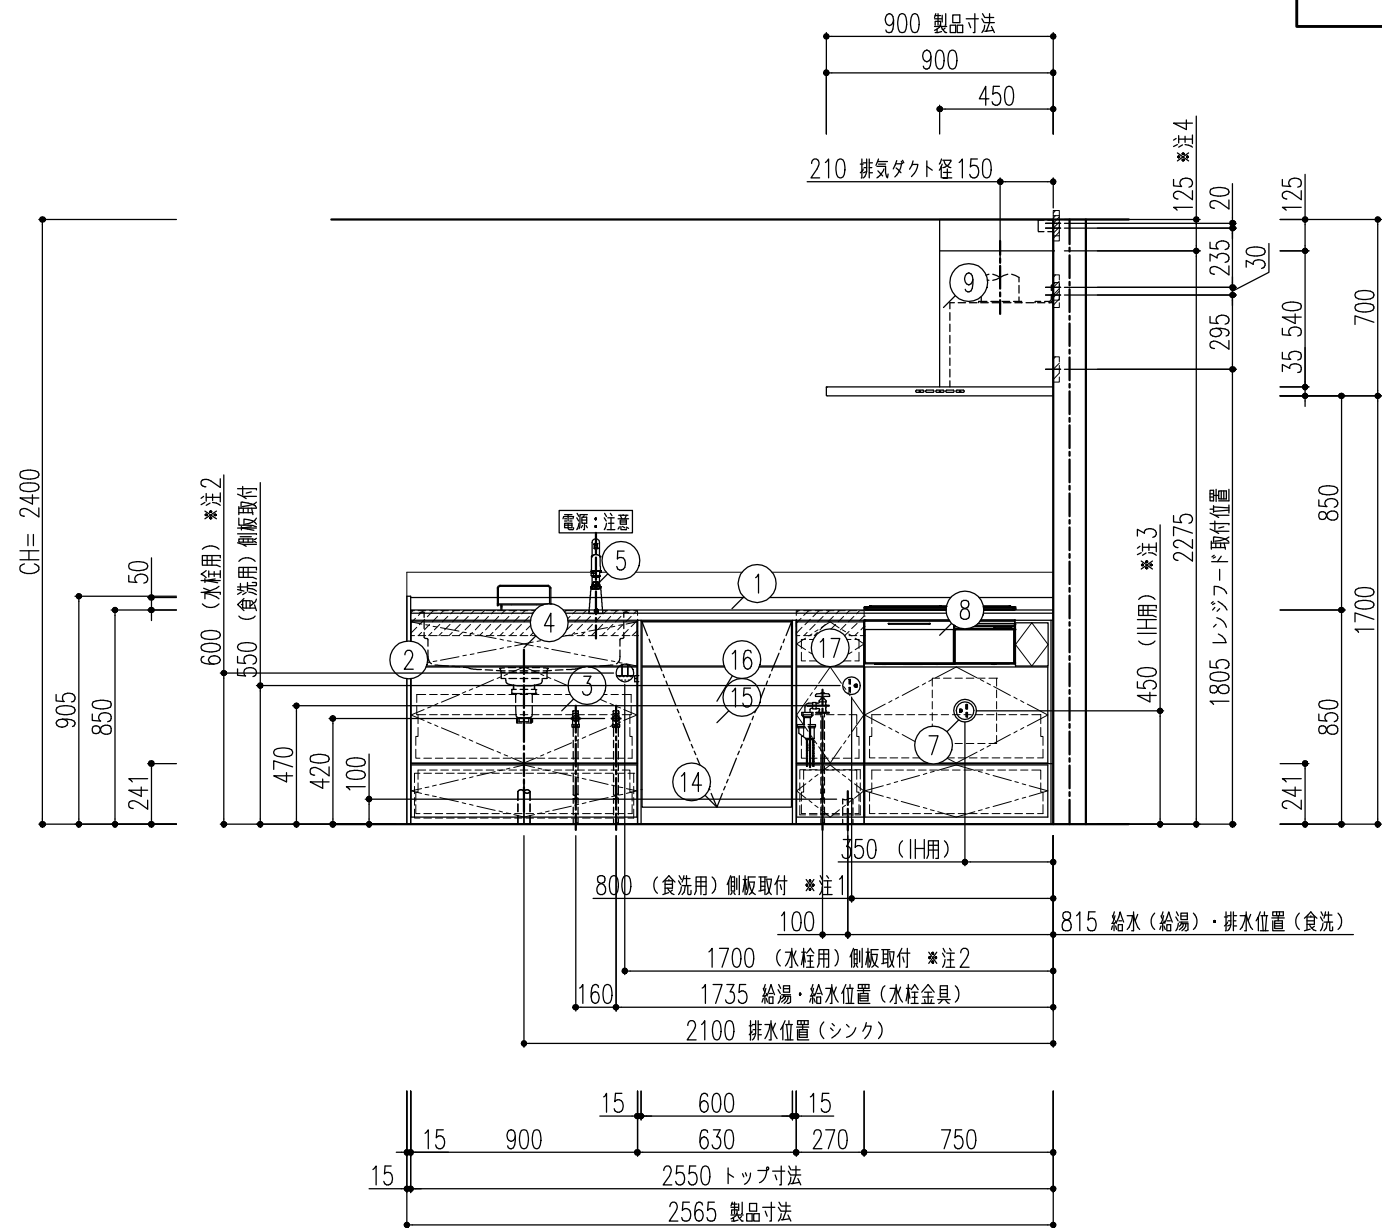


特記事項 扉色 WL2:ホワイトスタック 取手 [R]スリム取手R (シャインニッケル) ワークトップカラー 【DW】ソルティホワイト	物件名	中村悦久・裕子 様邸	案件No.	図面名	担当	図面	図番
	仕様	ND23	A2509DDDD0EUWCN	納まり図	栗野 友仁		株式会社 LIXIL
			見積No.	縮尺	日付		
			M25098825370-010-2	1/30	2025.12.22		

B面

C面

注5) 125V・15A 2極接地極付アースターミナル付コンセント 【専用】（フード用）

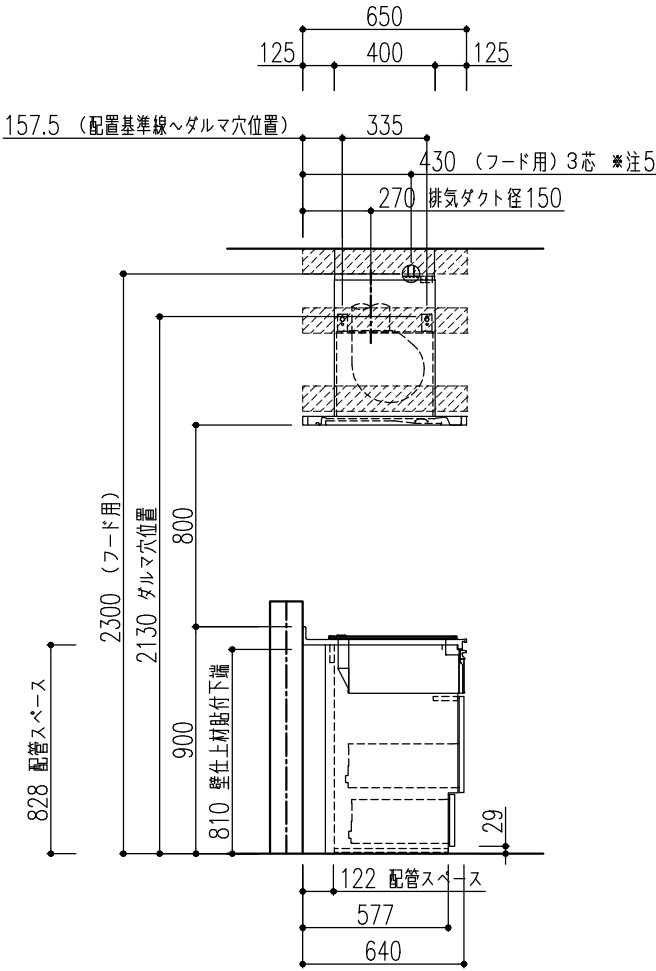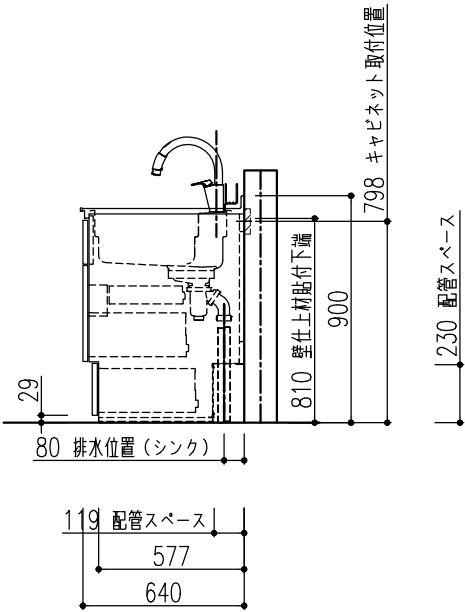

特記事項 扉色 WL2:ホワイトスタック 取手 [R]スリム取手R (シャインニッケル) ワークトップカラー 【DW】ソルティホワイト	物件名	中村悦久・裕子 様邸	案件No.	図面名	担当	図面	図番
	仕様	ND23	A2509DDD0EUWCN	納まり図	栗野 友仁		株式会社 LIXIL
			見積No.	縮尺	日付		
			M25098825370-010-2	1/30	2025.12.22		

■壁面仕上材（キッチンパネル、タイルなど）取付注意事項〔貼付下端位置〕

●キッチンパネルの貼付下端位置

キッチンパネルの貼付下端位置にご注意ください。

キッチンパネル

壁

810mm

(キッチンパネル貼付下端位置)

ワークトップ高さ：850mm以外の場合は、
下表を参照してください。

ワークトップ高さ	キッチンパネル貼付下端位置
900	860
875	835
825	785
800	760

●上表はキッチンパネルの場合です。ステンレスパネルの場合は、キッチンパネルの「取付・設置説明書」を参照してください。

《ワークトップ高さ：850mmの場合》

■壁面仕上材（キッチンパネル）取付注意事項〔貼付向き〕

●キッチンパネルの貼付向き

キッチンパネルの貼付向きにご注意ください。

【単位：mm】

レンジフード

ウォールキャビ（開き扉）

クイックポケット
クイックパレット

横貼り

縦貼り

フロアキャビ

700
(ウォールキャビ
レンジフード高さ)

800
(壁面寸法)

850
(ワークトップ高)

620
(クイックポケット・
パレット用キャビ高さ)

880
(壁面寸法)

850
(ワークトップ高)

《バックガード：なし、ワークトップ高さ：850mm、ウォールキャビ高さ：700mmの場合》

《キッチンパネル 貼付方向》
総高さ：2350mmの場合

	ウォールキャビ		
	開き扉	クイックポケット クイックパレット	
	H700	H600 H500	H700 (620) H600 (520)
キッチンパネル 貼付方向	横	縦	

【ご注意】
リシェ尔以外のクイックパレットは、
キャビネットの背板高さがショート
（－80mm）しておりませんので、
『開き扉』のキッチンパネル貼付方向
に合せてください。

■パナソニック製フロントオープン食洗機 給排水・コンセント取付注意事項

【床立上げ】
・止水栓はアングル式が必要となります。

排水ホース
L=1.8m

100

臭気止めパッキン
本体同梱品

排水管
HT40相当
※現地手配

100

▼FL

アングル止水栓 PJ1/2
※現地手配

変換エルボ管 G1/2
本体同梱品

() H875
< > H900を示す

給水（給湯）管
※現地手配

470
(495) < 520 >

給水（給湯）ホース
L=1.6m

▼FL

【コンセント 配管キャビネット内の場合】
・必ずパナソニック製フロントオープン食洗機専用のコンセントにしてください。
・コンセントは水滴が飛ばないように必ず500mm以上の位置に取り付けてください。
・必ず配管キャビネット内に設置してください。

() H875
< > H900を示す

550
(575) < 600 >

接地極付コンセント【専用】
250V・15A 2極接地極付コンセント
※パナソニック製フロントオープン食洗機
と反対側の側板へ取付け
※現地手配

配管キャビネット
正面図

75

100

200
(200) < 250 >

550
(575) < 600 >

▼FL

背板

配管キャビネット
側面図

切り欠き

物件名

仕様

中村悦久・裕子 様邸

ND23

案件No.

図面名

担当

図面

図番

A2509DDD0EUWCN

機能図

栗野 友仁

見積No.

縮尺

日付

M25098825370-010-2

2025.12.22

特記事項


屏色 WL2:ホワイトスタック
取手 [R]スリム取手R（シャインニッケル）
ワークトップカラー 【DW】ソルティホワイト

株式会社 LIXIL

A3

20251222NCVX-01

■ 床の不陸に関して

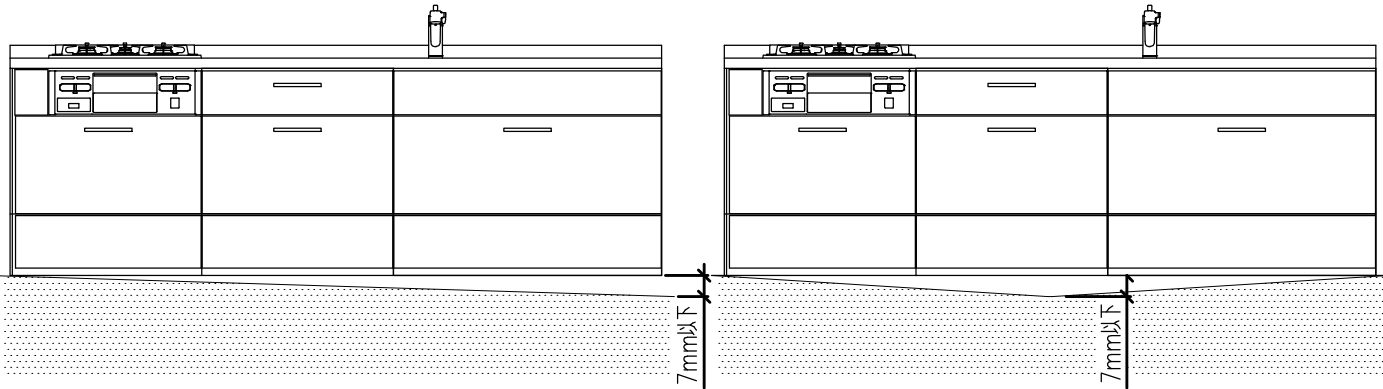


床の不陸は、7mm以下に抑えるようにしてください。不陸が大きい場合は、現場責任者に床の修正を依頼してください。
※キャビネット取付時には不陸調整スペーサー等で水平になるように設置してください。

■レンジフード取付注意事項（壁面取付時）


レンジフードを取付ける場合は下地の材が厚み30mm以上、幅100mm以上、ビス固定位置が材の端部から25mm以上であることを確認してください。
また、壁強度などの詳細は「レンジフード設置説明書」を必ず事前に確認してください。

取付位置については、取付設置図を確認してください。


参考図_CLS. SER. NST. ASR. ADR. RVJ. GSR. BFRS. TARシリーズ
（※RVJ. GSRシリーズの場合はレンジフードパネルの取付下地は不要です。）

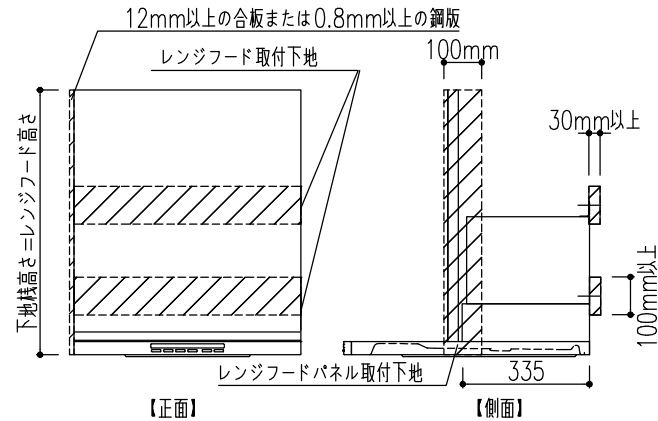


参考図_FED. HVR. NSDシリーズ（サイドマントルタイプ）

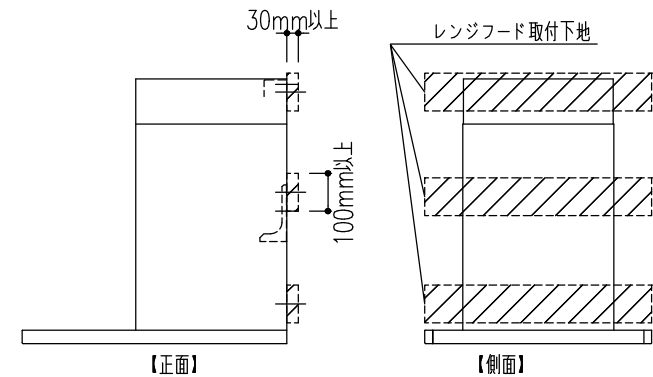


参考図_NBHシリーズ

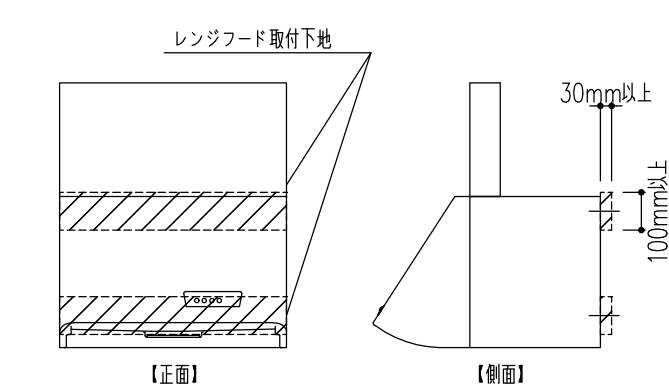

■SMHVRフード

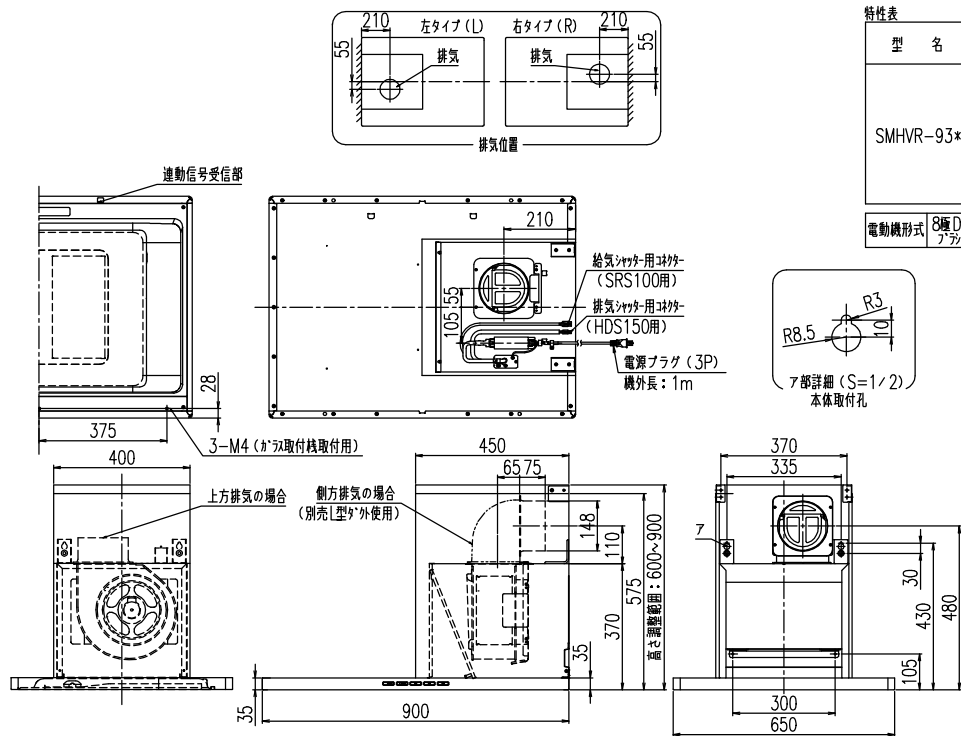


特性表									
型 名	定格電圧 (V)	/ノ	定格周波数 (Hz)	消費電力 (W)	風 量 OPa 100Pa	騒 音 (dB)	製品質量 (Kg)		
SMHVR-93*	100	強	50	70	530	435	48	26.5	
		中	30	28	370	—	39		
		弱	30	11	220	—	28		
		常時	30	7	155	—	22		
			60						
電動機形式		8極DC ブラシレスモーター	絶縁抵抗	10MΩ以上 (500V時)		耐電圧	AC1000V 1分間	絶縁区分	E種
風量値はJIS C9603「ファン」法による									

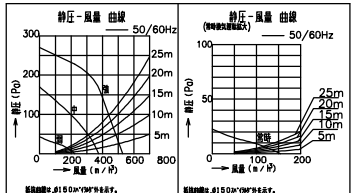

付 属 品	
座付ねじ (φ5.1×45)	10本
化粧ねじ (M4×8)	2本
トラスねじ (M4×10)	2本
ソフトテープ	1本


品 番	色 調
SMHVR-93*SL(R/L)	シルバー塗装
SMHVR-93*W(R/L)	ホワイト塗装

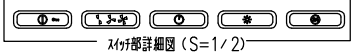

■IHヒーター用コンセント推奨位置図 / 壁付設置の場合

※コンセントや電源プラグが、引き出しおよびIHヒーター用仕切板（オプション）に接触しないように注意してください。
※木製キャビネットの配管スペース付キャビネットを使用する場合は点検口裏の配管スペース内にコンセントを設置してください。

キッチン高さ	電源線高さ
800	400
850	450
900	500

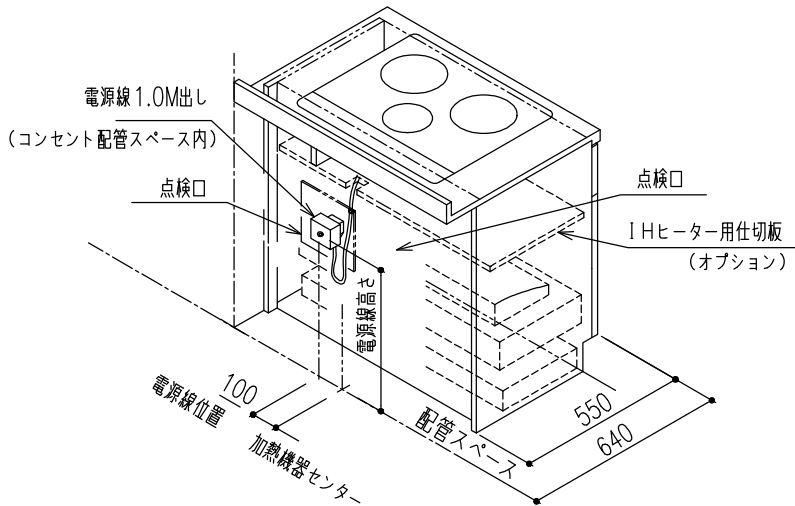

注意：引き出しおよびIHヒーター用仕切板（オプション）に接触しないように上記寸法を参照してください。

4. 製品名の末尾の（L）にはワッフルスによって記号が入る場合があります。
3. 電動シャッター（HDS150）（別売）を使用時は、中継ユニットを外して取り付けてください。
2. 赤外線連動型リモコンです。単独でも使用できます。
注）1. 排気方向は側方（L型が外使用・別売）と上方です。

特記事項
扉色 WL2:ホワイトスタック
取手 [R]スリム取手R（シャインニッケル）
ワークトップカラー 【DW】ソルティホワイト


物件名 中村悦久・裕子 様邸

仕様 ND23


案件No.	図面名	担当	図面	図番
A2509DDD0EUWCN	機能図	栗野 友仁		
見積No.	縮尺	日付		
M25098825370-010-2		2025.12.22		

株式会社 LIXIL

■ 止水栓図（床立上げ）

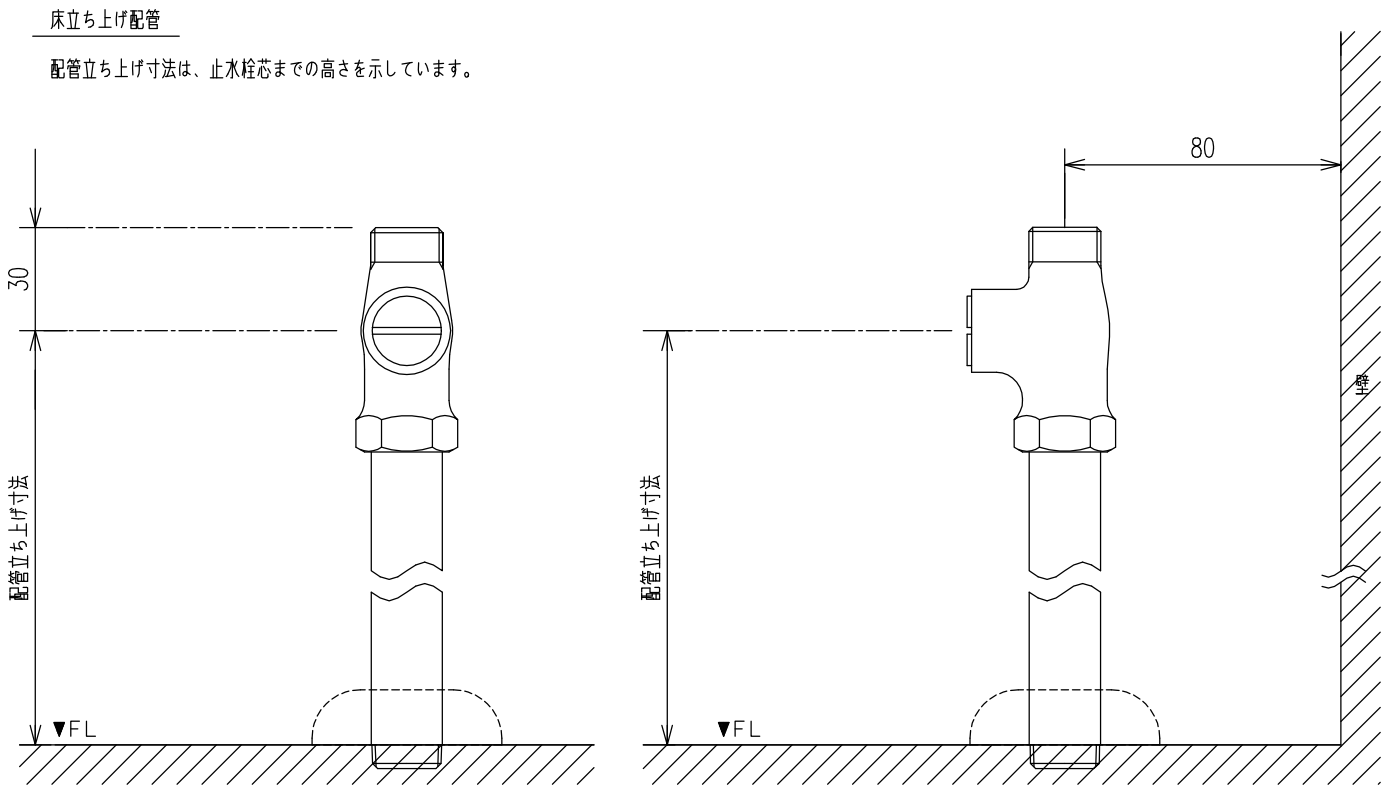

■ タッチレス水栓ナビッシュ 推奨電源位置図

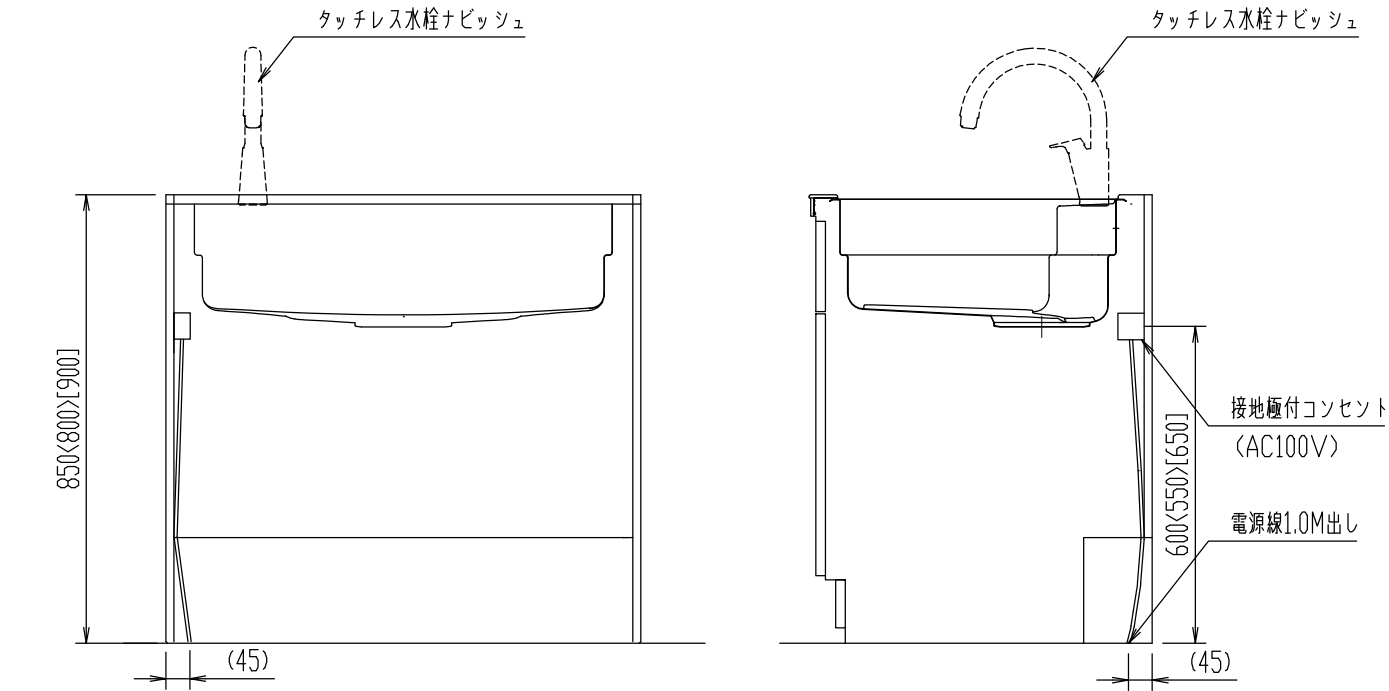

○水栓がシンク右側の場合、電源位置は左右対象の位置にしてください。
○水栓がシンク中央の場合、電源位置は左右どちらでも構いません。
○< >内寸法はワークトップ高さ80cmの場合、[]内寸法はワークトップ高さ90cmの場合。

■ キッチン取付者さま向け 動画コンテンツ ■

商品取付けの注意点を2次元コードでご視聴いただけます。
取付日より前に、是非ご確認ください。

1 ページ目

■ キッチン取付者さま向け 動画コンテンツ ■

商品取付けの注意点を2次元コードでご視聴いただけます。

取付日より前に、是非ご確認ください。

1 ページ目


■ キッチン取付者さま向け 動画コンテンツ ■

商品取付けの注意点を2次元コードでご視聴いただけます。
取付日より前に、是非ご確認ください。

1 ページ目

荷扱い・搬入


荷扱い・搬入

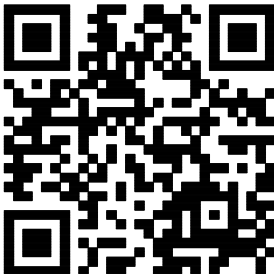

作成日：2024年10月01日

荷扱い・搬入

荷扱い・搬入

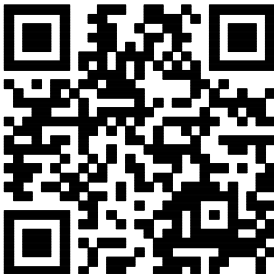


作成日：2024年10月01日



荷扱い・搬入


荷扱い・搬入

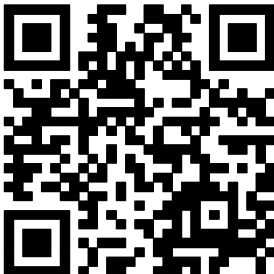

作成日：2024年10月01日

カウンター開梱搬入「養生ツール」


カウンター開梱搬入 「養生ツール」のご紹介

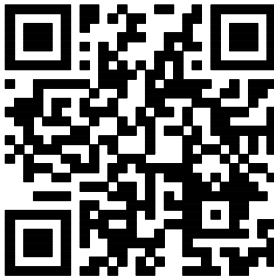

作成日：2024年10月01日

カウンター開梱搬入「養生ツール」

カウンター開梱搬入 「養生ツール」のご紹介

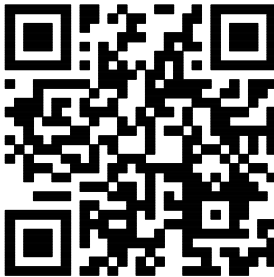


作成日：2024年10月01日




カウンター開梱搬入「養生ツール」

カウンター開梱搬入 「養生ツール」のご紹介


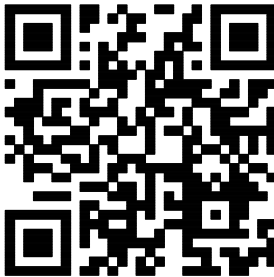


作成日：2024年10月01日


不陸の確認と調整

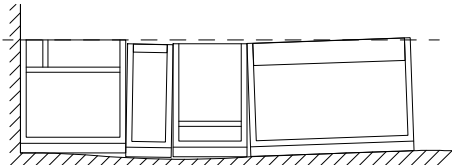

作成日：2024年02月07日

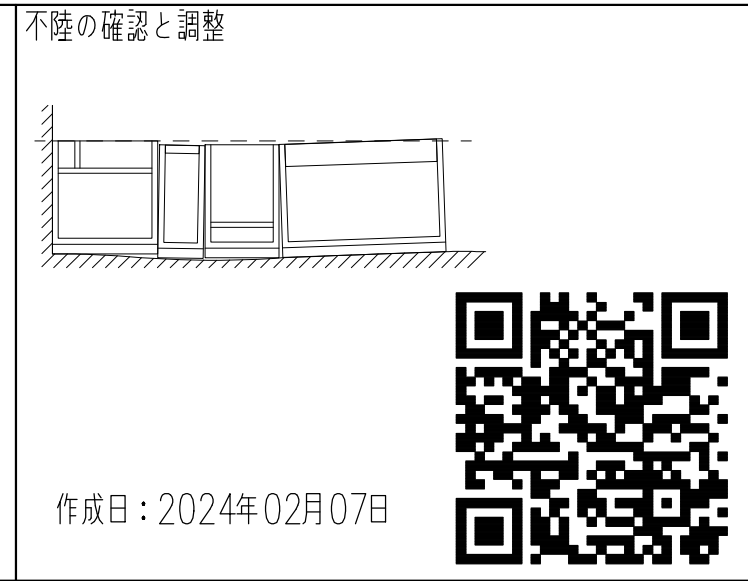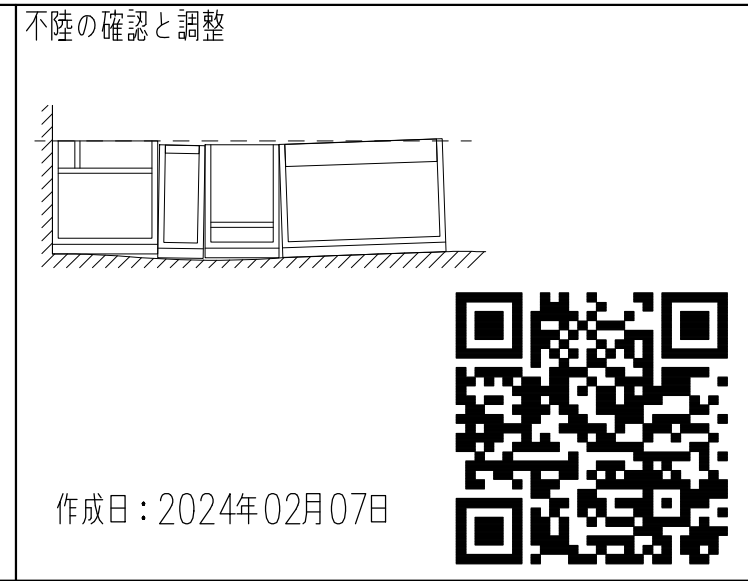

不陸の確認と調整

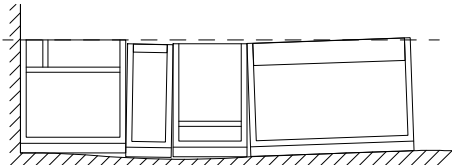

作成日：2024年02月07日



マグネット キッチンパネル

マグネット キッチンパネル 「取付・設置」ポイント



作成日：2024年03月06日

マグネット キッチンパネル

マグネット キッチンパネル 「取付・設置」ポイント



作成日：2024年03月06日




マグネット キッチンパネル

マグネット キッチンパネル 「取付・設置」ポイント



作成日：2024年03月06日


人造大理石カウンターL型キッチン

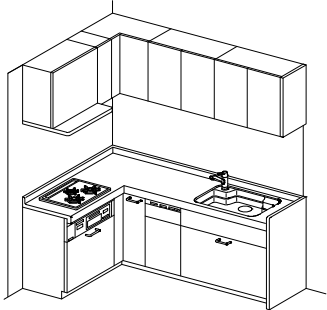

作成日：2024年02月07日




人造大理石カウンターL型キッチン

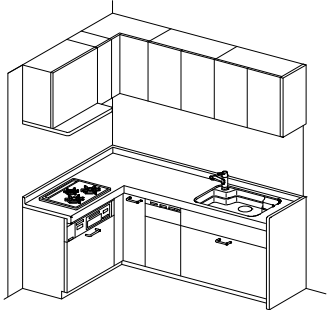



作成日：2024年02月07日




センターキッチン（ペニンシュラ型）

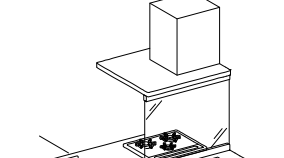

作成日：2024年02月07日

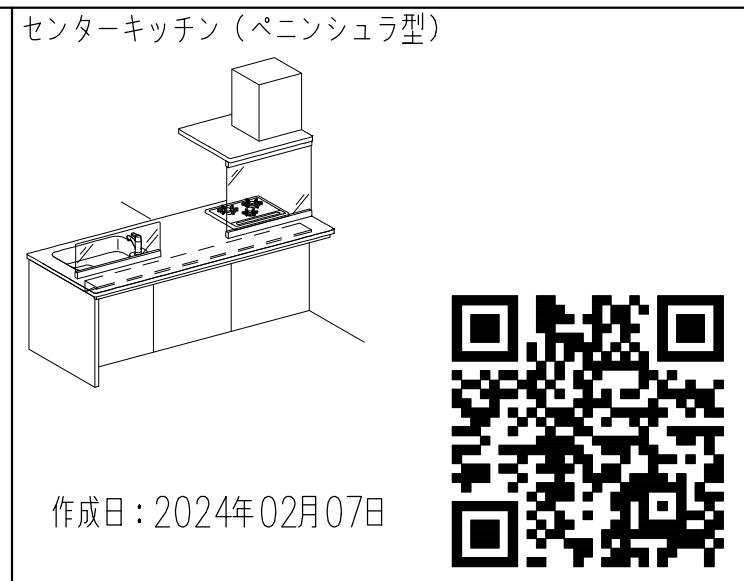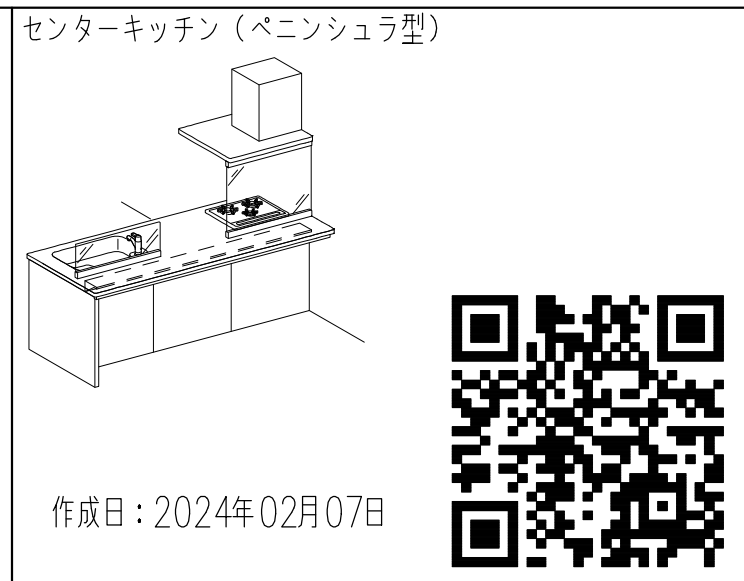




センターキッチン（ペニンシュラ型）

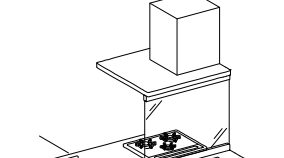

作成日：2024年02月07日



	特記事項 扉色 WL2:ホワイトスタック 取手 [R]スリム取手R (シャインニッケル) ワークトップカラー 【DW】 ソルティホワイト	物件名	中村悦久・裕子 様邸		案件No.		図面名		担当		図面		図番	
		A2509DDD0EUWCN			機能図		栗野 友仁							
		仕様	ND23	見積No.		縮尺		日付		株式会社 LIXIL				
				M25098825370-010-2				2025.12.22						

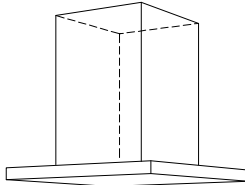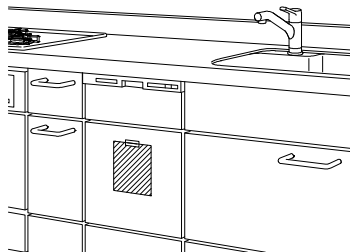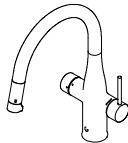■ キッチン取付者さま向け 動画コンテンツ ■										2 ページ目	
商品取付けの注意点を2次元コードでご視聴いただけます。											
取付日より前に、是非ご確認ください。											
センターフード型レンジフード (天吊りフード)  作成日：2024年06月03日			IH加熱機器関連 IH加熱機器 仕切り板  作成日：2024年02月07日			食器洗い乾燥機  作成日：2024年02月07日			ミネラル浄水栓 Greentap  作成日：2024年06月03日		
食器洗い機 ミーレ製 フロントオープン食洗器  作成日：2025年10月31日			食器洗い機 パナソニック製 フロントオープン食洗器  作成日：2025年10月31日								
		特記事項 扉色 WL2:ホワイトスタック 取手 [R]スリム取手R (シャインニッケル) ワークトップカラー 【DW】ソルティホワイト	物件名 仕様	中村悦久・裕子 様邸 ND23		案件No.		図面名	担当	図面	図番
						A2509DDD0EUWCN		機能図	栗野 友仁		株式会社 LIXIL
						見積No.		縮尺	日付		
						M25098825370-010-2			2025.12.22		