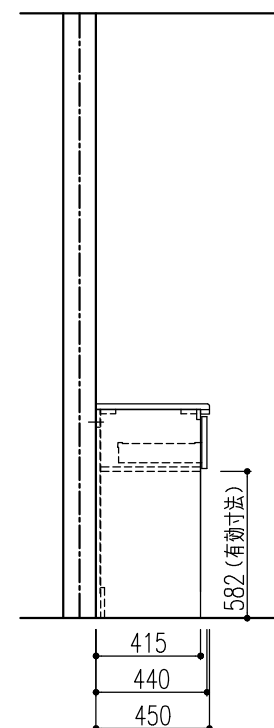


面



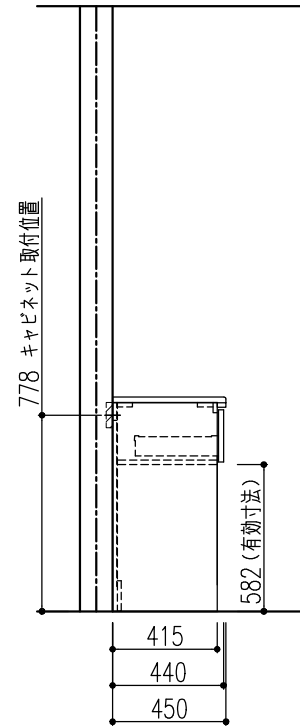
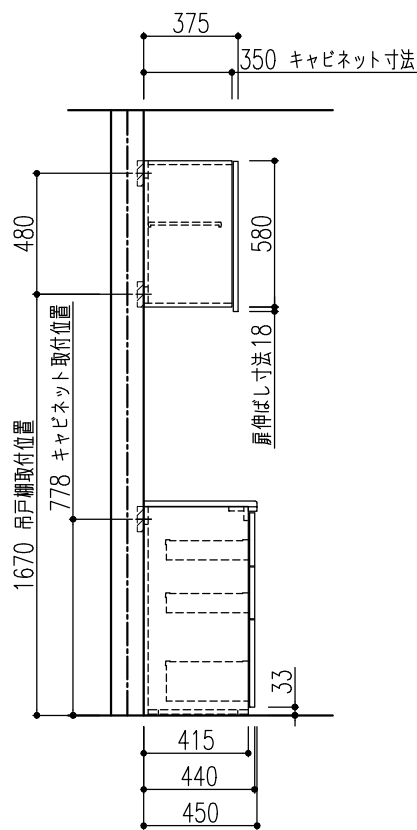
【 ご注意 】

- 記載のキャビネット寸法は扉前面までの呼び寸法です。キャビネット本体の寸法・扉厚み等は商品ガイドの巻末資料をご確認ください。
- 記載のワークトップ、カウンター、エンドパネル、サイドパネルの寸法は呼び寸法です。詳細寸法は商品ガイドの巻末資料をご確認ください。

A3 20251222NCVW-0

B面

B面




特記事項 扉色 WK5:ホワイトスタック 取手 [R]スリム取手（シャインニッケル）	物件名	中村悦久・裕子 様邸	案件No.	図面名	担当	図面	図番
	仕様	ES21	A2509DDD0EUWCN	納まり図	栗野 友仁		株式会社 LIXIL
			見積No.	縮尺	日付		
			M25098825370-010-3	1/30	2025.12.22		


■吊戸棚 取付注意事項

吊戸棚が落下する恐れがありますので、下記事項をお守りください。

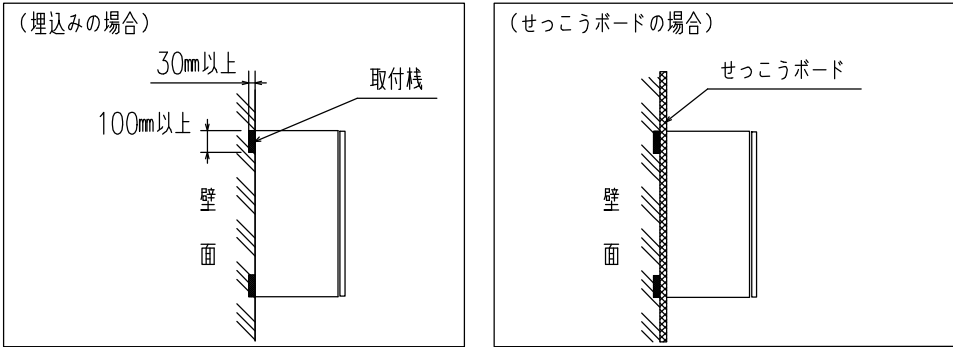
- 本体重量と収納重量の荷重に対して、取付棧（下地）が落ちないだけの強度をもたせてください。
最大300kg/1キャビネット当たりの強度がもつように柱・間柱に確実に固定してください。
- キャビネットを取付・設置する壁面には、取付棧（下地）を取付けるか、埋め込みます。
- 取付棧（下地）は広葉樹、マツ・ツガ等の強度のある針葉樹いずれかの無垢材を使用します。
また、厚さ30mm以上、幅100mm以上が必要です。
- 合板を取付棧（下地）として使用する場合は、ラワン合板などの硬い材質の普通合板
（表面が平滑でフシがない、虫くいや、くされのないもの）を使用します。
また、必ず厚さ12mm以上のものを使用してください。
- せっこうボードで仕上げる壁面は、せっこうボードの内側に取付棧（下地）を取付けます。



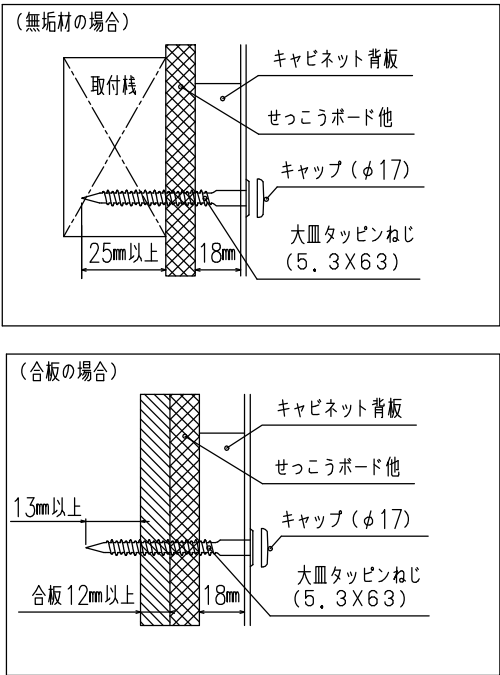- 吊戸棚の取付けは、必ず商品同梱の専用ネジ（大皿タッピンねじ5.3X63）を使用し、取付棧（下地）に25mm以上かかるようにしてください。
- 合板下地の場合は、下地からのネジ貫通しを13mm以上としてください。
- 合板下地はネジ箇所だけでなく、全面下地（吊戸棚全体）を原則とします。



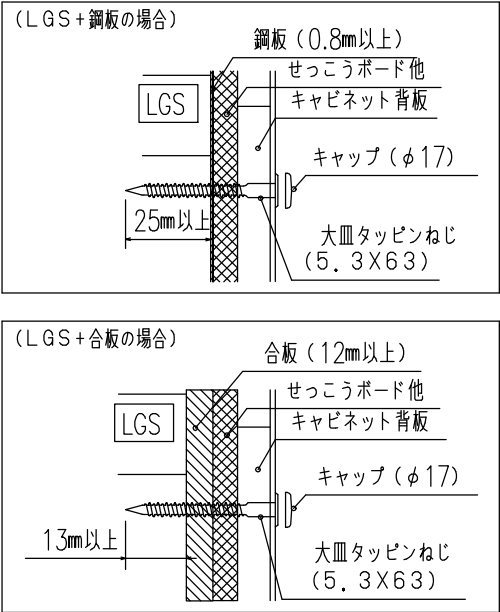
- 鋼板下地の場合 ・鋼板の変形を防ぐため必ずせっこうボード等で覆ってください。
・下地からのネジ貫通しを25mm以上としてください。
- 鋼板下地でせっこうボード2枚貼りの場合、その内側に下地を敷設する事は、
上記のネジ貫通しが確保出来ないため設置できません。
- 鋼板の厚みは必ず0.8mm以上のものを使用してください。
- 軽量鉄骨躯体（LGS）の設置間隔は300mm以下を守ってください。




■アイレベルレール 取付注意事項

※ アイレベルレール設置の場合

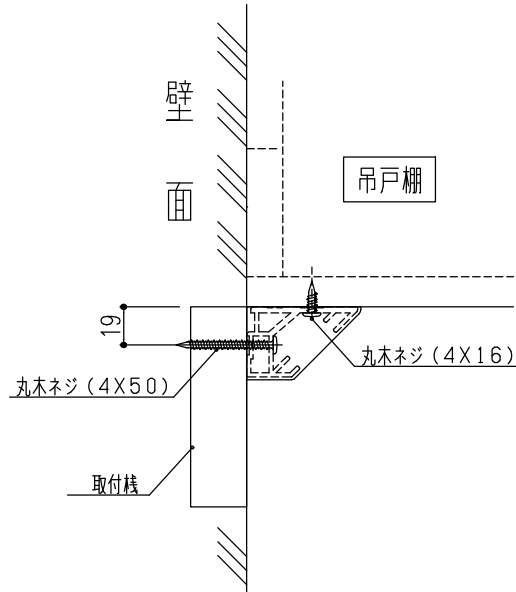- アイレベルレールの設置に関しては 下記要領で取付棧（下地）
を御用意願います。










■ 床の不陸に関して

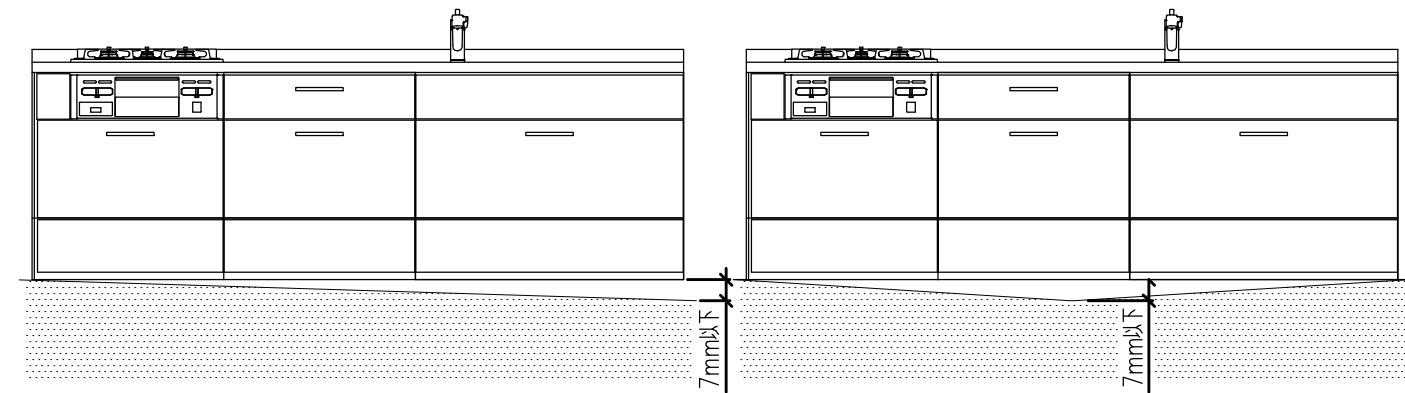






床の不陸は、7mm以下に抑えるようにしてください。不陸が大きい場合は、現場責任者に床の修正を依頼してください。
※キャビネット取付時には不陸調整スペーサー等で水平になるように設置してください。

特記事項 扉色 WK5:ホワイトスタック 取手 [R]スリム取手（シャインニッケル）	物件名	中村悦久・裕子 様邸	案件No.	図面名	担当	図面	図番
			A2509DDD0EUWCN	機能図	栗野 友仁		株式会社 LIXIL
	仕様	ES21	見積No.	縮尺	日付		
			M25098825370-010-3		2025.12.22		

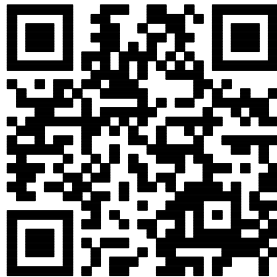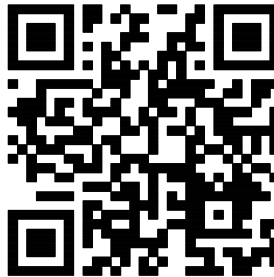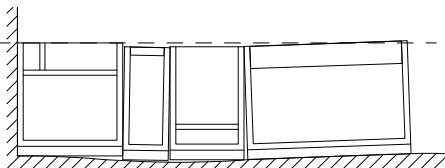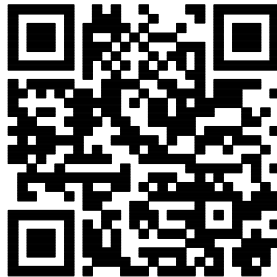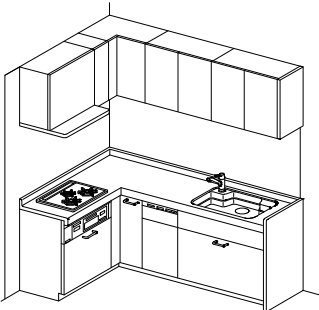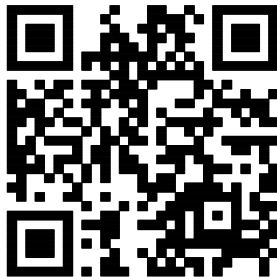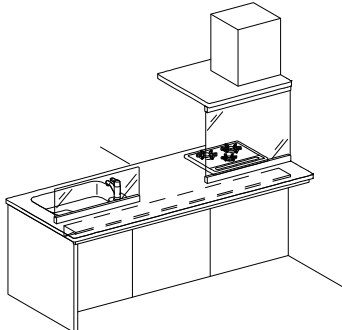■ キッチン取付者さま向け 動画コンテンツ ■ 商品取付けの注意点を2次元コードでご視聴いただけます。 取付日より前に、是非ご確認ください。												1 ページ目	
荷扱い・搬入 荷扱い・搬入  作成日：2024年10月01日			カウンター開梱搬入「養生ツール」 カウンター開梱搬入 「養生ツール」のご紹介  作成日：2024年10月01日			不陸の確認と調整   作成日：2024年02月07日			マグネットキッチンパネル マグネット キッチンパネル 「取付・設置」ポイント  作成日：2024年03月06日				
人造大理石カウンターL型キッチン   作成日：2024年02月07日			センターキッチン（ペニンシュラ型）   作成日：2024年02月07日										
		特記事項 扉色 WK5:ホワイトスタッコ 取手 [R]スリム取手（シャインニッケル）		物件名	中村悦久・裕子 様邸		案件No.	図面名	担当	図面	図番	株式会社 LIXIL	
				仕様	ES21		A2509DDD0EUWCN	機能図	栗野 友仁				
							見積No.	縮尺	日付				
							M25098825370-010-3		2025.12.22				

■ キッチン取付者さま向け 動画コンテンツ ■

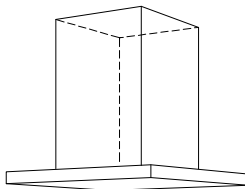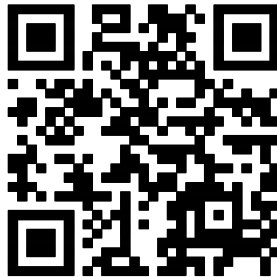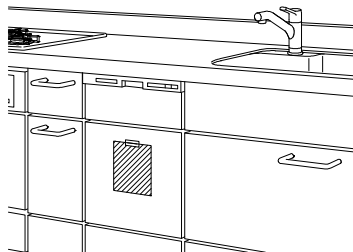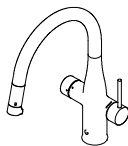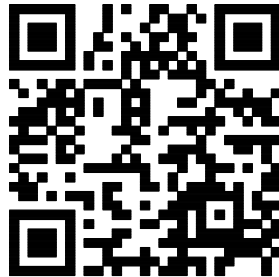商品取付けの注意点を2次元コードでご視聴いただけます。
取付日より前に、是非ご確認ください。

センターフード型レンジフード (天吊りフード)  作成日：2024年06月03日 		I H加熱機器関連 I H加熱機器 仕切り板 作成日：2024年02月07日 		食器洗い乾燥機  作成日：2024年02月07日 		ミネラル浄水栓 Greentap  作成日：2024年06月03日 			
	特記事項 扉色 WK5:ホワイトスタッコ 取手 [R]スリム取手 (シャインニッケル)	物件名 仕様	中村悦久・裕子 様邸		案件No.	図面名	担当	図面	図番
					A2509DDD0EUWCN	機能図	栗野 友仁		株式会社 LIXIL
			ES21		見積No.	縮尺	日付		
					M25098825370-010-3		2025.12.22		