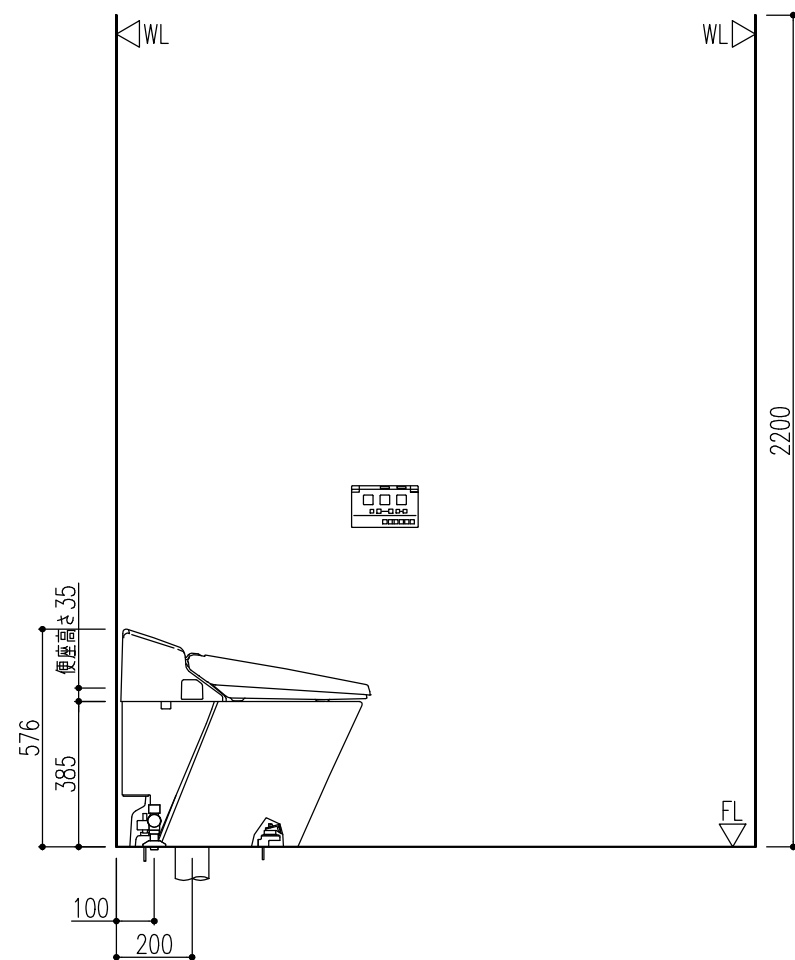
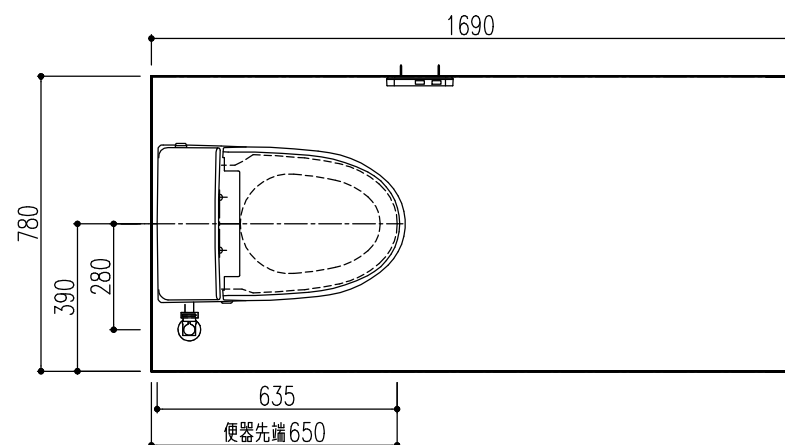
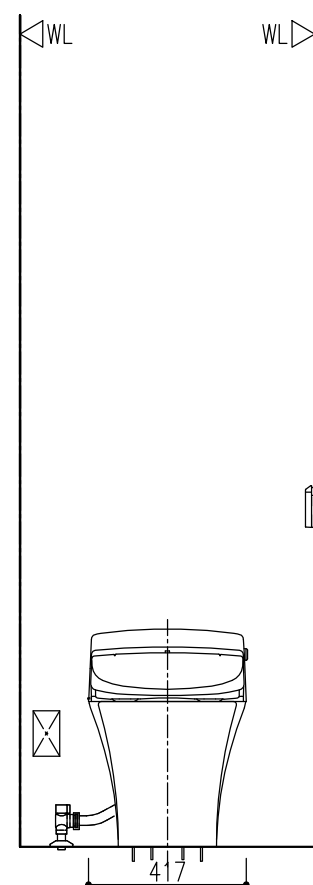


[illegible]

【共通】

- ※ 部品表の「図面」列に○がないものは図面表示されません。
- ・ このプランの施工情報については事前に商品の施工説明書や工事用図面集にてご確認ください。
2枚目以降の機能図にも商品情報の記載があります。
- ・ 商品仕様・図面の改良や仕様変更等は、予告なく行う場合があります。
- ・ 壁面に取り付ける商品にはあらかじめ壁補強が必要です。必要な壁面工事は2枚目以降の機能図にてご確認ください。
- ・ 壁埋込みの必要な商品はあらかじめ商品に合わせた開口を行ってください。
- ・ 電源が必要な商品には、商品の仕様に合わせたコンセント設置等の電気工事(別途工事)をあらかじめ行ってください。商品の施工説明書にて工事内容をご確認ください。
- ・ コンセントは、電源コードの届く範囲で床面より高く水のかからない位置に設けてください。
また、コンセントの壁給水真下部設置や給水ホースとの接触は感電・火災の原因になりますので避けてください。
- ・ 扉等の建築物による干渉をご確認ください。
- ・ アクセサリー類・手洗器の設置位置は参考寸法です。使いやすさに合わせて取付位置を決定ください。
- ・ ()内寸法は、参考寸法です。
- ・ 陶器寸法許容差はJIS A5207に準じています。
- ・ 結露水・小水によるシミの発生を防ぐため、トイレ床材には防水加工が施された床材をご使用ください。

【便器】

- ・ 洗浄水量：大5L、小3.8L
- ・ 製品両側面から120mm以上、背面に15mm以上の空周を確保してください。
- ・ 機能部上部に棚等を設置する場合は、床から1050mm以上の空周が必要です。
- ・ 一般地用、寒冷地用水抜式、寒冷地用流動式兼用品です。

【寒冷地用水抜式の場合】トイレ内使用限界：0℃以上(室内暖房)。

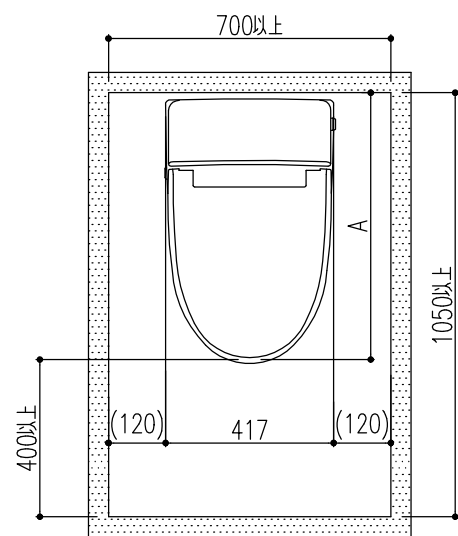
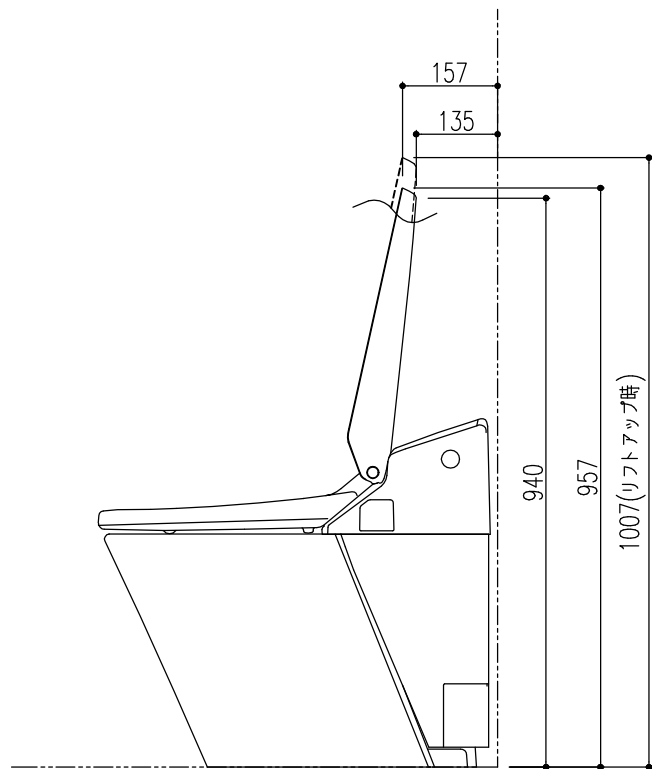
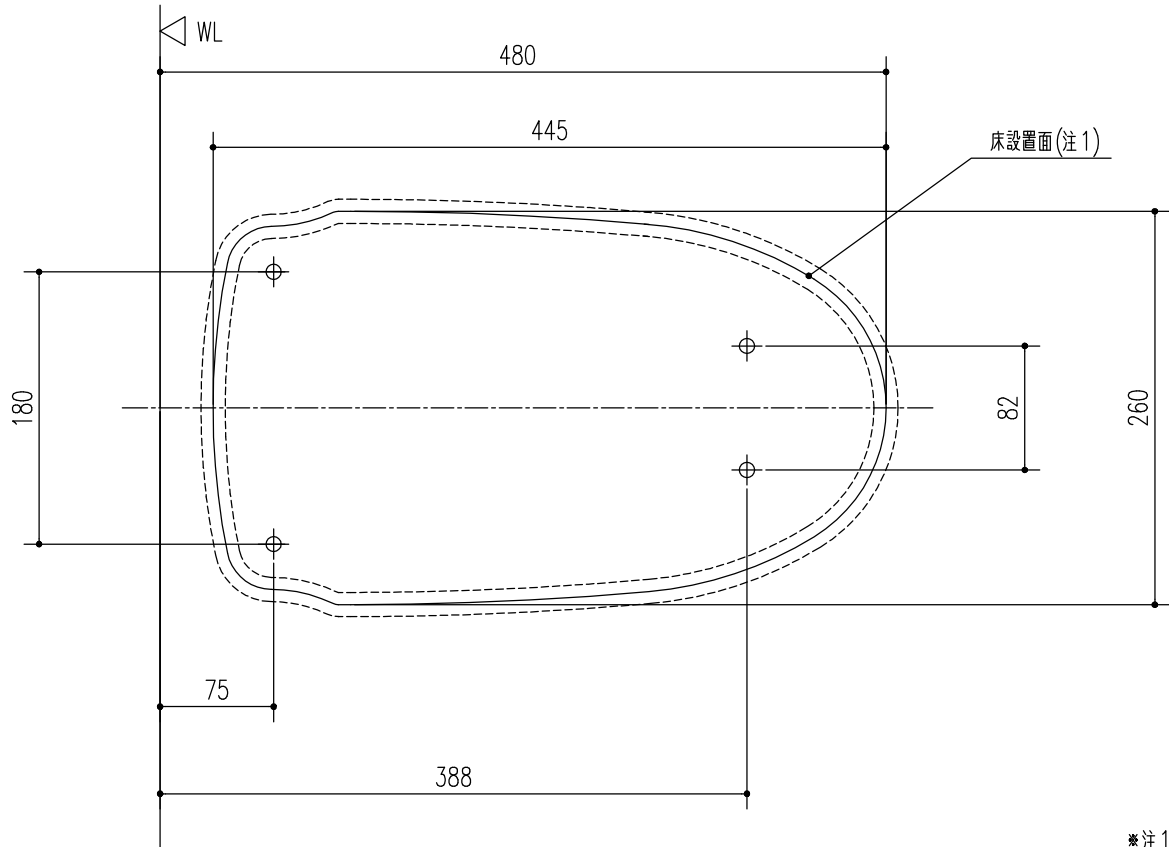
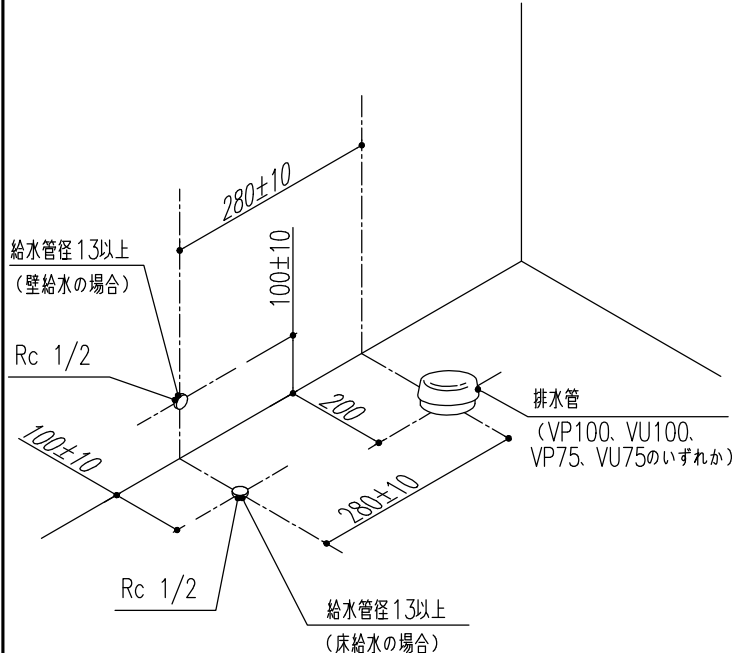
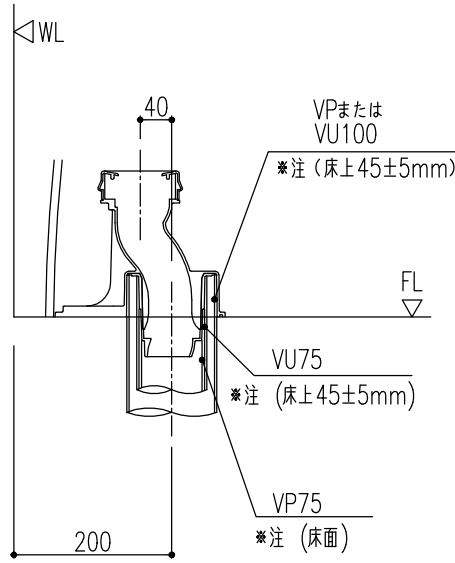
0℃を下回る場合は給水管内およびタンク内の水抜きをしてください。

【寒冷地用流動式の場合】トイレ内使用限界：0℃以上(室内暖房)、流動水量40L/h。

0℃を下回る場合は器具内の水を流動させてください。水圧により流動水量は変動します。

- ・ 凍結防止には器具への通電が必要です。
- ・ 最低必要水圧は0.05MPa(13L/分 流動時)、0.15MPa以上(静止時)です。
- ・ 最高水圧は0.75MPa(静止時)です。
- ・ 給水管呼び径13以上が必要です。
- ・ 設置前に水圧判定治具(CWA-234)で、水圧の確認を行ってください。
- ・ D種接地工事が必要です。アースターミナル付接地極付コンセントを使用してください。
- ・ 定格消費電力350W(機能部)
- ・ 機能部電源コード長さ1000mm
- ・ インバータ照明により誤作動する場合があります。

	特記事項	物件名	中村悦久・裕子 様邸	案件No.	図面名	担当	図面	図番 : 株式会社 LIXIL
				A2509DDD0EUWCN	簡易取付設置図	葉野 友仁		
		仕様	ベーシアハーモJタイプ/ECO5 床排水 一般地・水抜方式・流動方式兼用	見積No.	縮尺	日付		
				M25098825370-010-5	1/20	2025.12.22		

● ベーシアハーモJタイプ取付最小スペース		● ベーシアハーモJタイプ便フタ開時寸法		● 便器床設置面寸法・固定穴寸法							
 ※ 最少スペースはA寸法（前出寸法）+400となり、便器排水方向や既設配管により、異なります。 ※ 上図の空間寸法は、衣服の着脱などの行為に必要な最低寸法です。手すりや紙巻器などの機器を併設する場合は、必要に応じた広い空間が必要になります。 ※ 便器に向かって左右共に 120mm以上の空間を確保してください。		 ※上図は代表商品のイメージ図です。 ※防振シートを組み合わせる場合は、全体が5mm高くなります。		 ※注1:破線は±5%許容差範囲							
● 給排水の位置決めと取出し		● 排水塩ビ管の接続									
給水管、排水管を取り出します。 ※ 右給水の場合は、排水管を中心に左右反対の位置に給水管を取り出してください。 ※ 右給水の場合は、給水ホース（322-1135-62）を別途手配してください。 		※ 排水芯200のみの対応です。 ※ 接続は、塩ビ接着剤にて確実に行なって下さい。 ※ 接続（接着）位置及び立ち上げ高さは、配管サイズにより異なります。  ※注…防振シートを組み合わせる場合は5mm高くしてください。									
特記事項		物件名	中村悦久・裕子 様邸			案件No.	図面名	担当	図面	図番	
			ベーシアハーモJタイプ/ECO5 床排水 一般地・水抜方式・流動方式兼用			A2509DDD0EUWCN	機能図	栗野 友仁		株式会社 LIXIL	
						見積No.	縮尺	日付			
						M25098825370-010-5		2025.12.22			



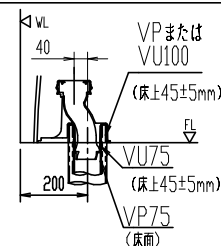
Technical drawing of a toilet showing dimensions and installation details. The drawing includes a side view of the toilet bowl and a front view. Key dimensions and labels are as follows:

- Top View Dimensions:**
 - Overall width: 417
 - Base width: 180
- Side View Details:**
 - Water level line: WL
 - Flush valve: アース (Earthing)
 - Flush valve cable length: コード有効長さ1.0m (Effective cable length 1.0m)

※ インバータ照明により誤作動する場合あり。
※ 機能部上部に輝等を設置する場合は床から1050mm以上の空留が必要。
備考) 上棚の止水栓は壁給水、床給水の双方に使用可能。
・ 右給水の栓は、オプション給水ホース(322-1135-62)を別途手配する。

排水塩ビ管の接続

- * 排水芯200のみの対応です。
- * 接続は、塩ビ接着剤にて確実に行なって下さい。
- * 接続(接着)位置及び立ち上げ高さは、配管サイズにより異なります。



YBC-J22S

洋風ダイレクトバルブ防露便器(シャワートイレ)

節水

洗淨水量：大5L、小3.8L

[illegible]

- * 製品両側面に120mm以上、背面に15mm以上の空留確保。
- * 設置前に水压判定治具(CWA-234)で、水压の確認を行ってください。

- * 静水圧0.15MPa、流動圧0.05MPa(瞬間流量13L/min)以上が必要。
 - * 最高水圧0.75MPa以下(静水圧)。 - * 給水管径φ13以上。
 - * D種接地工事必要。ア-ア-ミが接地極付コネクタを使用のこと。
 - * 一般地用、寒冷地用水板式、寒冷地用流動式を兼用。 - * 凍結防止には器具への通電が必要。
- 【寒冷地用水板式の場合】トレイル内使用限界：0℃以上(室内暖房)、器具の水抜き。
- 【寒冷地用流動式の場合】トレイル内使用限界：0℃以上(室内暖房)、流動水量40L/h。

縮尺	製図	釜山	検図	磯崎	備考
1:20	図番	GS-CJ22S-100001B/28252			
日付	2023.12.19				
株式会社 LIXIL					

陶器寸法許容差はJIS A5207に準ずる。壁取付商品には、補強木による壁補強が必要です。詳しくは、商品別「壁補強」一覧を参照ください。

