
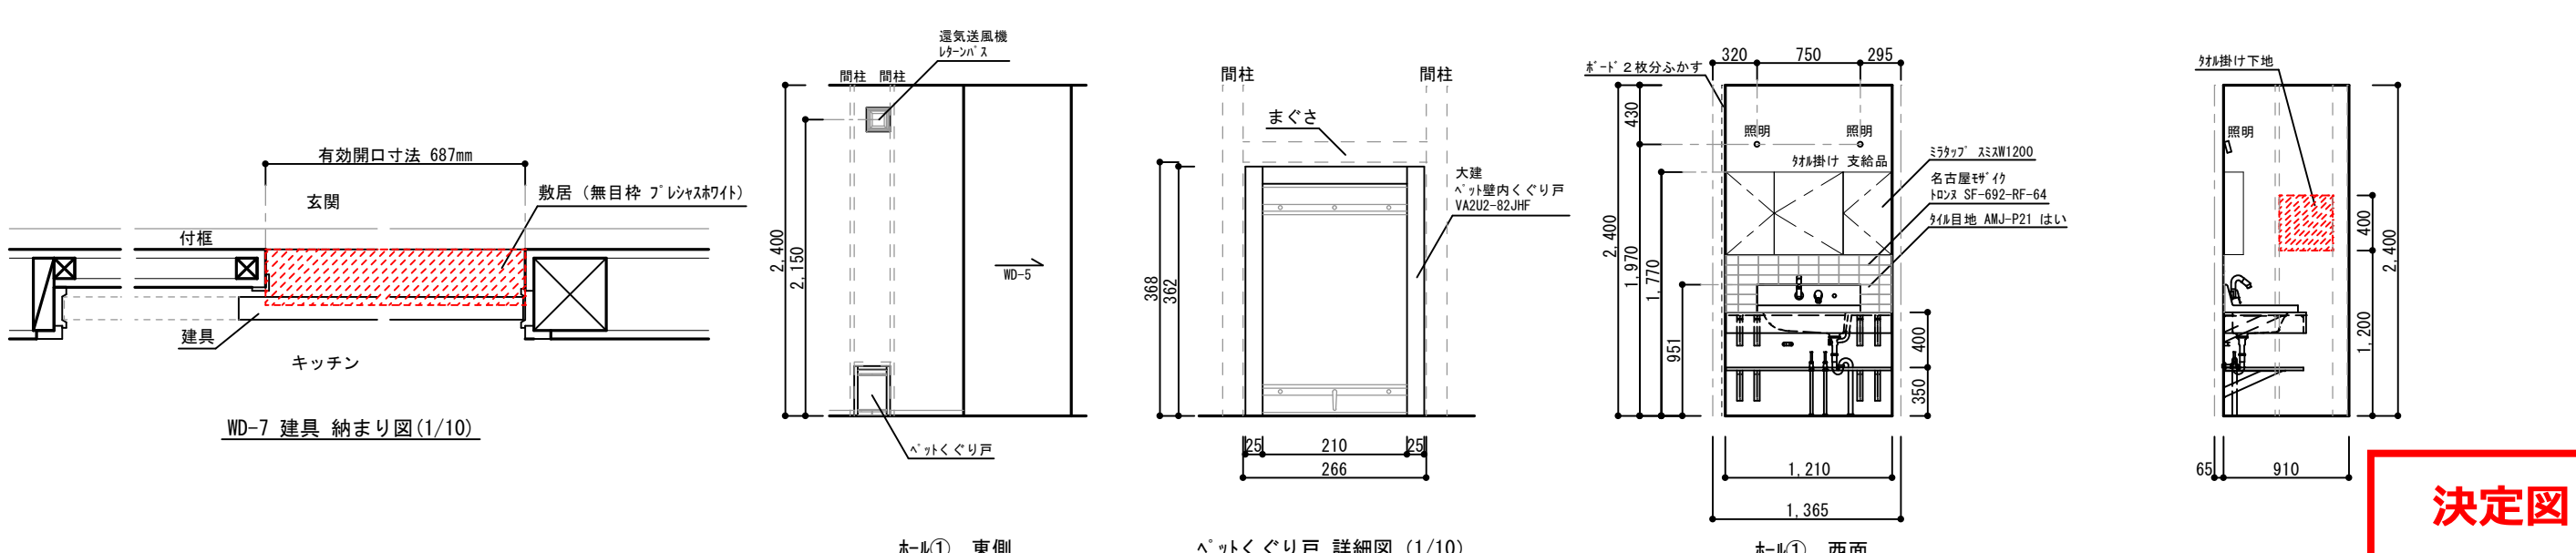
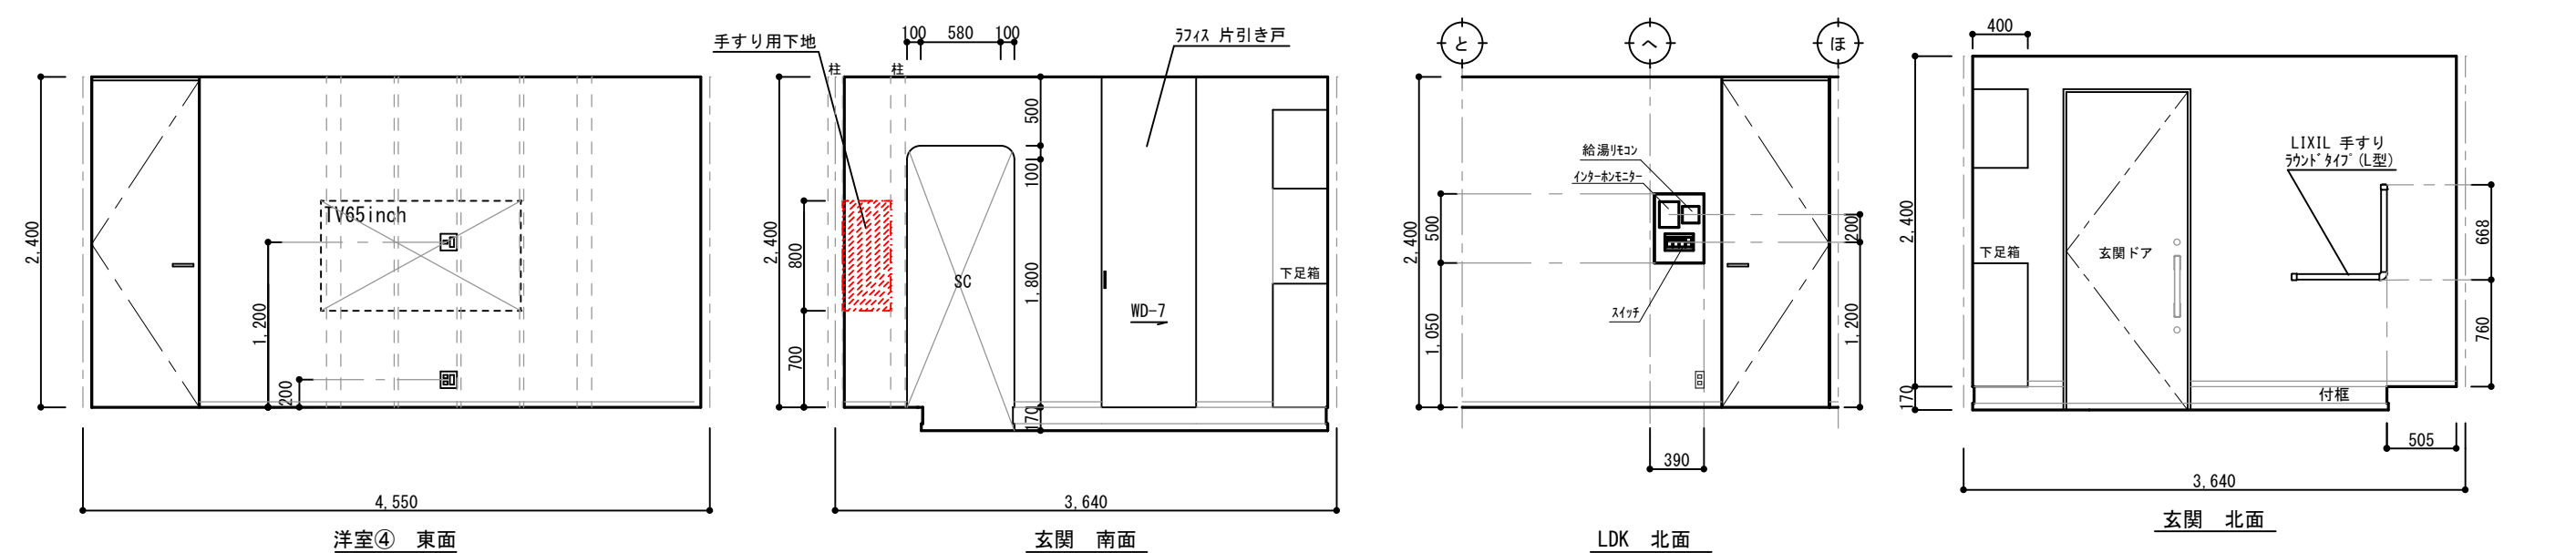


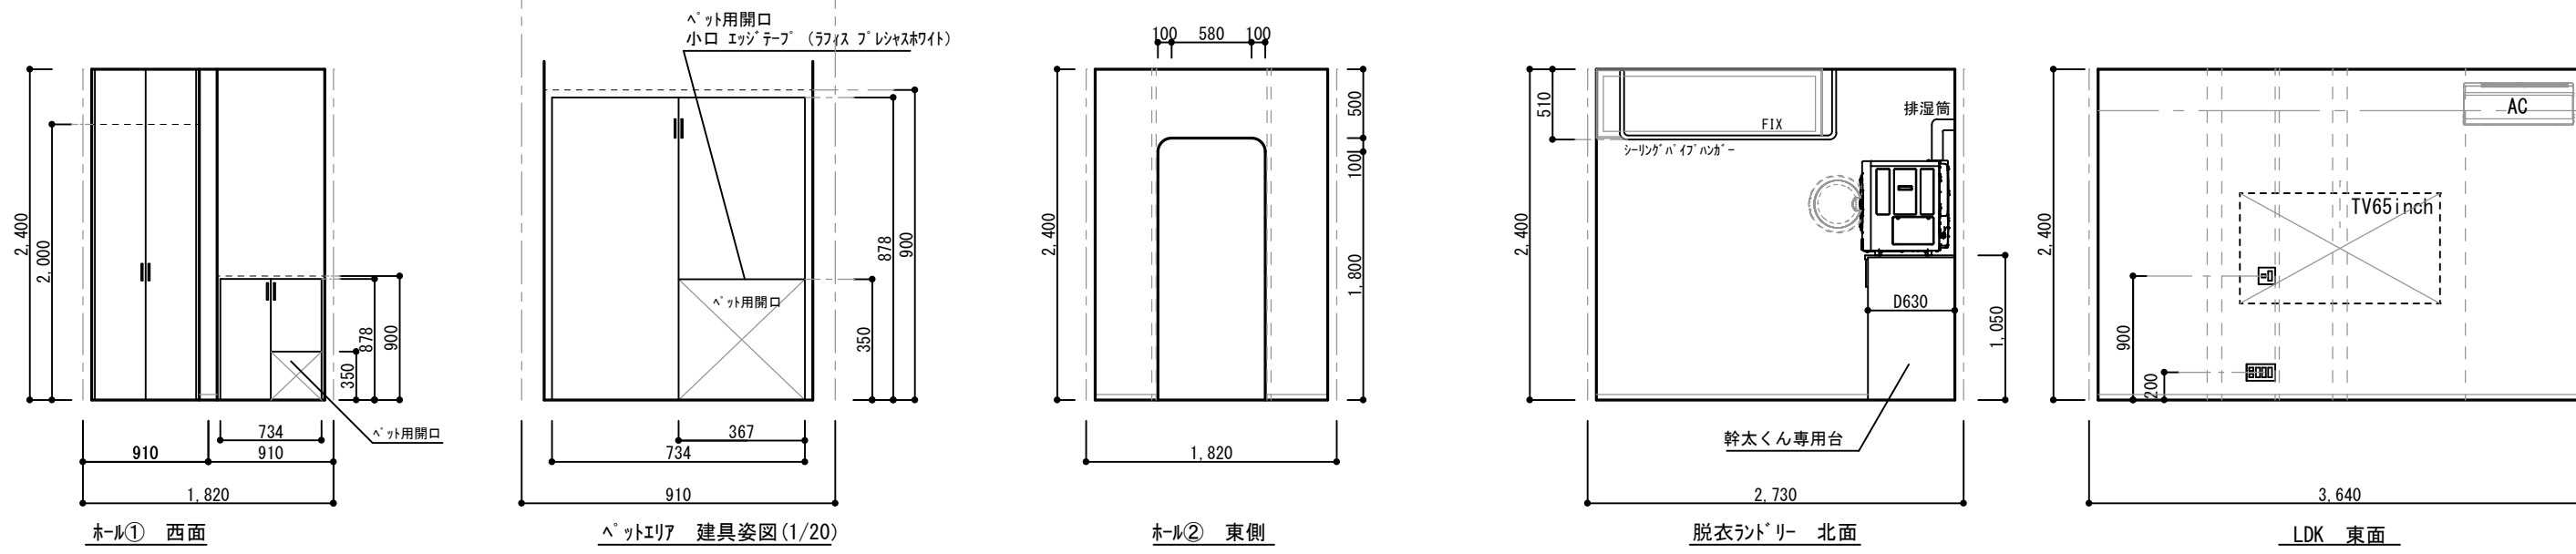

決定図

訂正	浜岡一級総合設計事務所 一級建築士事務所 静岡県知事登録第 (10)2441 号 一級建築士 大臣登録第 365879 号 西原利昌	LIFEFUND PG HOUSE	株式会社 LIFEFUND InDesign office 一級建築士事務所 事務所登録 (2)第7595号 一級建築士登録 第179770号 鈴木 達男 〒432-8023 静岡県浜松市中央区鴨江3丁目70番23号	年月日 2025.12.21 縮尺 1/50	件名 中村悦久様 裕子様 新築工事 図名 展開図-1	設計 酒井	IC	工事 青島	図番 6-1
----	--	----------------------	--	---------------------------------	-------------------------------------	----------	----	----------	-----------