

1Fアクセントクロス

12/15打合せにて決定

G2

壁付け 住宅用火災報知器			数量
[H] 熱感知器	電池式(単独型)		1
	露出型		
壁付け 住宅用火災報知器			数量
[S] 煙感知器	電池式(単独型)		1
	露出型		

※ 煙感知器は壁・梁より600mm以上離す
壁に取付ける場合、
天井から150mm以上500mm以内離す
換気扇・エアコン吹出口から1500mm以上離す
※ 全室LED照明とする。
※ 標準天井高さ2,400
※ 特記無きガラスは型ガラス

* 凡例

- ☒ 管柱 (105×105)
- ☒ Kダクト (3.30倍 FRM-0641)
- △ 片筋違い (2.00倍 45×90)
(例 左:柱脚 右:柱頭)
- ☒ たすき掛筋違い (4.00倍 45×90)
- 構造用合板 (2.70倍)
(t=9 タイガ-EXハイパー)
- ☒ 床点検口
- ☒ 天井点検口
- ☒ 換気扇
- ☒ 熱交換換気扇VLR-70

階段寸法表

有効幅: 750
踏面: 227.5
※ 廻り階段部分: 150以上確保
蹴上: 207.15


脱衣室ランドリー 仕上材

天井: ア9.5PB下地ビニルクロス貼り
壁: ア12.5PB下地ビニルクロス貼り
床: ア24+15耐水合板下地フローリング張り

※ 下屋部分点検口について
ダウンライト、FS天井点検口、UB点検口より
ボールカメラやファイバースコープ等の
検査機器等を使用して点検する

※ 給水設備: ヘッダー分岐後の全ての配管径は13A以下とする
※ 水栓: 一般社団法人日本バルブ工業会の定義による節湯水栓
台所: 2バルブ水栓以外のその他の水栓(水優先吐水機能)
浴室シャワー: 2バルブ水栓以外のその他の水栓(小流量吐水機能)
洗面: 2バルブ水栓以外のその他の水栓(水優先吐水機能)
※ 照明設備: 全室LED照明とし居室においては調光制御、非居室においては
人感センサーを採用する

決定図

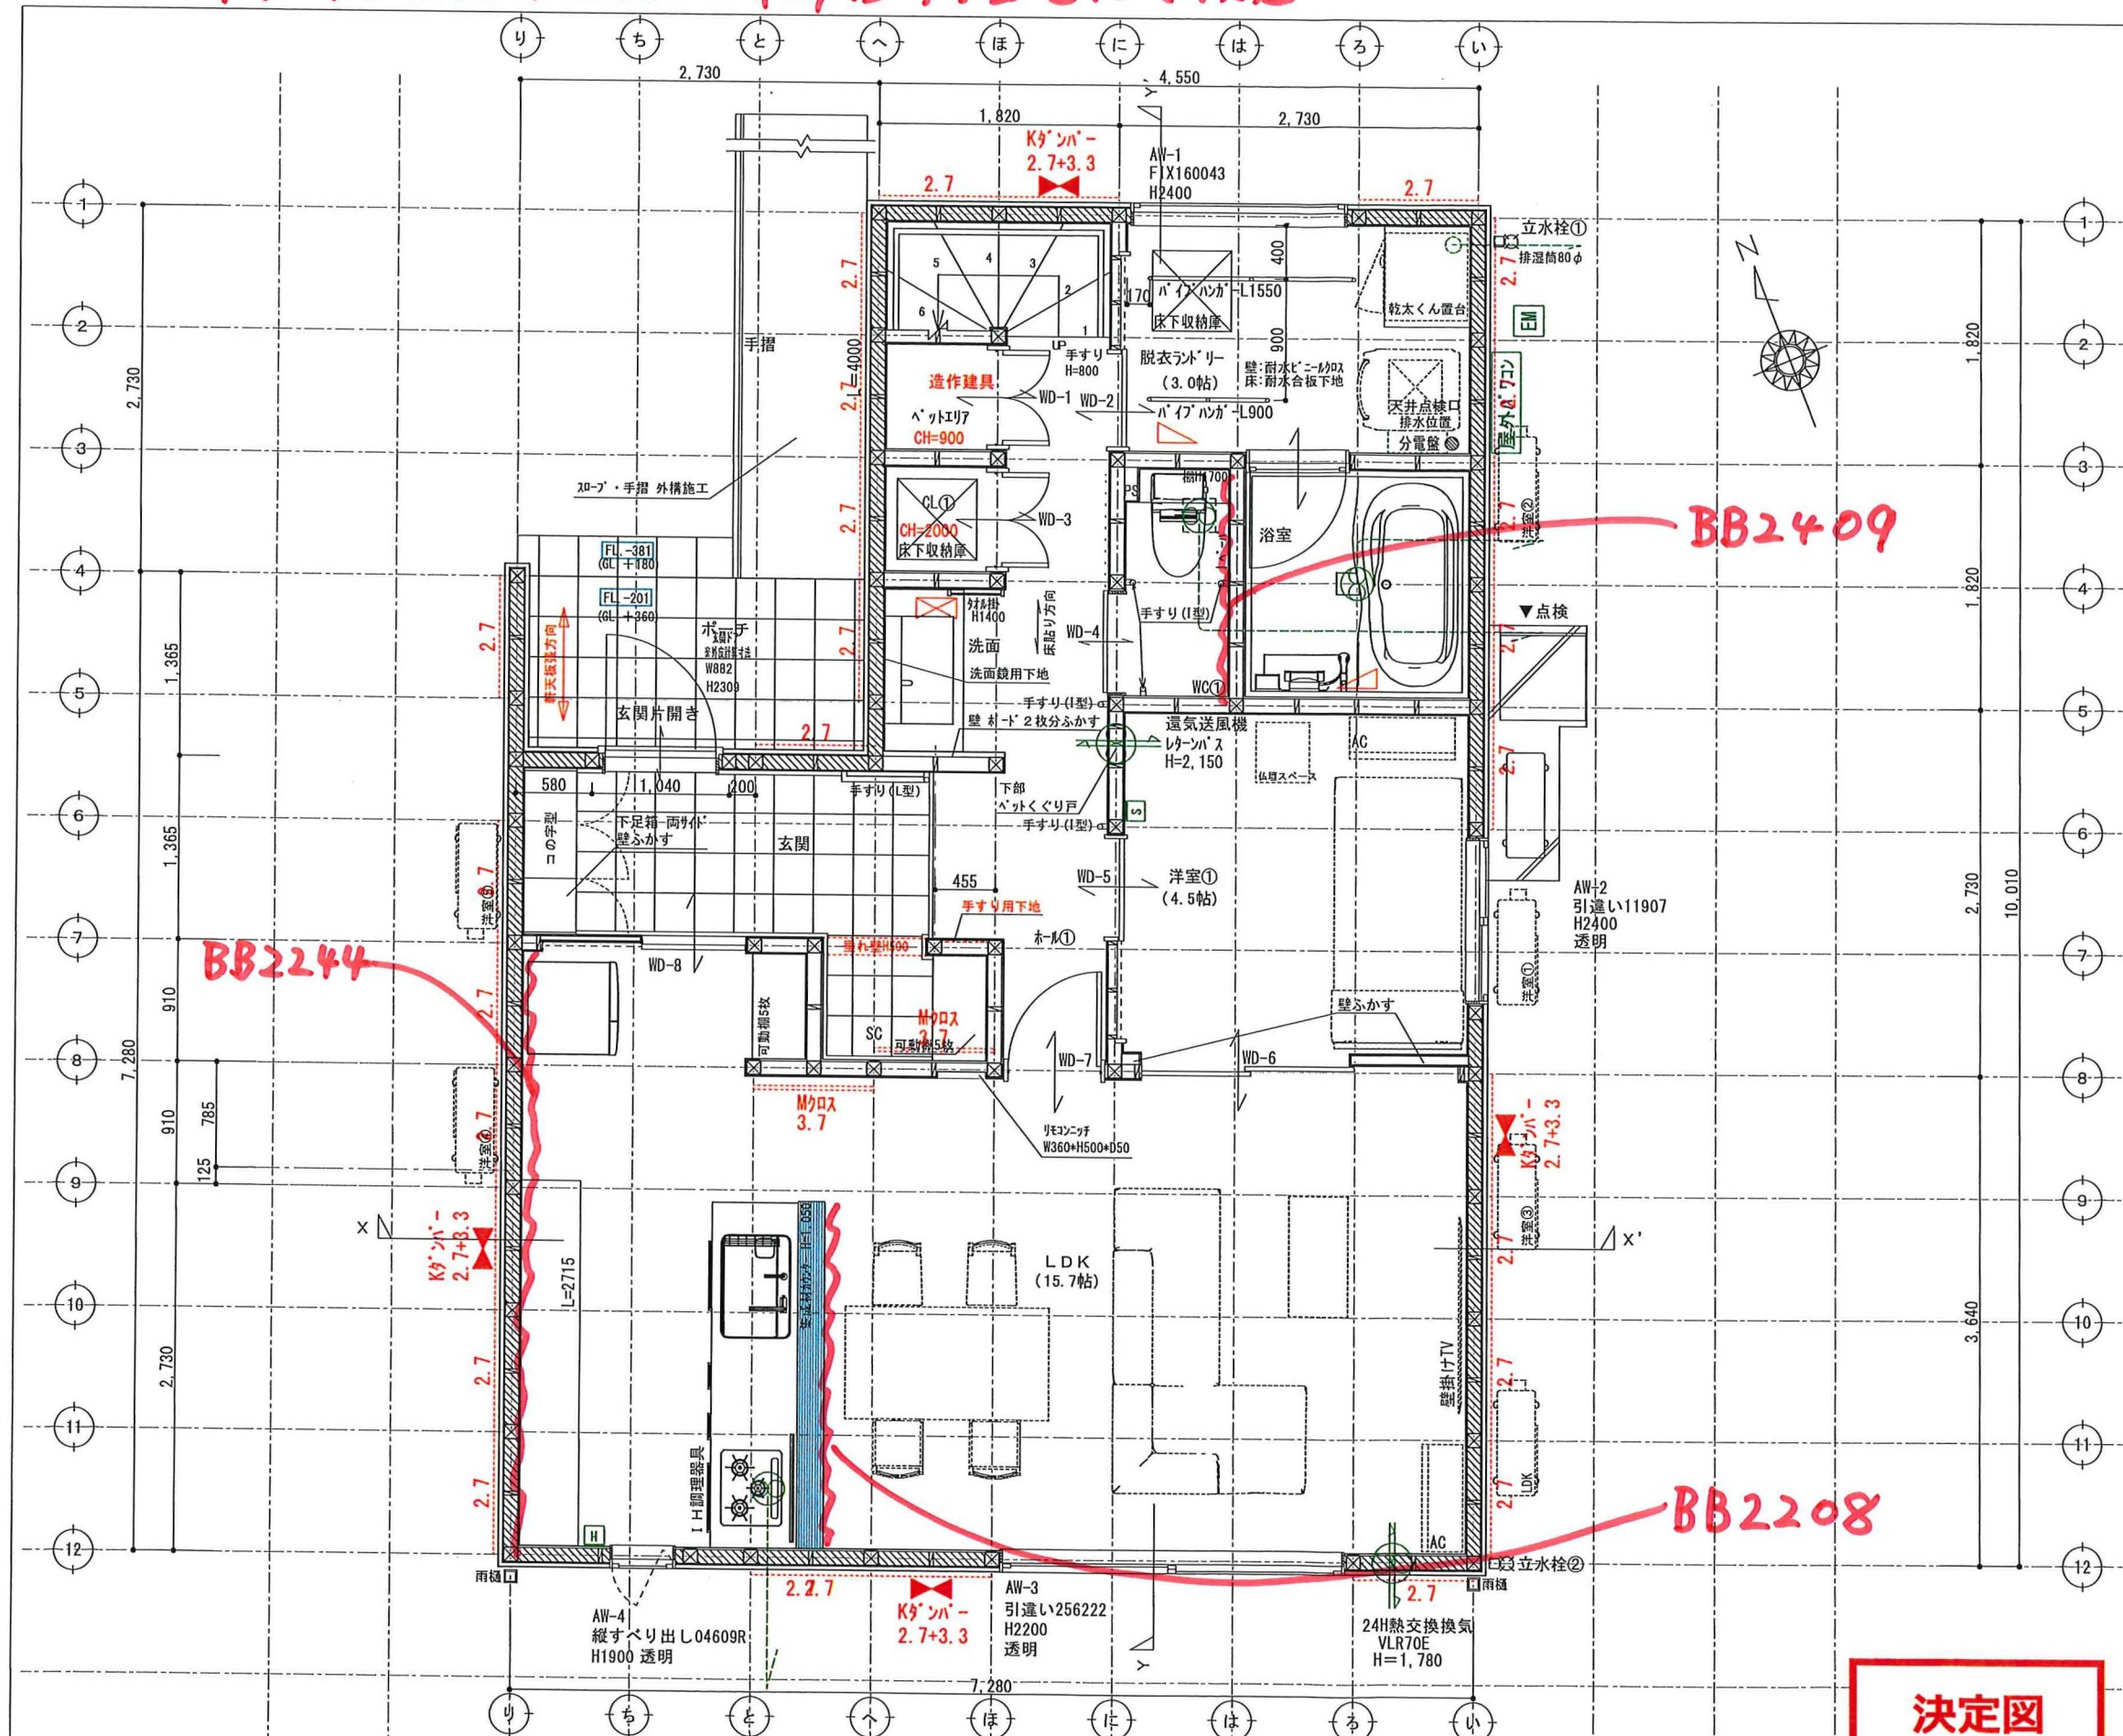

訂正

浜岡一級総合設計事務所
一級建築士事務所 静岡県知事登録第 (10)2441 号
一級建築士 大臣登録第 365879 号 西原利昌

PG HOUSE

株式会社 LIFE FUND InDesign office
事務所登録 (2) 第7595号 一級建築士登録 第179770号 鈴木 達男
〒432-8023 静岡県浜松市中央区鴨江3丁目70番23号

一級建築士事務所


年月日
2025.11.3
縮尺
1/50

件名
中村悦久様 裕子様邸 新築工事
図名
1階平面図

設計	IC	工事	図番
酒井		青島	3-1

2Fアクセントクロス 12/15打合せにて決定

G2

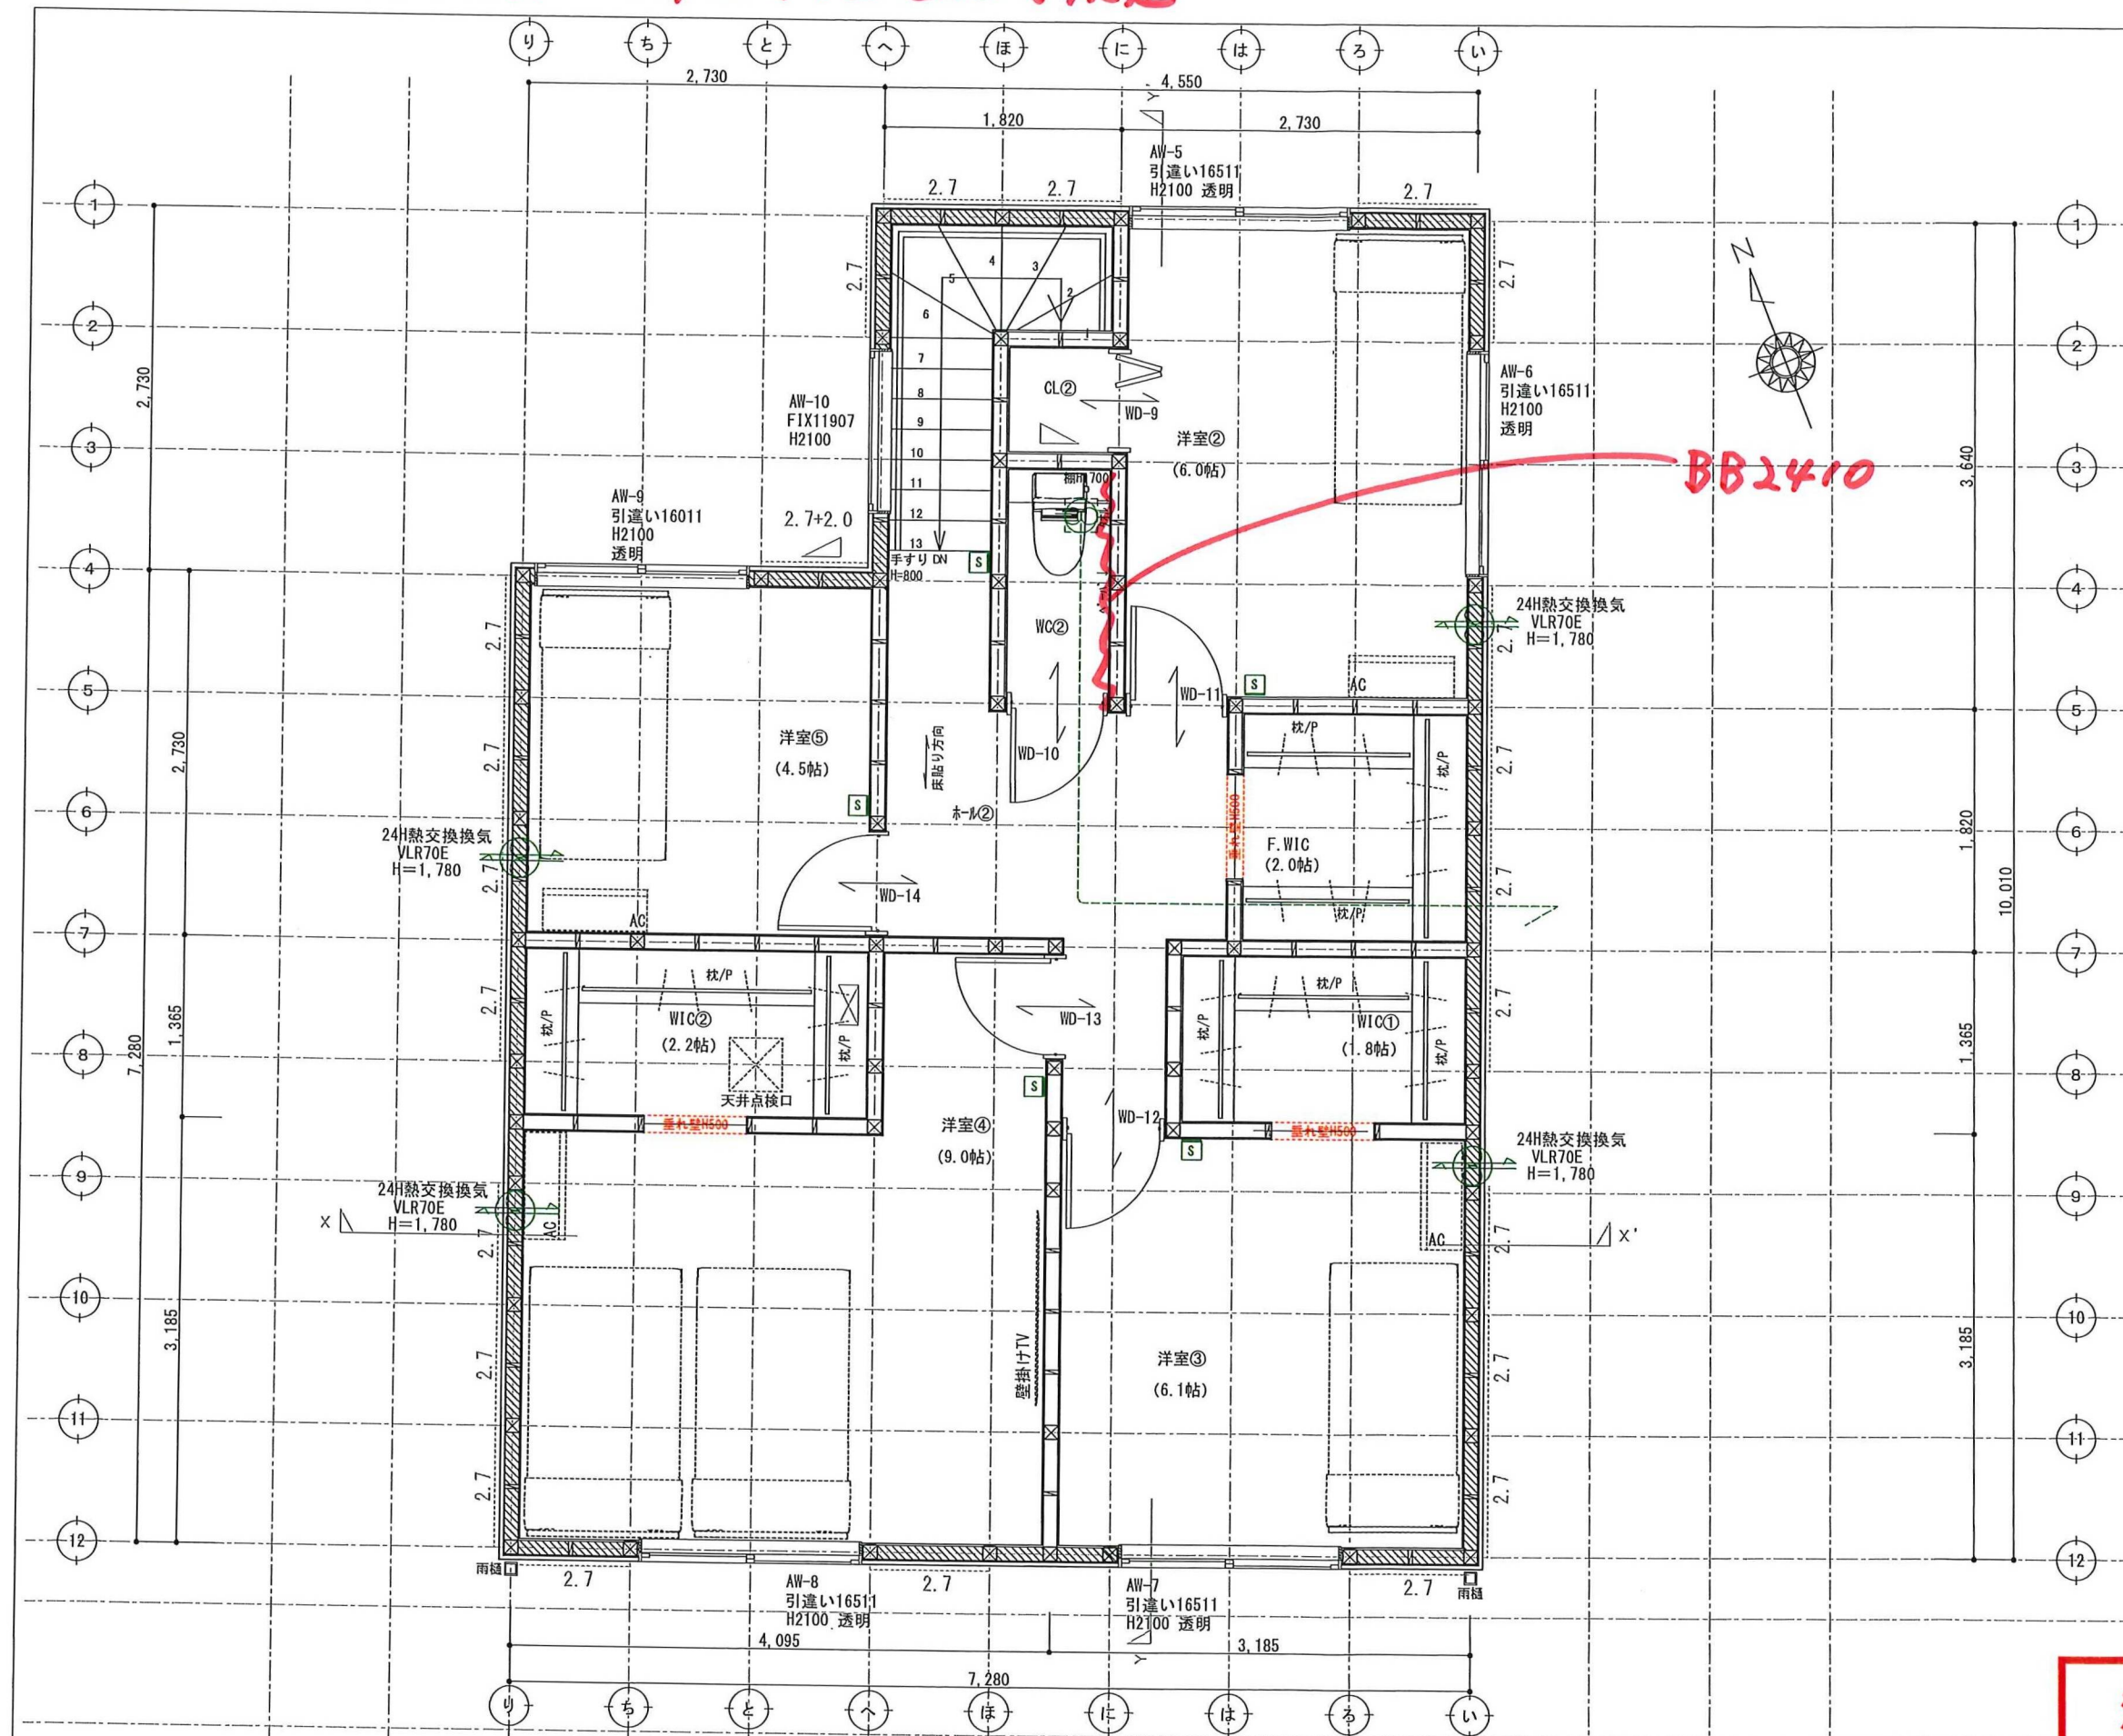

壁付け 住宅用火災報知器			数量
[H] 熱感知	電池式(単独型)		1
	露出型		
壁付け 住宅用火災報知器			数量
[S] 煙感知	電池式(単独型)		1
	露出型		

- ※ 煙感知器は壁・梁より600mm以上離す
壁に取付ける場合、
天井から150mm以上500mm以内離す
換気扇・エアコン吹出口から1500mm以上離す
- ※ 全室LED照明とする。
- ※ 標準天井高さ2,400
- ※ 特記無きガラスは型ガラス

* 凡例

- ☒ 管柱 (105×105)
- ◀▶ K' ヲハ- (3.30倍 FRM-0641)
- △ 片筋違い (2.00倍 45×90)
(例 左:柱脚 右:柱頭)
- ⊗ たすき掛筋違い (4.00倍 45×90)
- 構造用合板 (2.70倍)
(t=9 3/4" EXN/A-N)
- △ 床点検口
- ⊗ 天井点検口
- ⊕ 換気扇
- ⊕ 熱交換換気扇VLR-70

アドバンスシリーズ		
スマートデザイン (外部)		
凡例	1	コンセント 1ヶ所
①	2	コンセント 2ヶ所
②	3	コンセント 3ヶ所
①ET	1ヶ所	コンセント1ヶ所接地ターミナル付
②ET	2ヶ所	コンセント2ヶ所接地ターミナル付
①WP		コンセント 防水型
②WP		エアコン用コンセント
③WP		200V用コンセント
④WP		節電入換プレート
●	3	スイッチ 3割スイッチ
●	4	スイッチ 4割スイッチ
●		直結電源
⊕TV		テレビ取出口
⊕TEL		電話取出口 (テレホンガイド)
⊕LAN		LAN取出口 (テレホンガイド)
⊕		壁照明
⊕		リモコン (給湯関係・ルフロ)
⊕		メーター
⊕		分電盤
⊕		チャイム

- ※ACコンセント天井付け
- ※TVアンテナ工事
- ※スイッチはFL+1100、コンセントはFL+200

決定図