

■ 仕 様				■ HEAT20 G2	
断熱工事		■ 床:ネオフォーム t90		■ 土間床等の外周:スタイロフォームAT t50	
		■ 壁:アクアフォームLITE吹付 t90		■ 天井:アクファフォームLITE吹付 t220	
床下換気		■ 基礎パッキン JOTO (玄関・UB周り:気密基礎パッキン)			
防虫防蟻		■ 土壌処理・木部 ガントナーMC			
■ 外 部 仕 上 表				■ 22条地域	
部位		仕上・仕様・メーカー		色番・品番	
屋根		■ ガルバリウム鋼板(t0.35)UK立平 ニスクカラーPro GH 軒先通気金物 日本住環境株式会社【REV-15】		GHK01 Sブラック	
パラペット笠木		■ なし			
破風・鼻隠		■ なし			
雨樋	(軒樋)	■ Panasonic サーフeskエアFS-I型		ブラック	
	(縦樋)	■ Panasonic S30角樋		ブラック	
軒天	屋根軒	■			
	ポーチ軒	■ ニチハ軒天5 木目調 910×1820×5		ミディアム	
	バルコニー軒	■			
オーバーハング水切り		■ ガルバリウム鋼板 ※外壁合わせ JOTO:HF-A3550		ブラック	
外壁 通気金物(15mm) ※下地面材:タイガーEXハイパー 防火認定 PC030BE-4028	■メイン	Knewエクセレーヅ・シマンフラット 光セラ		ラント チタン モスグレー	
	■アクセントA	なし			
	■アクセントB	なし			
玄関ポーチ		■ 床 玄関に同じ		-	
基礎		■ 立上り巾木: モルタル刷毛引き		-	
基礎水切り金物		■ JOTO鋼板製 防鼠材付き水切り JOTO:WMF-N35		ブラック	
バルコニー	床・内壁	■ なし		-	
	笠木	■ なし			
外部建具		■ LIXIL EW(アルゴンガス高遮熱仕様LowEトリプルガラス クリア) ・SD、TSは、メーカー設定による。 ・オペレーター付サッシの場合は固定網戸とする ・グレモンハンドル式サッシの場合は可動網戸とする		外観 ブラック 内観 ホワイト ※樹脂パッキン・網戸付	
シャッター		■ なし			
軒天通気金物					
玄関扉		■ LIXIL ジエスタ2 K2仕様 LIXILファミロック タグキー×3 (電池式)		ドア型: M17 型 ドア色: ミディアムチェリー ハンドル: S型ハンドル 色 ブラック	
外部物干し金物		■			
換気フード	■ 局所換気扇(トイレ 浴室 キッチンフード) 防火ダンパー無		外気フード: ブラック		
	■ ダクトレス熱交換換気システム (日本スティーベル株式会社) VLR-70E		外気フード: B ブラック 室内パネル ホワイト		
	防火ダンパー無				

■ 構 造 概 要					
基礎	■ RCベタ基礎コンクリート				
通し柱・管柱	■ 構造用集成材 105×105		間柱	■ 集成材	
土台	■ 桧 105×105	大引き	■ 桧 90*90	筋交い	■ 構造用製材 火打梁 ■ 鋼製火打(当社基準により米松あり)
桁・梁	■ 構造用製材及び集成材			制震装置	■ Kダンパー (株)アイ・エム・エー
■ 設 備 装 着 品					
住宅設備	部位	メーカー	商品名 ※ 詳細は見積り、プレゼン参照	見積りNo.	(日付)
	キッチン	LIXIL	■ ND	見積り番号 : M25098825370-011-2	(日付) 2025.12.23
	バックカウンタ ※オプション	LIXIL	■ スライド`ストッカー×2、マルチスペース	見積り番号 : M25098825370-011-3	(日付) 2025.12.23
	浴室	LIXIL	■ AX1616 PGハウス標準仕様	見積り番号 : M25098825370-011-1	(日付) 2025.12.23
	1Fトイレ	LIXIL	■ ベーシアハーモJタイプ` 白 ● タオル掛け: なし(支給品取付) タンク手洗 無し ● 紙巻き器: なし(支給品取付)	見積り番号 : M25098825370-011-5	(日付) 2025.12.23
	2Fトイレ	LIXIL	■ ベーシアシャワートイレ 白 ● タオル掛け: なし(支給品取付) タンク手洗 有り ● 紙巻き器: なし(支給品取付)	見積り番号 : M25098825370-011-6	(日付) 2025.12.23
	洗面台	LIXIL	■ カスタムパニティ	見積り番号 : M25098825370-011-4	(日付) 2025.12.23
			その他 ● タオル掛け: なし(支給品取付)		
			永大産業 衣類乾燥機台(ホワイト)		
給排水設備	給湯器	■ エコキュート460L Panasonic Sシリーズ(高圧型)スタンダードモデル 追い焚きフルオート			
	排水	■ 下水			
	外水栓	■ 2 カ所 (平面図参照)	■ 外部立栓柱: PVC製 水栓柱12型【前澤化成工業】		
	外部ガーデンパン	■ 無し			
	その他	■ 洗濯機用単水栓 : 緊急止水弁付 ■ 洗濯機用排水: トラップ金物(標準) ■ 排水さや管(長期優良住宅仕様)			
ガス配管設備	■ あり(都市ガス) (配置図・平面図参照) ■ガス使用器具 乾太くん				
電気設備	インターホン	■ パナソニック VL-SE31XL			
	TVアンテナ	■ UHF + BS・110度CS／CSアンテナ [2K・4K・8K対応] ■ブラック ※電波状況によりホワイトになる可能性あり			
	エアコン	■ 設置場所:			
	ソーラー	■ あり(Qセルズ) 12 枚 5.28 KW Re.RISE-G3 440 (1722×1134×30)			
	※標準搭載	※メーカーのモデルチェンジ等で後継品に変更される可能性あり ■ 屋外パワコン エネルギーマネジメントシステム Cube J			
その他					

決定図

決定図

	浜 岡 一 級 総 合 設 計 事 務 所 一級建築士事務所 静岡県知事登録第 (10)2441 号 一級建築士 大臣登録第 365879 号 西原利昌	 株式会社 LIFEFUND InDesign office 一級建築士事務所 事務所登録 (2)第7595号 一級建築士登録 第179770号 鈴木 達男 〒432-8023 静岡県浜松市中央区鴨江3丁目70番23号	年 月 日	2025.12.21	件名	中村悦久様 裕子 様邸 新築工事		設計	IC	工務	図 番
			縮尺		図面	仕上表 1		酒井		青島	1-1


内 部 仕 上 表 (壁下地:石膏ボード12.5mm/天井下地:9.5mm) ※脱衣室:床合板特類 下地									
階		床	巾木	壁	品番	廻 縁	天 井	品番	特記事項
1F	ポーチ	LIXIL/パセオ300/PSO-BR 2							
	玄関	LIXIL/パセオ300/PSO-BR 2	ライン巾木(W)	ビニルクロス	SLP348	突付	ビニルクロス	SLP348	
	ホール①	イタ銘木フローラスティック12 ナラ桎3P	ライン巾木(W)	ビニルクロス	SLP348	突付	ビニルクロス	SLP348	
	LDK	イタ銘木フローラスティック12 ナラ桎3P	ライン巾木(W)	ビニルクロス	SLP348	突付	ビニルクロス	SLP348	カップボード背面 アクセント
	洋室①	イタ銘木フローラスティック12 ナラ桎3P	ライン巾木(W)	ビニルクロス	SLP348	突付	ビニルクロス	SLP348	
	洗面	イタ銘木フローラスティック12 ナラ桎3P	ライン巾木(W)	ビニルクロス	SLP348	突付	ビニルクロス	SLP348	
	脱衣ランドリー	フロアタイルt2.3 サンゲツIS-2070	H40ソフト巾木W97	ビニルクロス	SLP348	突付	ビニルクロス	SLP348	
	WC①	フロアタイルt2.3 サンゲツIS-2070	H40ソフト巾木W97	ビニルクロス	SLP348	突付	ビニルクロス	SLP348	東面 アクセント
2F	ホール②	イタ銘木フローラスティック12 ナラ桎3P	ライン巾木(W)	ビニルクロス	SLP348	突付	ビニルクロス	SLP348	
	洋室②	イタ銘木フローラスティック12 ナラ桎3P	ライン巾木(W)	ビニルクロス	SLP348	突付	ビニルクロス	SLP348	
	洋室③	イタ銘木フローラスティック12 ナラ桎3P	ライン巾木(W)	ビニルクロス	SLP348	突付	ビニルクロス	SLP348	
	洋室④	イタ銘木フローラスティック12 ナラ桎3P	ライン巾木(W)	ビニルクロス	SLP348	突付	ビニルクロス	SLP348	西面 アクセント
	WIC	イタ銘木フローラスティック12 ナラ桎3P	ライン巾木(W)	ビニルクロス	SLP348	突付	ビニルクロス	SLP348	
	FWIC	イタ銘木フローラスティック12 ナラ桎3P	ライン巾木(W)	ビニルクロス	SLP348	突付	ビニルクロス	SLP348	
	WC②	フロアタイルt2.3 サンゲツIS-2070	H40ソフト巾木W97	ビニルクロス	SLP348	突付	ビニルクロス	SLP348	東面 アクセント
物入・収納・CL etc		※接続する部屋と同仕様とする							

上框 ※	■ LIXILラシッサS 上框のみ30×150	色: クリエオーク
階段 KA階段で対応でき ない場合、オプション にてラシッサS階段	■ LIXIL KA 階段 段板: クリエオーク ラウンド手摺: クリエオーク 上段框: クリエオーク	ササラ: プレシヤスホワイト 蹴込板: プレシヤスホワイト 手摺金物: プレシヤスホワイト
窓枠	■ LIXIL スマート10(玄関以外) ※浴室ドア枠 フクビ3方枠	色: プレシヤスホワイト [ホワイト]
キッチン笠木 カウンター	■ ゴム集成カウンター(オスモカラー) 形状 I型	色: 3062フロアークリアmatt
天井点検口	■ 天井アルミ点検口枠 450角 TAN45BW	フクビ化学工業 ミルキーホワイト
床下収納庫	■ 高気密型床下点検口断熱型 (脱衣室)	SPF-R6060 城東テクノ 収納付 ライトグレー(LG)
トイレ棚	■ 1,2階トイレ D250	アートランバー棚(シェルホワイト)
室内物干し金物	■ シーリングパイプハンガー	L1550 × 1 L900 × 1
	■	色
下足入 プッシュタイプ	■ LIXILラシッサS サイズ: W1200 D400	色: クリエアイボリー 形状: コの字型ミラー付

支給品	■ 1,2階トイレ タオル掛け、紙巻き器 ■ 洗面台 タオル掛け ■ キッチン上部 オーデリック ペンダントライト×3
備考	※付框は(30×150)プレシャスホワイト 可動棚アートランバー色 シェルホワイト 棚受金物類は全てホワイト LIXIL L型手すり ラウンドタイプ 手摺棒、金物ともにフレッシュホワイト LIXIL I型手すり エントブラケット納め 手摺棒、金物ともにフレッシュホワイト ■洗面 三面鏡:ミラタップ スミス W1200 曇り止め、コンセント付き タイル:名古屋モザイク SF-692-RF-64 タイル目地:AMJ-P21 はい


[illegible]

	浜岡一級総合設計事務所	株式会社 LIFEFUND InDesign office 一級建築士事務所	年月日 2025.12.21	件名 中村悦久様 裕子 様邸 新築工事		設計	IC	工務	図番
	一級建築士事務所 静岡県知事登録第 (10)2441 号	事務所登録 (2) 第7595号 一級建築士登録 第179770号 鈴木 達男	縮尺	図面 仕上表 2		酒井		青島	1-2
	一級建築士 大臣登録第 365879 号 西原利昌	〒432-8023 静岡県浜松市中央区鶴江3丁目70番23号							

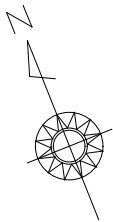

写真撮影方向. 2

写真撮影方向. 1

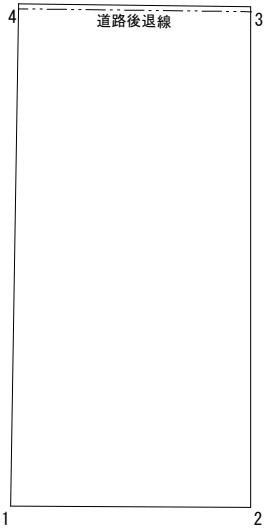

座標面積計算表



座標点	X _n (m)	Y _n (m)	(X _{n+1} - X _{n-1})・Y _n
1	0.000	0.000	0.000000
2	9.526	-0.051	-0.481814
3	9.526	19.621	-180.920422
4	0.305	19.732	-187.967293
敷地面積 184.68 m ²		倍面積	369.369529
		面積	184.684764

※この図面は、申請地及び周囲の現況を簡易測量し、利用状況及び公図形状から仮で求積した図面です。関係土地所有者及び道路管理者による境界立会・確認のもと作成された境界確定図ではありません。


決定図

- ※斜線適法
- ※雨水排水は道路側溝へ放流
- ※道路後退線内に既設工作物等はありません
- ※道路後退線内に工作物等を新設しません
- ※盛土規制法の規制に係る切土、盛土は無い

配置図 S = 1/100

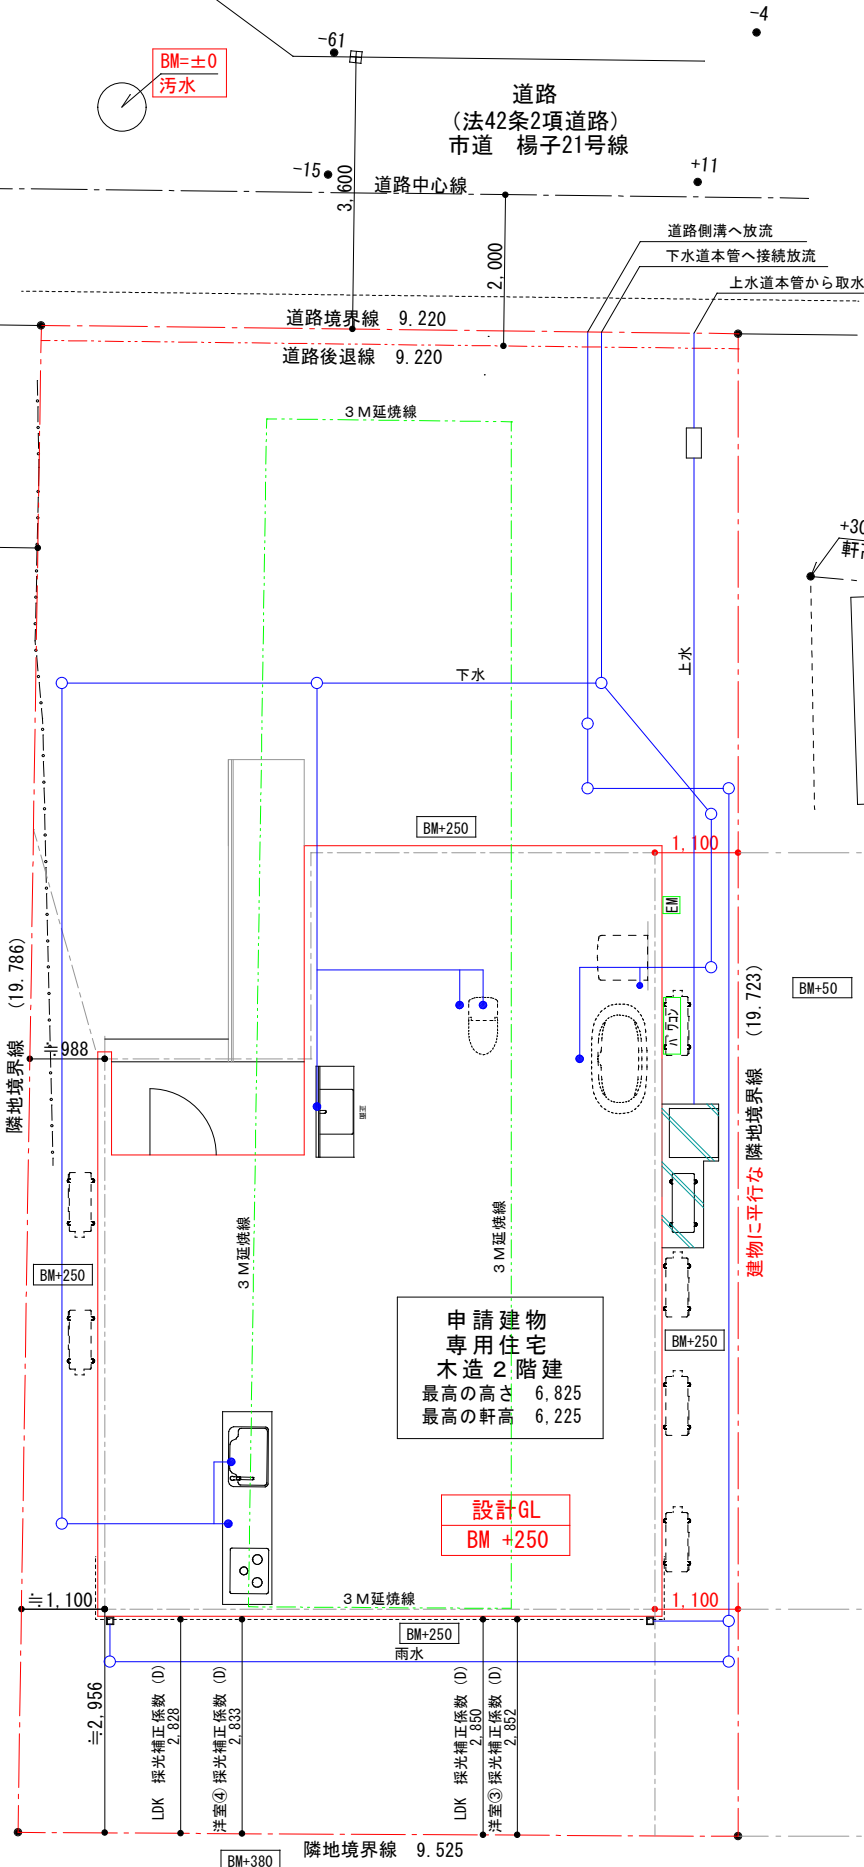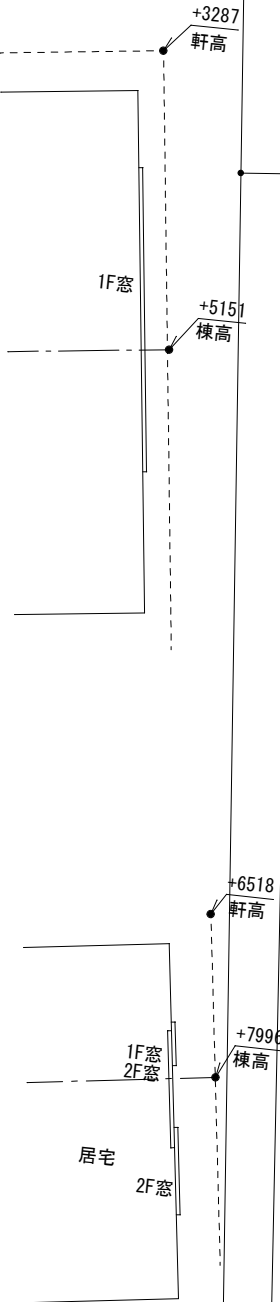


※5M延焼線は敷地全体にかかる

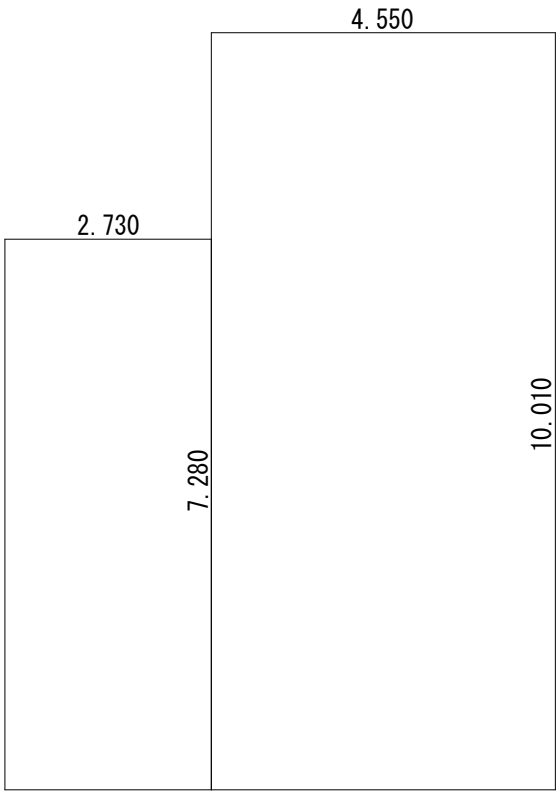

建築面積求積図 S=1/100

建築面積求積表


番号	計算式	(m)	面積 (㎡)
Ⓐ	2.730 × 7.28		19.8744
Ⓑ	4.550 × 10.010		45.5455
合計			65.4199 65.41 (19.7坪)

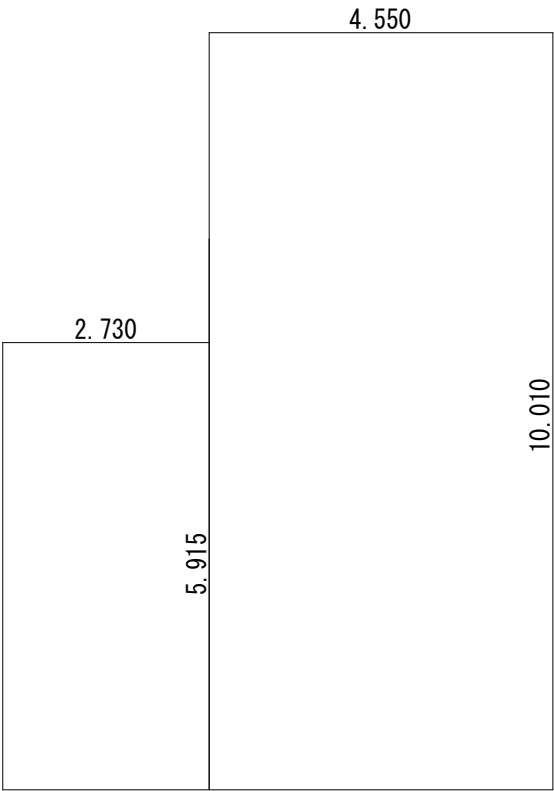

1階床面積図 S=1/100

1階床面積求積表

番号	計算式	(m)	面積 (㎡)
①	2.730 × 5.915		16.1480
②	4.550 × 10.010		45.5455
合計			61.6935 61.69 (18.6坪)

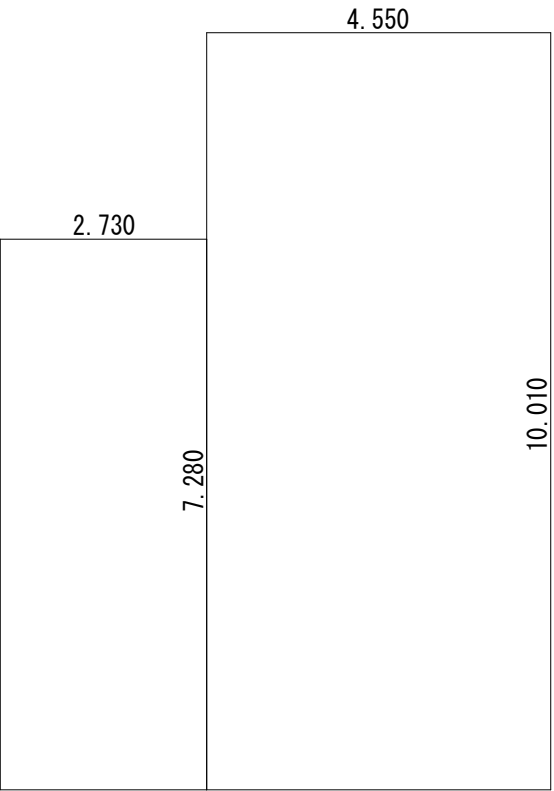

2階床面積図 S=1/100


2階床面積求積表

番号	計算式	(m)	面積 (㎡)
③	2.730 × 7.280		19.8744
④	4.550 × 10.010		45.5455
合計			65.4199 65.41 (19.7坪)

延べ床面積表

	番号	(m)	面積 (㎡)
1階床面積	① ②		61.69
2階床面積	③ ④		65.41
合計			127.11 (38.4坪)

決定図

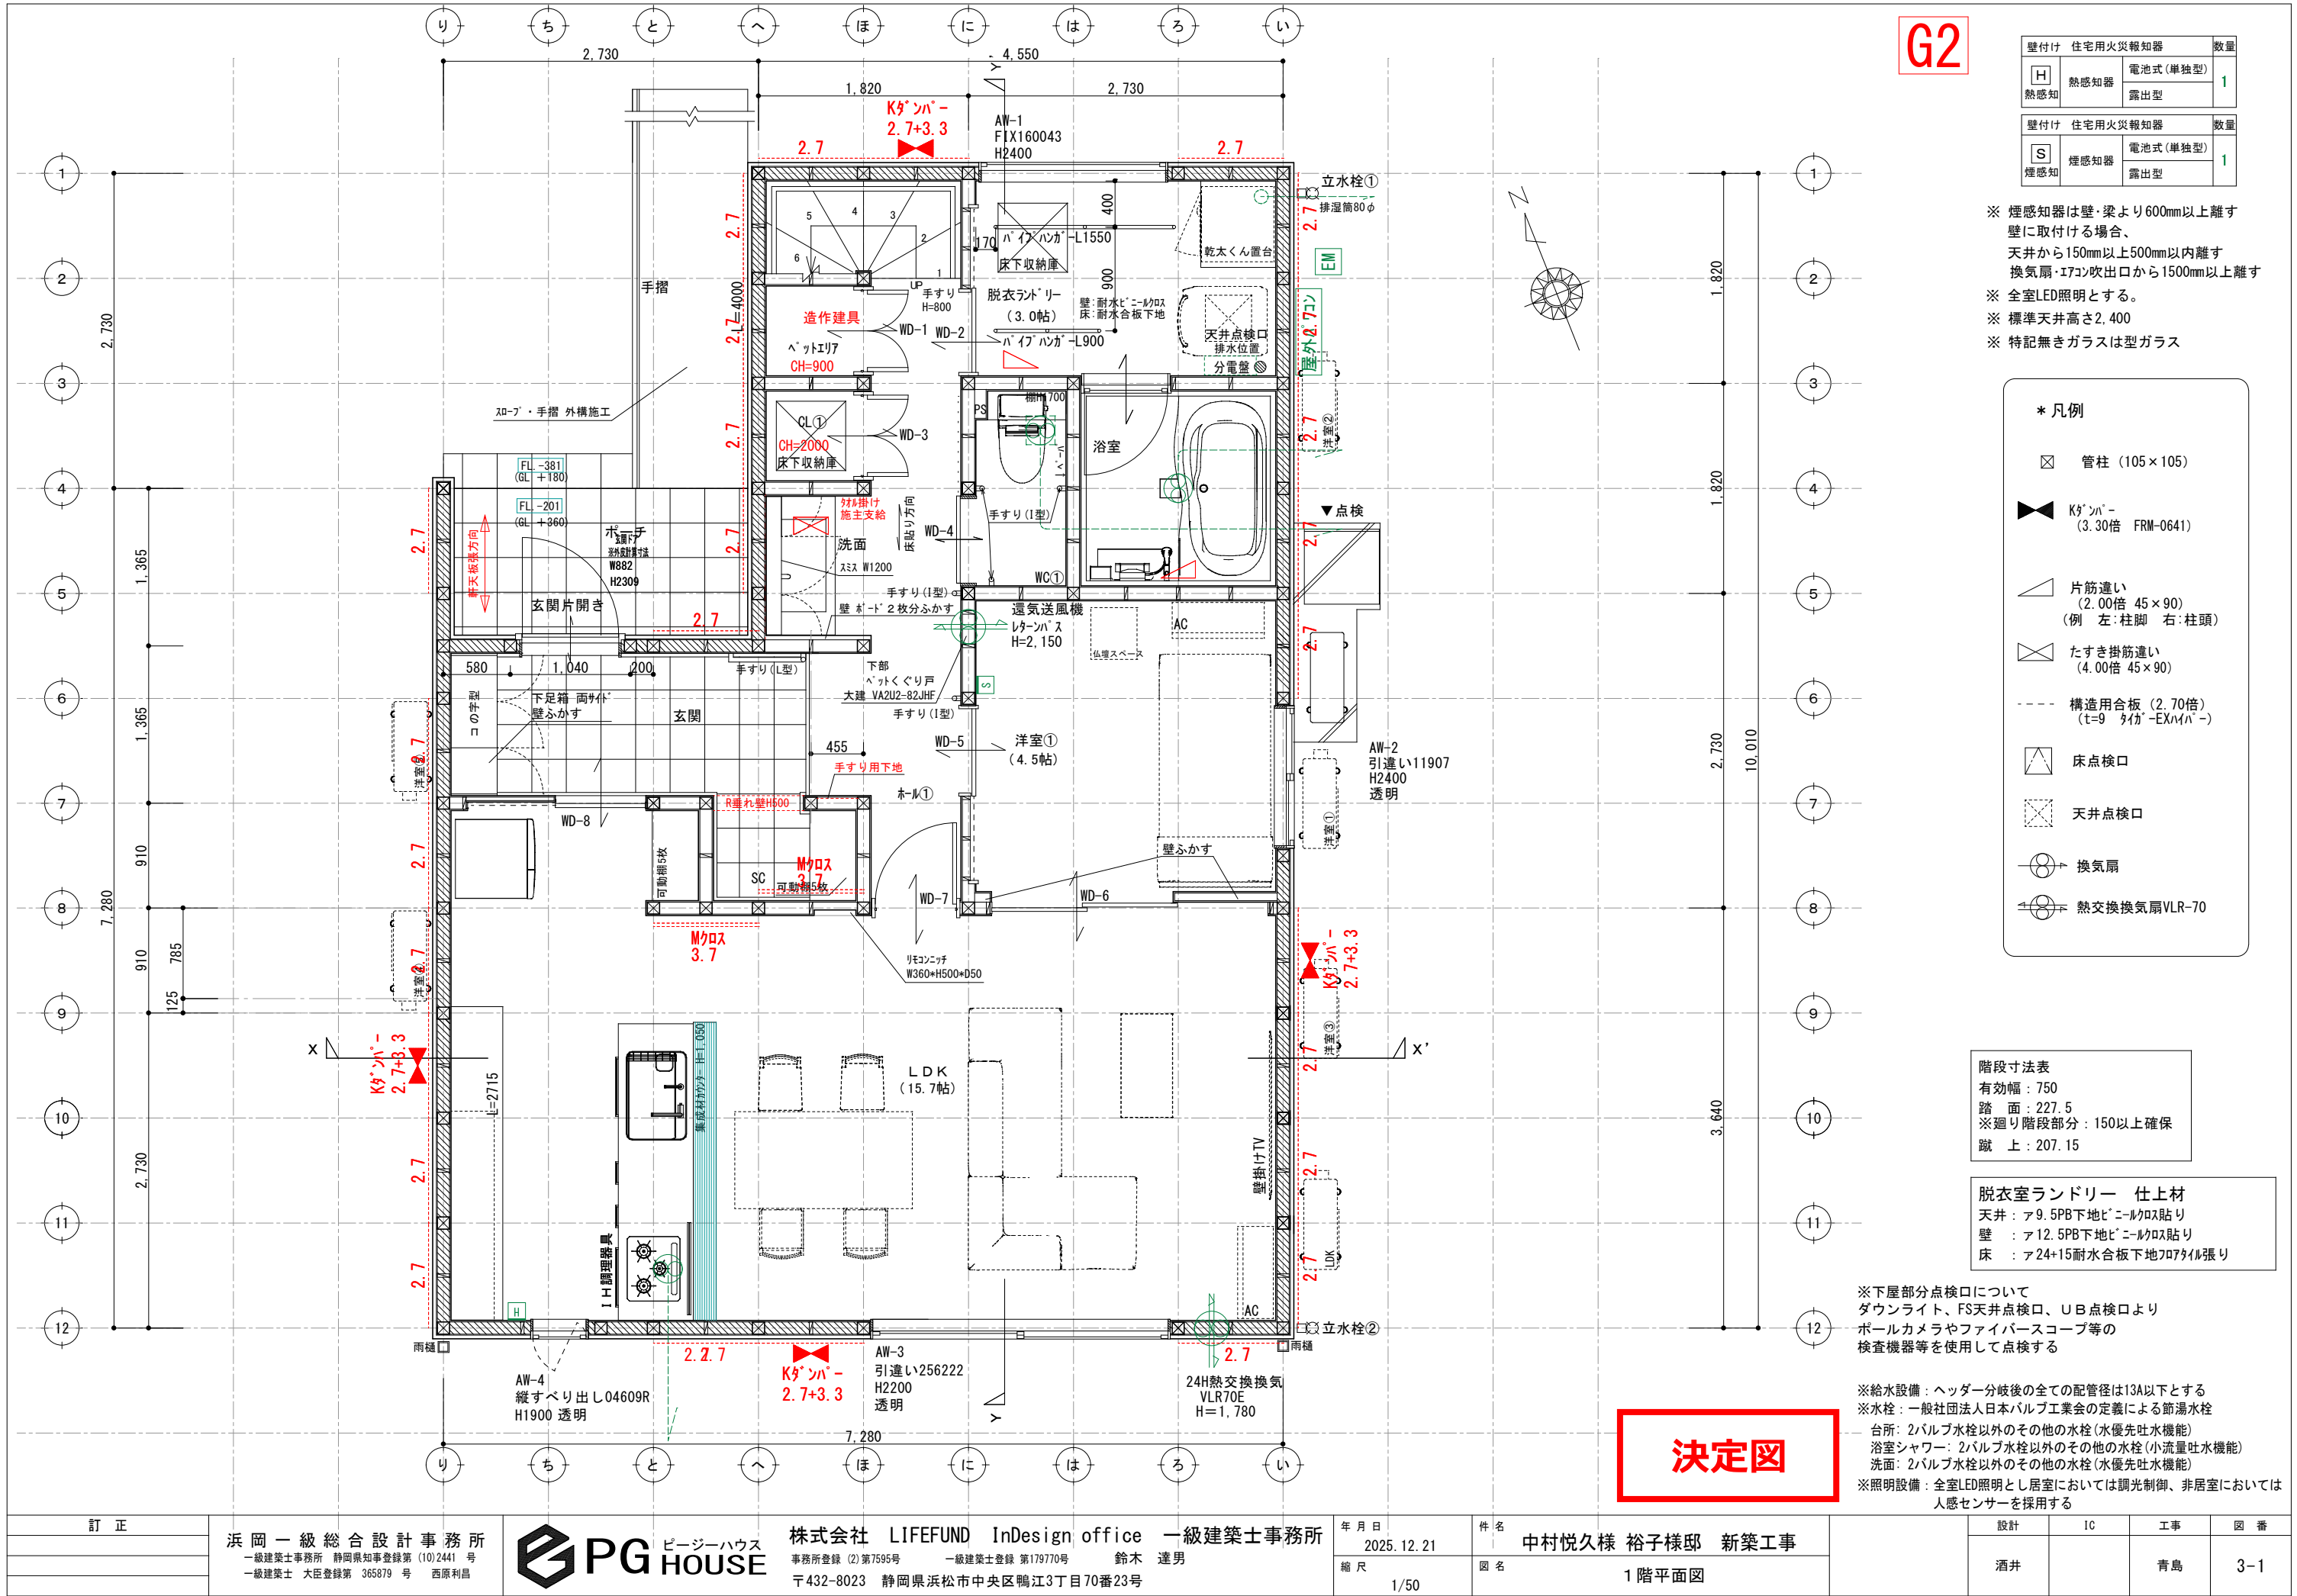

G2

壁付け 住宅用火災報知器			数量
熱感知	H	電池式(単独型)	1
		露出型	
壁付け 住宅用火災報知器			数量
煙感知	S	電池式(単独型)	1
		露出型	

※ 煙感知器は壁・梁より600mm以上離す
壁に取付ける場合、
天井から150mm以上500mm以内離す
換気扇・エアコン吹出口から1500mm以上離す
※ 全室LED照明とする。
※ 標準天井高さ2,400
※ 特記無きガラスは型ガラス

* 凡例

- 管柱 (105×105)
- Kタンパ (3.30倍 FRM-0641)
- 片筋違い (2.00倍 45×90)
(例 左:柱脚 右:柱頭)
- たすき掛筋違い (4.00倍 45×90)
- 構造用合板 (2.70倍)
(t=9 9材 EXハイパ)
- 床点検口
- 天井点検口
- 換気扇
- 熱交換換気扇 VLR-70

階段寸法表	
有効幅	750
踏面	227.5
※廻り階段部分: 150以上確保	
蹴上	207.15

脱衣室ランドリー 仕上材	
天井	ア9.5PB下地ビニルクロス貼り
壁	ア12.5PB下地ビニルクロス貼り
床	ア24+15耐水合板下地フロアタイル張り

※下屋部分点検口について
ダウンライト、FS天井点検口、UB点検口より
ポールカメラやファイバースコープ等の
検査機器等を使用して点検する

※給水設備: ヘッダー分岐後の全ての配管径は13A以下とする
※水栓: 一般社団法人日本バルブ工業会の定義による節湯水栓
台所: 2バルブ水栓以外のその他の水栓(水優先吐水機能)
浴室シャワー: 2バルブ水栓以外のその他の水栓(小流量吐水機能)
洗面: 2バルブ水栓以外のその他の水栓(水優先吐水機能)
※照明設備: 全室LED照明とし居室においては調光制御、非居室においては
人感センサーを採用する

決定図

G2

壁付け 住宅用火災報知器			数量
H 熱感知	電池式(単独型)		
	露出型		
壁付け 住宅用火災報知器			数量
S 煙感知	電池式(単独型)		8
	露出型		

※ 煙感知器は壁・梁より600mm以上離す
壁に取付ける場合、
天井から150mm以上500mm以内離す
換気扇・エアコン吹出口から1500mm以上離す
※ 全室LED照明とする。
※ 標準天井高さ2,400
※ 特記無きガラスは型ガラス


* 凡例

- ☒ 管柱 (105×105)
- ◀▶ Kダクト (3.30倍 FRM-0641)
- △ 片筋違い (2.00倍 45×90)
(例 左:柱脚 右:柱頭)
- ⊗ たすき掛筋違い (4.00倍 45×90)
- 構造用合板 (2.70倍)
(t=9 3枚 -EXハイバ-)
- △ 床点検口
- ⊗ 天井点検口
- ↻ 換気扇
- ↻ 熱交換換気扇VLR-70


アドバンスシリーズ		
スマートデザイン (外部)		
凡例	1	コンセント 1ヶ所
①	2	コンセント 2ヶ所
②	3	コンセント 3ヶ所
③	1ET	コンセント1ヶ所接地ターミナル付
④	2ET	コンセント2ヶ所接地ターミナル付
⑤	WP	コンセント 防水型
⑥		エアコン用コンセント
⑦		200V用コンセント
⑧	WP	防雨入線プレート
⑨		スイッチ
⑩	3	3路スイッチ
⑪	4	4路スイッチ
⑫		直結電源
⑬	TV	テレビ取出口
⑭	TEL	電話取出口 (テレホンガイド)
⑮	LAN	LAN取出口 (テレホンガイド)
⑯		壁照明
⑰		リモコン (給湯関係・ルフロ)
⑱		メーター
⑲		分電盤
⑳		チャイム

※ACコンセント天井付け
※TVアンテナ工事
※スイッチはFL+1100、コンセントはFL+200

決定図


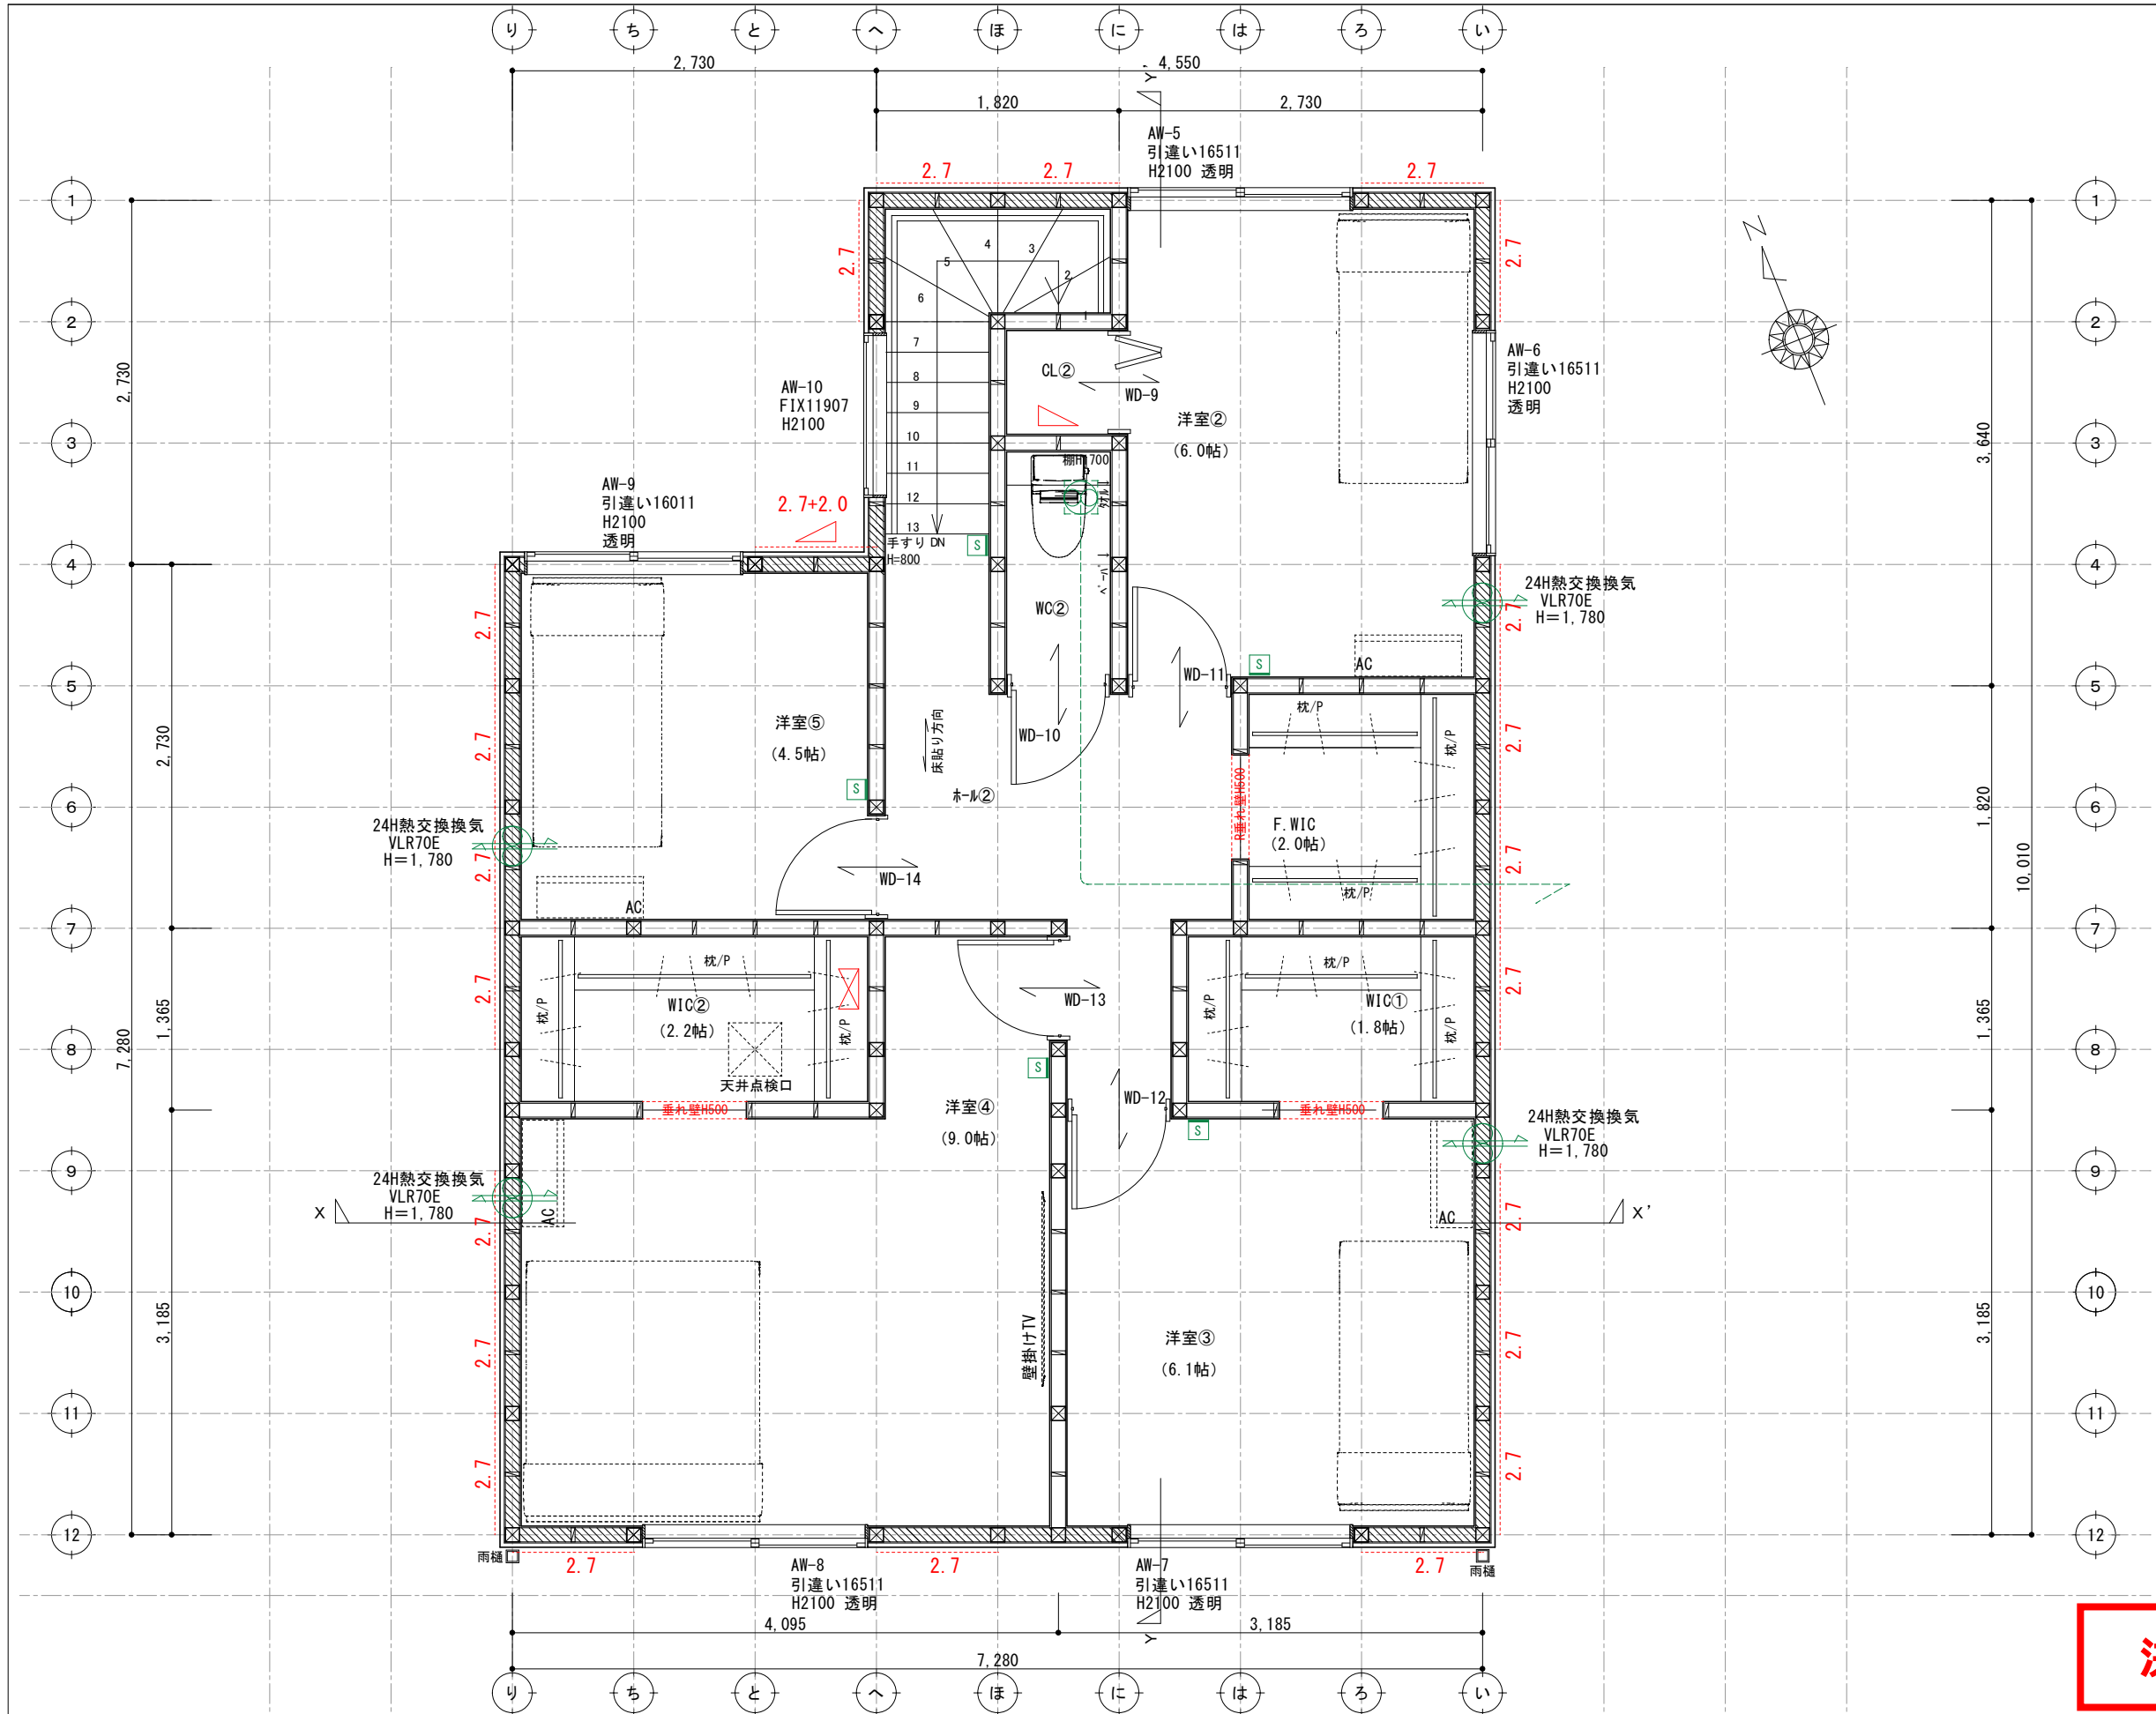


GX住宅 (Cube J付)
太陽光あり

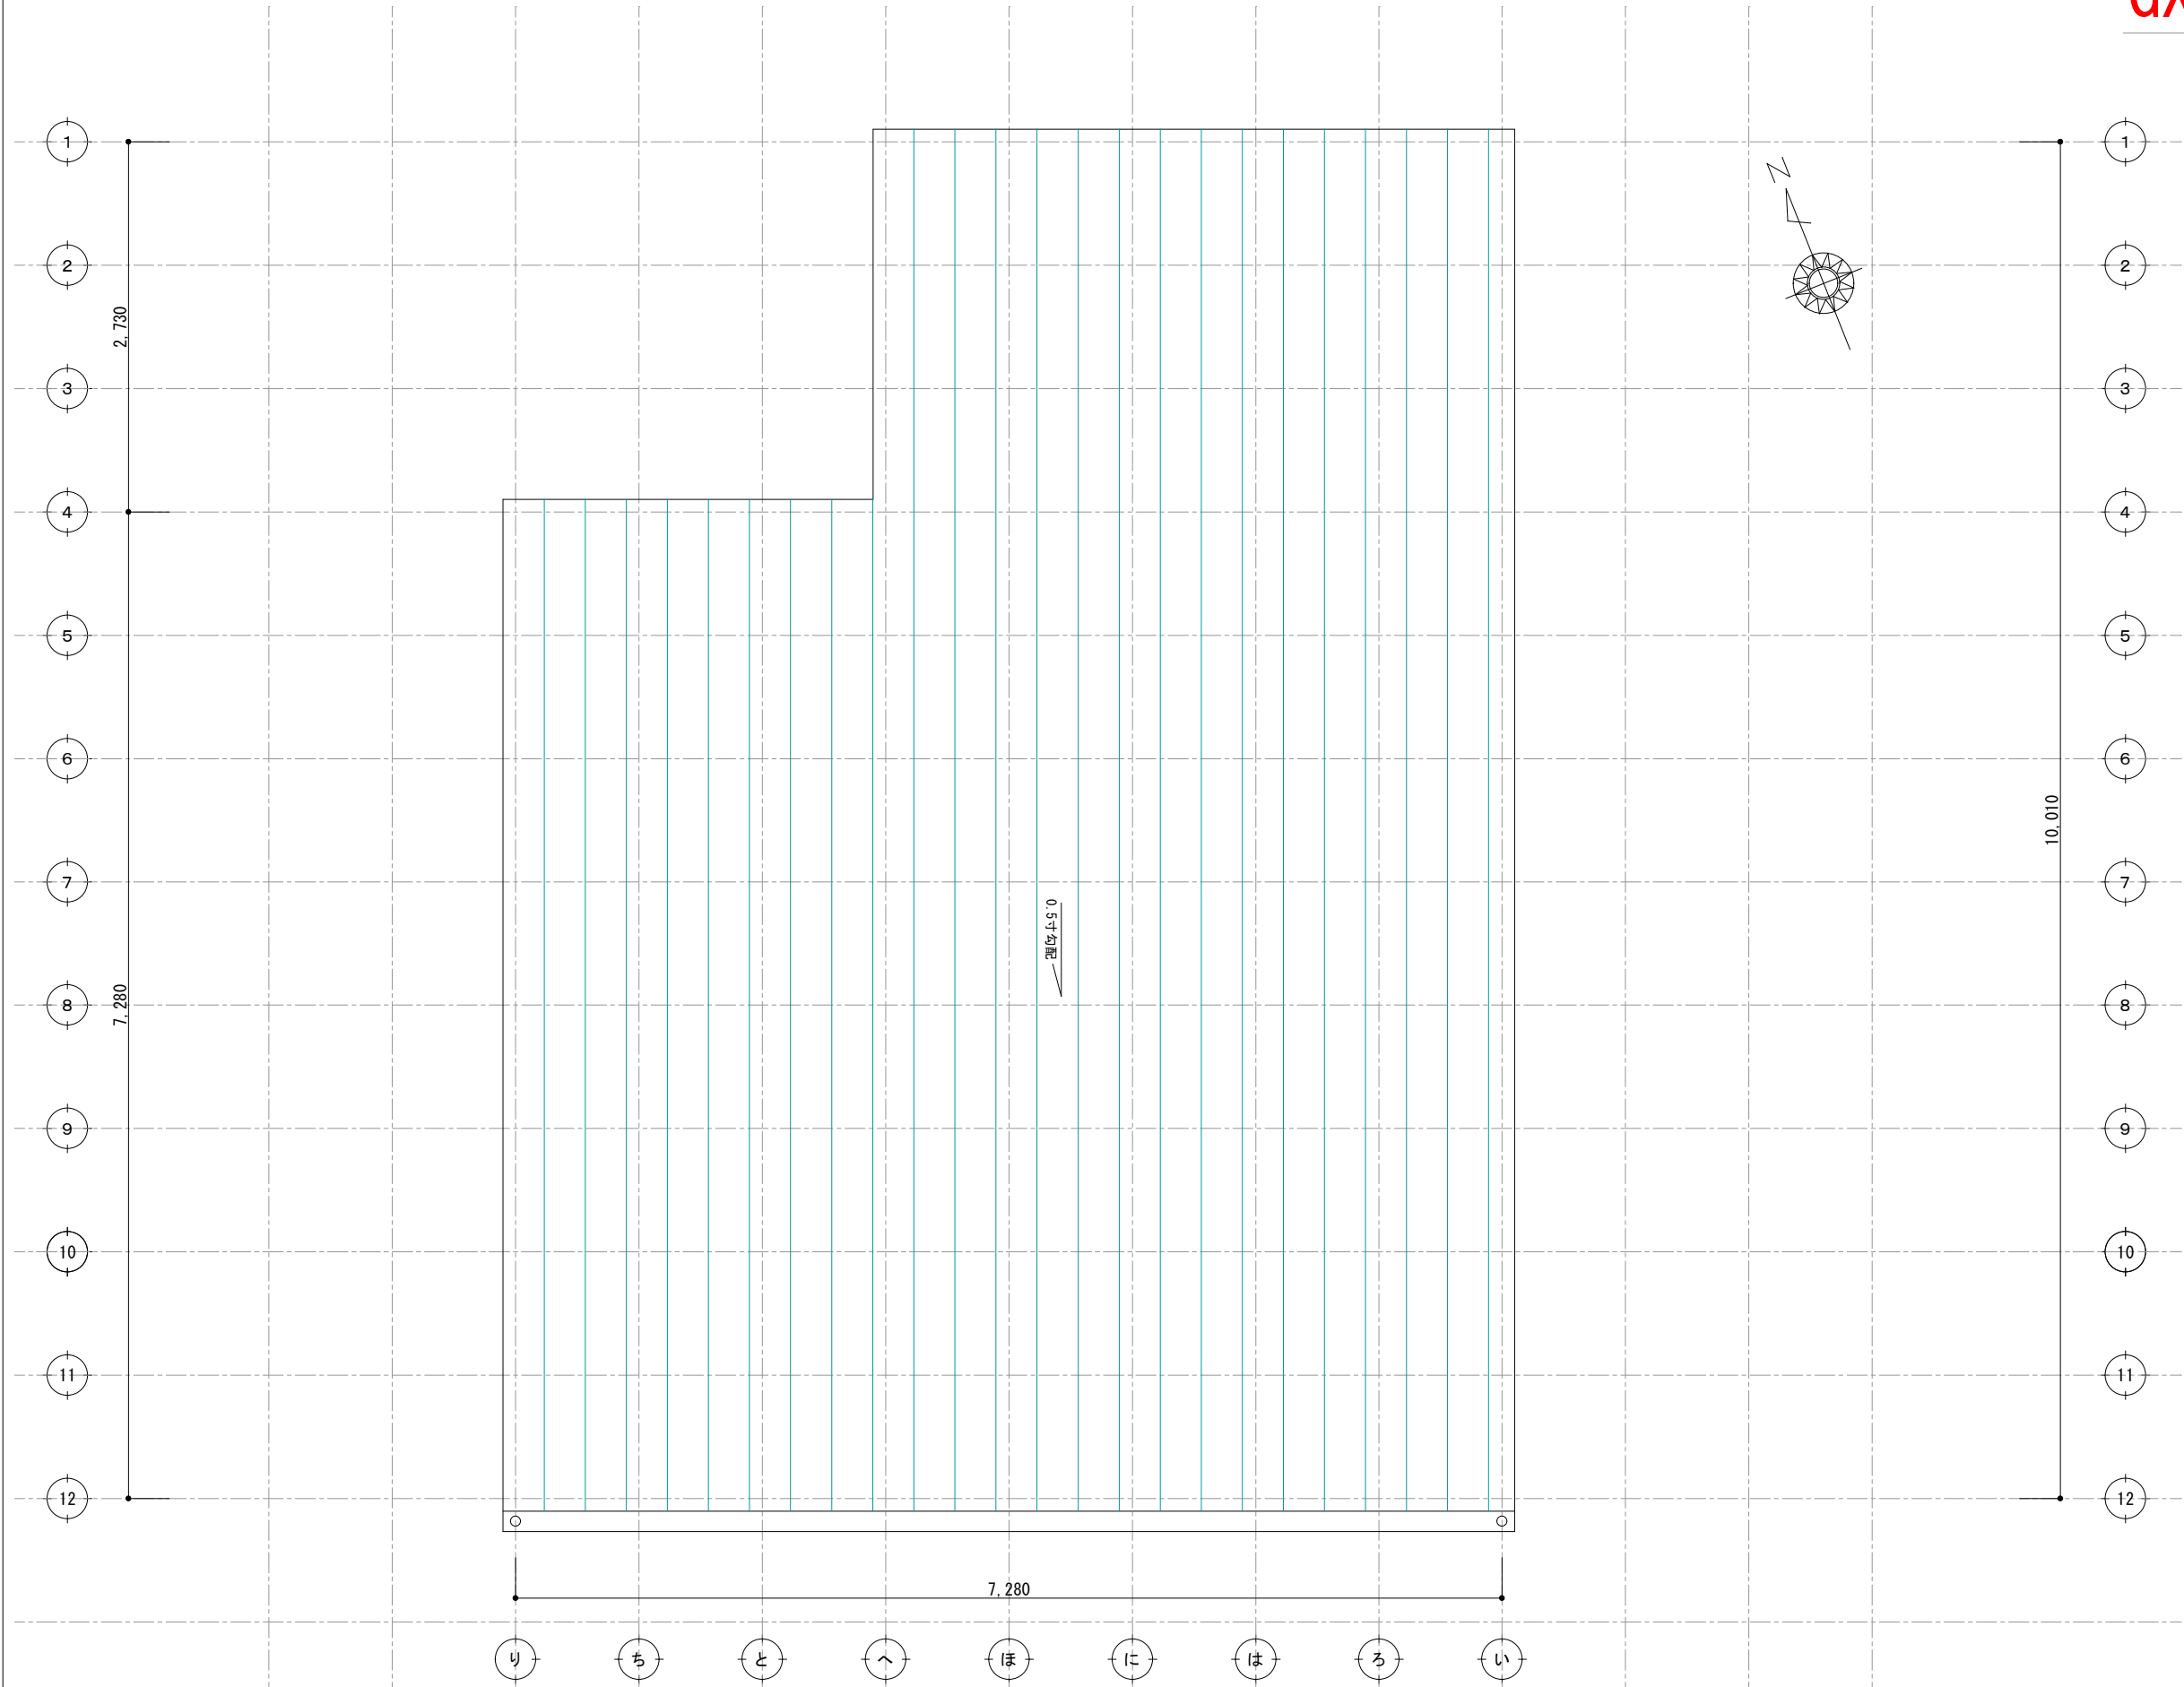

決定図

訂 正	浜 岡 一 級 総 合 設 計 事 務 所 一級建築士事務所 静岡県知事登録第 (10)2441 号 一級建築士 大臣登録第 365879 号 西原利昌		株式会社 LIFEFUND InDesign office 一級建築士事務所 事務所登録 (2) 第7595号 一級建築士登録 第179770号 鈴木 達男 〒432-8023 静岡県浜松市中央区鴨江3丁目70番23号	年 月 日	件 名		設計	IC	工事	図 番
				2025. 11. 3	中村悦久様 裕子様邸 新築工事		酒 井	青 島	3-3	
				縮 尺	図 名					
				1/100	屋根伏図					

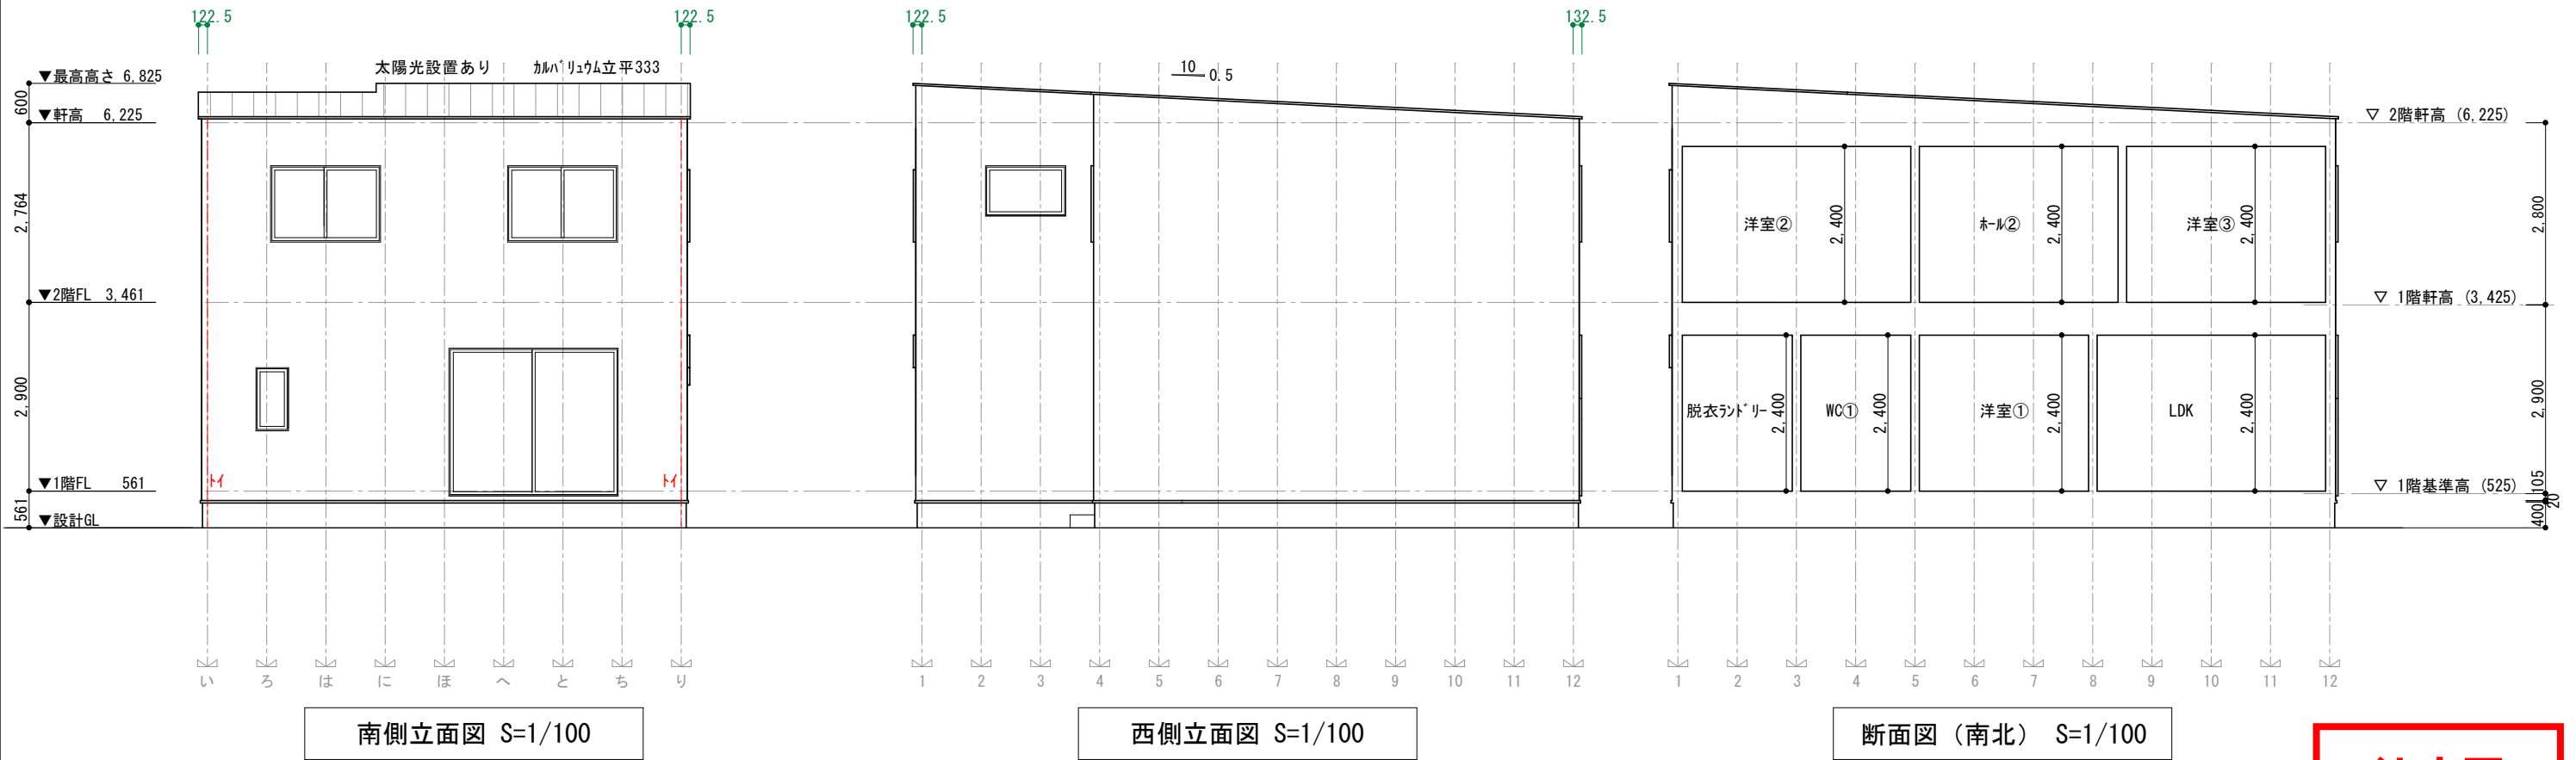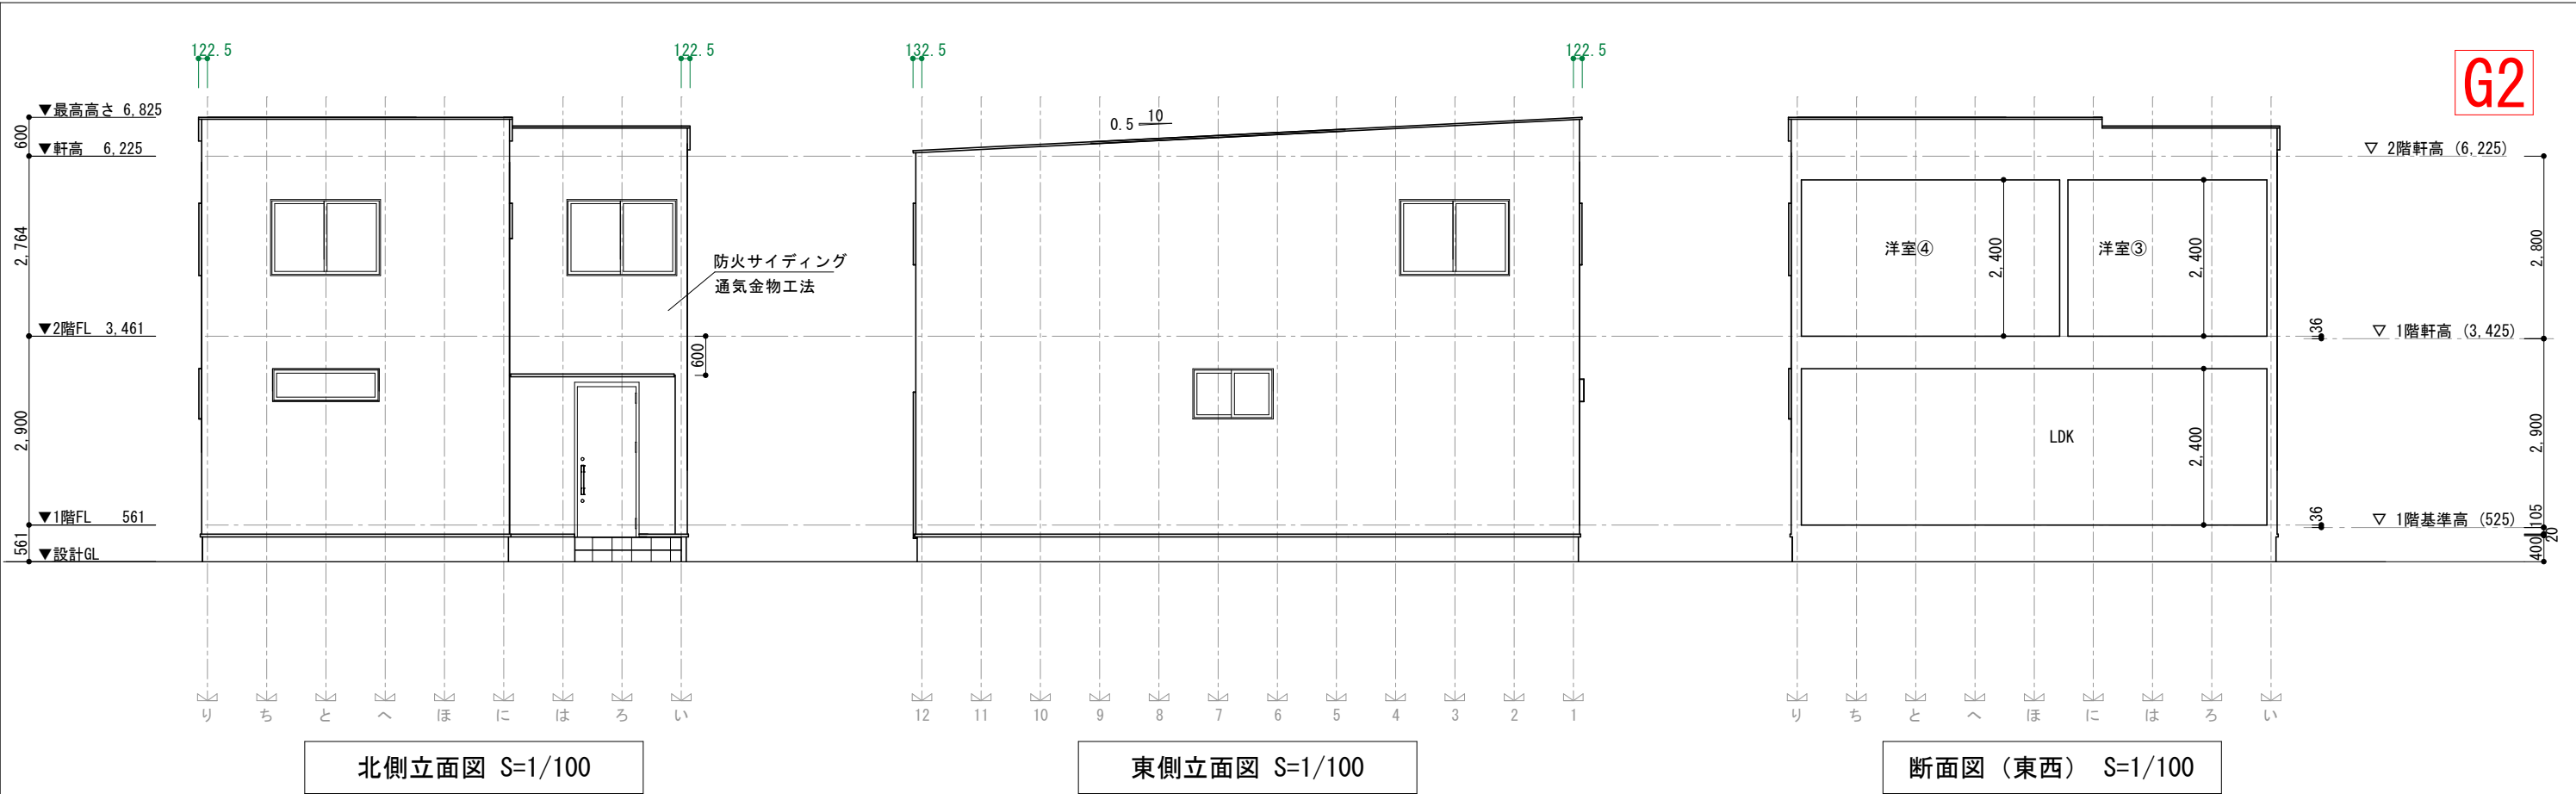

訂 正	浜 岡 一 級 総 合 設 計 事 務 所 一級建築士事務所 静岡県知事登録第 (10)2441 号 一級建築士 大臣登録第 365879 号 西原利昌			 PG HOUSE	株式会社 LIFEFUND InDesign office 一級建築士事務所 事務所登録 (2) 第7595号 一級建築士登録 第179770号 鈴木 達男 〒432-8023 静岡県浜松市中央区鴨江3丁目70番23号		年 月 日 2025. 11. 3	件 名 中村悦久様 裕子様邸 新築工事		設計	IC	工事	図 番
							縮 尺 1/100	図 名 立面図		酒井		青島	4




株式会社 LIFEFUND InDesign office 一級建築士事務所
事務所登録 (2) 第7595号 一級建築士登録 第179770号 鈴木 達男
〒432-8023 静岡県浜松市中央区鴨江3丁目70番23号




年月日
2025. 11. 3
縮尺
1/100

件名
中村悦久様 裕子様邸 新築工事
図名
立面図

設計
酒井
IC
青島
工事
青島
図番
4

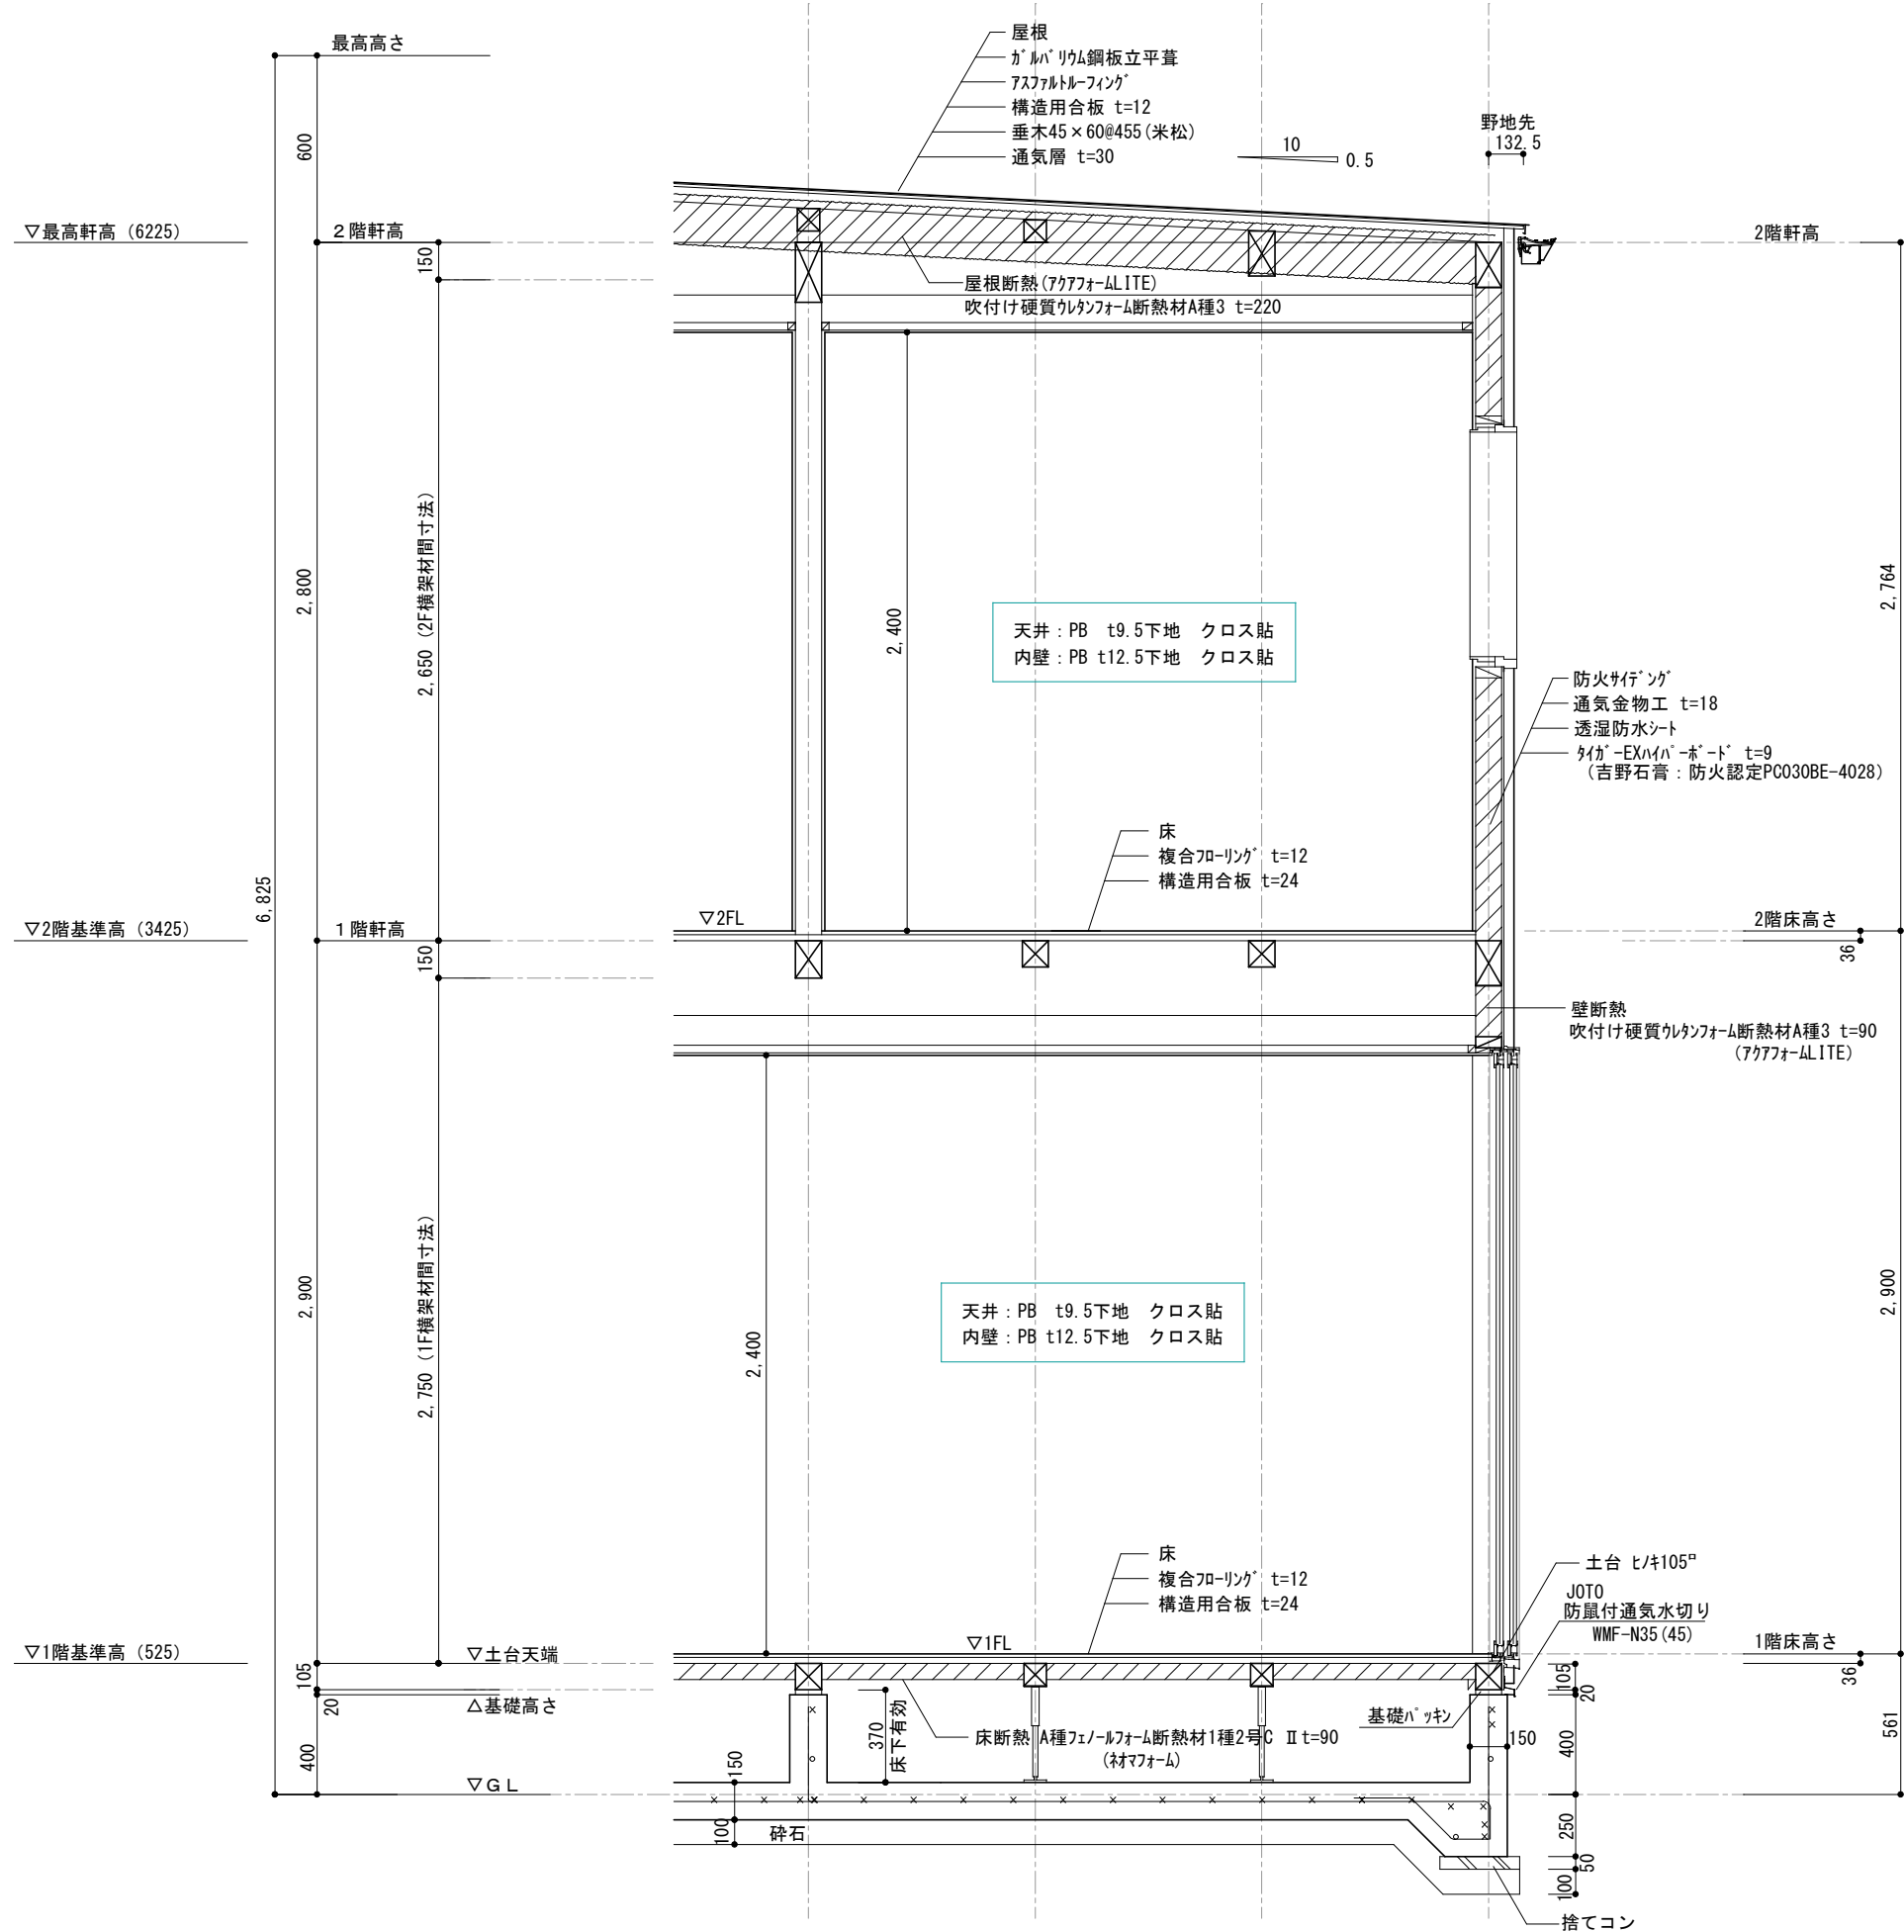


決定図

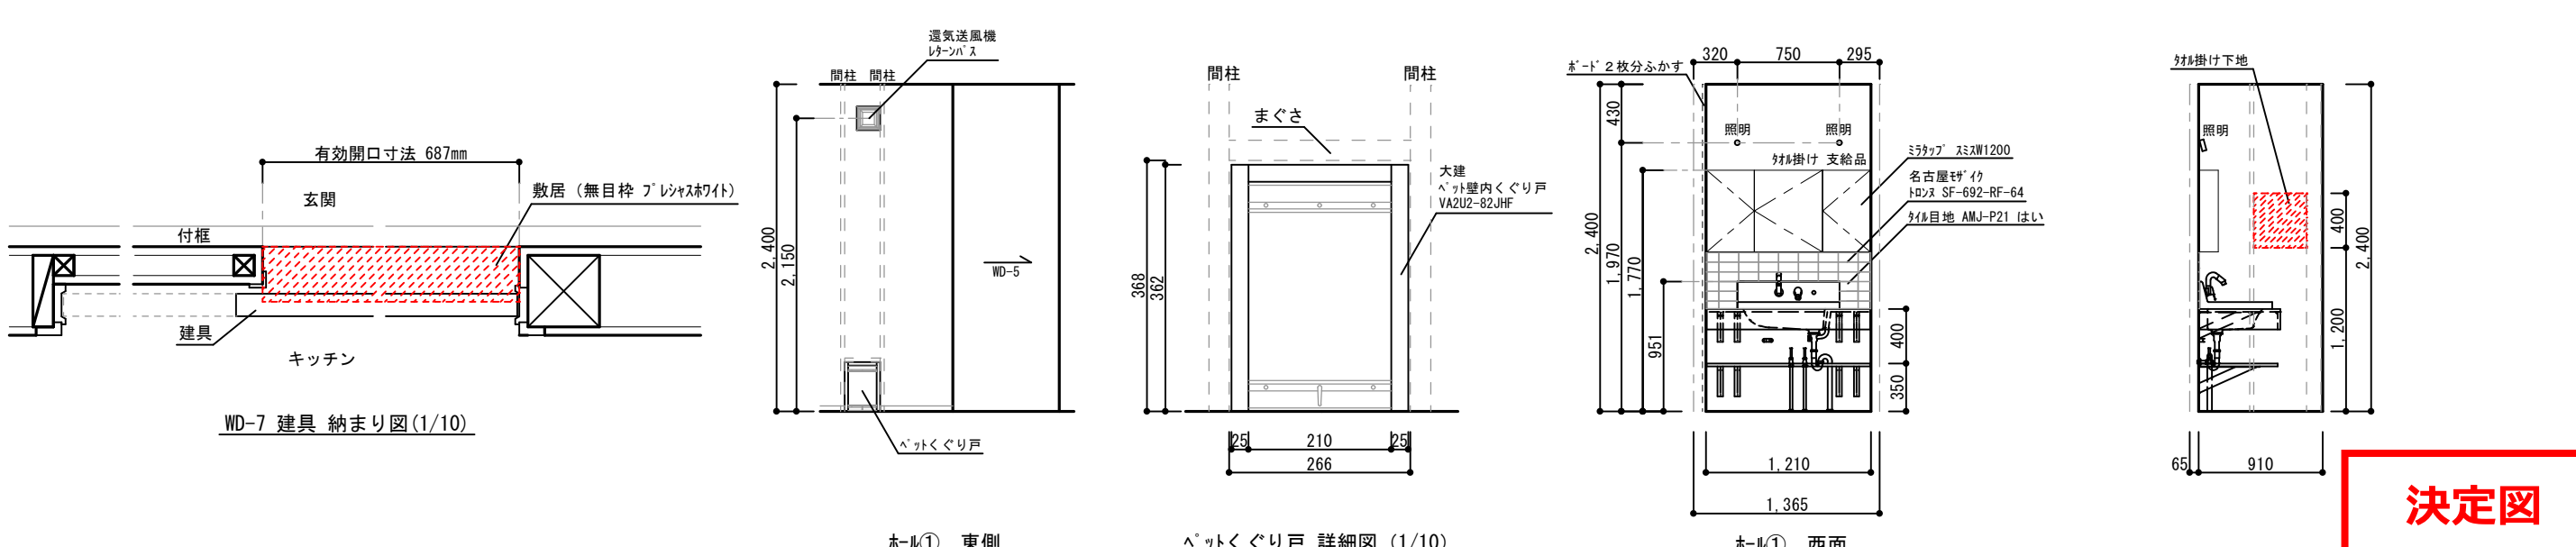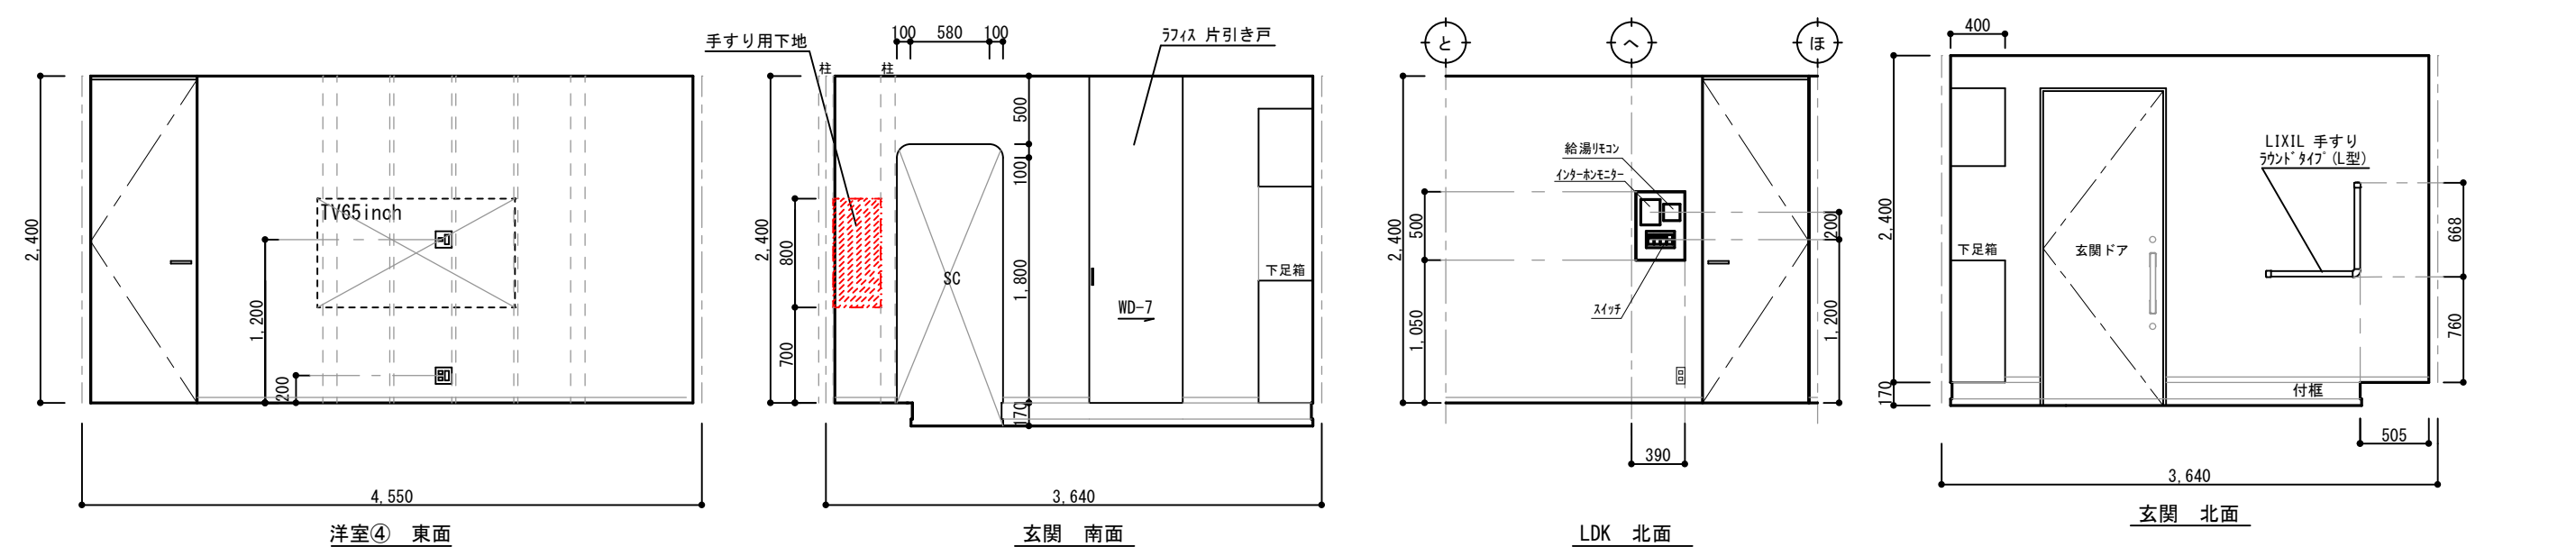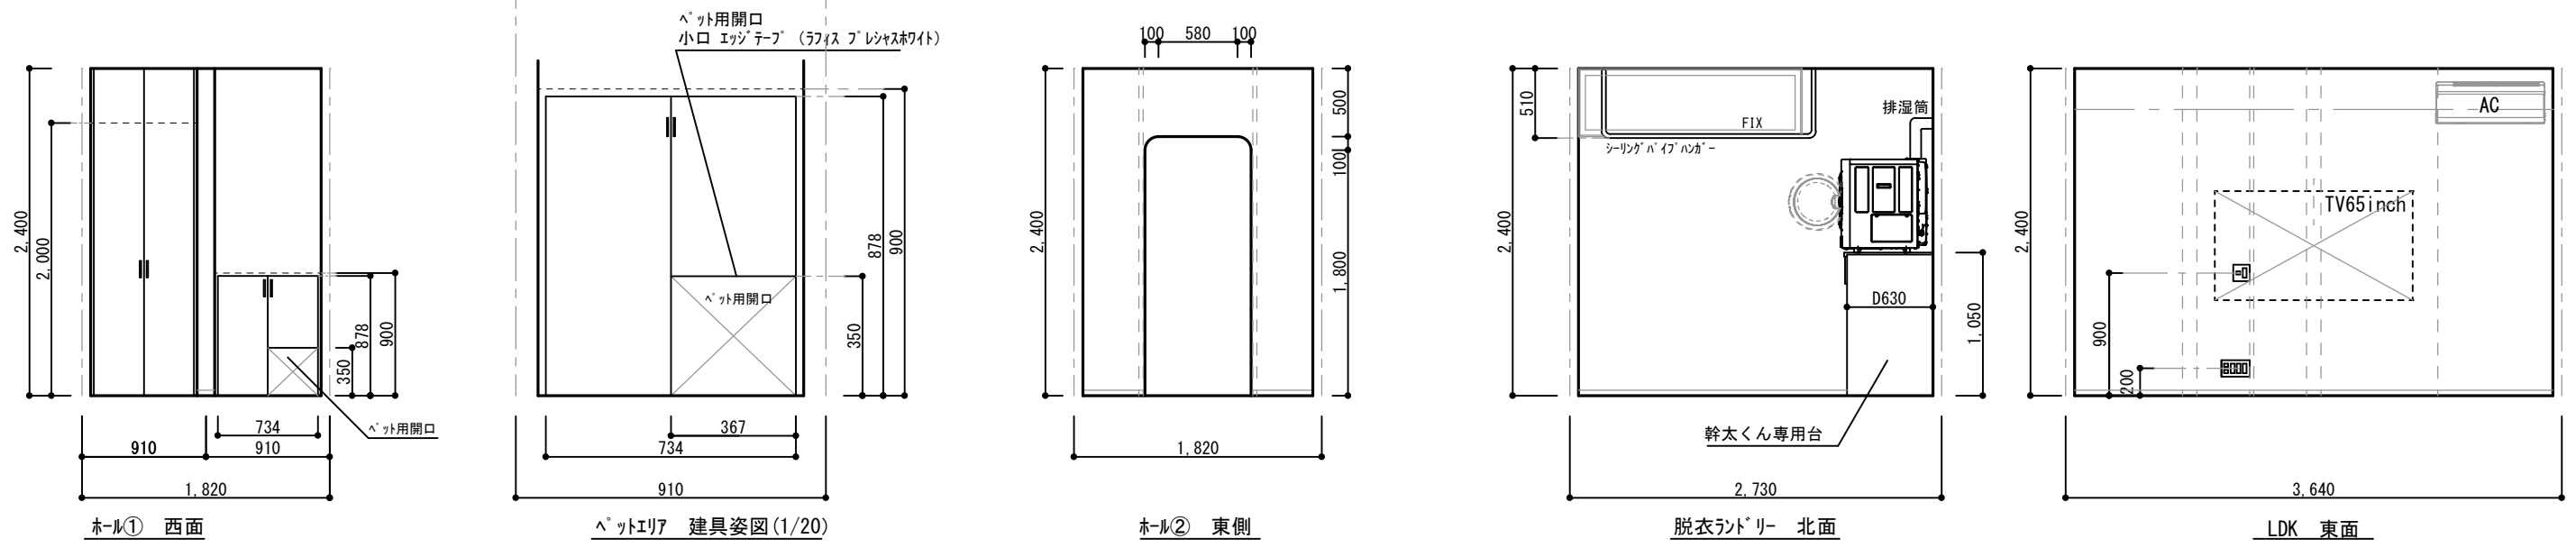

決定図

訂正	浜岡一級総合設計事務所 一級建築士事務所 静岡県知事登録第 (10)2441 号 一級建築士 大臣登録第 365879 号 西原利昌	LIFEFUND PG HOUSE	株式会社 LIFEFUND InDesign office 一級建築士事務所 事務所登録 (2)第7595号 一級建築士登録 第179770号 鈴木 達男 〒432-8023 静岡県浜松市中央区鴨江3丁目70番23号	年月日 2025.12.21 縮尺 1/50	件名 中村悦久様 裕子様 新築工事 図名 展開図-1	設計 酒井	IC	工事 青島	図番 6-1
----	--	----------------------	--	---------------------------------	-------------------------------------	----------	----	----------	-----------

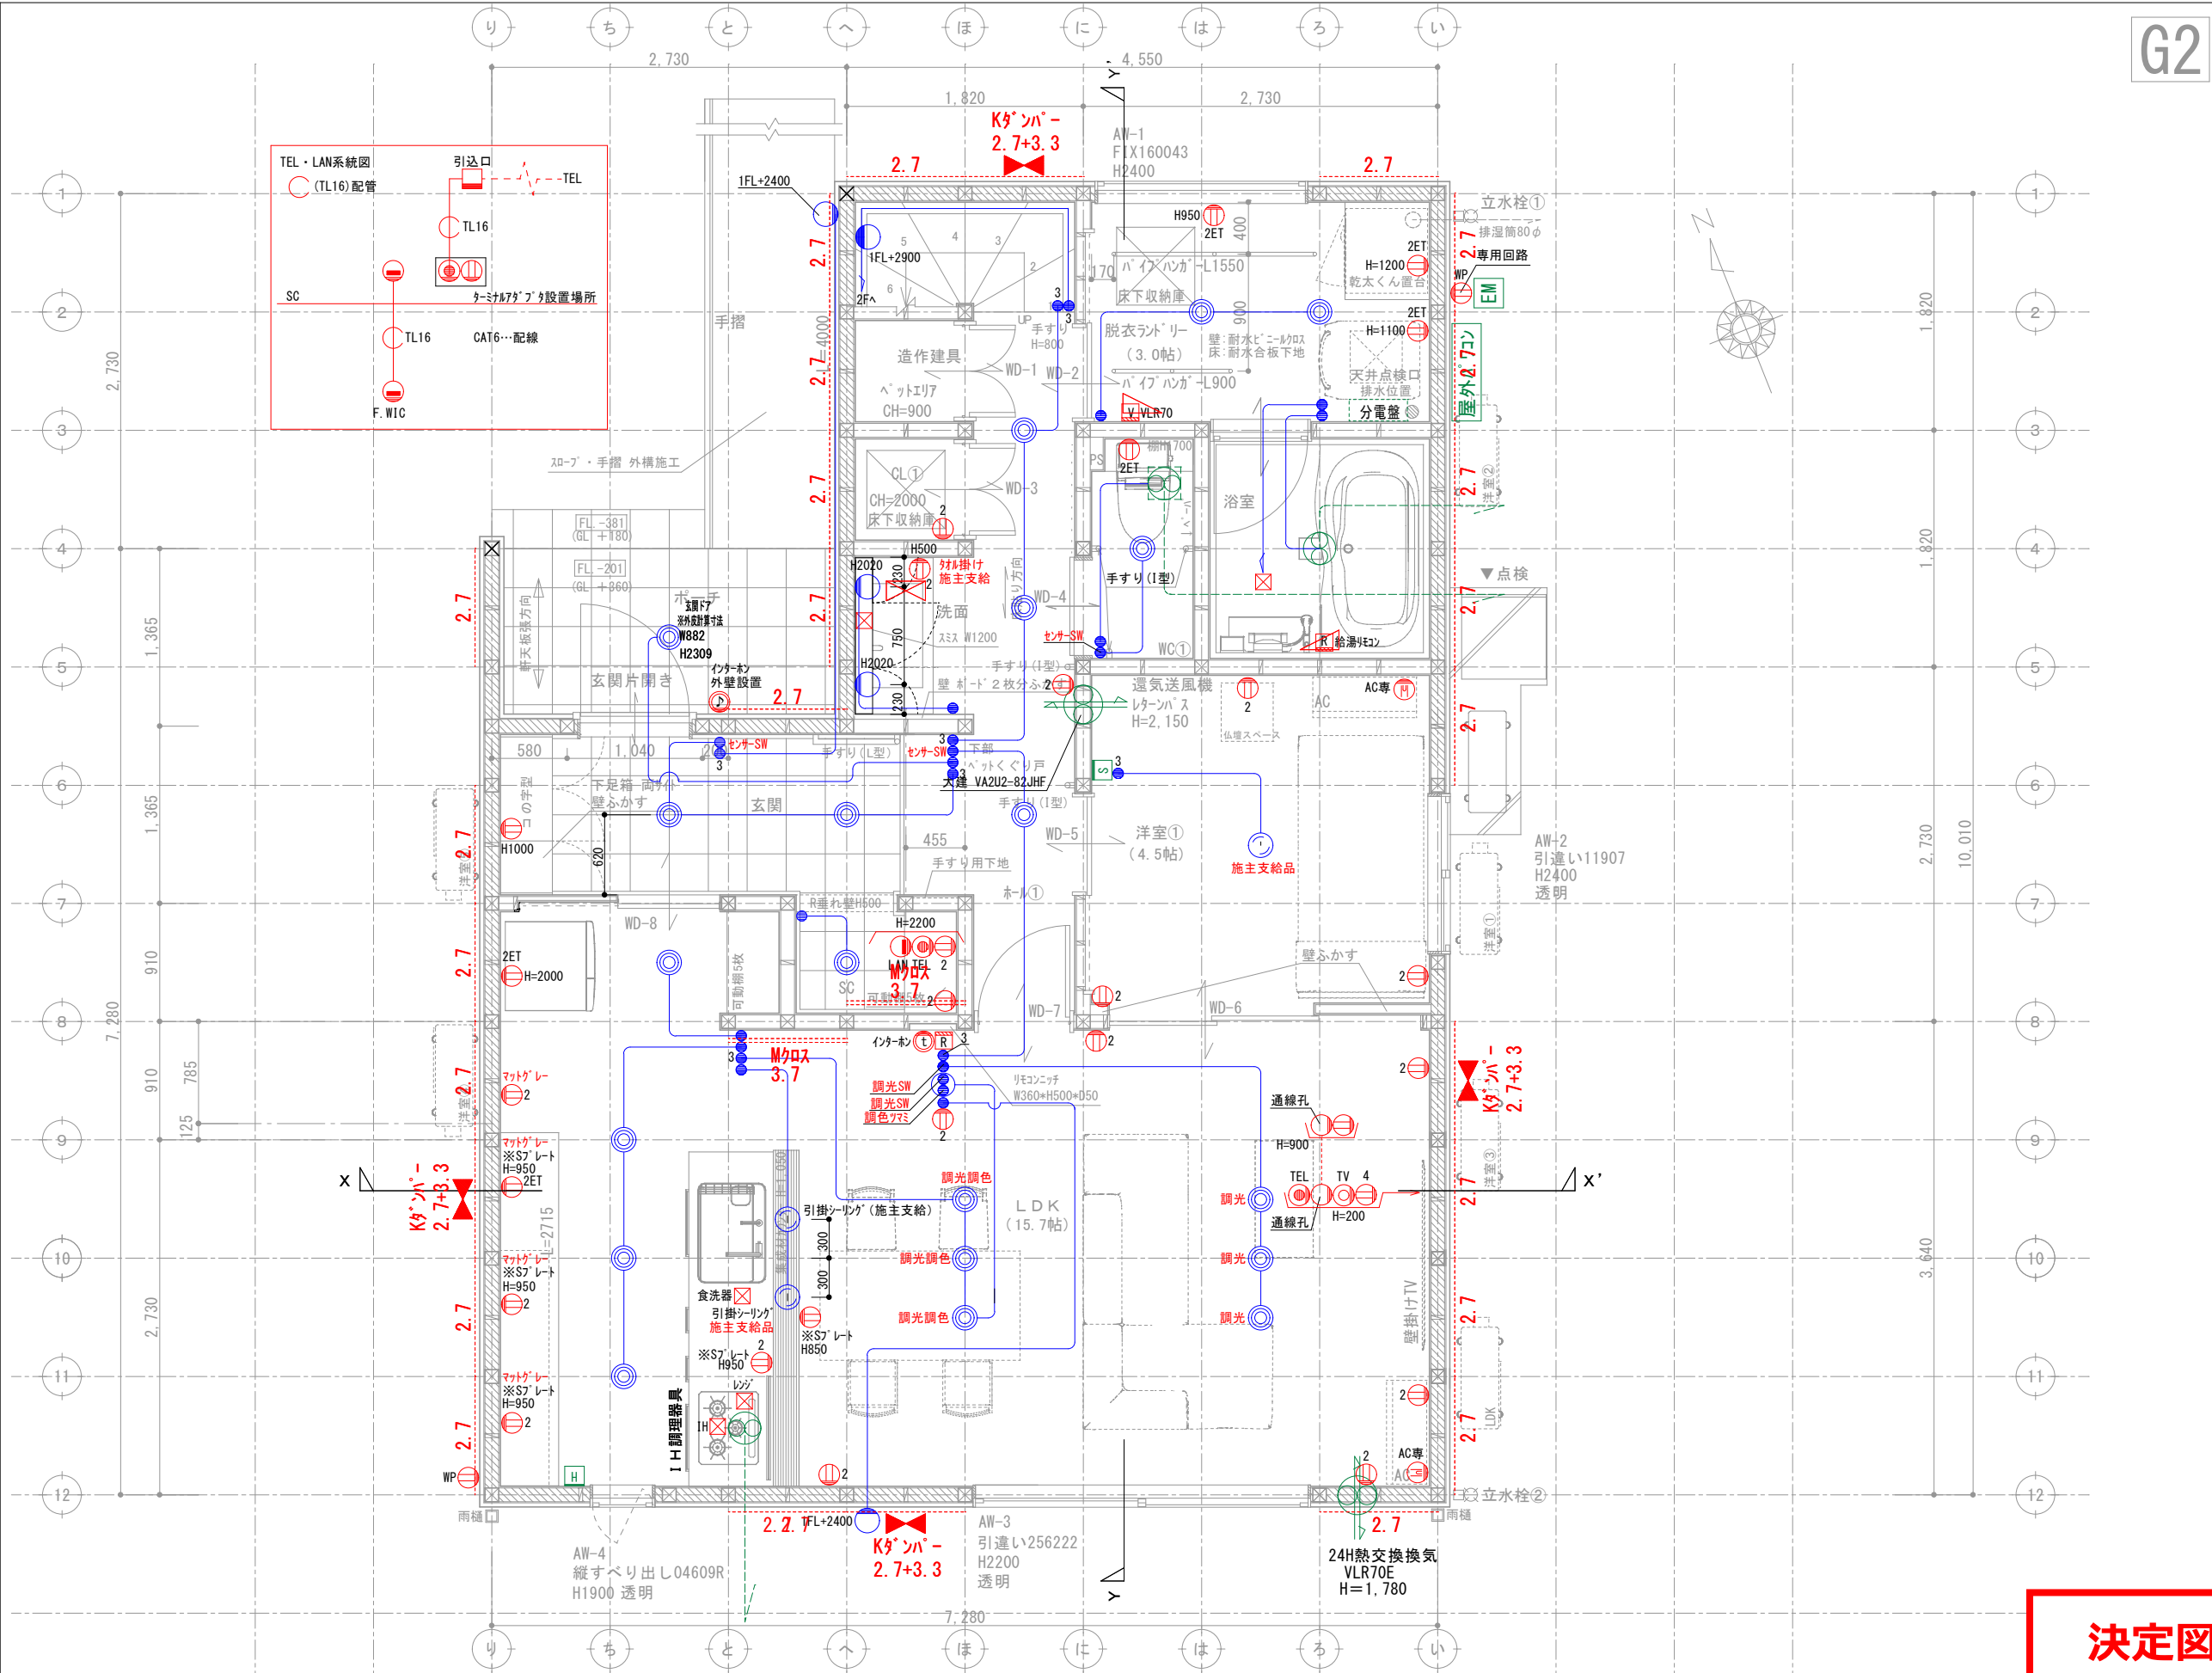

G2

壁付け 住宅用火災報知器			数量
H	熱感知器	電池式(単独型)	1
		露出型	
壁付け 住宅用火災報知器			数量
S	煙感知器	電池式(単独型)	1
		露出型	


※ 煙感知器は壁・梁より600mm以上離す
壁に取付ける場合、
天井から150mm以上500mm以内離す
換気扇・エアコン吹出口から1500mm以上離す
※ 全室LED照明とする。
※ 標準天井高さ2,400
※ 特記無きガラスは型ガラス

- * 凡例
- 管柱 (105×105)
 - Kタンパ (3.30倍 FRM-0641)
 - 片筋違い (2.00倍 45×90)
(例 左:柱脚 右:柱頭)
 - たすき掛筋違い (4.00倍 45×90)
 - 構造用合板 (2.70倍)
(t=9 材種-EXハイバ-)
 - 床点検口
 - 天井点検口
 - 換気扇
 - 熱交換換気扇VLR-70

アドバンスシリーズ		
スマートデザイン (外部)		
凡例	1	コンセント 1ヶ所
2	コンセント 2ヶ所	
3	コンセント 3ヶ所	
1ET	コンセント1ヶ所接地ターミナル付	
2ET	コンセント2ヶ所接地ターミナル付	
WP	コンセント 防水型	
200V	エアコン用コンセント	
WP	防雨入線プレート	
WP	スイッチ	
3	3路スイッチ	
4	4路スイッチ	
直結電源		
TV	テレビ取出口	
TEL	電話取出口 (テレホンガイド)	
LAN	LAN取出口 (テレホンガイド)	
壁照明		
リモコン	リモコン(給湯関係・ルフロ)	
メーター		
分電盤		
チャイム		

※ACコンセント天井付け
※TVアンテナ工事
※スイッチはFL+1100、コンセントはFL+200

決定図

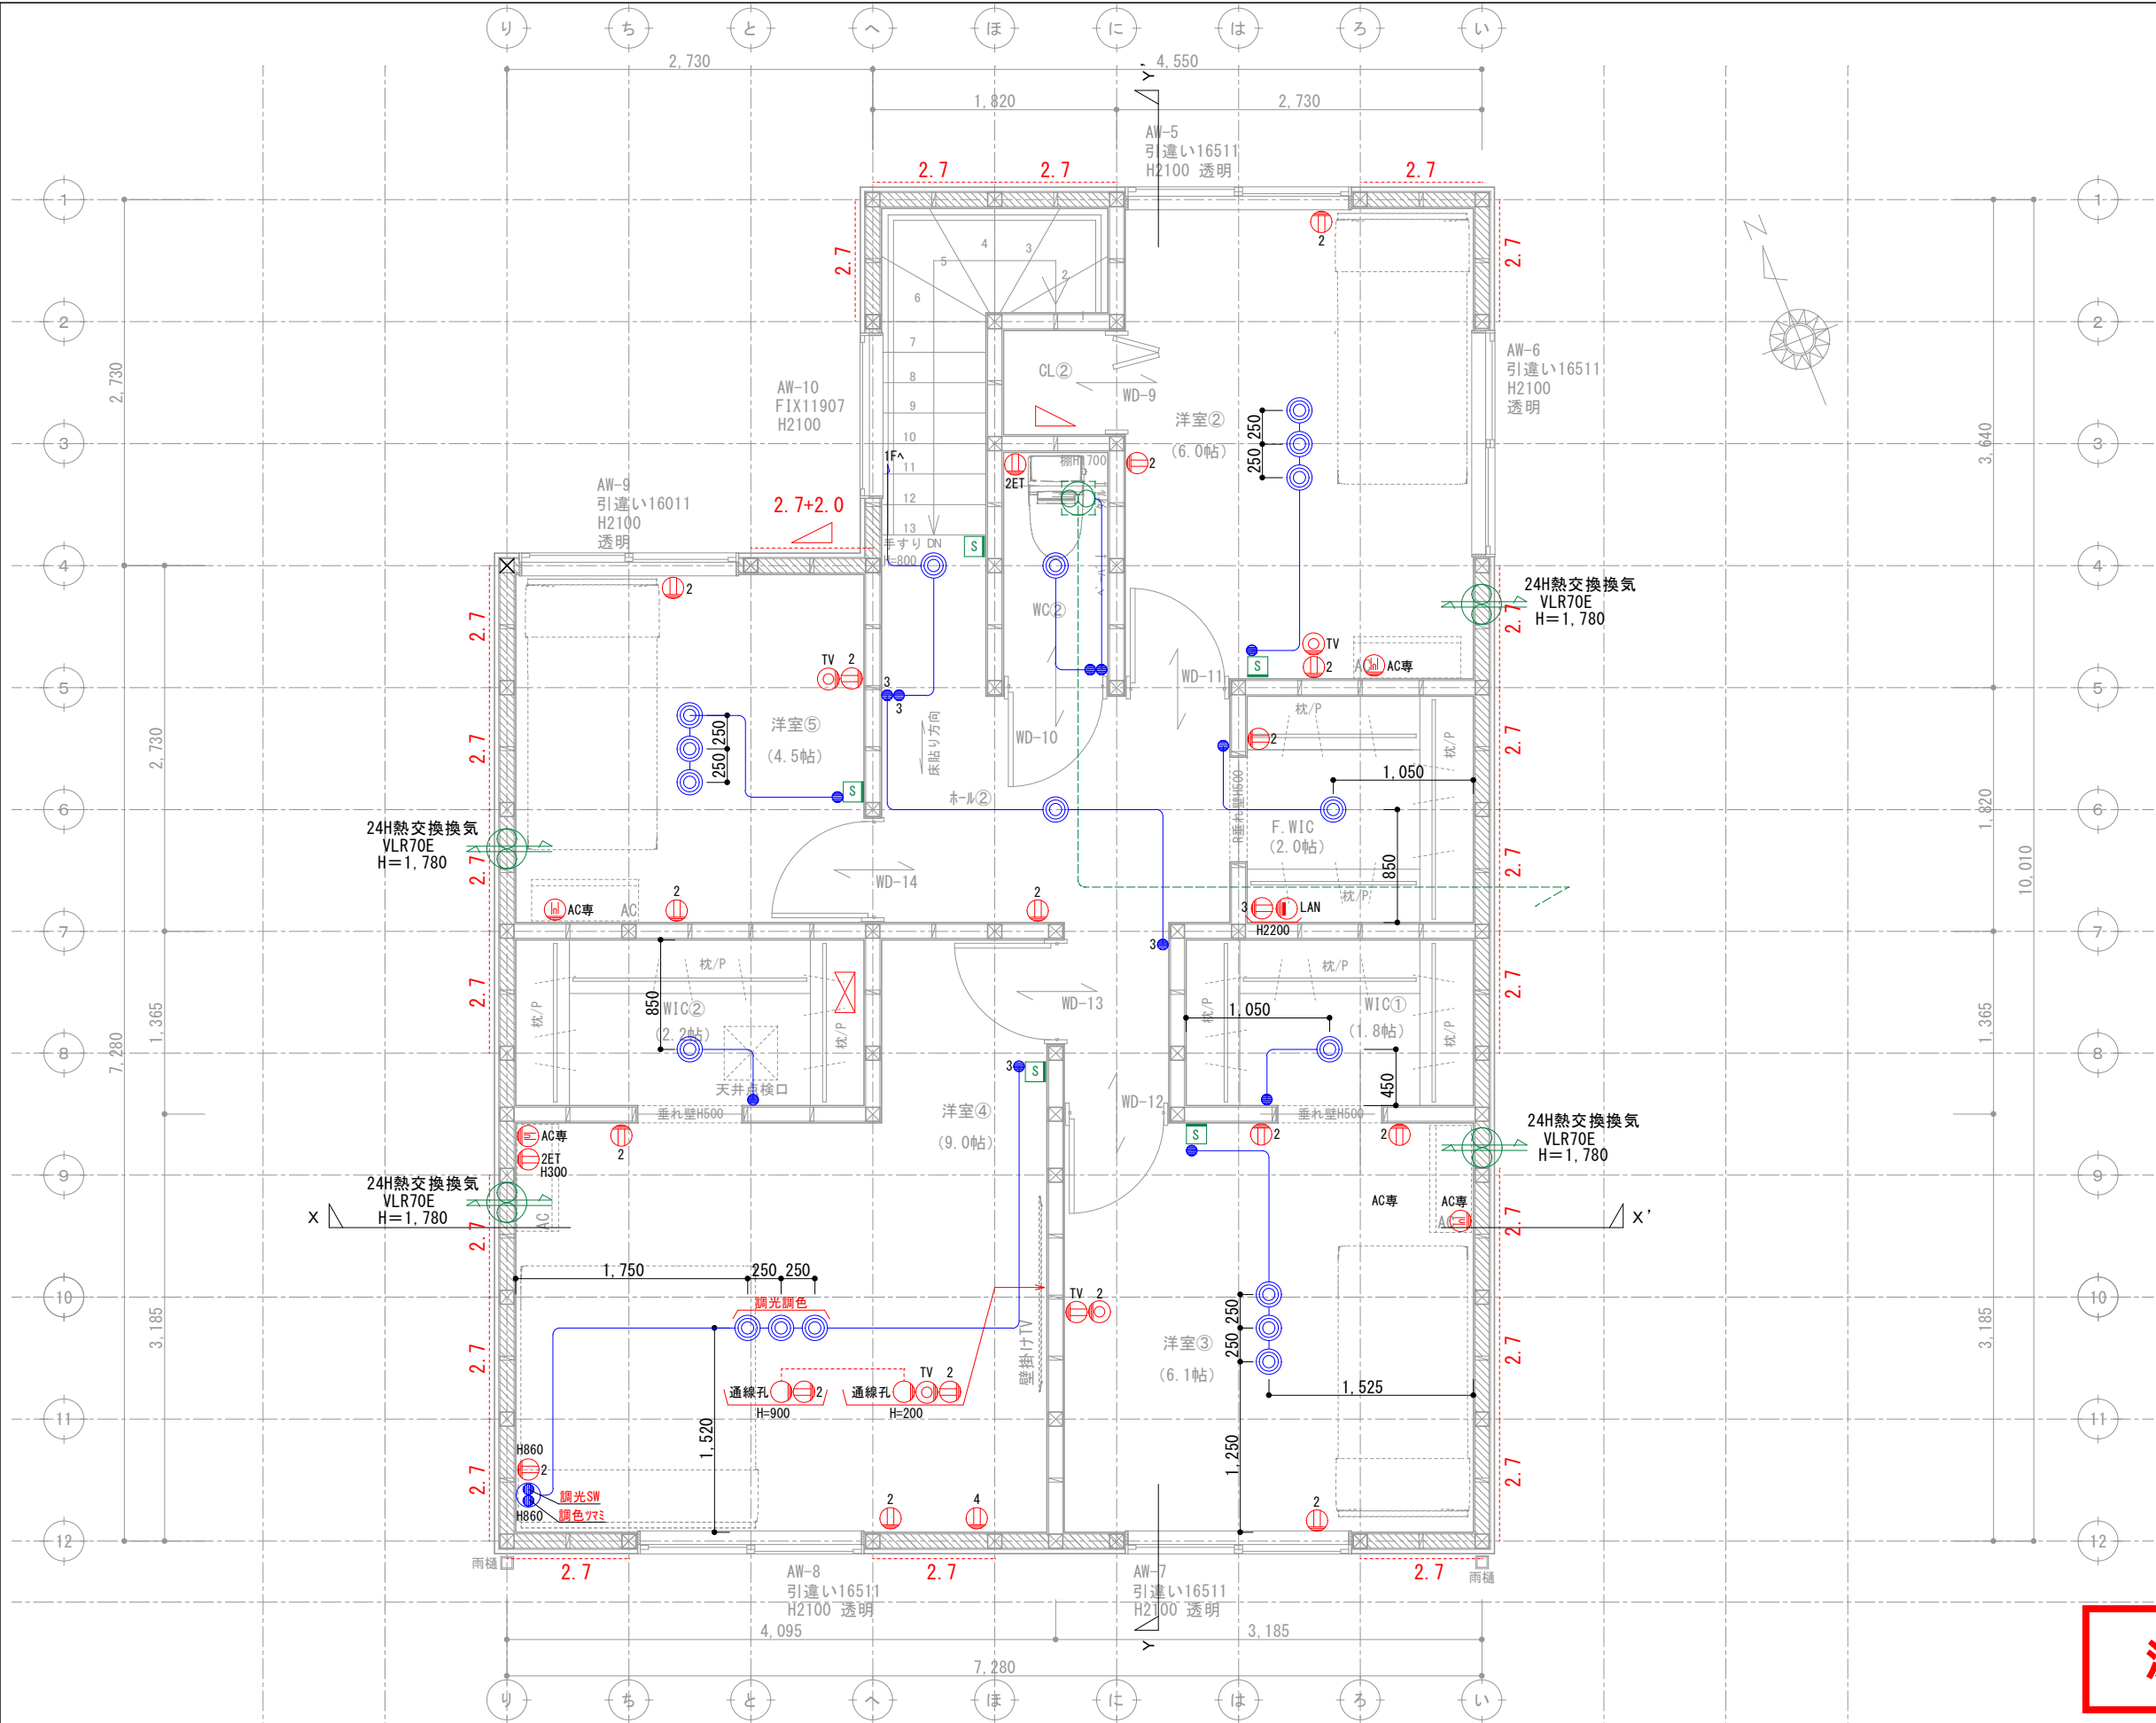

G2

壁付け 住宅用火災報知器			数量
熱感知	H	電池式(単独型)	
	露出型		
壁付け 住宅用火災報知器			数量
煙感知	S	電池式(単独型)	8
	露出型		

※ 煙感知器は壁・梁より600mm以上離す
壁に取付ける場合、
天井から150mm以上500mm以内離す
換気扇・エアコン吹出口から1500mm以上離す
※ 全室LED照明とする。
※ 標準天井高さ2,400
※ 特記無きガラスは型ガラス

* 凡例

管柱 (105×105)

Kタンパ (3.30倍 FRM-0641)

片筋違い (2.00倍 45×90)
(例 左:柱脚 右:柱頭)

たすき掛筋違い (4.00倍 45×90)

構造用合板 (2.70倍)
(t=9 3枚付 EXハイバ)

床点検口

天井点検口


換気扇

熱交換換気扇VLR-70


アドバンスシリーズ	
スマートデザイン (外部)	
凡例	
1	コンセント 1ヶ所
2	コンセント 2ヶ所
3	コンセント 3ヶ所
1ET	コンセント1ヶ所接地ターミナル付
2ET	コンセント2ヶ所接地ターミナル付
WP	コンセント 防水型
	エアコン用コンセント
	200V用コンセント
WP	防雨入線プレート
	スイッチ
3	3路スイッチ
4	4路スイッチ
	直結電源
TV	テレビ取出口
TEL	電話取出口 (テレホンガイド)
LAN	LAN取出口 (テレホンガイド)
	壁照明
	リモコン (給湯関係・ルフロ)
	メーター
	分電盤
①	チャイム

※ACコンセント天井付け
※TVアンテナ工事
※スイッチはFL+1100、コンセントはFL+200

決定図

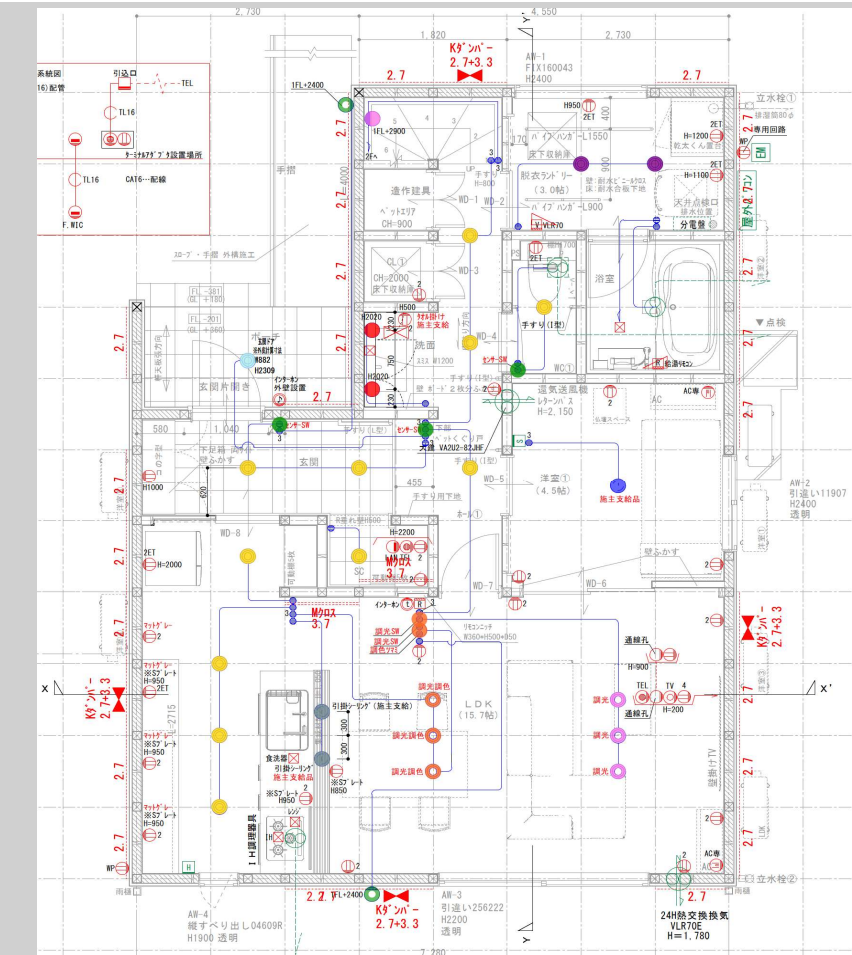

1階

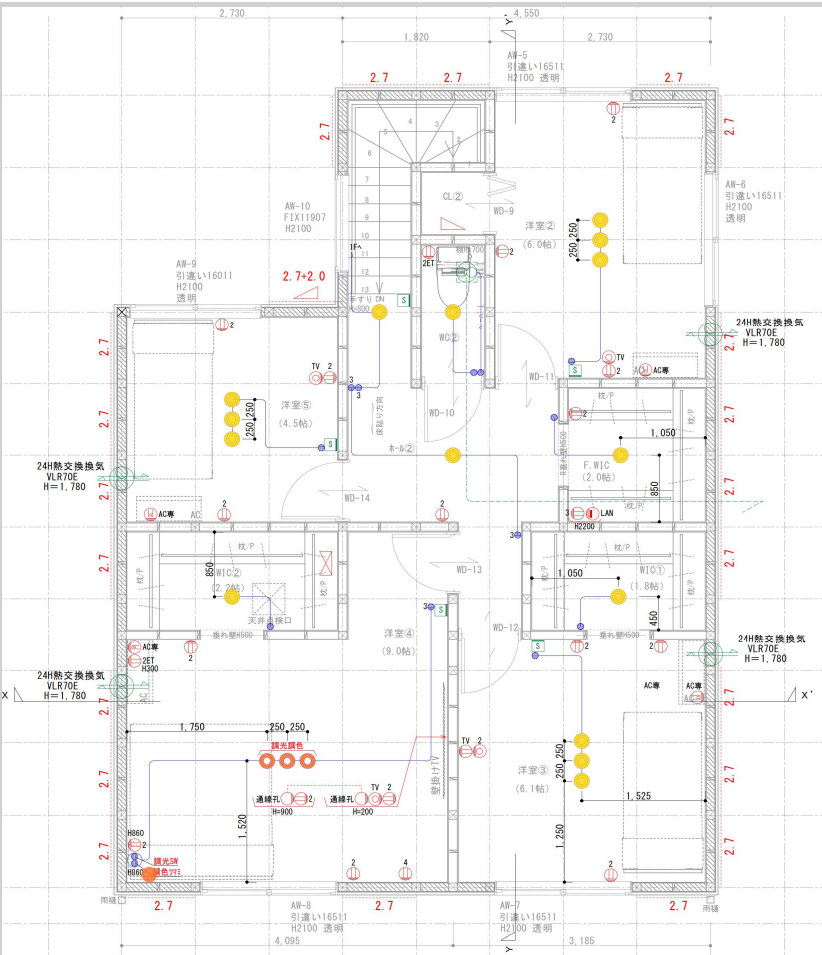


2階

引っ掛けシーリング
● × 2



外部：スマートデザインシリーズ
ブラック

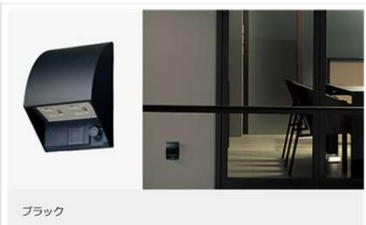

ドアホン：VL-SE31XL
(Panasonic)



内部SW：アドバンス
マットホワイト
LDK
○ × 3
調光ダウナイト
DDL_6032YWG



COBタイプ | 高気密SB形

DDL-6032 AWG
温白色 / 3500K Ra93(クラス2)
480 lm 5.8 W 82.7 lm/W
¥4,600(税抜) (LED内蔵)

LED LED 5.8W
白熱灯60W相当
●銅板 白塗装
●アクリル 乳白(マット)
●径φ116 埋込穴φ100 埋込深71mm 0.3kg
●7VA
●拡散パネル付
●調光可能(1%~100%)
●電光にはLED専用調光器(別売)をご使用ください。
●光束維持時間60,000時間
●取付可能天井厚5~25mm

LED交換不可
調光
防雨形
温度保護機能付
埋込穴 100
埋込必要高 80
埋込天井 55°
準耐火

内部コンセント：アドバンス
マットホワイト (一部マットグレー)
LDK、洋室④
○ × 6
調光調色ダウナイト
DDL-5641FW



高気密SB形

DDL-5641 FW
昼白色 / 5000K~ Ra93(クラス2)
電球色 / 2700K
540 lm 6.7 W 80.5 lm/W
¥11,800(税抜) (LED内蔵)

LED LED 6.7W
白熱灯60W相当
●アルミダイカスト 白塗装
●アクリル 乳白(マット)
●径φ111 埋込穴φ100 埋込深80mm 0.4kg
●7VA
●拡散パネル付
●調光機能付(5000K~2700K)
●調光機能付(5%~100%)
●AC100V
●シーコントロローラー別売
●PWM信号制御調光器別売
●光束維持時間50,000時間
●取付可能天井厚5~25mm
注) 調光機能のみご使用の場合は5000K固定となります。
※定額光電圧、消費電力、固有エネルギー
消費効率等は電球色での値です。

調色
調光
60°
0.1m
近接照度
80
埋込必要高
55°
LED交換不可
温度保護機能付
埋込穴 100

- ポーチ灯
● × 1
センサー付きダウナイト
DDL_6259AW
- 基本照明ダウナイト
● × 26
DDL_6132AW
- 脱衣ランドリー
● × 2
ダウナイト
DDL_6132WW
- 階段
● × 1
ブラケット
DBK_41544A
- ホール①
● × 2
スポットライト
DBK_42022AG
- 玄関、ホール①、WC①
● × 3
センサー-SW
WTA_14119W
- LDK、洋室④
● × 5
調光SW
DP-38458
- 洋室①
● × 1
シーリングライト
-
- 外部照明
○ × 2
外部灯
AU_55959

高気密SB形 | 人感センサー
連動マルチタイプ

DDL-6259 AW
温白色 / 3500K Ra93(クラス2)
530 lm 7.7 W 68.8 lm/W
¥21,800(税抜) (LED内蔵)

LED LED 7.7W
白熱灯60W相当
●銅板 白塗装
●アルミダイカスト 白塗装
●アクリル 乳白(マット)
●径φ116 埋込穴φ100 埋込深75mm 0.5kg
●14VA
●点灯照度調節機能付(暗・明切)
●光束維持時間40,000時間
●取付可能天井厚5~25mm
●調光器併用不可
[連動器具について]
LED調光タイプ60VAまで
LED非調光タイプ不可 蛍光灯不可
白熱灯60Wまで

強制ON
ソフトスタート
フェードアウト
60°
0.1m
近接照度
埋込穴 100
埋込必要高 80
埋込天井 55°
準耐火
LED交換不可
防雨形
温度保護機能付

COBタイプ | 高気密SB形

DDL-6132 AW
温白色 / 3500K Ra93(クラス2)
480 lm 4.6 W 104.3 lm/W
¥3,600(税抜) (LED内蔵)

LED LED 4.6W
白熱灯60W相当
●銅板 白塗装
●アクリル 乳白(マット)
●径φ116 埋込穴φ100 埋込深70mm 0.3kg
●8VA
●拡散パネル付
●AC100V
●光束維持時間60,000時間
●取付可能天井厚5~25mm
●調光器併用不可

LED交換不可
非調光
防雨形
温度保護機能付
埋込穴 100
埋込必要高 70
埋込天井 55°
準耐火

COBタイプ | 高気密SB形

DDL-6132 WW
昼白色 / 5000K Ra93(クラス2)
480 lm 4.6 W 104.3 lm/W
¥3,600(税抜) (LED内蔵)

LED LED 4.6W
白熱灯60W相当
●銅板 白塗装
●アクリル 乳白(マット)
●径φ116 埋込穴φ100 埋込深70mm 0.3kg
●8VA
●拡散パネル付
●AC100V
●光束維持時間60,000時間
●取付可能天井厚5~25mm
●調光器併用不可

LED交換不可
非調光
防雨形
温度保護機能付
埋込穴 100
埋込必要高 70
埋込天井 55°
準耐火

DBK-41544 A
温白色 / 3500K Ra83
125 lm 4.6 W 27.1 lm/W
¥10,800(税抜) (LED内蔵)

LED LED 4.6W
白熱灯60W相当
●銅板 白塗装
●径φ120 出36mm 0.5kg
●8VA
●AC100V
●光束維持時間40,000時間
●調光器併用不可

LED交換不可
非調光
防雨形
温度保護機能付
埋込穴 100
埋込必要高 70
埋込天井 55°
準耐火

DBK-42022 AG
温白色 / 3500K Ra93
430lm 4W 107.5lm/W
¥17,800(税抜) (ランプ付)

LED 4W(E11) 中角形
12Vダイクロハロゲン35W相当
●アルミ型材 白塗装
●アルミダイカスト 白塗装
●市70高133 出8mm 0.3kg ●5VA
●スイッチ付(入切)
●首振り90°回転360°
●AC100V
●調光可能(5%~100%)
●調光にはLED専用(逆位相制御)調光器(別売)をご使用ください。
●光源寿命40,000時間

調光
27°
0.1m
近接照度
埋込天井可能
LED交換可能

3線 / 4線式
WTA14119W

壁取付 熱線センサー付自動スイッチ(親器)
(検知後連続動作時間 約10秒~30分可変形)
(明るさセンサー・手動スイッチ付) (マットホワイト)
3A 100V AC
プレート別売

調光器 | PWM信号制御

DP-38458
¥16,800(税抜)

LED
●プラスチック 白
●市70 高120 埋込穴51×71 埋込深30 出20mm 0.2kg
●制御器具容量1000VAまで
●連結使用可能台数12台まで
●3路オフライトスイッチ付
●1個用スイッチボックス(カバー付)に適合
(明るさセンサー・手動スイッチ付) (Pφ0.9~1.2 (総配線長100mまで)
●AC100V
注) 調光信号線は別途お買い求めください。


埋込穴 51×71

施主
支給品


人感センサータイマー付
ON-OFFタイプ

AU 55959 G 非調光 LED交換不可 拡散
¥39,800(税抜)
電球色 2700K Ra93 8.3W 740 lm 89.1 lm/W

LED
本 体：アルミダイカスト・サンブラック塗装
パネル：ガラス・透明
●重・1.0kg
●光束維持時間:40,000時間
●照度センサー付
●セグメント切替可能
●点灯照度調節可能
●点灯時間切替可能:約30秒/1分/3分/5分/10分
(点灯中に動作を感知するとセンサーが作動し
点灯時間が延長されます)
●照射近接照度10cm
●灯体を下に向けた場合は感知エリアが狭くなります
●調光器併用不可
●17VA(100V)
防雨型 R

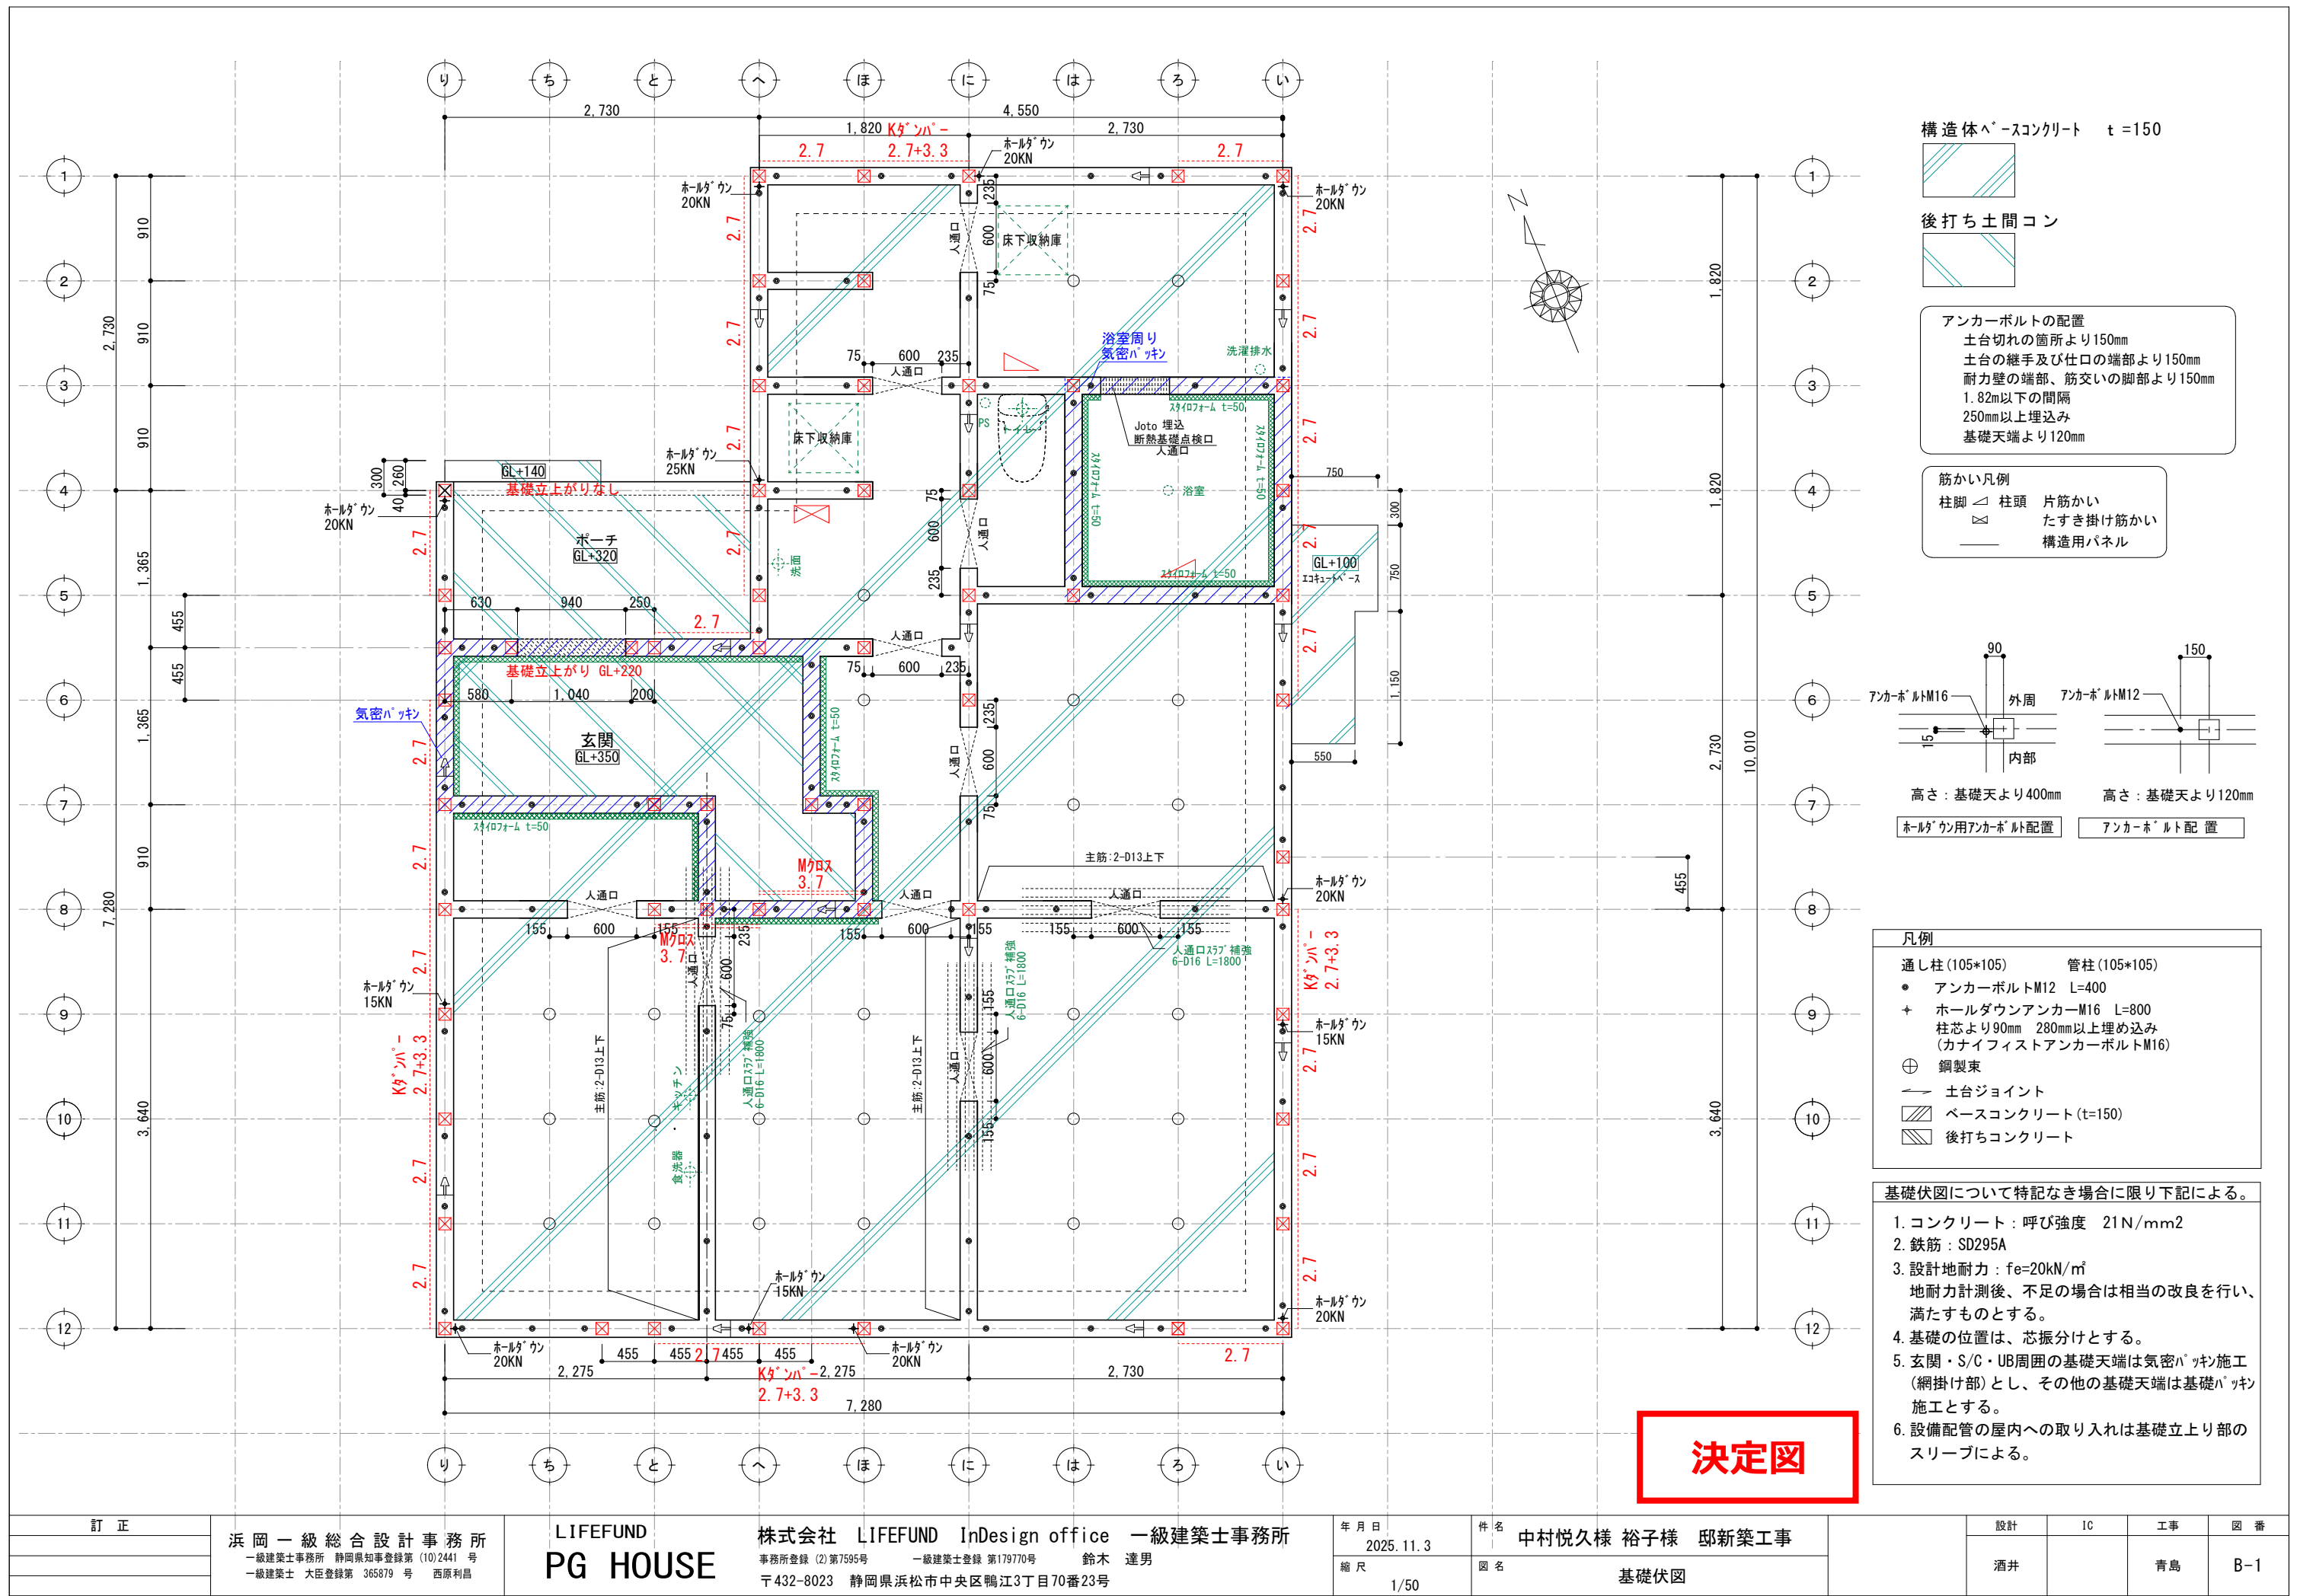


- 構造体ベースコンクリート t=150
- 後打ち土間コン
- アンカーボルトの配置
土台切れの箇所より150mm
土台の継手及び仕口の端部より150mm
耐力壁の端部、筋交いの脚部より150mm
1.82m以下の間隔
250mm以上埋込み
基礎天端より120mm
- 筋かい凡例
柱脚 柱頭 片筋かい
たすき掛け筋かい
構造用パネル


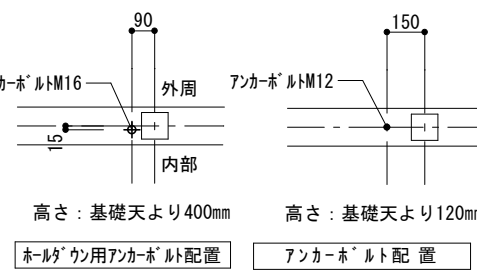


- 凡例
- 通し柱 (105*105) 管柱 (105*105)
- アンカーボルトM12 L=400
 - ホールダウンアンカーM16 L=800
柱芯より90mm 280mm以上埋め込み
(カナイフリストアンカーボルトM16)
 - 鋼製束
 - 土台ジョイント
 - ベースコンクリート (t=150)
 - 後打ちコンクリート

- 基礎伏図について特記なき場合に限り下記による。
- コンクリート：呼び強度 21N/mm²
 - 鉄筋：SD295A
 - 設計地耐力：fe=20kN/m²
地耐力計測後、不足の場合は相当の改良を行い、満たすものとする。
 - 基礎の位置は、芯振分けとする。
 - 玄関・S/C・UB周囲の基礎天端は気密パッキン施工（網掛け部）とし、その他の基礎天端は基礎パッキン施工とする。
 - 設備配管の屋内への取り入れは基礎立上り部のスリーブによる。

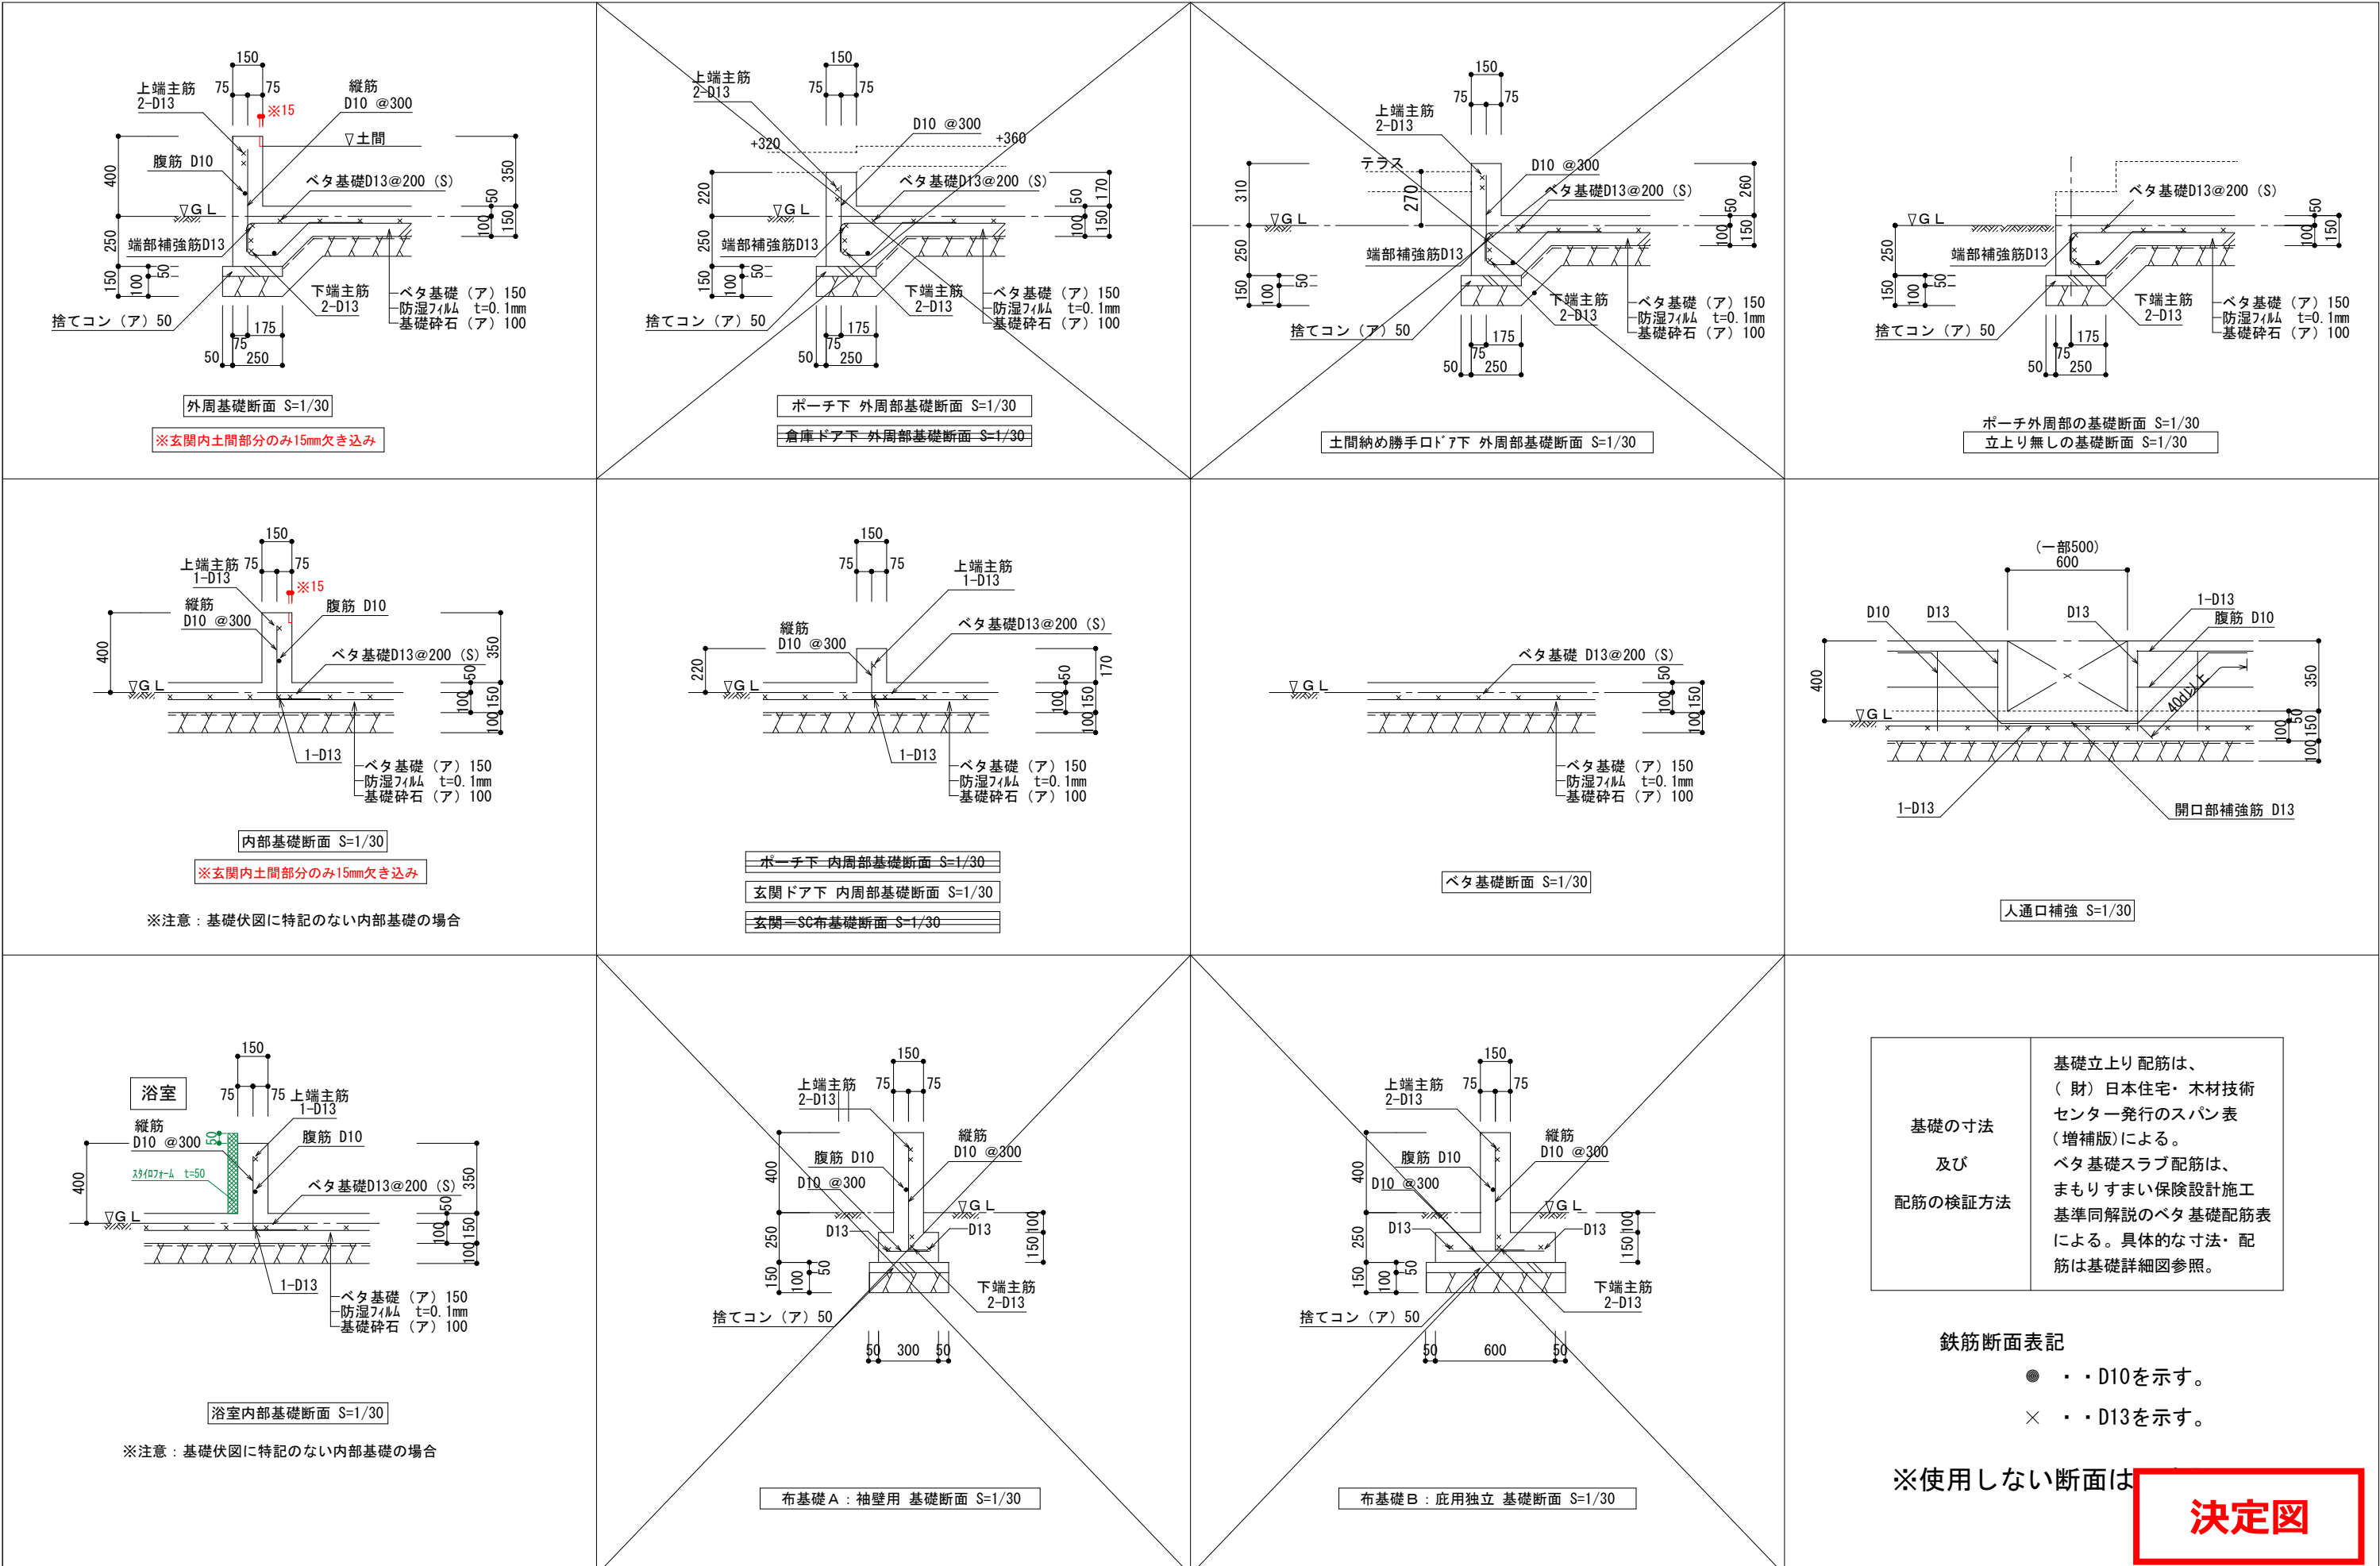

決定図

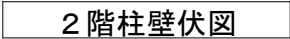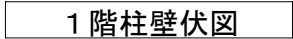

梁繼手・仕口用
梁繼手・仕口用

梁繼手・仕口用
梁繼手・仕口用

胴差と通し柱の接合部の仕様		
	胴差と通し柱の条件	仕口
T1	通し柱の片側に胴差が来る場合	胴差を柱にかたぎ大入れ短ほぞ差しの上、羽子板ボルト、かね折り金物又は同等以上の仕口
T2	通し柱の両側に胴差が来る場合	胴差を柱にかたぎ大入れ短ほぞ差しの上、短冊金物又は、同等以上の仕口で胴差相互を緊結
T3	通し柱と胴差の接合部の近くに90×90以上の筋かいが来る場合(通し柱が建物の出隅にあるか、筋かい壁が外壁と直交して接する場合)	胴差を通し柱に、15KN用引き寄せ金物を水平に用いて緊結

決定図