


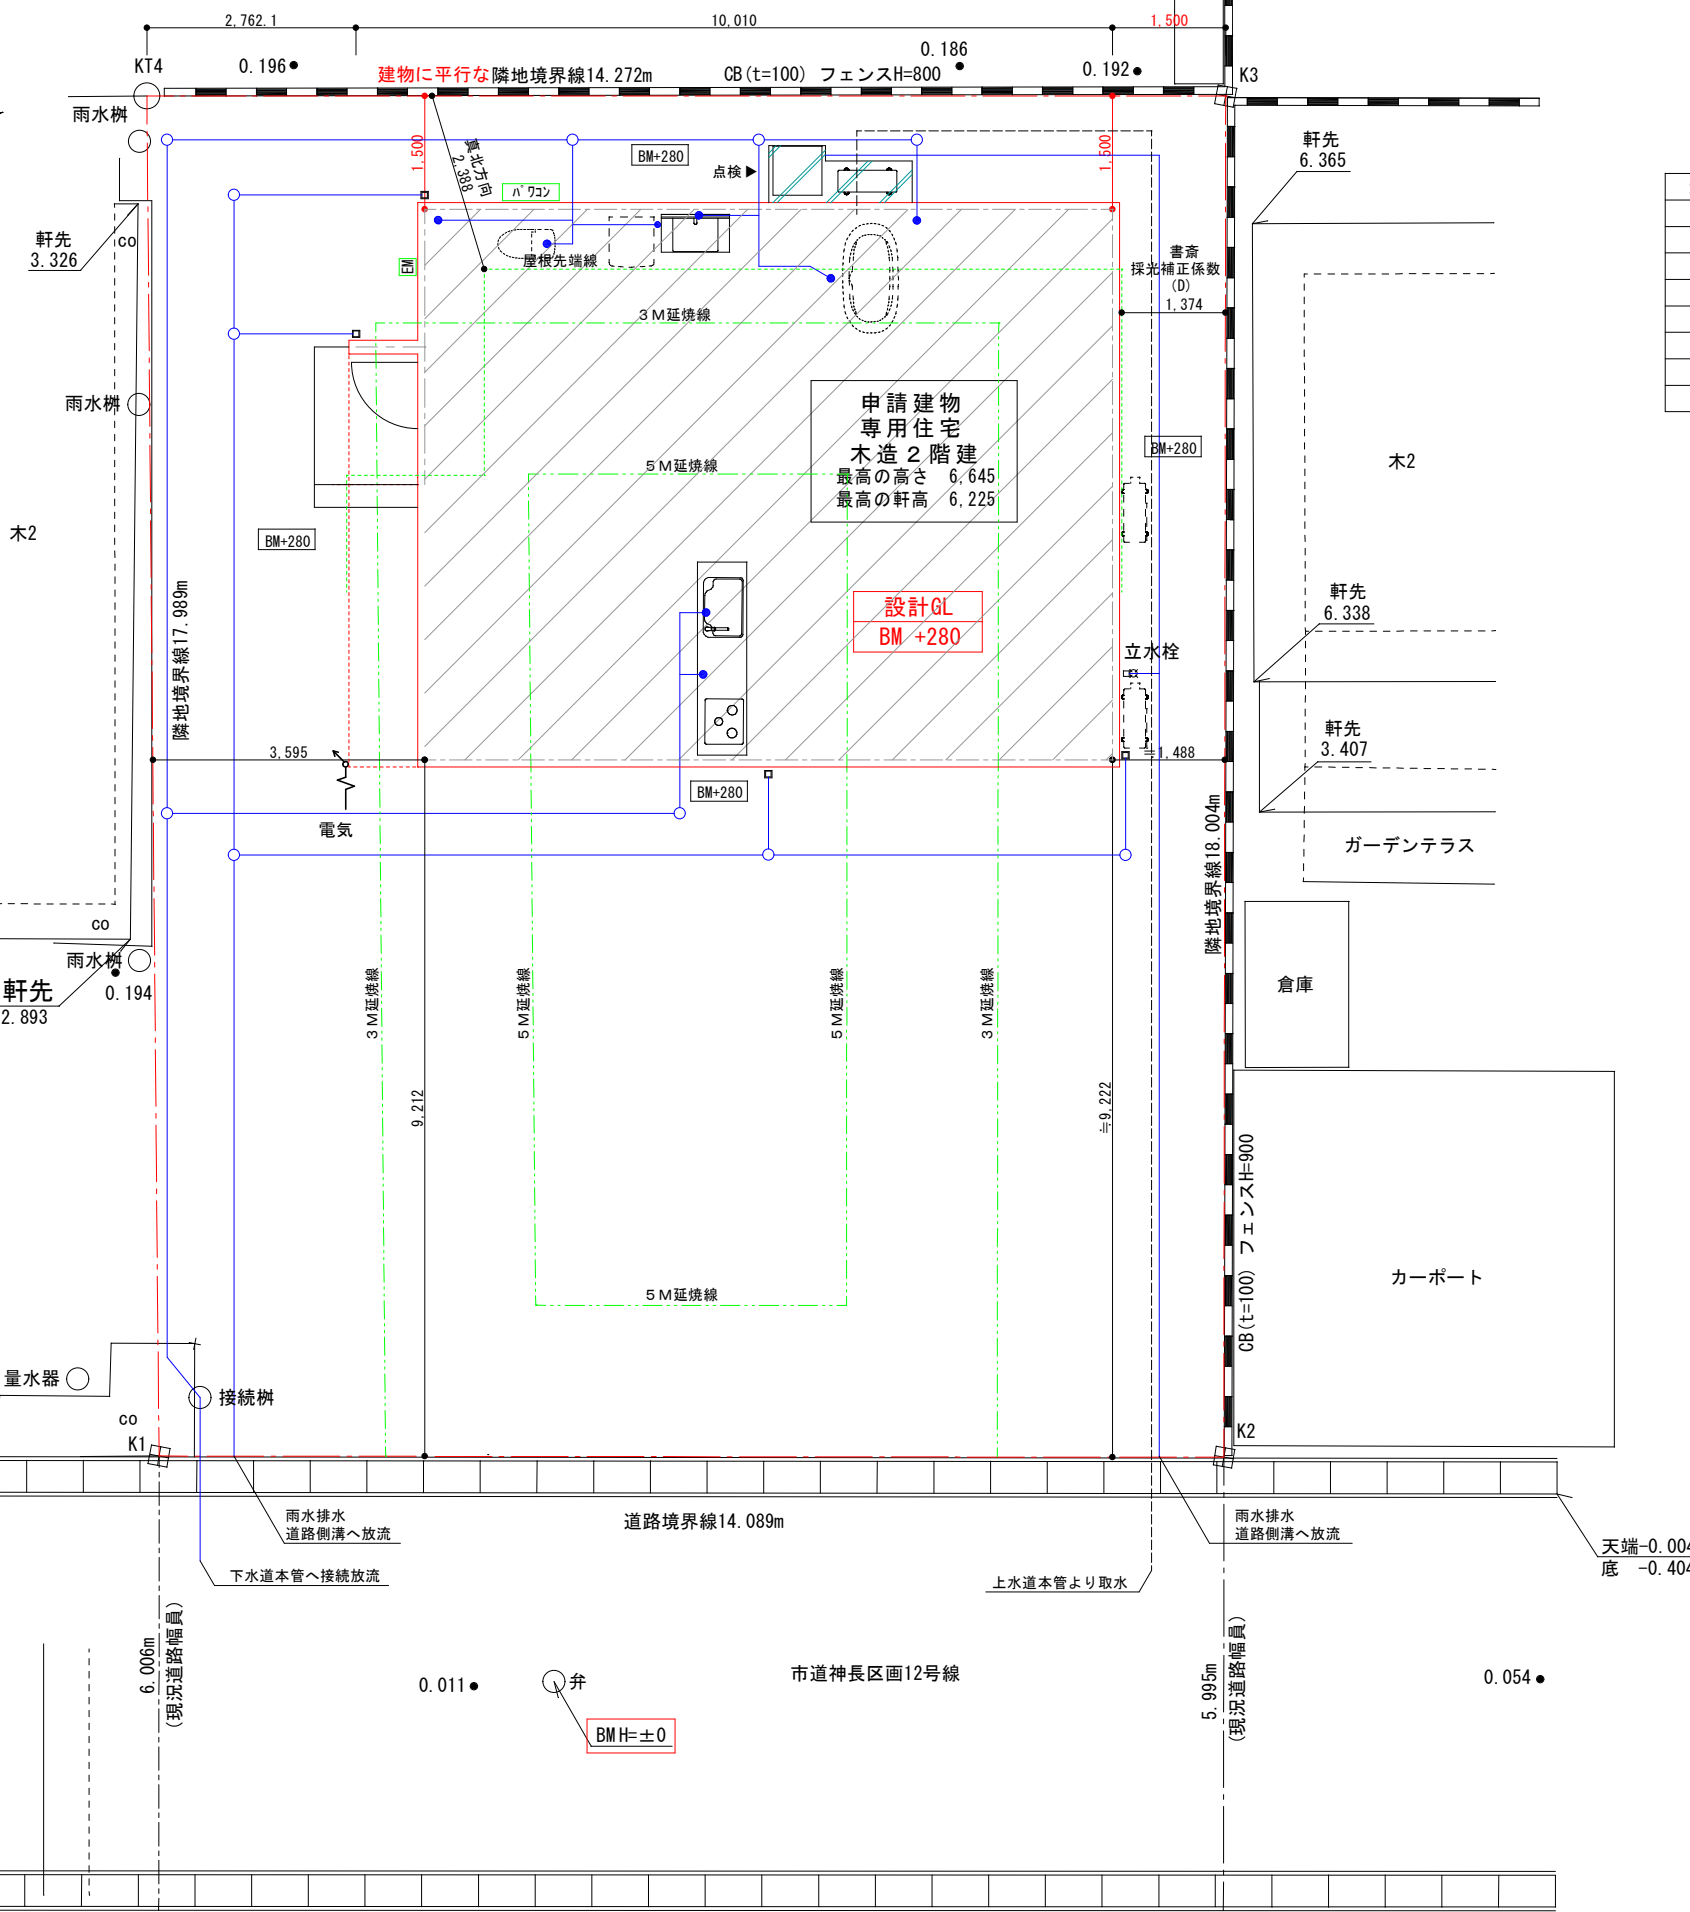

G2

地 番	1 21-6			
NO	X _n	Y _n	Y _{n+1} - Y _{n-1}	X _n ・(Y _{n+1} - Y _{n-1})
K2	13.475	-2.916	-20.228	-272.572300
K3	10.271	-20.633	-15.158	-155.687818
KT4	-3.769	-18.074	20.228	-76.239332
K1	-0.389	-0.405	15.158	-5.896462
合 計				-510.395912
合 計 面 積				255.1979560
地 積				255.19 m ²

斜線
 $5,000 + (2,388 \times 1.25) = 7,985$
 建物高さ 6,645
 $7,985 > 6,645$ ゆえに OK

※斜線適法
※雨水排水は道路側溝へ放流
※盛土規制法の規制に係る切土・盛土無し

配置図 S = 1/100

決定図

訂 正	浜 岡 一 級 総 合 設 計 事 務 所 一級建築士事務所 静岡県知事登録第 (10)2441 号 一級建築士 大丘登録第 365879 号 西原利昌	LIFEFUND PG HOUSE	株式会社 LIFEFUND InDesign office 一級建築士事務所 事務所登録 (2)第7595号 一級建築士登録 第179770号 鈴木 達男 〒432-8023 静岡県浜松市中央区鴨江3丁目70番23号	年 月 日	件 名		設計	IC	工事	図 番
				2026. 1. 10	寺田慎介様 邸新築工事					
				縮 尺	図 名					
		1/100	配置図				酒井		青島	2-1