
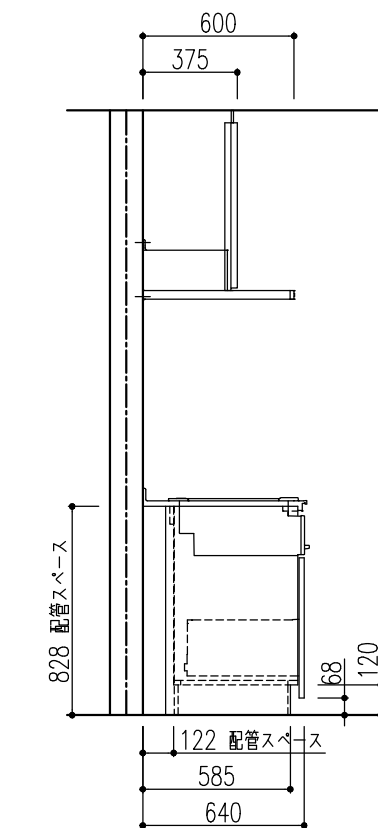


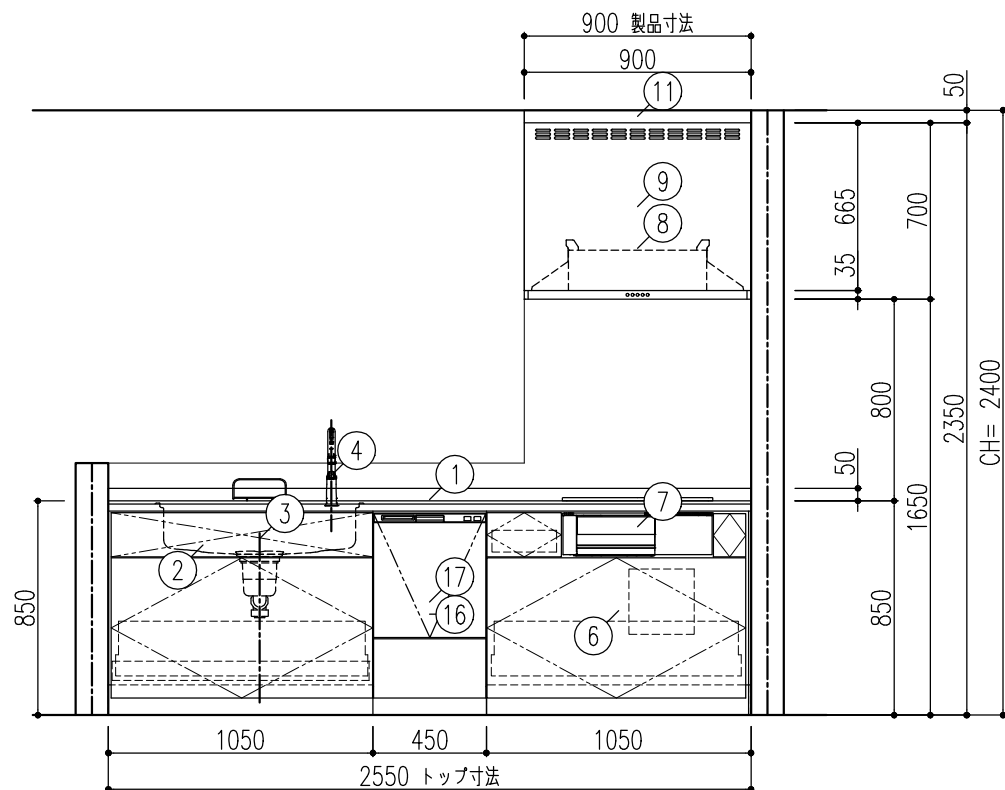



【 ご注意 】

- 壁面仕上材（キッチンパネル・タイルなど）の貼付下端位置が変わります。　〔機能図参照〕
- 記載のキャビネット寸法は扉前面までの呼び寸法です。キャビネット本体の寸法・扉厚み等は商品ガイドの巻末資料をご確認ください。
- 記載のワークトップ、カウンター、エンドパネル、サイドパネルの寸法は呼び寸法です。詳細寸法は商品ガイドの巻末資料をご確認ください。
- レンジフード電源プラグ仕様：3芯電源プラグ（アース工事が必要です。）

A3 20251201M30F-01

B面

C面

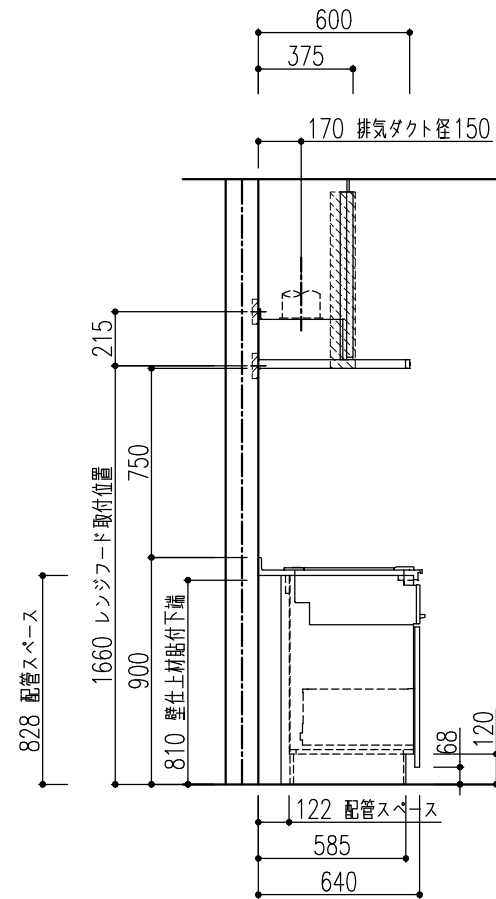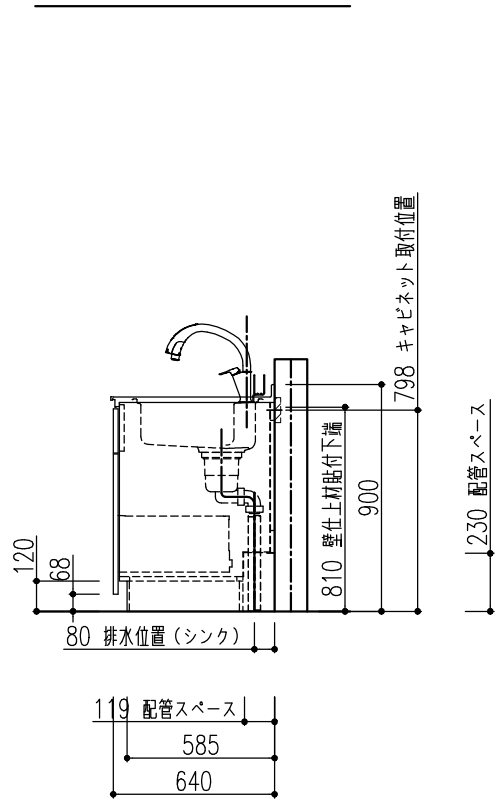

特記事項 扉色 KK5:ブラックスタック 取手 [M]スリム取手 (ブラック) ワークトップカラー 【DW】 ソルティホワイト	物件名	寺田慎介 様邸	案件No.	図面名	担当	図面	図番
	仕様	ES21	A2512DDD0EYYK2	納まり図	栗野 友仁		株式会社 LIXIL
			見積No.	縮尺	日付		
			M25129443443-001-2	1/30	2025.12.01		

■壁面仕上材（キッチンパネル、タイルなど）取付注意事項〔貼付下端位置〕

●キッチンパネルの貼付下端位置

キッチンパネルの貼付下端位置にご注意ください。

キッチンパネル

壁

810mm

(キッチンパネル貼付下端位置)

ワークトップ高さ：850mm以外の場合は、
下表を参照してください。

ワークトップ高さ	キッチンパネル貼付下端位置
900	860
875	835
825	785
800	760

●上表はキッチンパネルの場合です。ステンレスパネルの場合は、キッチンパネルの「取付・設置説明書」を参照してください。

《ワークトップ高さ：850mmの場合》

■壁面仕上材（キッチンパネル）取付注意事項〔貼付向き〕

●キッチンパネルの貼付向き

キッチンパネルの貼付向きにご注意ください。

【単位：mm】

レンジフード

ウォールキャビ（開き扉）

クイックポケット
クイックパレット

横貼り

縦貼り

フロアキャビ

700
(ウォールキャビ・レンジフード高さ)

620
(クイックポケット・パレット用キャビ高さ)

880
(壁面寸法)

850
(ワークトップ高さ)

《バックガード：なし、ワークトップ高さ：850mm、ウォールキャビ高さ：700mmの場合》

《キッチンパネル 貼付方向》
総高さ：2350mmの場合

	ウォールキャビ		
	開き扉	クイックポケット クイックパレット	
	H700	H600 H500	H700 (620) H600 (520)
キッチンパネル貼付方向	横	縦	

【ご注意】
リシエル以外のクイックパレットは、キャビネットの背板高さがショート（－80mm）しておりませんので、『開き扉』のキッチンパネル貼付方向に合せてください。

■床の不陸に関して

7mm以下

7mm以下

床の不陸は、7mm以下に抑えるようにしてください。不陸が大きい場合は、現場責任者に床の修正を依頼してください。
※キャビネット取付時には不陸調整スペーサー等で水平になるように設置してください。

■食器洗い乾燥機内配管図 床立上げ配管例

※給水接続か給湯接続かお客様に確認したうえで施工願います。

給水（給湯の場合は耐熱配管）

①アングル型止水栓（ドライバー式）

②硬質塩化ビニルライニング鋼管相当品

③Rc1/2エルボ

④断熱材（Φ48）

排水（耐熱塩ビ使用のこと）

⑤排水パイプHT20相当品

⑥HT20エルボ

キッチン高さ	H825	H850	H875	H900
本体高さ	775	800	825	850
A	147	172	197	222
B	100	125	150	175

125V・15A 2極接地極付
アースターミナル付コンセント

615
キャビネット奥行
557~577

65

75

132
472~492

615
キャビネット奥行

30°

270

350

食洗機間口
450

案件No.

図面名

担当

図面

図番

A2512DDD0EYYK2

機能図

栗野 友仁

見積No.

縮尺

日付

M25129443443-001-2

2025.12.01

株式会社 LIXIL

寺田慎介 様邸

ES21

特記事項

扉色 KK5:ブラックスタック

取手 [M]スリム取手（ブラック）

ワークトップカラー 【DW】ソルティホワイト

物件名

仕様

A3


20251201M30F-01

■レンジフード 取付注意事項（壁面取付時）


レンジフードを取付ける場合は下地の材が厚み30mm以上、幅100mm以上、ビス固定位置が材の端部から25mm以上であることを確認してください。
また、壁強度などの詳細は「レンジフード設置説明書」を必ず事前に確認してください。

取付位置については、取付設置図を確認してください。


参考図_CLS. SER. NST. ASR. ADR. RVJ. GSR. BFRS. TARシリーズ
（※RVJ. GSRシリーズの場合はレンジフードパネルの取付下地は不要です。）

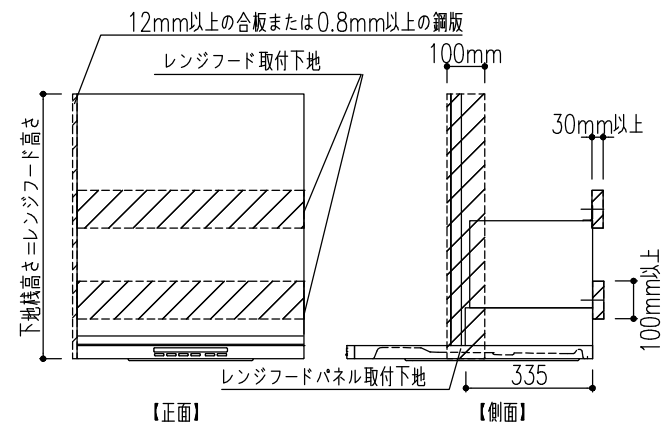

参考図_FED. HVR. NSDシリーズ（サイドマントルタイプ）

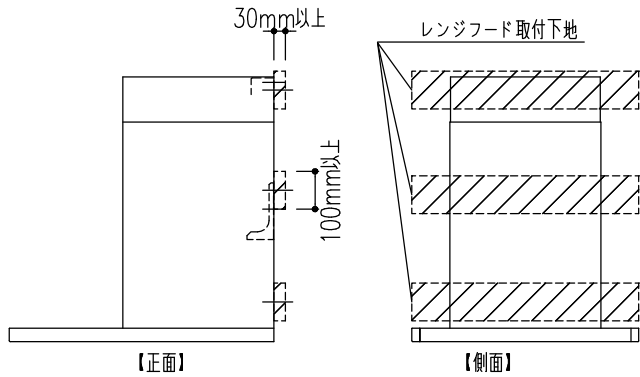

参考図_NBHシリーズ

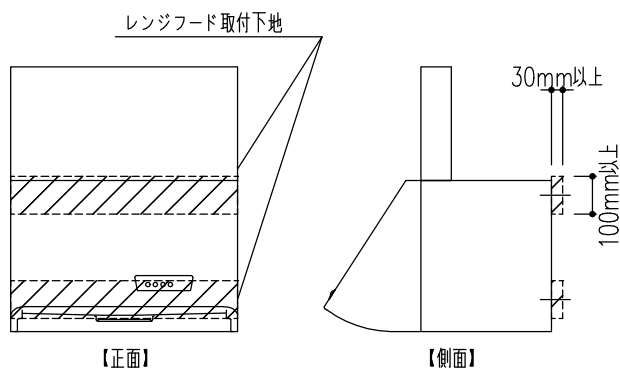


■天井フィラーの取付（レンジフード上部）

レンジフード横に壁がくるレイアウト時は、横壁にも取付材が必要になります。


は、取付下地位置を示します。

レンジフードの上端を基準に下地を入れてください。


12mm以上の合板 または
0.8mm以上の鋼板

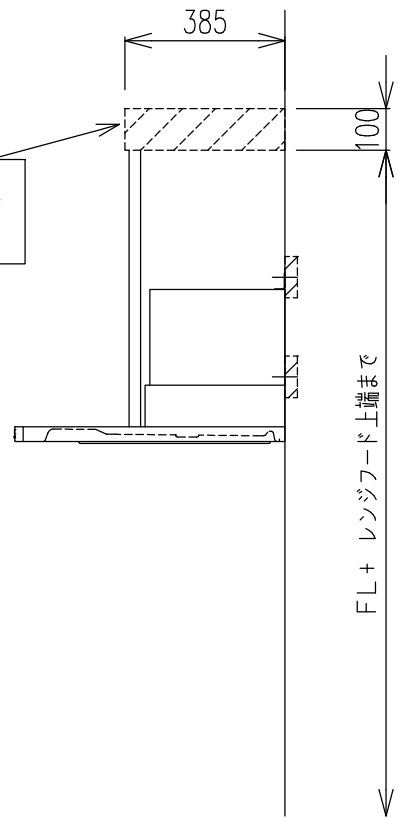

■ASRフード


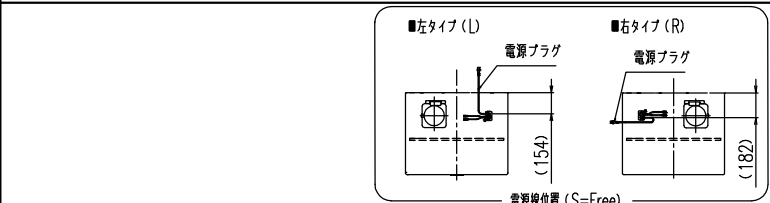


特 性 表							
型 名	定格電圧 (V)	ノッチ	定格周波数 (Hz)	消費電力 (W)	風 量 (m³/h)	騒 音 (dB)	
ASR-93*・73*・63* SI/W R/L	100	強	50	105	520	420	47
			60	125	500	430	46
		弱	50	60	330	—	37
			60	61	300	—	35
		常時	50	29	180	—	23
			60	29	160	—	22

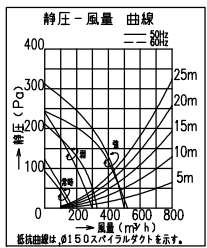

変換寸法表・質量表				
品番	A	B	質量	
ASR-93*SI/W	900	800	13.5	
ASR-73*SI/W	750	650	13.0	
ASR-63*SI/W	600	500	12.5	

付 属 品
座付ねじシルバー (φ4.8×45) 2本
座付ねじブラック (φ5.1×45) 2本
ソフトテープ 1本

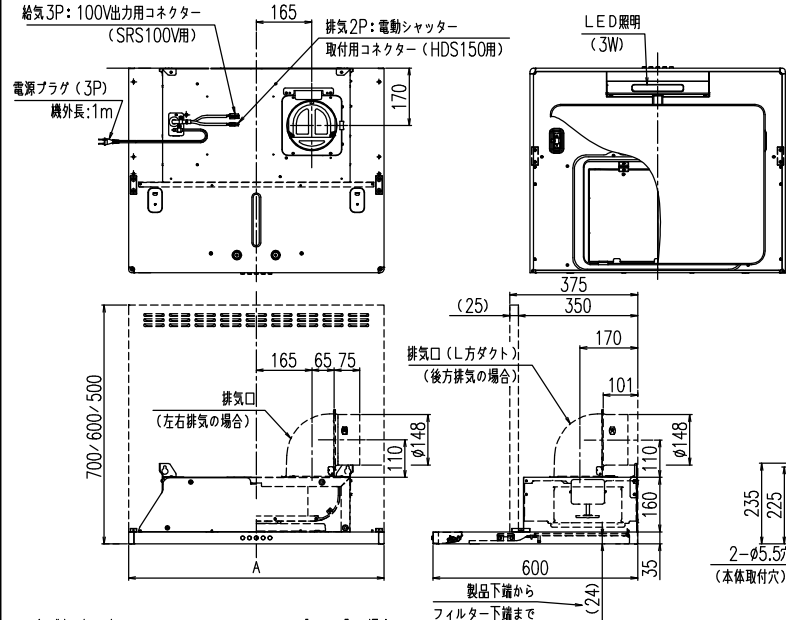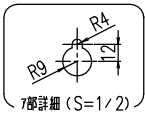


4. 製品名の末尾の () にはワザンリスによって記号が入る場合があります。
3. 品番の SI/W は色調を示します。(SI: シルバー、W: ホワイト)
2. 本図は右排気を示します。左排気は対称 (電源線位置を除く) となります。
注) 1. 排気方向は上方・後方・左右排気です。(後方・左右排気の場合は別売のL型ダクトを使用)

■IHヒーター用コンセント推奨位置図 / 壁付設置の場合

※コンセントや電源プラグが、引き出しおよびIHヒーター用仕切板（オプション）に接触しないように注意してください。
※木製キャビネットの配管スペース付キャビネットを使用する場合は点検口裏の配管スペース内にコンセントを設置してください。



キッチン高さ	電源線高さ
800	400
850	450
900	500

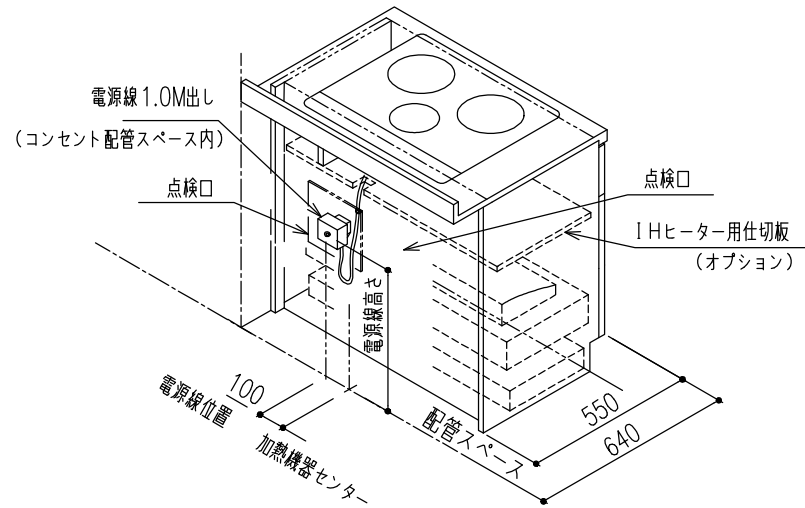


注意: 引き出しおよびIHヒーター用仕切板（オプション）に接触しないように上記寸法を参照してください。

特記事項 扉色 KK5:ブラックスタック 取手 [M]スリム取手 (ブラック) ワークトップカラー 【DW】ソルティホワイト	物件名 寺田慎介 様邸	案件No.	図面名	担当	図面	図番
		A2512DDDOEYK2	機能図	栗野 友仁		株式会社 LIXIL
		見積No.	縮尺	日付		
		M25129443443-001-2		2025.12.01		
仕様	ES21					

■ 止水栓図（床立上げ）

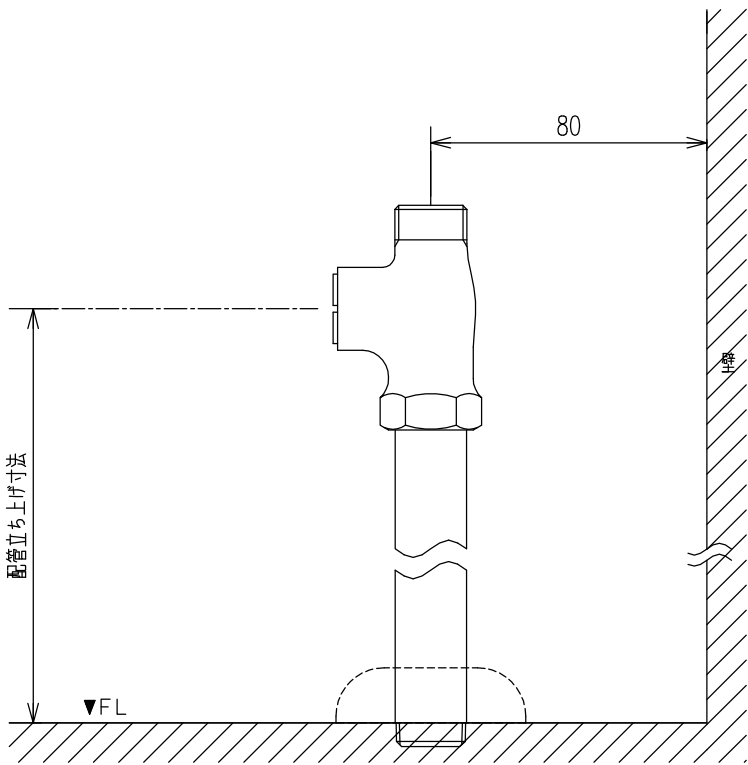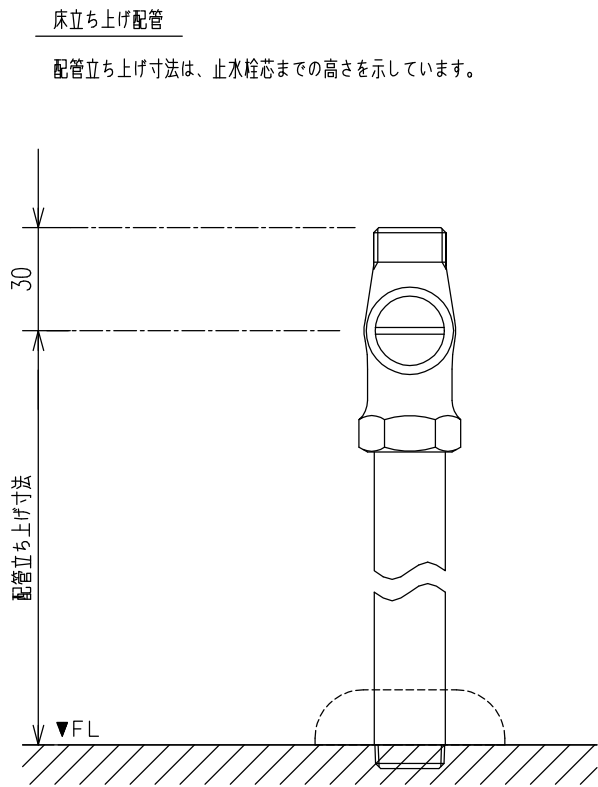


■ タッチレス水栓ナビッシュ 推奨電源位置図


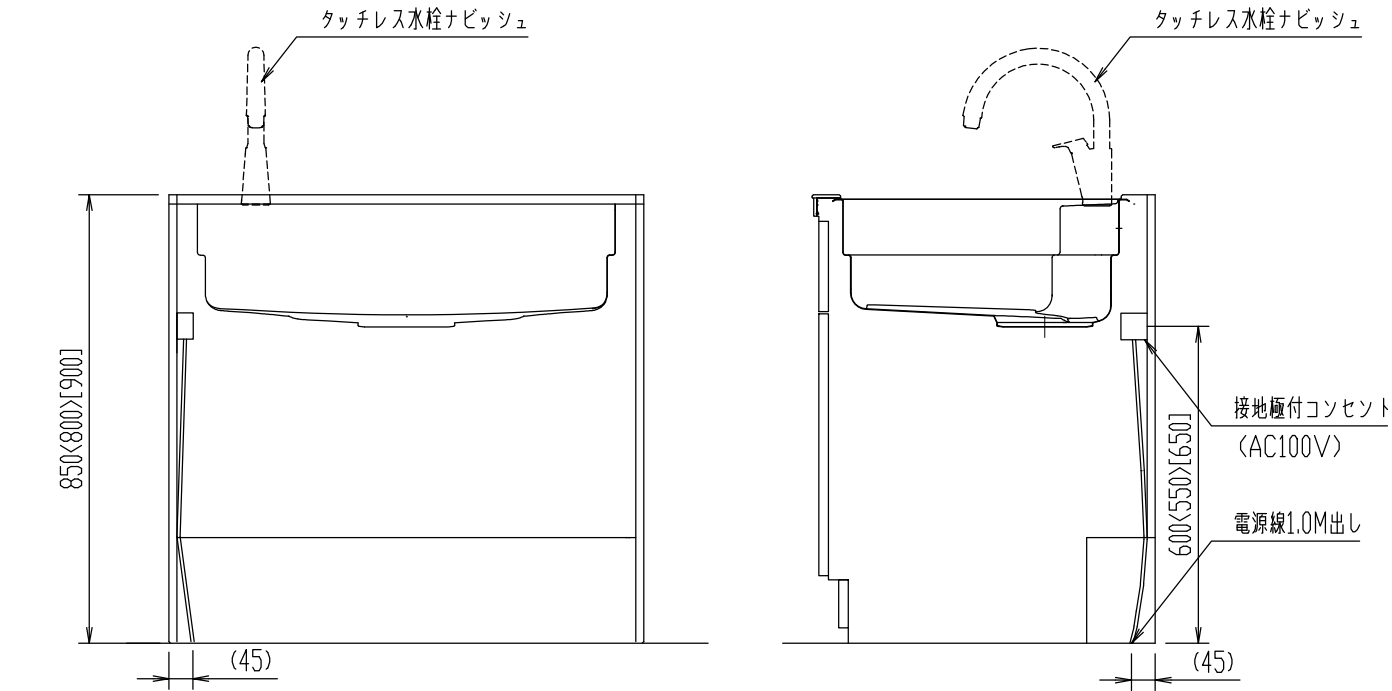


○水栓がシンク右側の場合、電源位置は左右対象の位置にしてください。
○< >内寸法はワークトップ高さ80cmの場合、[]内寸法はワークトップ高さ90cmの場合。

■ キッチン取付者さま向け 動画コンテンツ ■

商品取付けの注意点を2次元コードでご視聴いただけます。
取付日より前に、是非ご確認ください。

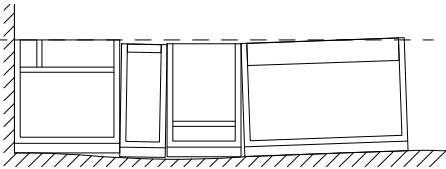荷扱い・搬入	カウンター開梱搬入「養生ツール」	不陸の確認と調整	マグネットキッチンパネル
荷扱い・搬入	カウンター開梱搬入「養生ツール」のご紹介		マグネット キッチンパネル「取付・設置」ポイント
作成日：2024年10月01日	作成日：2024年10月01日	作成日：2024年02月07日	作成日：2024年03月06日



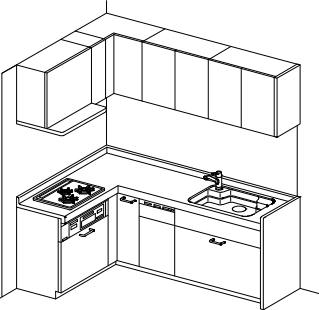
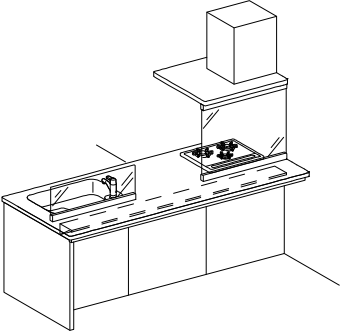
人造大理石カウンターL型キッチン	センターキッチン（ペニンシュラ型）		
			
作成日：2024年02月07日	作成日：2024年02月07日		

--	--	--	--

特記事項 扉色 KK5:ブラックスタック 取手 [M]スリム取手 (ブラック) ワークトップカラー 【DW】ソルティホワイト	物件名	寺田慎介 様邸	案件No.	図面名	担当	図面	図番
	仕様	ES21	A2512DDD0EYYK2	機能図	栗野 友仁		株式会社 LIXIL
			見積No.	縮尺	日付		
			M25129443443-001-2		2025.12.01		

■ キッチン取付者さま向け 動画コンテンツ ■

商品取付けの注意点を2次元コードでご視聴いただけます。
取付日より前に、是非ご確認ください。

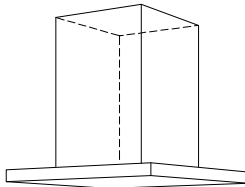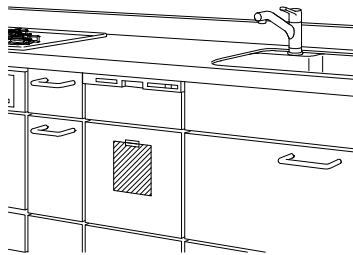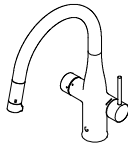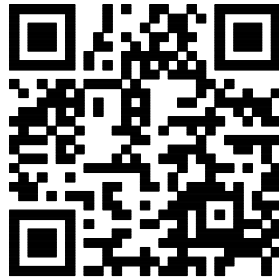センターフード型レンジフード (天吊りフード)  作成日：2024年06月03日 		I H加熱機器関連 I H加熱機器 仕切り板 作成日：2024年02月07日 		食器洗い乾燥機  作成日：2024年02月07日 		ミネラル浄水栓 Greentap  作成日：2024年06月03日 		
	特記事項 扉色 KK5:ブラックスタック 取手 [M]スリム取手 (ブラック) ワークトップカラー 【DW】 ソルティホワイト	物件名 寺田慎介 様邸 仕様 ES21	案件No.		図面名	担当	図面	図番
			A2512DDD0EYYK2		機能図	栗野 友仁		株式会社 LIXIL
			見積No.		縮尺	日付		
			M25129443443-001-2			2025.12.01		