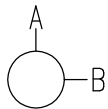
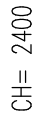


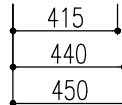
面



A面



面

[illegible]

【ご注意】

- 記載のキャビネット寸法は扉前面までの呼び寸法です。キャビネット本体の寸法・扉厚等商品は商品ガイドの巻末資料をご確認ください。
- 記載のワークトップ、カウンター、エンドパネル、サイドパネルの寸法は呼び寸法です。詳細寸法は商品ガイドの巻末資料をご確認ください。

特記事項 扉色 KK5:ブラックスタック 取手 [M]スリム取手 (ブラック)	物件名	寺田 慎介 様邸	案件No.	図面名	担当	図面	図番 : 株式会社 LIXIL
			A2512DDDD0EYYK2	レイアウト図	栗野 友仁		
	仕様	ES21	見積No.	縮尺	日付		
			M25129443443-001-3	1/30	2025.12.01		



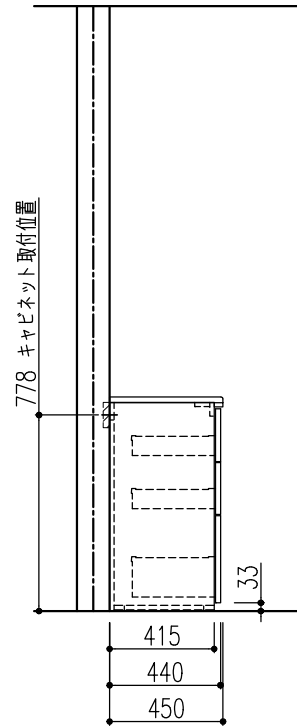
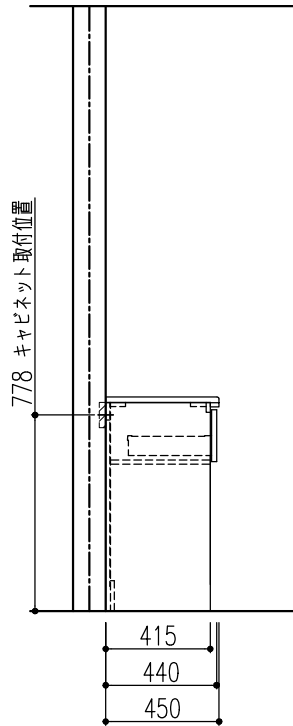
【ご注意】

- 記載のキャビネット寸法は扉前面までの呼び寸法です。キャビネット本体の寸法・扉厚等は商品ガイドの巻末資料をご確認ください。
- 記載のワークトップ、カウンター、エンドパネル、サイドパネルの寸法は呼び寸法です。詳細寸法は商品ガイドの巻末資料をご確認ください。
- 取付・設置に際し、各製品の取付・設置説明書や図面の機能図を必ずお読み下さい。

特記事項 扉色 KK5:ブラックスタック 取手 [M]スリム取手（ブラック）	物件名	寺田 慎介 様邸	案件No.	図面名	担当	図面	図番 : 株式会社 LIXIL
			A2512DDD0EYYK2	納まり図	葉野 友仁		
	仕様	ES21	見積No.	縮尺	日付		
			M25129443443-001-3	1/30	2025.12.01		

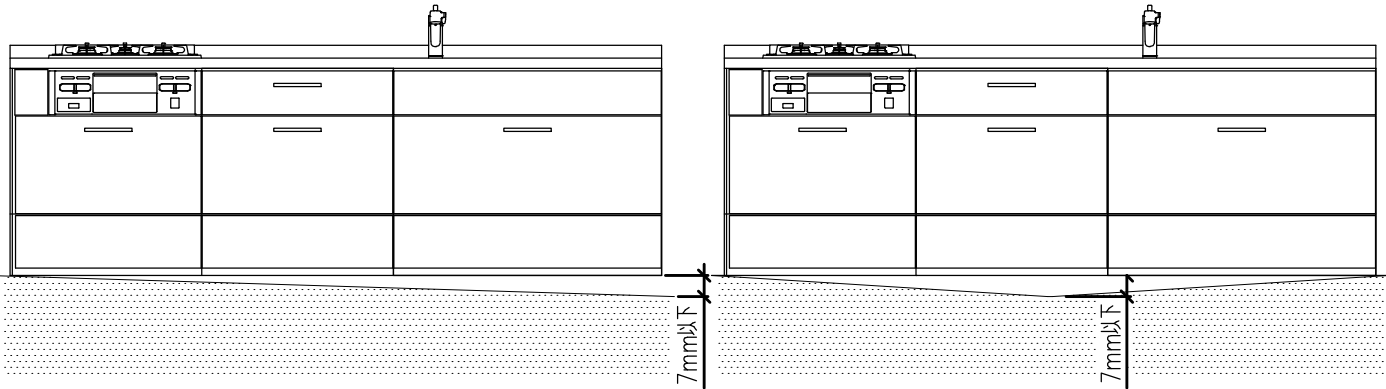
B面

B面



特記事項 扉色 KK5:ブラックスタック 取手 [M]スリム取手 (ブラック)	物件名	寺田慎介 様邸	案件No.	図面名	担当	図面	図番
			A2512DDD0EYYK2	納まり図	栗野 友仁		株式会社 LIXIL
	仕様	ES 2 1	見積No.	縮尺	日付		
			M25129443443-001-3	1/30	2025.12.01		

■ 床の不陸に関して

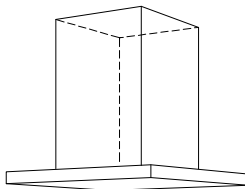
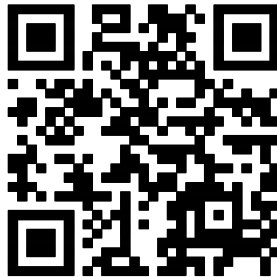
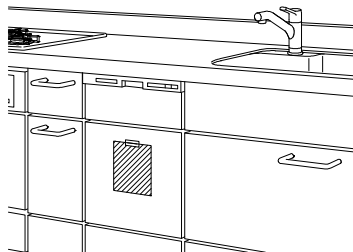
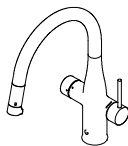
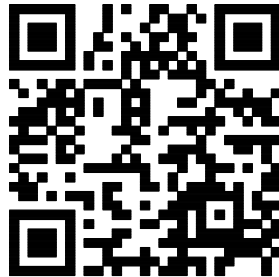


床の不陸は、7 m m 以下に抑えるようにしてください。不陸が大きい場合は、現場責任者に床の修正を依頼してください。
※キャビネット取付時には不陸調整スペーサー等で水平になるように設置してください。

	特記事項 扉色 KK5:ブラックスタック 取手 [M]スリム取手（ブラック）	物件名	寺田慎介 様邸	案件No.	図面名	担当	図面	図番
				A2512DDD0EYYK2	機能図	栗野 友仁		株式会社 LIXIL
		仕様	ES 2 1	見積No.	縮尺	日付		
				M25129443443-001-3		2025.12.01		

■ キッチン取付者さま向け 動画コンテンツ ■

商品取付けの注意点を2次元コードでご視聴いただけます。
取付日より前に、是非ご確認ください。

センターフード型レンジフード (天吊りフード)  作成日：2024年06月03日 		I H加熱機器関連 I H加熱機器 仕切り板 作成日：2024年02月07日 		食器洗い乾燥機  作成日：2024年02月07日 		ミネラル浄水栓 Greentap  作成日：2024年06月03日 			
	特記事項 扉色 KK5:ブラックスタック 取手 [M]スリム取手 (ブラック)	物件名 仕様	寺田慎介 様邸		案件No.	図面名	担当	図面	図番
					A2512DDD0EYYK2	機能図	栗野 友仁		
			ES21		見積No.	縮尺	日付		
					M25129443443-001-3		2025.12.01		

株式会社 LIXIL