



●ベーシアハーモJタイプ取付最小スペース

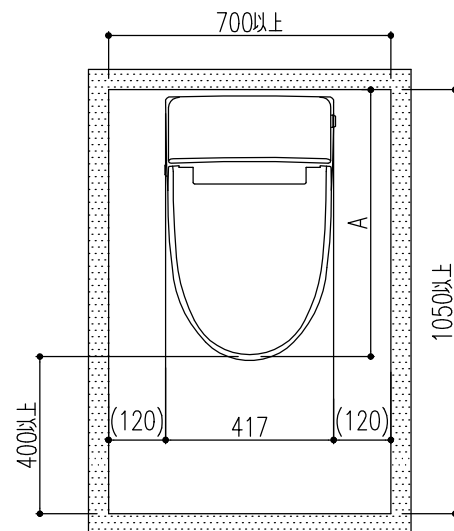


- ※ 最少スペースはA寸法(前出寸法)+400となり、便器排水方向や既設配管により、異なります。
- ※ 上図の空間寸法は、衣服の着脱などの行為に必要な最低寸法です。手すりや紙巻器などの機器を併設する場合は、必要に応じて広い空間が必要になります。
- ※ 便器に向かって左右共に120mm以上の空間を確保してください。

● ベーシアハーモJタイプ便フタ開時寸法

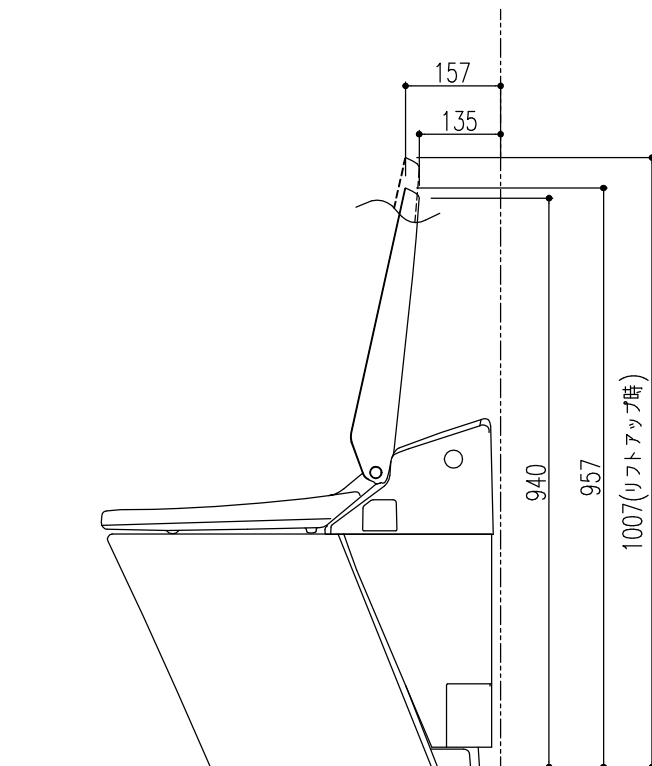

- ※上図は代表商品のイメージ図です。
※防振シートを組み合わせる場合は、全体が5mm高くなります。

●便器床設置面寸法・固定穴寸法

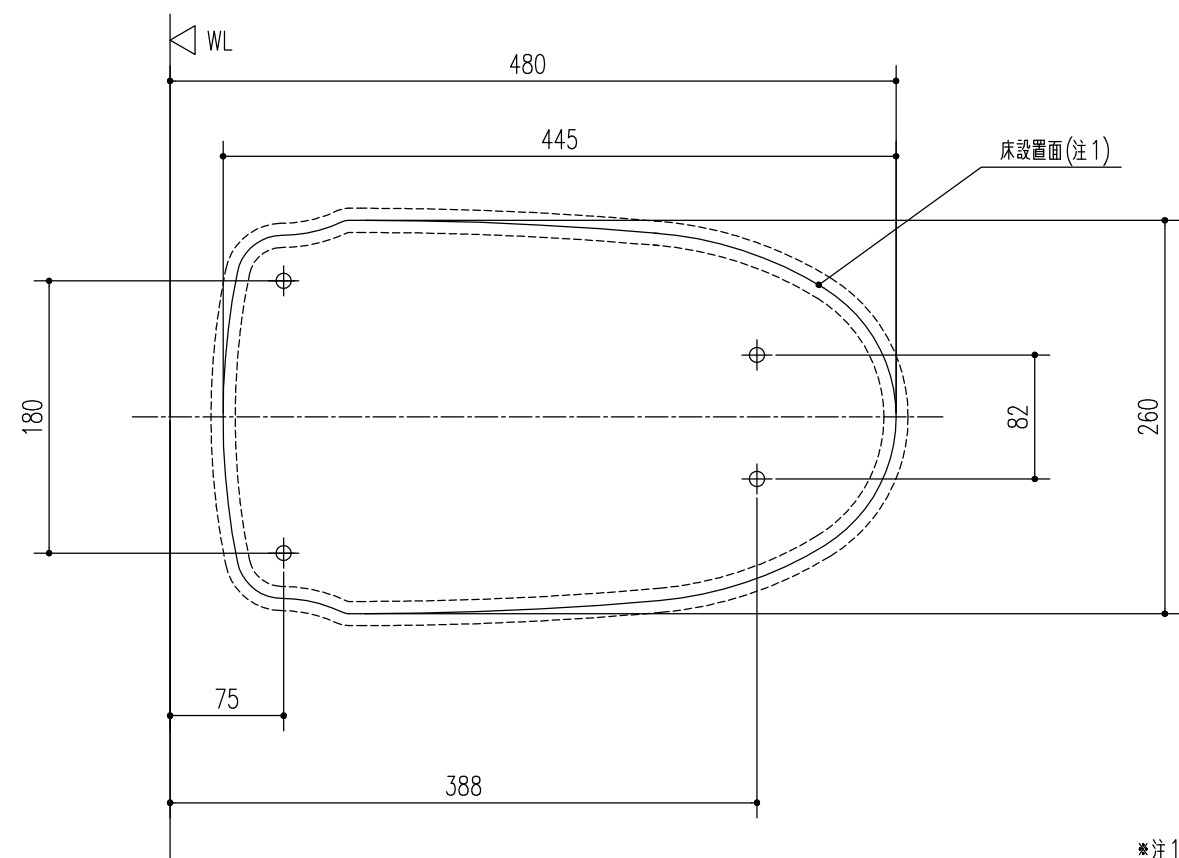


※注1:破線は±5%許容差範囲

●給排水の位置決めと取出し


給水管、排水管を取り出します。

- ※ 右給水の場合は、排水管を中心に左右反対の位置に給水管を取り出してください。
※ 右給水の場合は、給水ホース(322-1135-62)を別途手配してください。

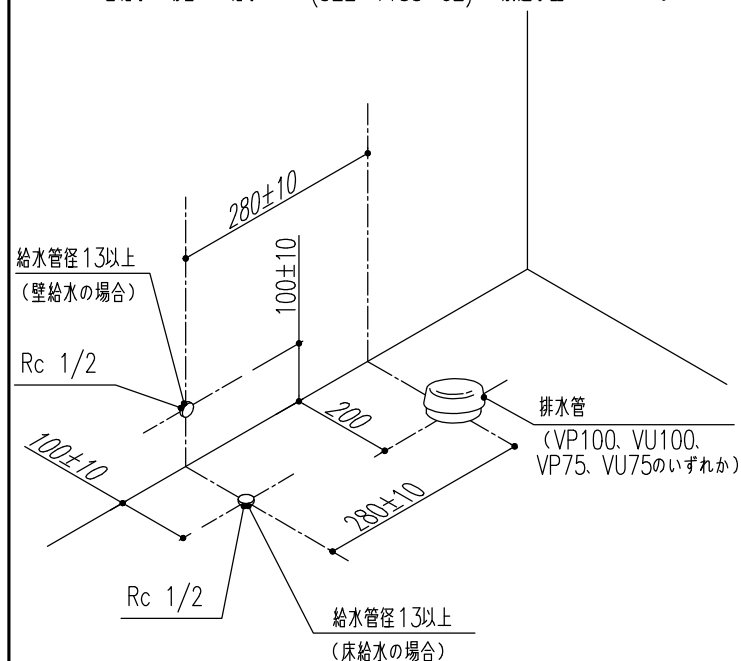


●排水塩ビ管の接続

- ※ 排水芯200のみの対応です。
- ※ 接続は、塩ビ接着剤にて確実に行って下さい。
- ※ 接続(接着)位置及び立ち上げ高さは、配管サイズにより異なります。

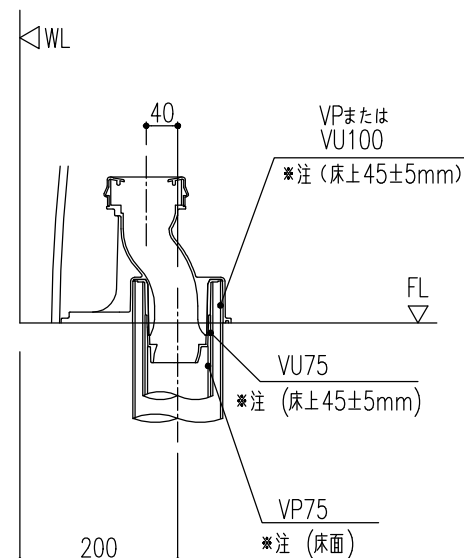



*注…防振シートを組み合わせる場合は5mm高くしてください。

●コフレルスリム(壁付)施工例

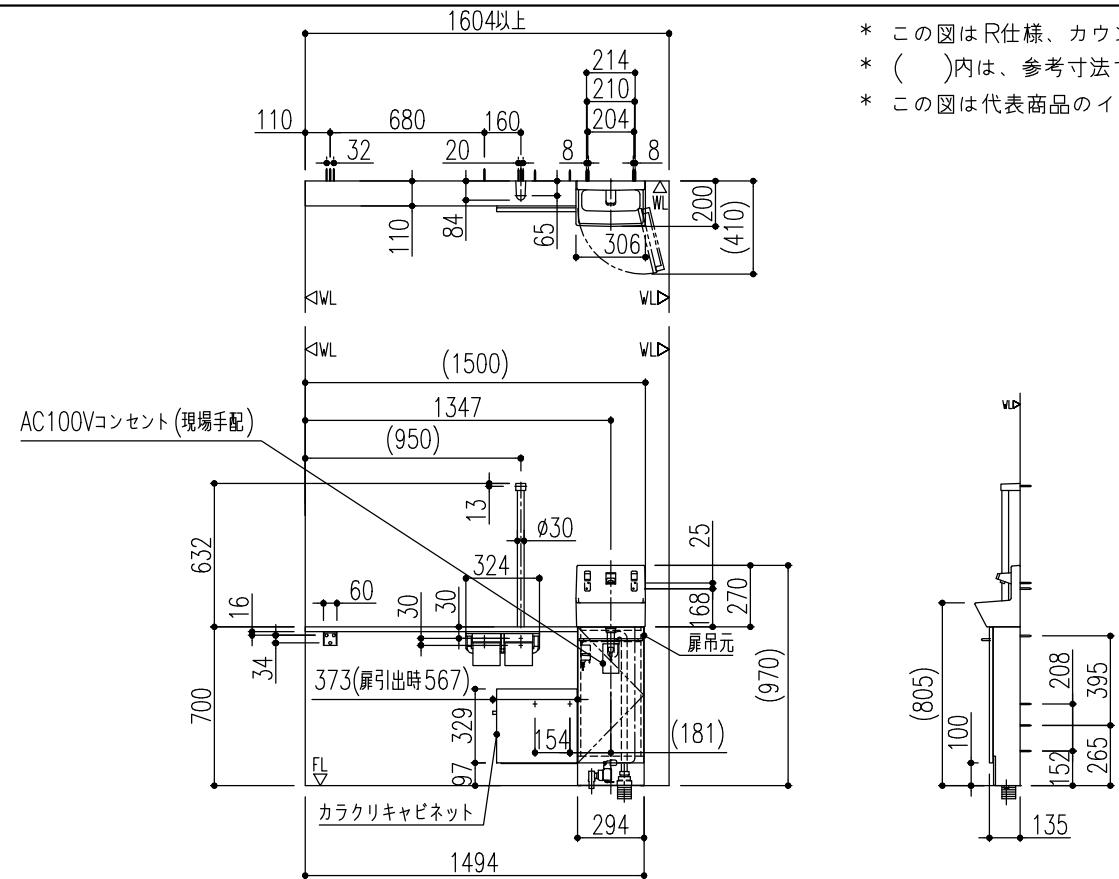

- * この図はR仕様、カウンター1500タイプです。
- * ()内は、参考寸法です。
- * この図は代表商品のイメージ図です。

	特記事項	物件名	寺田 慎介 様邸	案件No.	図面名	担当	図面	図番 : 株式会社 LIXIL
				A2512DDD0EYYK2	機能図	栗野 友仁		
		仕様	ベーシアハーモJタイプ/ECO5 床排水 一般地・水抜方式・流動方式兼用	見積No.	縮尺	日付		
				M25129443443-001-6		2025.12.01		

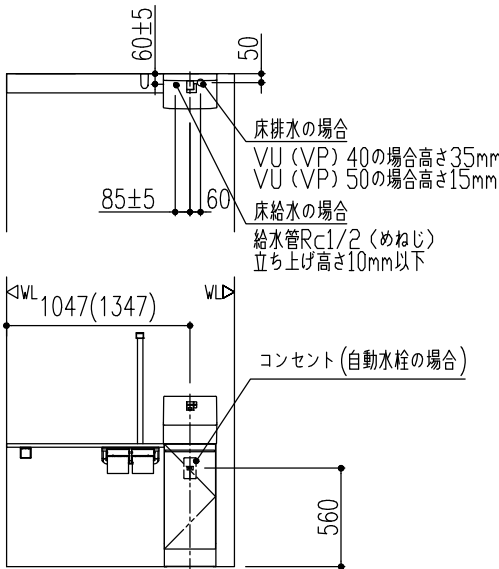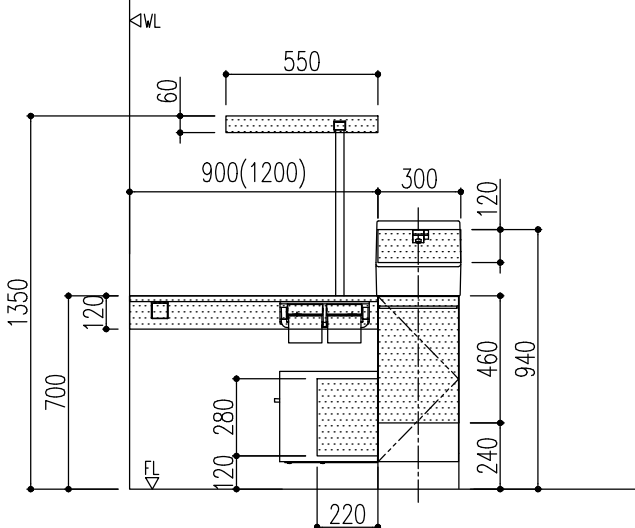●コフレルスリム(壁付)給排水・コンセント位置		●補強木位置							
* 下図は1200サイズの場合を示し、 ()内寸法は、1500サイズの場合を示します。 【カウンター長さ注文サイズ対応】 * 下図は1000～1190の場合を示し、 ()内寸法は、1210～1490の場合を示します。 * 自動水栓の場合は下図を参照し、コンセントを設置してください。 * 温水自動水栓の場合は、D種接地工事が必要です。 アースターミナル付接地極付コンセントを使用してください。 		* 下図は1200サイズの場合を示し、 ()内寸法は、1500サイズの場合を示します。 【カウンター長さ注文サイズ対応】 * 下図は1000～1190の場合を示し、 ()内寸法は、1210～1490の場合を示します。 * 取付強度を保つために、取付部に下地補強木 (厚さ30mm以上)を入れてください。 							
	特記事項	物件名	寺田慎介 様邸	案件No.	図面名	担当	図面	図番	
				A2512DDD0EYYK2	機能図	栗野 友仁		株式会社 LIXIL	
				見積No.	縮尺	日付			
				M25129443443-001-6		2025.12.01			
仕様			ベーシアハーモJタイプ/EC05 床排水 一般地・水抜方式・流動方式兼用						

排水塩ビ管の接続

- * 排水芯200のみの対応です。
- * 接続は、塩ビ接着剤にて確実にこなして下さい。
- * 接続(接着)位置及び立ち上げ高さは、配管サイズにより異なります。

YBC-J22S

洋風ダイレクトバルブ防露便器<シャートイル>

節水 洗浄水量:大5L、小3.8L

品番	品名	数
YBC-J22S	便器部	1
DV-J223G	機能部	1
YL-DA82SCHB	手洗キャビネット	1

* 製品両側面に120mm以上、背面に15mm以上の空留確保。

* 設置前に水压判定治具(CWA-234)で、水压の確認を行ってください。

* 静水压0.15MPa、流動圧0.05MPa(瞬間流量13L/min)以上が必要。

* 最高水压0.75MPa以下(静水压)。* 給水管呼び径13以上。

* D種接地工事必要。アースミナ付接地極付コンセントを使用のこと。

* 一般地用、寒冷地用排水式、寒冷地用流動式を兼用。* 凍結防止には器具への通電が必要。

【寒冷地用排水式の場合】トイレ内使用限界:0℃以上(室内暖房)、器具の水抜き。

【寒冷地用流動式の場合】トイレ内使用限界:0℃以上(室内暖房)、流動水量40L/h。

* トイレ開口780mm。

* 手洗キャビネット取付位置先方指定。

縮尺	製図	森下	校図	松田	備考	GE
1:20	図番	XS-CJ22S-100082A				
2023.12.15	株式会社 LIXIL					

* ()内は、参考寸法。

* インバータ照明により誤作動する場合あり。

* 機能部上部に棚を設置する場合は床から1050mm以上の空間が必要。

備考)・同梱の止水栓は壁給水、床給水の双方に使用可能。

・右給水の場合は、オプション給水ホース(322-1135-62)を別途手配する。

陶器寸法許容差はJIS A5207に準ずる。 壁取付商品には、補強木による壁補強が必要です。詳しくは、商品別「壁補強」一覧を参照ください。

