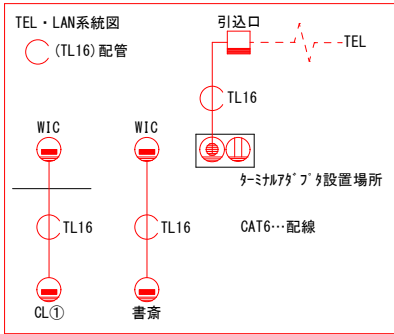
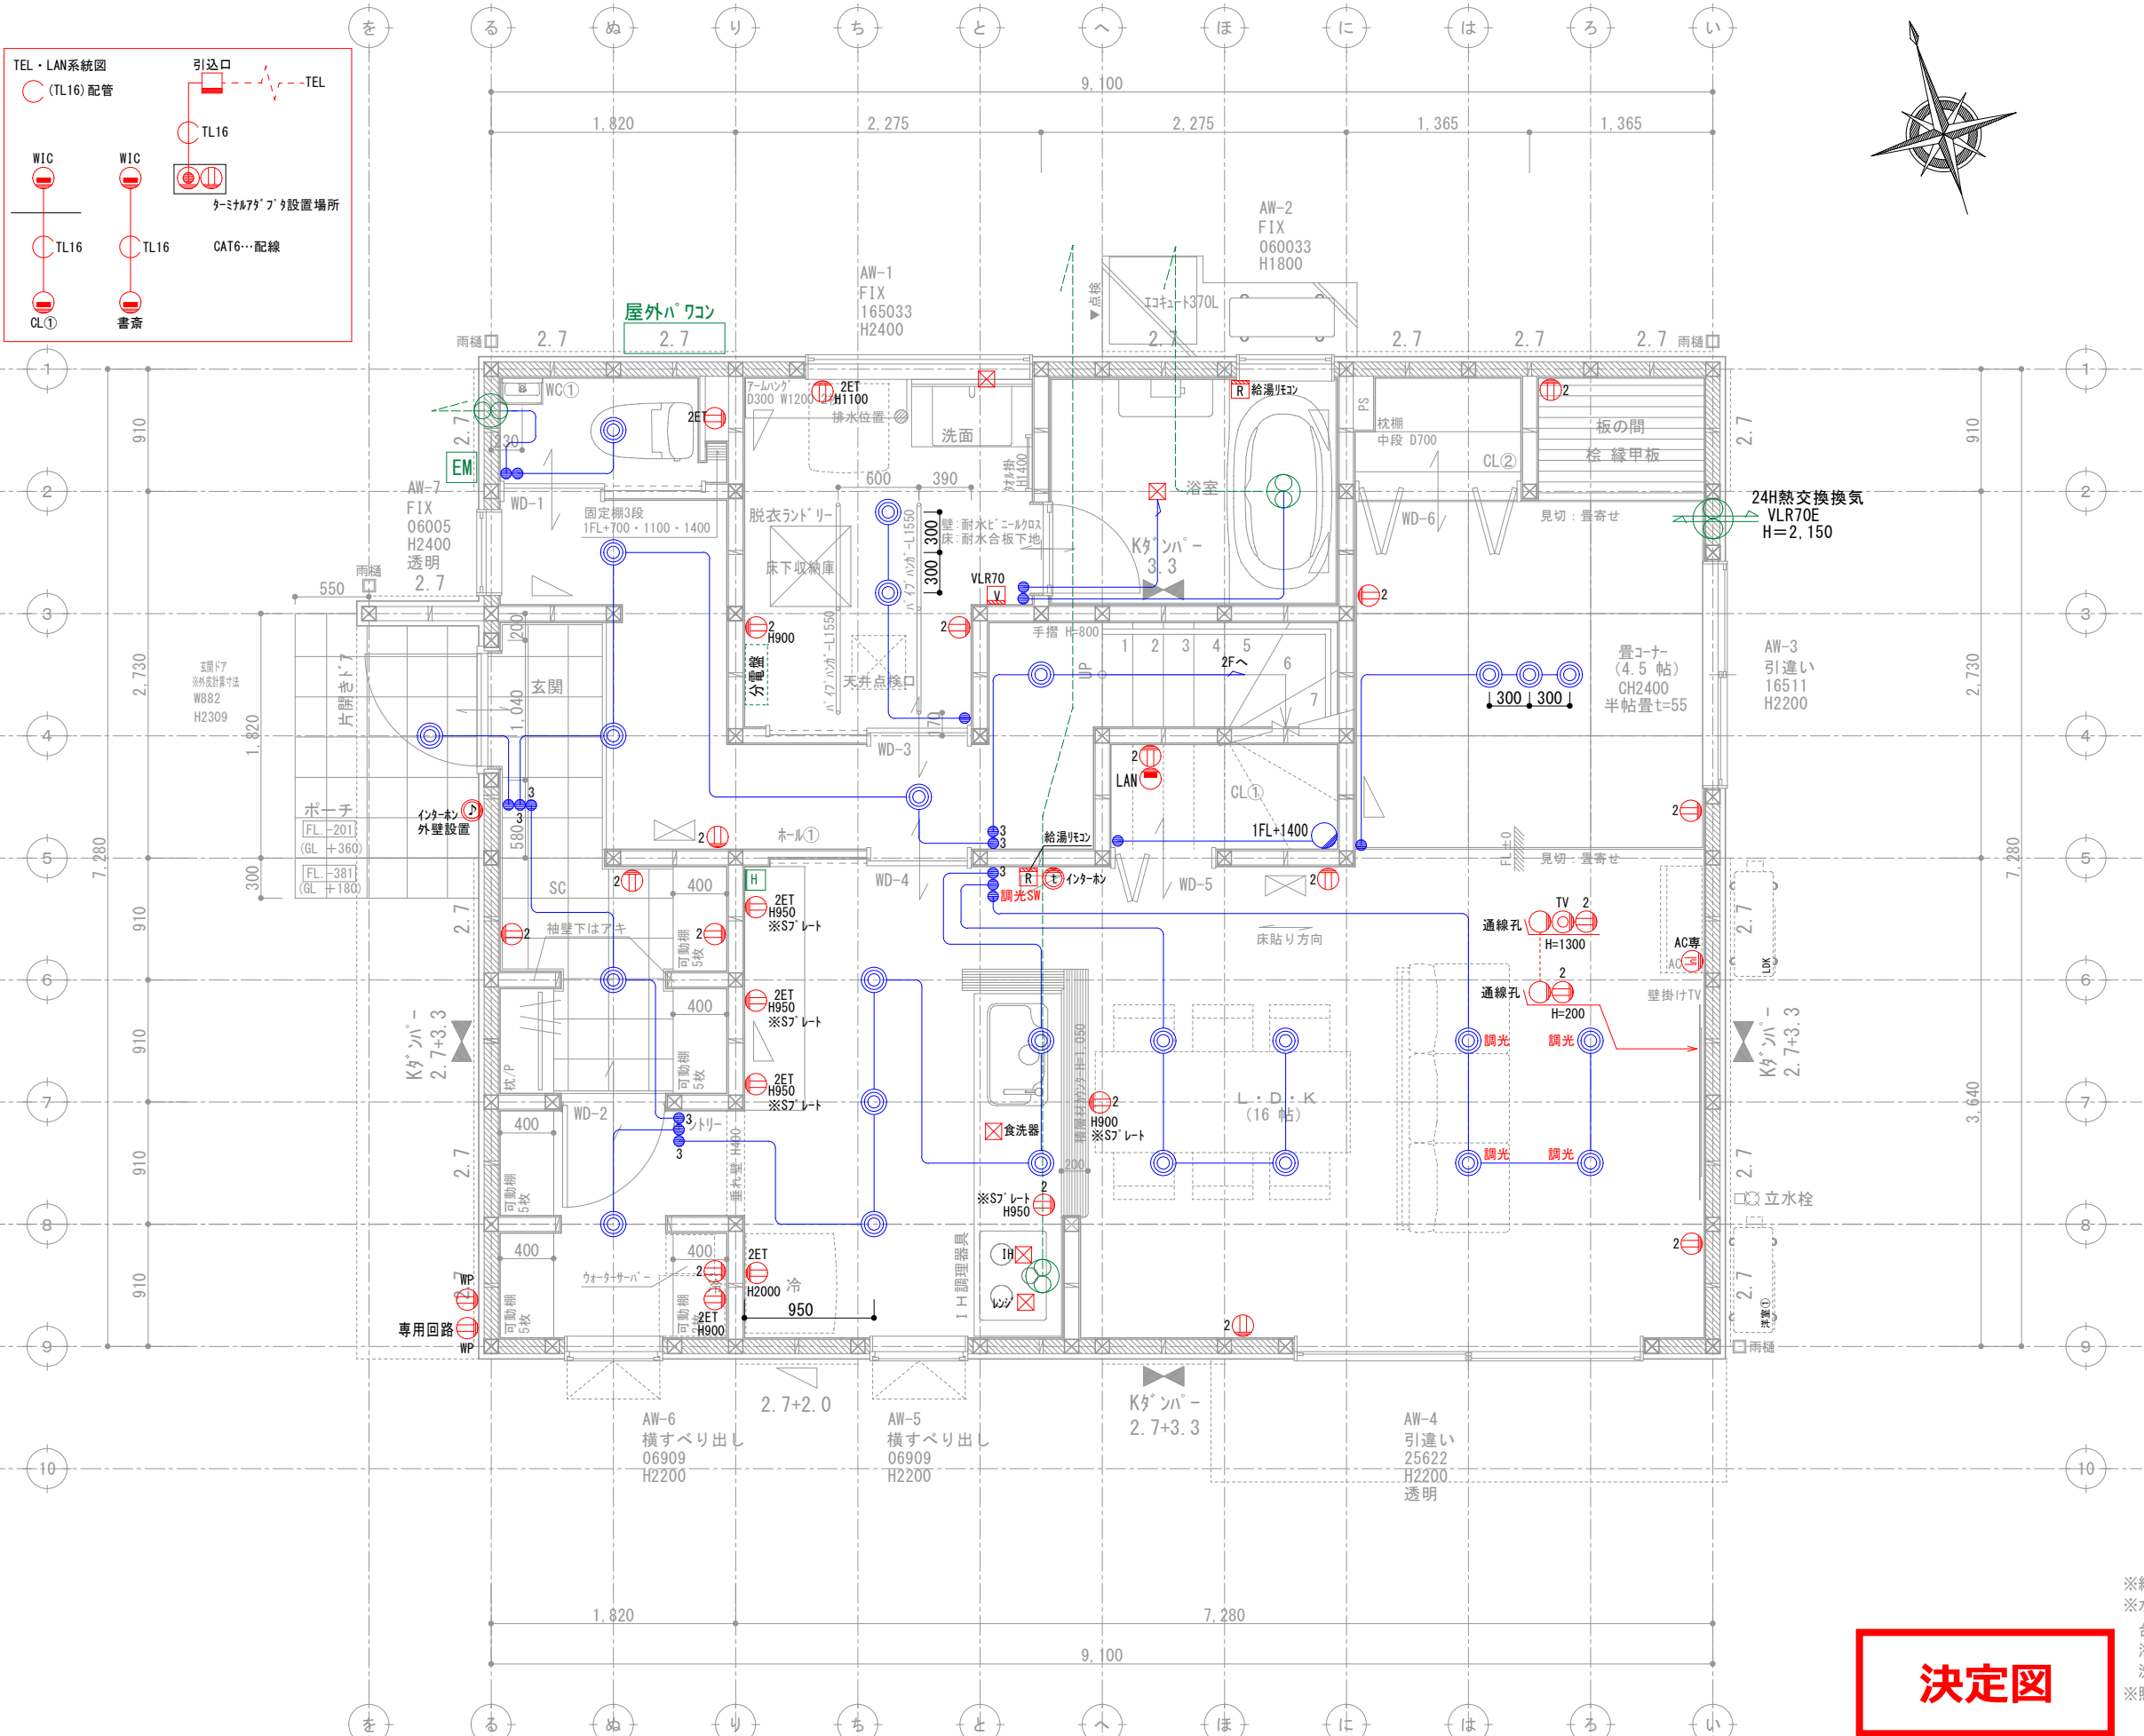


G2

壁付け 住宅用火災報知器			数量
H	熱感知器	電池式(単独型)	1
	露出型		
壁付け 住宅用火災報知器			数量
S	煙感知器	電池式(単独型)	
	露出型		

- ※ 煙感知器は壁・梁より600mm以上離す
壁に取付ける場合、
天井から150mm以上500mm以内離す
換気扇・エアコン吹出口から1500mm以上離す
- ※ 全室LED照明とする。
- ※ 標準天井高さ2,400
- ※ 特記無きガラスは型ガラス

- * 凡例**
- 管柱 (105×105)
 - Kタンパ (3.30倍 FRM-0641)
 - 片筋違い (2.00倍 45×90)
(例 左:柱脚 右:柱頭)
 - たすき掛筋違い (4.00倍 45×90)
 - 構造用合板 (2.70倍)
(t=9 タイプ-EXハイパー)
 - 床点検口
 - 天井点検口
 - 換気扇
 - 熱交換換気扇VLR-70

脱衣・ランドリー 仕上材
天井: ア9.5PB下地ビニルクロス貼り
壁: ア12.5PB下地ビニルクロス貼り
床: ア24+15耐水合板下フロアタイル張り

階段寸法表	
有効幅	750
踏面	210
蹴上	207.15

※下屋部分点検口について
ダウンライト、FS天井点検口、UB点検口より
ポールカメラやファイバースコープ等の
検査機器等を使用して点検する

- ※給水設備: ヘッダー分岐後の全ての配管径は13A以下とする
- ※水栓: 一般社団法人日本バルブ工業会の定義による節湯水栓
台所: 2バルブ水栓以外のその他の水栓(水優先吐水機能)
浴室シャワー: 2バルブ水栓以外のその他の水栓(小流量吐水機能)
洗面: 2バルブ水栓以外のその他の水栓(水優先吐水機能)
- ※照明設備: 全室LED照明とし居室においては調光制御、非居室においては
人感センサーを採用する

決定図