

■ 仕 様		■ HEAT20	G2
断熱工事	■ 床:ネオマフォーム t90 ■ 土間床等の外周:スタイロフォームAT t50 ■ 壁:アクアフォームLITE吹付 t90 ■ 天井:アクアフォームLITE吹付 t220		
床下換気	■ 基礎パッキン JOTO (玄関・UB周り:気密基礎パッキン)		
防虫防蟻	■ 土壌処理・木部 ガントナーMC		

■ 外 部 仕 上 表	■ 22条地域
-------------	---------

部位		仕上・仕様・メーカー	色番・品番
屋根		■ ガルバリウム鋼板(t0.35)UK立平 ニスカカラーPro GH 軒先通気金物 日本住環境株式会社【REV-15】	GHK01 Sブラック
パラペット笠木		■ なし	
破風・鼻隠		■ なし	
雨樋	(軒樋)	■ Panasonic サーフেসケアFS-I型	ブラック
	(縦樋)	■ Panasonic 瞬水S15	ブラック
軒天	屋根軒	■	
	ポーチ軒	■ 神島化学 t= 6mm 軒天ボード エンボス	Wチャコールブラック
	バルコニー軒	■ 神島化学 t= 6mm 軒天ボード エンボス	Wチャコールブラック
オーバーハング水切り		■ ガルバリウム鋼板 ※外壁合わせ JOTO:HF-A3550	ブラック
外壁	通気金物(15mm)	■メイン Knewエクセレージ・シマンフラット 光セラ	ソイル チタン マルーンブラック
	※下地面材:タイガーEXハイパー	■アクセントA なし	
	防火認定 PC030BE-4028	■アクセントB なし	
玄関ポーチ		■ 床 玄関タイルに同じ	-
基礎		■ 立上り巾木: モルタル刷毛引き	-
基礎水切り金物		■ JOTO鋼板製 防鼠材付き水切り JOTO:WMF-N35	ブラック
バルコニー	床・内壁	■ 床:FRP防水仕上(グレー) 壁:外壁同仕上げ	-
	笠木	■ アルミ笠木	ブラック
外部建具		■ LIXIL EW(アルゴン)ガス高遮熱仕様LowEトリプルガラス クリア ・SD、TSは、メーカー設定による。 ・オペレーター付サッシの場合は固定網戸とする ・グレモンハンドル式サッシの場合は可動網戸とする	外観 ブラック 内観 ホワイト ※樹脂パッキン・網戸付
シャッター		■ なし	
軒天通気金物			
玄関扉		■ LIXIL ジェスタ2 K2仕様 LIXILファミロック タグキー×3 (電池式)	ドア型: M17 型 ドア色: マットブラック ハンドル: S型ハンドル 色: ブラック
外部物干し金物		■ 川口技研RK型-55 外壁付	ブラック
換気フード	■ 局所換気扇(トイレ 浴室 キッチンフード) 防火ダンパー無		外気フード: ブラック
	■ ダクトレス熱交換換気システム (日本スティーベル株式会社) VLR-70E		外気フード: B ブラック 室内パネル: ホワイト
	防火ダンパー無		

■ 構 造 概 要			
基礎	■ RCベタ基礎コンクリート		
通し柱・管柱	■ 構造用集成材 105×105	間柱	■ 集成材
土台	■ 桧 105×105 大引き ■ 桧 90*90	筋交い	■ 構造用製材 火打梁 ■ 鋼製火打(当社基準により米松あり)
桁・梁	■ 構造用製材及び集成材	制震装置	■ Kダンパー (株)アイ・エム・エー

■ 設 備 装 着 品			
-------------	--	--	--

住宅設備	部位	メーカー	商品名	※ 詳細は見積り、プレゼン参照	見積りNo.	(日付)
	キッチン	LIXIL	■ ES		見積り番号	: M25129443443-002-2 (日付) 2025.12.01
	バックカウンタ ※オプション	LIXIL	■ ES		見積り番号	: M25129443443-002-3 (日付) 2025.12.01
	浴室	LIXIL	■ AX1620 PGハウス標準仕様		見積り番号	: M25129443443-002-1 (日付) 2025.12.01
	1Fトイレ	LIXIL	■ ベーシアシャワートイレ 白 ● タオル掛け: なし(支給品取付) タンク手洗 無し ● 紙巻き器: なし(支給品取付)		見積り番号	: M25129443443-002-6 (日付) 2025.12.01
	2Fトイレ	LIXIL	■ ベーシアシャワートイレ 白 ● タオル掛け: なし(支給品取付) タンク手洗 有り ● 紙巻き器: なし(支給品取付)		見積り番号	: M25129443443-002-7 (日付) 2025.12.01
	1F 洗面台	LIXIL	■ EV その他 ● タオル掛け: KF-AA71D(バー)		見積り番号	: M25129443443-002-4 (日付) 2025.12.01
	2F 洗面台	LIXIL	■ EV その他 ● タオル掛け: KF-AA71D(バー)		見積り番号	: M25129443443-002-5 (日付) 2025.12.01
			1階トイレ コフレルスリム 有			
給排水設備	給湯器	■ エコキュート370L Panasonic Sシリーズ スタンダードモデル 追い焚きフルオート				
	排水	■ 下水				
	外水栓	■ 1 カ所 (平面図参照)		■ 外部立栓柱: PVC製 水栓柱12型【前澤化成工業】		
	外部ガーデンパン	■ 無し				
	その他	■ 洗濯機用単水栓: 緊急止水弁付		■ 洗濯機用排水: トラップ金物(標準)		
		■ 排水さや管(長期優良住宅仕様)				
ガス配管設備		■ なし (配置図・平面図参照) ■ ガス使用器具				
電気設備	インターホン	■ パナソニック VL-SE31XL				
	TVアンテナ	■ UHF + BS・110度CS／CSアンテナ [2K・4K・8K対応] ■ブラック ※電波状況によりホワイトになる可能性あり				
	エアコン	■ 設置場所:				
	ソーラー	■ あり(Qセルズ) 12 枚 5.28 KW Re.RISE-G3 440 (1722×1134×30)				
	※標準搭載	※メーカーのモデルチェンジ等で後継品に変更される可能性あり				
		■ 屋外パワコン				
その他						
		決定図				

決定図

	浜 岡 一 級 総 合 設 計 事 務 所 一級建築士事務所 静岡県知事登録第 (10)2441 号 一級建築士 大臣登録第 365879 号 西原利昌	 PG HOUSE 株式会社 LIFEFUND InDesign office 一級建築士事務所 事務所登録 (2) 第7596号 一級建築士登録 第179770号 鈴木 達男 〒432-8023 静岡県浜松市中央区鴨江3丁目70番23号	年 月 日	件名		設計	IC	工務	図 番
			2026.1.10	寺田慎介 様邸 新築工事		酒井		青島	1-1
			縮尺	図面					
				仕上表 1					

内 部 仕 上 表 （壁下地:石膏ボード12.5mm/天井下地:9.5mm）※脱衣室:床合板特類 下地									
階		床	巾木	壁	品番	廻 縁	天 井	品番	特記事項
1F	ポーチ	LIXIL/パセオ300/PSO-BR 2							
	玄関	LIXIL/パセオ300/PSO-BR 2	ライン巾木(W)	ビニルクロス	SLP-340	突付	ビニルクロス	SLP-340	
	SC	LIXIL/パセオ300/PSO-BR 2	ライン巾木(W)	ビニルクロス	SLP-340	突付	ビニルクロス	SLP-340	
	ホール①	イクタ プリオスjapan サンドオーク2P	ライン巾木(W)	ビニルクロス	SLP-340	突付	ビニルクロス	SLP-340	
	LDK	イクタ プリオスjapan サンドオーク2P	ライン巾木(W)	ビニルクロス	SLP-340	突付	ビニルクロス	SLP-340	
	パントリー	イクタ プリオスjapan サンドオーク2P	ライン巾木(W)	ビニルクロス	SLP-340	突付	ビニルクロス	SLP-340	
	畳コーナー	健やかおもて 清流	畳寄せ	ビニルクロス	SLP-340	突付	ビニルクロス	SLP-340	銀鼠色、墨染色
	脱衣ランドリー	フロアタイルt2.3 サンゲツIS-2071	H40ソフト巾木W97	ビニルクロス	SLP-340	突付	ビニルクロス	SLP-340	
	WC①	フロアタイルt2.3 サンゲツIS-2071	H40ソフト巾木W97	ビニルクロス	SLP-340	突付	ビニルクロス	SLP-340	アクセント有
	CL①	イクタ プリオスjapan サンドオーク2P	ライン巾木(W)	ビニルクロス	SLP-340	突付	ビニルクロス	SLP-340	
2F	CL②	イクタ プリオスjapan サンドオーク2P	ライン巾木(W)	ビニルクロス	SLP-340	突付	ビニルクロス	SLP-340	
	ホール②	イクタ プリオスjapan サンドオーク2P	ライン巾木(W)	ビニルクロス	SLP-340	突付	ビニルクロス	SLP-340	
	WC②	フロアタイルt2.3 サンゲツIS-2071	H40ソフト巾木W97	ビニルクロス	SLP-340	突付	ビニルクロス	SLP-340	アクセント有
	洋室①	イクタ プリオスjapan サンドオーク2P	ライン巾木(W)	ビニルクロス	SLP-340	突付	ビニルクロス	SLP-340	アクセント有
	洋室②	イクタ プリオスjapan サンドオーク2P	ライン巾木(W)	ビニルクロス	SLP-340	突付	ビニルクロス	SLP-340	
	洋室③	イクタ プリオスjapan サンドオーク2P	ライン巾木(W)	ビニルクロス	SLP-340	突付	ビニルクロス	SLP-340	
	洋室④	イクタ プリオスjapan サンドオーク2P	ライン巾木(W)	ビニルクロス	SLP-340	突付	ビニルクロス	SLP-340	
	CL③	イクタ プリオスjapan サンドオーク2P	ライン巾木(W)	ビニルクロス	SLP-340	突付	ビニルクロス	SLP-340	
	WIC	イクタ プリオスjapan サンドオーク2P	ライン巾木(W)	ビニルクロス	SLP-340	突付	ビニルクロス	SLP-340	
	書斎	イクタ プリオスjapan サンドオーク2P	ライン巾木(W)	ビニルクロス	SLP-340	突付	ビニルクロス	SLP-340	アクセント有
物入・収納・CL etc		※接続する部屋と同仕様とする							

上 框 ※	■ LIXILランシッサS 上框のみ30×150 色: クリエオーク
階 段	■ LIXIL KA 階段 ササラ: プレシャスホワイト
KA階段で対応できない場合、オプションにてランシッサS階段	段 板 : クリエダーク 蹴込板: プレシャスホワイト ラウト手摺: クリエダーク 手摺金物: ダークアンバー 上段框: クリエオーク 長尺笠木156: LIXIL プレシャスホワイト
窓 枠	■ LIXIL スマート10(玄関以外) 色 プレシャスホワイト ※浴室ドア枠 フクビ3方枠 [ホワイト]
キッチン笠木 カウンター	■ ゴム集成カウンター(オスモカラー) 色 3062707アークリアmatt 形状 L型(ジョイント加工) t=30
天井点検口	■ 天井アルミ点検口枠 450角 TAN45BW フクビ化学工業 ミルキーホワイト
床下収納庫	■ 高気密型床下点検口断熱型 SPF-R6060 城東テクノ 収納付 (脱衣室) ライトグレー(LG)
トイレ棚	■ 2階トイレ D250 アートランパー棚(シェルホワイト)
室内物干し金物	■ シーリングパイプハンガー L1550×2
書斎カウンター	■ ゴム集成カウンター(オスモカラ) 色 3169 ブラック t=25
下足入 プッシュタイプ	■ なし 色 サイズ: 形状:

支給品	■ 無し
備考	※付框は(30×150) プレシャスホワイト 可動棚アートランパー シェルホワイト(パントリー)、パールグレー(脱衣室)、ダークグレー(SC) 棚受金物類は SSホワイト(パントリー)、SSブラック(SC、脱衣室)


内 部 建 具 表							
LIXIL		建具色: プレシャスホワイト 枠色 : 扉同色 ※その他、下記特記による					
ラフィス		把手 : スクエアL (アイアンブラック) 丁番 固定枠(156) 外付戸当り ガイドピン床色合せ 引戸のみ上吊W/フトモーション					
階	No	室名	形式	枠外W サイズ 枠外H サイズ	デザイ ン 建具色	枠色 把手	特記事項
1	1	WC①	片引き戸	— 2400	— —	— —	明り窓・表示錠
	WD						
	2	パントリー	片開き戸	— 2400	— RAA	— —	
	WD						
	3	脱衣ランドリー	片引き戸	— 2400	— RAA	— —	明り窓・表示錠
	WD						
	4	LDK	片引き戸	— 2400	— RAA	— —	
	WD						
	5	CL①	折れ戸	— 2400	— RAA	— —	
	WD						
2	6	CL②	折れ戸	— 2400	— RAA	— —	
	WD						
	7	洋室③	片開き戸	— 2400	— RAA	— —	
	WD						
	8	CL③	折れ戸	— 2400	— RAA	— —	
	WD						
	9	洋室④	片開き戸	— 2400	— RAA	— —	
	WD						
	10	洋室②	片開き戸	— 2400	— RAA	— —	
	WD						
	11	洋室①	片開き戸	— 2400	— RAA	— —	グレー 簡易錠付き
	WD						
	12	WC②	片開き戸	— 2400	— RAA	— —	明り窓・表示錠
	WD						
	13	書斎	片開き戸	— 2400	— RAA	— —	
	WD						
決定図							

袋井市神長地内

G2

求積表

地番	1 21-6			
NO	X _n	Y _n	Y _{n+1} - Y _{n-1}	X _n × (Y _{n+1} - Y _{n-1})
K2	13.475	-2.916	-20.228	-272.572300
K3	10.271	-20.633	-15.158	-155.687818
KT4	-3.769	-18.074	20.228	-76.239332
K1	-0.389	-0.405	15.158	-5.896462
合計				-510.395912
合計面積				255.1979560
地積				255.19 m ²

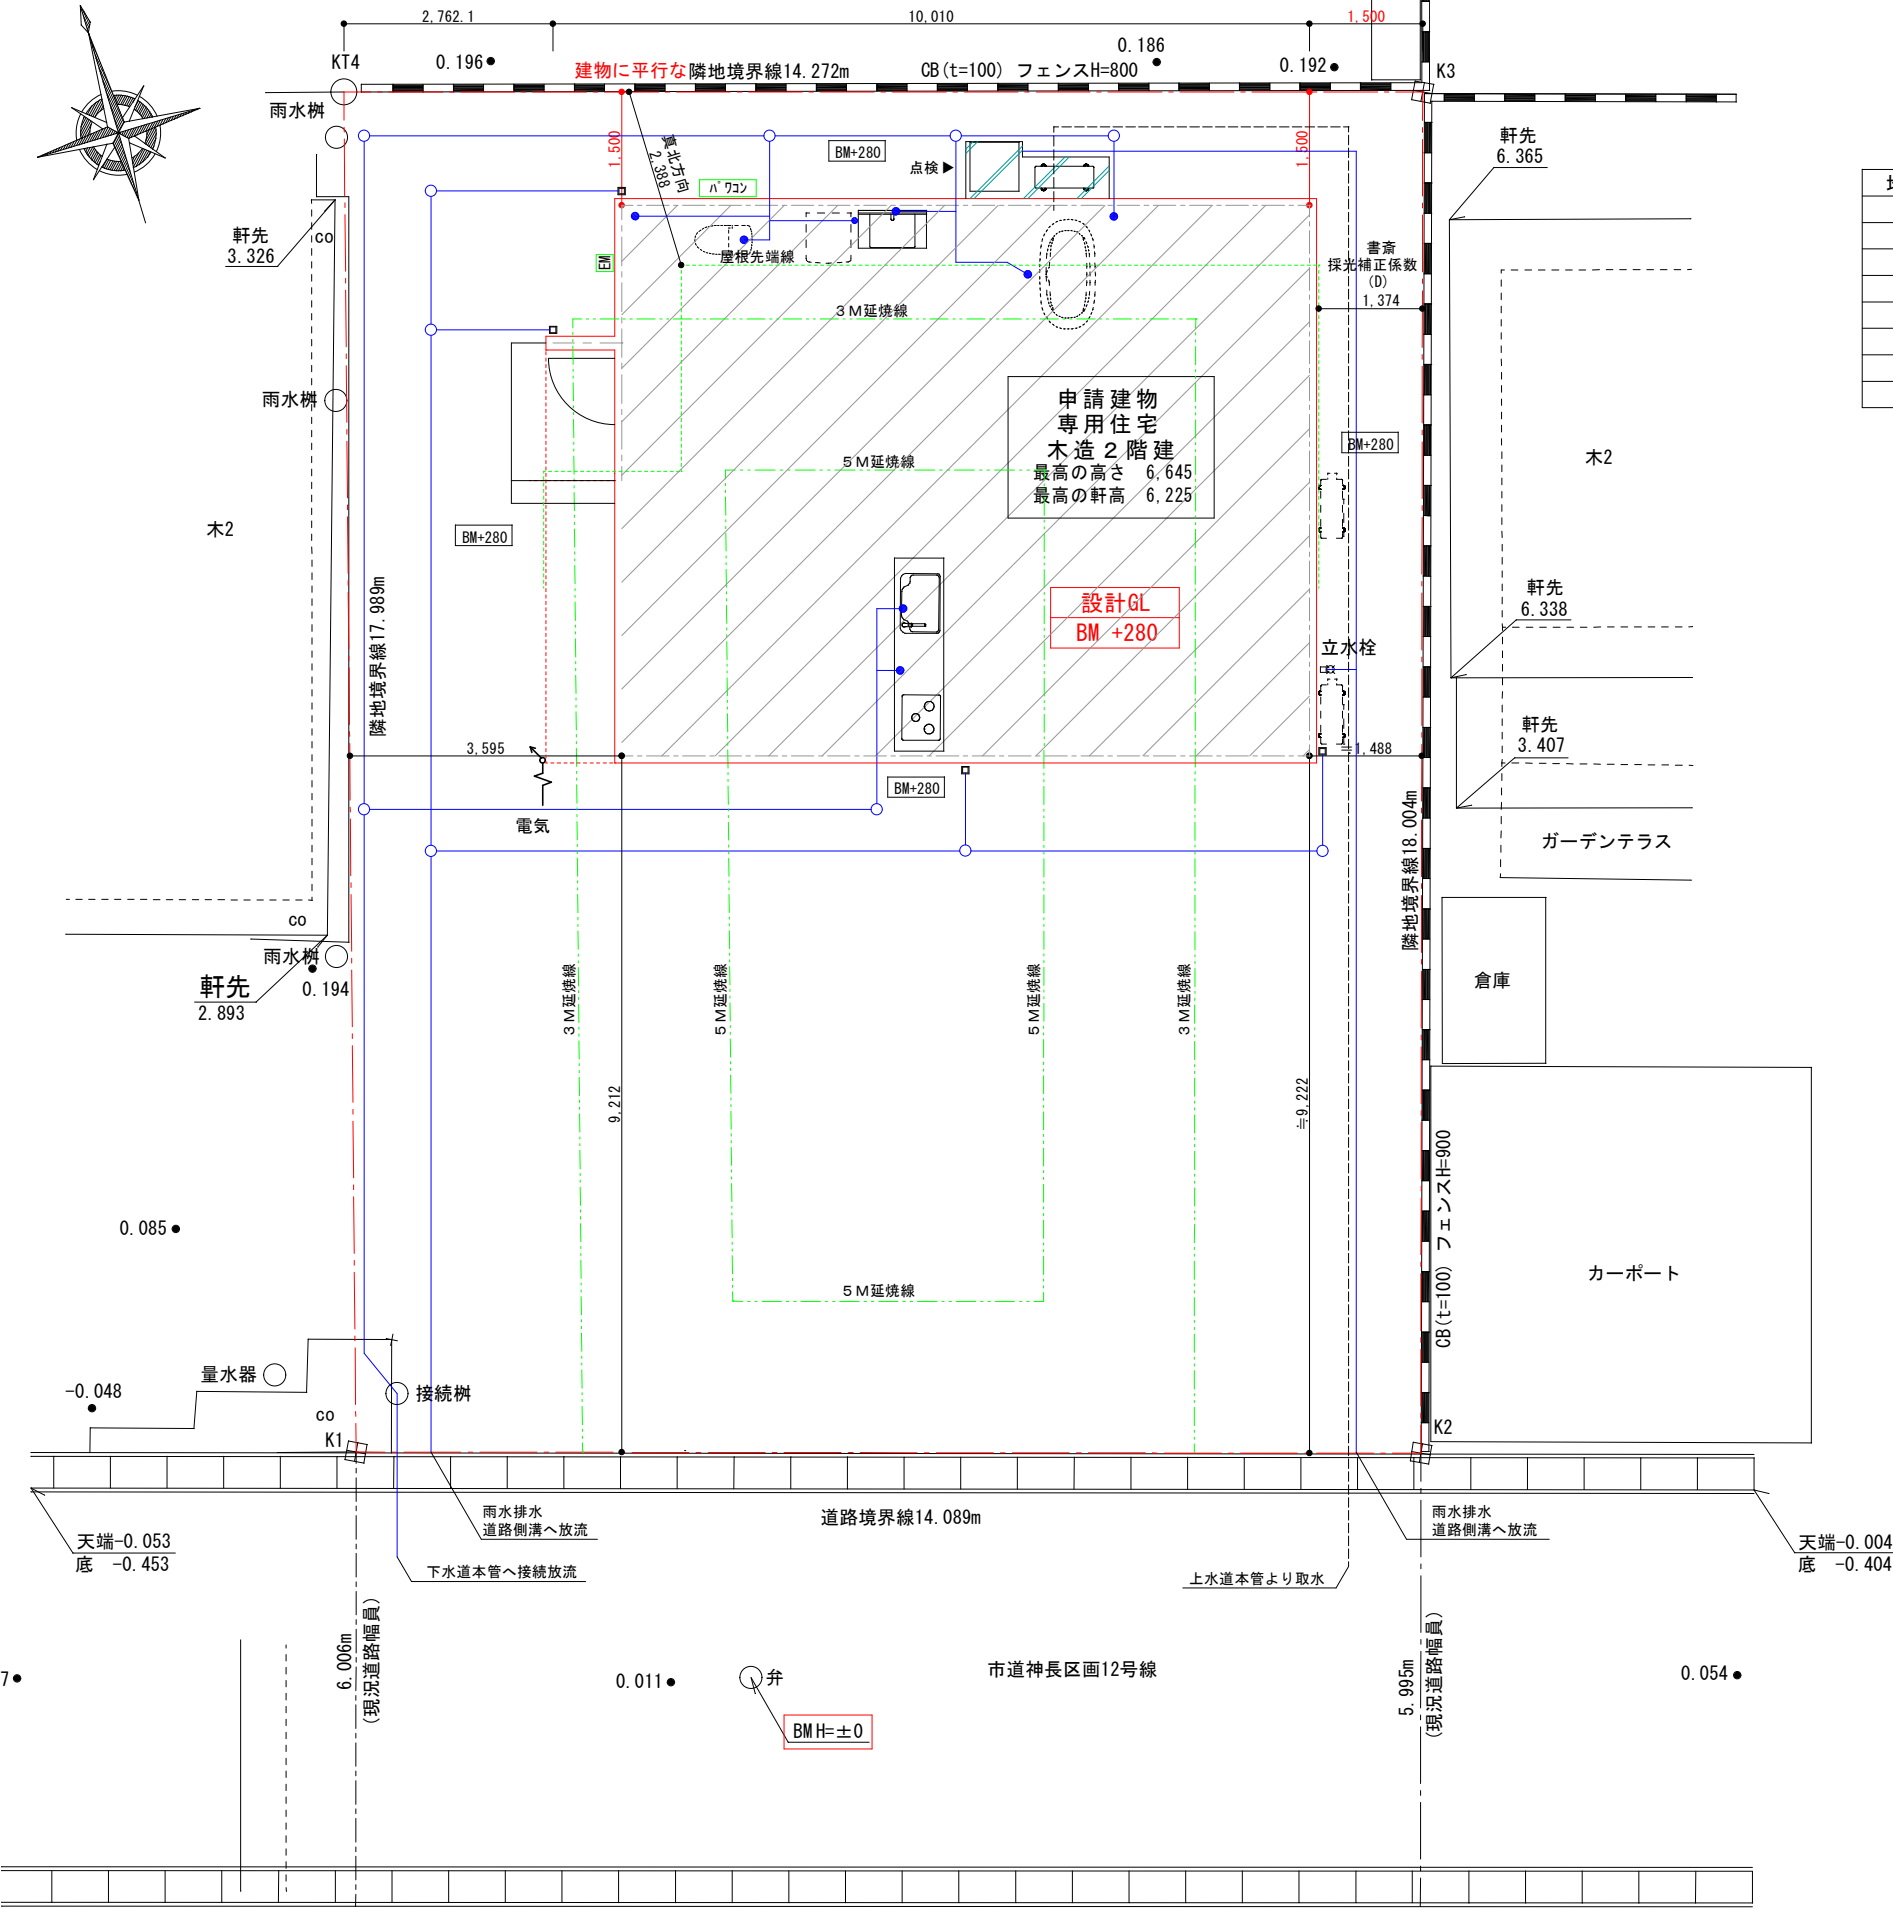


北側斜線
斜線
 $5,000 + (2,388 \times 1.25) = 7,985$
建物高さ 6,645
 $7,985 > 6,645$ ゆえに OK

※斜線適法
※雨水排水は道路側溝へ放流
※盛土規制法の規制に係る切土・盛土無し

配置図 S = 1/100

決定図


訂正	浜岡一級総合設計事務所 一級建築士事務所 静岡県知事登録第 (10)2441 号 一級建築士 大臣登録第 365879 号 西原利昌	LIFEFUND PG HOUSE	株式会社 LIFEFUND InDesign office 一級建築士事務所 事務所登録 (2) 第7595号 一級建築士登録 第179770号 鈴木 達男 〒432-8023 静岡県浜松市中央区鴨江3丁目70番23号	年月日 2026.1.10 縮尺 1/100	件名 寺田慎介様 邸新築工事 図名 配置図		設計 酒井	IC	工事 青島	図番 2-1
----	--	----------------------	---	---------------------------------	--------------------------------	--	----------	----	----------	-----------

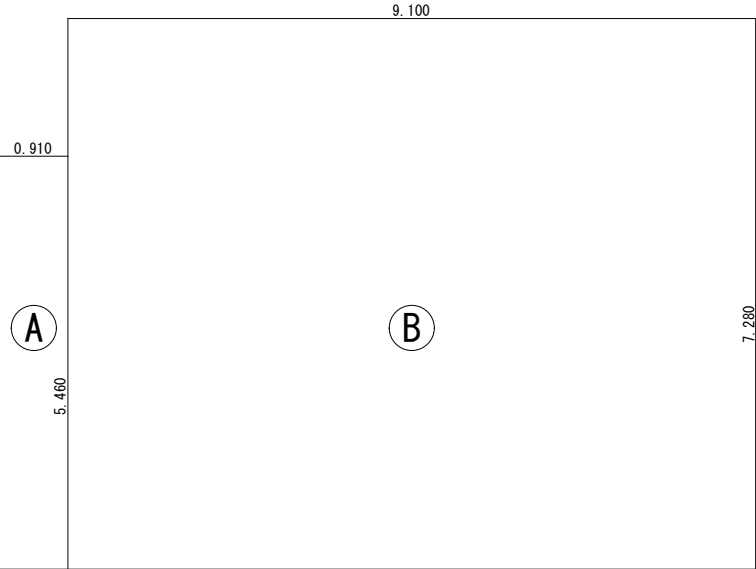

建築面積求積図 S=1/100

建築面積求積表


番号	計算式	(m)	面積 (㎡)
A	0.910 × 5.460		4.9686
B	9.100 × 7.280		66.2480
合計			71.2166 71.21 (21.5坪)

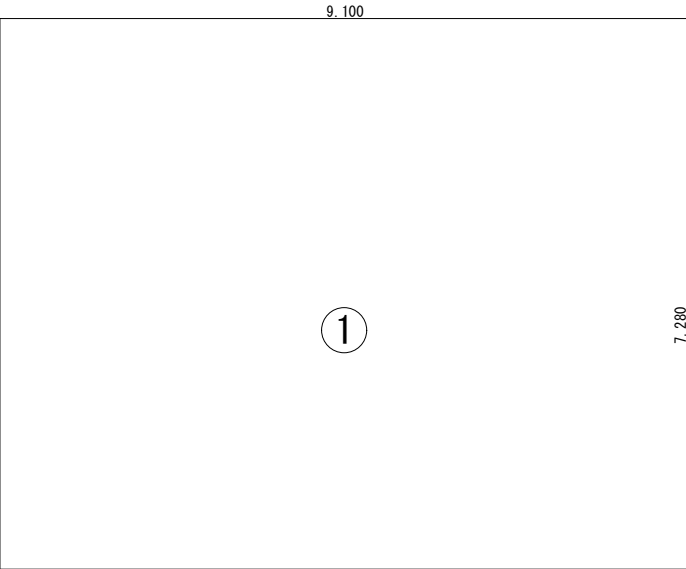

1階床面積図 S=1/100

1階床面積求積表

番号	計算式	(m)	面積 (㎡)
1	9.100 × 7.280		66.2480
合計			66.2480 66.24 (20.0坪)

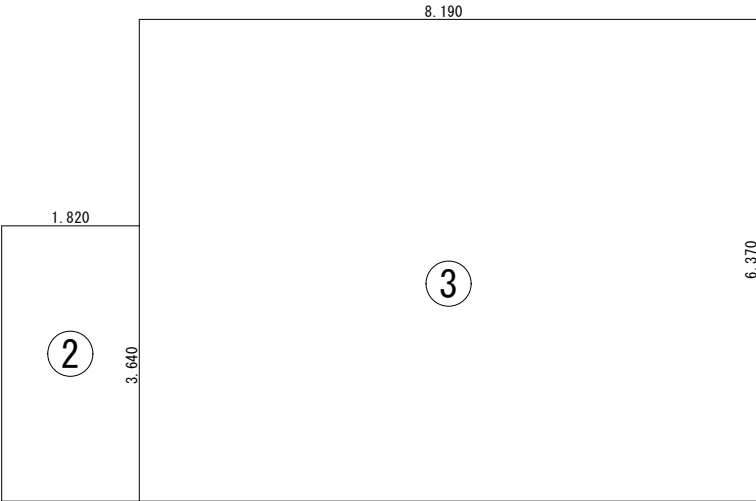

2階床面積図 S=1/100


2階床面積求積表

番号	計算式	(m)	面積 (㎡)
2	1.820 × 3.640		6.6248
3	8.190 × 6.370		52.1703
合計			58.7951 58.79 (17.7坪)

延べ床面積表

	番号	(m)	面積 (㎡)
1階床面積	1		66.24
2階床面積	2 3		58.79
合計			125.04 (37.8坪)

決定図

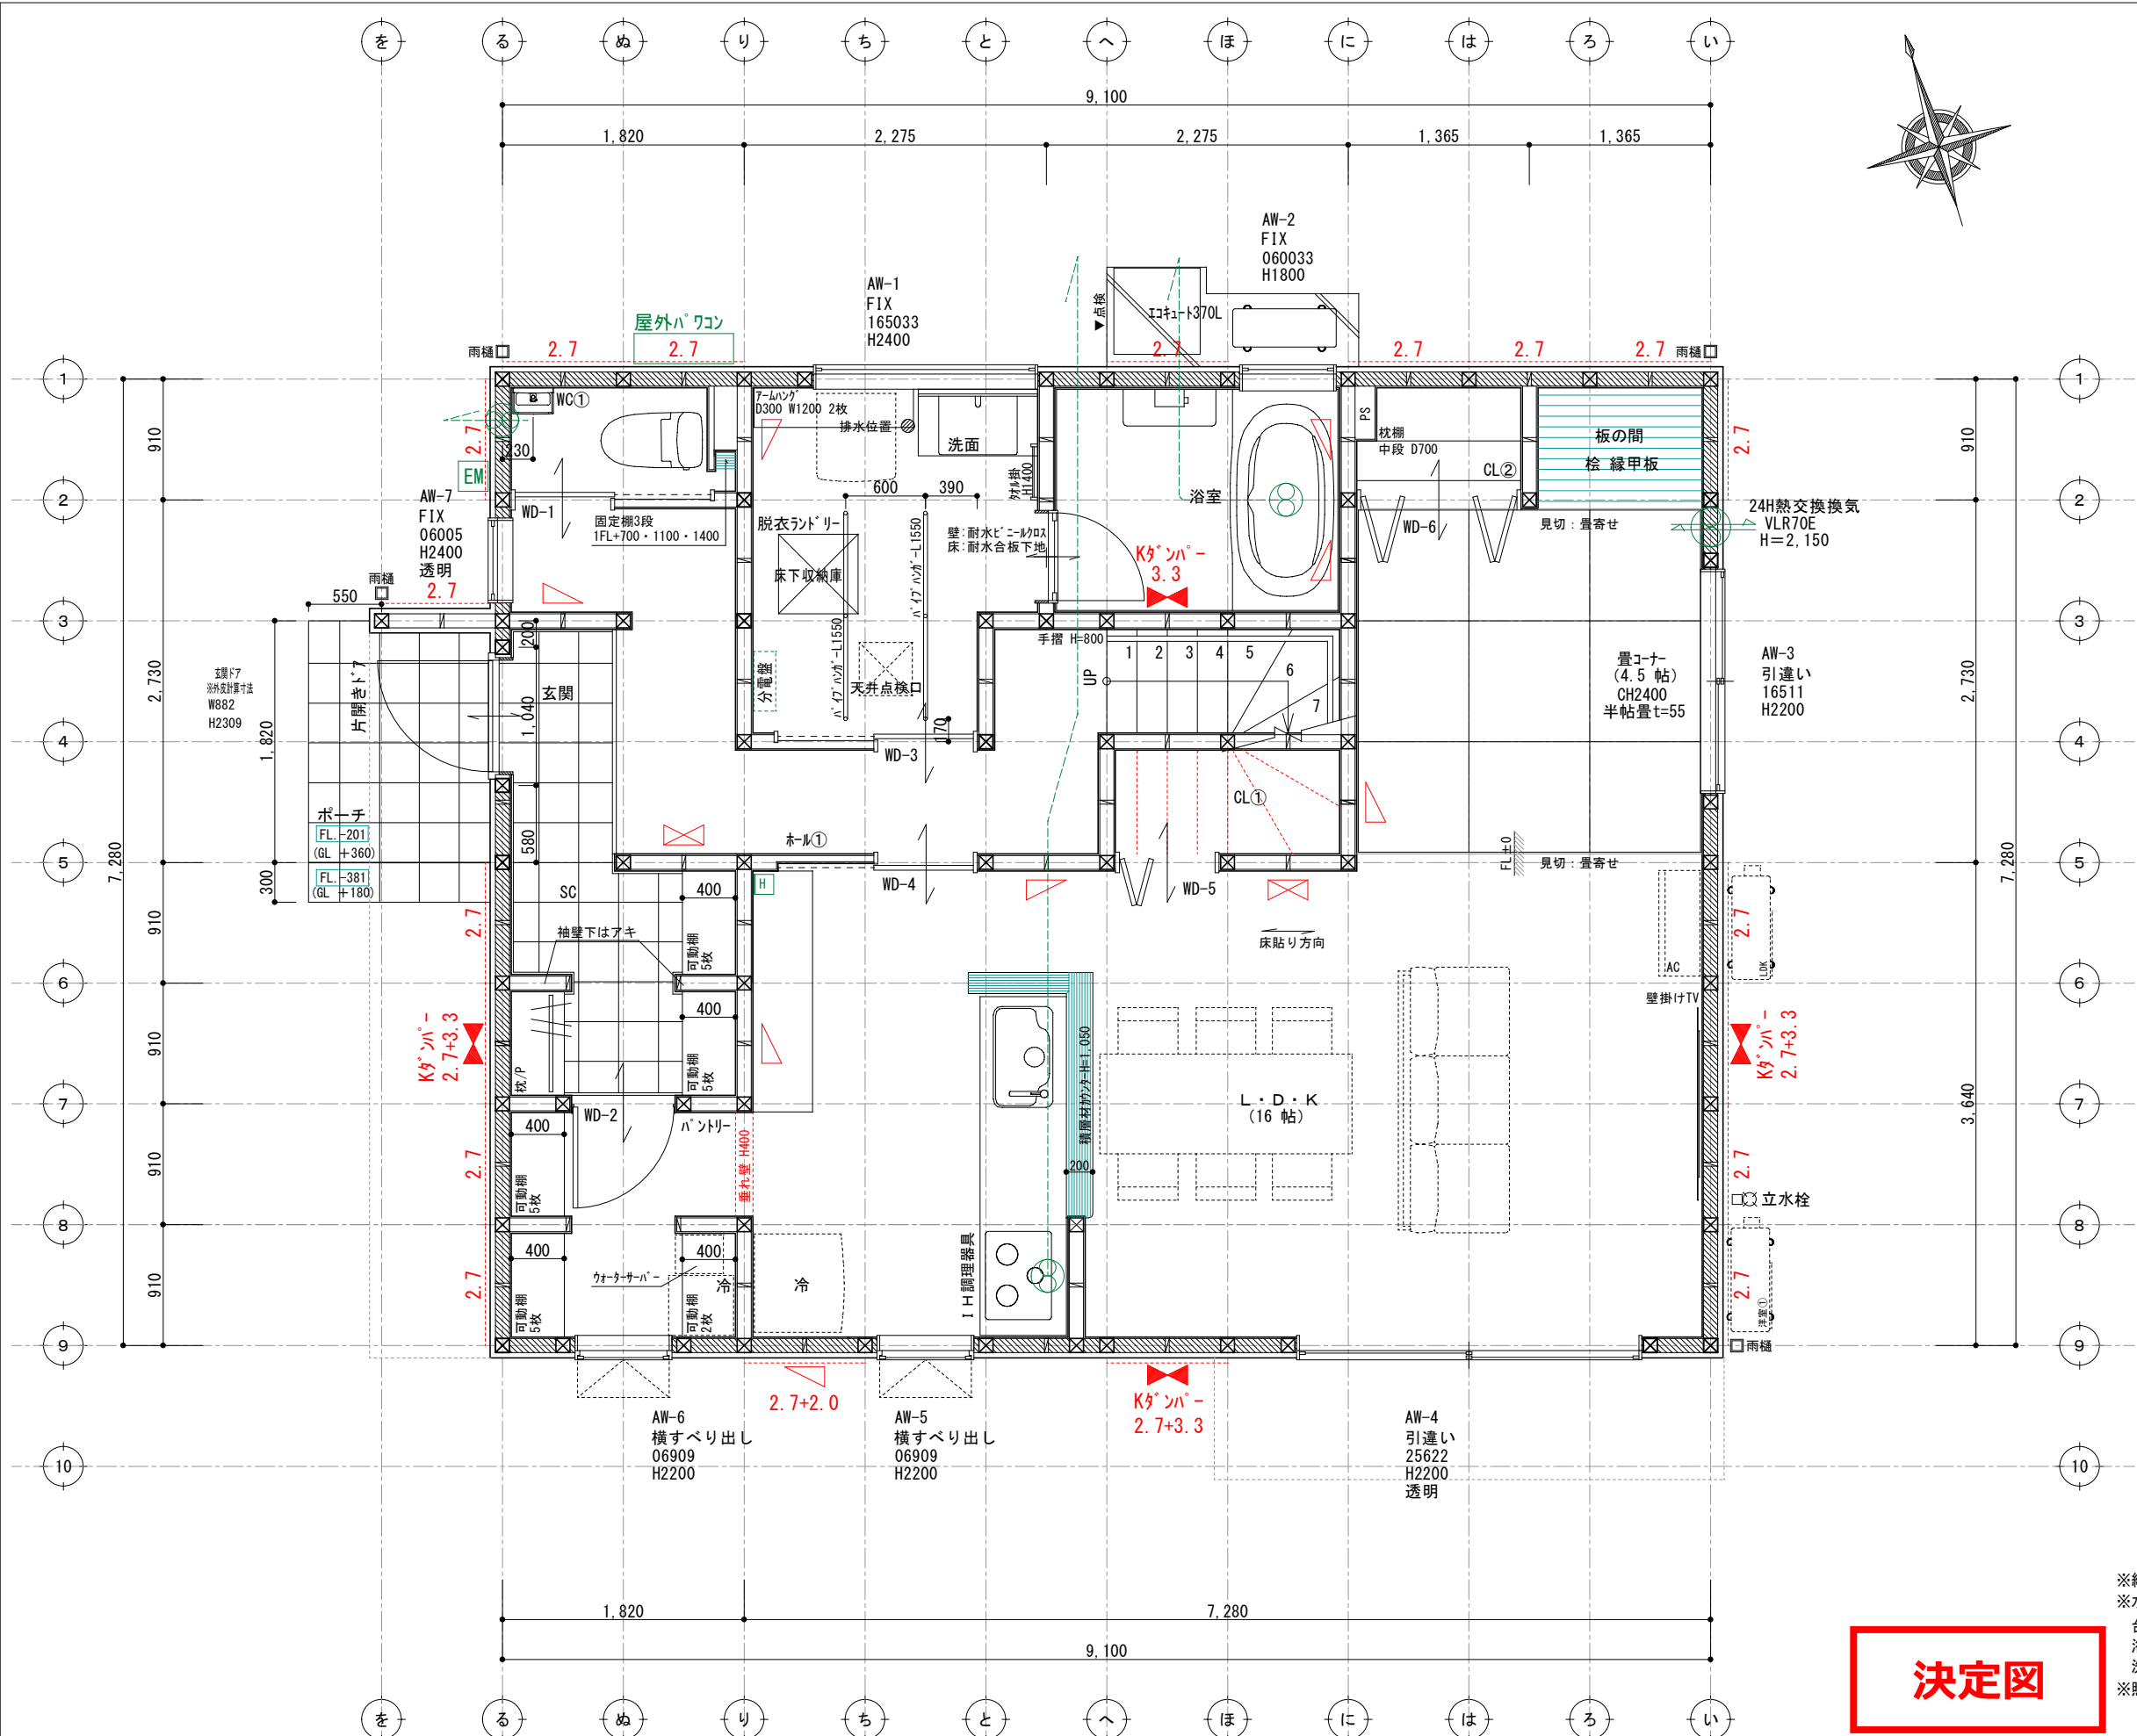

G2

壁付け 住宅用火災報知器			数量
熱感知	H	電池式(単独型)	1
	露出型		
壁付け 住宅用火災報知器			数量
煙感知	S	電池式(単独型)	
	露出型		

- ※ 煙感知器は壁・梁より600mm以上離す壁に取付ける場合、天井から150mm以上500mm以内離す換気扇・エアコン吹出口から1500mm以上離す
- ※ 全室LED照明とする。
- ※ 標準天井高さ2,400
- ※ 特記無きガラスは型ガラス

* 凡例

管柱 (105×105)

K&Nバ- (3.30倍 FRM-0641)

片筋違い (2.00倍 45×90)
(例 左:柱脚 右:柱頭)

たすき掛筋違い (4.00倍 45×90)

構造用合板 (2.70倍)
(t=9 タイプ-EKハイバ-)

床点検口

天井点検口

換気扇

熱交換換気扇VLR-70

脱衣・ランドリー 仕上材
天井：ア9.5PB下地ビニルクロス貼り
壁：ア12.5PB下地ビニルクロス貼り
床：ア24+15耐水合板下地フローリング張り


階段寸法表	
有効幅	750
踏面	210
蹴上	207.15

※下屋部分点検口について
ダウンライト、FS天井点検口、UB点検口より
ポールカメラやファイバースコープ等の
検査機器等を使用して点検する

- ※給水設備：ヘッダー分岐後の全ての配管径は13A以下とする
- ※水栓：一般社団法人日本バルブ工業会の定義による節湯水栓
台所：2バルブ水栓以外のその他の水栓(水優先吐水機能)
浴室シャワー：2バルブ水栓以外のその他の水栓(小流量吐水機能)
洗面：2バルブ水栓以外のその他の水栓(水優先吐水機能)
- ※照明設備：全室LED照明とし居室においては調光制御、非居室においては人感センサーを採用する

決定図

G2

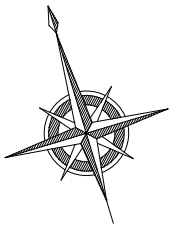

壁付け 住宅用火災報知器			数量
H 熱感知	電池式(単独型)		
	露出型		
壁付け 住宅用火災報知器			数量
S 煙感知	電池式(単独型)		6
	露出型		

- ※ 煙感知器は壁・梁より600mm以上離す
壁に取付ける場合、
天井から150mm以上500mm以内離す
換気扇・エアコン吹出口から1500mm以上離す
- ※ 全室LED照明とする。
- ※ 標準天井高さ2,400
- ※ 特記無きガラスは型ガラス

* 凡例

- ☒ 管柱 (105×105)
- ◀▶ Kダクト (3.30倍 FRM-0641)
- △ 片筋違い (2.00倍 45×90)
(例 左:柱脚 右:柱頭)
- ⊠ たすき掛筋違い (4.00倍 45×90)
- 構造用合板 (2.70倍)
(t=9 9材-EKハイパ-)
- ◻ 床点検口
- ⊠ 天井点検口
- ⊙ 換気扇
- ⊙ 熱交換換気扇VLR-70


決定図

訂 正	浜 岡 一 級 総 合 設 計 事 務 所			株式会社 LIFEFUND InDesign office 一級建築士事務所		年 月 日	件 名		設計	IC	工事	図 番
	一級建築士事務所 静岡県知事登録第 (10)2441 号			事務所登録 (2) 第7595号 一級建築士登録 第179770号 鈴木 達男	2026. 1. 10	寺田 慎介様邸 新築工事						
	一級建築士 大臣登録第 365879 号 西原利昌			〒432-8023 静岡県浜松市中央区鴨江3丁目70番23号	縮 尺	図 名						
						1/50	2 階平面図		酒 井		青 島	3-2



訂 正	浜 岡 一 級 総 合 設 計 事 務 所 一級建築士事務所 静岡県知事登録第 (10)2441 号 一級建築士 大臣登録第 365879 号 西原利昌	 PG HOUSE ビーjeeハウス	株式会社 LIFEFUND InDesign office 一級建築士事務所 事務所登録 (2) 第7595号 一級建築士登録 第179770号 鈴木 達男 〒432-8023 静岡県浜松市中央区鴨江3丁目70番23号	年 月 日 2026. 1. 10 縮 尺 1/100	件 名 寺田慎介様邸 新築工事 図 名 屋根伏図	設計 酒井	IC	工事 青島	図 番 3-3
-----	--	---	---	--------------------------------------	-----------------------------------	----------	----	----------	------------


G2

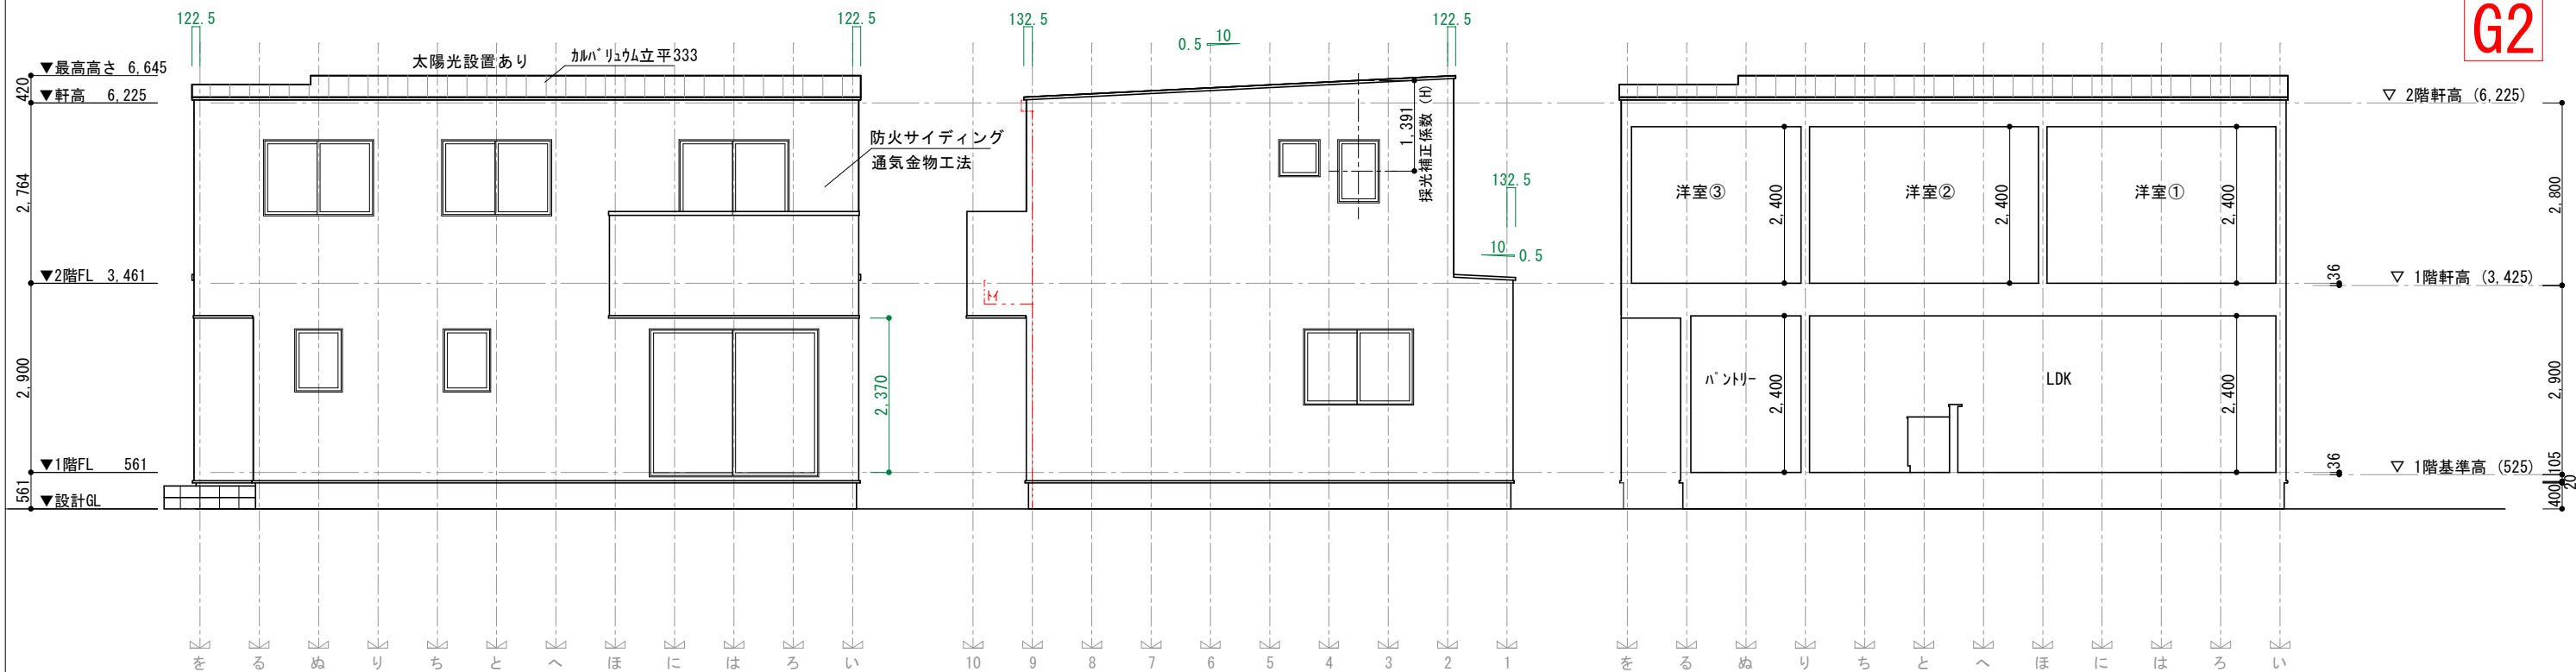

南側立面図 S=1/100

東側立面図 S=1/100

断面図（東西） S=1/100

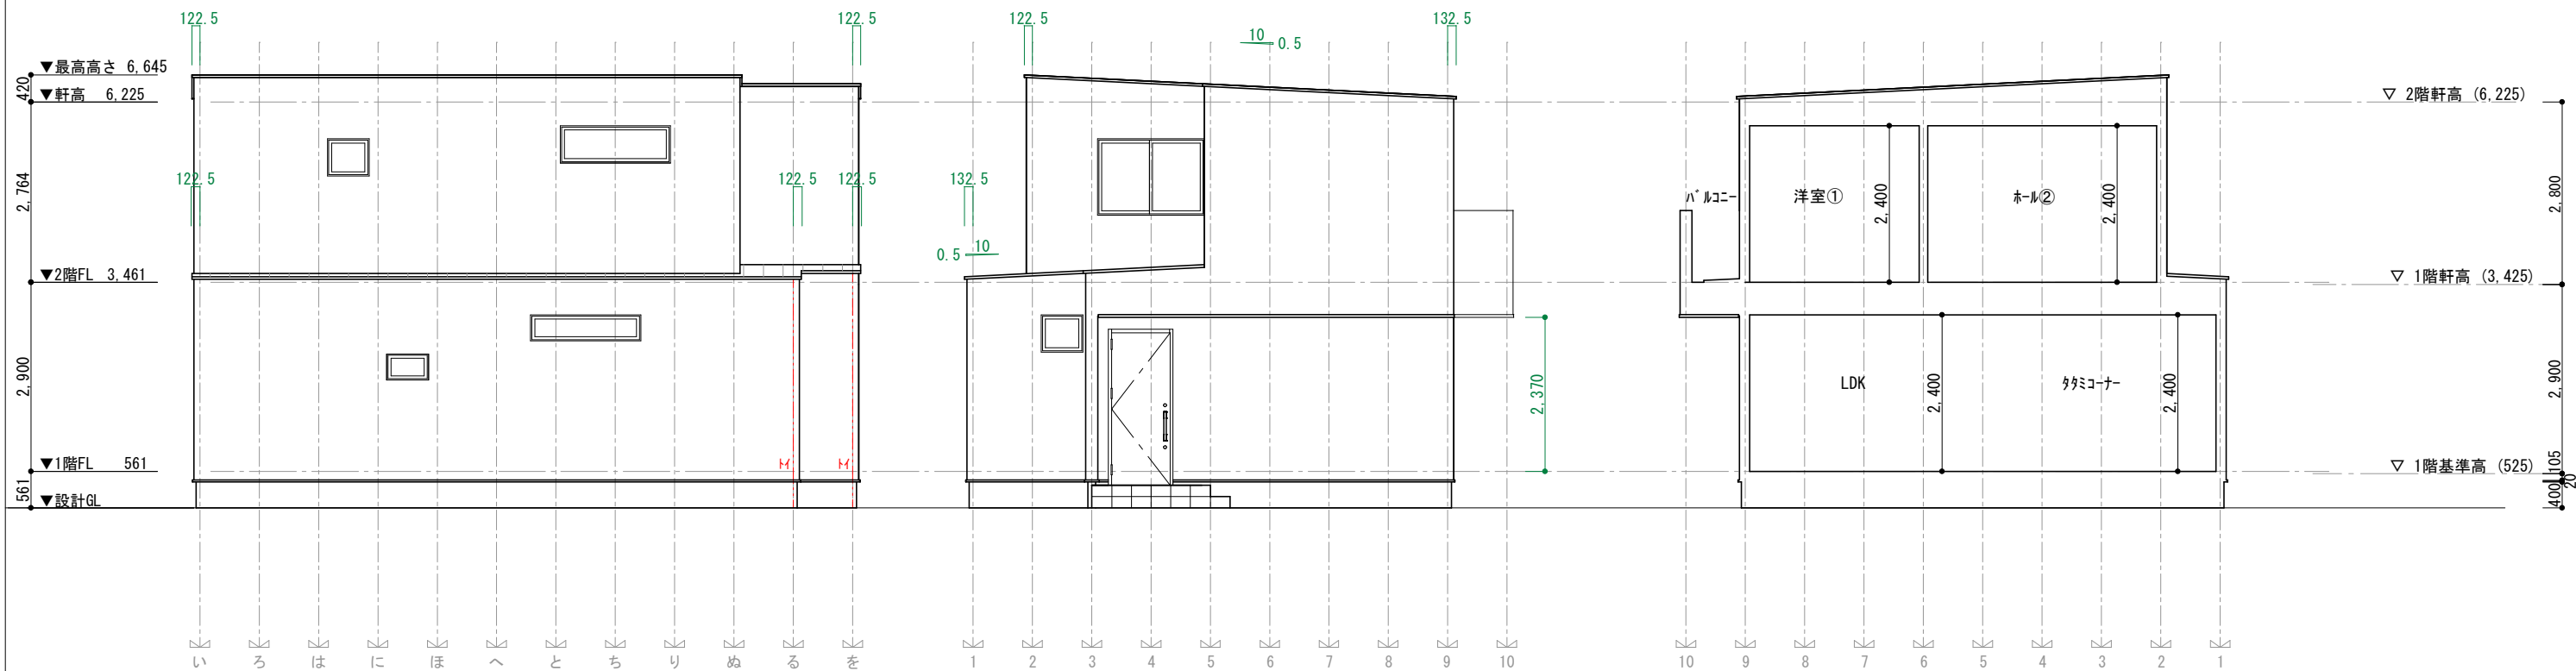


北側立面図 S=1/100

西側立面図 S=1/100

断面図（南北） S=1/100


決定図

訂正	浜岡一級総合設計事務所 一級建築士事務所 静岡県知事登録第 (10)2441 号 一級建築士 大臣登録第 365879 号 西原利昌	PG HOUSE ピージーハウス	株式会社 LIFEFUND InDesign office 一級建築士事務所 事務所登録 (2) 第7595号 一級建築士登録 第179770号 鈴木 達男 〒432-8023 静岡県浜松市中央区鴨江3丁目70番23号	年月日 2026.1.10 縮尺 1/100	件名 寺田慎介様邸 新築工事 図名 立面図		設計 酒井	IC	工事 青島	図番 4
----	--	---------------------	---	---------------------------------	--------------------------------	--	----------	----	----------	---------

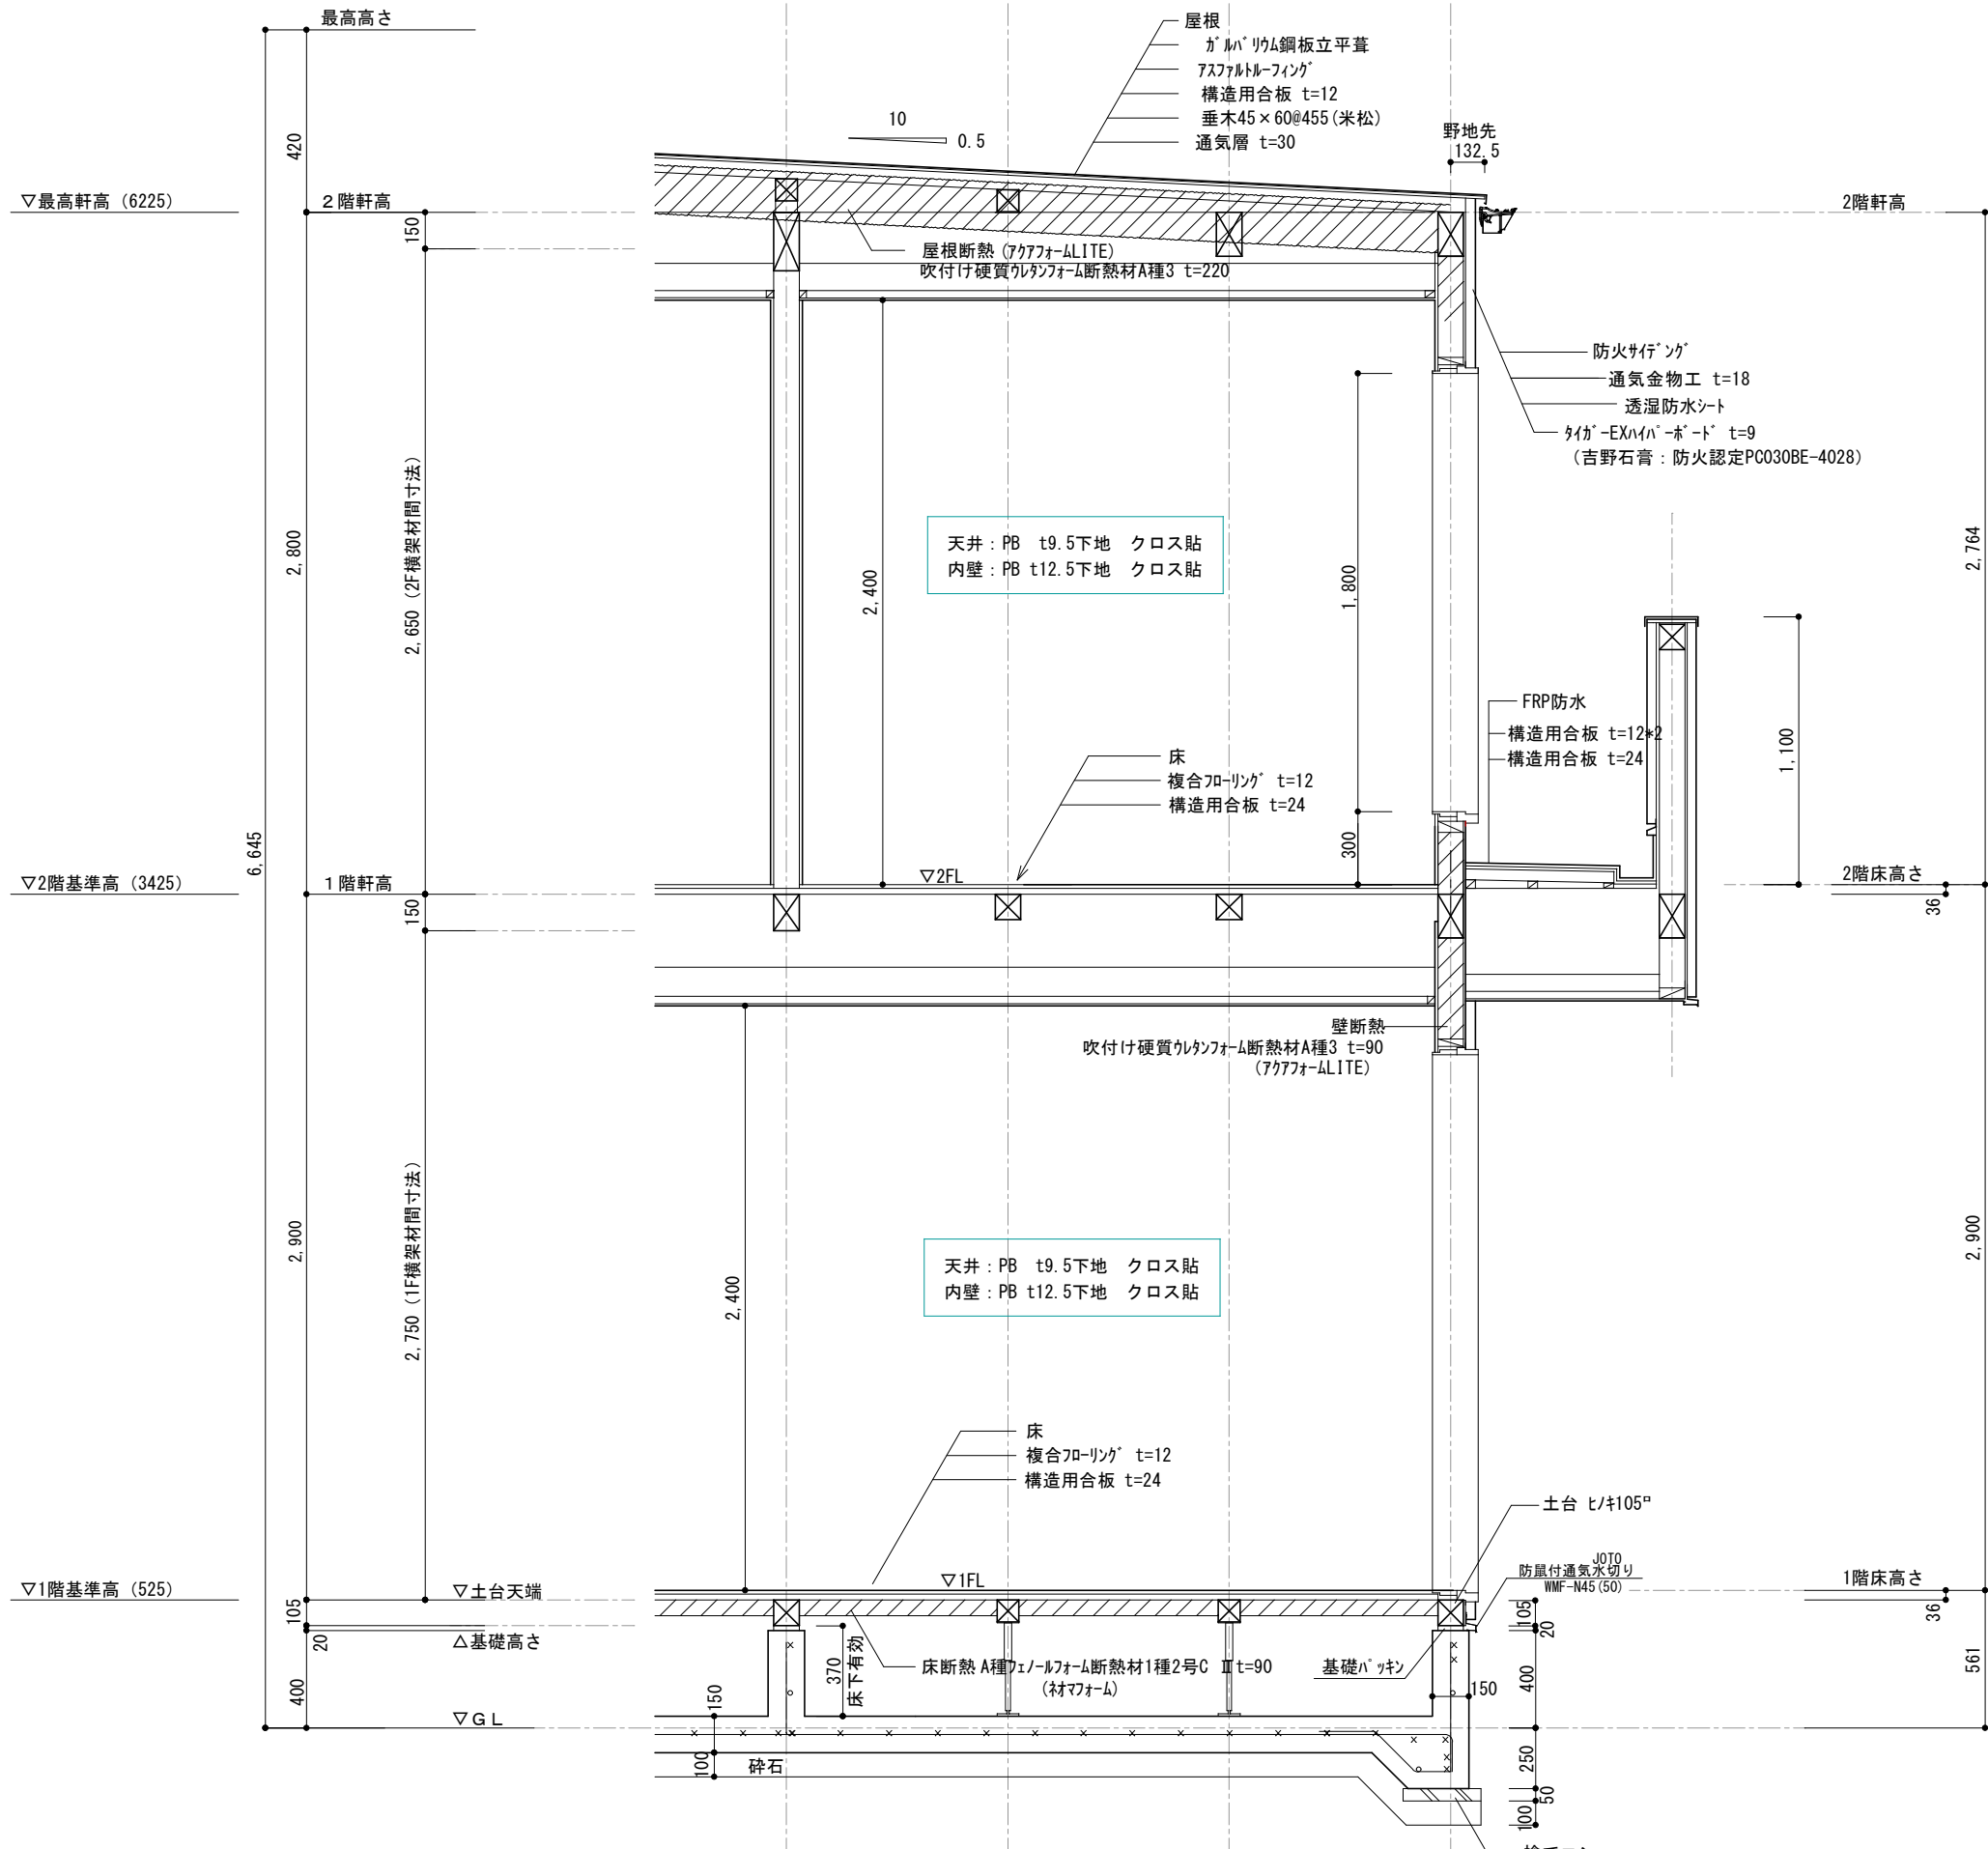


決定図


訂正	浜岡一級総合設計事務所		株式会社 LIFEFUND InDesign office		年 月 日	件 名	設計	IC	工事	図 番
	一級建築士事務所 静岡県知事登録第 (10)2441 号		事務所登録 (2)第7595号		2026. 1. 10					
	一級建築士 大臣登録第 365879 号 西原利昌		一級建築士登録 第179770号 鈴木 達男		縮 尺					
	PG HOUSE		〒432-8023 静岡県浜松市中央区鴨江3丁目70番23号		1/30	図 名	寺田慎介様 邸新築工事	酒井	青島	5
						矩計図				

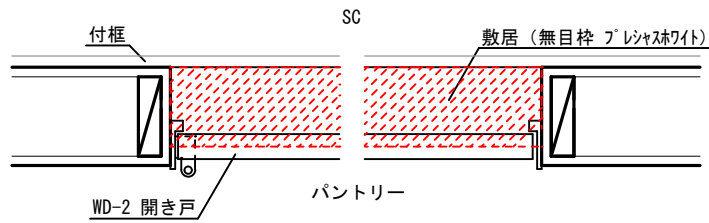


WD-2 建具 納まり図 (1/10)

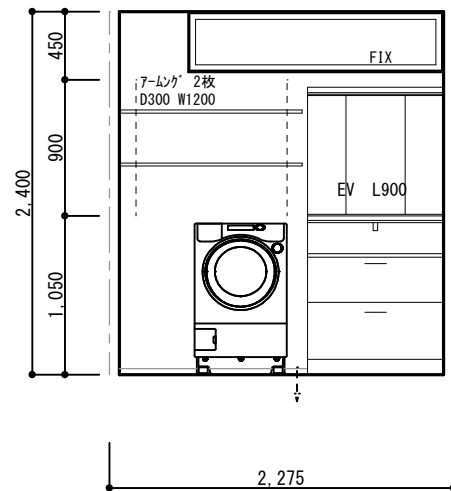


脱衣ラントリー 北面

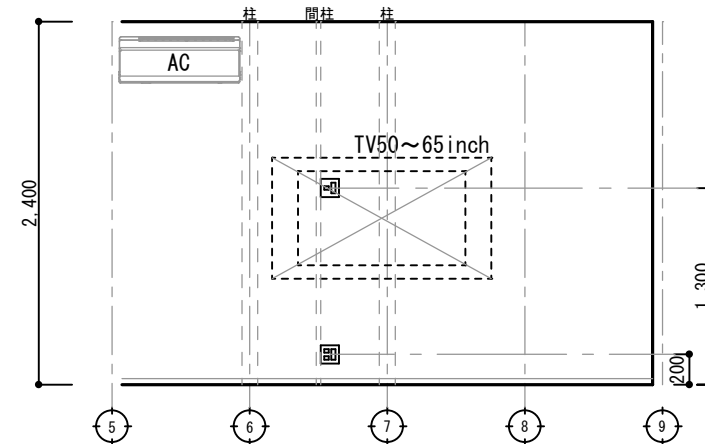


LDK 東面

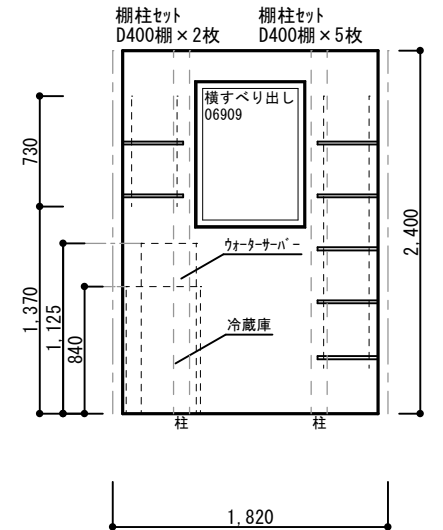


パントリー 南面

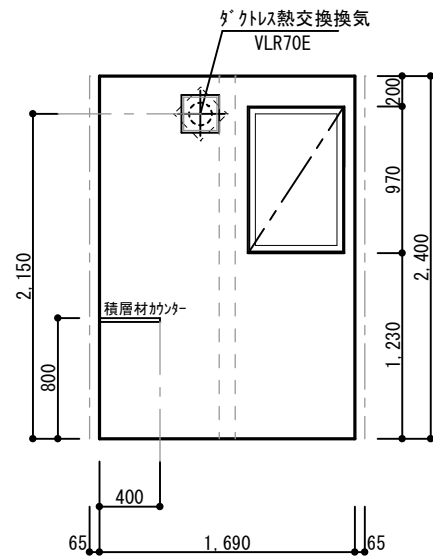


書斎 東面

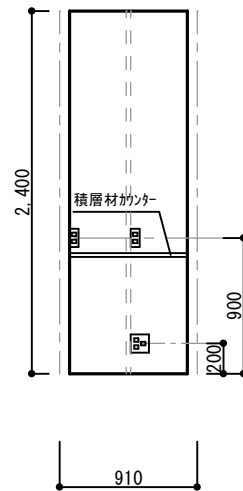

書斎 北面

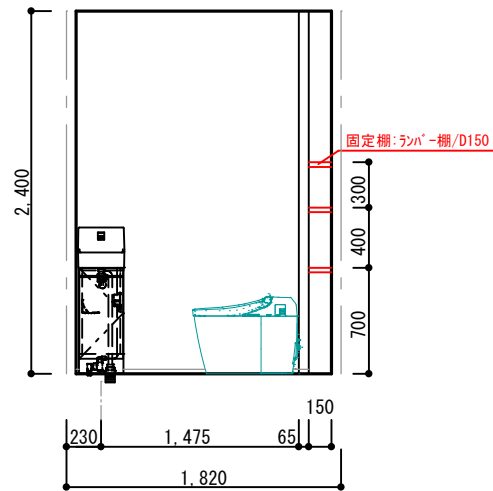




WC① 北面

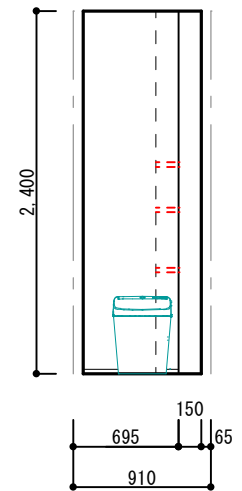

WC① 東面

決定図

訂正	浜岡一級総合設計事務所 一級建築士事務所 静岡県知事登録第 (10)2441 号 一級建築士 大臣登録第 365879 号 西原利昌	LIFEFUND PG HOUSE	株式会社 LIFEFUND InDesign office 一級建築士事務所 事務所登録 (2) 第7595号 一級建築士登録 第179770号 鈴木 達男 〒432-8023 静岡県浜松市中央区鶴江3丁目70番23号	年月日 2026.1.10 縮尺 1/50	件名 寺田慎介様邸 新築工事 図名 展開図-1		設計 酒井	IC	工事 青島	図番 6-1
----	--	----------------------	---	--------------------------------	----------------------------------	--	----------	----	----------	-----------

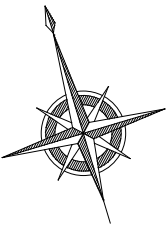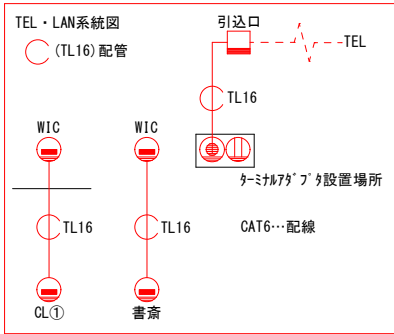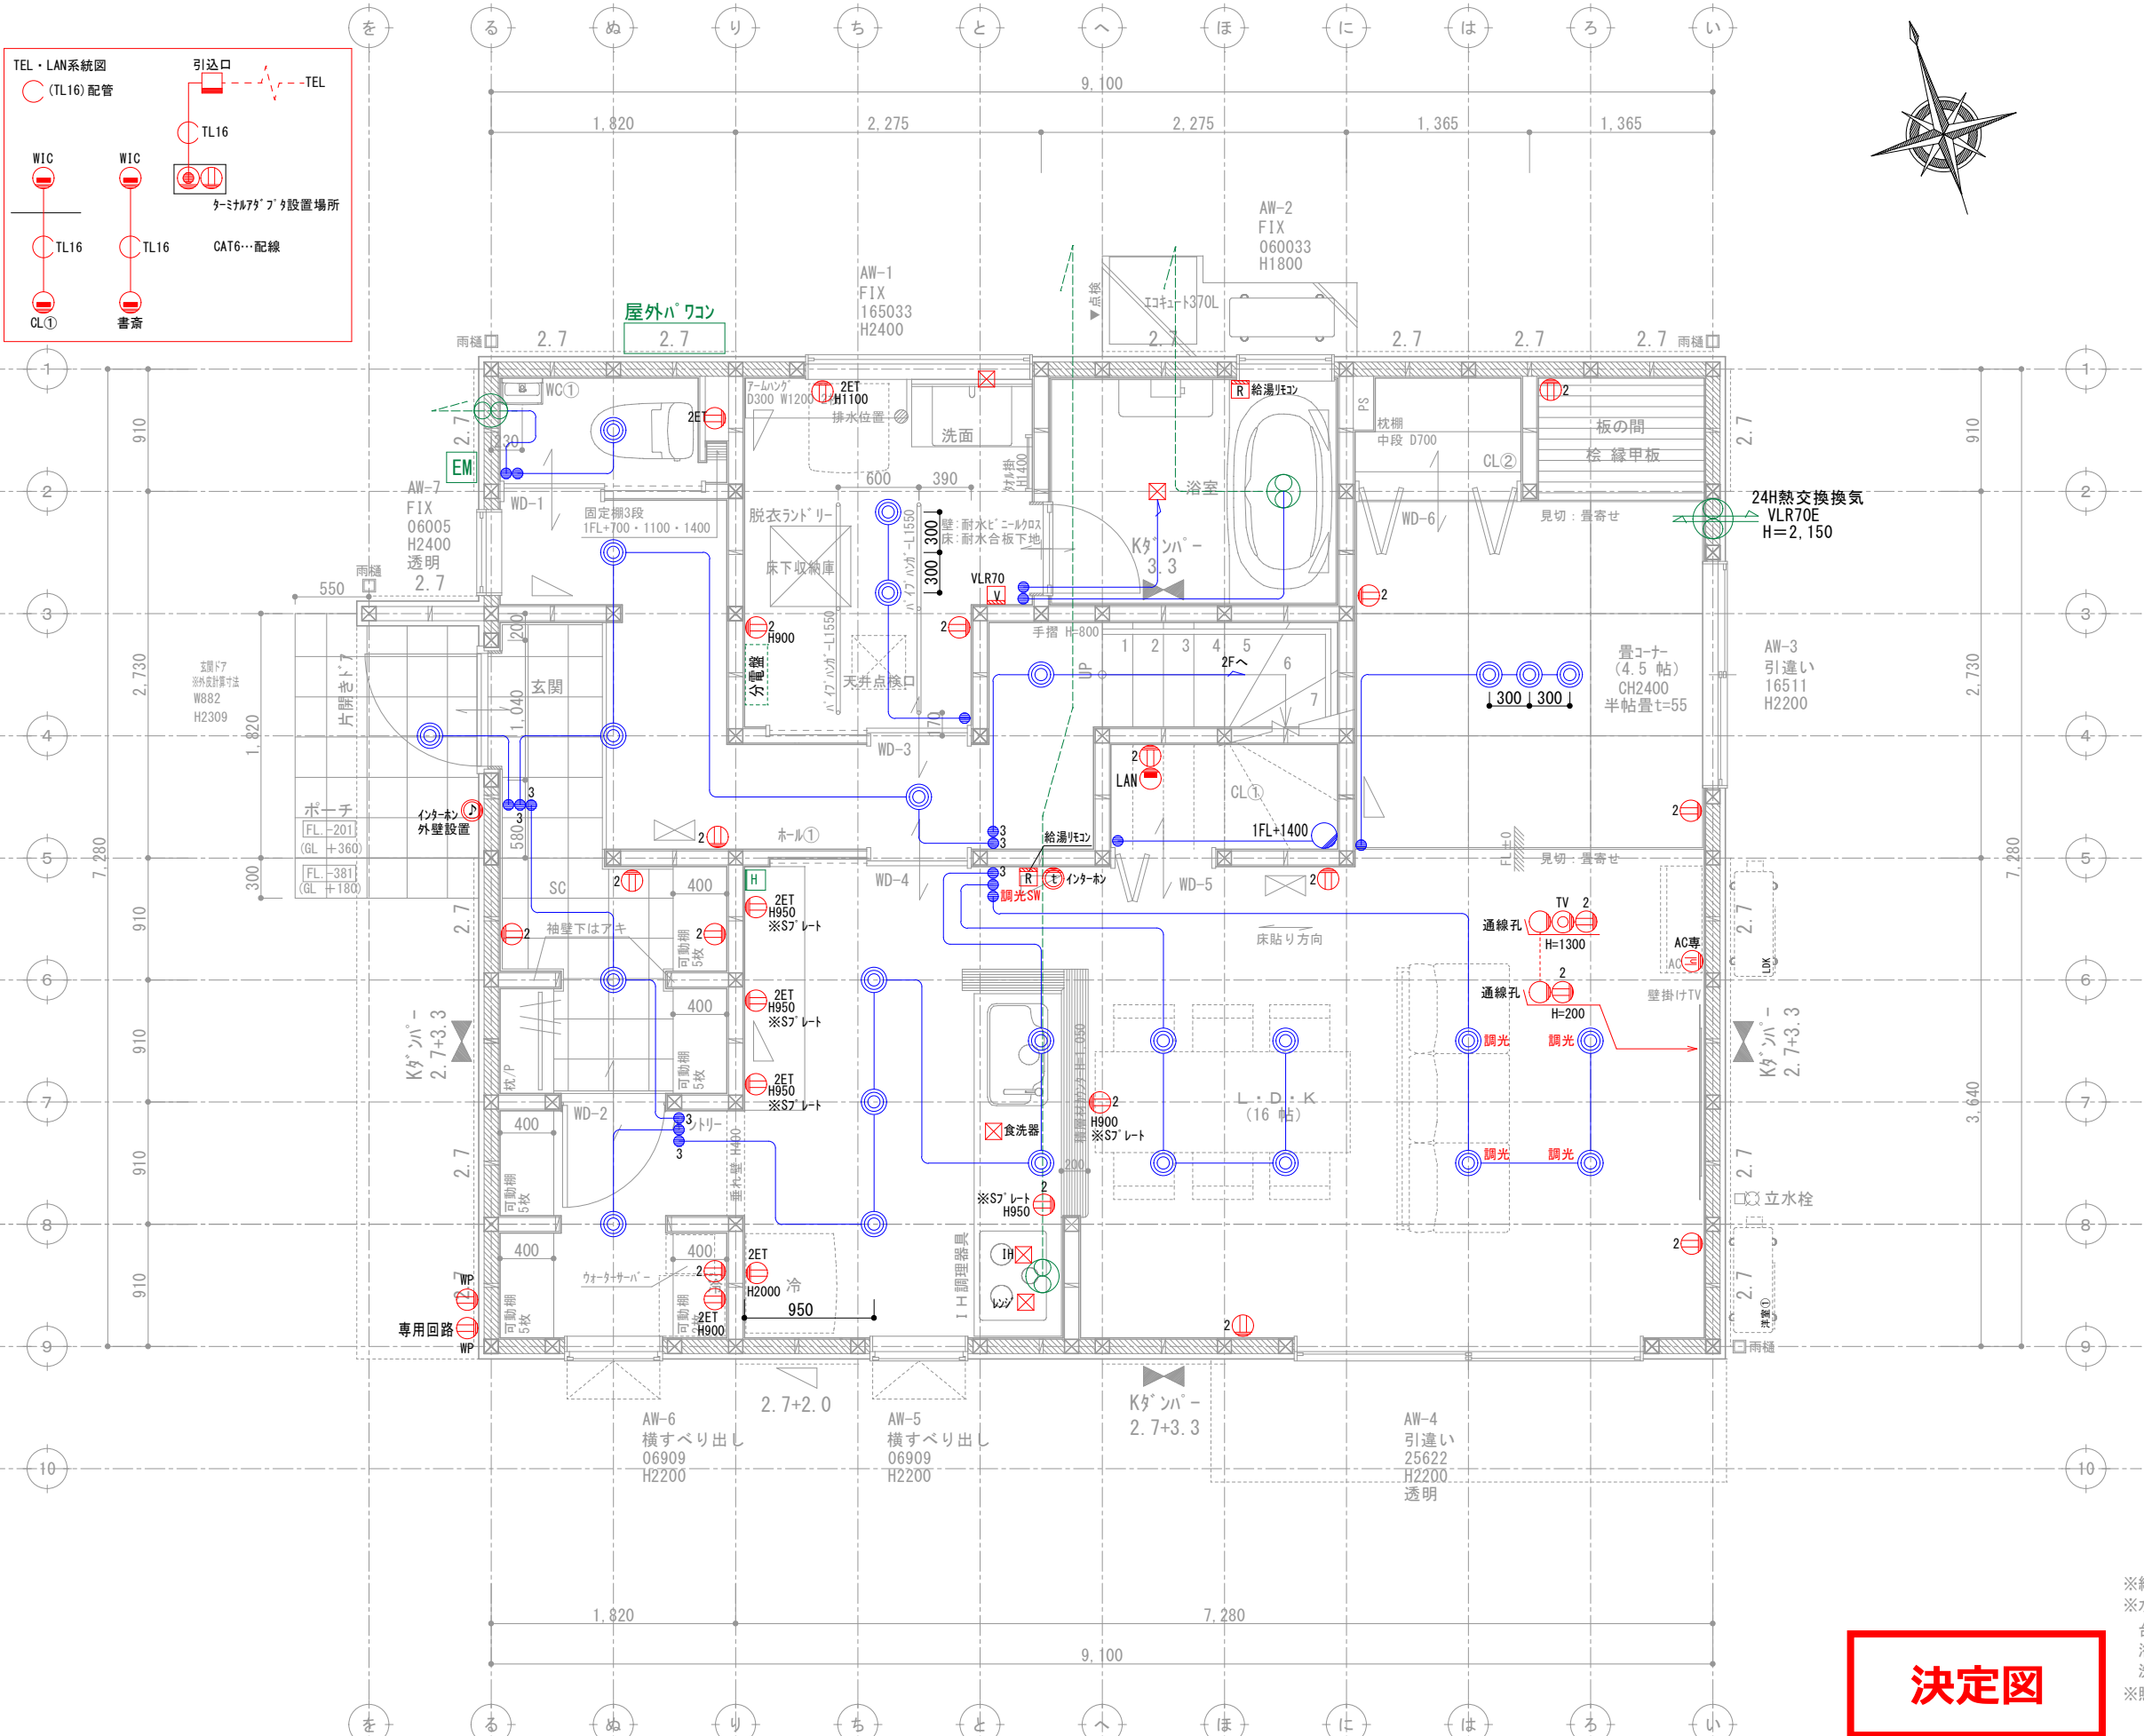

G2

壁付け 住宅用火災報知器			数量
H 熱感知	電池式(単独型)		1
	露出型		
壁付け 住宅用火災報知器			数量
S 煙感知	電池式(単独型)		
	露出型		

- ※ 煙感知器は壁・梁より600mm以上離す
壁に取付ける場合、
天井から150mm以上500mm以内離す
換気扇・エアコン吹出口から1500mm以上離す
- ※ 全室LED照明とする。
- ※ 標準天井高さ2,400
- ※ 特記無きガラスは型ガラス

* 凡例

- 管柱 (105×105)
- Kタンパ (3.30倍 FRM-0641)
- 片筋違い (2.00倍 45×90)
(例 左:柱脚 右:柱頭)
- たすき掛筋違い (4.00倍 45×90)
- 構造用合板 (2.70倍)
(t=9 9材-EKハイパー)
- 床点検口
- 天井点検口
- 換気扇
- 熱交換換気扇VLR-70

脱衣・ランドリー 仕上材
天井: ア9.5PB下地ビニルクロス貼り
壁: ア12.5PB下地ビニルクロス貼り
床: ア24+15耐水合板下地フロアタイル張り


階段寸法表
有効幅: 750
踏面: 210
蹴上: 207.15

※下屋部分点検口について
ダウンライト、FS天井点検口、UB点検口より
ポールカメラやファイバースコープ等の
検査機器等を使用して点検する

- ※給水設備: ヘッダー分岐後の全ての配管径は13A以下とする
- ※水栓: 一般社団法人日本バルブ工業会の定義による節湯水栓
台所: 2バルブ水栓以外のその他の水栓(水優先吐水機能)
浴室シャワー: 2バルブ水栓以外のその他の水栓(小流量吐水機能)
洗面: 2バルブ水栓以外のその他の水栓(水優先吐水機能)
- ※照明設備: 全室LED照明とし居室においては調光制御、非居室においては
人感センサーを採用する

決定図

訂正	浜岡一級総合設計事務所 一級建築士事務所 静岡県知事登録第 (10)2441 号 一級建築士 大臣登録第 365879 号 西原利昌	PG HOUSE ピージーハウス	株式会社 LIFEFUND InDesign office 一級建築士事務所 事務所登録 (2) 第7595号 一級建築士登録 第179770号 鈴木 達男 〒432-8023 静岡県浜松市中央区鴨江3丁目70番23号	年月日	2026. 1. 10	件名	寺田慎介様邸 新築工事		設計	IC	工事	図番
				縮尺	1/50	図名	1階電気配線図		酒井		青島	7-1

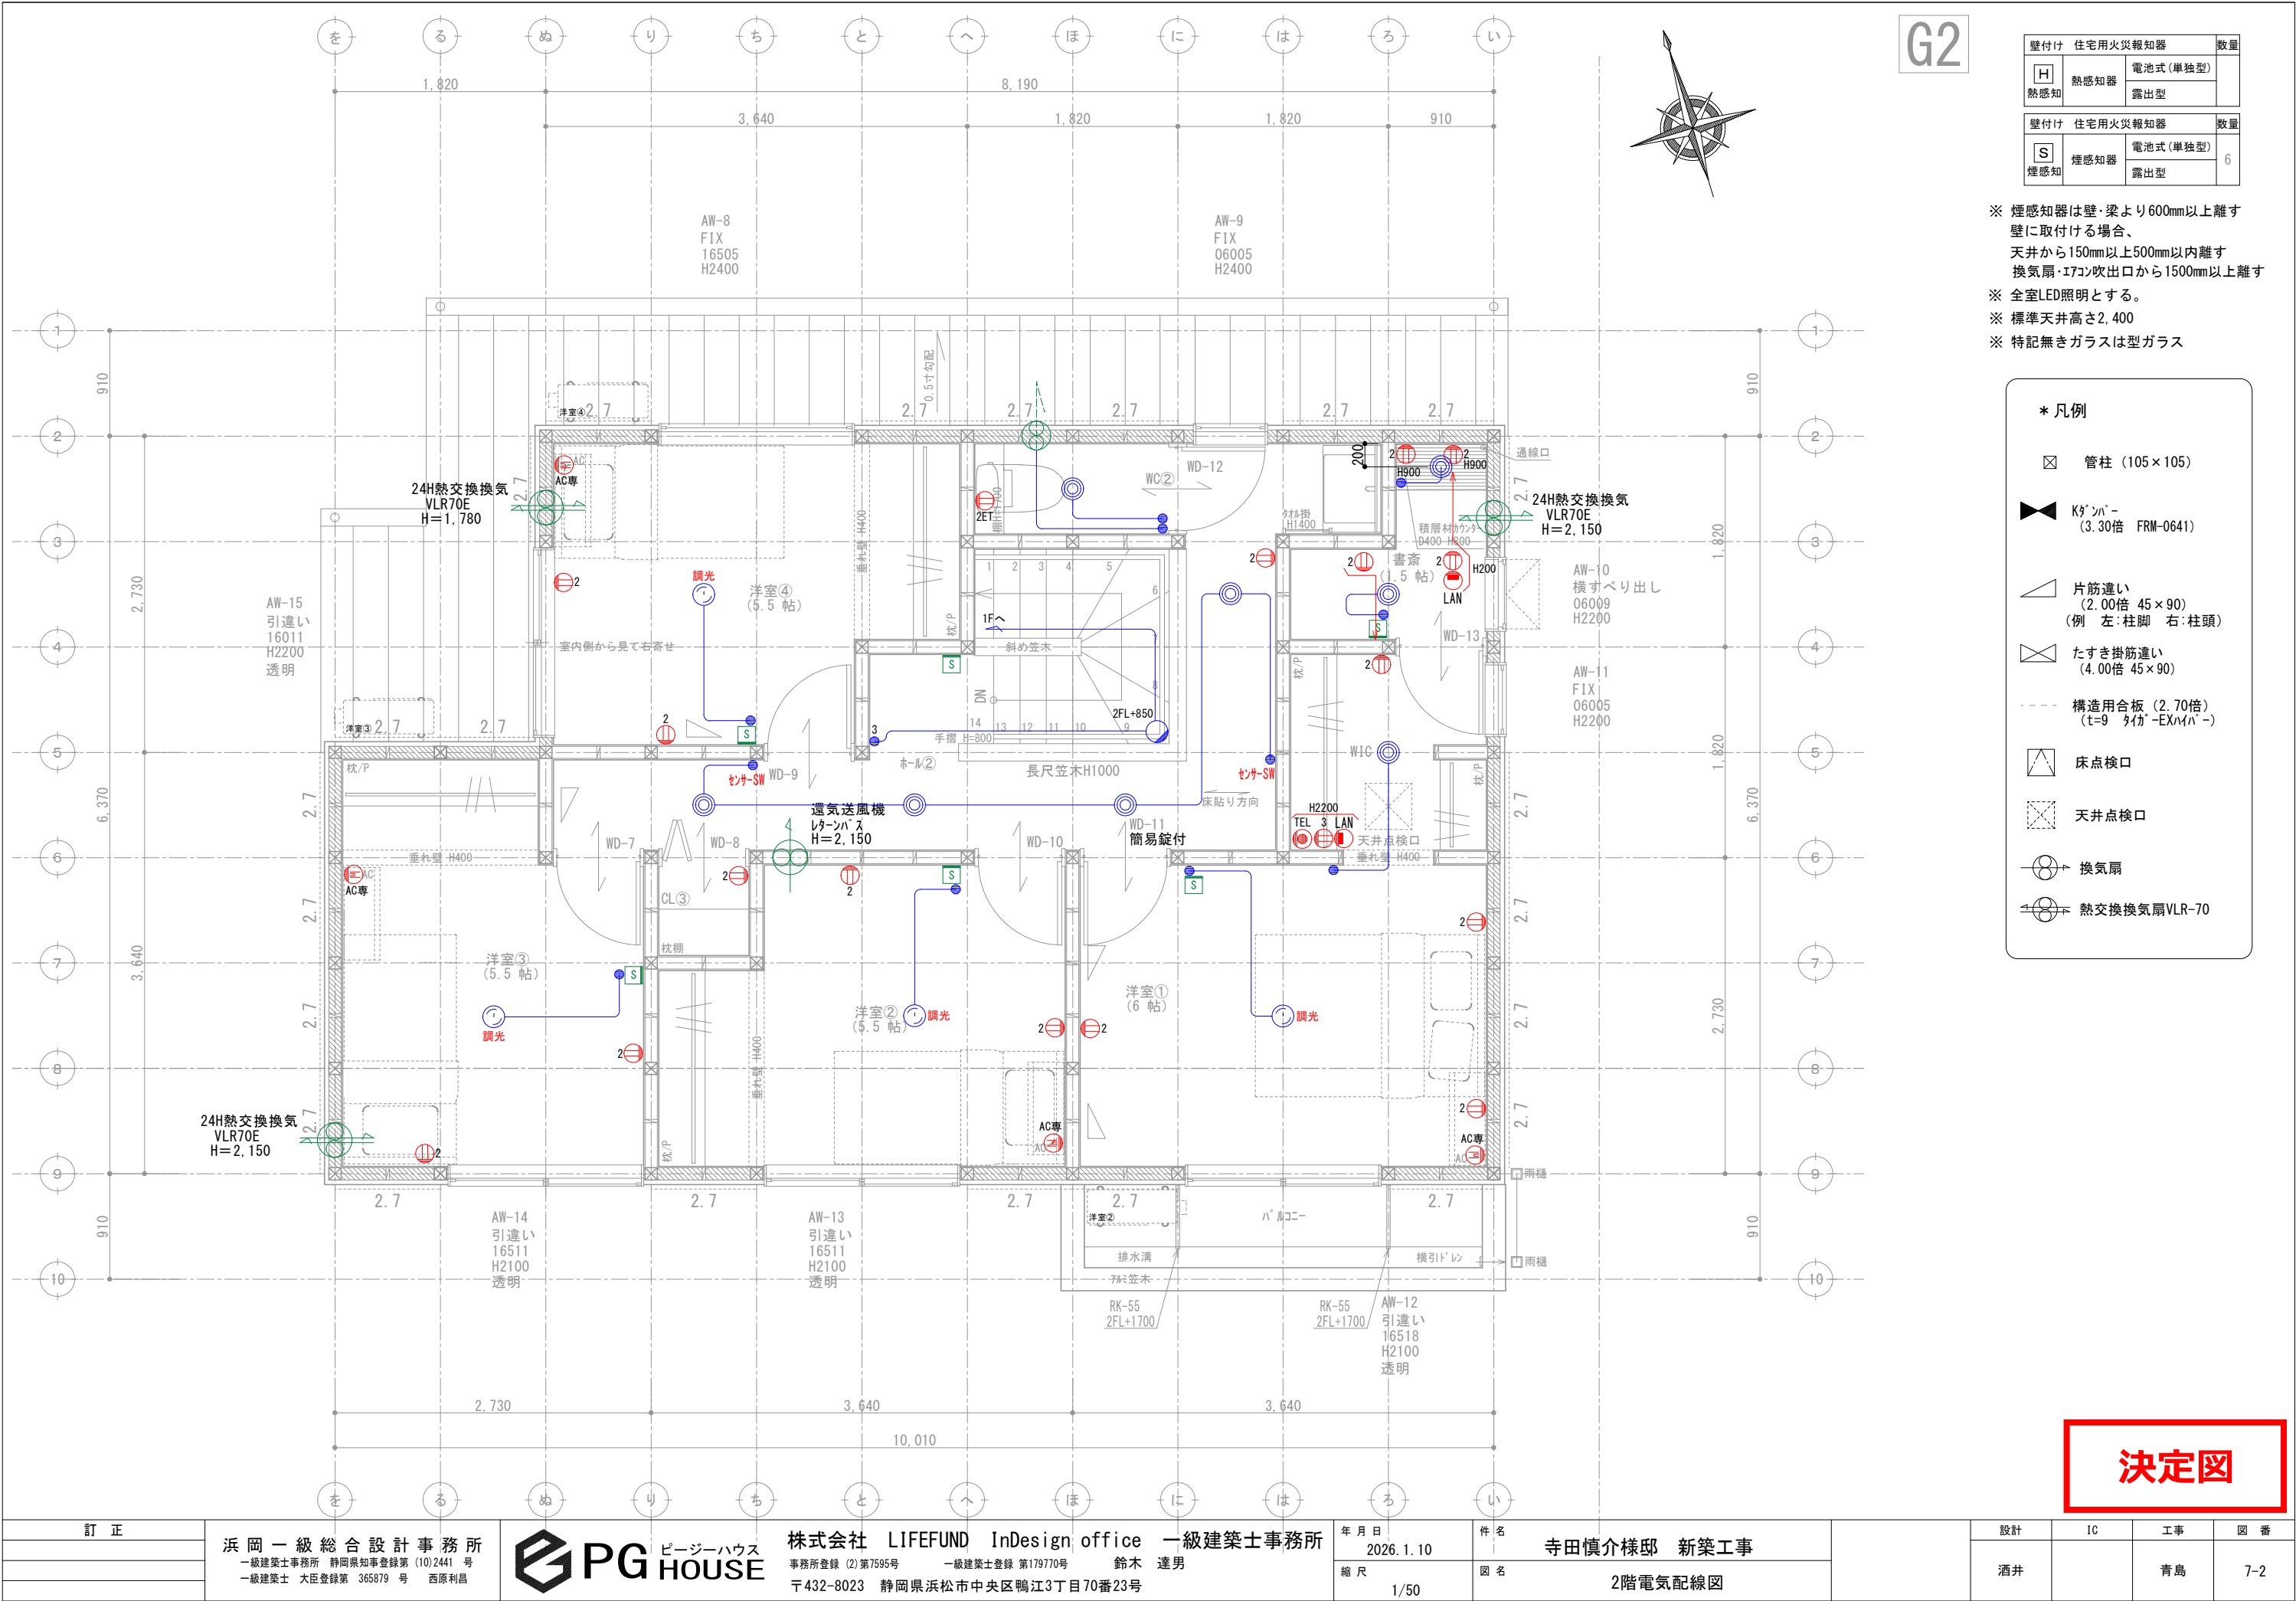

G2

壁付け 住宅用火災報知器			数量
H 熱感知	電池式(単独型)		
	露出型		
壁付け 住宅用火災報知器			数量
S 煙感知	電池式(単独型)		6
	露出型		

※ 煙感知器は壁・梁より600mm以上離す
壁に取付ける場合、
天井から150mm以上500mm以内離す
換気扇・エアコン吹出口から1500mm以上離す
※ 全室LED照明とする。
※ 標準天井高さ2,400
※ 特記無きガラスは型ガラス

- * 凡例
- 管柱 (105×105)

Kagami (3.30倍 FRM-0641)

片筋違い (2.00倍 45×90)
(例 左:柱脚 右:柱頭)

たすき掛筋違い (4.00倍 45×90)

構造用合板 (2.70倍)
(t=9 材種-EXハイバ-)

床点検口

天井点検口

換気扇

熱交換換気扇VLR-70

決定図

ドアホン：VL-SE31XL(Panasonic)


エコエクト リモコン




内部SW：アドバンス
マットブラック




外部：スマートデザインシリーズ
ブラック

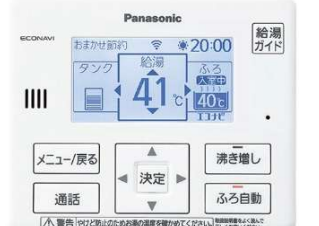

24時間換気 VLR-70

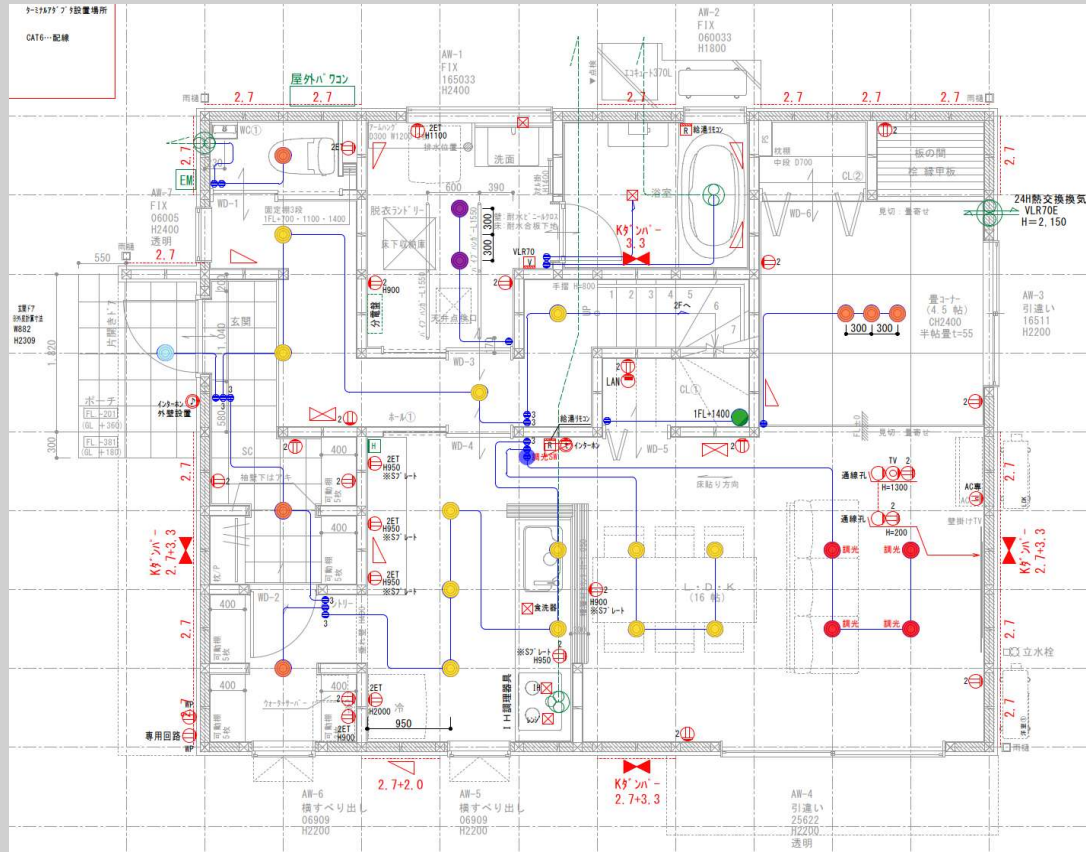

1階

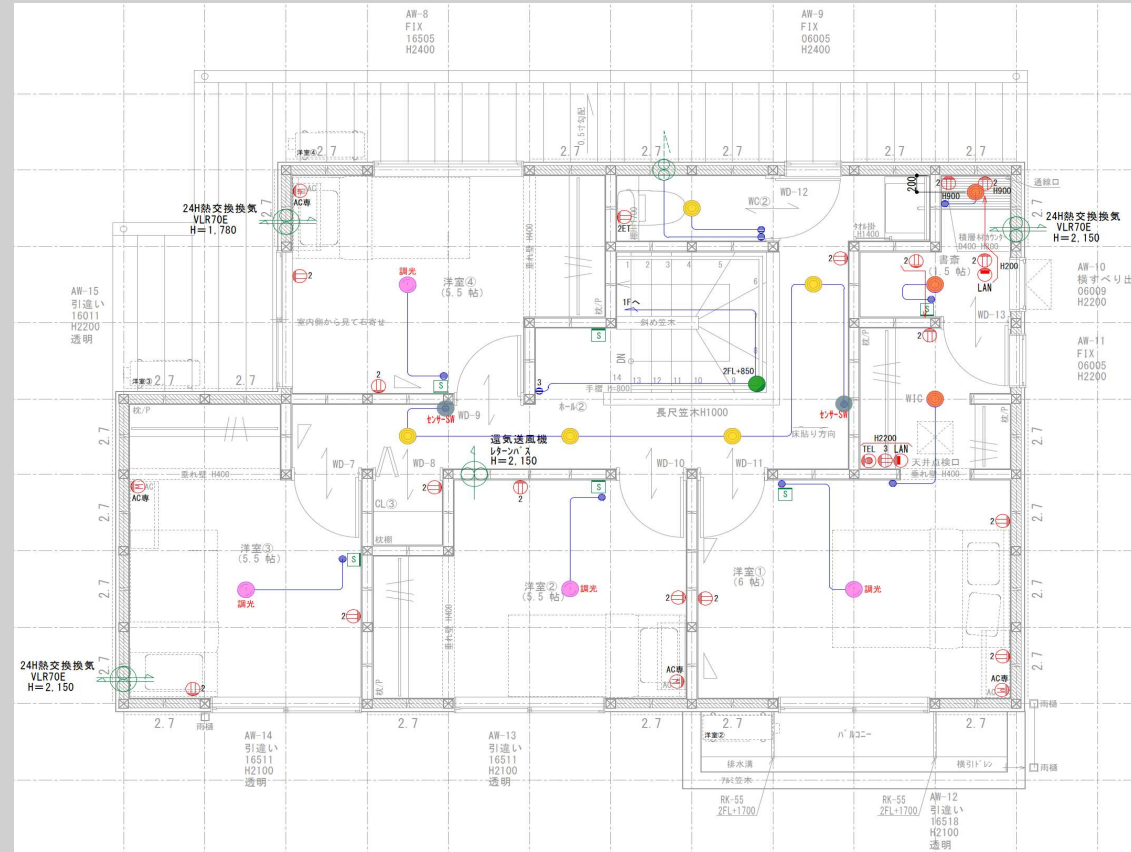

2階

ポーチ灯

×1

センサー付きダウナイト

DDL_6259YB

基本照明ダウナイト

×18

DDL_6132YW

脱衣ランドリー

×2

ダウナイト

DDL_6132AB

洋室①②③④

×4

シーリングライト

DCL_42121

LDK

×4

調光ダウナイト

DDL_6032YWG

CL①、階段

×2

ブラケット

DBK_41545Y

WC①、SC、パントリー、畳コナ、WIC、書斎

×9

ダウナイト

DDL_6132YB

LDK

×1

調光SW

WTA_575831BK

ホール②

×2

センサー-SW

WTA_14119B



高気密SB形 | 人感センサー
連動マルチタイプ

DDL-6259 YB
電球色 / 2700K Ra93(クラス2)

415 lm 7.7 w 53.8 lm/W

¥21,800(税抜) (LED内蔵)

LED 7.7W 白熱灯60W相当

- 鋼板 黒塗装
- アルミダイカスト 黒塗装
- アクリル 乳白(マット)
- 径φ116 埋込穴φ100 埋込深75mm 0.5kg
- 14VA
- 点灯照度調節機能付(暗-明切)
- 点灯保持時間(1分)
- 拡散バネル付
- AC100V
- 光束維持時間40,000時間
- 取付可能天井厚5~25mm
- 調光器併用不可

[連動器具について]
LED調光タイプ60VAまで
LED非調光タイプ不可 電球灯不可
白熱灯60Wまで

強制ON
ソフトスタート
60°
0.1m
近接検知
防雨形
準耐火
LED交換不可
温度保護機能付



COBタイプ | 高気密SB形

DDL-6132 YW
電球色 / 2700K Ra93(クラス2)

440 lm 4.6 w 95.6 lm/W

¥3,600(税抜) (LED内蔵)

LED 4.6W 白熱灯60W相当

- 鋼板 白塗装
- アクリル 乳白(マット)
- 径φ116 埋込穴φ100 埋込深70mm 0.3kg
- 8VA
- 拡散バネル付
- AC100V
- 光束維持時間60,000時間
- 取付可能天井厚5~25mm
- 調光器併用不可

LED交換不可
非調光
防雨形
60°
0.1m
近接検知
温度保護機能付
準耐火



COBタイプ | 高気密SB形

DDL-6132 AB
温白色 / 3500K Ra93(クラス2)

400 lm 4.6 w 86.9 lm/W

¥3,600(税抜) (LED内蔵)

LED 4.6W 白熱灯60W相当

- 鋼板 黒塗装
- アクリル 乳白(マット)
- 径φ116 埋込穴φ100 埋込深70mm 0.3kg
- 8VA
- 拡散バネル付
- AC100V
- 光束維持時間60,000時間
- 取付可能天井厚5~25mm
- 調光器併用不可

LED交換不可
非調光
防雨形
60°
0.1m
近接検知
温度保護機能付
準耐火



タイマー付リモコンフルレール | 調色調光タイプ

DCL-42121
昼光色 / 6500K ~ 電球色 / 2700K Ra93

LED 27.1W 28VA 3699 lm 27.1 w 136.4 lm/W

¥22,000(税抜) (LED内蔵)

再生アクリル 乳白(マット)
径φ510 重138mm 1.4kg
フルレールスイッチ付(全灯・各点灯・常夜灯)
※ 点灯前の調色調光状態
調色機能付(6500K~2700K) ● 調光機能付(5%~100%)
● AC100V ● 光束維持時間40,000時間
調光器併用不可 ● シーンコントロールは使用できません
※ 定電圧電圧、消費電力、固有エネルギー消費効率は
黒白色での値です。

LED交換不可
調光
防雨形
60°
0.1m
近接検知
温度保護機能付
準耐火



COBタイプ | 高気密SB形

DDL-6032 YWG
電球色 / 2700K Ra93(クラス2)


440 lm 5.8 w 75.8 lm/W

¥4,600(税抜) (LED内蔵)

LED 5.8W 白熱灯60W相当

- 鋼板 白塗装
- アクリル 乳白(マット)
- 径φ116 埋込穴φ100 埋込深71mm 0.3kg
- 7VA
- 拡散バネル付
- AC100V
- 調光可能(1%~100%)
- 調光にはLED専用調光器(別売)をご使用ください。
- 光束維持時間60,000時間
- 取付可能天井厚5~25mm

LED交換不可
調光
防雨形
60°
0.1m
近接検知
温度保護機能付
準耐火

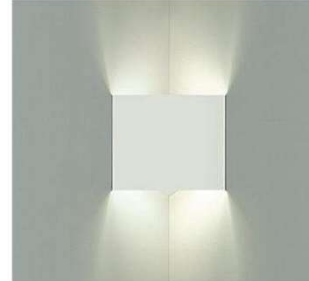

DBK-41545 Y
電球色 / 2700K Ra83

160 lm 4.6 w 34.7 lm/W

¥10,800(税抜) (LED内蔵)

LED 4.6W 白熱灯60W相当

- 鋼板 白塗装
- 市154 高130 出77mm 0.6kg
- 7VA
- 拡散バネル付
- AC100V
- 光束維持時間40,000時間
- 取付可能天井厚5~25mm
- 調光器併用不可

LED交換不可
非調光
防雨形
60°
0.1m
近接検知
温度保護機能付
準耐火



COBタイプ | 高気密SB形

DDL-6132 YB
電球色 / 2700K Ra93(クラス2)

370 lm 4.6 w 80.4 lm/W

¥3,600(税抜) (LED内蔵)

LED 4.6W 白熱灯60W相当

- 鋼板 黒塗装
- アクリル 乳白(マット)
- 径φ116 埋込穴φ100 埋込深70mm 0.3kg
- 8VA
- 拡散バネル付
- AC100V
- 光束維持時間60,000時間
- 取付可能天井厚5~25mm
- 調光器併用不可

LED交換不可
非調光
防雨形
60°
0.1m
近接検知
温度保護機能付
準耐火



WTA575831BK
希望小売価格 13,330円(税抜)
※掲載の価格には消費税は含まれていません。

アドバンスシリーズ(ソリッド)
[LED]埋込逆位相調光スイッチC(はたるスイッチC)
(適合LED専用3.2A)(ロータリー式)
(下照照度設定機能付)(ネームなし)(マットブラック)

プレート別売
WTA7101BK
希望小売価格 430円(税抜)
※掲載の価格には消費税は含まれていません。

アドバンスシリーズ スイッチプレート(1連用)
(マットブラック)

Archi Design



WTA14119B
希望小売価格 12,800円(税抜)
※掲載の価格には消費税は含まれていません。

壁取付 熱線センサー付自動スイッチ(鏡器)
(検知後連続動作時間 約10秒~30分可変形)
(明るさセンサー・手動スイッチ付)(マットブラック)

3A 100V AC

プレート別売

決定図


PG House

寺田慎介 様邸新築工事


Lighting Plan

2026.1.10

(図面 7-3)

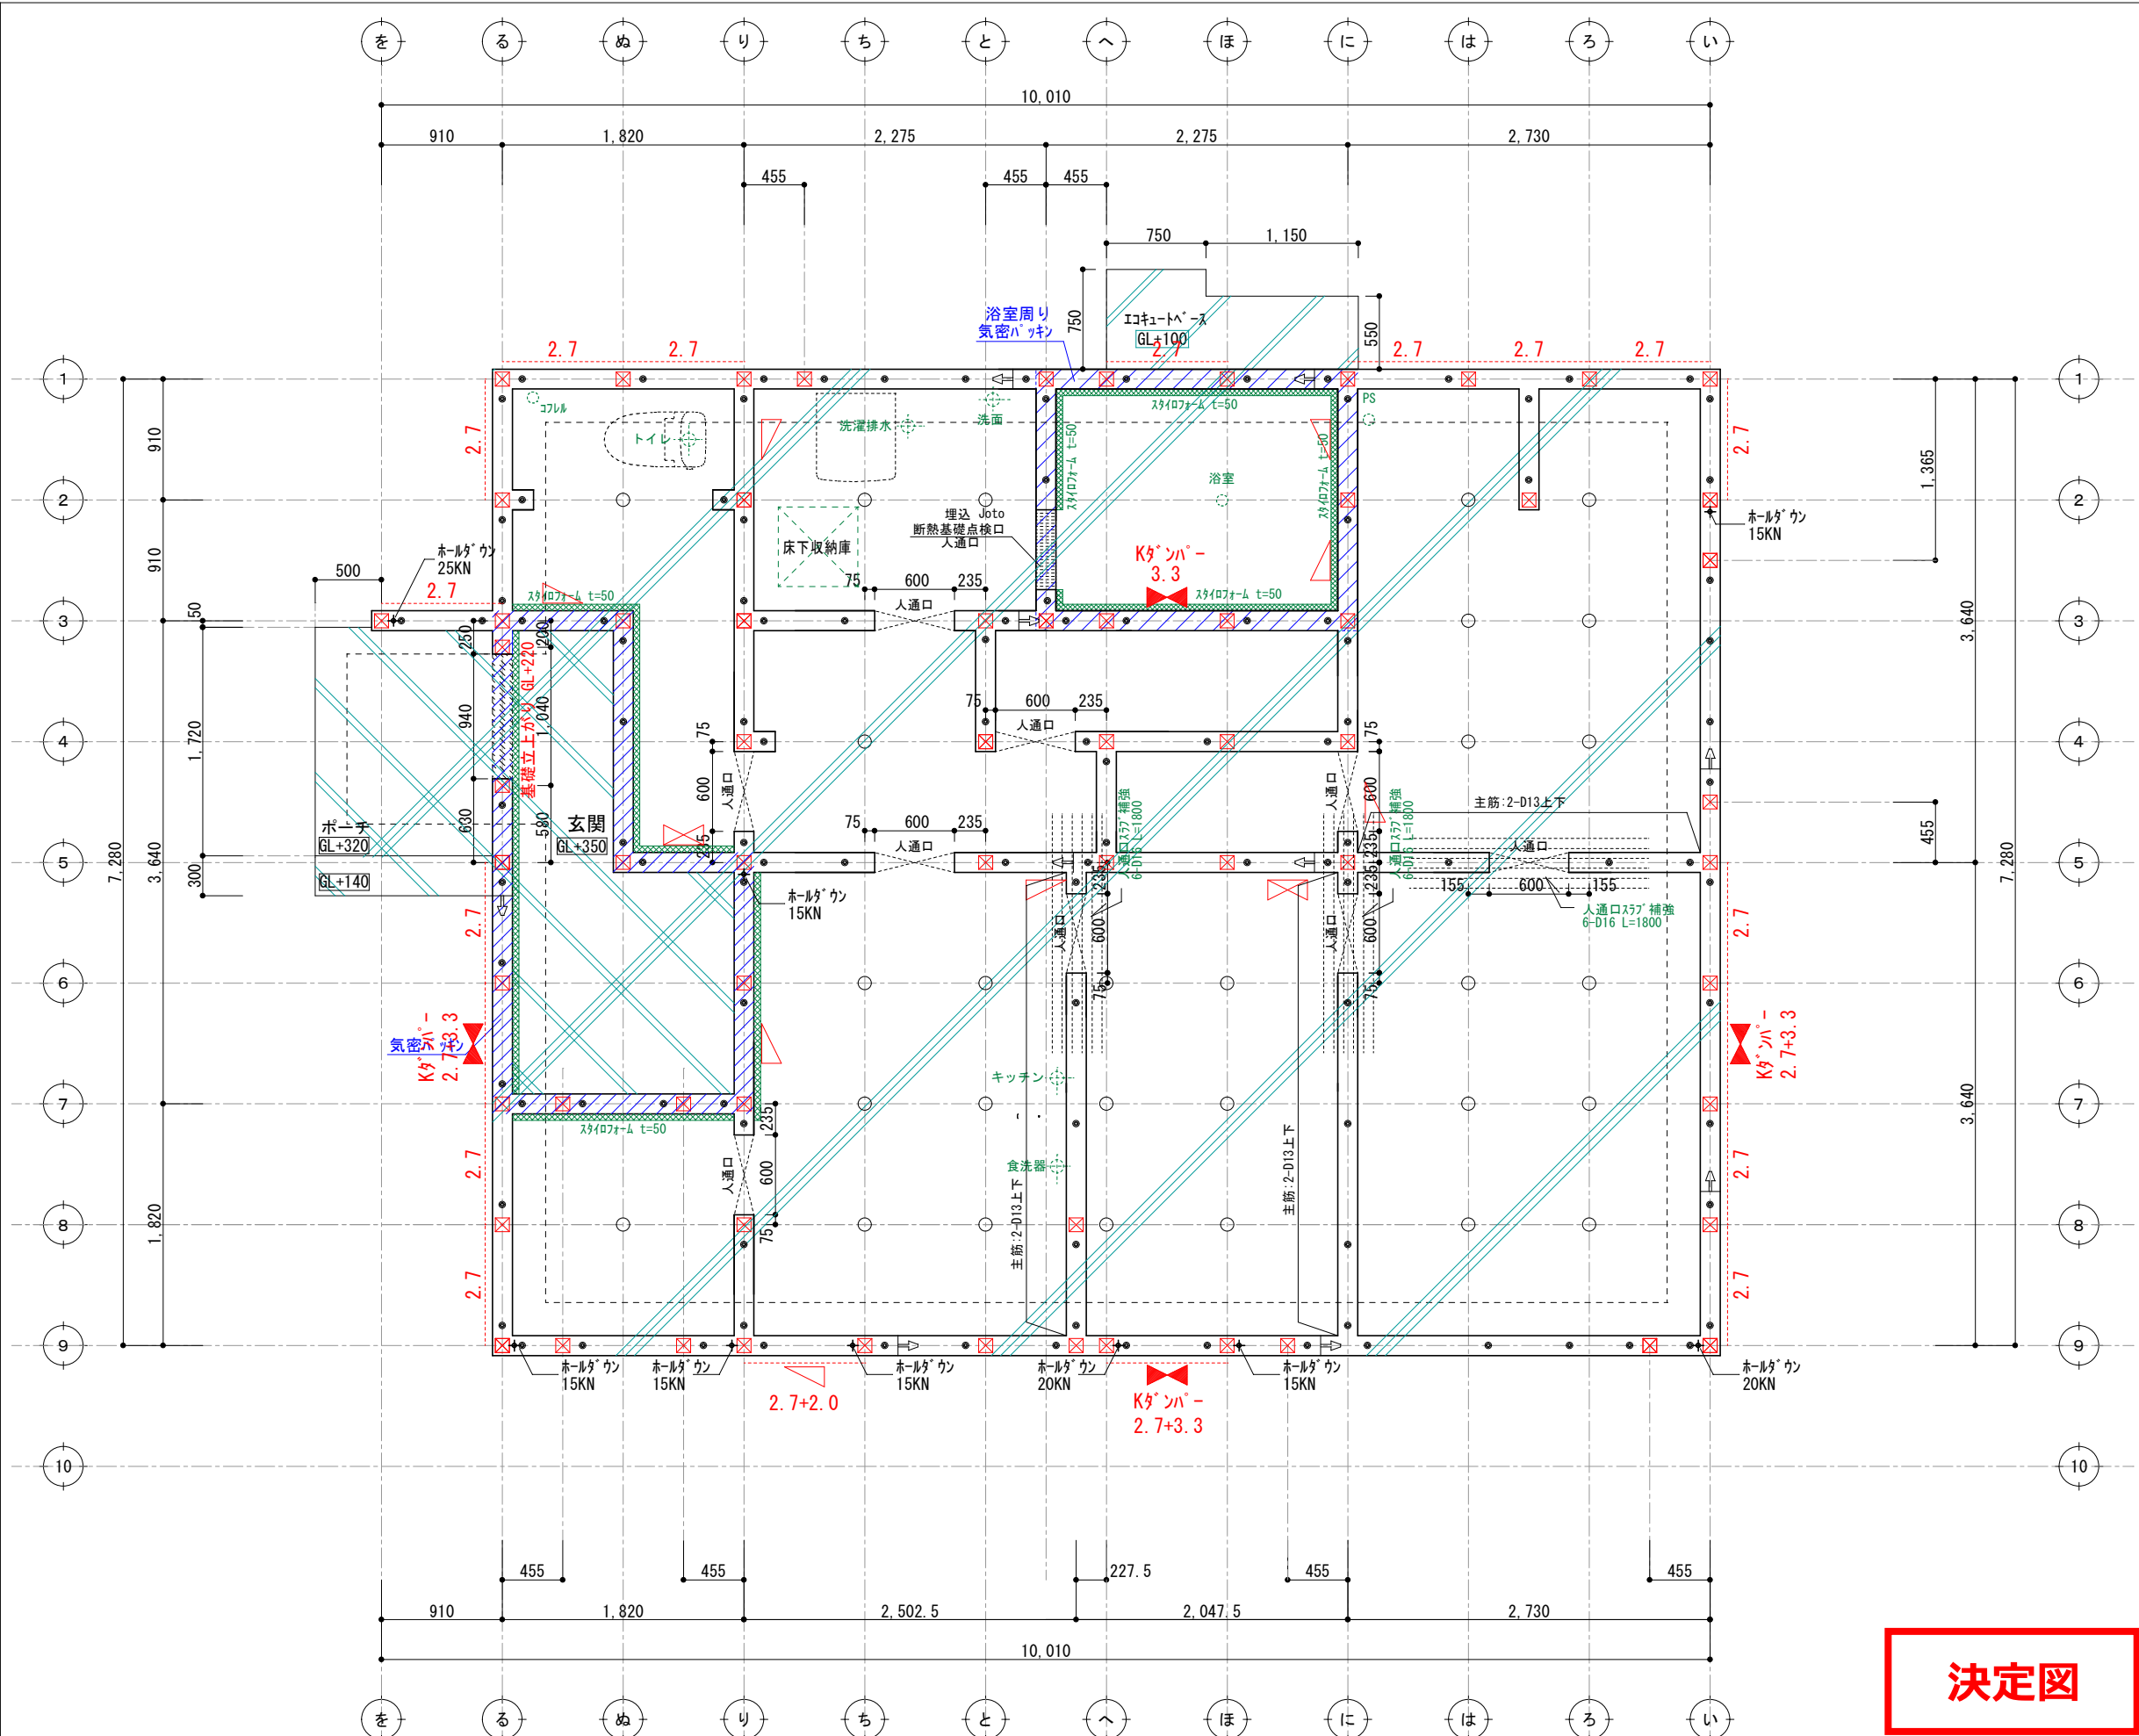

構造体ベースコンクリート t=150

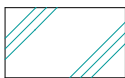


後打ち土間コン



- アンカーボルトの配置
- 土台切れの箇所より150mm
 - 土台の継手及び仕口の端部より150mm
 - 耐力壁の端部、筋交いの脚部より150mm
 - 1.82m以下の間隔
 - 250mm以上埋込み
 - 基礎天端より120mm

- 筋かい凡例
- 柱脚 柱頭 片筋かい
 - たすき掛け筋かい
 - 構造用パネル

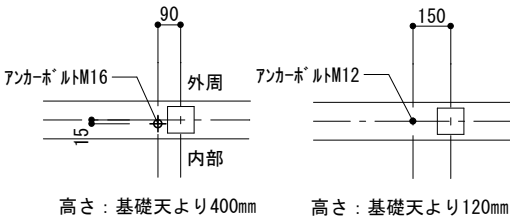

高さ：基礎天より400mm

高さ：基礎天より120mm







ホールダウン用アンカーボルト配置

アンカーボルト配置

- 凡例
- 通し柱 (105*105) 管柱 (105*105)
 - アンカーボルトM12 L=400
 - + ホールダウンアンカーM16 L=800
 - 柱芯より90mm 280mm以上埋め込み (カナイフリストアンカーボルトM16)
 - ⊕ 鋼製束
 - 土台ジョイント
 - ベースコンクリート (t=150)
 - 後打ちコンクリート

- 基礎伏図について特記なき場合に限り下記による。
1. コンクリート：呼び強度 21N/mm²
 2. 鉄筋：SD295A
 3. 設計地耐力：fe=20kN/m²
地耐力計測後、不足の場合は相当の改良を行い、満たすものとする。
 4. 基礎の位置は、芯振分けとする。
 5. 玄関・S/C・UB周囲の基礎天端は気密パッキン施工 (網掛け部) とし、その他の基礎天端は基礎パッキン施工とする。
 6. 設備配管の屋内への取り入れは基礎立上り部のスリーブによる。

決定図

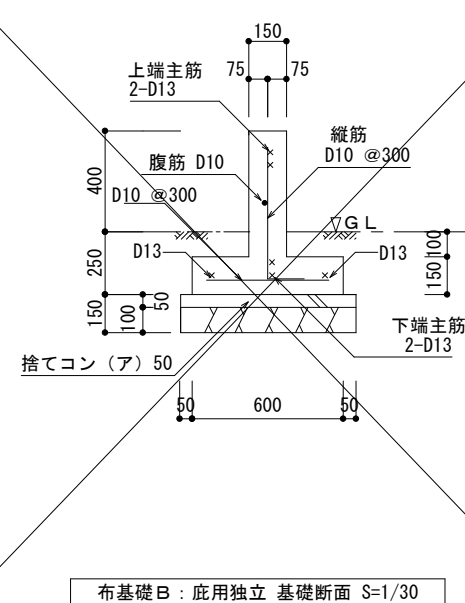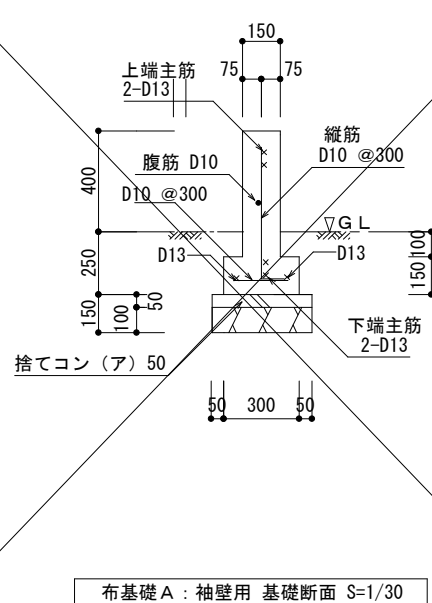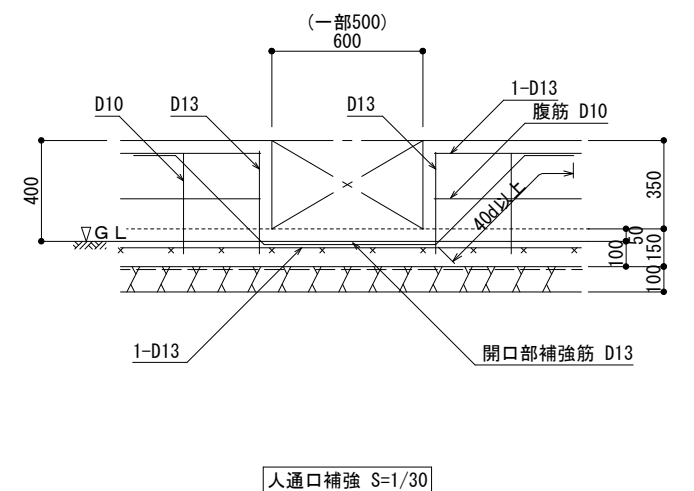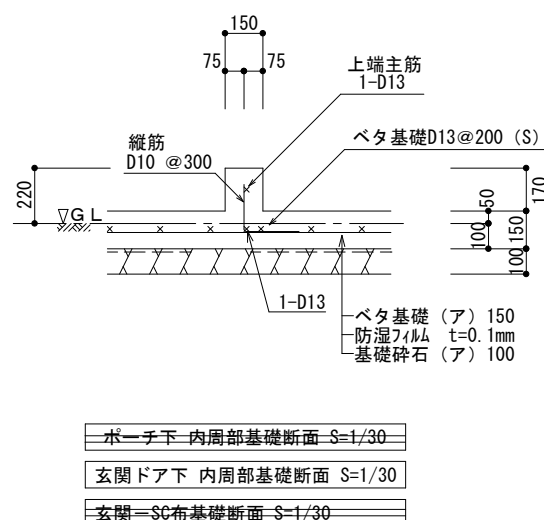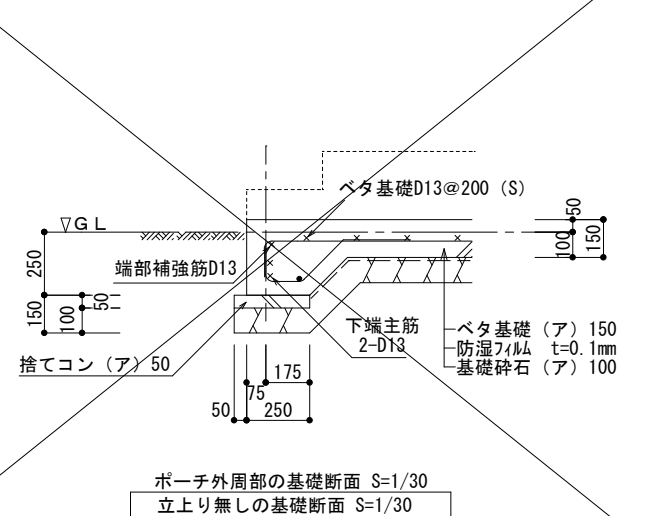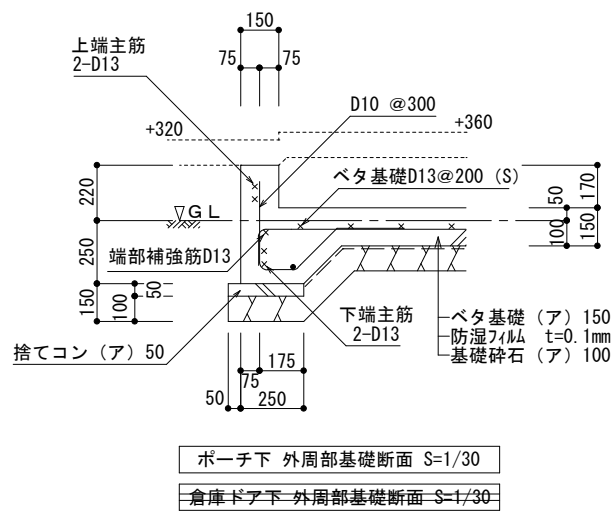

基礎の寸法 及び 配筋の検証方法	基礎立上り配筋は、 (財)日本住宅・木材技術 センター発行のスパン表 (増補版)による。 ベタ基礎スラブ配筋は、 まもりすまい保険設計施工 基準同解説のベタ基礎配筋表 による。具体的な寸法・配 筋は基礎詳細図参照。
---------------------------------------	--


鉄筋断面表記

・ D10を示す。


× ・ ・ D13を示す。

※使用しない断面は

決定図

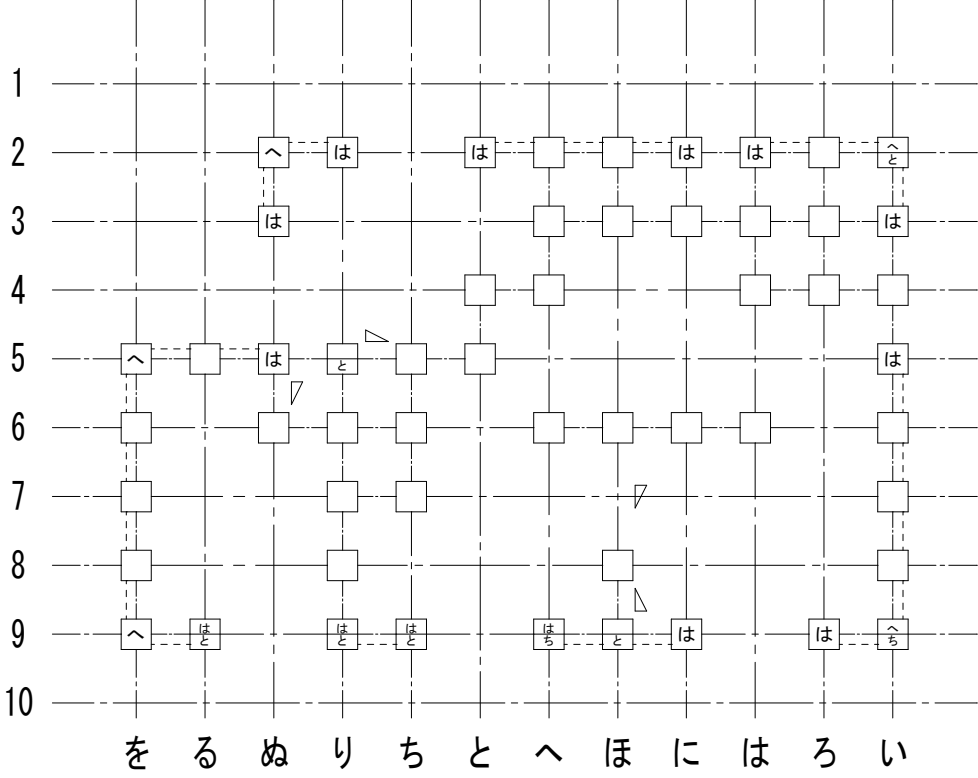

2階柱壁伏図

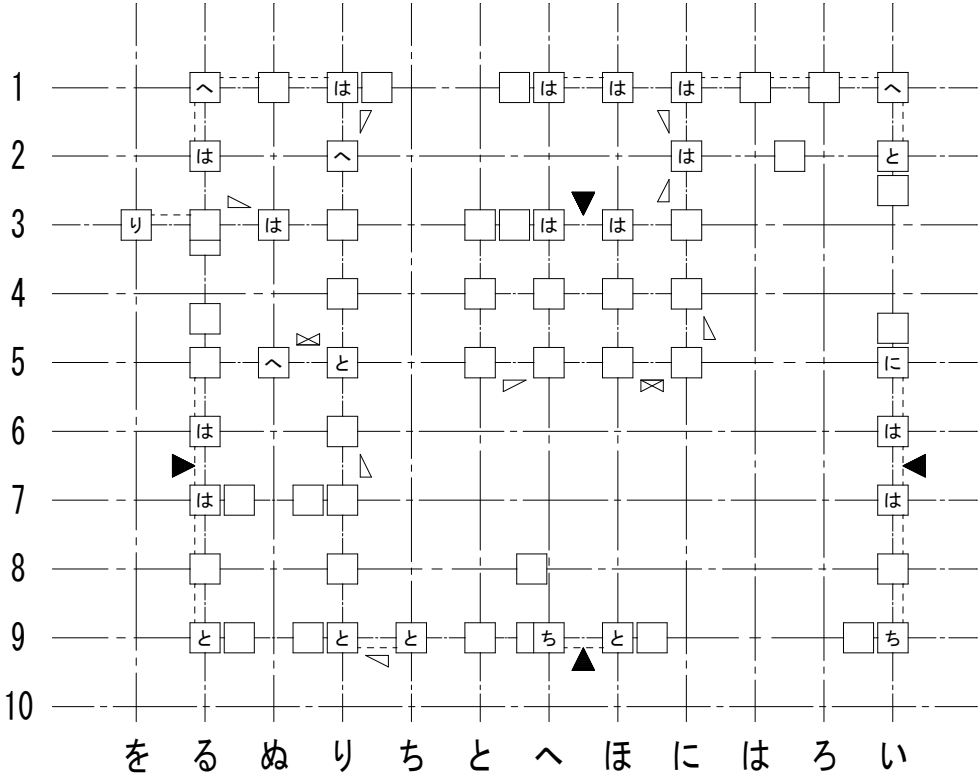

1階柱壁伏図

接合部凡例				*接合部凡例はユーザ設定されたものです。	
記号	仕様（カナイ金物）		N	倍率	
SBCP	スリムビルドコーナー75, チビクリCK(化粧柱の場合)		0.00	1.00	
SBCP	スリムビルドコーナー75, チビクリCK(化粧柱の場合)		0.65	1.00	
SBCP	は	スリムビルドコーナー75	1.00	1.00	
ARCG	に	アレントコーナー合板用	1.40	2.20	
ARCG	ほ	アレントコーナー合板用	1.60	2.20	
ARCG	へ	アレントコーナー合板用	1.80	2.20	
HD15	と	ブレイブホールダウン B-HD15	2.80	3.60	
HD20	ち	ブレイブホールダウン B-HD20	3.70	4.70	
HD25	り	ブレイブホールダウン B-HD25	4.70	4.80	
HD30	ぬ	ブレイブホールダウン B-HD30	5.60	7.20	
J1	る	腰掛け蟻若しくは大入れ蟻掛け+羽子板*ルト、短冊金物		1.90	梁継手・仕口用
J2	を	腰掛け蟻若しくは大入れ蟻掛け+羽子板*ルト、短冊金物×2		3.00	梁継手・仕口用

※表示なき金物は「は」とする。

接合部凡例				*接合部凡例はユーザ設定されたものです。	
記号	仕様（タナカ金物）		N	倍率	
FCP	フックコーナー, チビクリCK(化粧柱の場合)		0.00	1.00	
FCP	フックコーナー, チビクリCK(化粧柱の場合)		0.65	1.00	
FCP	は	フックコーナー	1.00	1.00	
CCP	に	シナコーナー	1.40	2.20	
CCP	ほ	シナコーナー	1.60	2.20	
CCP	へ	シナコーナー	1.80	2.20	
HD15	と	ビス止めホールダウンU HD15	2.80	3.60	
HD20	ち	ビス止めホールダウンU HD20	3.70	4.70	
HD25	り	ビス止めホールダウンU HD25	4.70	4.80	
HD30	ぬ	ビス止めホールダウンU HD15×2 (HD35)	5.60	7.20	
J1	る	腰掛け蟻若しくは大入れ蟻掛け+羽子板*ルト、短冊金物		1.90	梁継手・仕口用
J2	を	腰掛け蟻若しくは大入れ蟻掛け+羽子板*ルト、短冊金物×2		3.00	梁継手・仕口用

※表示なき金物は「は」とする。

筋かいの種類に応じた筋かいの端部の接合部の仕様		
	筋かいの種類	接合部の仕様（構造方法）
イ	鉄筋φ9	柱又は横架材を貫通し、三角座金を介してナット締め、又は鋼板添え板を用い鋼板を柱及び横架材にCN90, 8本平打ち
ロ	筋かい:15×90	柱・横架材を欠き込み、柱・横架材双方に対してN65, 5本平打ち
ハ	筋かい:30×90	鋼板添え板t=1.6mmを筋かいに対してボルトφ12及びCN65, 3本平打ち、柱に対してCN65, 3本平打ち、横架材に対してCN65, 4本平打ち。筋かいプレートBP同等品
ニ	筋かい:45×90	鋼板添え板t=2.3mmを筋かいに対してボルトφ12及びスクリュー釘φ4.5L50, 7本平打ち、柱及び横架材に対してスクリュー釘φ4.5L50, 5本平打ち。筋かいプレートBP-2同等品
ホ	筋かい:90×90	柱又は横架材にボルトφ12mmを用いて一面剪断接合


胴差と通し柱の接合部の仕様		
	胴差と通し柱の条件	仕口
T1	通し柱の片側に胴差が来る場合	胴差を柱にかたぎ大入れ短ほぞ差しの上、羽子板ボルト、かね折り金物又は同等以上の仕口
T2	通し柱の両側に胴差が来る場合	胴差を柱にかたぎ大入れ短ほぞ差しの上、短冊金物又は、同等以上の仕口で胴差相互を緊結
T3	通し柱と胴差の接合部の近くに90×90以上の筋かいが来る場合(通し柱が建物の出隅にあるか、筋かい壁が外壁と直交して接する場合)	胴差を通し柱に、15KN用引き寄せ金物を水平に用いて緊結

決定図

アクセントクロス指示書

G2

SLP-375

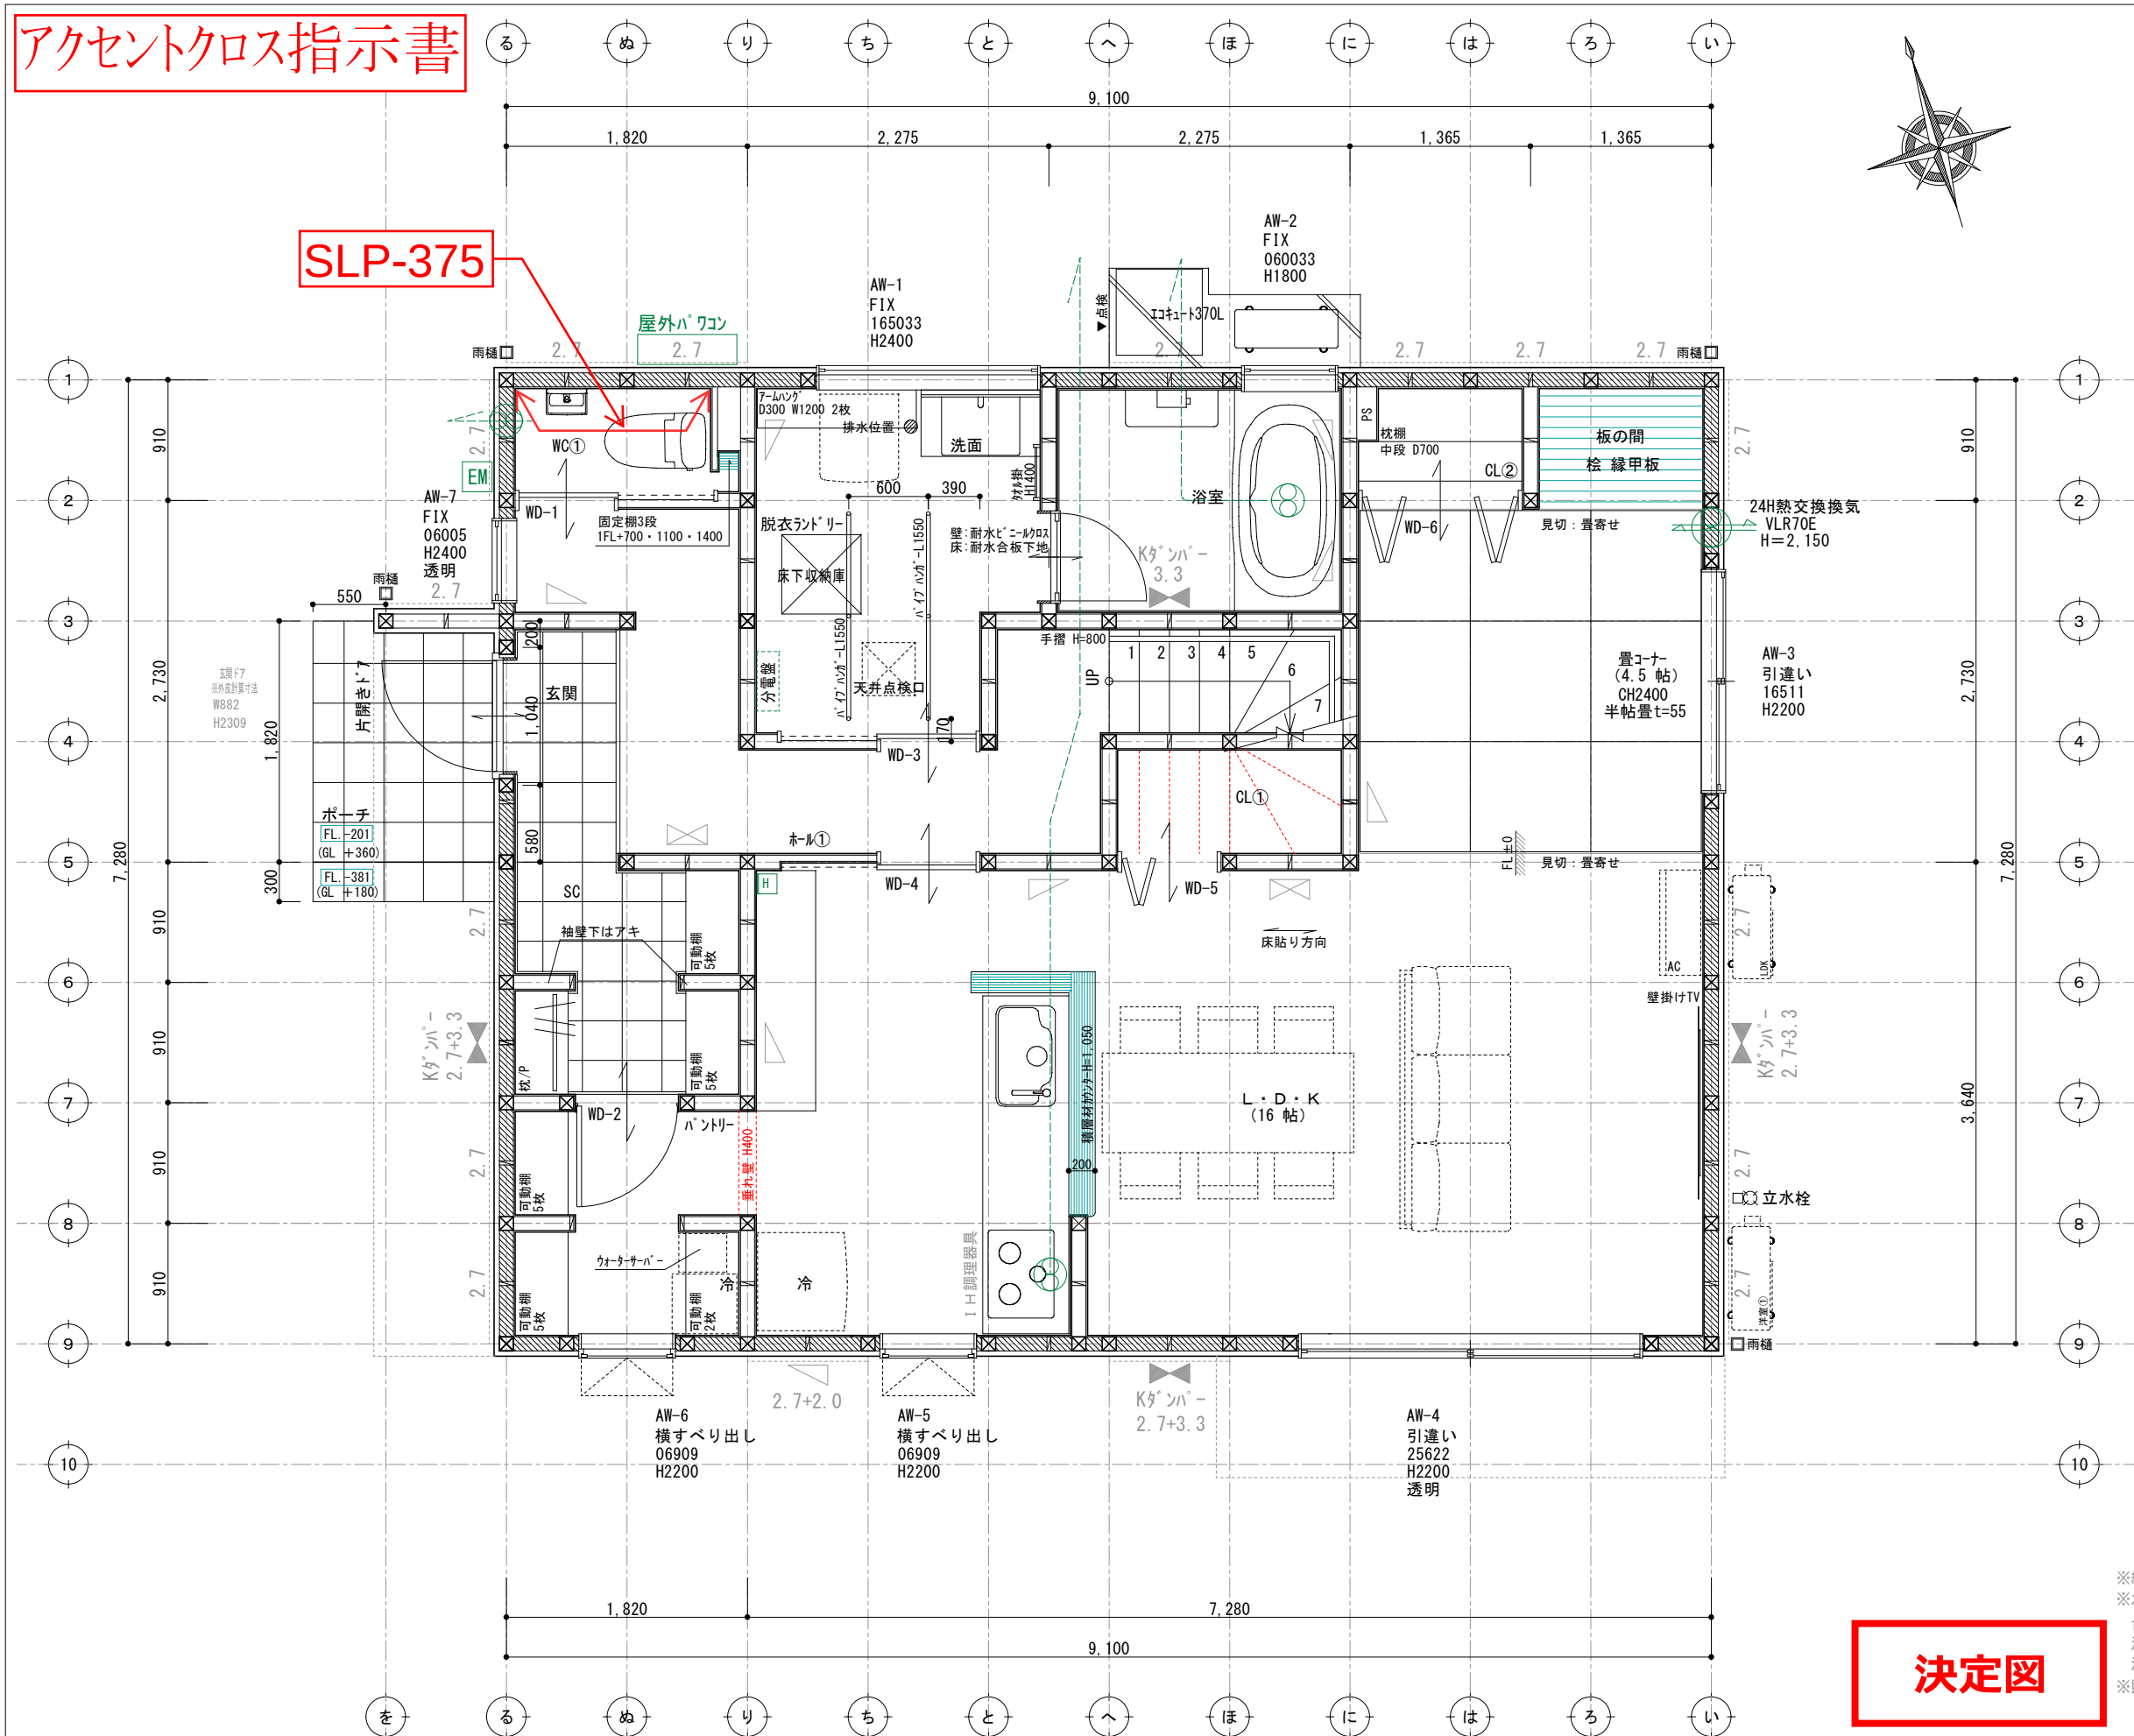

壁付け 住宅用火災報知器			数量
H 熱感知	電池式(単独型)		1
	露出型		
壁付け 住宅用火災報知器			数量
S 煙感知	電池式(単独型)		
	露出型		

- ※ 煙感知器は壁・梁より600mm以上離す壁に取付ける場合、天井から150mm以上500mm以内離す換気扇・エアコン吹出口から1500mm以上離す
- ※ 全室LED照明とする。
- ※ 標準天井高さ2,400
- ※ 特記無きガラスは型ガラス

* 凡例

- 管柱 (105×105)
- Kタンパ (3.30倍 FRM-0641)
- 片筋違い (2.00倍 45×90) (例 左:柱脚 右:柱頭)
- たすき掛筋違い (4.00倍 45×90)
- 構造用合板 (2.70倍) (t=9 タイプ-Eハイバ)
- 床点検口
- 天井点検口
- 換気扇
- 熱交換換気扇VLR-70

脱衣・ランドリー 仕上材
天井: ア9.5PB下地ビニルクロス貼り
壁: ア12.5PB下地ビニルクロス貼り
床: ア24+15耐水合板下地フローリング張り


階段寸法表
有効幅: 750
踏面: 210
蹴上: 207.15

※下屋部分点検口について
ダウンライト、FS天井点検口、UB点検口より
ポールカメラやファイバースコープ等の
検査機器等を使用して点検する

※給水設備: ヘッダー分岐後の全ての配管径は13A以下とする
※水栓: 一般社団法人日本バルブ工業会の定義による節湯水栓
台所: 2バルブ水栓以外のその他の水栓(水優先吐水機能)
浴室シャワー: 2バルブ水栓以外のその他の水栓(小流量吐水機能)
洗面: 2バルブ水栓以外のその他の水栓(水優先吐水機能)
※照明設備: 全室LED照明とし居室においては調光制御、非居室においては
人感センサーを採用する

決定図

訂正	浜岡一級総合設計事務所 一級建築士事務所 静岡県知事登録第 (10)2441 号 一級建築士 大臣登録第 365879 号 西原利昌	PG HOUSE	株式会社 LIFEFUND InDesign office 一級建築士事務所 事務所登録 (2) 第7595号 一級建築士登録 第179770号 鈴木 達男 〒432-8023 静岡県浜松市中央区鴨江3丁目7番23号	年月日 2026. 1. 10 縮尺 1/50	件名 寺田慎介様邸 新築工事 図名 1階平面図	設計 酒井	IC	工事 青島	図番 3-1
----	--	----------	--	----------------------------------	----------------------------------	----------	----	----------	-----------

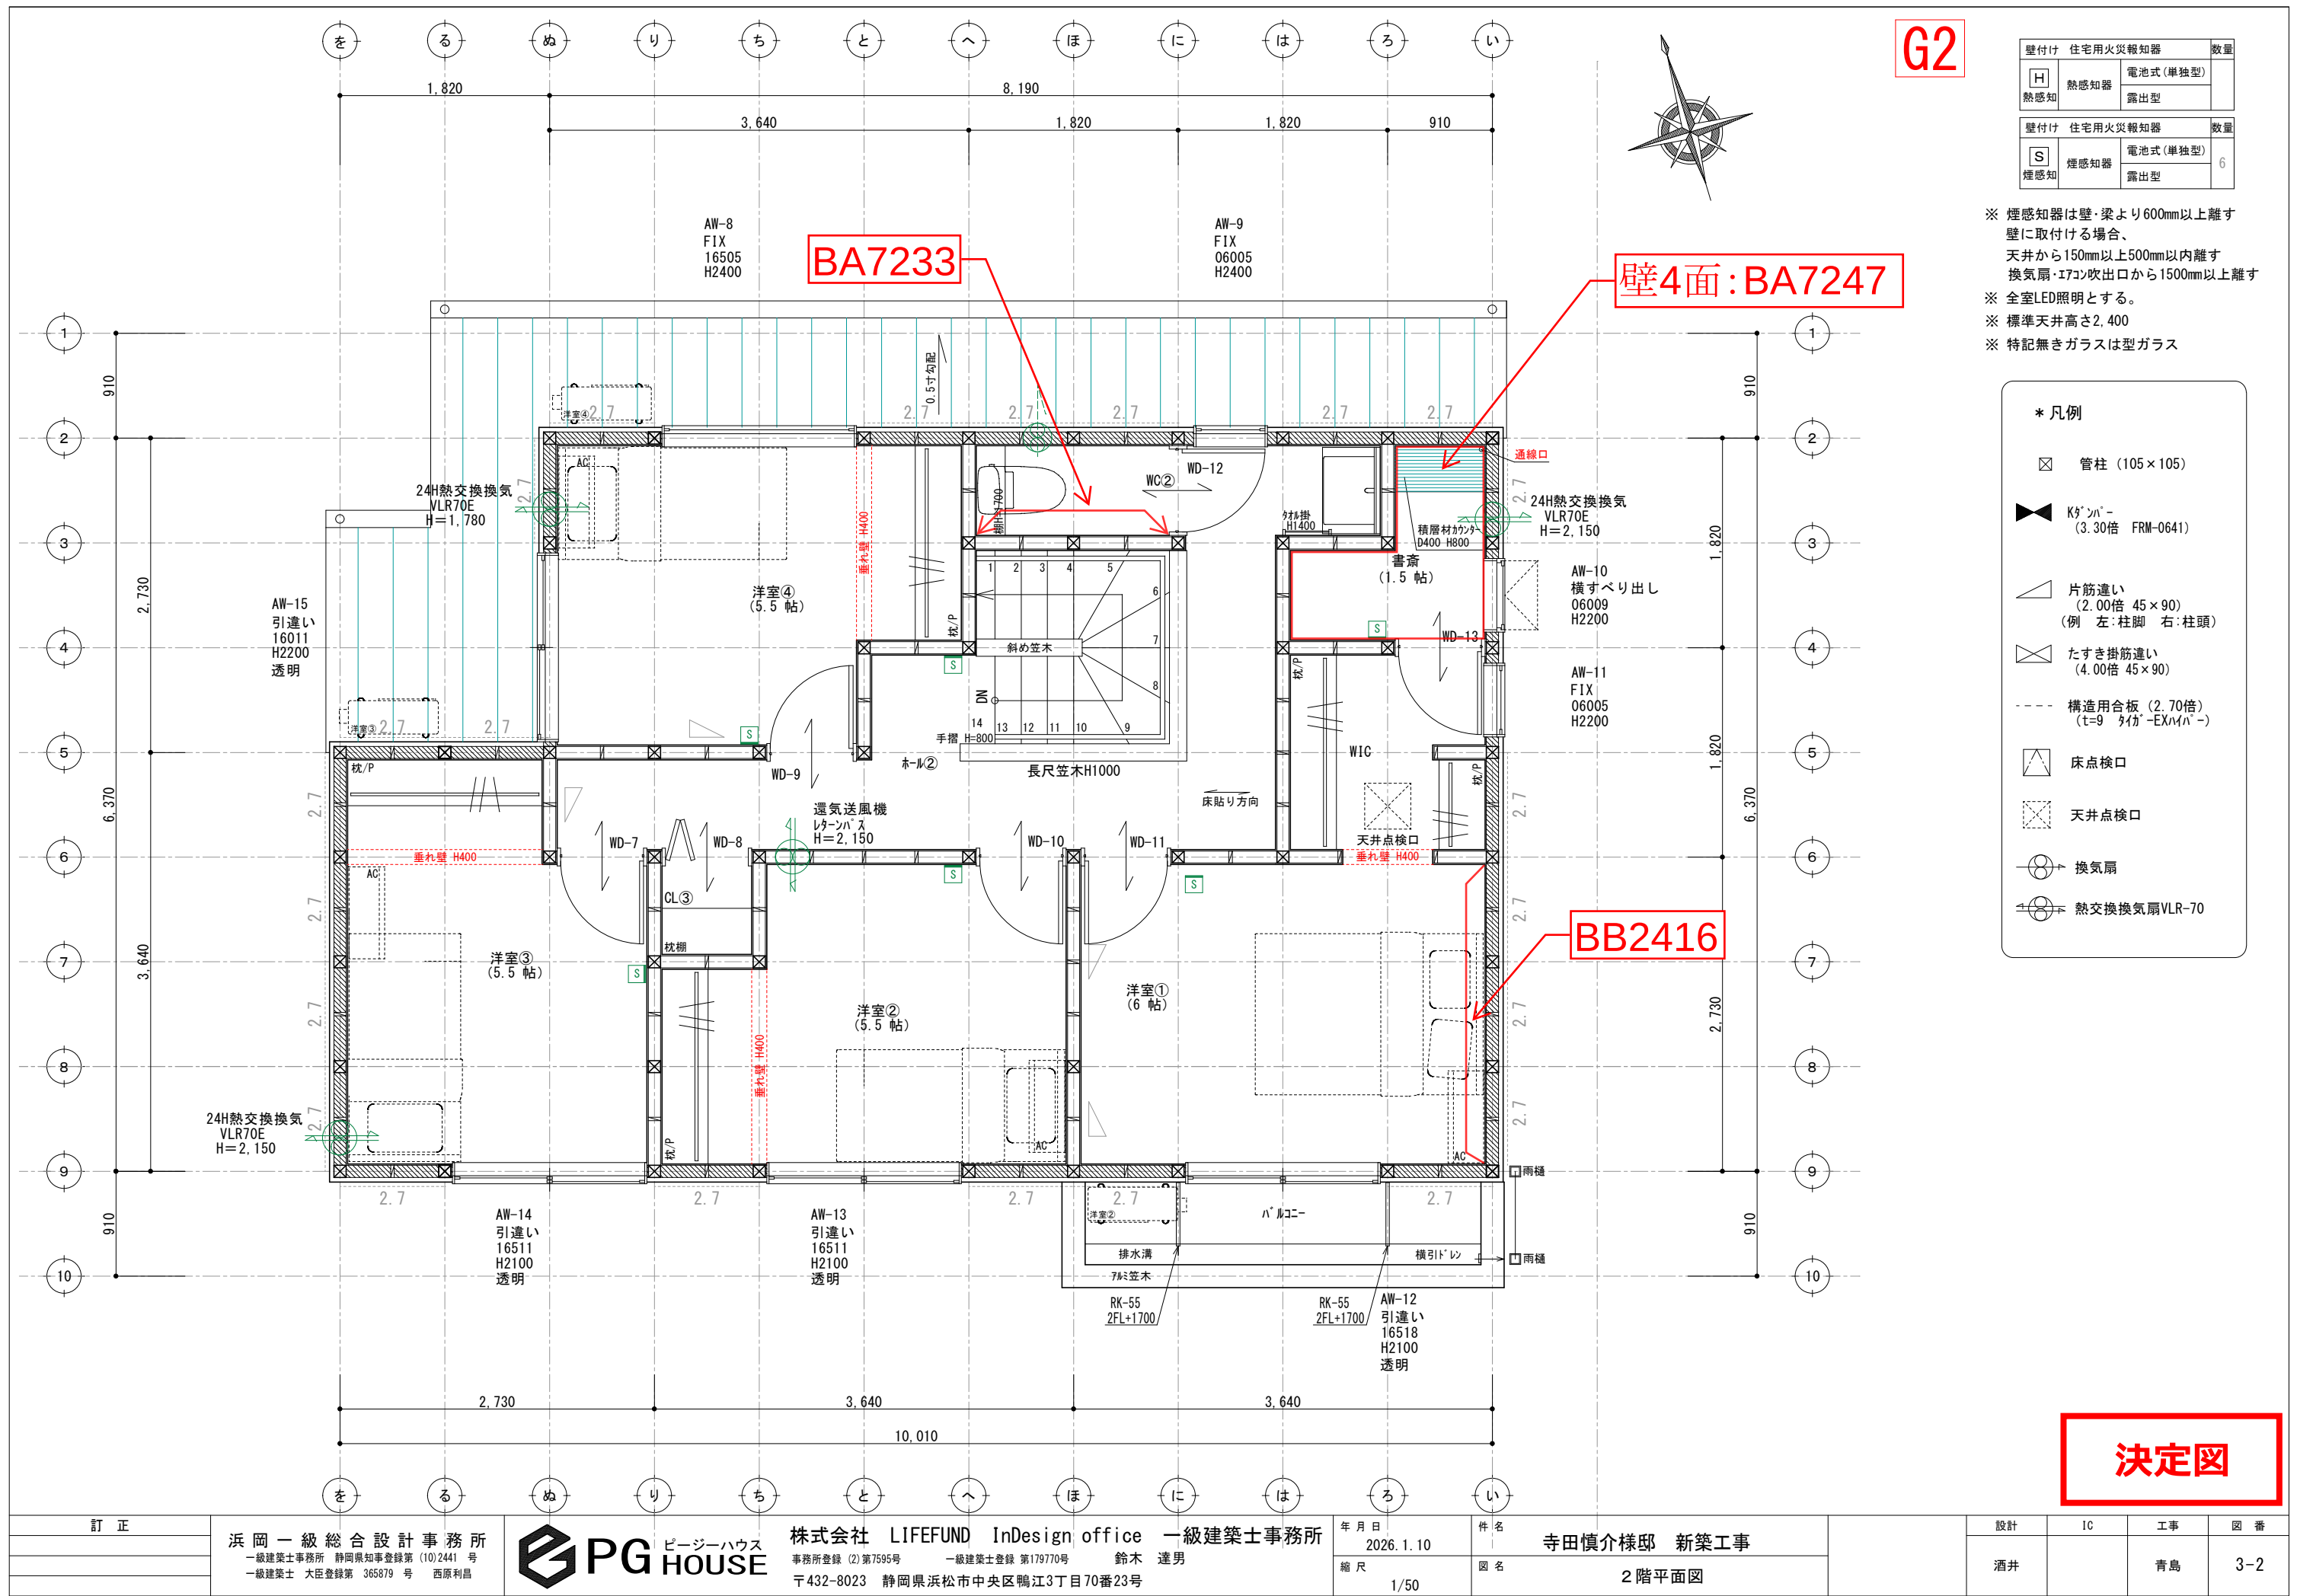

G2

壁付け 住宅用火災報知器			数量
H	熱感知器	電池式(単独型)	
	露出型		
壁付け 住宅用火災報知器			数量
S	煙感知器	電池式(単独型)	6
	露出型		

※ 煙感知器は壁・梁より600mm以上離す
壁に取付ける場合、
天井から150mm以上500mm以内離す
換気扇・エアコン吹出口から1500mm以上離す
※ 全室LED照明とする。
※ 標準天井高さ2,400
※ 特記無きガラスは型ガラス

- * 凡例
- 管柱 (105×105)
 - Kタンパー (3.30倍 FRM-0641)
 - 片筋違い (2.00倍 45×90)
(例 左:柱脚 右:柱頭)
 - たすき掛筋違い (4.00倍 45×90)
 - 構造用合板 (2.70倍)
(t=9 タイプ-EXハイバ-)
 - 床点検口
 - 天井点検口
 - 換気扇
 - 熱交換換気扇VLR-70

決定図