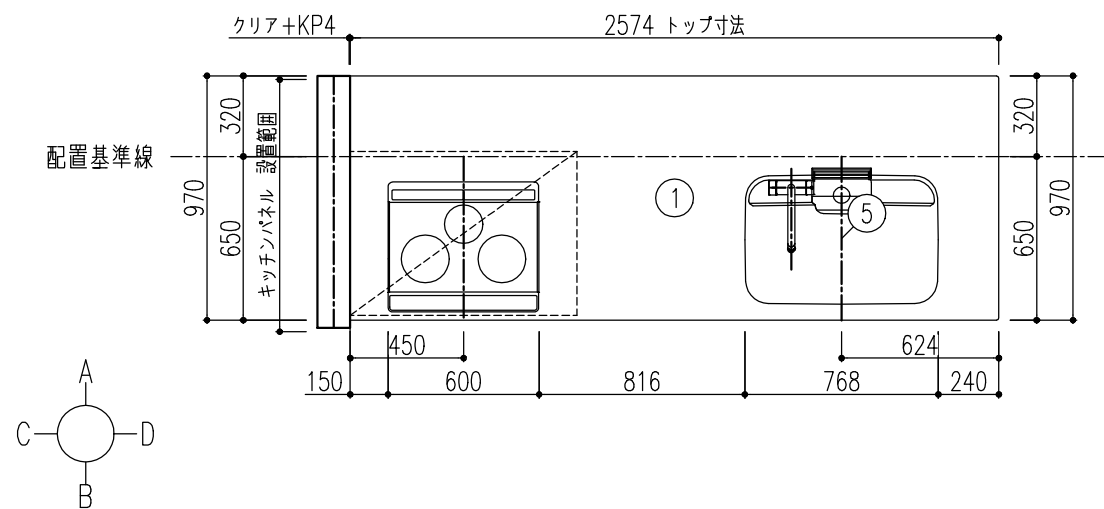



[illegible]

【 ご注意 】


- 記載のキャビネット寸法は扉前面での呼び寸法です。キャビネット本体の寸法・扉厚み等は商品ガイドの巻末資料をご確認ください。
- 記載のワークトップ、カウンター、エンドパネル、サイドパネルの寸法は呼び寸法です。詳細寸法は商品ガイドの巻末資料をご確認ください。
- レンジフード電源プラグ仕様：3芯電源プラグ（アース工事が必要です。）

特記事項 扉色 VK5:グレージュスタック 取手 [M]スリム取手（ブラック） ワークトップカラー 【LE】シルフィーグレー	物件名	寺本唯麻 様邸	案件No.	図面名	担当	図面	図番 : 株式会社 LIXIL
			A2510DDD0EW02L	レイアウト図	栗野 友仁		
	仕様	ES21	見積No.	縮尺	日付		
			M25109107270-007-2	1/30	2025.12.02		


A面

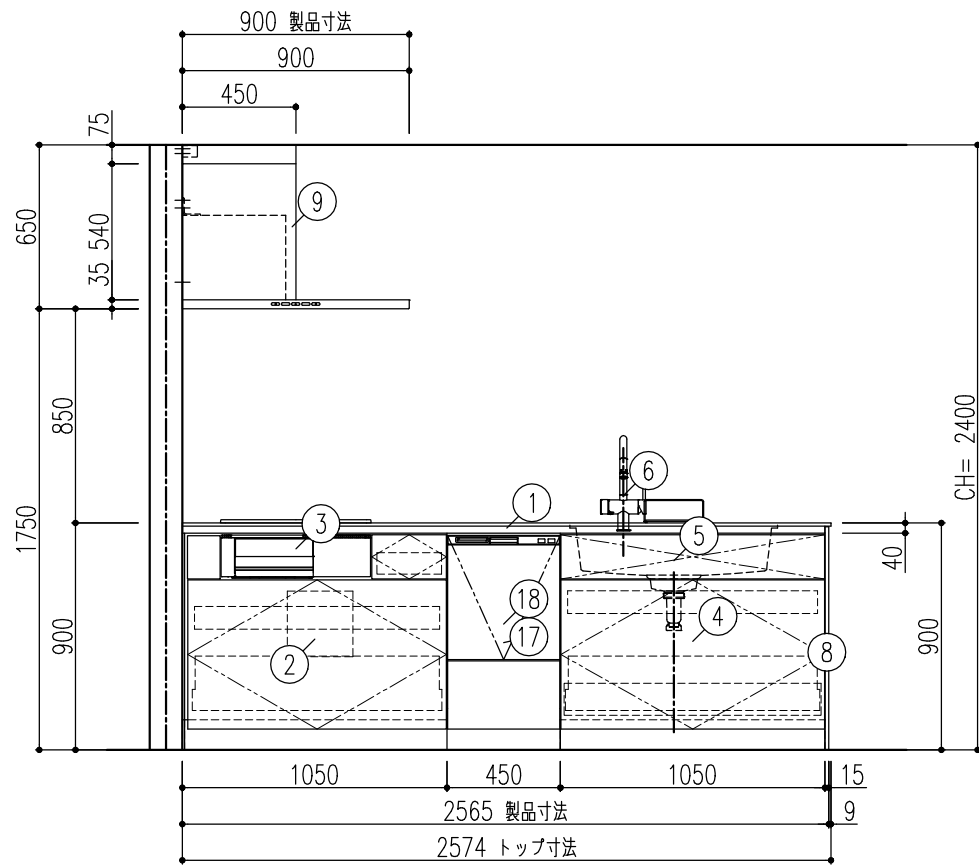


B面

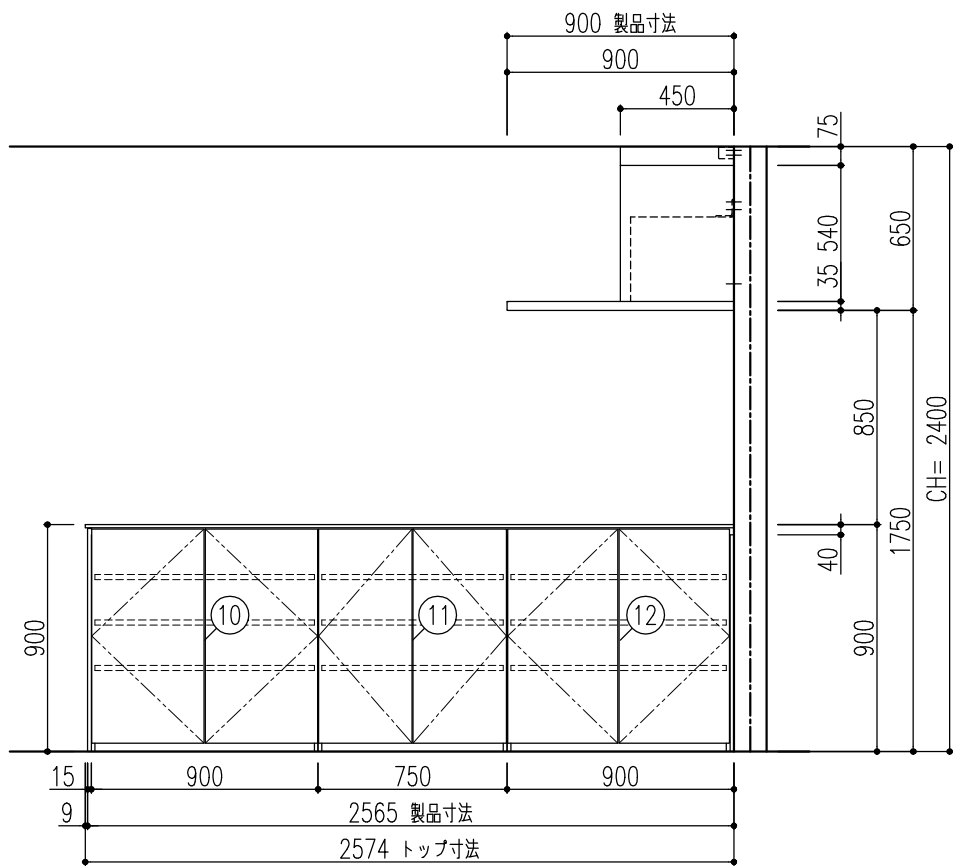

C面

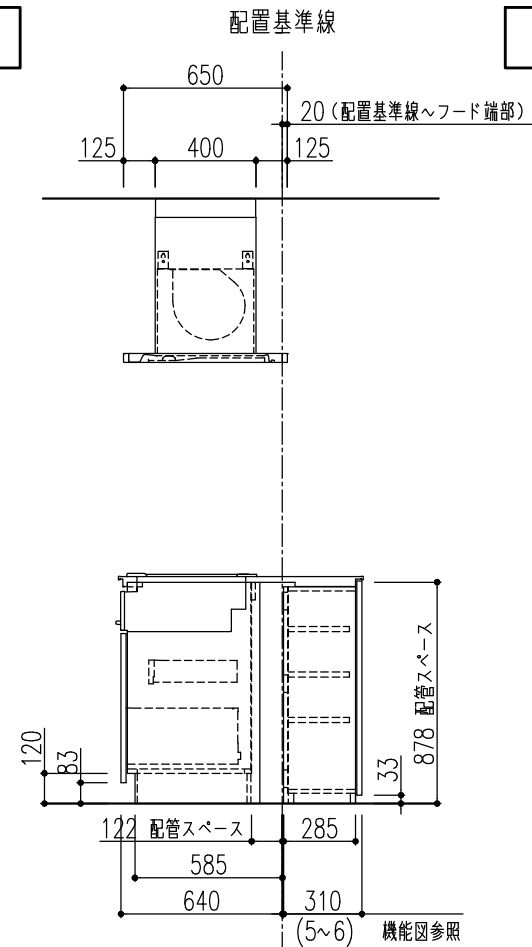


D面

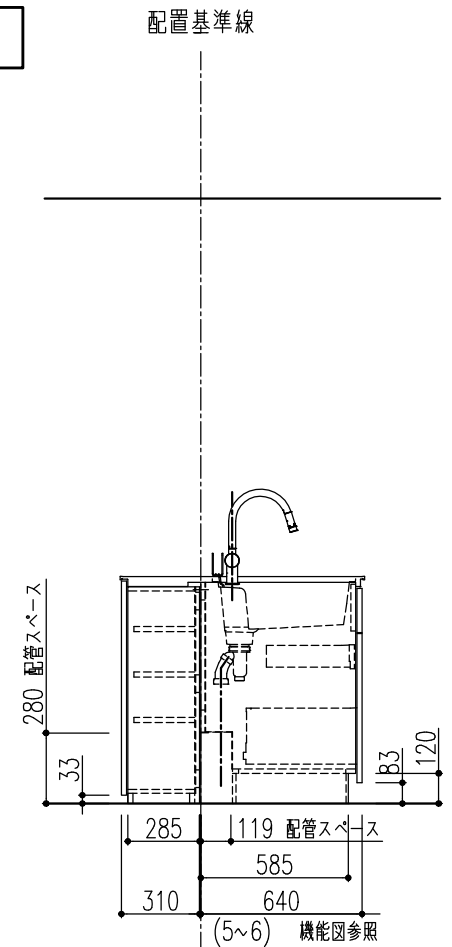


特記事項 扉色 VK5:グレージュスタック 取手 [M]スリム取手 (ブラック) ワークトップカラー 【LE】シルフィィグレー	物件名	寺本唯麻 様邸	案件No.	図面名	担当	図面	図番
			A2510DDDD0EW02L	レイアウト図	栗野 友仁		株式会社 LIXIL
	仕様	ES21	見積No.	縮尺	日付		
			M25109107270-007-2	1/30	2025.12.02		

A面

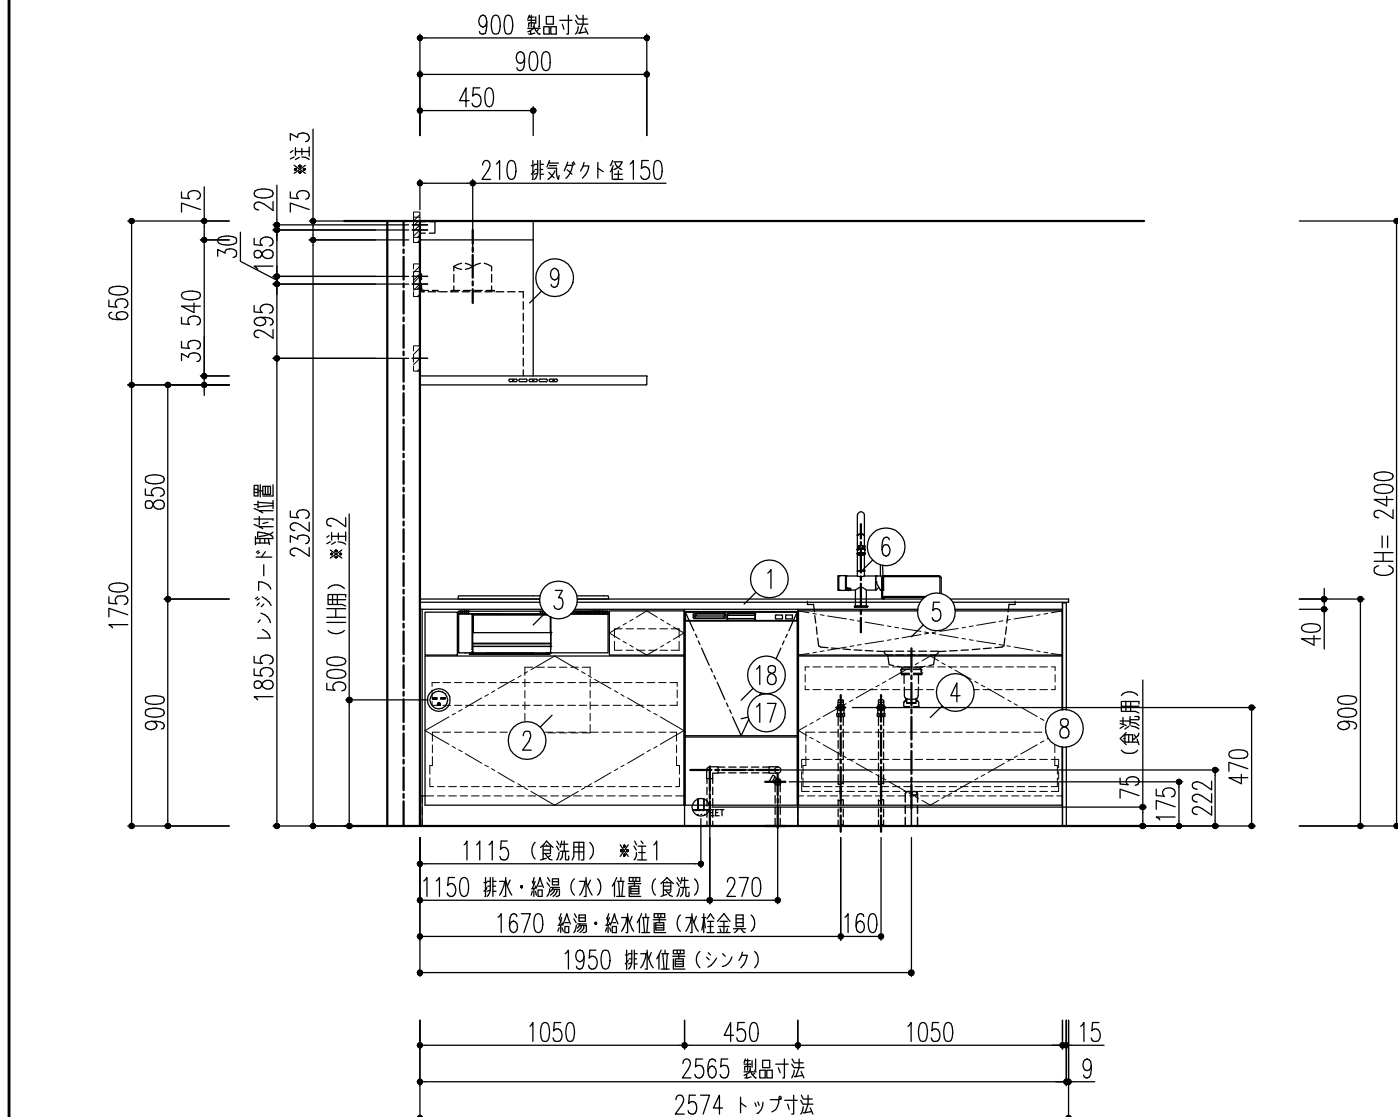

面

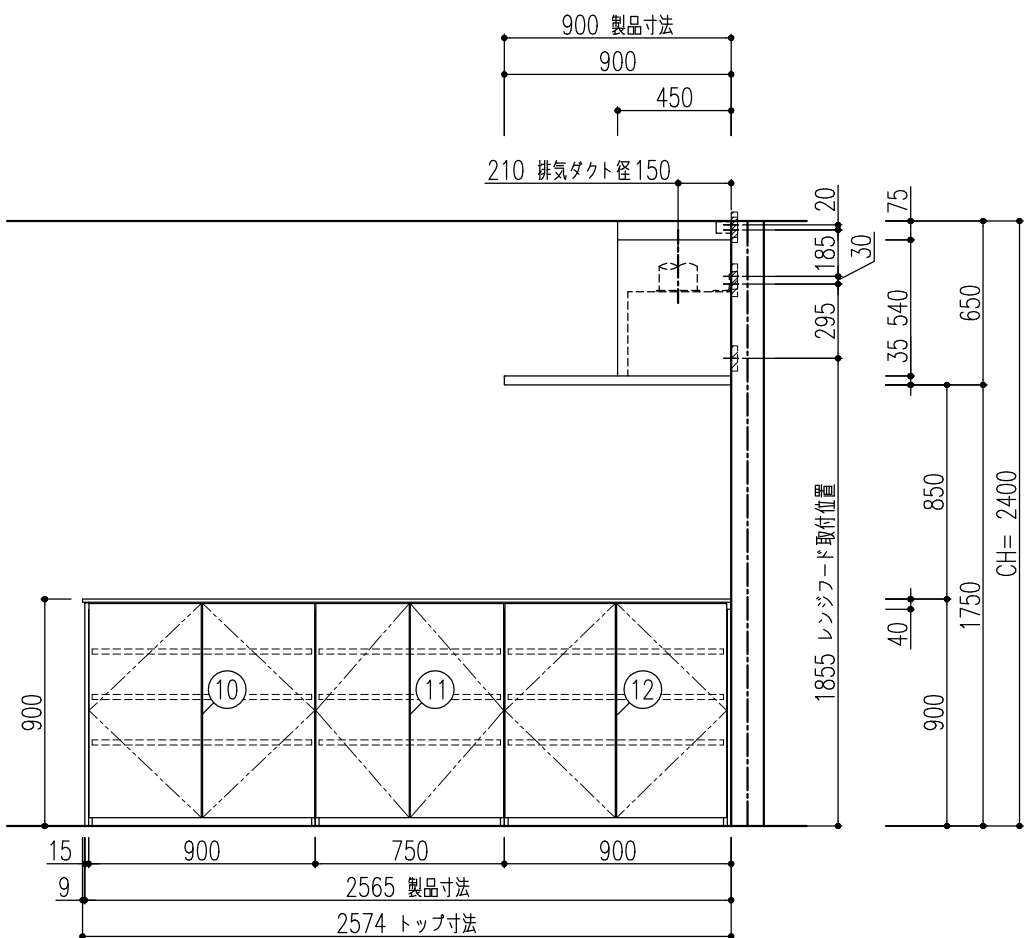


注1) 125V・15A 2極接地極付アースターミナル付コンセント 【専用】

注2) 250V・30A 2極接地極付コンセント(コンセントベース固定)【専用】


注3) レンジフード総高さ(600~900)の時 ダクトカバー範囲(25~325)

特記事項 扉色 VK5:グレージュスタッコ 取手 [M]スリム取手(ブラック) ワークトップカラー 【LE】シルフィングレー	物件名	寺本唯麻 様邸	案件No.	図面名	担当	図面	図番 : 株式会社 LIXIL
			A2510DDD0EW02L	納まり図	栗野 友仁		
	仕様	ES21	見積No.	縮尺	日付		
			M25109107270-007-2	1/30	2025.12.02		

C面

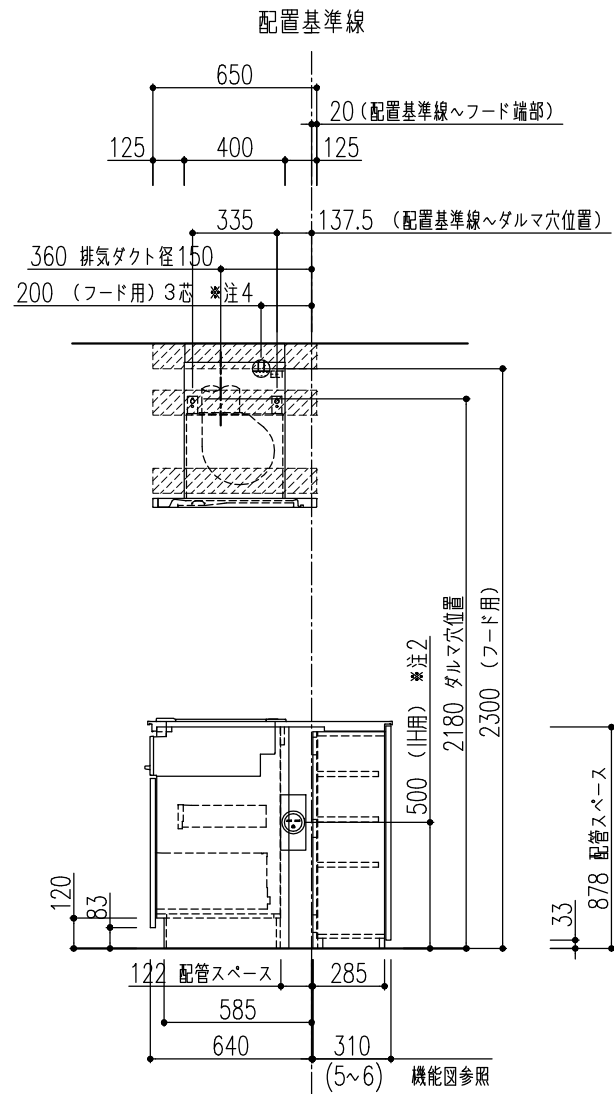


D面

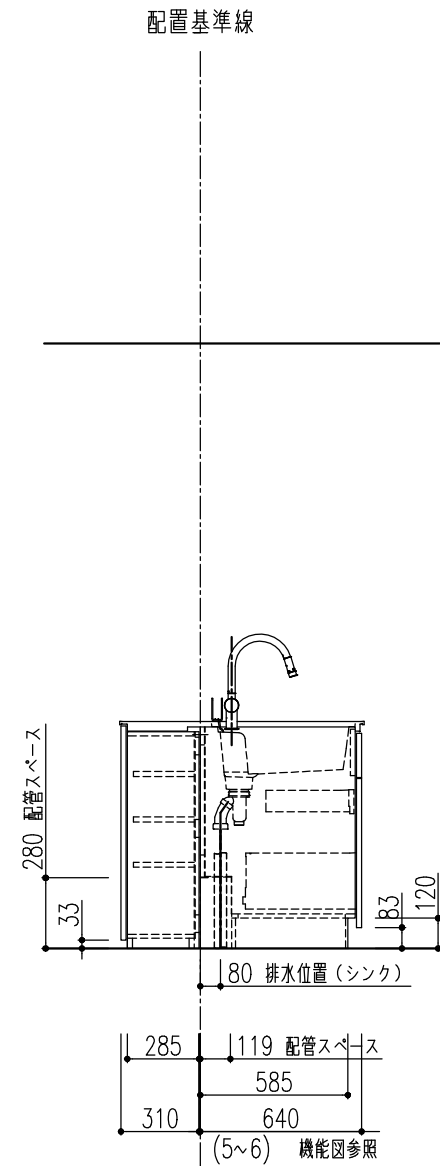

注2) 250V・30A 2極接地極付コンセント (コンセントベース固定) 【専用】
注4) 125V・15A 2極接地極付アースターミナル付コンセント 【専用】 (フード用)

特記事項 扉色 VK5:グレージュスタック 取手 [M]スリム取手 (ブラック) ワークトップカラー 【LE】シルフィークレー	物件名	寺本唯麻 様邸	案件No.	図面名	担当	図面	図番
	仕様	ES21	A2510DDDOEW02L	納まり図	栗野 友仁		株式会社 LIXIL
			見積No.	縮尺	日付		
			M25109107270-007-2	1/30	2025.12.02		




■ 床の不陸に関して

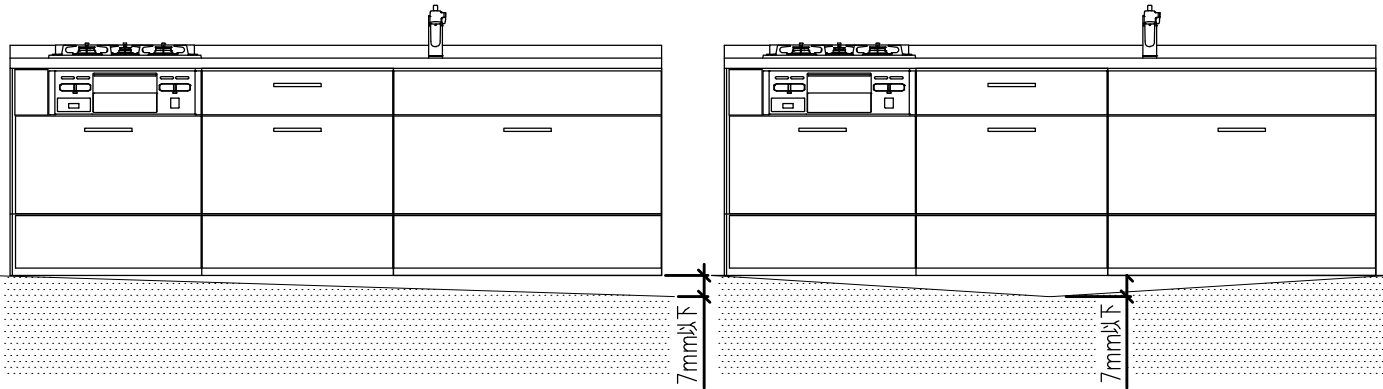

床の不陸は、7mm以下に抑えるようにしてください。不陸が大きい場合は、現場責任者に床の修正を依頼してください。
※キャビネット取付時には不陸調整スペーサー等で水平になるように設置してください。

■ 裏面キャビネット納まりについて

(キッチン側キャビネット背面) 配置基準▽

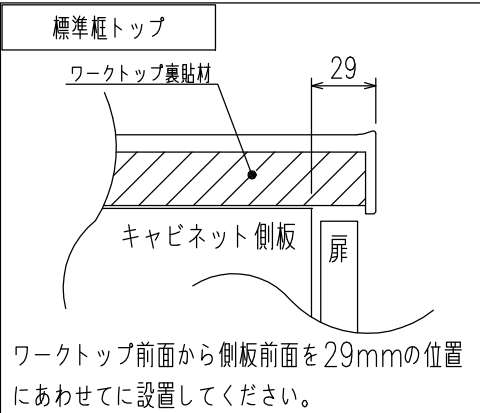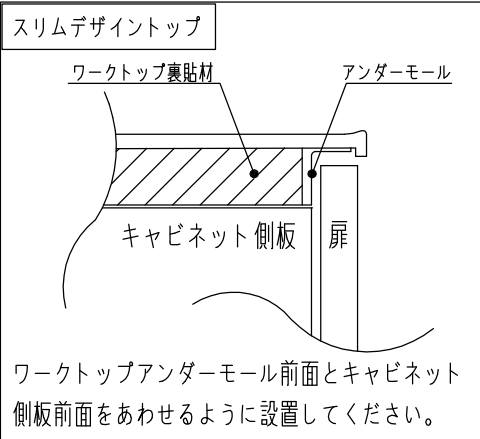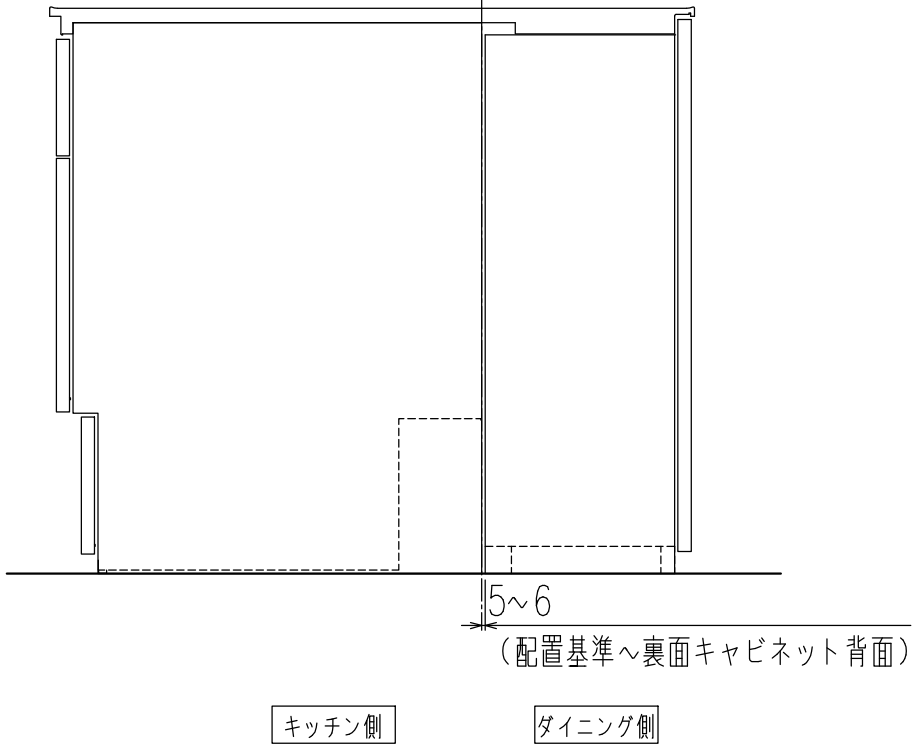

■ 食器洗い乾燥機内配管図 床立上げ配管例

※給水接続か給湯接続かお客様に確認したうえで施工願います。


給水 (給湯の場合は耐熱配管)

- ①アングル型止水栓 (ドライバー式)
- ②硬質塩化ビニルライニング鋼管相当品
- ③Rc1/2エルボ
- ④断熱材 (Φ48)

排水 (耐熱塩ビ使用のこと)

- ⑤排水パイプHT20相当品
- ⑥HT20エルボ

キッチン高さ	H825	H850	H875	H900
本体高さ	775	800	825	850
A	147	172	197	222
B	100	125	150	175

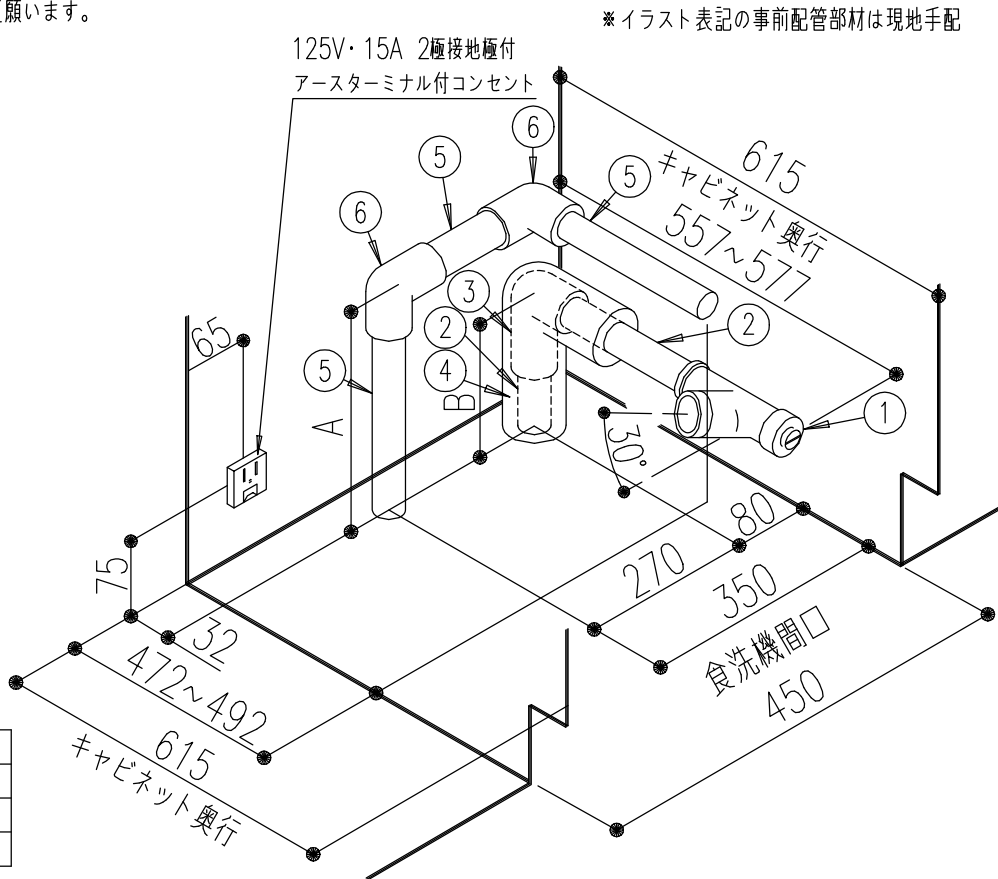


■ レンジフード取付注意事項 (壁面取付時)


レンジフードを取付ける場合は下地の材が厚み30mm以上、幅100mm以上、ビス固定位置が材の端部から25mm以上であることを確認してください。また、壁強度などの詳細は「レンジフード設置説明書」を必ず事前に確認してください。

取付位置については、取付設置図を確認してください。


参考図_CLS. SER. NST. ASR. ADR. RVJ. GSR. BFRS. TARシリーズ
(※RVJ. GSRシリーズの場合はレンジフードパネルの取付下地は不要です。)

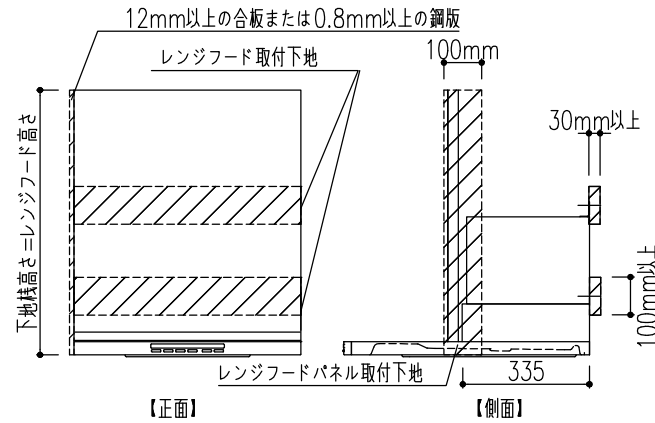

参考図_FED. HVR. NSDシリーズ (サイドマントルタイプ)

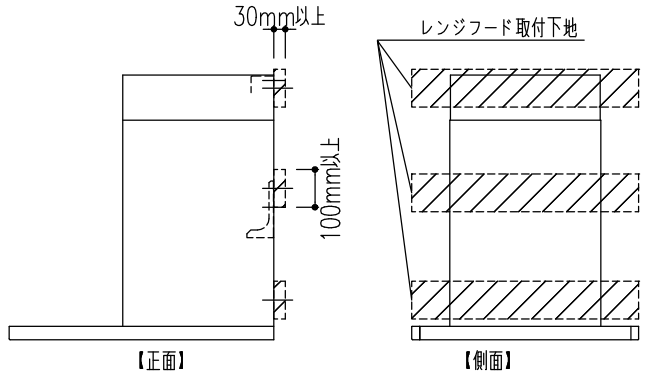

参考図_NBHシリーズ

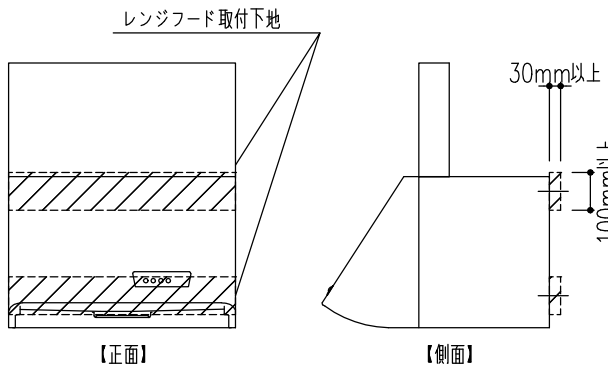


特記事項
扉色 VK5:グレージュスタック
取手 [M]スリム取手 (ブラック)
ワークトップカラー 【LE】シルフィィグレー

物件名 寺本唯麻 様邸
仕様 ES21

案件No. A2510DDDOEW02L
図面名 機能図
縮尺 日付 2025.12.02
担当 栗野 友仁
図番

株式会社 LIXIL

■ SMHVRフード

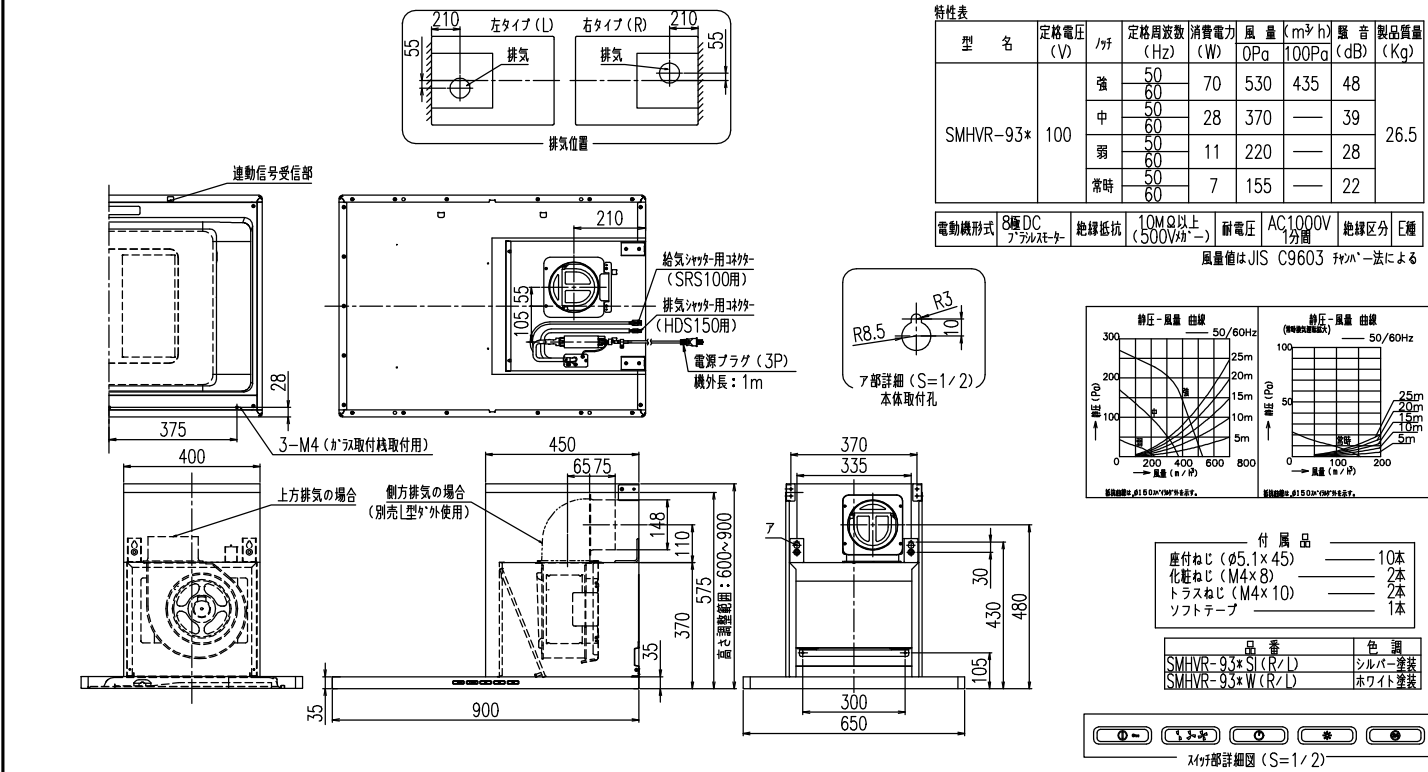


4. 製品名の末尾の () にはワザンリスによって記号が入る場合があります。
5. 電動シャッター (HDS150) (別売) を使用時は、中継コトを外して取り付けてください。
6. 赤外線連動型ソフトです。単独でも使用できます。
注) 1. 排気方向は側方 (L型) 外使用: 別売) と上方です。

■ IHヒーター用コンセント推奨位置図 / 側面設置の場合


※コンセントや電源プラグが、引き出しおよびIHヒーター用仕切板 (オプション) に接触しないように注意してください。
※木製キッチンの配管スペース付キャビネットは、キャビネット内にコンセントを取り付けるスペースがありませんので、別売のコンセントベース (W-SOCKET-B) などを使用して配管スペース内にコンセントを設置してください。

キッチン高さ	コンセント下端高さ	コンセントセンター高さ
800	355	400
850	405	450
900	455	500

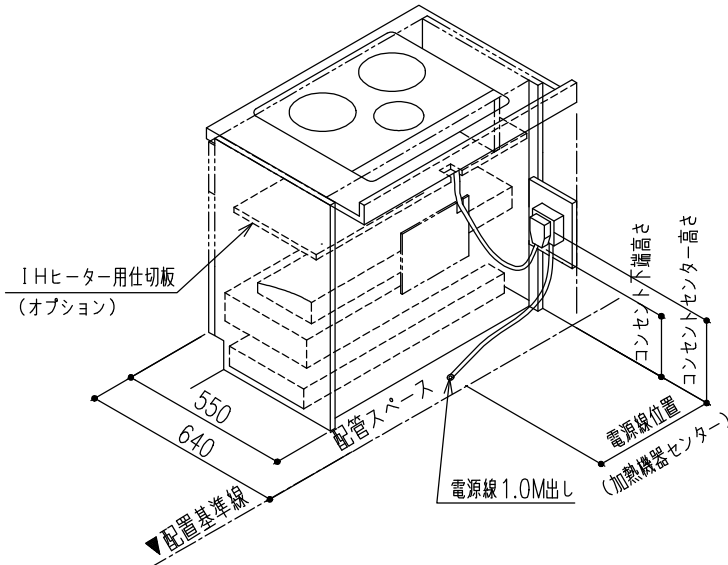

注意: 引き出しおよびIHヒーター用仕切板 (オプション) に接触しないように上記寸法を参照してください。

■ 止水栓図 (床立上げ)

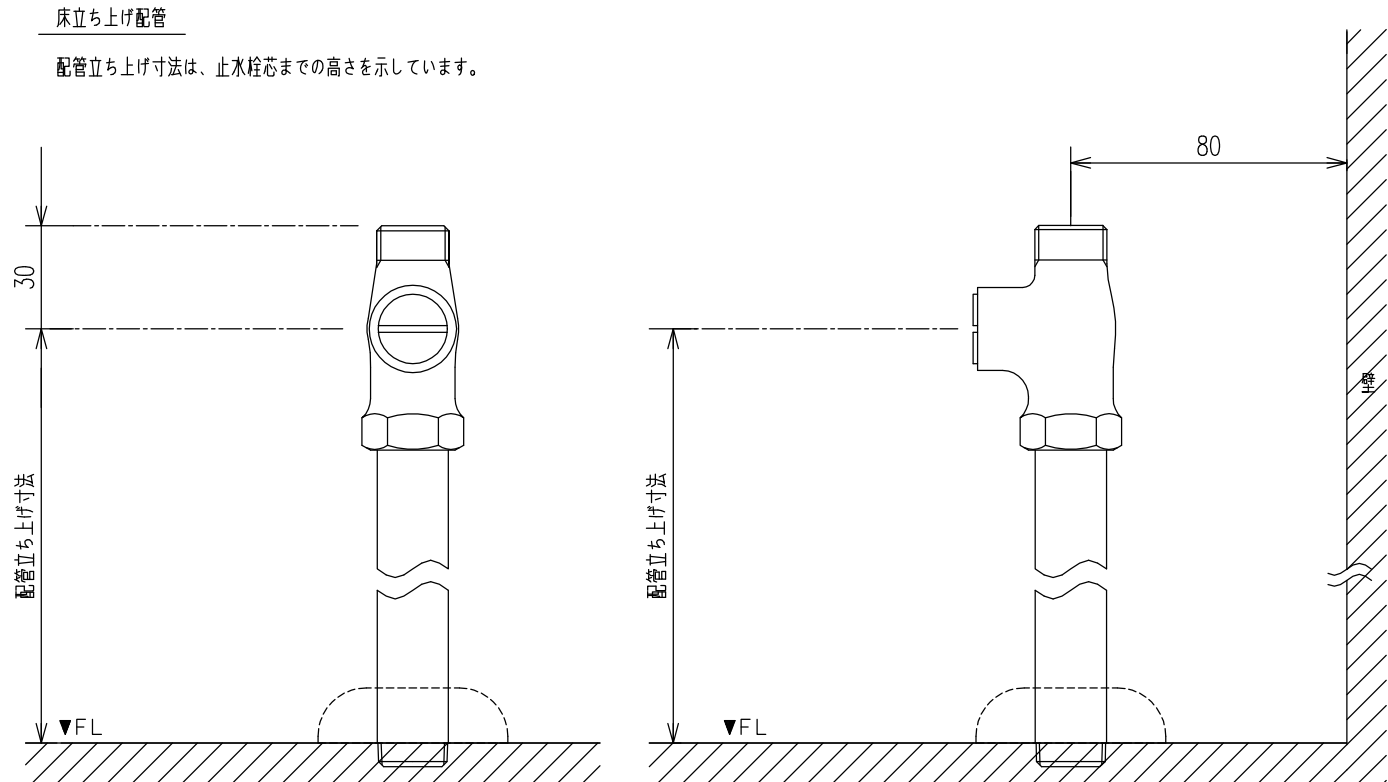

特記事項
扉色 VK5:グレージュスタック
取手 [M]スリム取手 (ブラック)
ワークトップカラー 【LE】シルフィィグレー

物件名
仕様

寺本唯麻 様邸

ES21

案件No.	図面名	担当	図面	図番
A2510DDDOEW02L	機能図	栗野 友仁		
見積No.	縮尺	日付		
M25109107270-007-2		2025.12.02		

株式会社 LIXIL

■ キッチン取付け者さま向け 動画コンテンツ ■
商品取付けの注意点を2次元コードでご視聴いただけます。
取付日より前に、是非ご確認ください。


1 ページ目


■ キッチン取付者さま向け 動画コンテンツ ■
商品取付けの注意点を2次元コードでご視聴いただけます。
取付日より前に、是非ご確認ください。


1 ページ目


■ キッチン取付者さま向け 動画コンテンツ ■
商品取付けの注意点を2次元コードでご視聴いただけます。
取付日より前に、是非ご確認ください。


1 ページ目


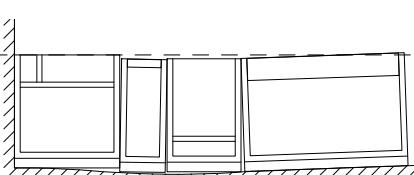
荷扱い・搬入 荷扱い・搬入  作成日：2024年10月01日	カウンター開梱搬入「養生ツール」 カウンター開梱搬入 「養生ツール」のご紹介  作成日：2024年10月01日	不陸の確認と調整   作成日：2024年02月07日	マグネットキッチンパネル マグネット キッチンパネル 「取付・設置」ポイント  作成日：2024年03月06日
--	---	--	---

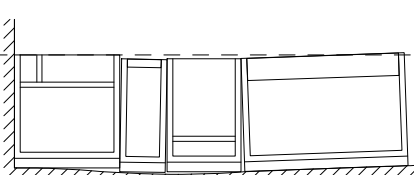
荷扱い・搬入 荷扱い・搬入  作成日：2024年10月01日	カウンター開梱搬入「養生ツール」 カウンター開梱搬入 「養生ツール」のご紹介  作成日：2024年10月01日	不陸の確認と調整   作成日：2024年02月07日	マグネットキッチンパネル マグネット キッチンパネル 「取付・設置」ポイント  作成日：2024年03月06日
--	---	--	---


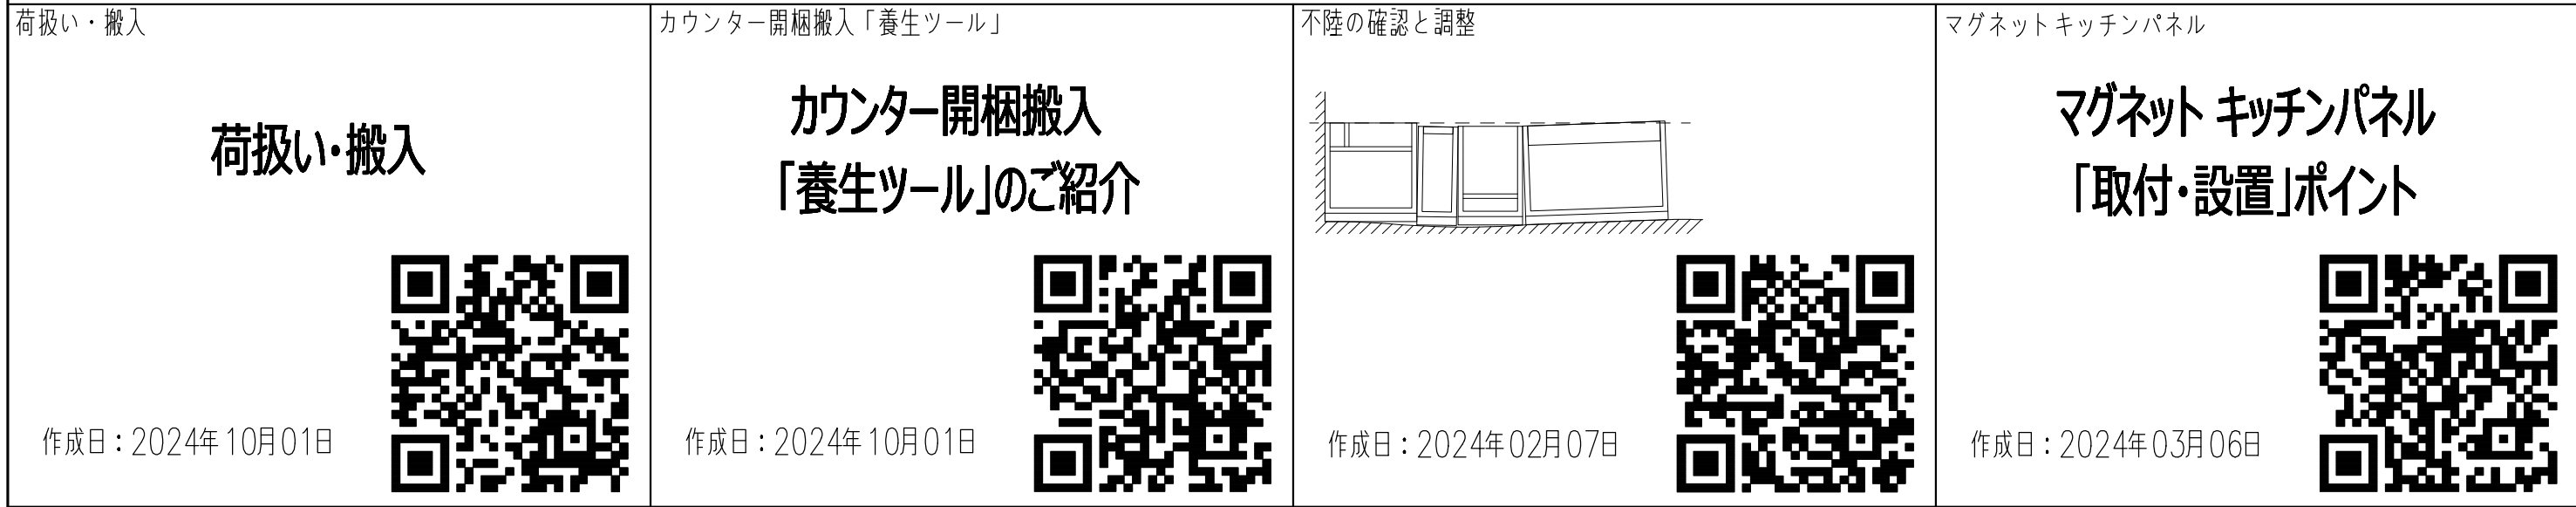


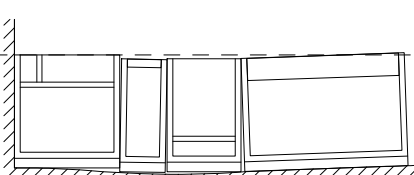
荷扱い・搬入 荷扱い・搬入  作成日：2024年10月01日	カウンター開梱搬入「養生ツール」 カウンター開梱搬入 「養生ツール」のご紹介  作成日：2024年10月01日	不陸の確認と調整   作成日：2024年02月07日	マグネットキッチンパネル マグネット キッチンパネル 「取付・設置」ポイント  作成日：2024年03月06日
--	---	--	---

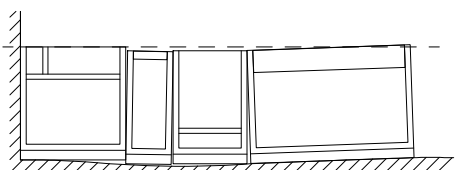カウンター開梱搬入「養生ツール」 カウンター開梱搬入 「養生ツール」のご紹介  作成日：2024年10月01日	不陸の確認と調整   作成日：2024年02月07日	マグネットキッチンパネル マグネット キッチンパネル 「取付・設置」ポイント  作成日：2024年03月06日
---	--	---

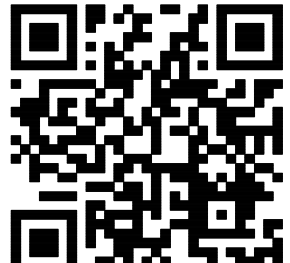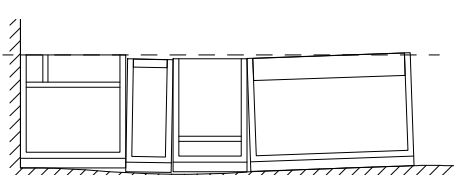
カウンター開梱搬入「養生ツール」 カウンター開梱搬入 「養生ツール」のご紹介  作成日：2024年10月01日	不陸の確認と調整   作成日：2024年02月07日	マグネットキッチンパネル マグネット キッチンパネル 「取付・設置」ポイント  作成日：2024年03月06日
---	--	---

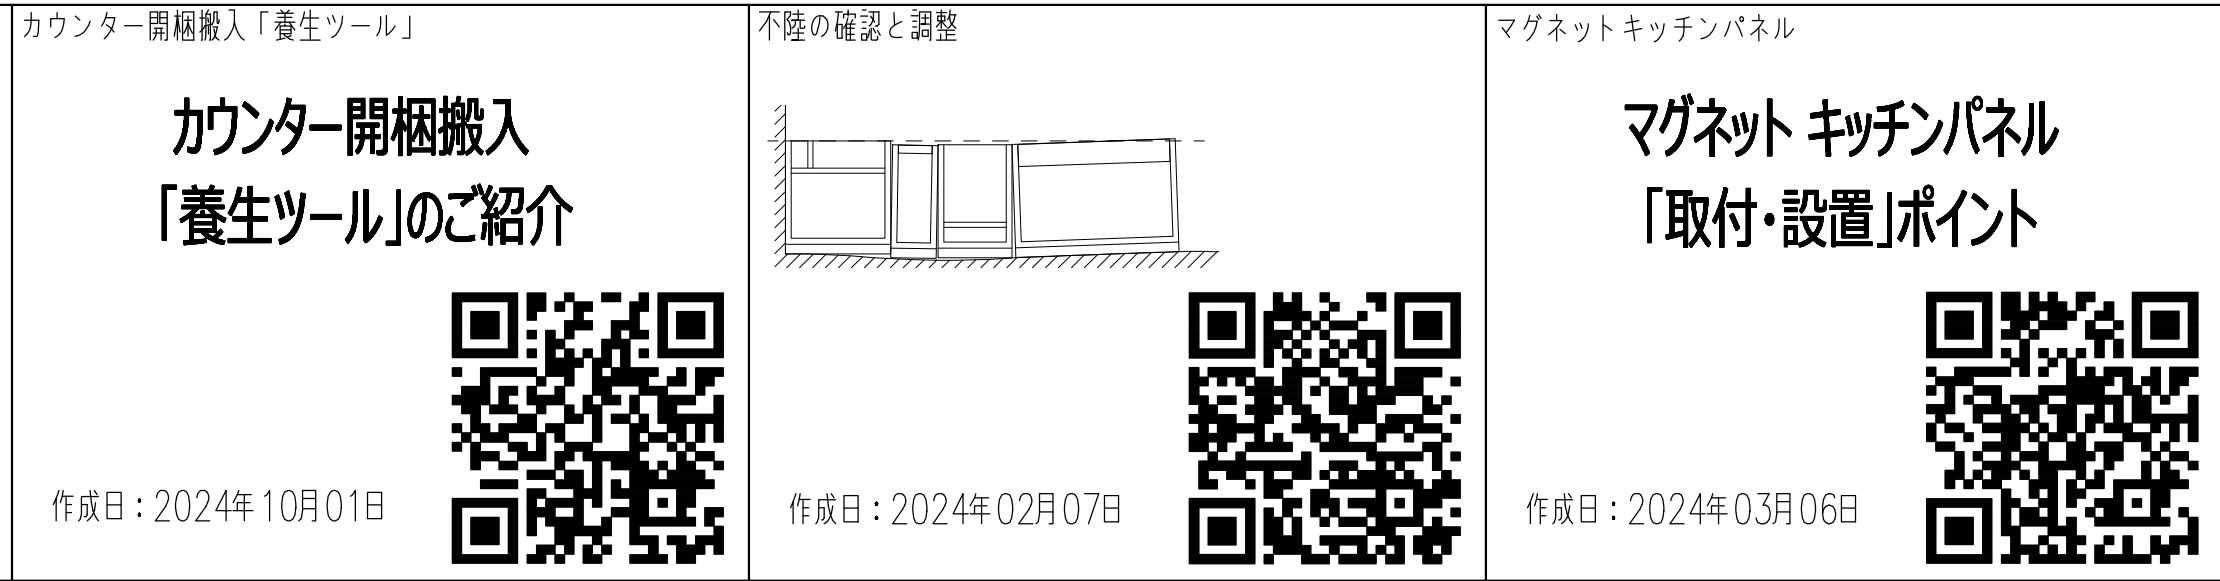

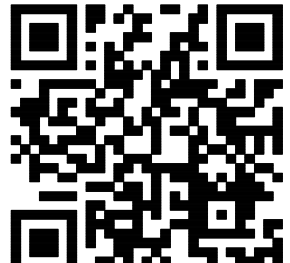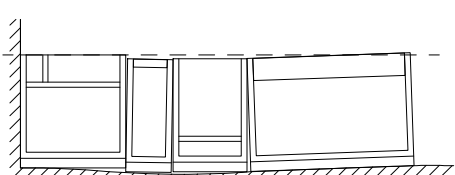カウンター開梱搬入「養生ツール」 カウンター開梱搬入 「養生ツール」のご紹介  作成日：2024年10月01日	不陸の確認と調整   作成日：2024年02月07日	マグネットキッチンパネル マグネット キッチンパネル 「取付・設置」ポイント  作成日：2024年03月06日
---	--	---

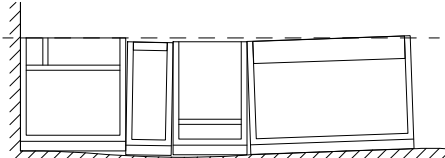不陸の確認と調整  作成日：2024年02月07日 	マグネットキッチンパネル マグネット キッチンパネル 「取付・設置」ポイント  作成日：2024年03月06日
--	---

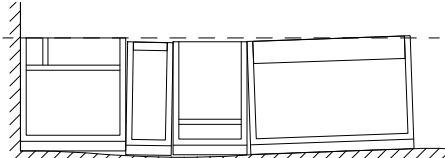

不陸の確認と調整  作成日：2024年02月07日 	マグネットキッチンパネル マグネット キッチンパネル 「取付・設置」ポイント  作成日：2024年03月06日
--	---

マグネット キッチンパネル

マグネット キッチンパネル 「取付・設置」ポイント



作成日：2024年03月06日

マグネット キッチンパネル

マグネット キッチンパネル 「取付・設置」ポイント



作成日：2024年03月06日






マグネット キッチンパネル



マグネット キッチンパネル 「取付・設置」ポイント





作成日：2024年03月06日

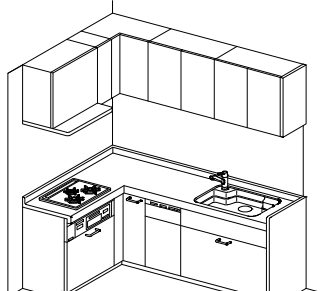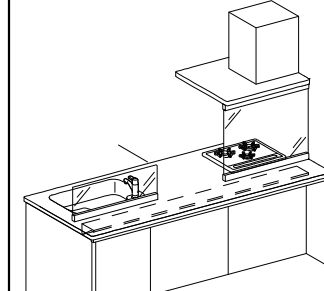人造大理石カウンターL型キッチン   作成日：2024年02月07日	センターキッチン（ペニンシュラ型）   作成日：2024年02月07日		
---	---	--	--

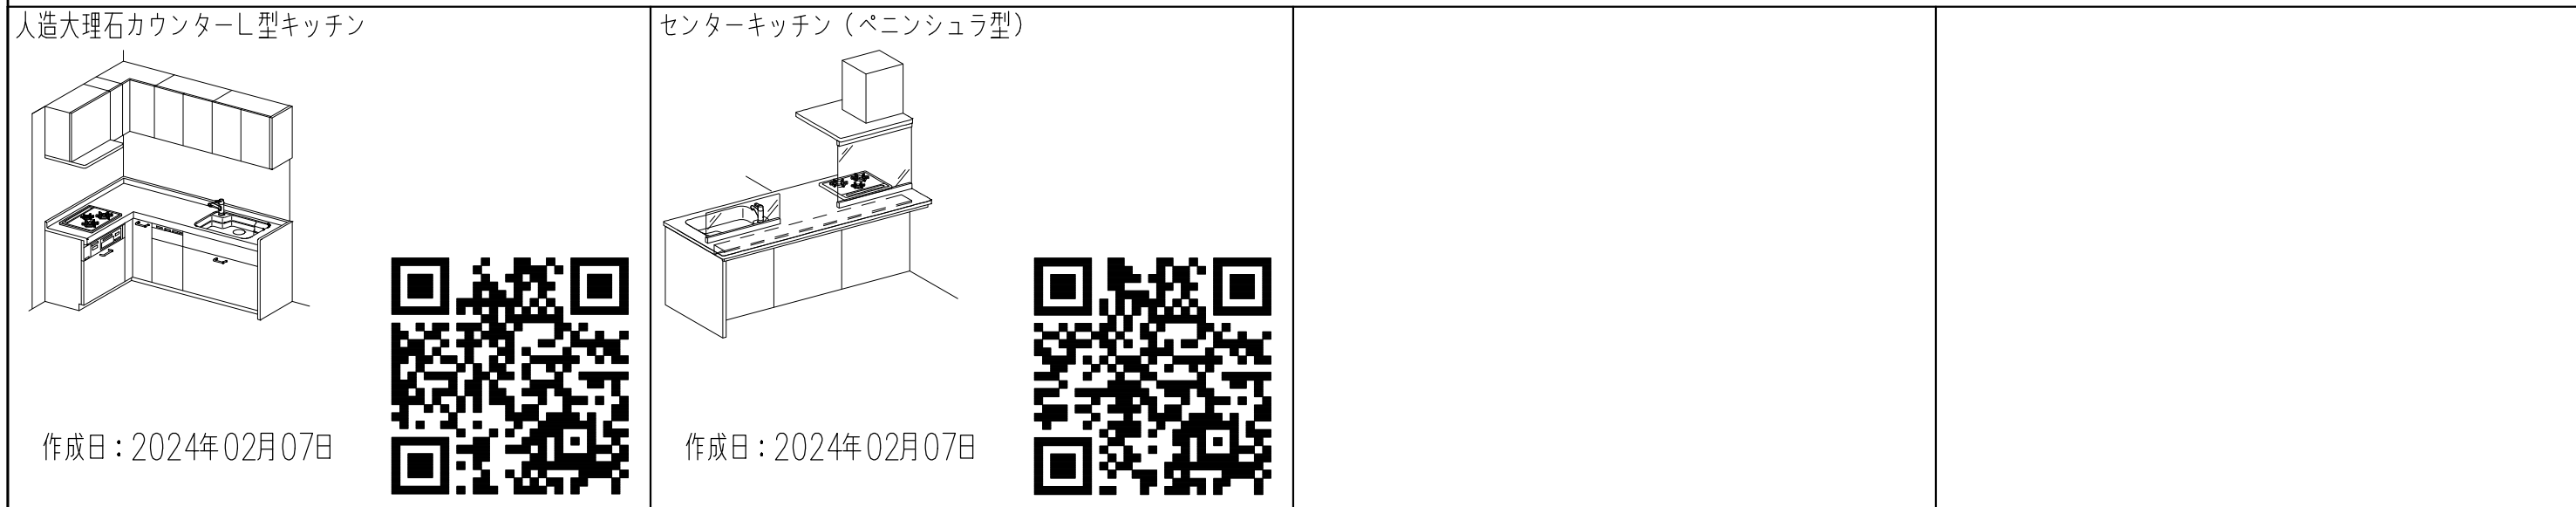


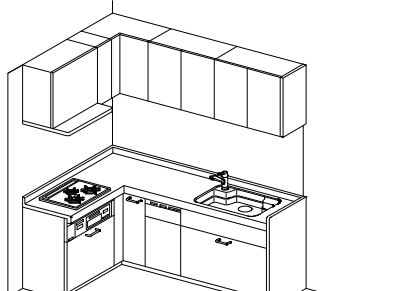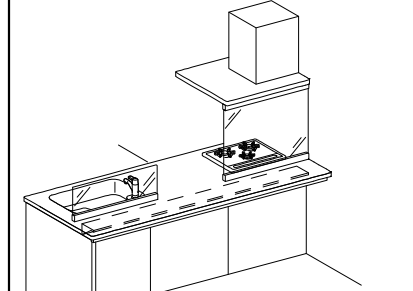人造大理石カウンターL型キッチン   作成日：2024年02月07日	センターキッチン（ペニンシュラ型）   作成日：2024年02月07日		
---	---	--	--

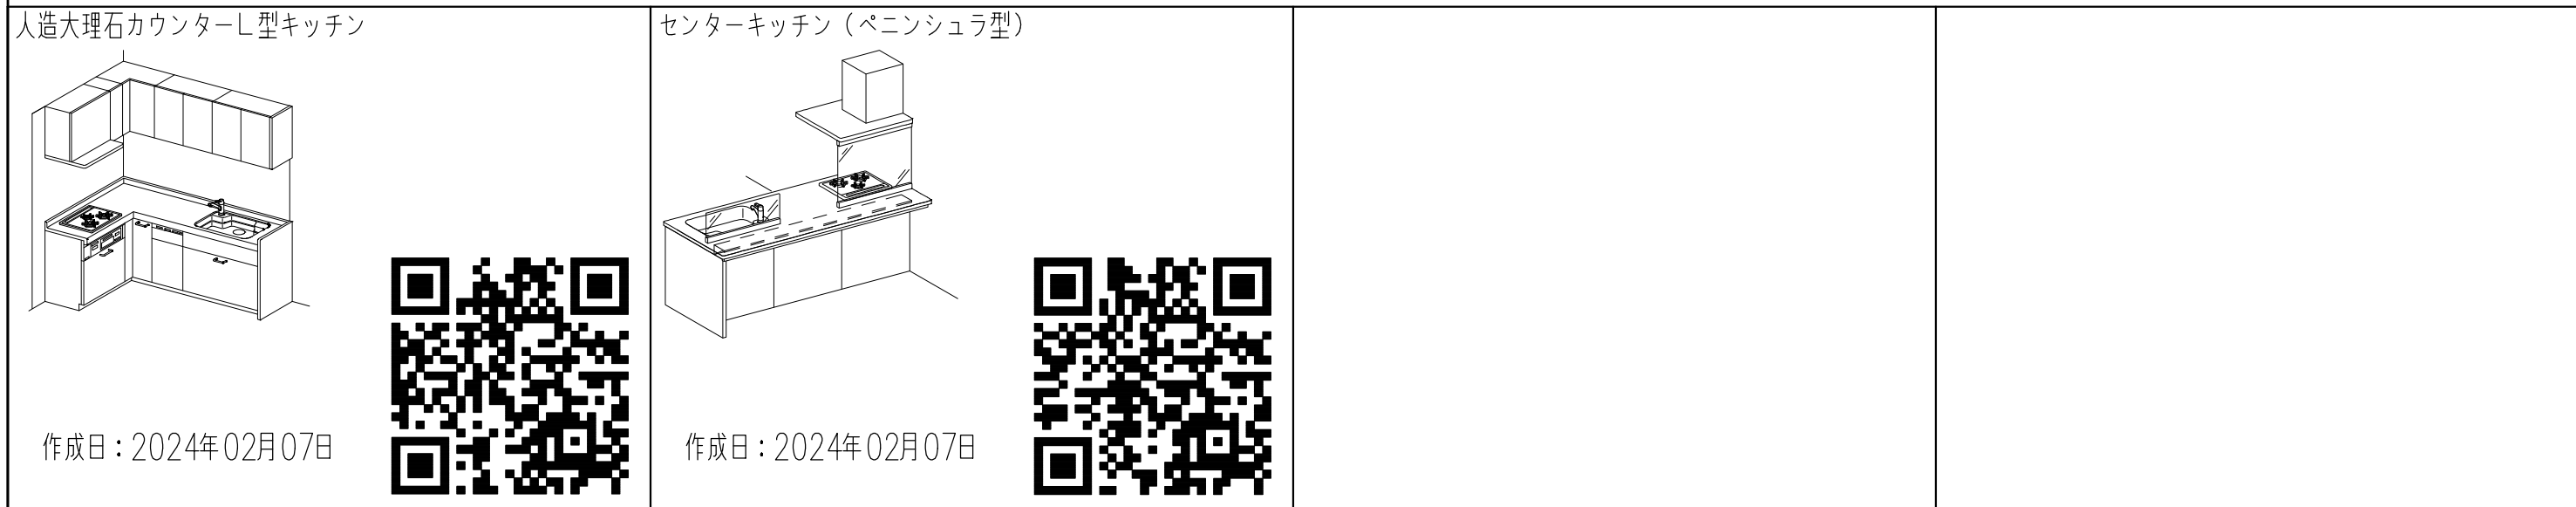

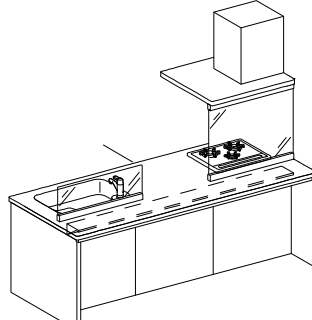センターキッチン（ペニンシュラ型）  作成日：2024年02月07日		
---	---	--





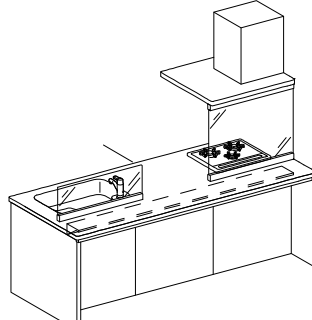


センターキッチン（ペニンシュラ型）  作成日：2024年02月07日		
---	---	--

		特記事項 扉色 VK5:グレージュスタック 取手 [M]スリム取手 (ブラック) ワークトップカラー 【LE】シルフィーグレー	物件名	寺本唯麻 様邸		案件No.	図面名	担当	図面	図番 :
			仕様	E S 2 1	A2510DDD0EW02L	機能図	栗野 友仁		株式会社 LIXIL	
					見積No.	縮尺	日付			
					M25109107270-007-2		2025.12.02			

■ キッチン取付者さま向け 動画コンテンツ ■

商品取付けの注意点を2次元コードでご視聴いただけます。
取付日より前に、是非ご確認ください。

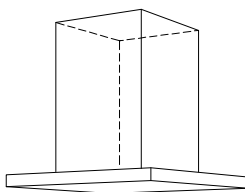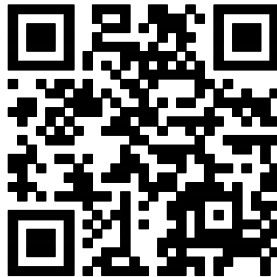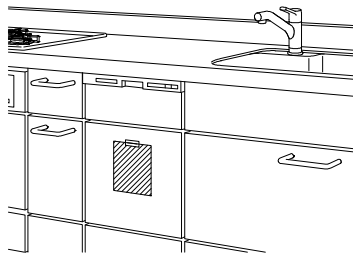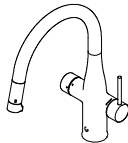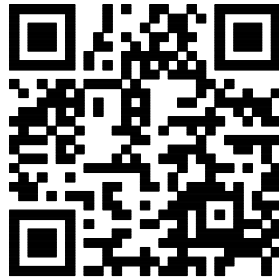センターフード型レンジフード (天吊りフード)  作成日：2024年06月03日 		I H加熱機器関連 I H加熱機器 仕切り板 作成日：2024年02月07日 		食器洗い乾燥機  作成日：2024年02月07日 		ミネラル浄水栓 Greentap  作成日：2024年06月03日 	
	特記事項 扉色 VK5:グレージュスタック 取手 [M]スリム取手 (ブラック) ワークトップカラー 【LE】シルフィーグレー	物件名 寺本唯麻 様邸 仕様 ES21	案件No.	図面名	担当	図面	図番
			A2510DDD0EW02L	機能図	栗野 友仁		株式会社 LIXIL
			見積No.	縮尺	日付		
			M25109107270-007-2		2025.12.02		