


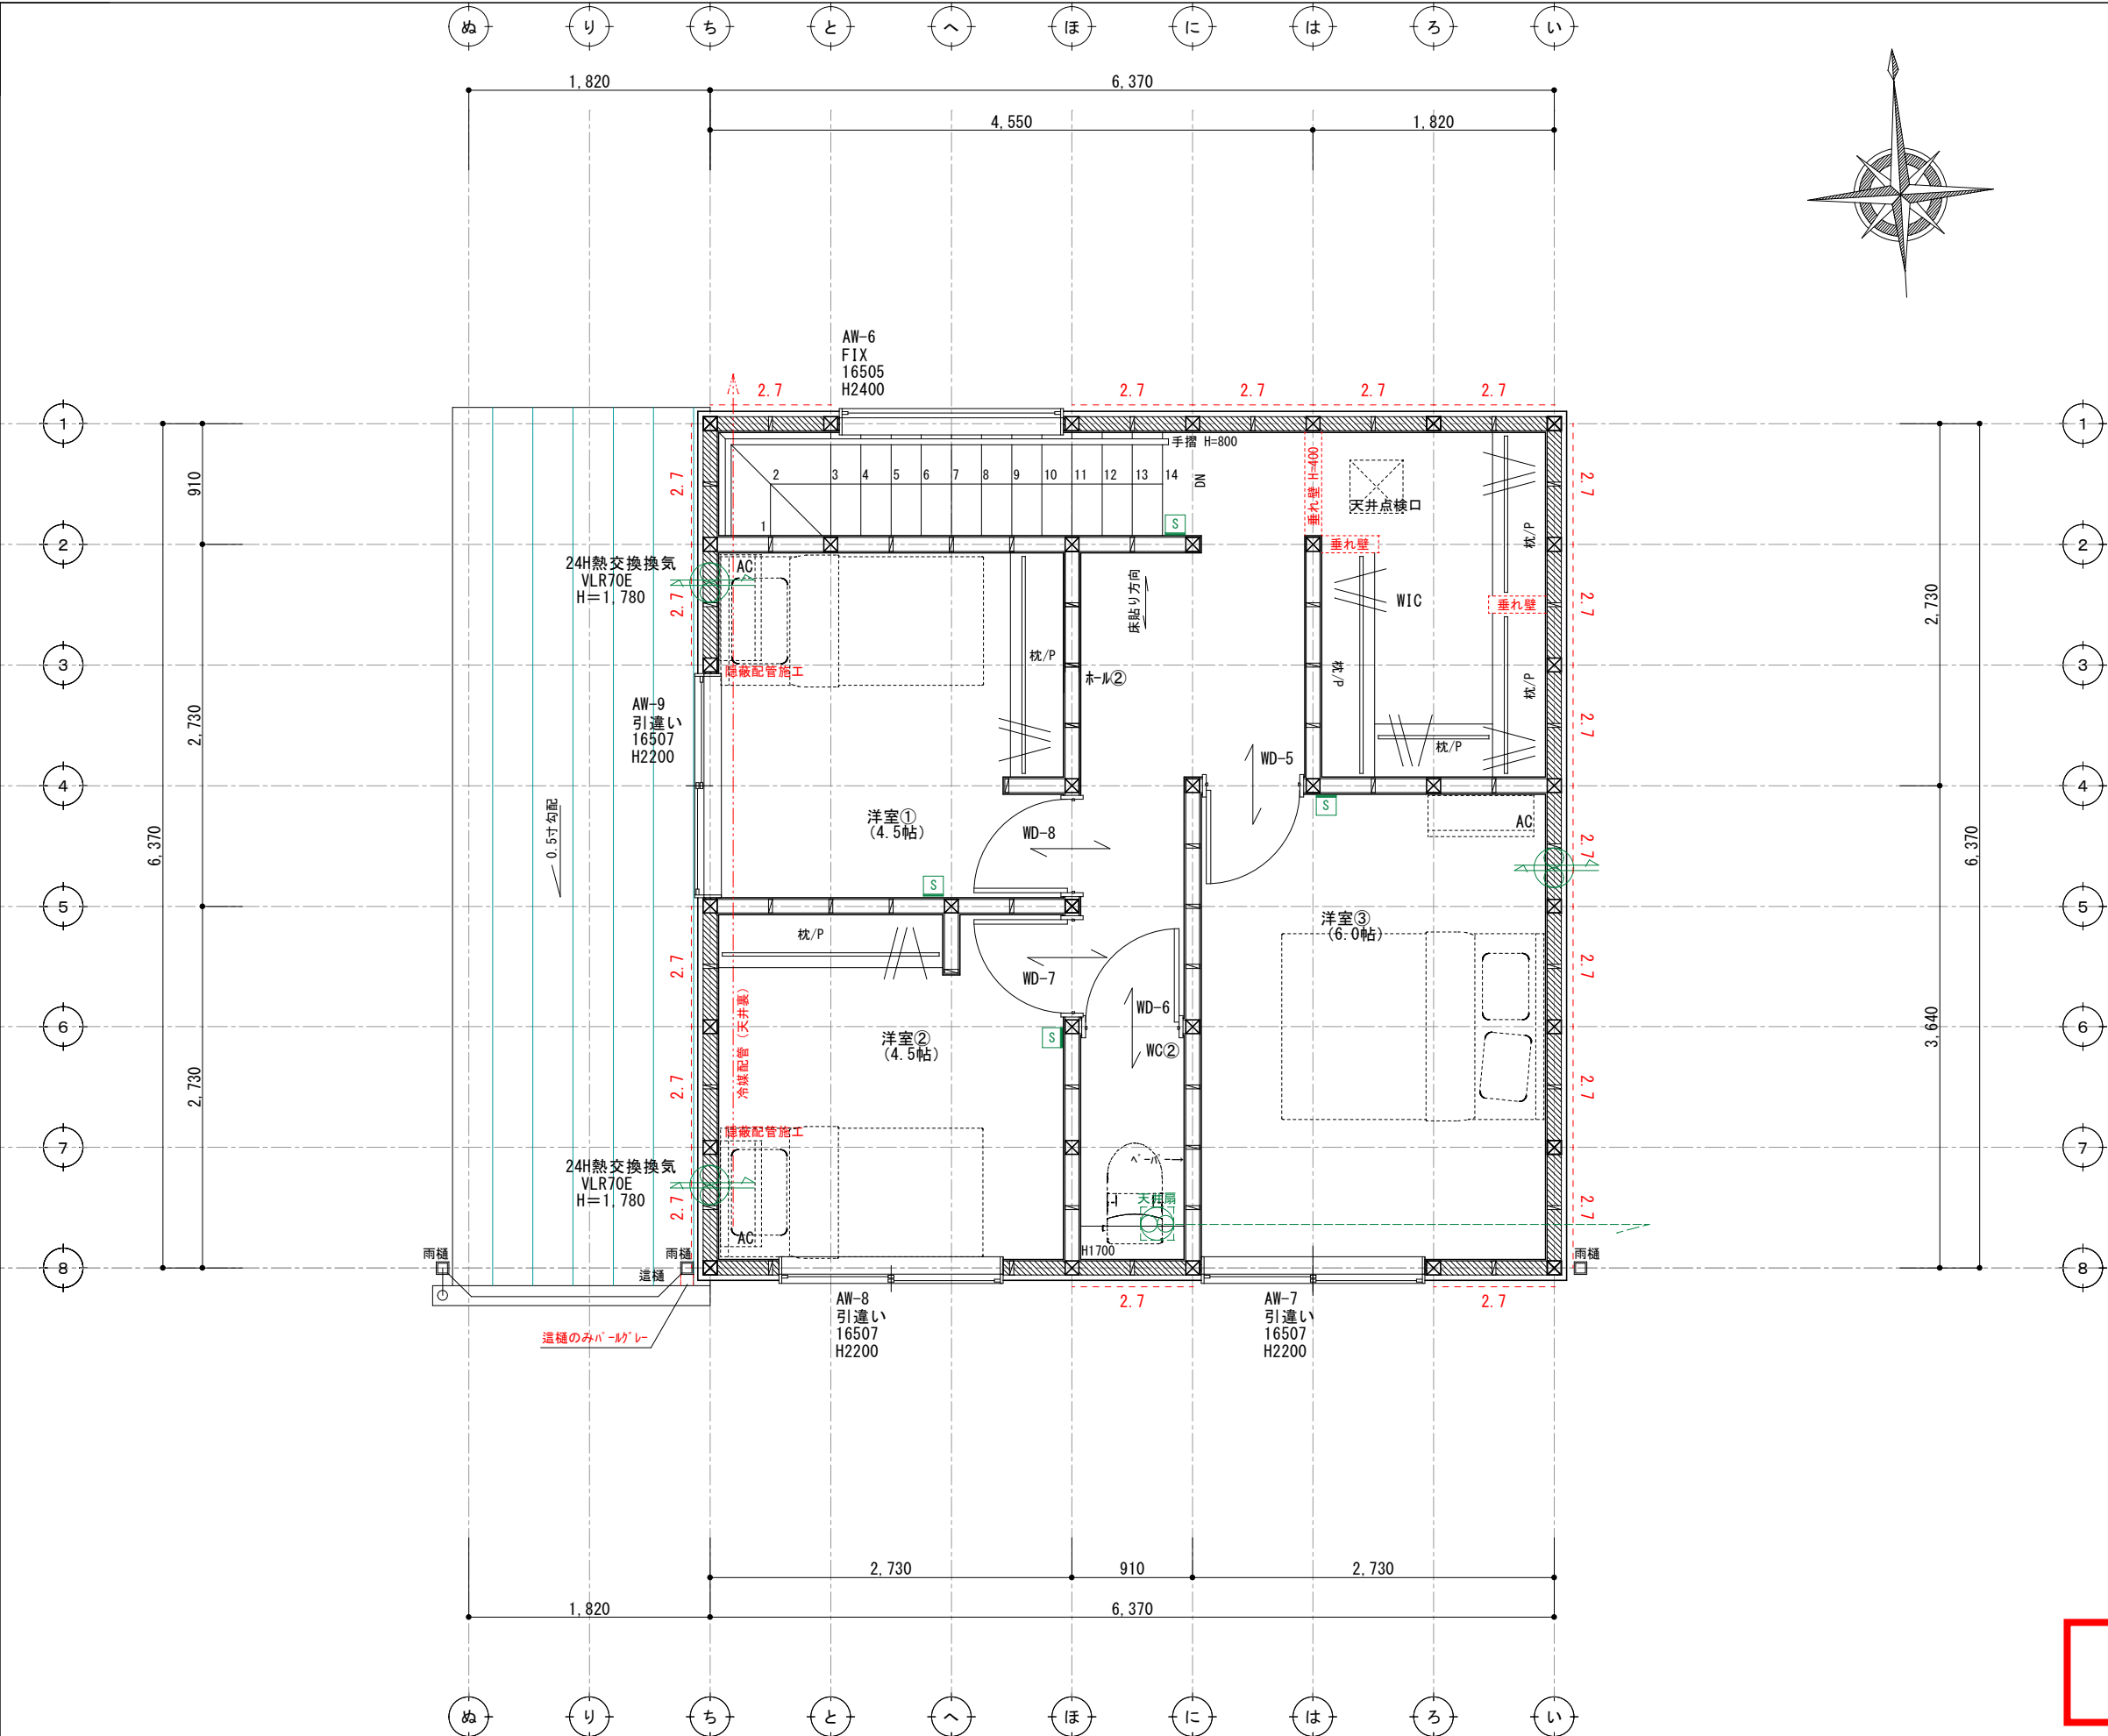

G2

| 壁付け 住宅用火災報知器 |      |          | 数量 |
|--------------|------|----------|----|
| H            | 熱感知器 | 電池式(単独型) |    |
|              | 露出型  |          |    |
| 壁付け 住宅用火災報知器 |      |          | 数量 |
| S            | 煙感知器 | 電池式(単独型) | 4  |
|              | 露出型  |          |    |

- ※ 煙感知器は壁・梁より600mm以上離す壁に取付ける場合、天井から150mm以上500mm以内離す換気扇・エアコン吹出口から1500mm以上離す
- ※ 全室LED照明とする。
- ※ 標準天井高さ2,400
- ※ 特記無きガラスは型ガラス

**\* 凡例**

- 管柱 (105×105)
- Kダクト (3.30倍 FRM-0641)
- 片筋違い (2.00倍 45×90) (例 左:柱脚 右:柱頭)
- たすき掛筋違い (4.00倍 45×90)
- 構造用合板 (2.70倍) (t=9 9材 EXハイバ)
- 床点検口
- 天井点検口
- 換気扇
- 熱交換換気扇VLR-70

- ※ 全室LED照明とし、調光制御を採用する。
- ※ 非居室の照明は人感センサーを採用する。

| アドバンスシリーズ                                                                             |     |                  |
|---------------------------------------------------------------------------------------|-----|------------------|
| スマートデザイン (外部)                                                                         |     |                  |
| 凡例                                                                                    |     |                  |
|  | 1   | コンセント 1ヶ所        |
|  | 2   | コンセント 2ヶ所        |
|  | 3   | コンセント 3ヶ所        |
|  | 1ET | コンセント1ヶ所接地ターミナル付 |
|  | 2ET | コンセント2ヶ所接地ターミナル付 |
|  | WP  | コンセント 防水型        |
|  |     | エアコン用コンセント       |
|  |     | 200V用コンセント       |
|  | WP  | 防雨入線プレート         |
|  |     | スイッチ             |
|  | 3   | 3路スイッチ           |
|  | 4   | 4路スイッチ           |
|  |     | 直結電源             |
|  | TV  | テレビ取出口           |
|  | TEL | 電話取出口 (テレホンガイド)  |
|  | LAN | LAN取出口 (テレホンガイド) |
|  |     | 壁照明              |
|  |     | リモコン (給湯関係・ルフロ)  |
|  |     | メーター             |
|  |     | 分電盤              |
|  |     | チャイム             |

- ※ACコンセント天井付け
- ※TVアンテナ工事
- ※スイッチはFL+1100、コンセントはFL+200

決定図