




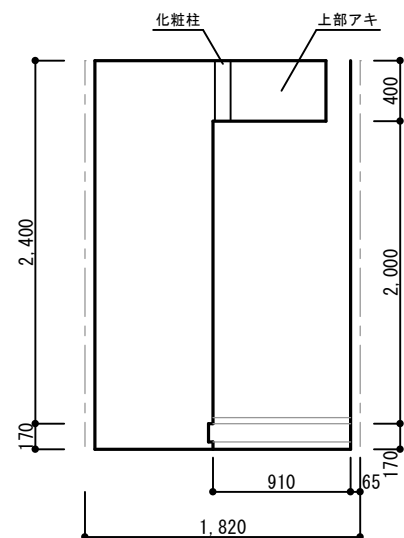


玄関 東面

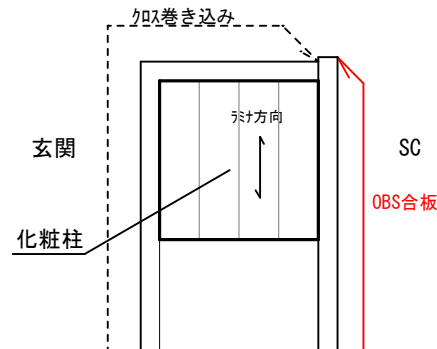


玄関 SC 腰壁出隅 収まり

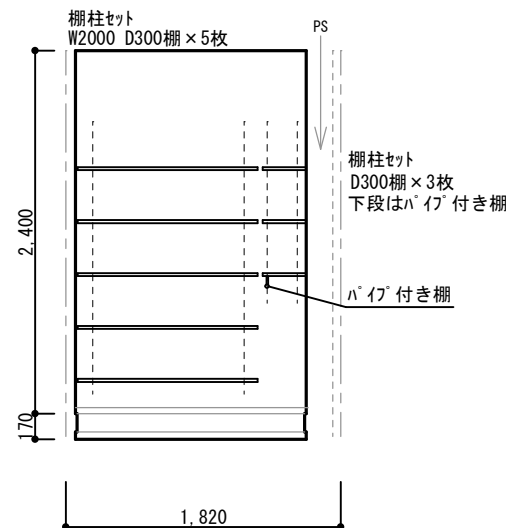


SC 東面

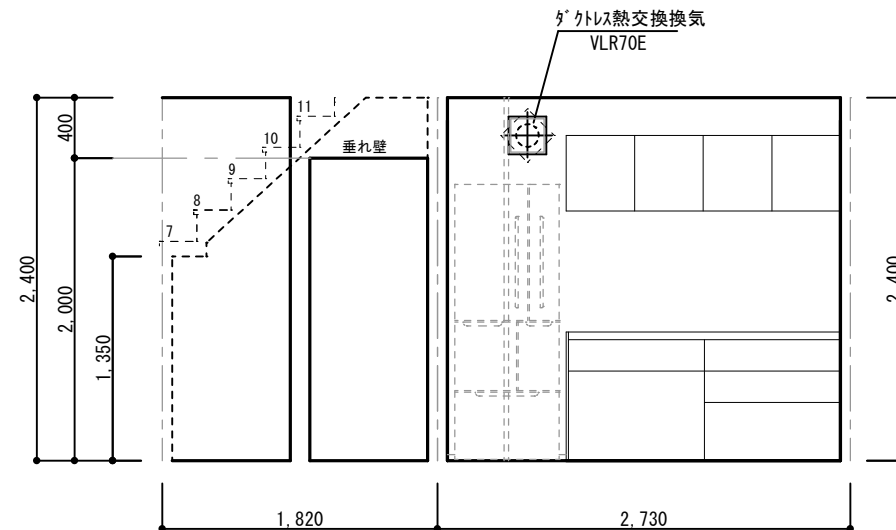


LDK 北面

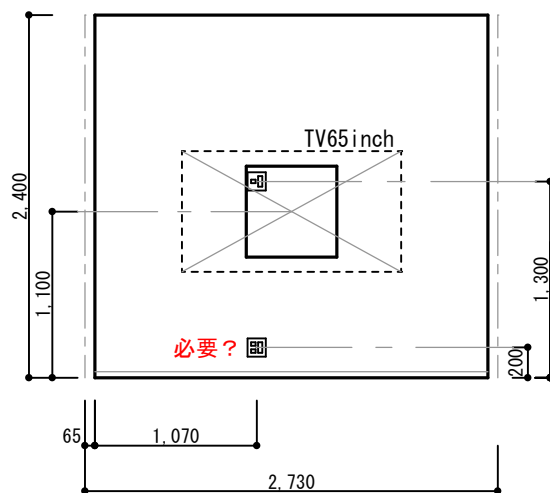


LDK 西面

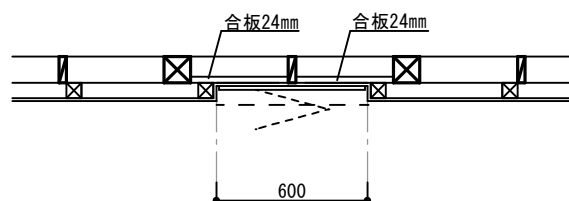

壁掛けTVブラケット用ニッチ 断面図 (1/30)

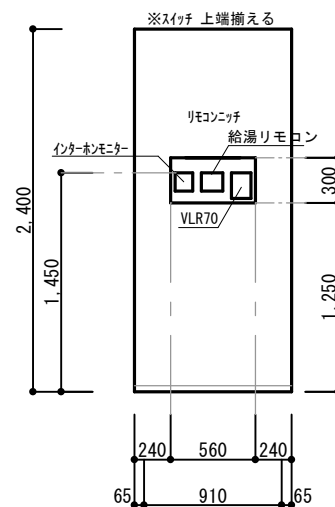

玄関 東面

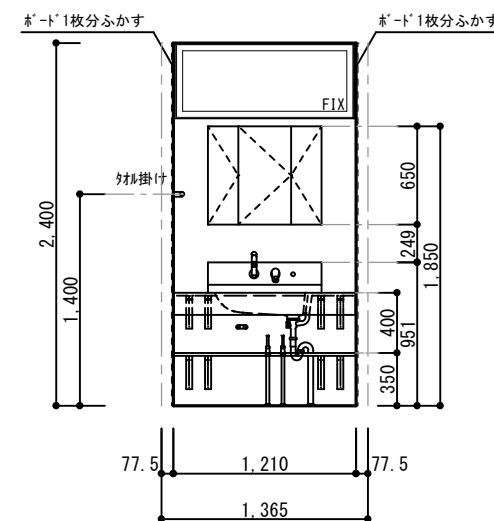

洗面所 西面

決定図

訂正	浜岡一級総合設計事務所 一級建築士事務所 静岡県知事登録第 (10)2441 号 一級建築士 大庄登録第 365879 号 西原利昌	LIFEFUND PG HOUSE	株式会社 LIFEFUND InDesign office 一級建築士事務所 事務所登録 (2) 第7595号 一級建築士登録 第179770号 鈴木 達男 〒432-8023 静岡県浜松市中央区鶴江3丁目70番23号	年月日 2026.1.4 縮尺 1/50	件名 寺本唯麻様 新築工事 図名 展開図-1		設計 酒井	IC	工事 青島	図番 6-1
----	--	----------------------	---	-------------------------------	---------------------------------	--	----------	----	----------	-----------