



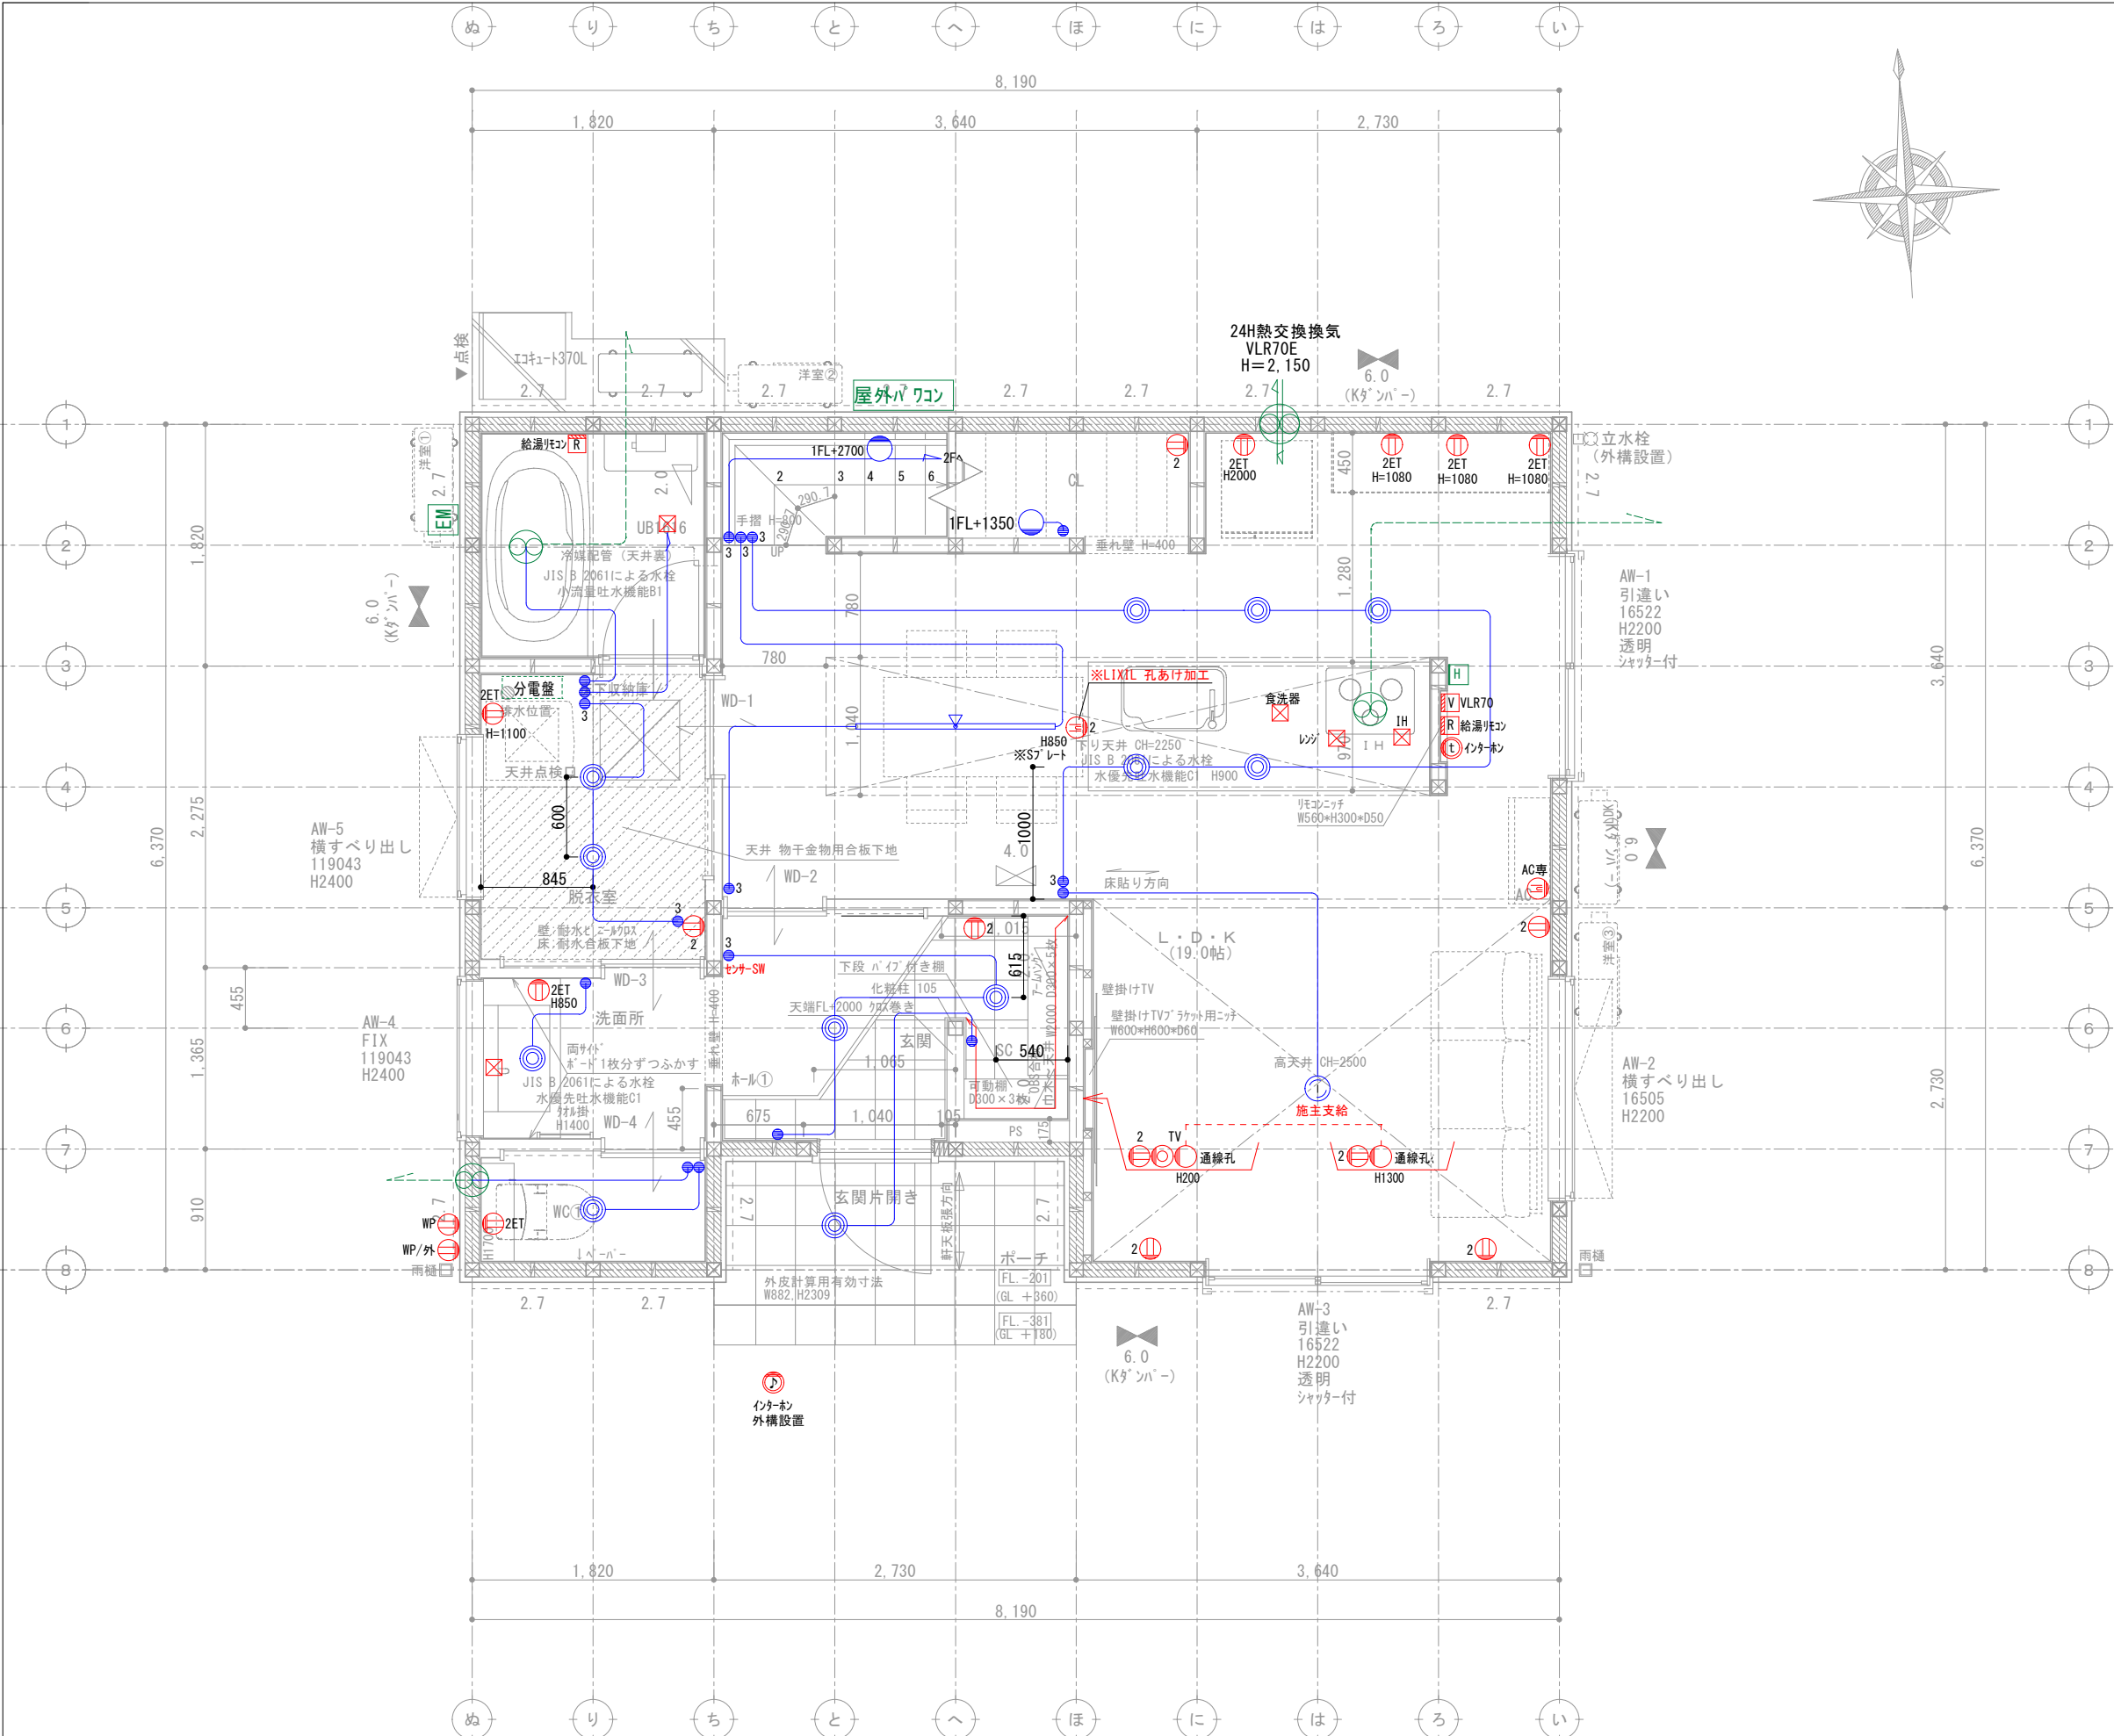

G2

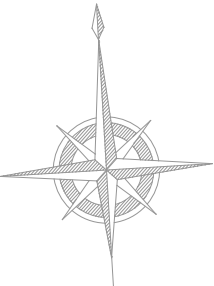

壁付け 住宅用火災報知器			数量
H 熱感知	熱感知器	電池式(単独型)	1
		露出型	
壁付け 住宅用火災報知器			数量
S 煙感知	煙感知器	電池式(単独型)	
		露出型	

- ※ 煙感知器は壁・梁より600mm以上離す
壁に取付ける場合、
天井から150mm以上500mm以内離す
換気扇・エアコン吹出口から1500mm以上離す
- ※ 全室LED照明とする。
- ※ 標準天井高さ2,400
- ※ 特記無きガラスは型ガラス

*** 凡例**

☒ 管柱 (105×105)

◀▶ Kダクト (3.30倍 FRM-0641)

△ 片筋違い (2.00倍 45×90)
(例 左:柱脚 右:柱頭)

⊠ たすき掛筋違い (4.00倍 45×90)

--- 構造用合板 (2.70倍)
(t=9 材種-EXハイバ-)

◻ 床点検口

⊠ 天井点検口

⊙ 換気扇

⊙ 熱交換換気扇VLR-70

- ※ 全室LED照明とし、調光制御を採用する。
- ※ 非居室の照明は人感センサーを採用する。
- ※ 階段寸法
蹴上：207.14 (2900÷14段)
踏面：227.5
有効幅：780
手摺出幅100mm以下

決定図