

■ 仕 様			■ HEAT20 G2		
断熱工事		■ 床:カネライトフォーム t90 ■ 土間床等の外周:スタイロフォームAT t50 ■ 壁:アクアフォームLITE吹付 t90 ■ 天井:アクファフォームLITE吹付 t220			
床下換気		■ 基礎パッキン JOTO (玄関・UB周り:気密基礎パッキン)			
防虫防蟻		■ 土壌処理・木部 ガントナーMC			
■ 外 部 仕 上 表			■ 22条地域		
部位		仕上・仕様・メーカー		色番・品番	
屋根		■ ガルバリウム鋼板(t0.35)UK立平 ニスクカラーPro GH 軒先通気金物 日本住環境株式会社【REV-15】		GCM36 Cペールゴールド	
パラペット笠木		■ なし			
破風・鼻隠		■ なし			
雨樋	(軒樋)	■ Panasonic サーフeskエアFS-I型		ブラック	
	(縦樋)	■ Panasonic S30角樋		ブラック	
軒天	屋根軒	■ なし			
	ポーチ軒	■ 神島化学 アルテザード		レッドシダーエイジング	
	バルコニー軒	■ なし			
オーバーハング水切り		■ ガルバリウム鋼板 ※外壁合わせ JOTO:HF-A3550		ブラック	
外壁	通気金物(15mm)	■メイン	Kmewエクセラージ・シックイフラット 光セラ	QFセラノ チタン ディープグレー	
	※下地面材:タイガーEXハイパー	■アクセントA	なし		
	防火認定 PC030BE-4028	■アクセントB	なし		
玄関ポーチ		■ 床 玄関に同じ		-	
基礎		■ 立上り巾木: モルタル刷毛引き		-	
基礎水切り金物		■ JOTO鋼板製 防鼠材付き水切り JOTO:WMF-N35		ブラック	
バルコニー	床・内壁	■ なし		-	
	笠木	■ なし			
外部建具		■ LIXIL EW(アルゴンガス高遮熱仕様LowEトリプルガラス クリア) ・SD、TSは、メーカー設定によるが、オペレーターハンドル優先とする ・オペレーター付サッシの場合は固定網戸とする ・グレモンハンドル式サッシの場合は可動網戸とする		外観 ブラック 内観 ホワイト ※樹脂パッキン・網戸付	
シャッター		■ LDK 掃き出しサッシ 手動 2ヶ所			
軒天通気金物					
玄関扉		■ LIXIL ジエスタ2 K2仕様 LIXILファミロック タグキー×3 (電池式)		ドア型: M17 型 ドア色: チーク浮造 ハンドル: S型ハンドル 色 ブラック	
外部物干し金物		■			
換気フード		■ 局所換気扇(トイレ 浴室 キッチンフード) 防火ダンパー無		外気フード: ブラック	
		■ ダクトレス熱交換換気システム (日本スティーベル株式会社) VLR-70E 防火ダンパー無		外気フード: B ブラック 室内パネル ホワイト	

■ 構 造 概 要					
基礎	■ RCベタ基礎コンクリート				
通し柱・管柱	■ 構造用集成材 105×105		間柱	■ 集成材	
土台	■ 桧 105×105	大引き	■ 桧 90*90	筋交い	■ 構造用製材 火打梁 ■ 鋼製火打(当社基準により米松あり)
桁・梁	■ 構造用製材及び集成材			制震装置	■ Kダンパー (株)アイ・エム・エー
■ 設 備 装 着 品					
住宅設備	部位	メーカー	商品名 ※ 詳細は見積り、プレゼン参照	見積りNo.	(日付)
	キッチン	LIXIL	■ ES	見積り番号 : M25109107270-008-2	(日付) 2025.12.03
	バックカウンタ ※オプション	LIXIL	■ ES	見積り番号 : M25109107270-008-3	(日付) 2025.12.03
	浴室	LIXIL	■ AX1616 PGハウス標準仕様	見積り番号 : M25109107270-008-1	(日付) 2025.12.03
	1Fトイレ	LIXIL	■ ベーシアシャワートイレ 白 ● タオル掛け: なし(支給品取付) タンク手洗 無し ● 紙巻き器: CF-AA22H /BW1	見積り番号 : M25109107270-008-5	(日付) 2025.12.03
	2Fトイレ	LIXIL	■ ベーシアシャワートイレ 白 ● タオル掛け: なし(支給品取付) タンク手洗 有り ● 紙巻き器: CF-AA22H /BW1	見積り番号 : M25109107270-008-6	(日付) 2025.12.03
	洗面台	LIXIL	■ カスタム パニティ その他 ● タオル掛け: KF-AA70D(リンク)	見積り番号 : M25109107270-008-4	(日付) 2025.12.03
			■		
給排水設備	給湯器	■ エコキュート370L Panasonic Sシリーズ スタンダードモデル 追い焚きフルオート			
	排水	■ 下水			
	外水栓	■ 1 カ所 (平面図参照)	■ 外部立栓柱: 立水栓(外構で施工)		
	外部ガーデンパン	■ 無し			
	その他	■ 洗濯機用単水栓: 緊急止水弁付 ■ 洗濯機用排水: トラップ金物(標準) ■ 排水さや管(長期優良住宅仕様)			
ガス配管設備	■ なし (配置図・平面図参照) ■ガス使用器具				
電気設備	インターホン	■ パナソニック VL-SE31XL			
	TVアンテナ	■ UHF + BS・110度CS／CSアンテナ [2K・4K・8K対応] ■ブラック ※電波状況によりホワイトになる可能性あり			
	エアコン	■ 設置場所: 洋室①② 隠蔽配管			
	ソーラー	■ あり(Qセルズ) 12 枚 5.28 KW Re.RISE-G3 440 (1722×1134×30)			
	※標準搭載	※メーカーのモデルチェンジ等で後継品に変更される可能性あり ■ 屋外パワコン エネルギーマネジメントシステム Cube J			
その他					
決定図					

決定図

	浜 岡 一 級 総 合 設 計 事 務 所 一級建築士事務所 静岡県知事登録第 (10)2441 号 一級建築士 大臣登録第 365879 号 西原利昌	 株式会社 LIFEFUND InDesign office 一級建築士事務所 事務所登録 (2)第7595号 一級建築士登録 第179770号 鈴木 達男 〒432-8023 静岡県浜松市中央区鴨江3丁目70番23号	年 月 日	2026.1.4		件名	寺本唯麻 様邸 新築工事			設計	IC	工務	図 番
			縮尺			図面	仕上表 1			酒井		青島	1-1

内 部 仕 上 表 （壁下地:石膏ボード12.5mm/天井下地:9.5mm）※脱衣室:床合板特類 下地									
階		床	巾木	壁	品番	廻 縁	天 井	品番	特記事項
1F	ポーチ	LIXILパセオ300/PSO-FIO 4							
	玄関	LIXILパセオ300/PSO-FIO 4	ライン巾木(W)	ビニルクロス	SLP-341	突付	ビニルクロス	SLP-341	
	SC	LIXILパセオ300/PSO-FIO 4	ライン巾木(W)	ビニルクロス	SLP-341	突付	ビニルクロス	SLP-341	壁 OSB合板::キワミ クリア
	ホール①	イタ銘木フロアースティックt12 ナラ桜3P	ライン巾木(W)	ビニルクロス	SLP-341	突付	ビニルクロス	SLP-341	
	LDK	イタ銘木フロアースティックt12 ナラ桜3P	ライン巾木(W)	ビニルクロス	SLP-341	突付	ビニルクロス	SLP-341	アクセントあり
	洗面	イタ銘木フロアースティックt12 ナラ桜3P	ライン巾木(W)	ビニルクロス	SLP-341	突付	ビニルクロス	SLP-341	
	脱衣ランドリー	フロアタイルt2.3 サンゲツIS-2071	H40ソフト巾木W97	ビニルクロス	SLP-341	突付	ビニルクロス	SLP-341	
	WC①	フロアタイルt2.3 サンゲツIS-2071	H40ソフト巾木W97	ビニルクロス	SLP-341	突付	ビニルクロス	SLP-341	アクセントあり
2F	ホール②	イタ銘木フロアースティックt12 ナラ桜3P	ライン巾木(W)	ビニルクロス	SLP-341	突付	ビニルクロス	SLP-341	
	主寝室	イタ銘木フロアースティックt12 ナラ桜3P	ライン巾木(W)	ビニルクロス	SLP-341	突付	ビニルクロス	SLP-341	
	洋室①	イタ銘木フロアースティックt12 ナラ桜3P	ライン巾木(W)	ビニルクロス	SLP-341	突付	ビニルクロス	SLP-341	アクセントあり
	洋室②	イタ銘木フロアースティックt12 ナラ桜3P	ライン巾木(W)	ビニルクロス	SLP-341	突付	ビニルクロス	SLP-341	
	WIC	イタ銘木フロアースティックt12 ナラ桜3P	ライン巾木(W)	ビニルクロス	SLP-341	突付	ビニルクロス	SLP-341	
	WC②	フロアタイルt2.3 サンゲツIS-2071	H40ソフト巾木W97	ビニルクロス	SLP-342	突付	ビニルクロス	SLP-342	
物入・収納・CL etc		※接続する部屋と同仕様とする							

上 框 ※	■ LIXILラシッサS 上框のみ30×150 色: クリエチェリー
階 段	■ LIXIL KA 階段 ササラ: プレシャスホワイト
KA階段で対応できない場合、オプション	段 板 : クリエチェリー 蹴込板: プレシャスホワイト
ラウンド手摺: ブラック	手摺金物 ブラック
にてラシッサS階段	上段框: クリエチェリー 長尺笠木156: LIXIL
窓 枠	■ スマート10(玄関以外) 色 プレシャスホワイト
	※浴室ドア枠 フクビ3方枠 [ホワイト]
キッチン笠木	■ なし 色
カウンター	形状
天井点検口	■ 天井アルミ点検口枠 450角 TAN45BW フクビ化学工業
	ミルキーホワイト
床下収納庫	■ 高気密型床下点検口断熱型 SPF-R6060 城東テクノ 収納付
	(脱衣室) ライトグレー(LG)
トイレ棚	■ 1,2階トイレ D250 アートランバー棚(シェルホワイト)
室内物干し金物	■
LDK-カウンター	■ なし 色
	t=25
下足入	■ なし 色
プッシュタイプ	サイズ: 形状:



支給品	
備考	※付框は(30×150)プレシャスホワイト 可動棚アートランバー色 ダークグレー 棚受金物類は全てブラック

内 部 建 具 表							
LIXIL		建具色：プレシャスホワイト		枠色 ： 扉同色		※その他、下記特記による	
ラフィス		把手 ： スクエアL (シャインニッケル) 丁番 固定枠(156) 外付戸当り ガイドピン床色合せ 引戸のみ上吊W70フモーション					
階	No	室名	形式	枠外W サイズ	デザイン	枠色	特記事項
				枠外H サイズ	建具色	把手	
1	1	脱衣室	片引き戸	—	RAA	—	明り窓・表示錠
	WD			2400	—	—	
	2	LDK	片引き戸	—	RAA	—	
	WD			2400	トープ	—	
	3	脱衣室	片引き戸	—	RAA	—	明り窓・表示錠
	WD			2400	—	—	
	4	WC①	片引き戸	—	RAA		明り窓・表示錠
	WD			2400	-		
2	5	洋室③	片開き戸	—	RAA	—	
	WD			2400	—	—	
	6	WC②	片開き戸	—	RAA	—	明り窓・表示錠
	WD			2400	—	—	
	7	洋室②	片開き戸	—	RAA	—	
	WD			2400	—	—	
	8	洋室①	片開き戸	—	RAA	—	
	WD			2400	—	—	


浜 岡 一 級 総 合 設 計 事 務 所		 PG HOUSE	株式会社 LIFEFUND InDesign office 一級建築士事務所		年 月 日	件名		設計	IC	工務	図 番
一級建築士事務所 静岡県知事登録第 (10)2441 号			事務所登録 (2) 第7595号 一級建築士登録 第179770号 鈴木 達男		2026.1.4	寺本唯麻 様邸 新築工事		酒井	0	青島	1-2
一級建築士 大臣登録第 365879 号 西原利昌			〒432-8023 静岡県浜松市中央区鴨江3丁目70番23号		縮尺	図面					
					仕上表 2						

浜松市中央区新橋町地内

G2

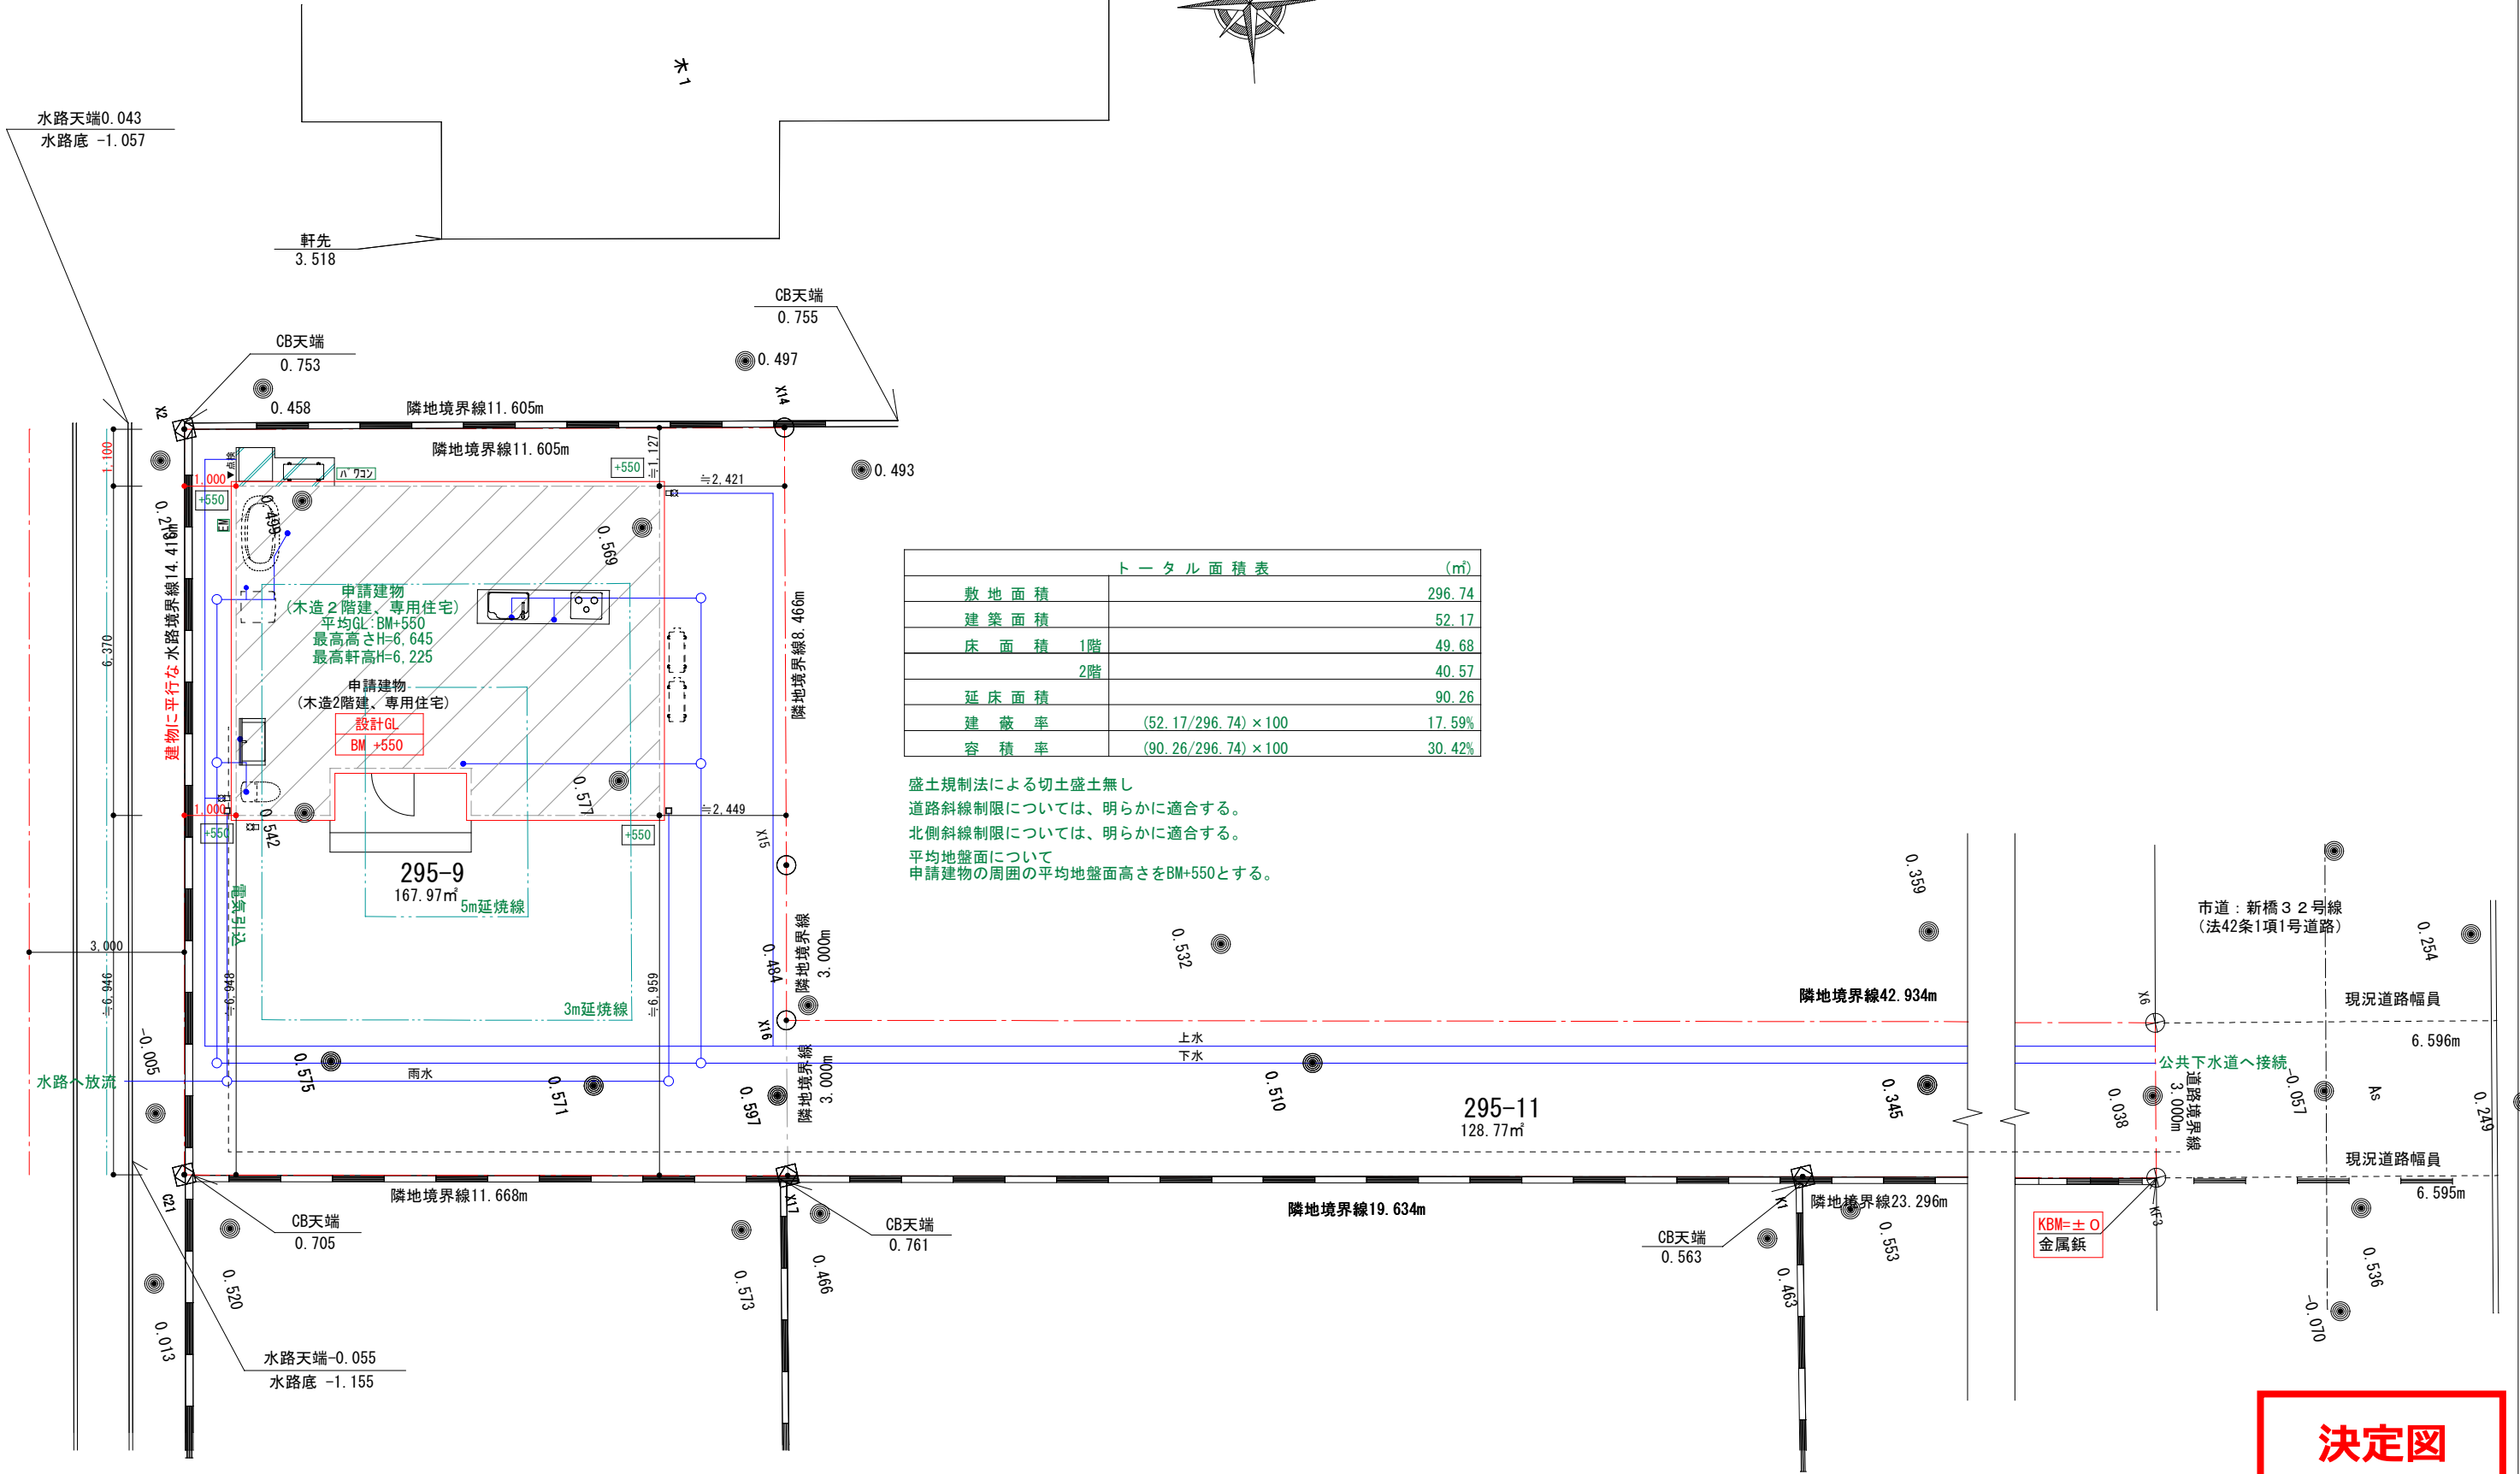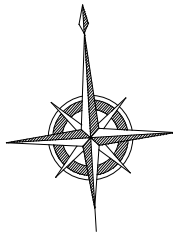


決定図

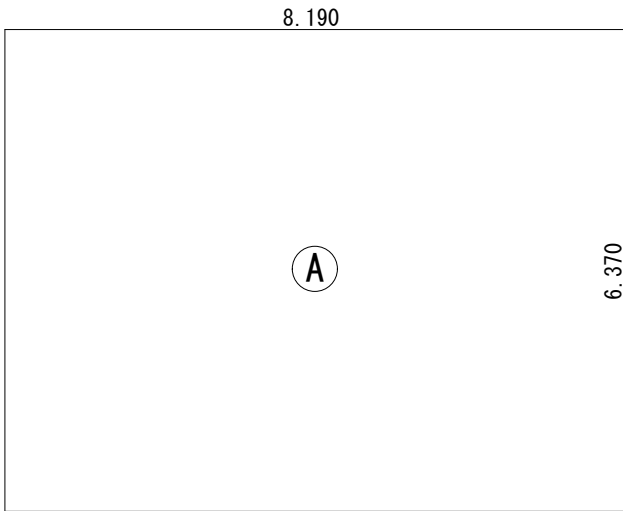

建築面積求積図 S=1/100

建築面積求積表


番号	計算式	(m)	面積 (㎡)
Ⓐ	8.190 × 6.370		52.1703
合計			52.1703 52.17 (15.7坪)

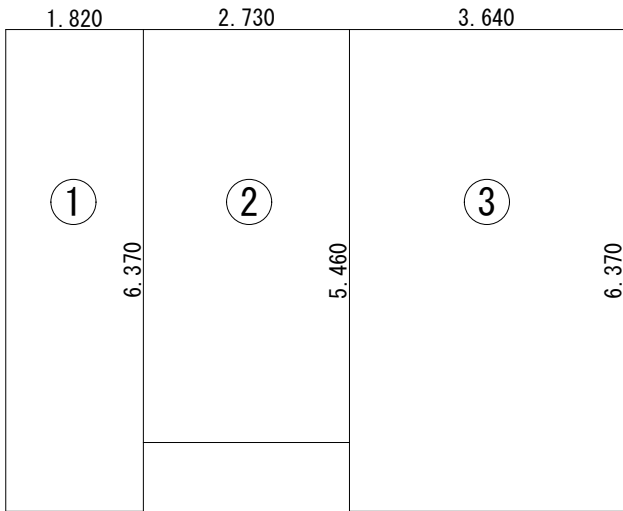

1階床面積図 S=1/100

1階床面積求積表

番号	計算式	(m)	面積 (㎡)
①	1.820 × 6.370		11.5934
②	2.730 × 5.460		14.9058
③	3.640 × 6.370		23.1868
合計			49.6860 49.68 (15.0坪)

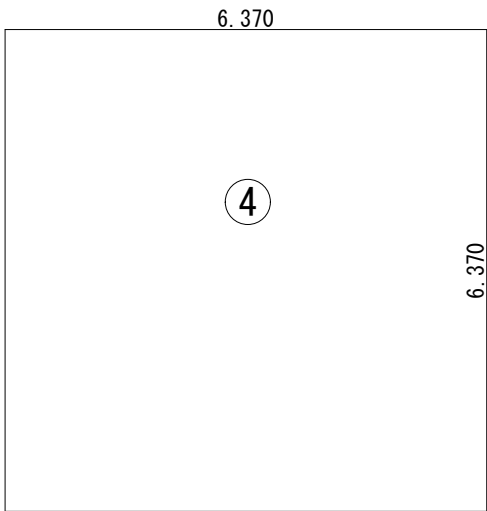

2階床面積図 S=1/100


2階床面積求積表

番号	計算式	(m)	面積 (㎡)
④	6.370 × 6.370		40.5769
合計			40.5769 40.57 (12.2坪)

延べ床面積表

	番号	(m)	面積 (㎡)
1階床面積	① ② ③		49.68
2階床面積	④		40.57
合計			90.26 (27.3坪)

決定図

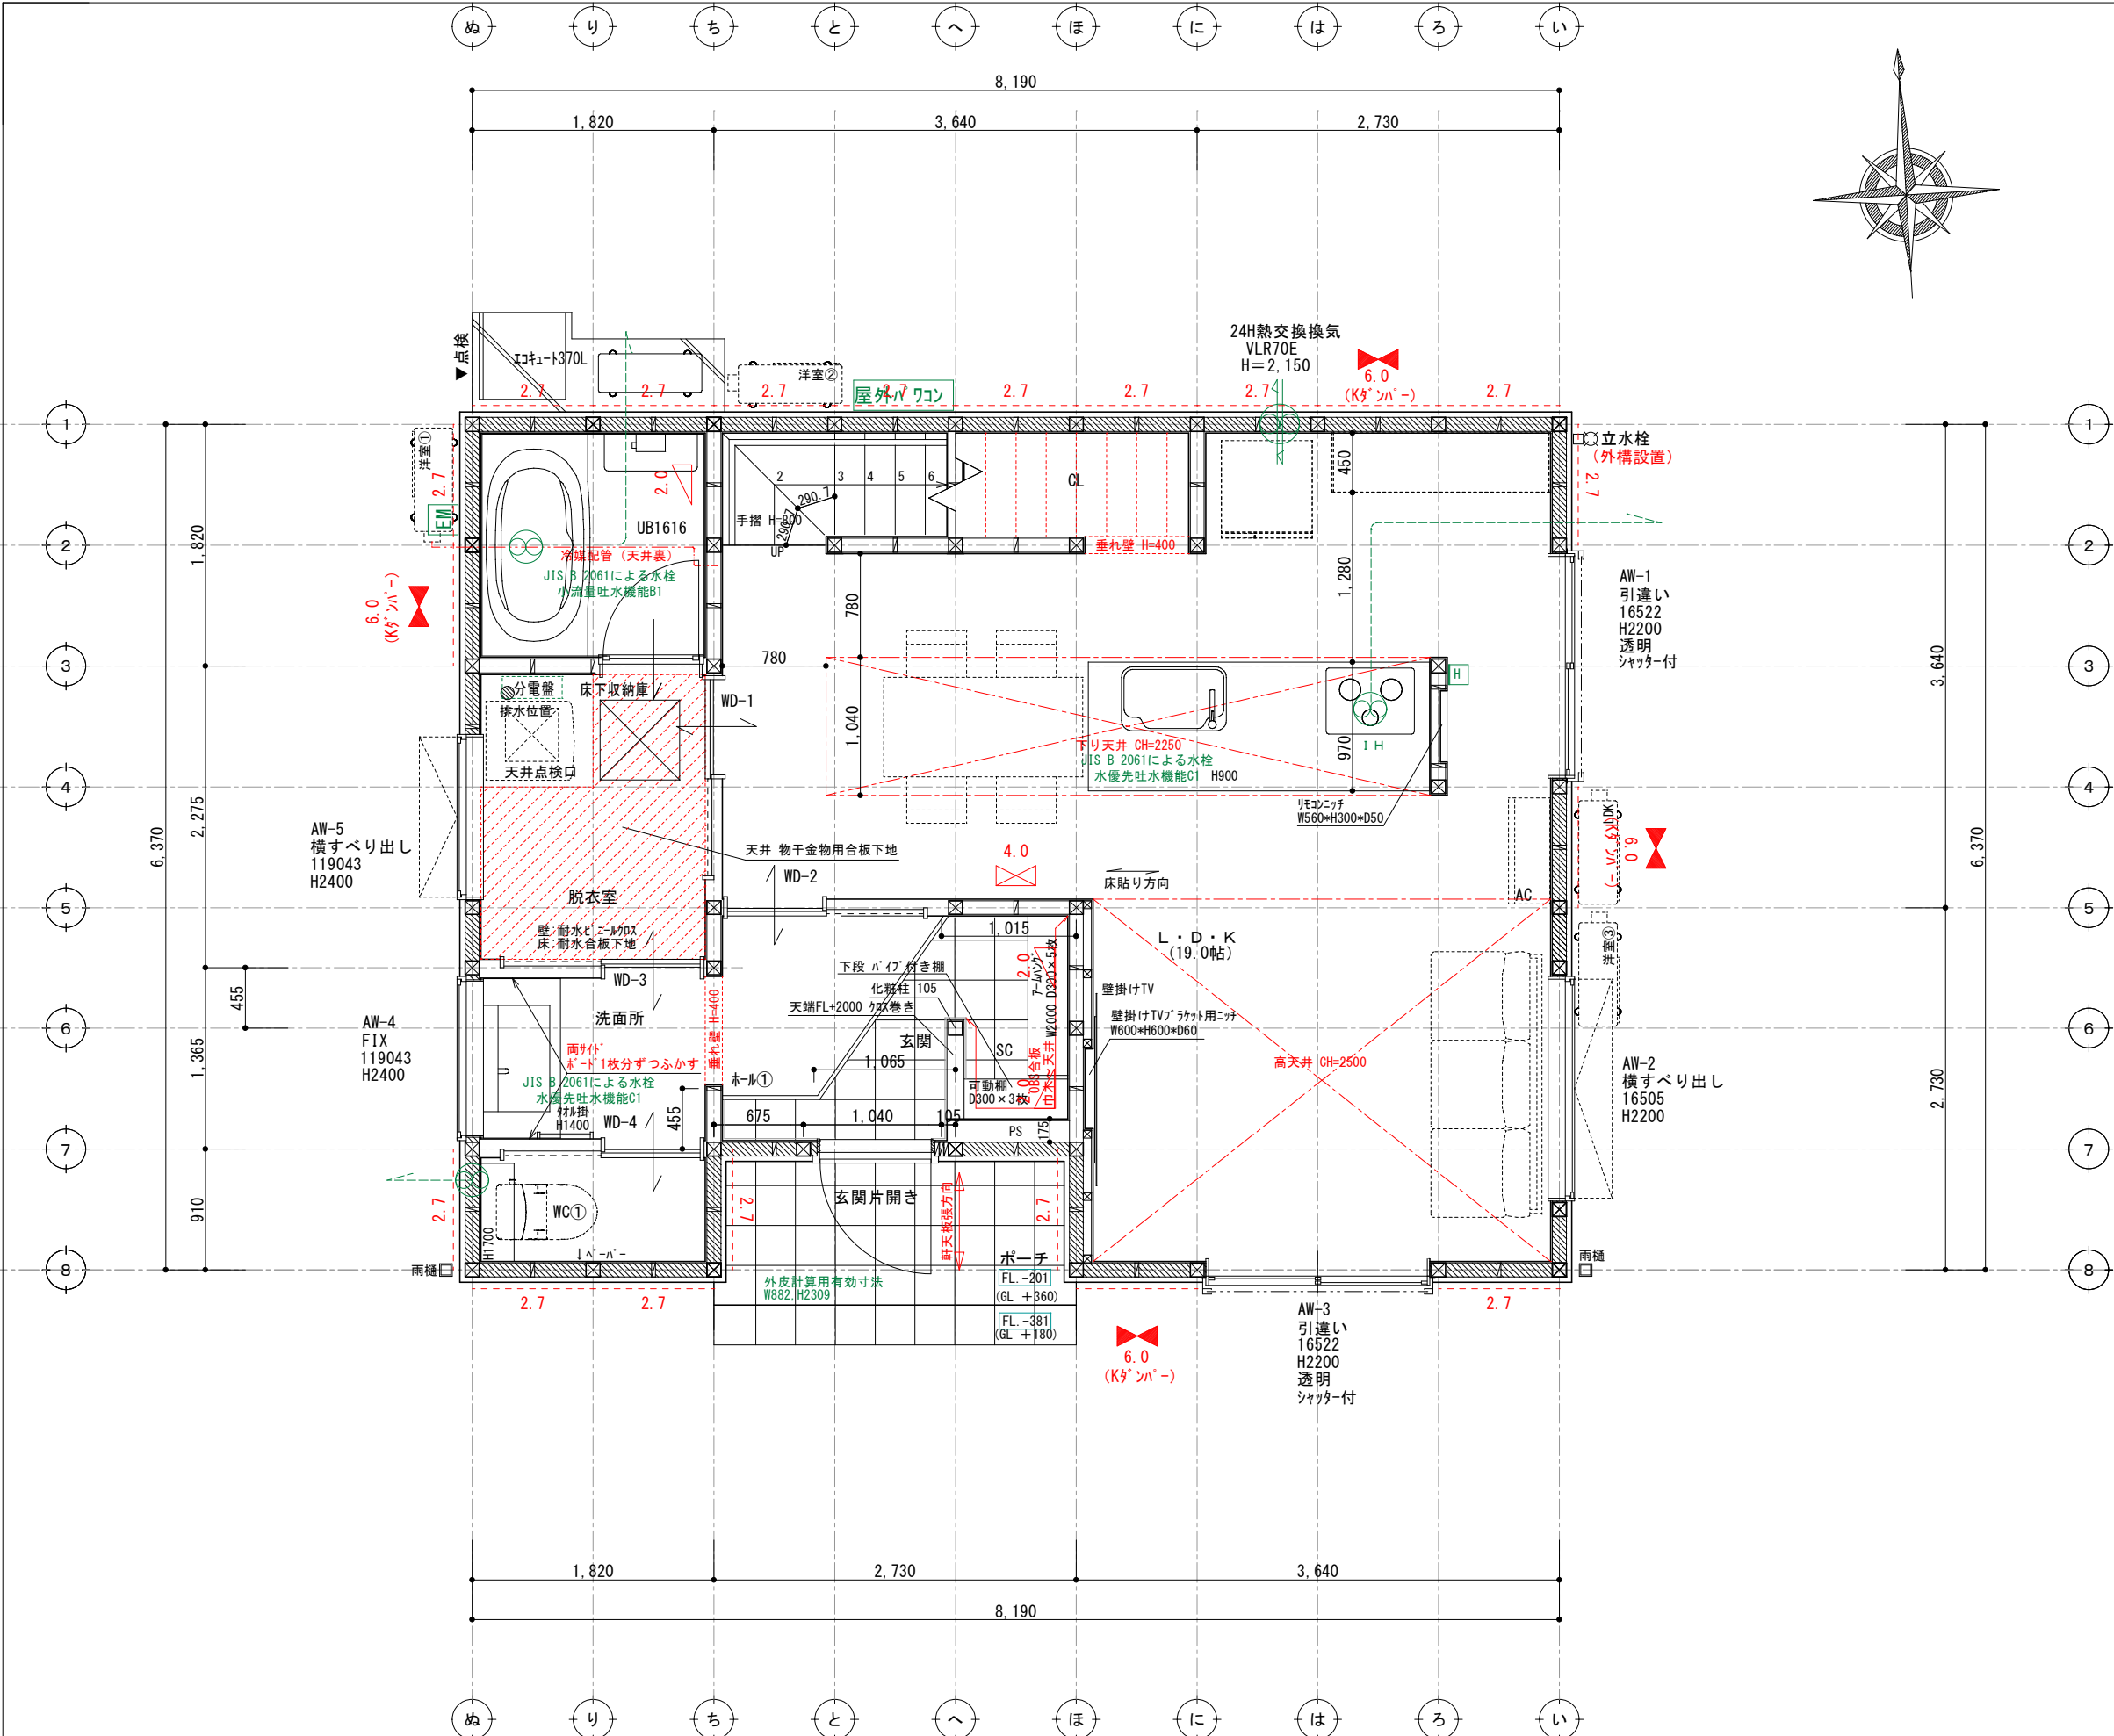

G2

壁付け 住宅用火災報知器			数量
H 熱感知	熱感知器	電池式(単独型)	1
		露出型	
壁付け 住宅用火災報知器			数量
S 煙感知	煙感知器	電池式(単独型)	
		露出型	

- ※ 煙感知器は壁・梁より600mm以上離す
壁に取付ける場合、
天井から150mm以上500mm以内離す
換気扇・エアコン吹出口から1500mm以上離す
- ※ 全室LED照明とする。
- ※ 標準天井高さ2,400
- ※ 特記無きガラスは型ガラス

* 凡例


- 管柱 (105×105)
- Kタツパ- (3.30倍 FRM-0641)
- 片筋違い (2.00倍 45×90)
(例 左:柱脚 右:柱頭)
- たすき掛筋違い (4.00倍 45×90)
- 構造用合板 (2.70倍)
(t=9 材種-EXハイパ-)
- 床点検口
- 天井点検口
- 換気扇
- 熱交換換気扇VLR-70

- ※ 全室LED照明とし、調光制御を採用する。
- ※ 非居室の照明は人感センサーを採用する。

※ 階段寸法

- 蹴上: 207.14 (2900÷14段)
- 路面: 227.5
- 有効幅: 780
- 手摺出幅100mm以下

決定図

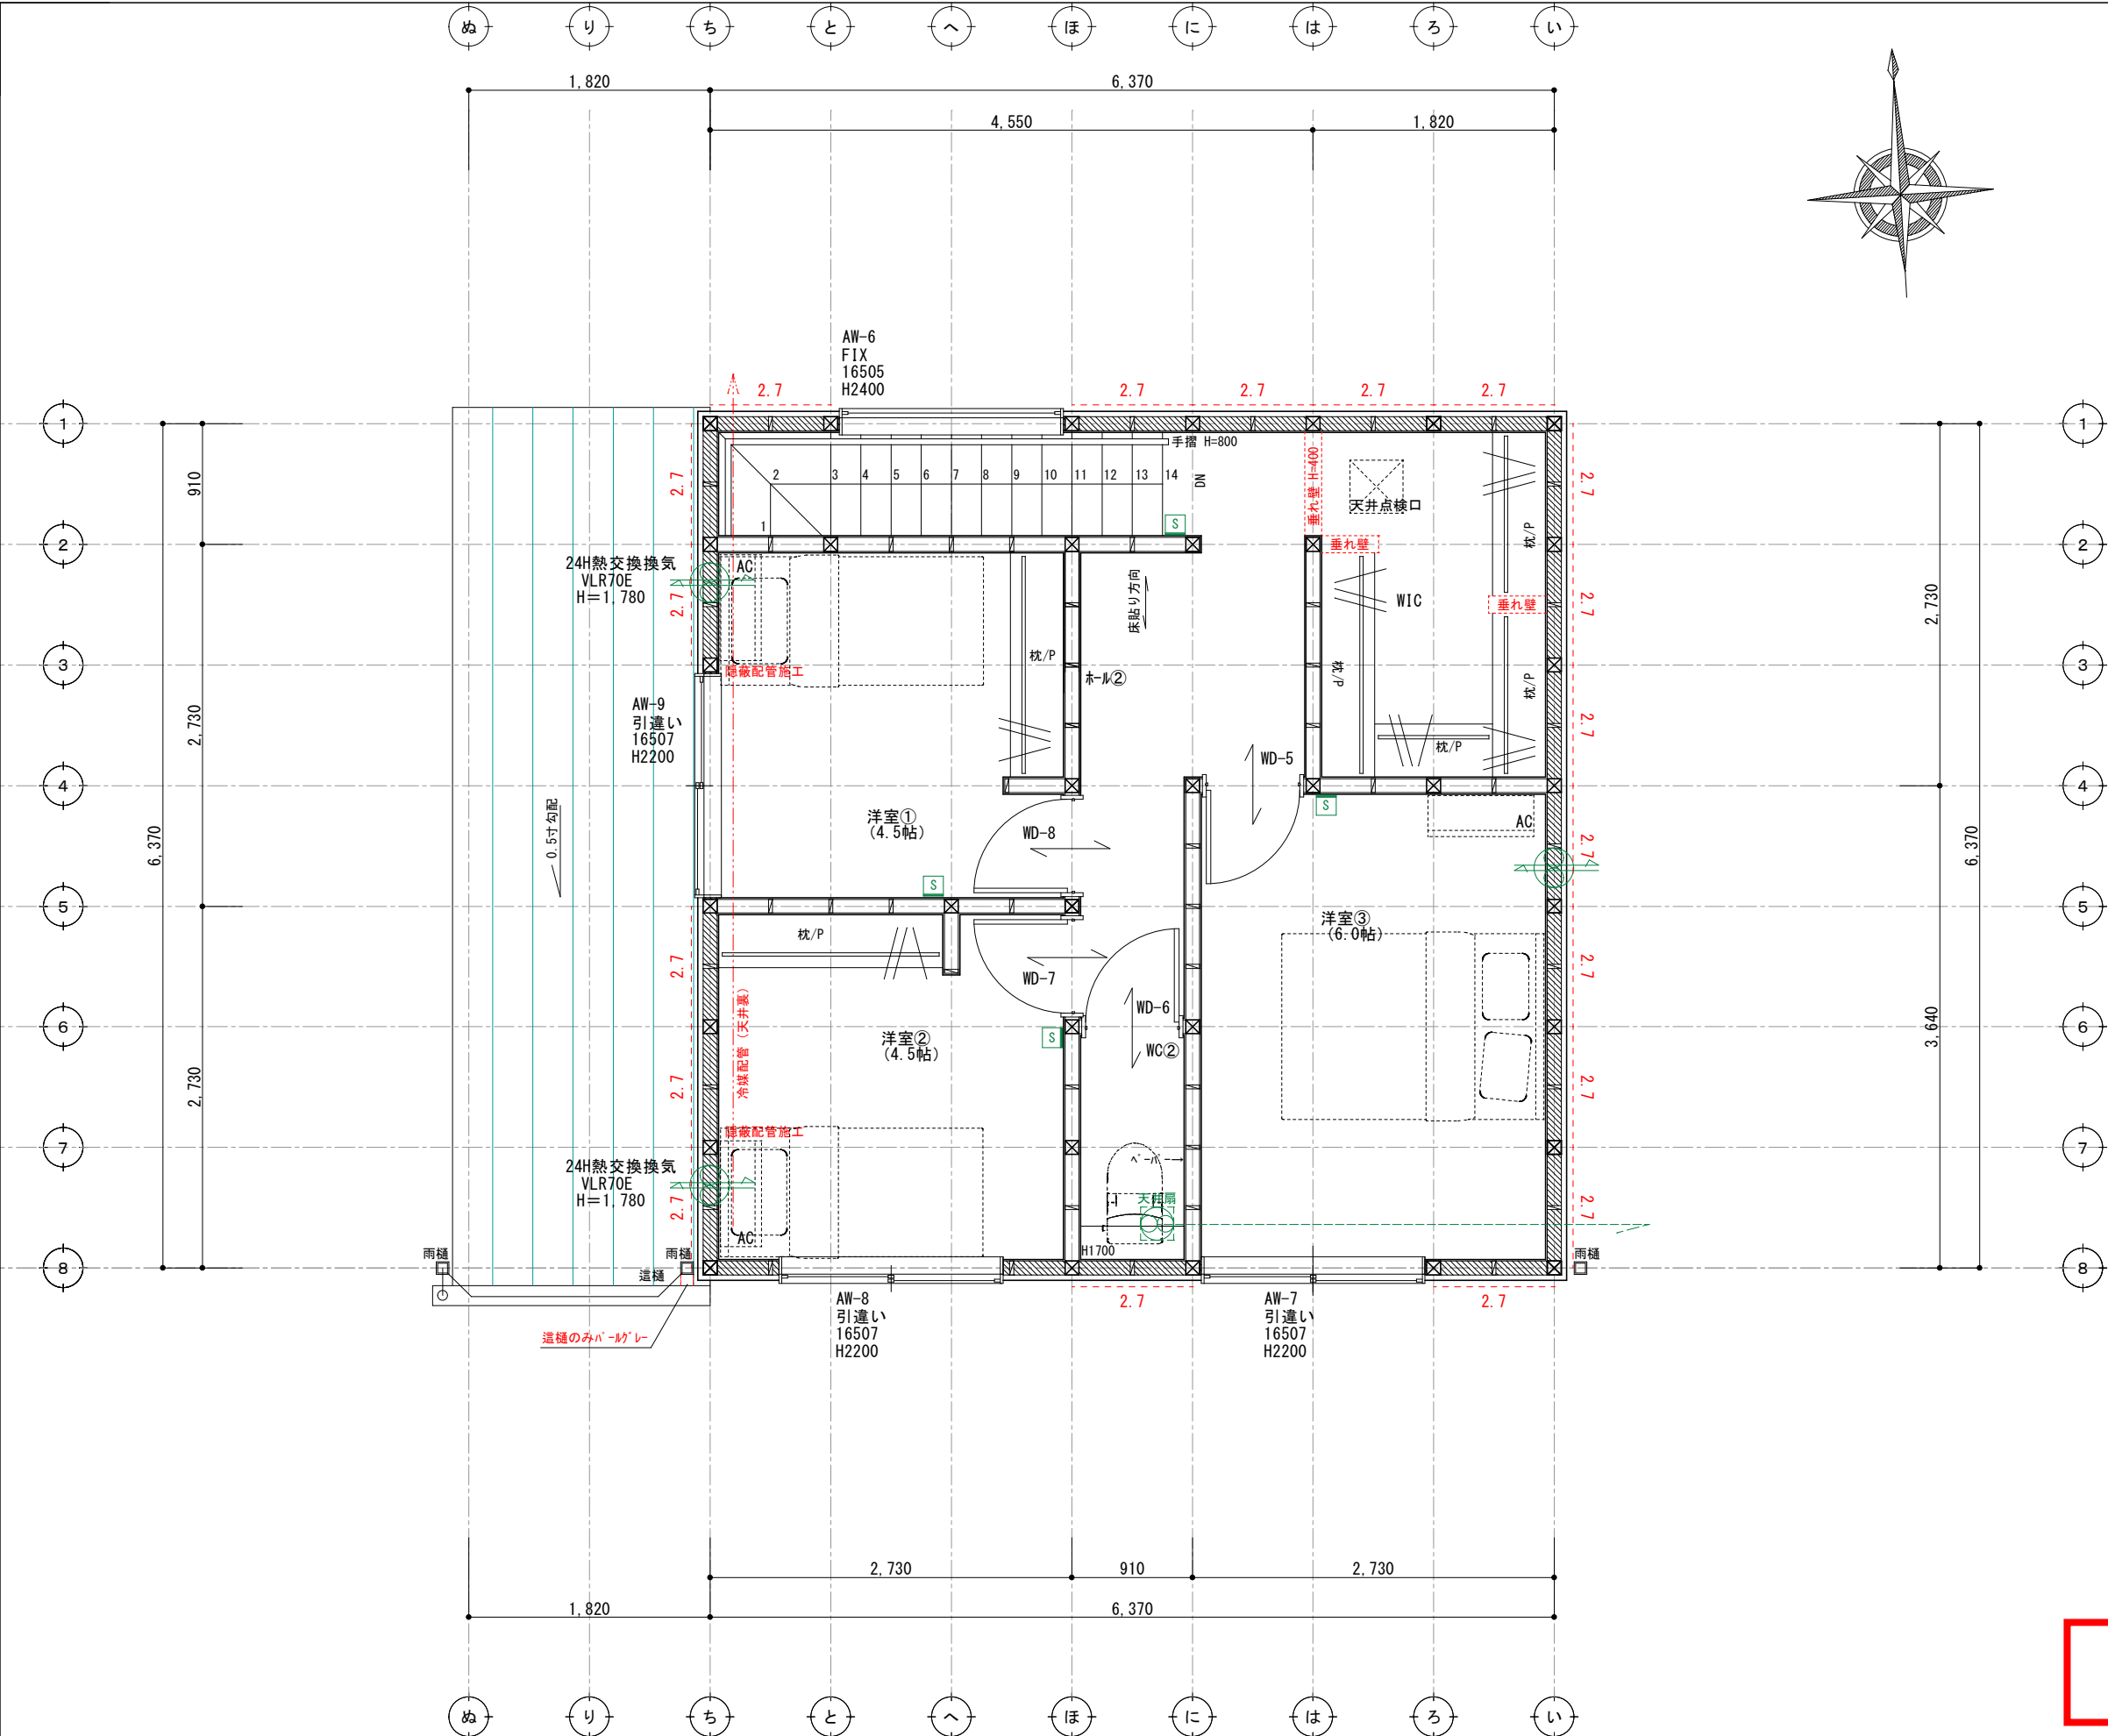

G2

壁付け 住宅用火災報知器			数量
H	熱感知器	電池式(単独型)	
	熱感知器	露出型	
壁付け 住宅用火災報知器			数量
S	煙感知器	電池式(単独型)	4
	煙感知器	露出型	

※ 煙感知器は壁・梁より600mm以上離す
壁に取付ける場合、
天井から150mm以上500mm以内離す
換気扇・エアコン吹出口から1500mm以上離す
※ 全室LED照明とする。
※ 標準天井高さ2,400
※ 特記無きガラスは型ガラス

* 凡例

管柱 (105×105)

Kダクト (3.30倍 FRM-0641)

片筋違い (2.00倍 45×90)
(例 左:柱脚 右:柱頭)

たすき掛筋違い (4.00倍 45×90)

構造用合板 (2.70倍)
(t=9 9材 EXハイバ)

床点検口

天井点検口

換気扇


熱交換換気扇VLR-70

※ 全室LED照明とし、調光制御を採用する。
※ 非居室の照明は人感センサーを採用する。

アドバンスシリーズ			
スマートデザイン (外部)			
凡例	1	コンセント	1ヶ所
2	コンセント	2ヶ所	
3	コンセント	3ヶ所	
1ET	コンセント1ヶ所接地ターミナル付		
2ET	コンセント2ヶ所接地ターミナル付		
WP	コンセント	防水型	
WP	エアコン用コンセント		
WP	200V用コンセント		
WP	防雨入線プレート		
スイッチ			
3	3路スイッチ		
4	4路スイッチ		
直結電源			
TV	テレビ取出口		
TEL	電話取出口 (テレホンガイド)		
LAN	LAN取出口 (テレホンガイド)		
壁照明			
リモコン (給湯関係・ルフロ)			
メーター			
分電盤			
チャイム			



※ACコンセント天井付け
※TVアンテナ工事
※スイッチはFL+1100、コンセントはFL+200

決定図

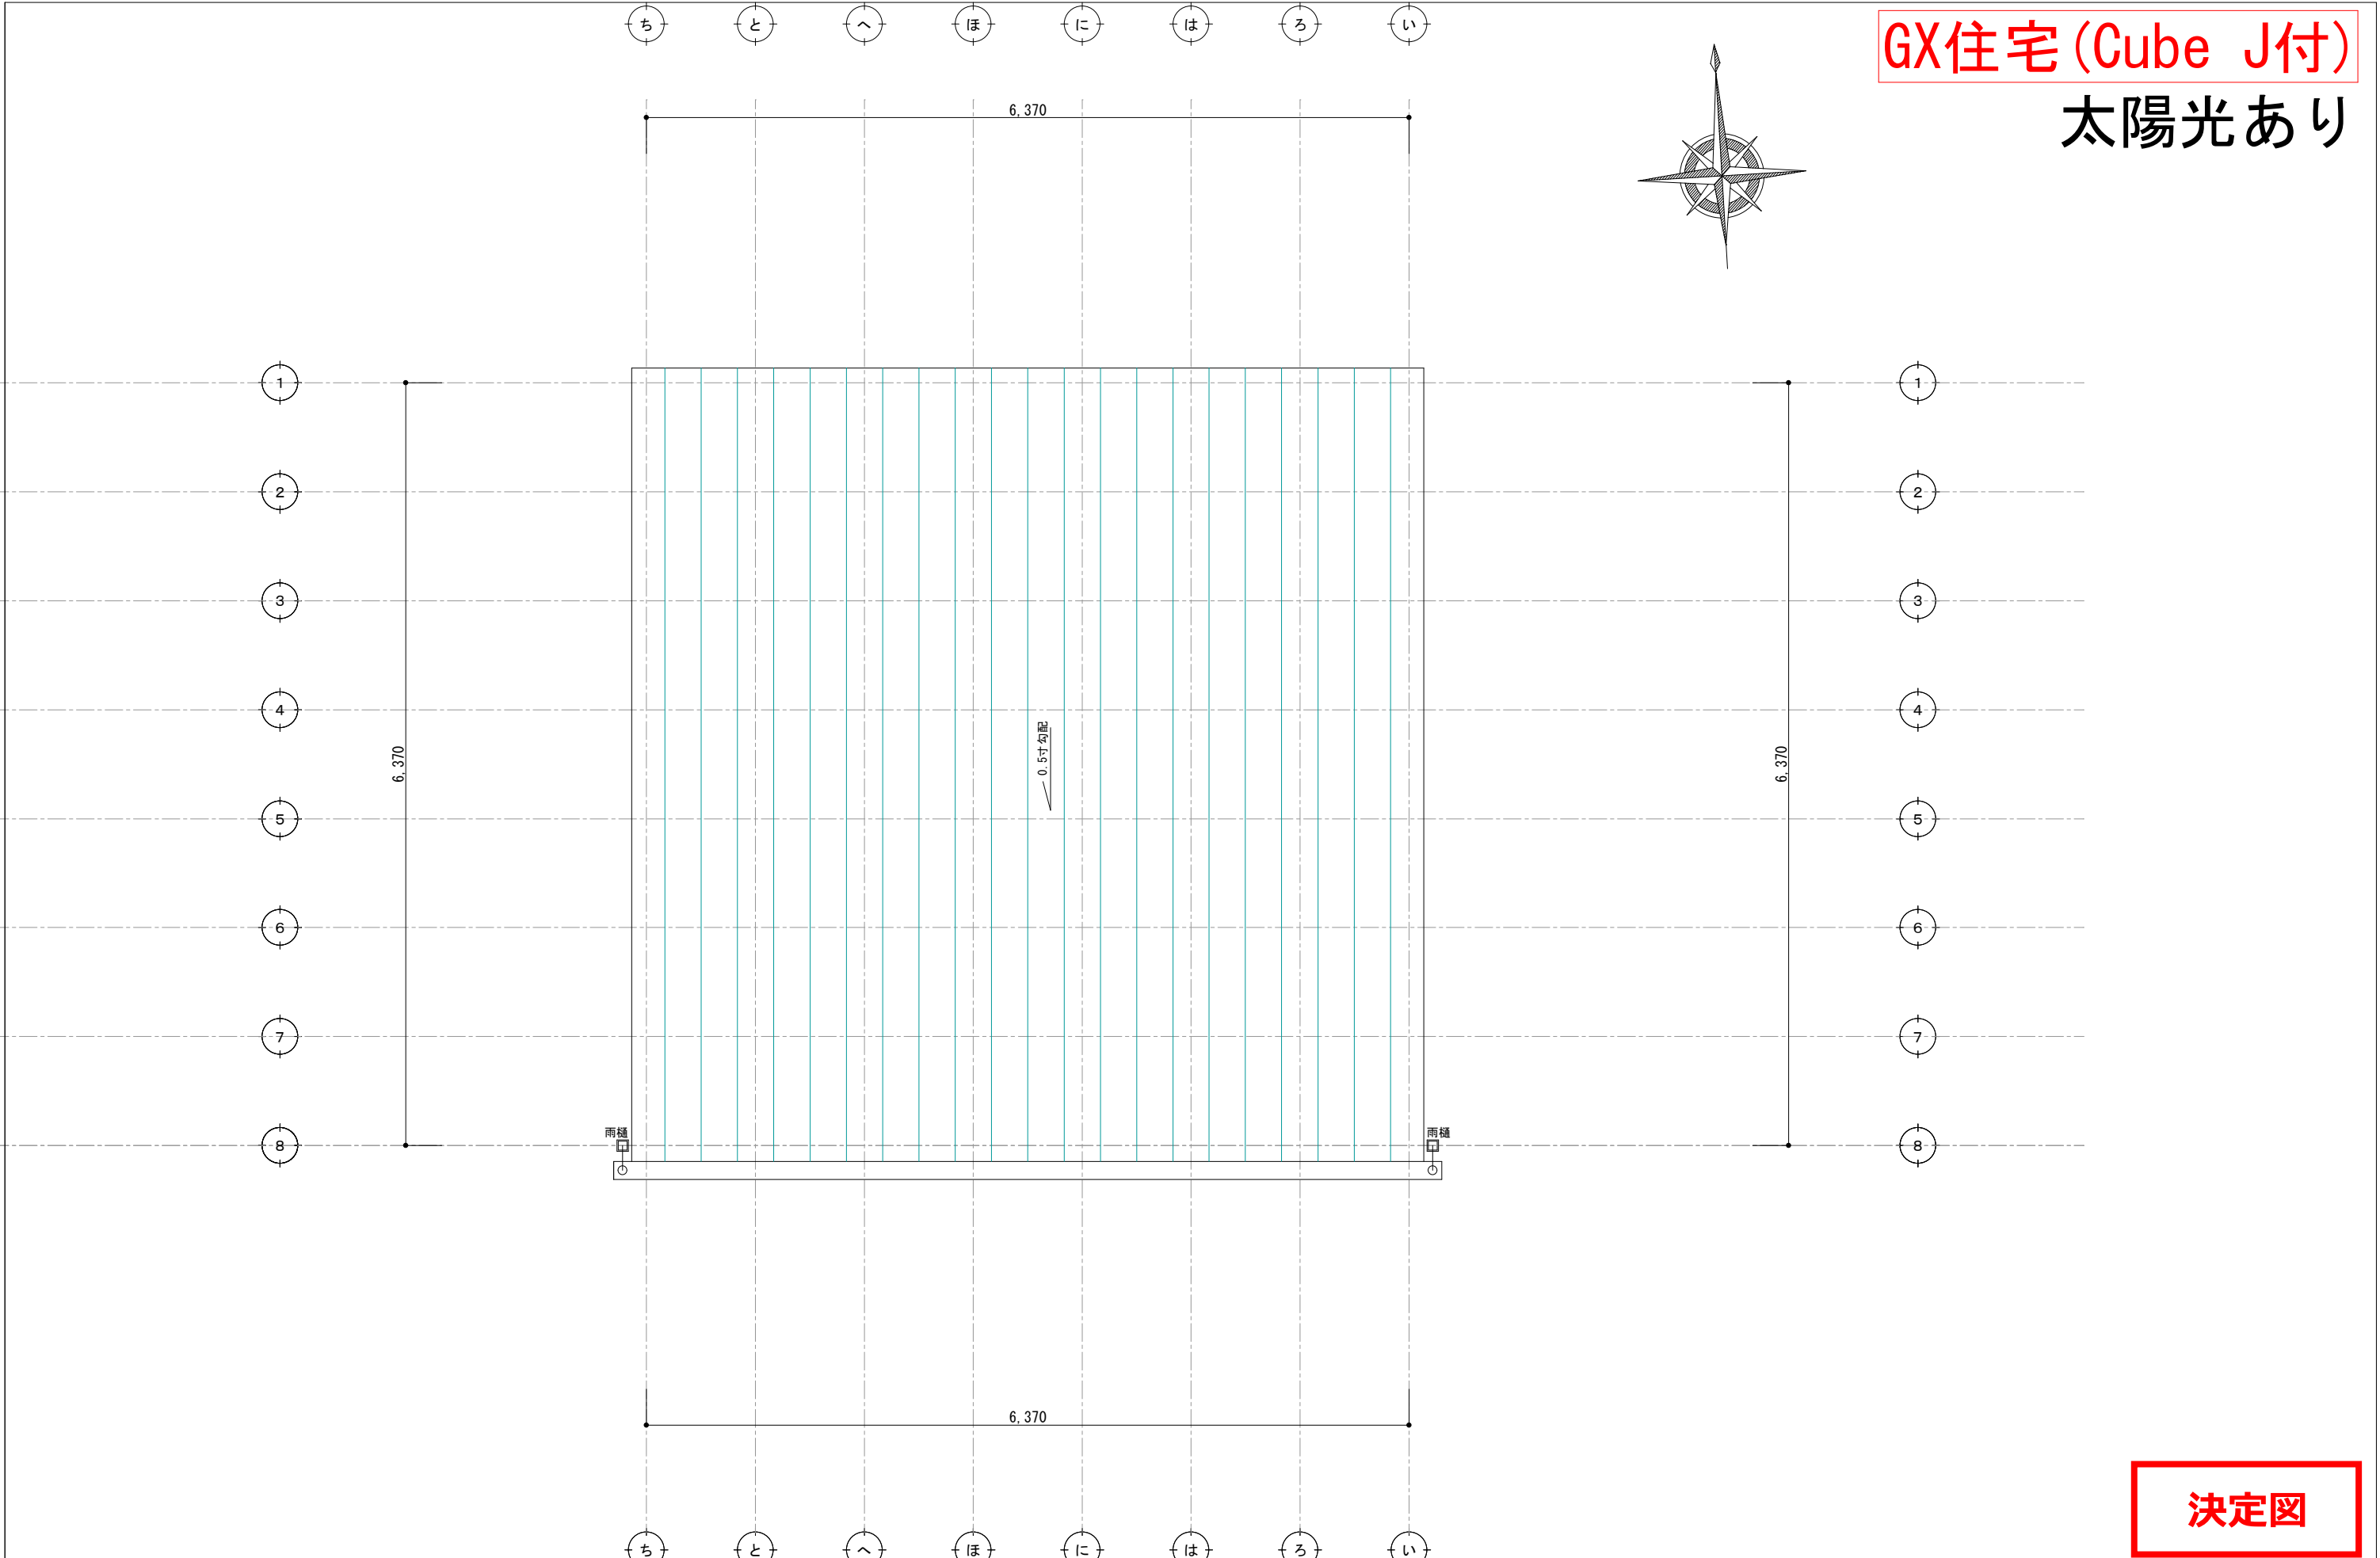


訂 正	浜 岡 一 級 総 合 設 計 事 務 所 一級建築士事務所 静岡県知事登録第 (10)2441 号 一級建築士 大臣登録第 365879 号 西原利昌		株式会社 LIFEFUND InDesign office 一級建築士事務所 事務所登録 (2) 第7595号 一級建築士登録 第179770号 鈴木 達男 〒432-8023 静岡県浜松市中央区鴨江3丁目70番23号	年 月 日	件 名		設 計	IC	工 事	図 番
				2026. 1. 4			酒 井		青 島	3-3
				縮 尺	図 名					
				1/100	寺本唯麻様邸 新築工事 屋根伏図					

G2







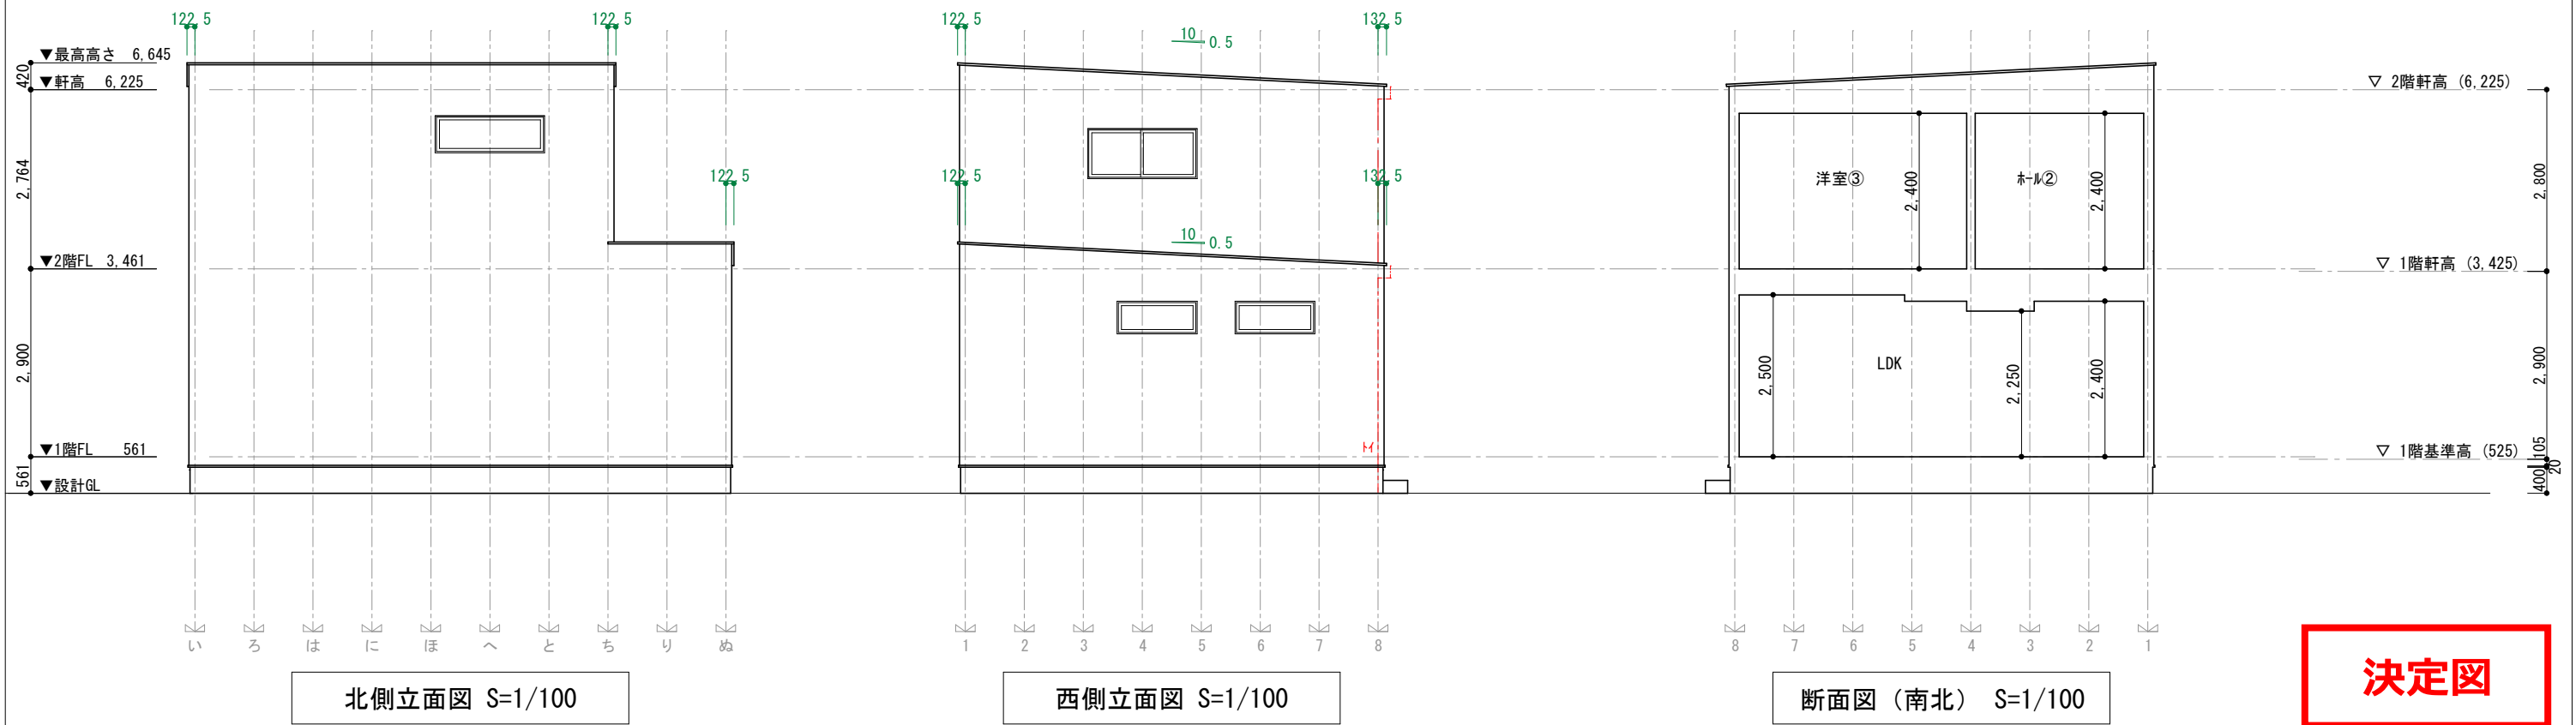
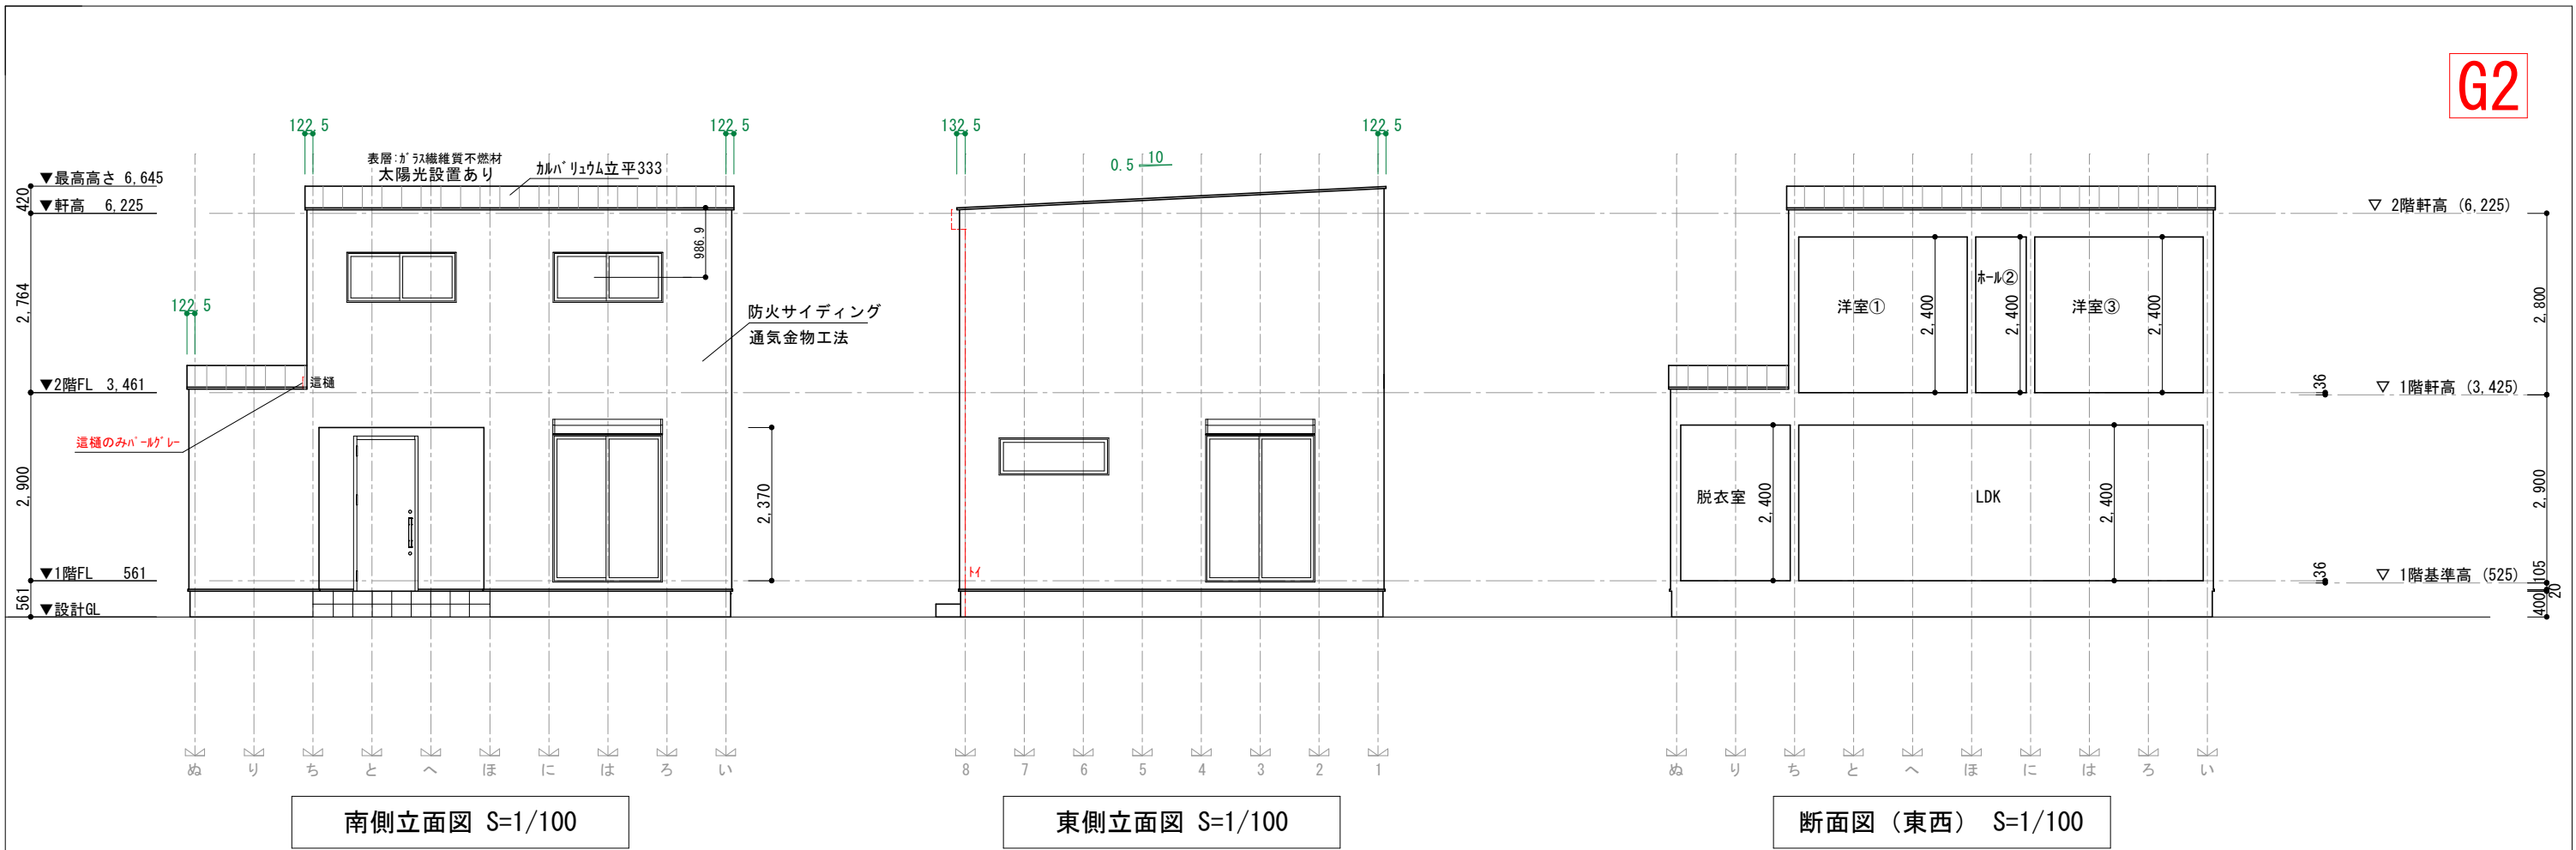


決定図

訂正	浜岡一級総合設計事務所 一級建築士事務所 静岡県知事登録第 (10)2441 号 一級建築士 大臣登録第 365879 号 西原利昌	PG HOUSE ピージーハウス	株式会社 LIFEFUND InDesign office 一級建築士事務所 事務所登録 (2) 第7595号 一級建築士登録 第179770号 鈴木 達男 〒432-8023 静岡県浜松市中央区鴨江3丁目70番23号	年月日 2026.1.4 縮尺 1/100	件名 寺本唯麻様邸 新築工事 図名 立面図		設計 酒井	IC	工事 青島	図番 4
----	--	---------------------	---	--------------------------------	--------------------------------	--	----------	----	----------	---------

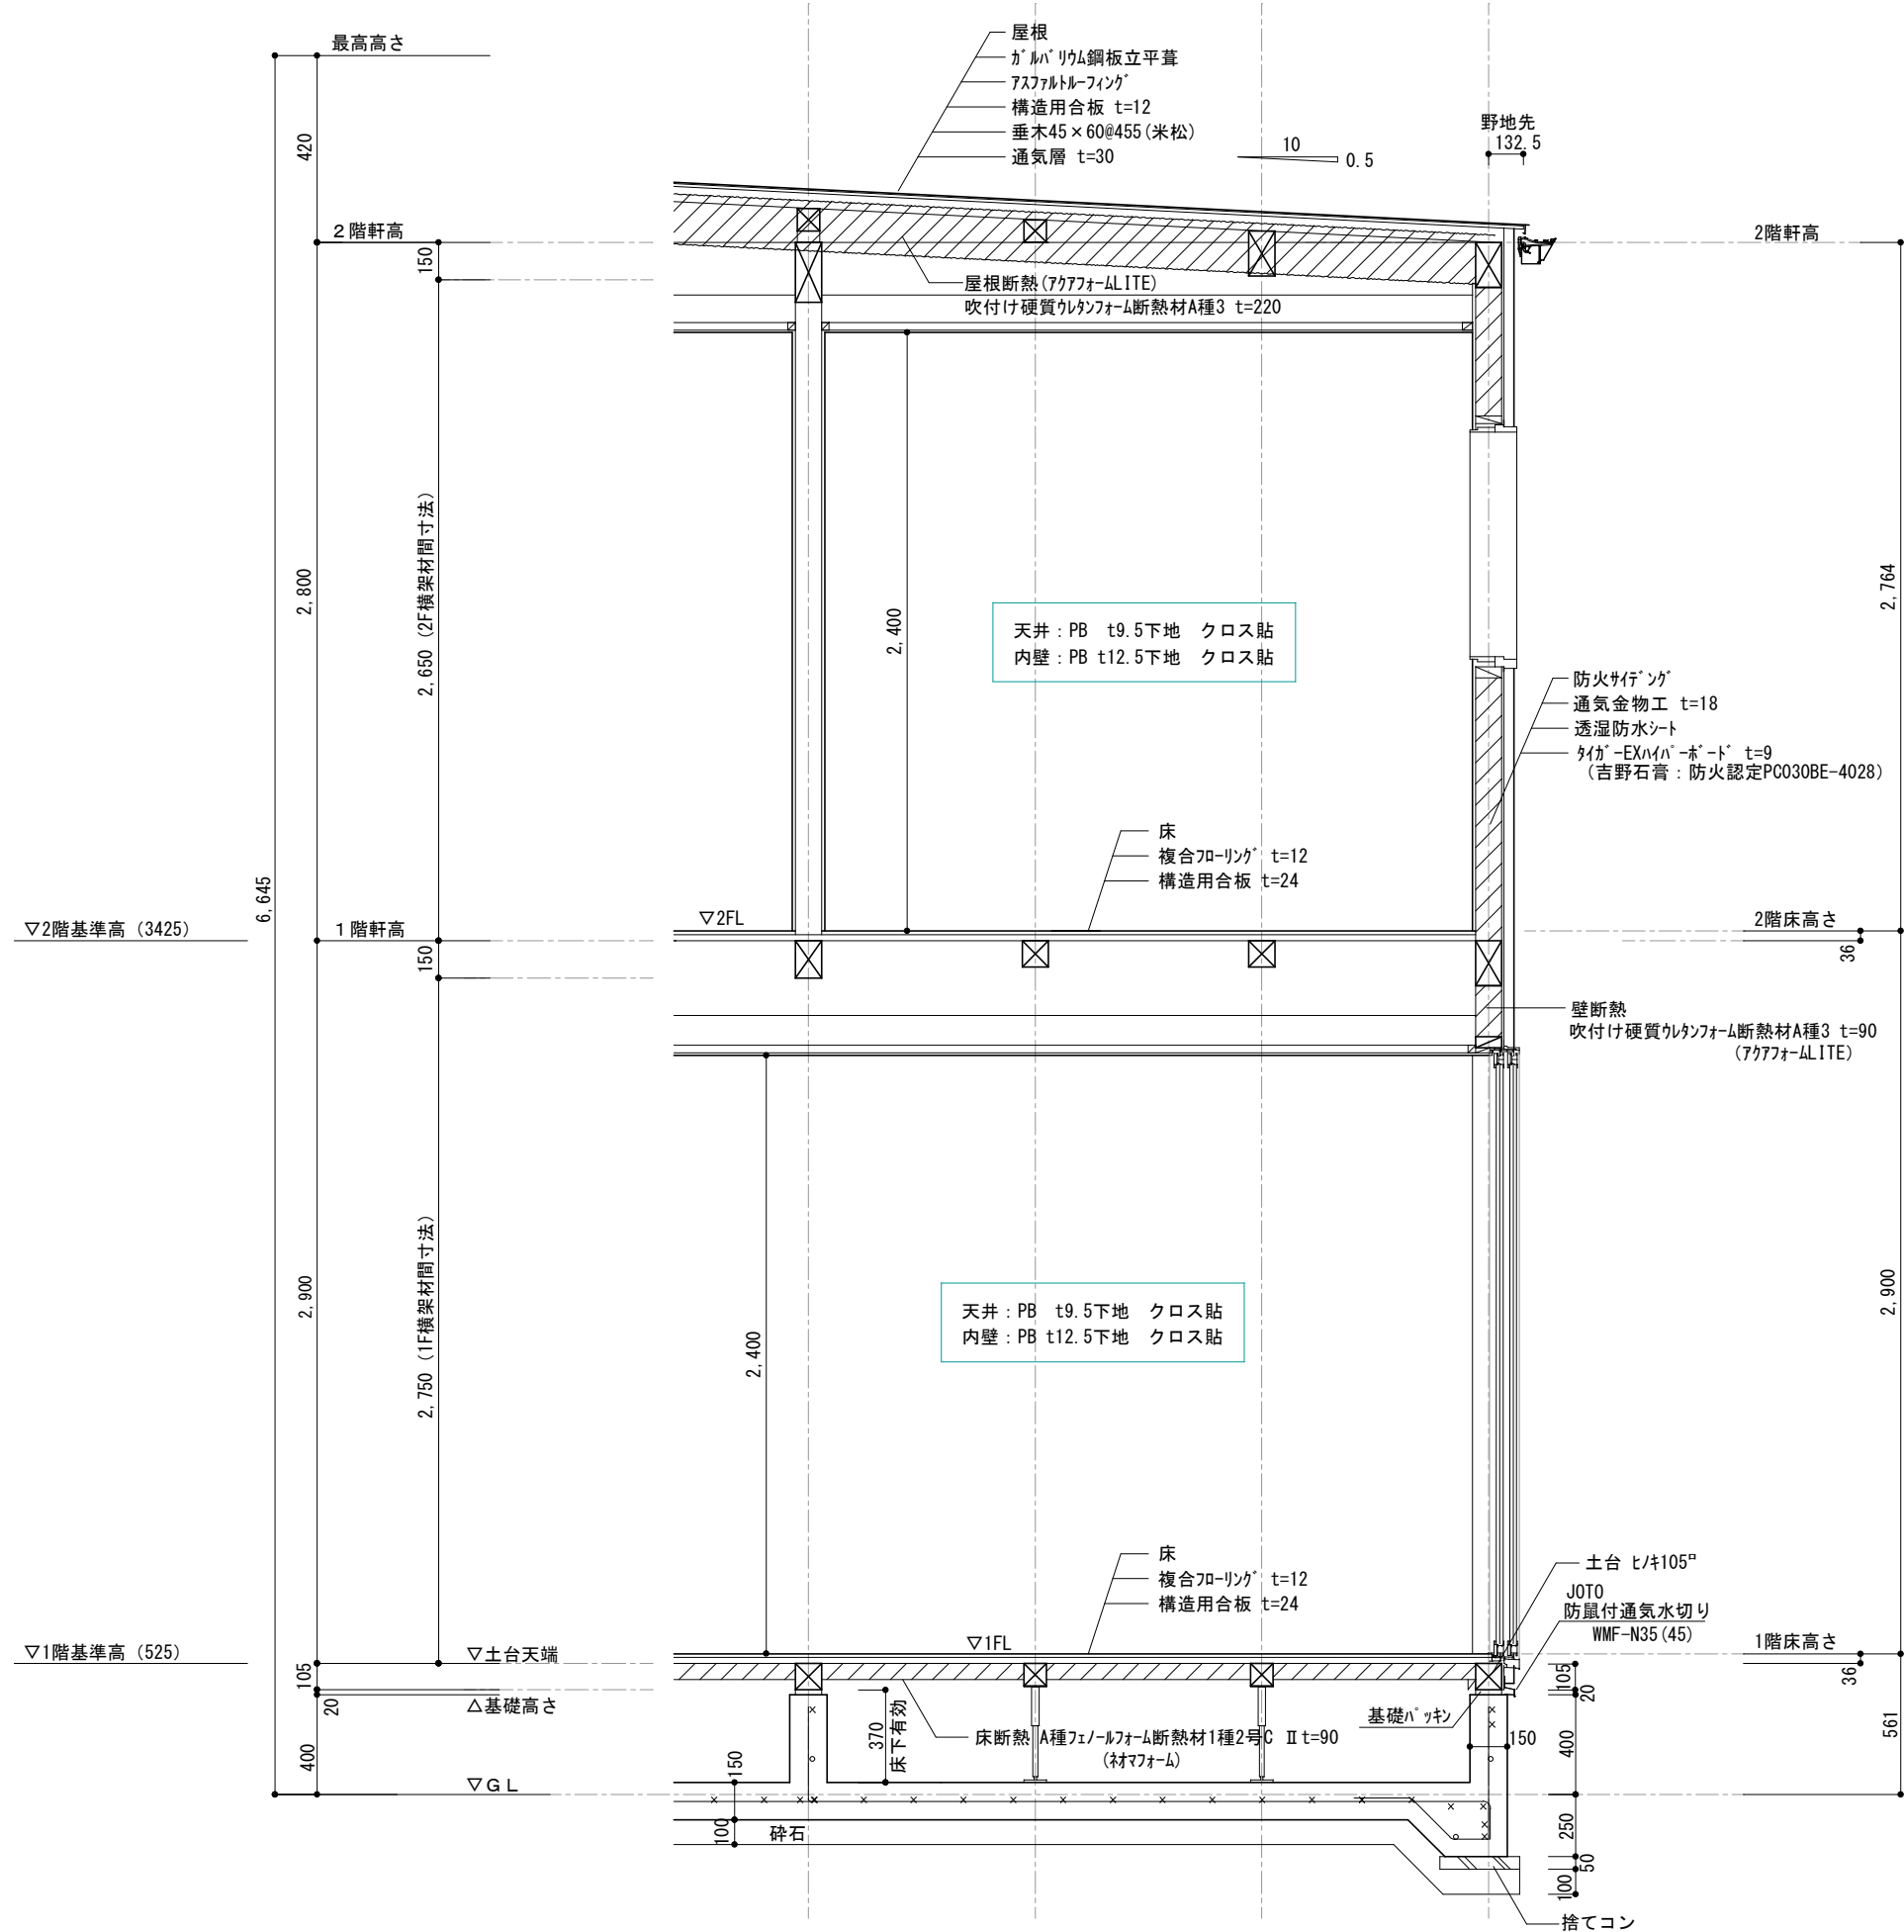


決定図

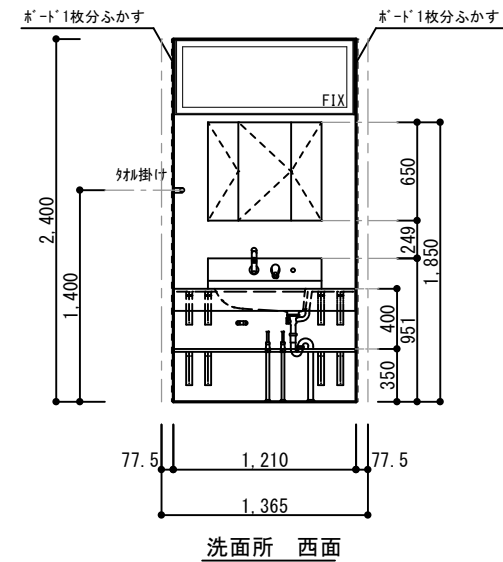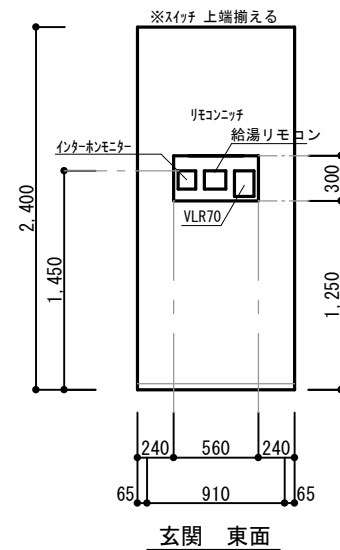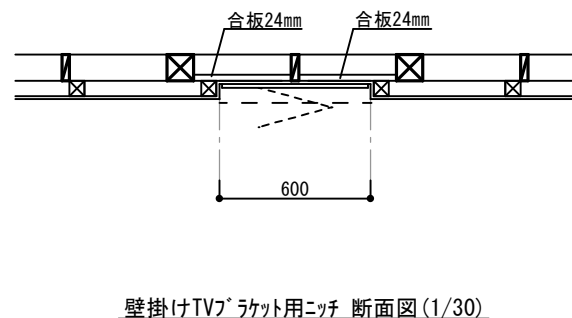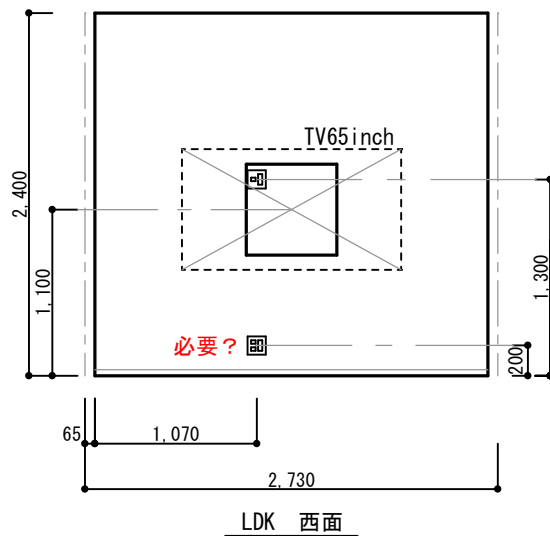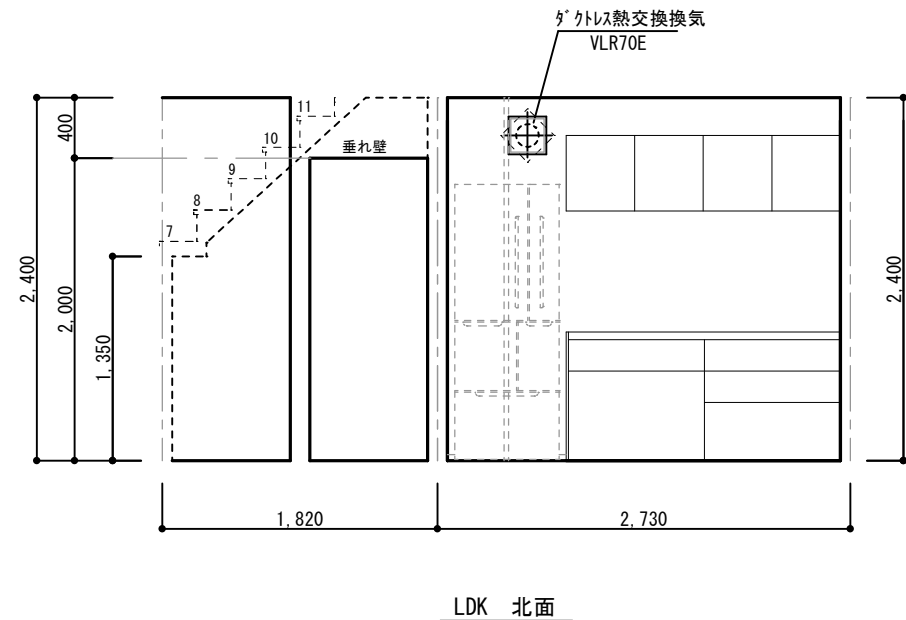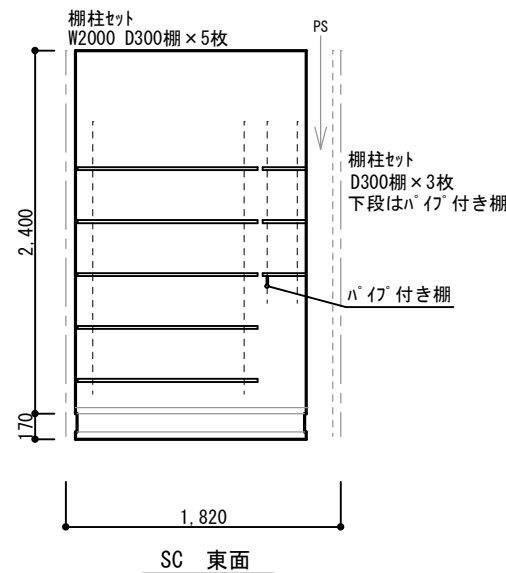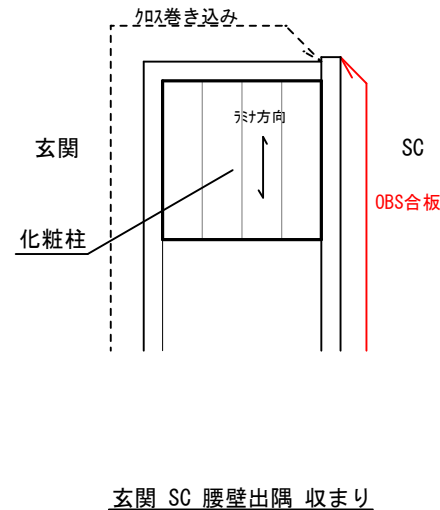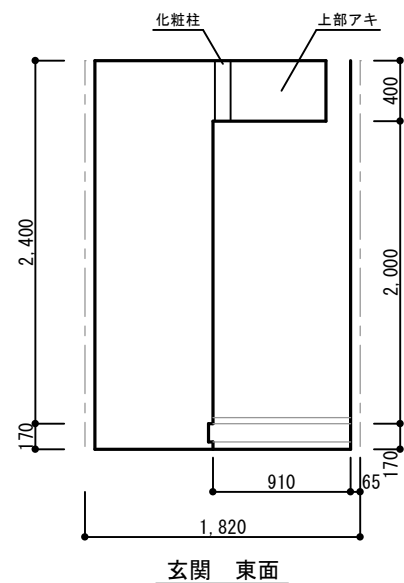


決定図

訂正	浜岡一級総合設計事務所 一級建築士事務所 静岡県知事登録第 (10)2441 号 一級建築士 大庄登録第 365879 号 西原利昌	LIFEFUND PG HOUSE	株式会社 LIFEFUND InDesign office 一級建築士事務所 事務所登録 (2) 第7595号 一級建築士登録 第179770号 鈴木 達男 〒432-8023 静岡県浜松市中央区鶴江3丁目70番23号	年月日 2026.1.4 縮尺 1/50	件名 寺本唯麻様 新築工事 図名 展開図-1		設計 酒井	IC	工事 青島	図番 6-1
----	--	----------------------	---	-------------------------------	---------------------------------	--	----------	----	----------	-----------

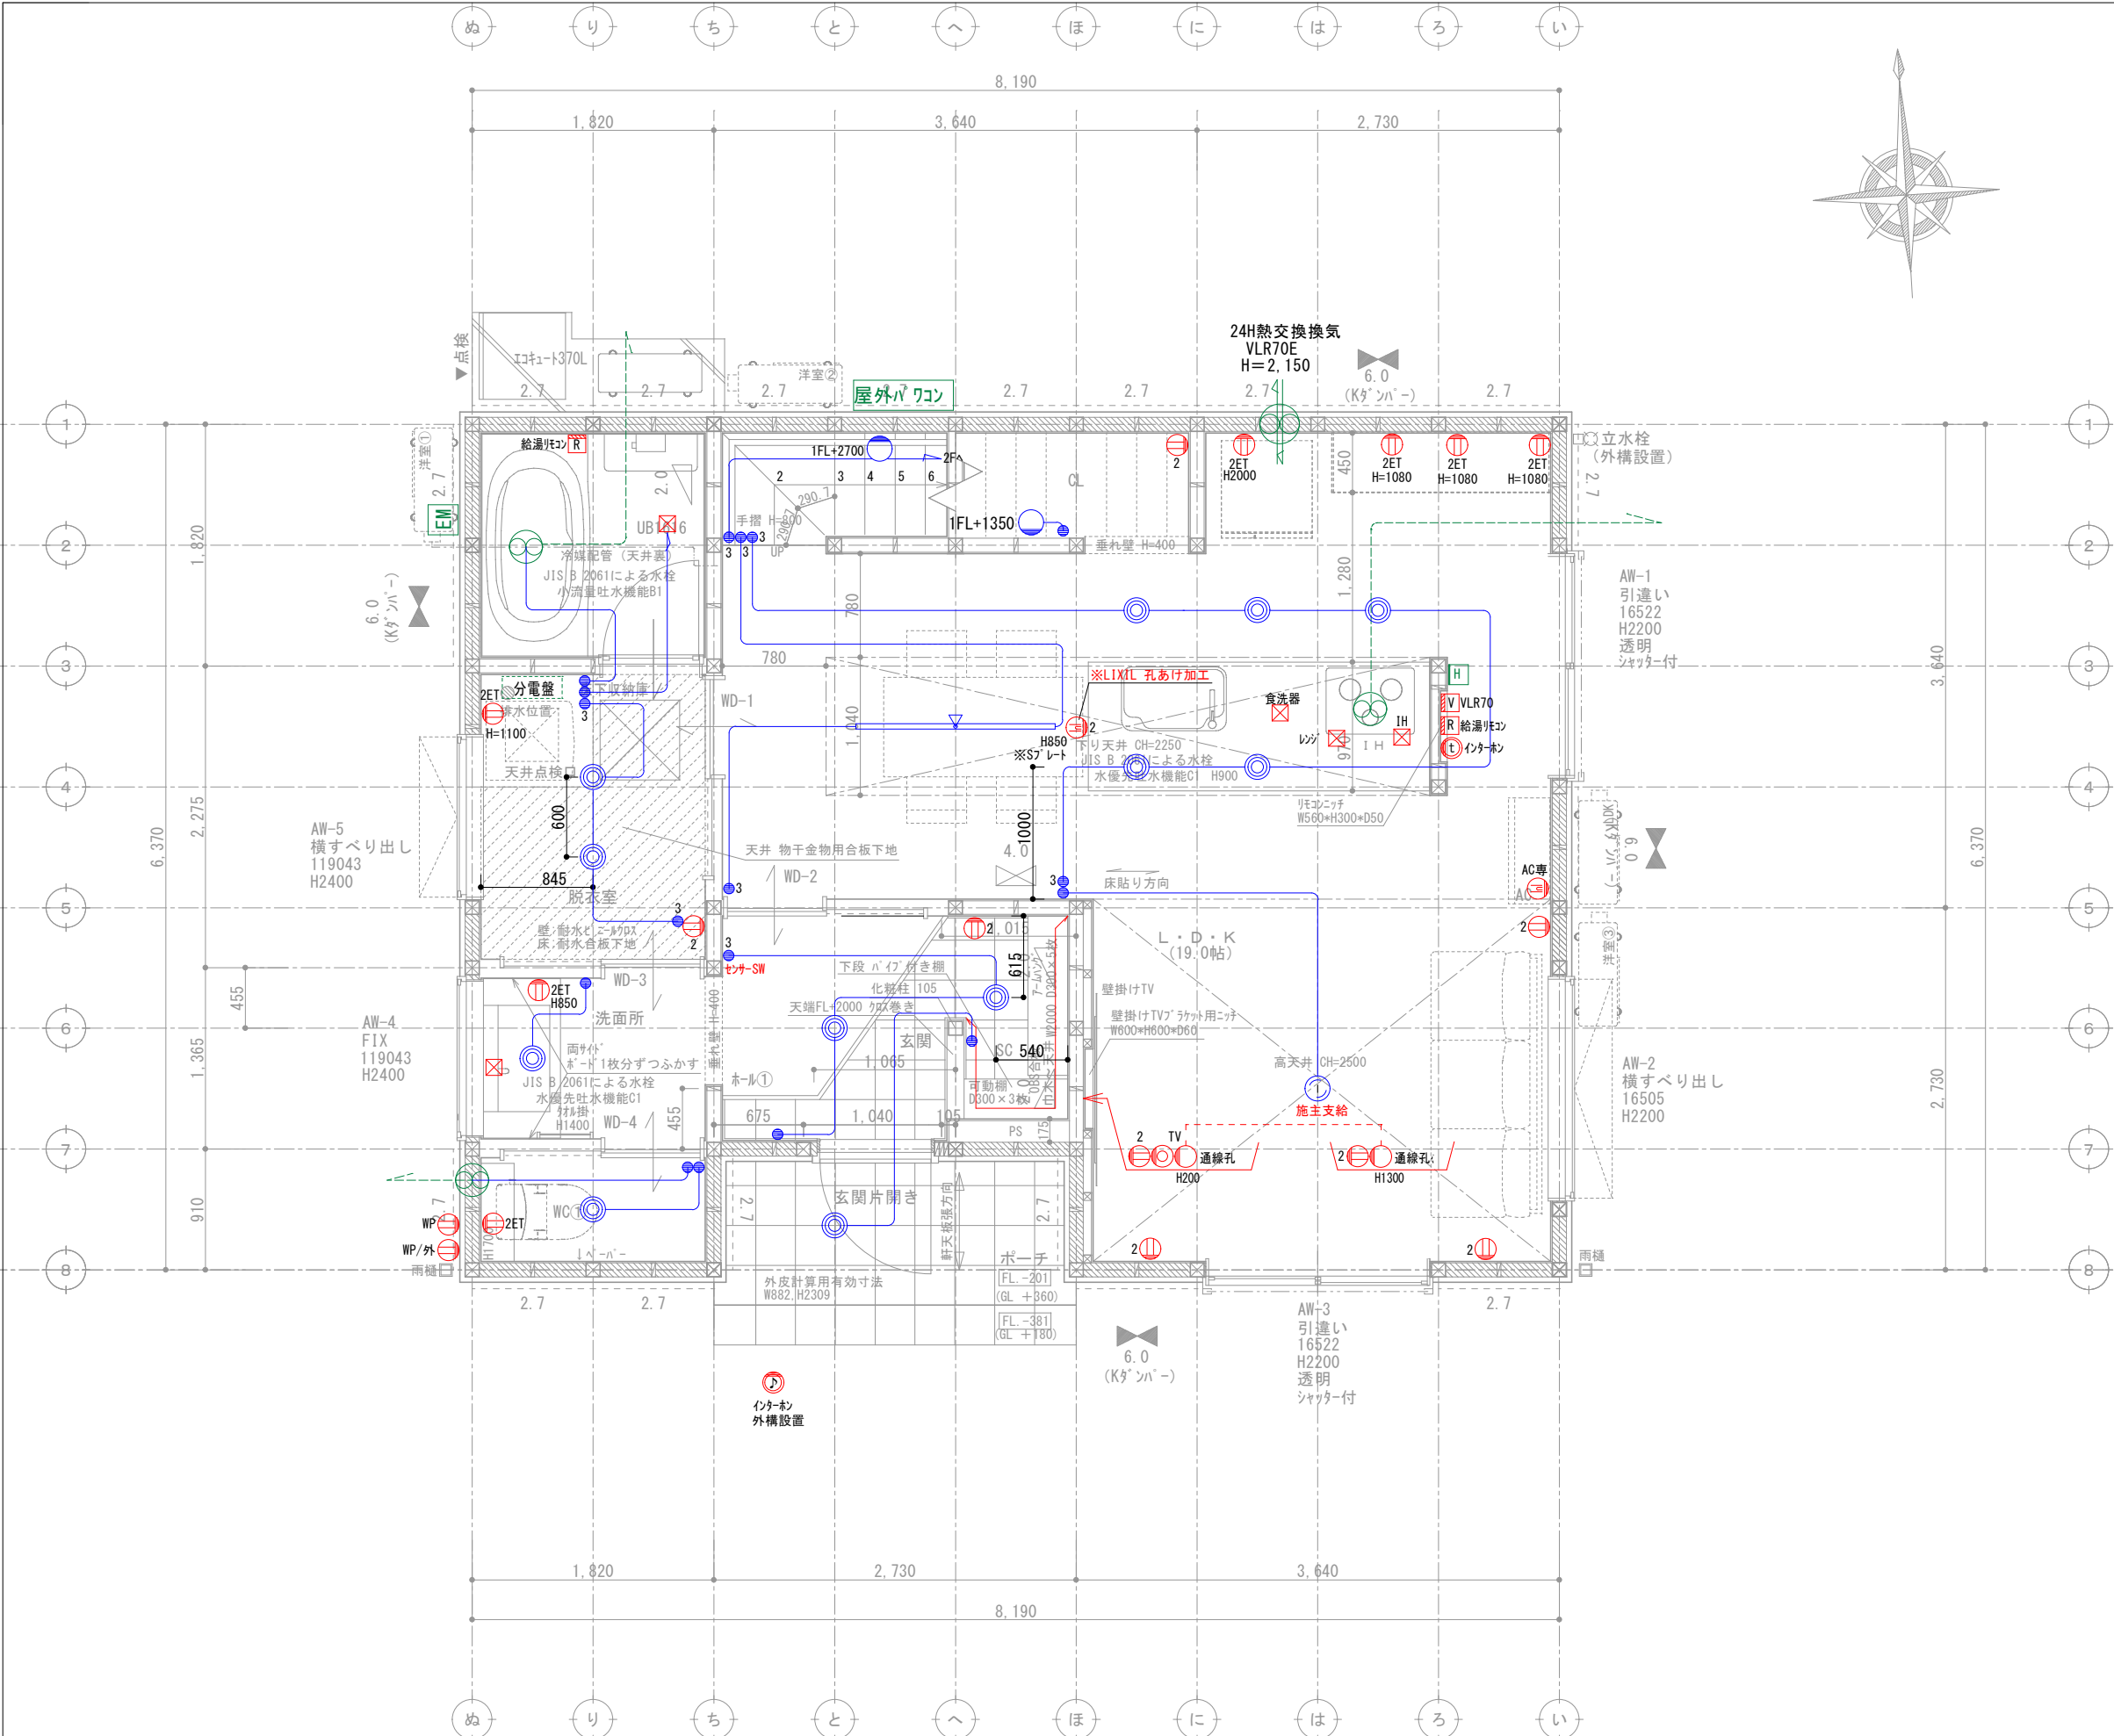

G2

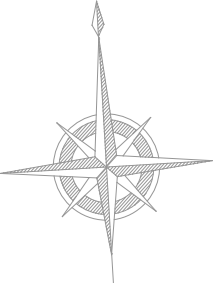

壁付け 住宅用火災報知器			数量
H 熱感知	熱感知器	電池式(単独型)	1
		露出型	
壁付け 住宅用火災報知器			数量
S 煙感知	煙感知器	電池式(単独型)	
		露出型	

- ※ 煙感知器は壁・梁より600mm以上離す
壁に取付ける場合、
天井から150mm以上500mm以内離す
換気扇・エアコン吹出口から1500mm以上離す
- ※ 全室LED照明とする。
- ※ 標準天井高さ2,400
- ※ 特記無きガラスは型ガラス

* 凡例

管柱 (105×105)

K&Nパイプ
(3.30fix FRM-0641)

片筋違い
(2.00倍 45×90)
(例 左:柱脚 右:柱頭)

たすき掛筋違い
(4.00倍 45×90)

構造用合板 (2.70倍)
(t=9 材質:EXハイバード)

床点検口

天井点検口

換気扇

熱交換換気扇VLR-70

- ※ 全室LED照明とし、調光制御を採用する。
- ※ 非居室の照明は人感センサーを採用する。
- ※ 階段寸法
蹴上：207.14 (2900÷14段)
踏面：227.5
有効幅：780
手摺出幅100mm以下

決定図



G2

壁付け 住宅用火災報知器			数量
H 熱感知	熱感知器	電池式(単独型)	
		露出型	
壁付け 住宅用火災報知器			数量
S 煙感知	煙感知器	電池式(単独型)	4
		露出型	

- ※ 煙感知器は壁・梁より600mm以上離す壁に取付ける場合、天井から150mm以上500mm以内離す換気扇・エアコン吹出口から1500mm以上離す
- ※ 全室LED照明とする。
- ※ 標準天井高さ2,400
- ※ 特記無きガラスは型ガラス

* 凡例


- 管柱 (105×105)
- Kタンパー (3.30倍 FRM-0641)
- 片筋違い (2.00倍 45×90) (例 左:柱脚 右:柱頭)
- たすき掛筋違い (4.00倍 45×90)
- 構造用合板 (2.70倍) (t=9 3枚 -EXハイパー-)
- 床点検口
- 天井点検口
- 換気扇
- 熱交換換気扇VLR-70

- ※ 全室LED照明とし、調光制御を採用する。
- ※ 非居室の照明は人感センサーを採用する。

アドバンスシリーズ			
スマートデザイン (外部)			
凡例			
1	コンセント	1ヶロ	
2	コンセント	2ヶロ	
3	コンセント	3ヶロ	
1ET	コンセント1ヶロ接地ターミナル付		
2ET	コンセント2ヶロ接地ターミナル付		
WP	コンセント	防水型	
	エアコン用コンセント		
	200V用コンセント		
WP	防雨入線プレート		
	スイッチ		
3	3路スイッチ		
4	4路スイッチ		
	直結電源		
TV	テレビ取出口		
TEL	電話取出口 (テレホンガイド)		
LAN	LAN取出口 (テレホンガイド)		
	壁照明		
R	リモコン (給湯関係・ルフロ)		
WH	メーター		
	分電盤		
t	チャイム		

- ※ACコンセント天井付け
- ※TVアンテナ工事
- ※スイッチはFL+1100、コンセントはFL+200

決定図

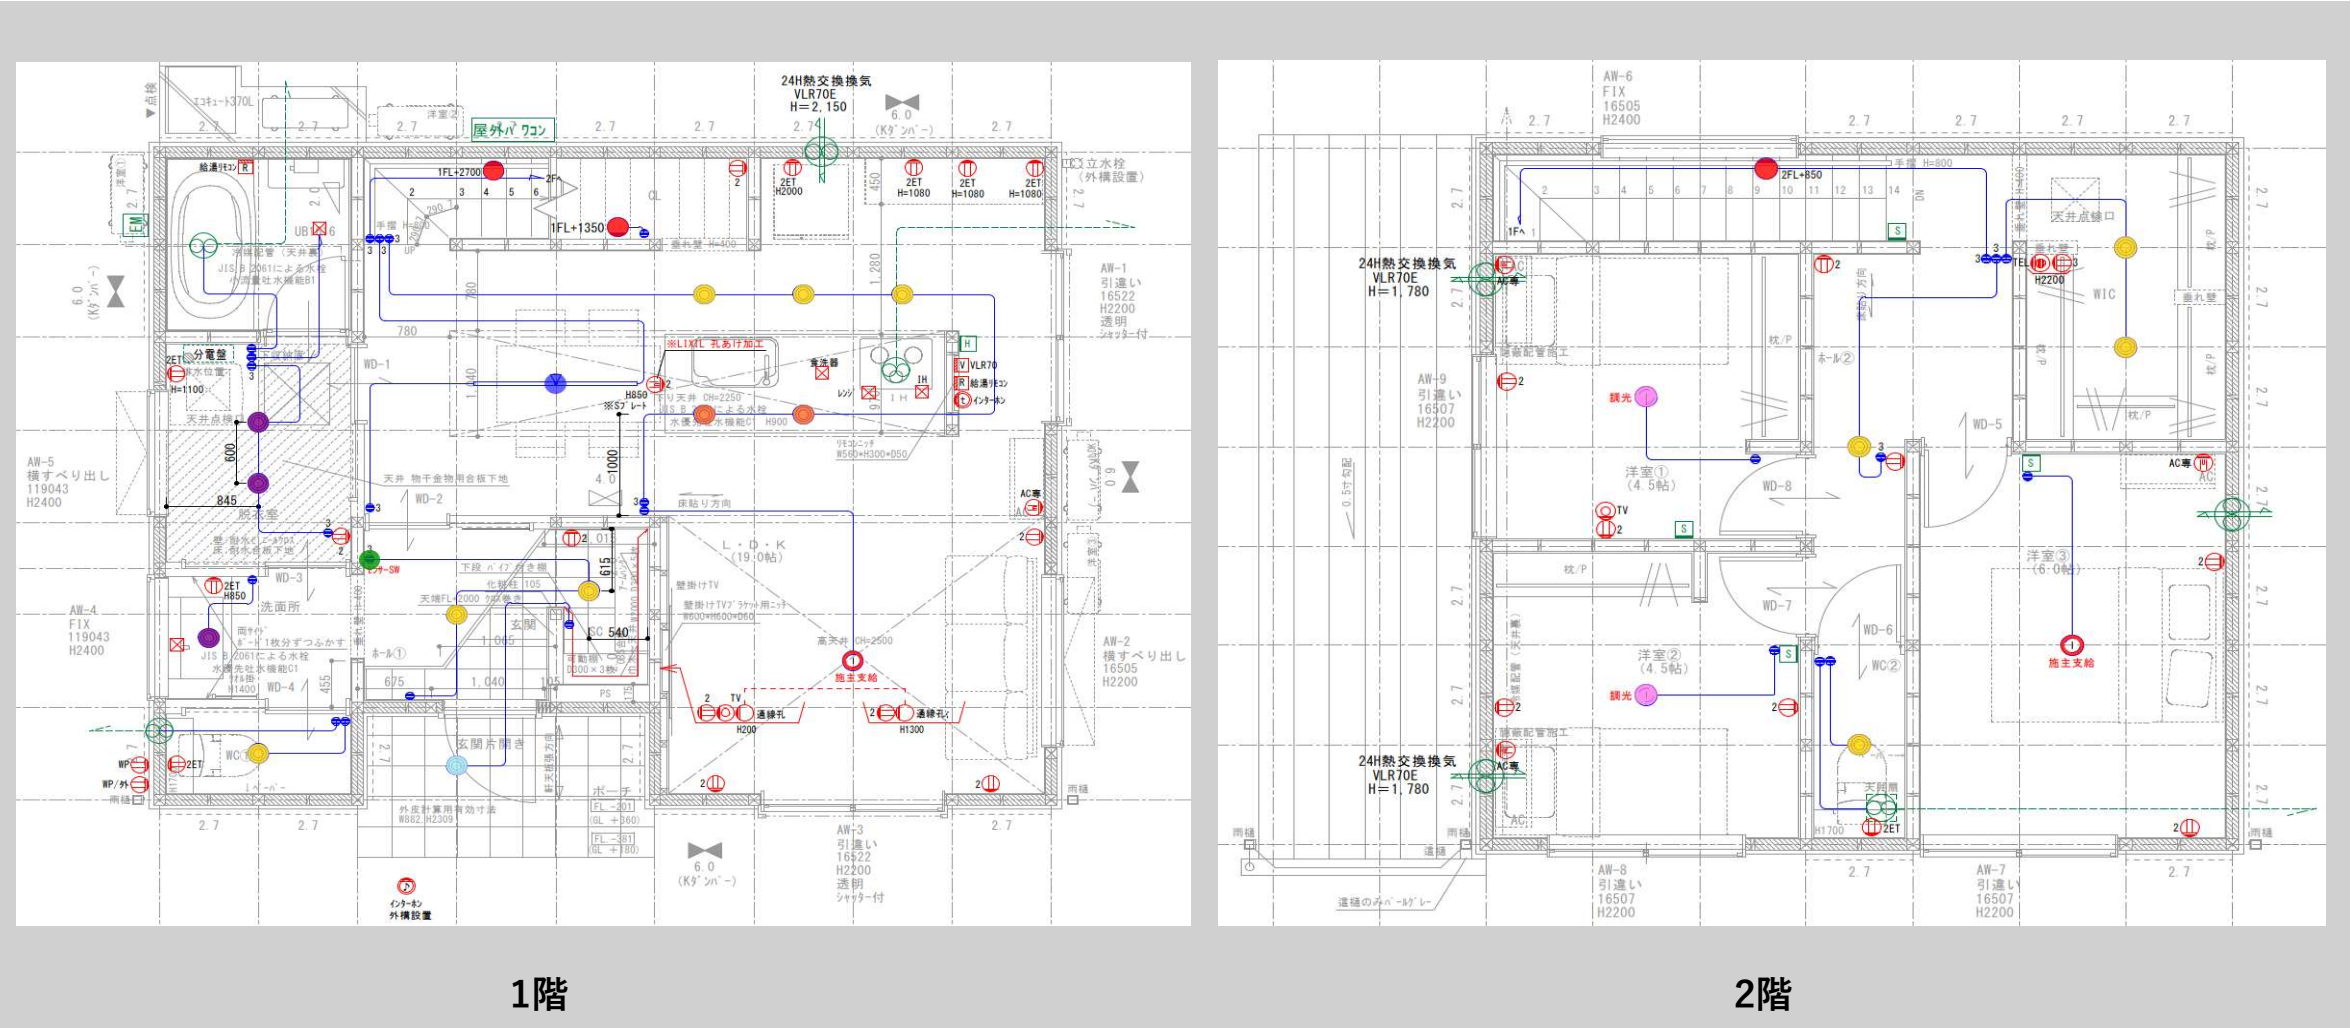

ドアホン：VL-SE31XL(Panasonic)



内部SW：アドバンス
マットホワイト



外部：スマートデ ザ インシリーズ
ブラック



ブラック

エコキュート リモコン



24時間換気 VLR-70



引っ掛けシーリング
○ × 2



ポーチ灯

● × 1

センサー付きダ ウンライト

DDL_6259YB

基本照明ダ ウンライト

● × 11

DDL_6132YW

脱衣室、洗面所

● × 4

ダ ウンライト

DDL_6132AW

LDK、洋室①②

● × 3

調光ダ ウンライト

DDL_6032YWG

CL、階段

● × 3

ブラケット

DBK_41544Y

玄関

● × 1

センサー-SW

WTA_14119W

LDK

● × 2

ダ ウンライト

DDL_6132YB

LDK

● × 1

レール照明

DP_02915K



高気密SB形 | 人感センサー
運動マルチタイプ

DDL-6259 YB
電球色 / 2700K Ra93(クラス2)

415 lm 7.7 W 53.8 lm/W

¥21,800(税抜) (LED内蔵)

LED LED 7.7W
白熱灯60W相当

- 銅板 白塗装
- アルミダイキャスト 黒塗装
- アクリル 乳白(マット)
- 径φ116 埋込穴φ100 埋込深75mm 0.5kg
- 14VA
- 点灯照度調節機能付(暗・明切)
- 点灯保持時間(1分)
- 拡散/ベネル付
- AC100V
- 光束維持時間40,000時間
- 取付可能天井厚5~25mm
- 調光器併用不可

[運動器具について]
LED調光タイプ60VAまで
LED非調光タイプ不可 蛍光灯不可
白熱灯60Wまで

強制 ON
ソフト
60°
0.1m
近接検知
100
80
準耐火
防雨形
遮光保護
機能付



COBタイプ | 高気密SB形

DDL-6132 YW
電球色 / 2700K Ra93(クラス2)

440 lm 4.6 W 95.6 lm/W

¥3,600(税抜) (LED内蔵)

LED LED 4.6W
白熱灯60W相当

- 銅板 白塗装
- アクリル 乳白(マット)
- 径φ116 埋込穴φ100 埋込深70mm 0.3kg
- 8VA
- 拡散/ベネル付
- AC100V
- 光束維持時間60,000時間
- 取付可能天井厚5~25mm
- 調光器併用不可

LED交換 不可
非調光
防雨形
遮光保護
機能付
0.1m
近接検知
100
70
準耐火



COBタイプ | 高気密SB形

DDL-6132 AW
温白色 / 3500K Ra93(クラス2)

480 lm 4.6 W 104.3 lm/W

¥3,600(税抜) (LED内蔵)

LED LED 4.6W
白熱灯60W相当

- 銅板 白塗装
- アクリル 乳白(マット)
- 径φ116 埋込穴φ100 埋込深70mm 0.3kg
- 8VA
- 拡散/ベネル付
- AC100V
- 光束維持時間60,000時間
- 取付可能天井厚5~25mm
- 調光器併用不可

LED交換 不可
非調光
防雨形
遮光保護
機能付
0.1m
近接検知
100
70
準耐火



COBタイプ | 高気密SB形

DDL-6032 YWG
電球色 / 2700K Ra93(クラス2)

440 lm 5.8 W 75.8 lm/W

¥4,600(税抜) (LED内蔵)

LED LED 5.8W
白熱灯60W相当

- 銅板 白塗装
- アクリル 乳白(マット)
- 径φ116 埋込穴φ100 埋込深71mm 0.3kg
- 7VA
- 拡散/ベネル付
- AC100V
- 調光可能(1%~100%)
- 調光にはLED専用調光器(別売)をご使用ください
- 光束維持時間60,000時間
- 取付可能天井厚5~25mm
- 調光器併用不可

LED交換 不可
調光
防雨形
遮光保護
機能付
0.1m
近接検知
100
80
準耐火



DBK-41544 Y
電球色 / 2700K-Ra83

定格光束 119lm 消費電力 4.6W 固有エネルギー消費効率 25.8lm/W

¥10,800-(税抜) (LED内蔵)

LED LED 4.6W
白熱灯60W相当

- 銅板 白塗装
- 径 120 出36mm 0.5kg
- 8VA
- AC100V
- 光源寿命40,000時間
- 調光器併用不可

カバー化粧ネジ式

LED交換 不可
非調光



3線 / 4線式

WTA14119W

壁取付 熱線センサー付自動スイッチ(観器)
(検知後連続動作時間 約10秒~30分可変形)
(明るさセンサー・手動スイッチ付)(マットホワイト)

3A 100V AC

プレート別売



COBタイプ | 高気密SB形

DDL-6132 YB
電球色 / 2700K Ra93(クラス2)

370 lm 4.6 W 80.4 lm/W

¥3,600(税抜) (LED内蔵)

LED LED 4.6W
白熱灯60W相当

- 銅板 黒塗装
- アクリル 乳白(マット)
- 径φ116 埋込穴φ100 埋込深70mm 0.3kg
- 8VA
- 拡散/ベネル付
- AC100V
- 光束維持時間60,000時間
- 取付可能天井厚5~25mm
- 調光器併用不可

LED交換 不可
非調光
防雨形
遮光保護
機能付
0.1m
近接検知
100
70
準耐火



フィードインボックス・エンドキャップセット

ダクトレール1.5m用
DP-02915 K
¥8,800(税抜)

- アルミ型材 黒アルマイト
- 巾33 ダクト長1500 全長1603 高19mm
- 2P 15A 125V
- フィードインボックス・エンドキャップ1個付

照明器具
施主手配

決定図


PG House

寺本唯麻 様邸新築工事


Lighting Plan

2026.1.4

(図面 7-3)

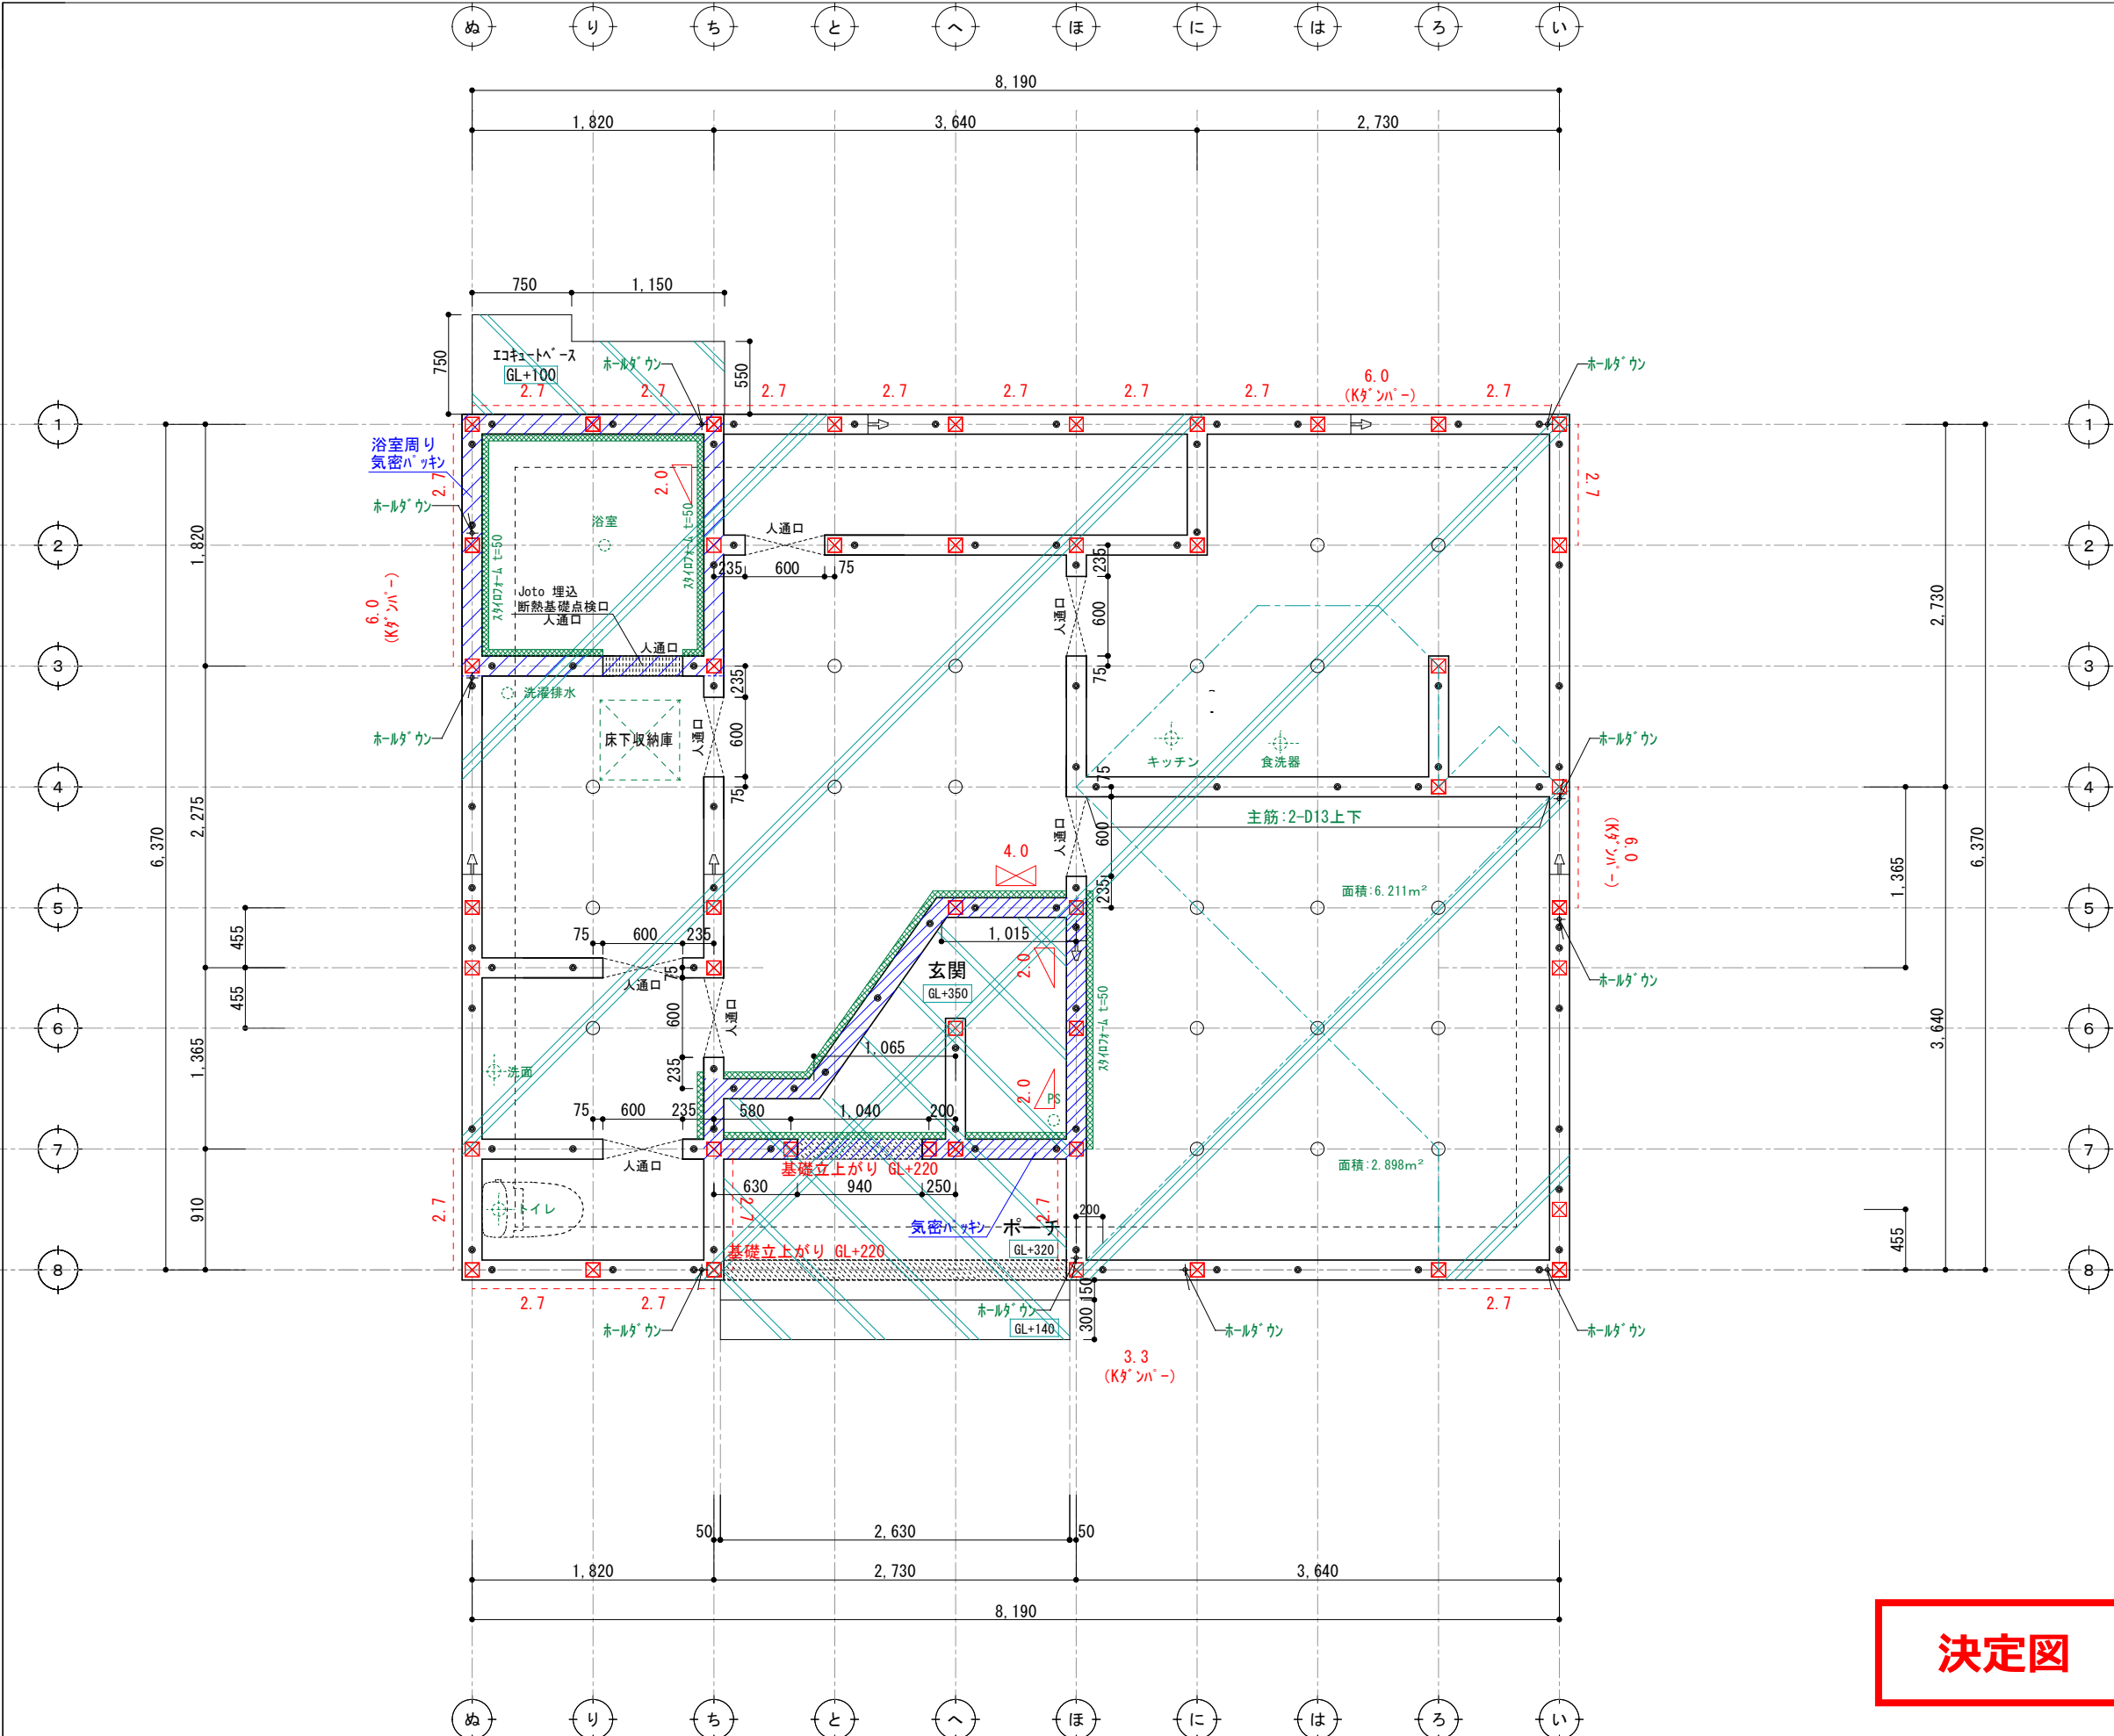

構造体ベースコンクリート t=150

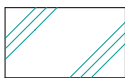


後打ち土間コン



アンカーボルトの配置
土台切れの箇所より150mm
土台の継手及び仕口の端部より150mm
耐力壁の端部、筋交いの脚部より150mm
1.82m以下の間隔
250mm以上埋込み
基礎天端より120mm

筋かい凡例
柱脚 柱頭 筋かい
たすき掛け筋かい
構造用パネル

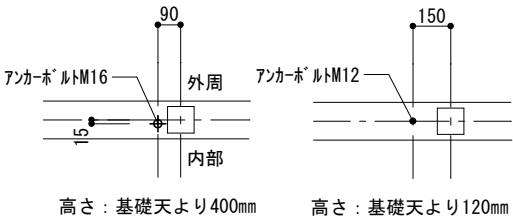

高さ：基礎天より400mm

高さ：基礎天より120mm

ホールダウン用アンカーボルト配置

アンカーボルト配置

※Kダンパーの取り付け柱の土台アンカーボルトは柱芯より200mm離すこと







凡例
通し柱 (105*105) 管柱 (105*105)
● アンカーボルトM12 L=400
+ ホールダウンアンカーM16 L=800
柱芯より90mm 280mm以上埋め込み
(カナイフリストアンカーボルトM16)
⊕ 鋼製束
→ 土台ジョイント
▨ ベースコンクリート (t=150)
▨ 後打ちコンクリート

基礎伏図について特記なき場合に限り下記による。

1. コンクリート：呼び強度 21N/mm²
2. 鉄筋：SD295A
3. 設計地耐力：fe=20kN/m²
地耐力計測後、不足の場合は相当の改良を行い、満たすものとする。
4. 基礎の位置は、芯振分けとする。
5. 玄関・S/C・UB周囲の基礎天端は気密パッキン施工（網掛け部）とし、その他の基礎天端は基礎パッキン施工とする。
6. 設備配管の屋内への取り入れは基礎立上り部のスリーブによる。

決定図

訂正	浜岡一級総合設計事務所 一級建築士事務所 静岡県知事登録第 (10)2441 号 一級建築士 大臣登録第 365879 号 西原利昌	LIFEFUND PG HOUSE	株式会社 LIFEFUND InDesign office 一級建築士事務所 事務所登録 (2) 第7595号 一級建築士登録 第179770号 鈴木 達男 〒432-8023 静岡県浜松市中央区鴨江3丁目70番23号	年月日 2026.1.4 縮尺 1/50	件名 寺本唯麻様 邸新築工事 図名 基礎伏図		設計 酒井	IC	工事 青島	図番 B-1
----	--	----------------------	---	-------------------------------	---------------------------------	--	----------	----	----------	-----------

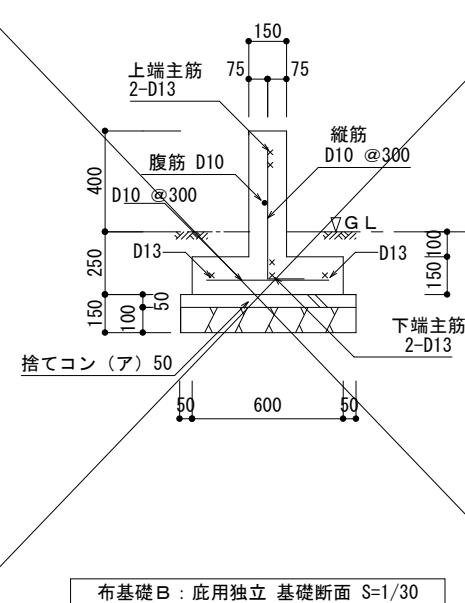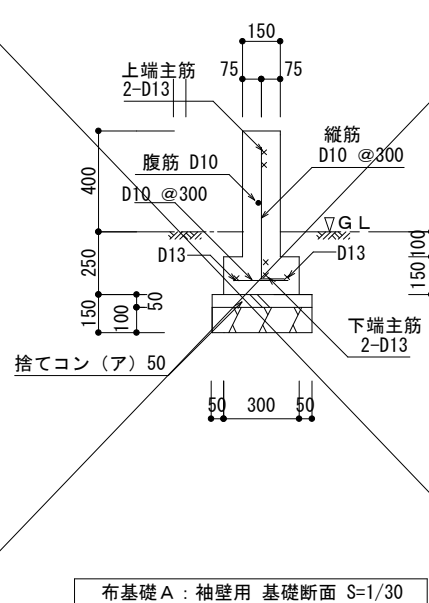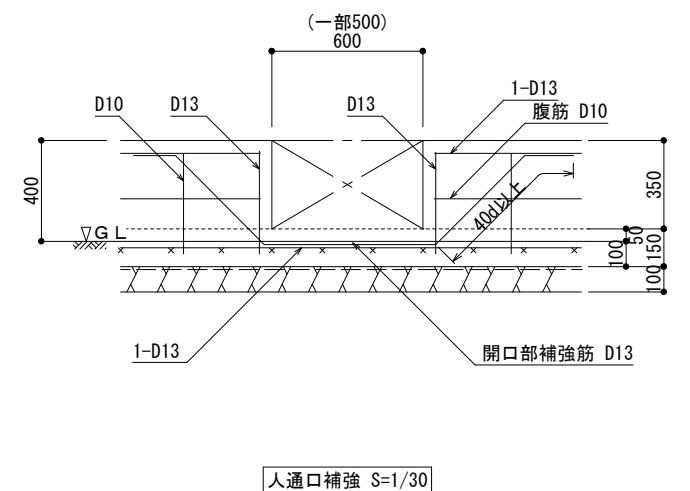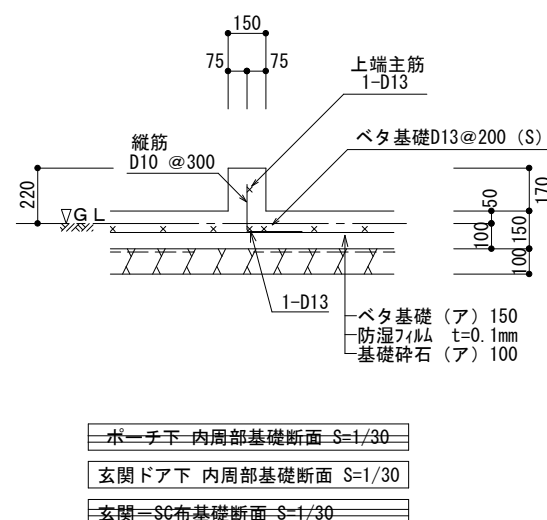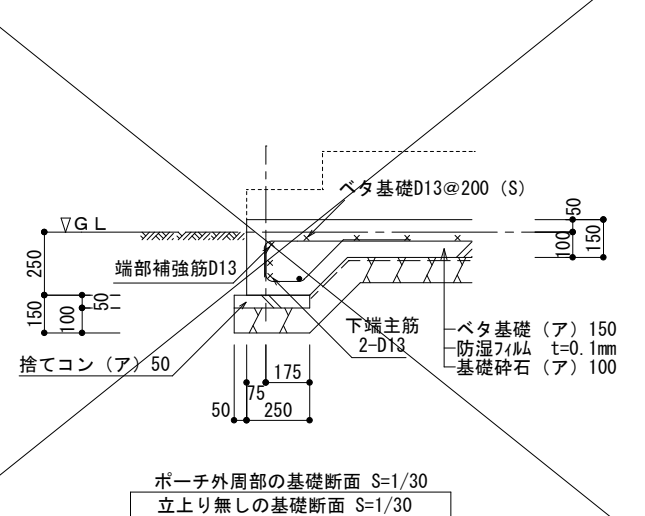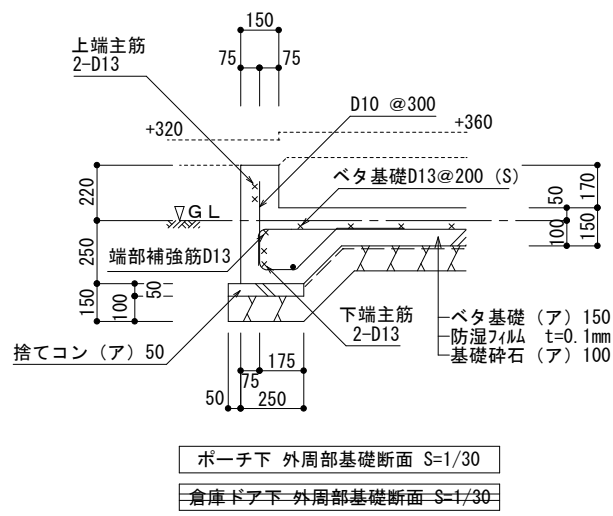


基礎の寸法 及び 配筋の検定方法	基礎立上り配筋は、 (財)日本住宅・木材技術 センター発行のスパン表 (増補版)による。 ベタ基礎スラブ配筋は、 まもりすまい保険設計施工 基準同解説のベタ基礎配筋表 による。具体的な寸法・配 筋は基礎詳細図参照。
---------------------------------------	--


- ・ D10を示す。
- × ・ D13を示す。

※使用しない断面は

決定図

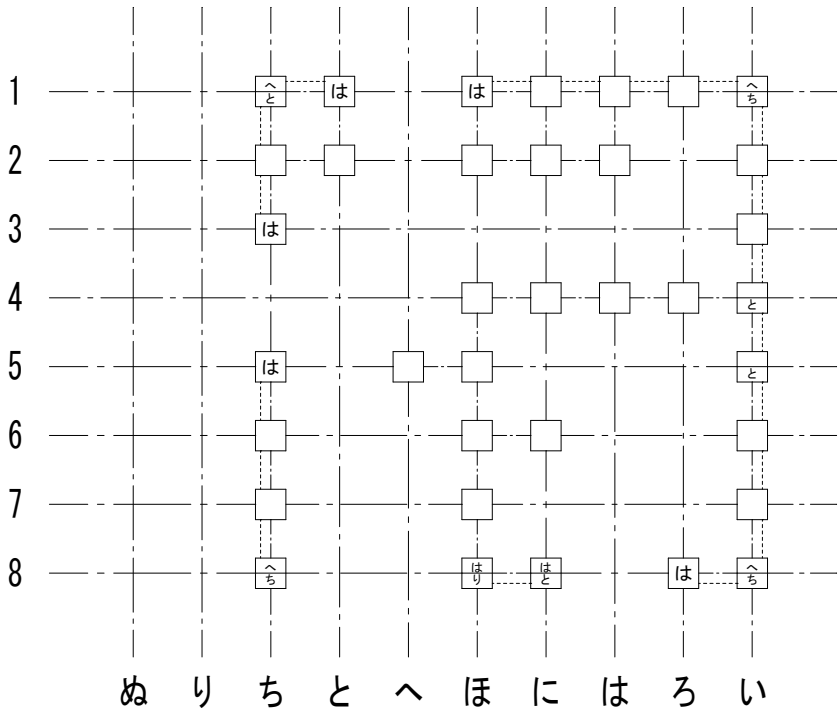

2階柱壁伏図

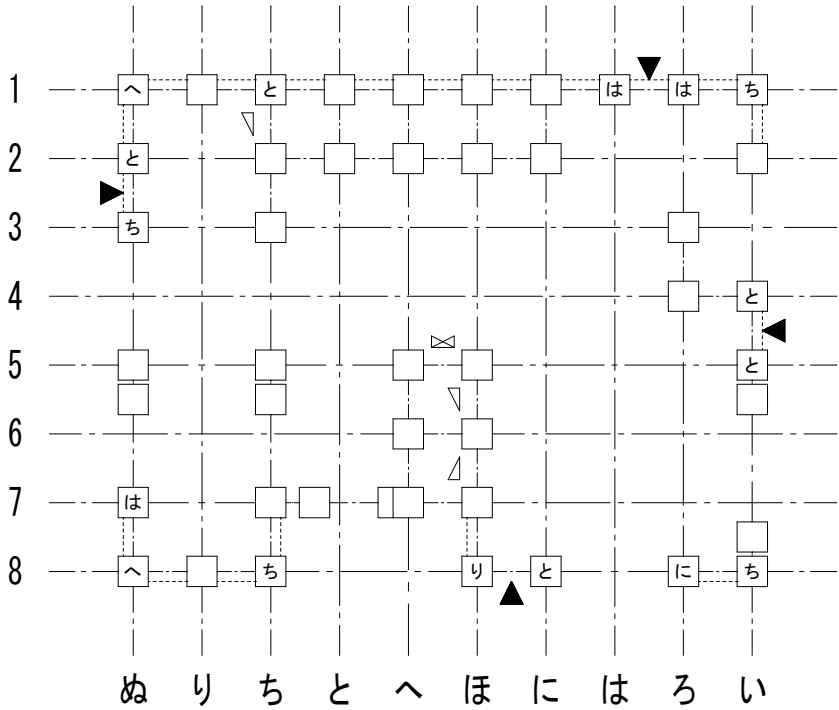

1階柱壁伏図

接合部凡例				*接合部凡例はユーザ設定されたものです。	
記号	仕様（カナイ金物）		N	倍率	
SBCP	スリムビルドコーナー75, チビクリCK(化粧柱の場合)		0.00	1.00	
SBCP	スリムビルドコーナー75, チビクリCK(化粧柱の場合)		0.65	1.00	
SBCP	は	スリムビルドコーナー75	1.00	1.00	
ARCG	に	アレントコーナー合板用	1.40	2.20	
ARCG	ほ	アレントコーナー合板用	1.60	2.20	
ARCG	へ	アレントコーナー合板用	1.80	2.20	
HD15	と	ブレイブホールダウン B-HD15	2.80	3.60	
HD20	ち	ブレイブホールダウン B-HD20	3.70	4.70	
HD25	り	ブレイブホールダウン B-HD25	4.70	4.80	
HD30	ぬ	ブレイブホールダウン B-HD30	5.60	7.20	
J1	る	腰掛け蟻若しくは大入れ蟻掛け+羽子板ボルト、短冊金物		1.90	
J2	を	腰掛け蟻若しくは大入れ蟻掛け+羽子板ボルト、短冊金物×2		3.00	

※表示なき金物は「は」とする。

梁継手・仕口用

梁継手・仕口用

接合部凡例				*接合部凡例はユーザ設定されたものです。	
記号	仕様（タナカ金物）		N	倍率	
FCP	フックコーナー, チビクリCK(化粧柱の場合)		0.00	1.00	
FCP	フックコーナー, チビクリCK(化粧柱の場合)		0.65	1.00	
FCP	は	フックコーナー	1.00	1.00	
GCP	に	シナコーナー	1.40	2.20	
GCP	ほ	シナコーナー	1.60	2.20	
GCP	へ	シナコーナー	1.80	2.20	
HD15	と	ビス止めホールダウンU HD15	2.80	3.60	
HD20	ち	ビス止めホールダウンU HD20	3.70	4.70	
HD25	り	ビス止めホールダウンU HD25	4.70	4.80	
HD30	ぬ	ビス止めホールダウンU HD15×2 (HD35)	5.60	7.20	
J1	る	腰掛け蟻若しくは大入れ蟻掛け+羽子板ボルト、短冊金物		1.90	
J2	を	腰掛け蟻若しくは大入れ蟻掛け+羽子板ボルト、短冊金物×2		3.00	

※表示なき金物は「は」とする。


梁継手・仕口用

梁継手・仕口用

筋かいの種類に応じた筋かいの端部の接合部の仕様		
	筋かいの種類	接合部の仕様（構造方法）
イ	鉄筋φ9	柱又は横架材を貫通し、三角座金を介してナット締め、又は鋼板添え板を用い鋼板を柱及び横架材にCN90, 8本平打ち
ロ	筋かい:15×90	柱・横架材を欠き込み、柱・横架材双方に対してN65, 5本平打ち
ハ	筋かい:30×90	鋼板添え板t=1.6mmを筋かいに対してボルトφ12及びCN65, 3本平打ち、柱に対してCN65, 3本平打ち、横架材に対してCN65, 4本平打ち。筋かいプレートBP同等品
ニ	筋かい:45×90	鋼板添え板t=2.3mmを筋かいに対してボルトφ12及びスクリュー釘φ4.5L50, 7本平打ち、柱及び横架材に対してスクリュー釘φ4.5L50, 5本平打ち。筋かいプレートBP-2同等品
ホ	筋かい:90×90	柱又は横架材にボルトφ12mmを用いて一面剪断接合

胴差と通し柱の接合部の仕様		
	胴差と通し柱の条件	仕口
T1	通し柱の片側に胴差が来る場合	胴差を柱にかたぎ大入れ短ほぞ差しの上、羽子板ボルト、かね折り金物又は同等以上の仕口
T2	通し柱の両側に胴差が来る場合	胴差を柱にかたぎ大入れ短ほぞ差しの上、短冊金物又は、同等以上の仕口で胴差相互を緊結
T3	通し柱と胴差の接合部の近くに90×90以上の筋かいが来る場合(通し柱が建物の出隅にあるか、筋かい壁が外壁と直交して接する場合)	胴差を通し柱に、15KN用引き寄せ金物を水平に用いて緊結

決定図

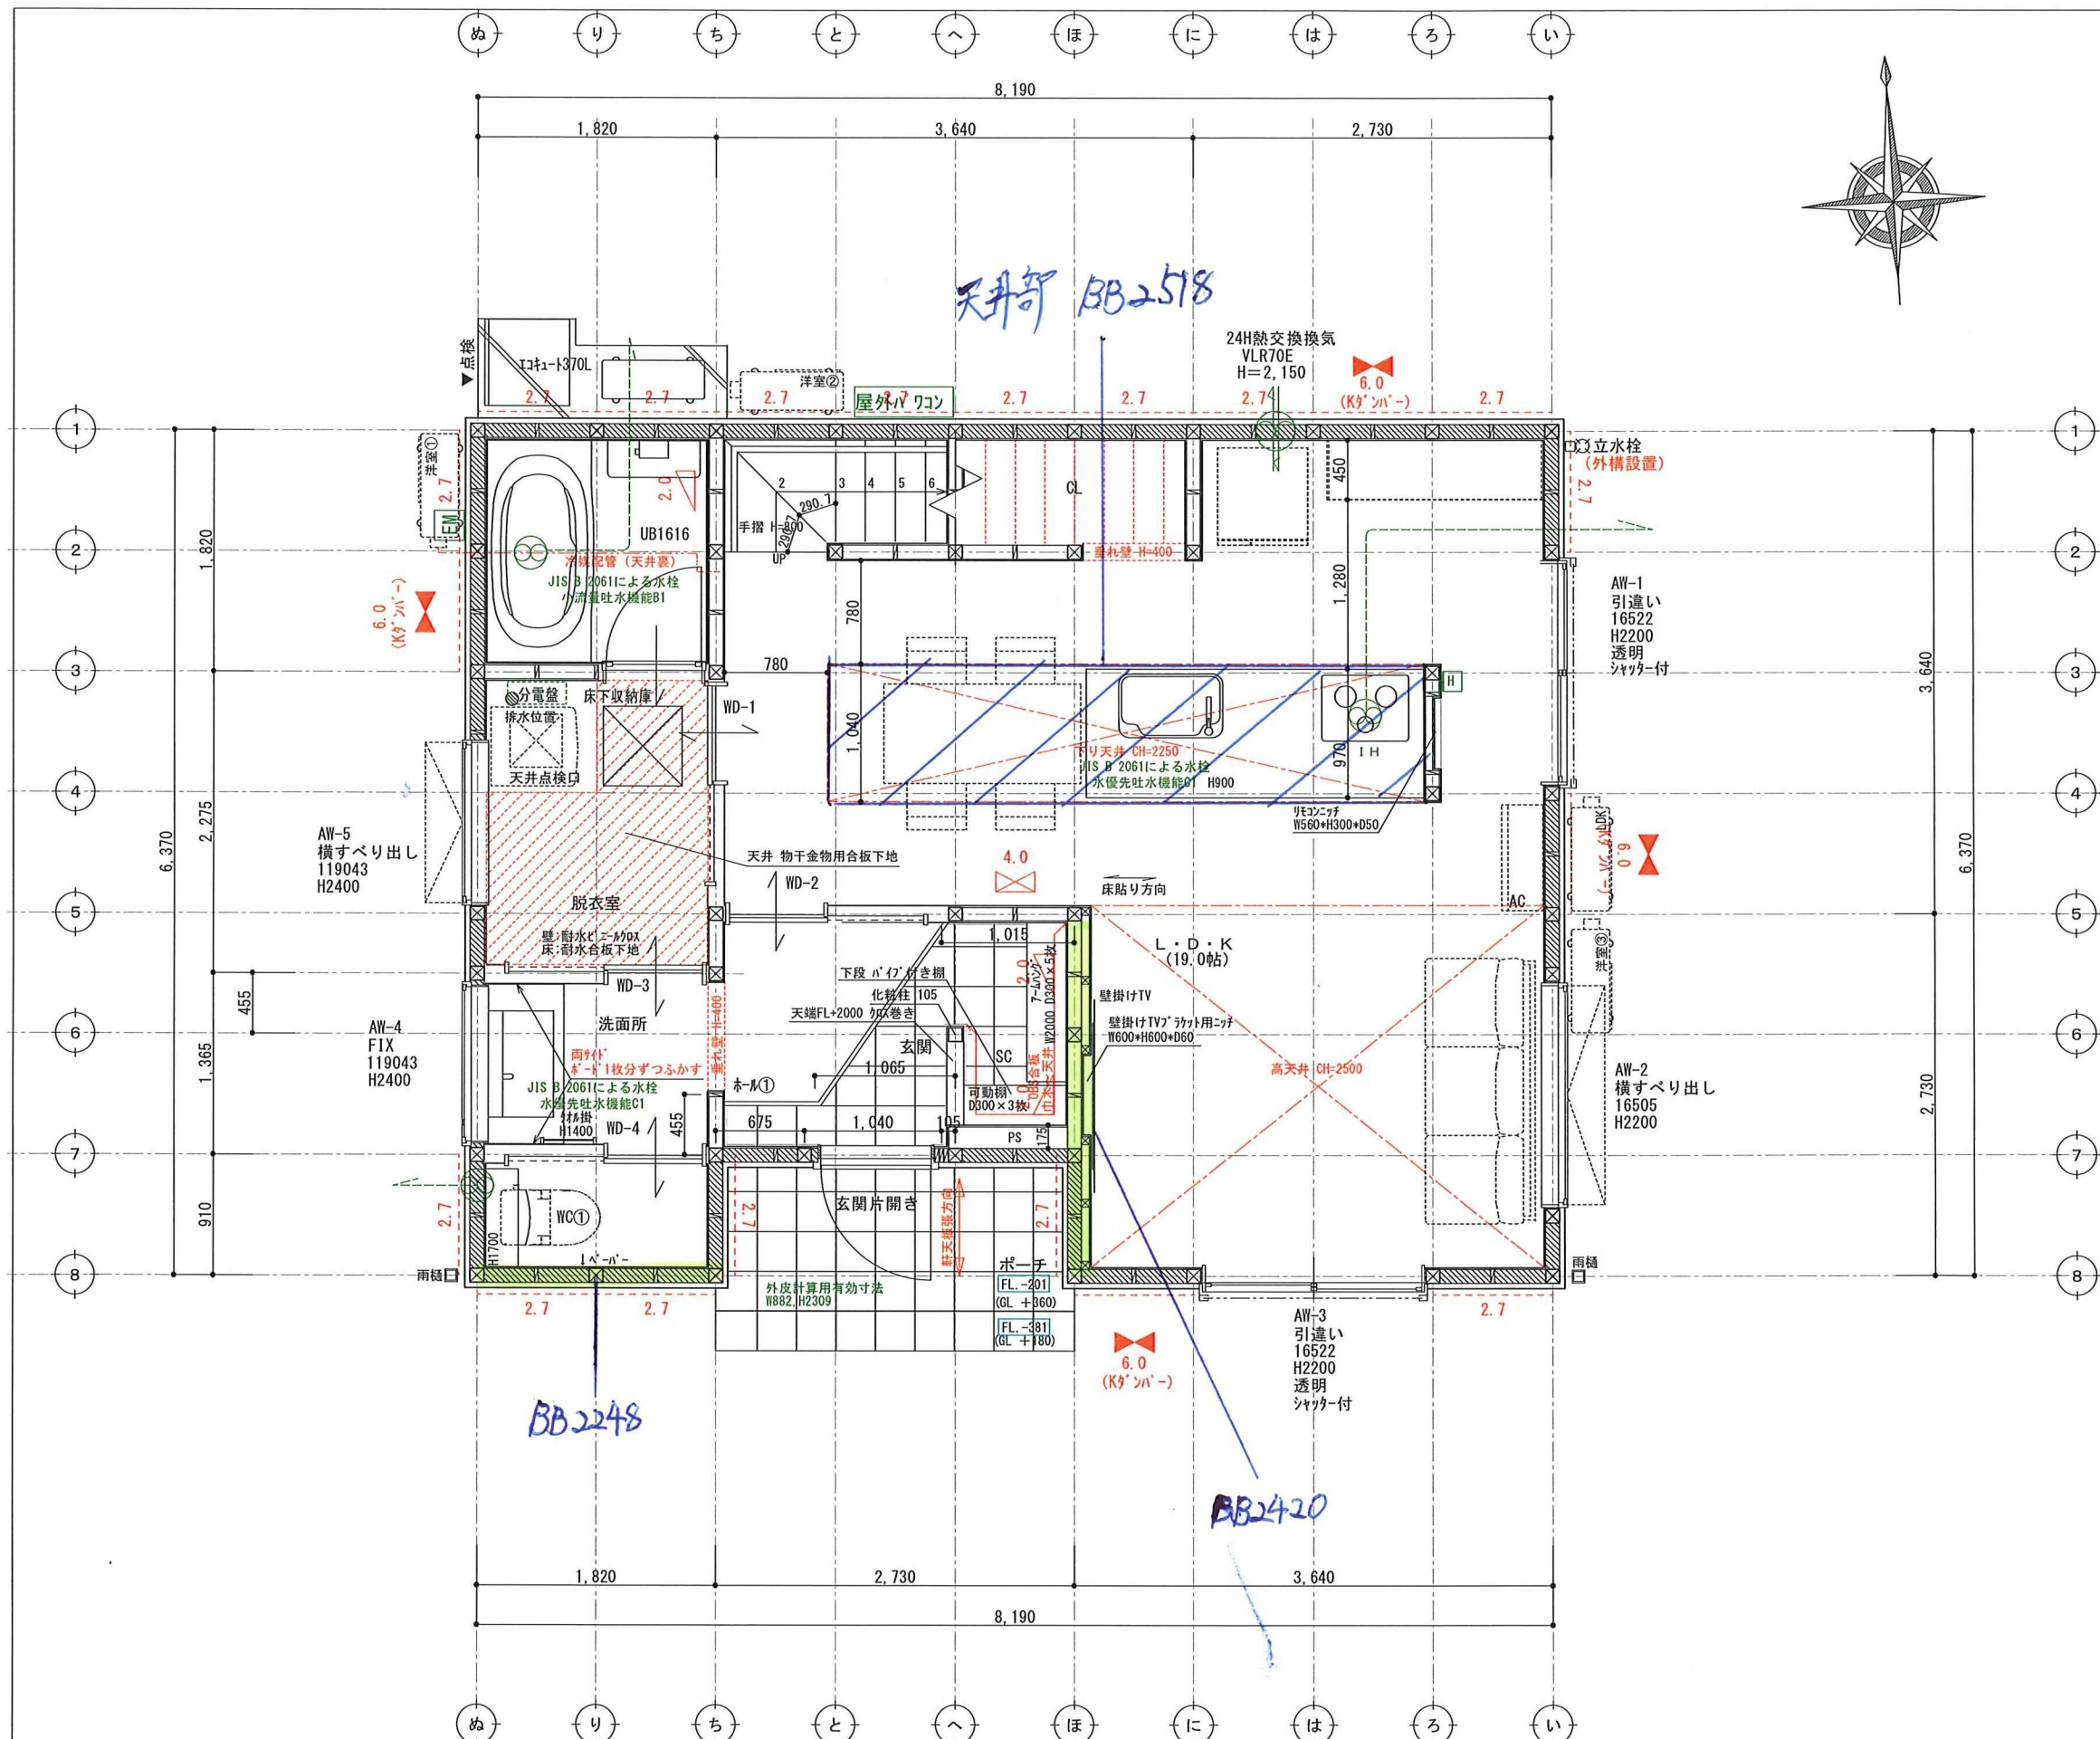

G2


壁付け 住宅用火災報知器			数量
[H] 熱感知	熱感知器	電池式(単独型)	1
	露出型		
壁付け 住宅用火災報知器			数量
[S] 煙感知	煙感知器	電池式(単独型)	
	露出型		

※ 煙感知器は壁・梁より600mm以上離す
壁に取付ける場合、
天井から150mm以上500mm以内離す
換気扇・エアコン吹出口から1500mm以上離す
※ 全室LED照明とする。
※ 標準天井高さ2,400
※ 特記無きガラスは型ガラス

- * 凡例
- ☒ 管柱 (105×105)
 - ≡ K'ンバ' (3.30倍 FRM-0641)
 - △ 片筋違い (2.00倍 45×90) (例 左:柱脚 右:柱頭)
 - ⊠ たすき掛筋違い (4.00倍 45×90)
 - 構造用合板 (2.70倍) (t=9 タイプ-EX/MIN-)
 - ◻ 床点検口
 - ⊠ 天井点検口
 - ⊕ 換気扇
 - ⊕ 熱交換換気扇VLR-70

※ 全室LED照明とし、調光制御を採用する。
※ 非居室の照明は人感センサーを採用する。
※ 階段寸法
蹴上: 207.14 (2900÷14段)
踏面: 227.5
有効幅: 780
手摺出幅100mm以下

決定図

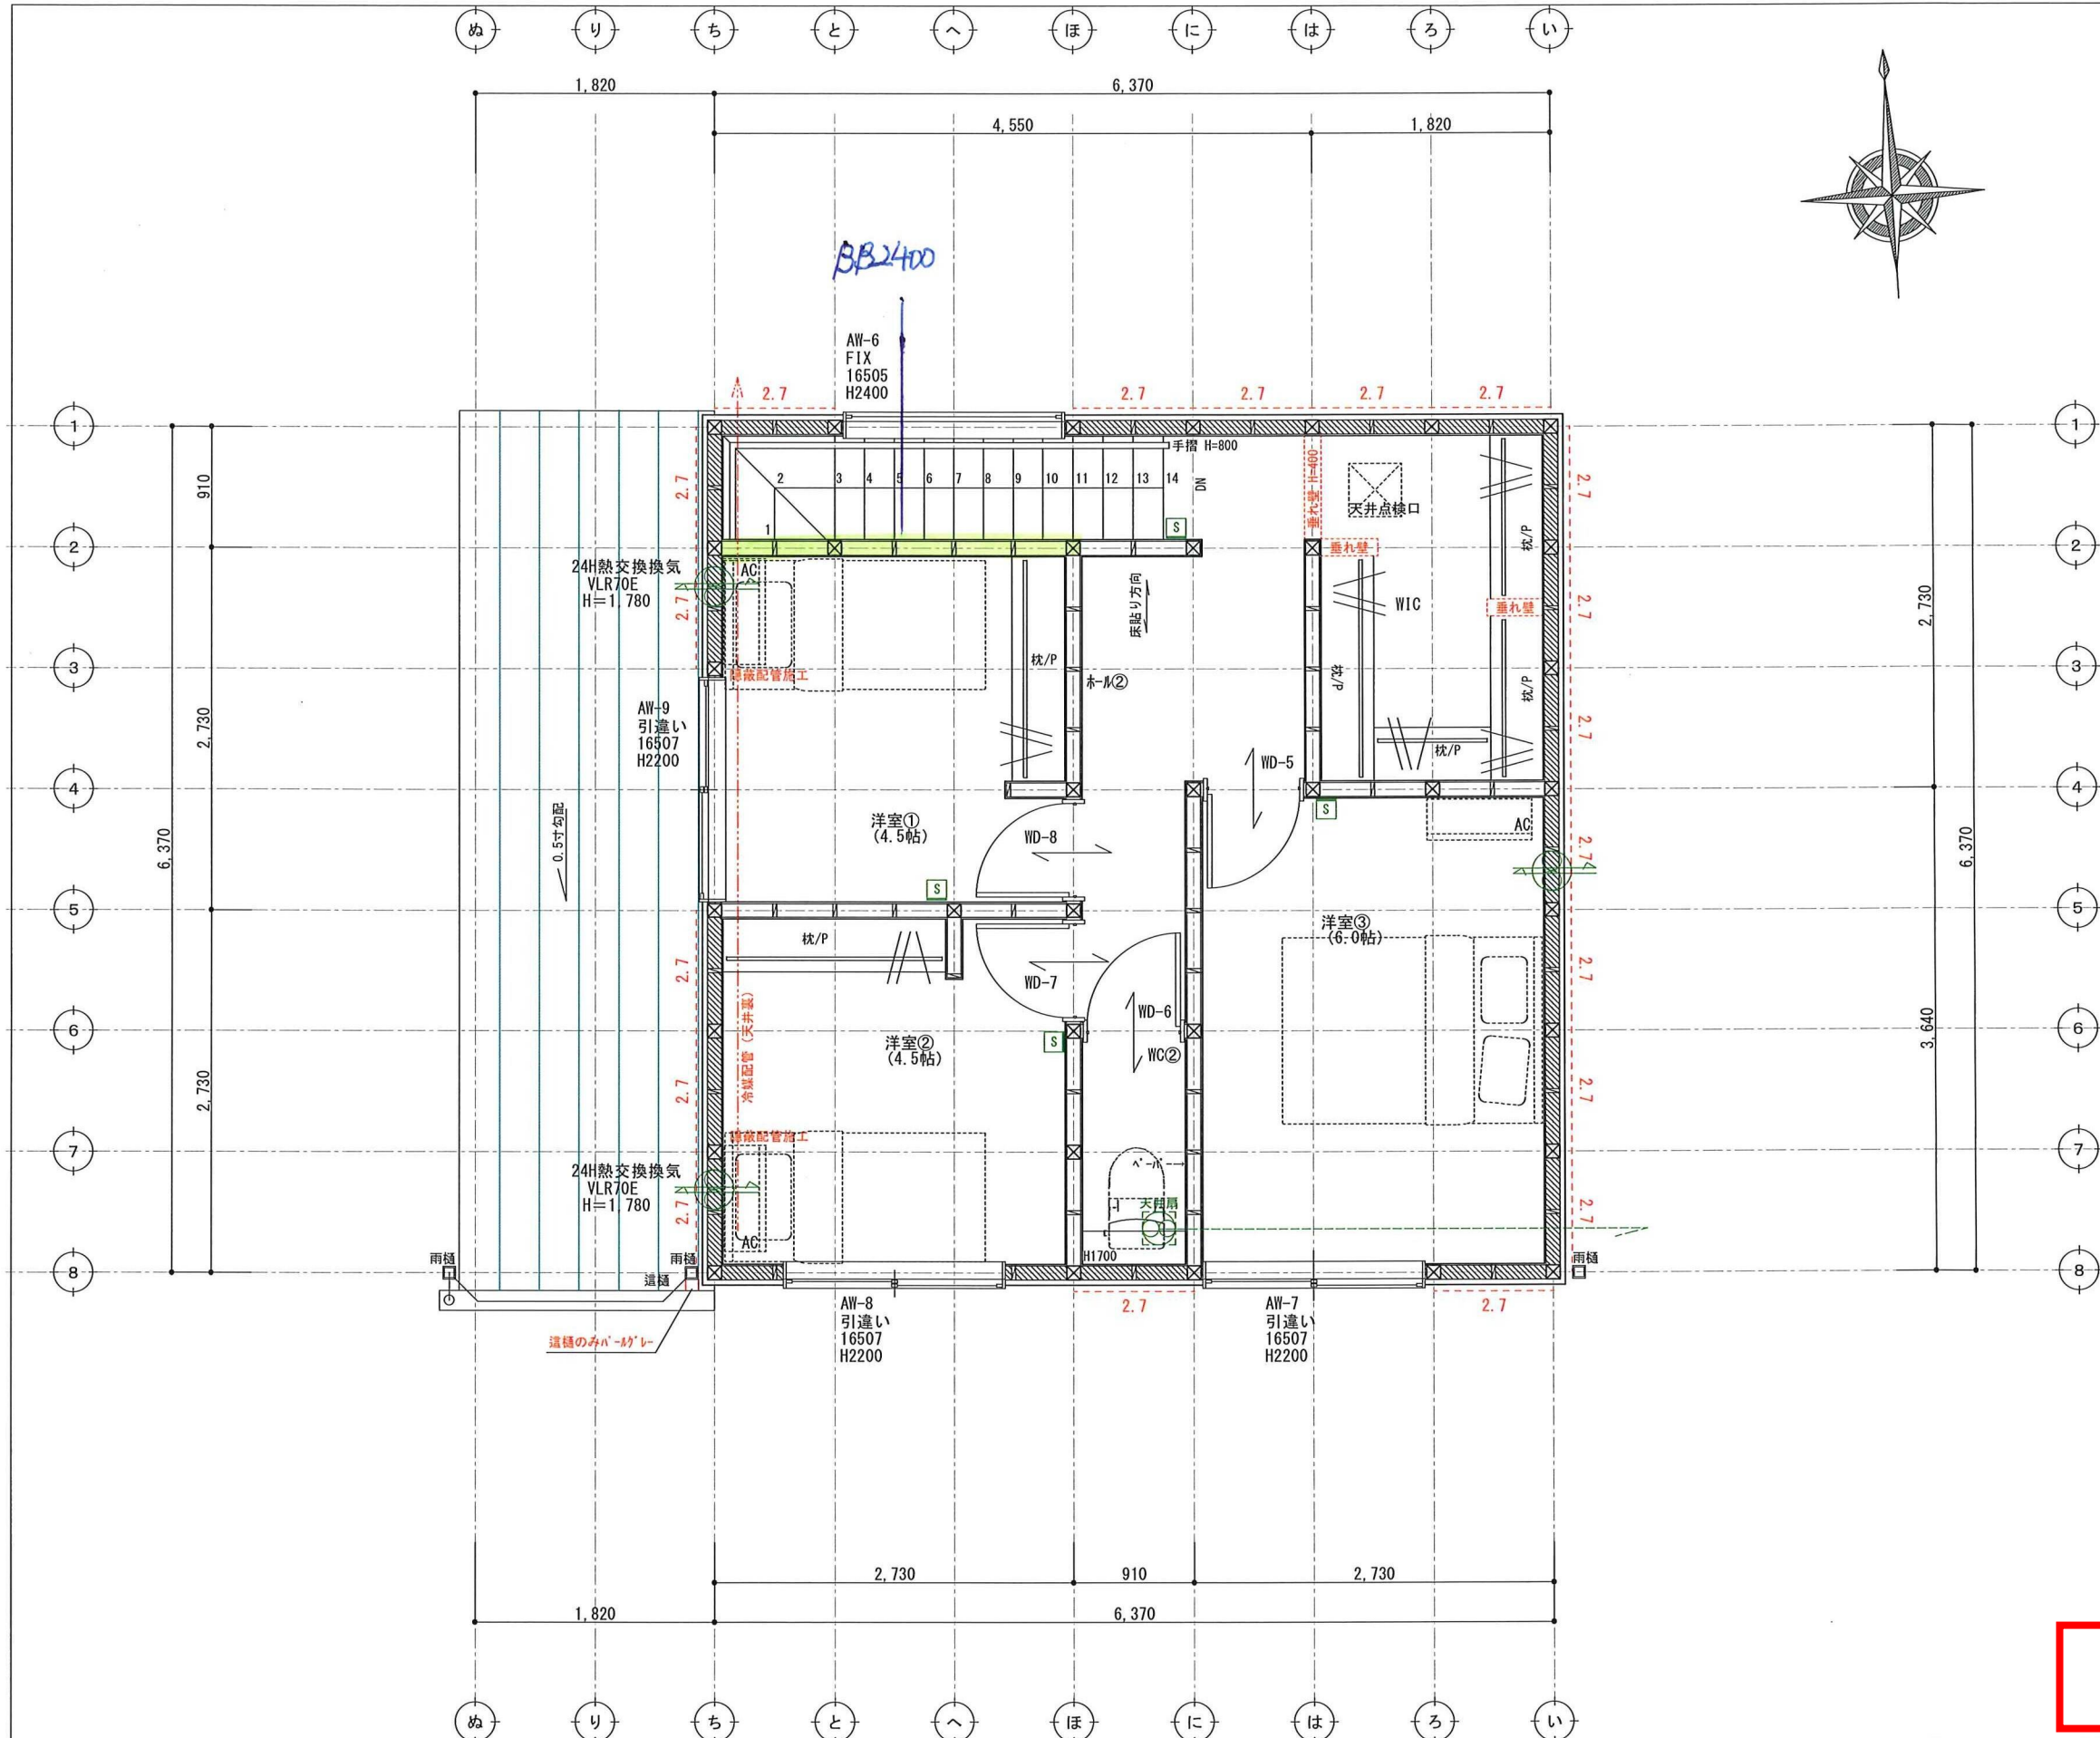

G2

壁付け 住宅用火災報知器			数量
H 熱感知	電池式(単独型)		
	露出型		
壁付け 住宅用火災報知器			数量
S 煙感知	電池式(単独型)		4
	露出型		

- ※ 煙感知器は壁・梁より600mm以上離す
壁に取付ける場合、
天井から150mm以上500mm以内離す
換気扇・エアコン吹出口から1500mm以上離す
- ※ 全室LED照明とする。
- ※ 標準天井高さ2,400
- ※ 特記無きガラスは型ガラス

* 凡例

- ☒ 管柱 (105×105)
- ≡ K9' ヌ' - (3.30倍 FRM-0641)
- △ 片筋違い (2.00倍 45×90)
(例 左:柱脚 右:柱頭)
- ⊠ たすき掛筋違い (4.00倍 45×90)
- 構造用合板 (2.70倍)
(t=9 9' - EXAMIN -)
- ⬆ 床点検口
- ⬆ 天井点検口
- ⊕ 換気扇
- ⊕ 熱交換換気扇VLR-70

- ※ 全室LED照明とし、調光制御を採用する。
- ※ 非居室の照明は人感センサーを採用する。

アドバンスシリーズ	
スマートデザイン (外部)	
凡例	
①	コンセント 1ヶ所
②	コンセント 2ヶ所
③	コンセント 3ヶ所
①ET	コンセント1ヶ所接地ターミナル付
②ET	コンセント2ヶ所接地ターミナル付
WP	コンセント 防水型
⊕	エアコン用コンセント
⊕	200V用コンセント
WP	防雨入線プレート
●	スイッチ
●3	3路スイッチ
●4	4路スイッチ
⊕	直結電源
TV	テレビ取出口
TEL	電話取出口 (テレホンガイド)
LAN	LAN取出口 (テレホンガイド)
⊕	壁照明
⊕	リモコン (給湯関係・ルフロ)
⊕	メーター
⊕	分電盤
⊕	チャイム

- ※ACコンセント天井付け
- ※TVアンテナ工事
- ※スイッチはFL+1100、コンセントはFL+200

決定図

訂正	浜岡一級総合設計事務所 一級建築士事務所 静岡県知事登録第 (10)2441 号 一級建築士 大臣登録第 365879 号 西原利昌	PG HOUSE ピージーハウス	株式会社 LIFEFUND InDesign office 事務所登録 (2)第7595号 一級建築士登録 第179770号 鈴木 達男 〒432-8023 静岡県浜松市中央区鶴江3丁目70番23号	年月日 2026.1.4 縮尺 1/50	件名 寺本唯麻様邸 新築工事 図名 2階平面図	設計 酒井	IC	工事 青島	図番 3-2
----	--	---------------------	---	-------------------------------	----------------------------------	----------	----	----------	-----------