


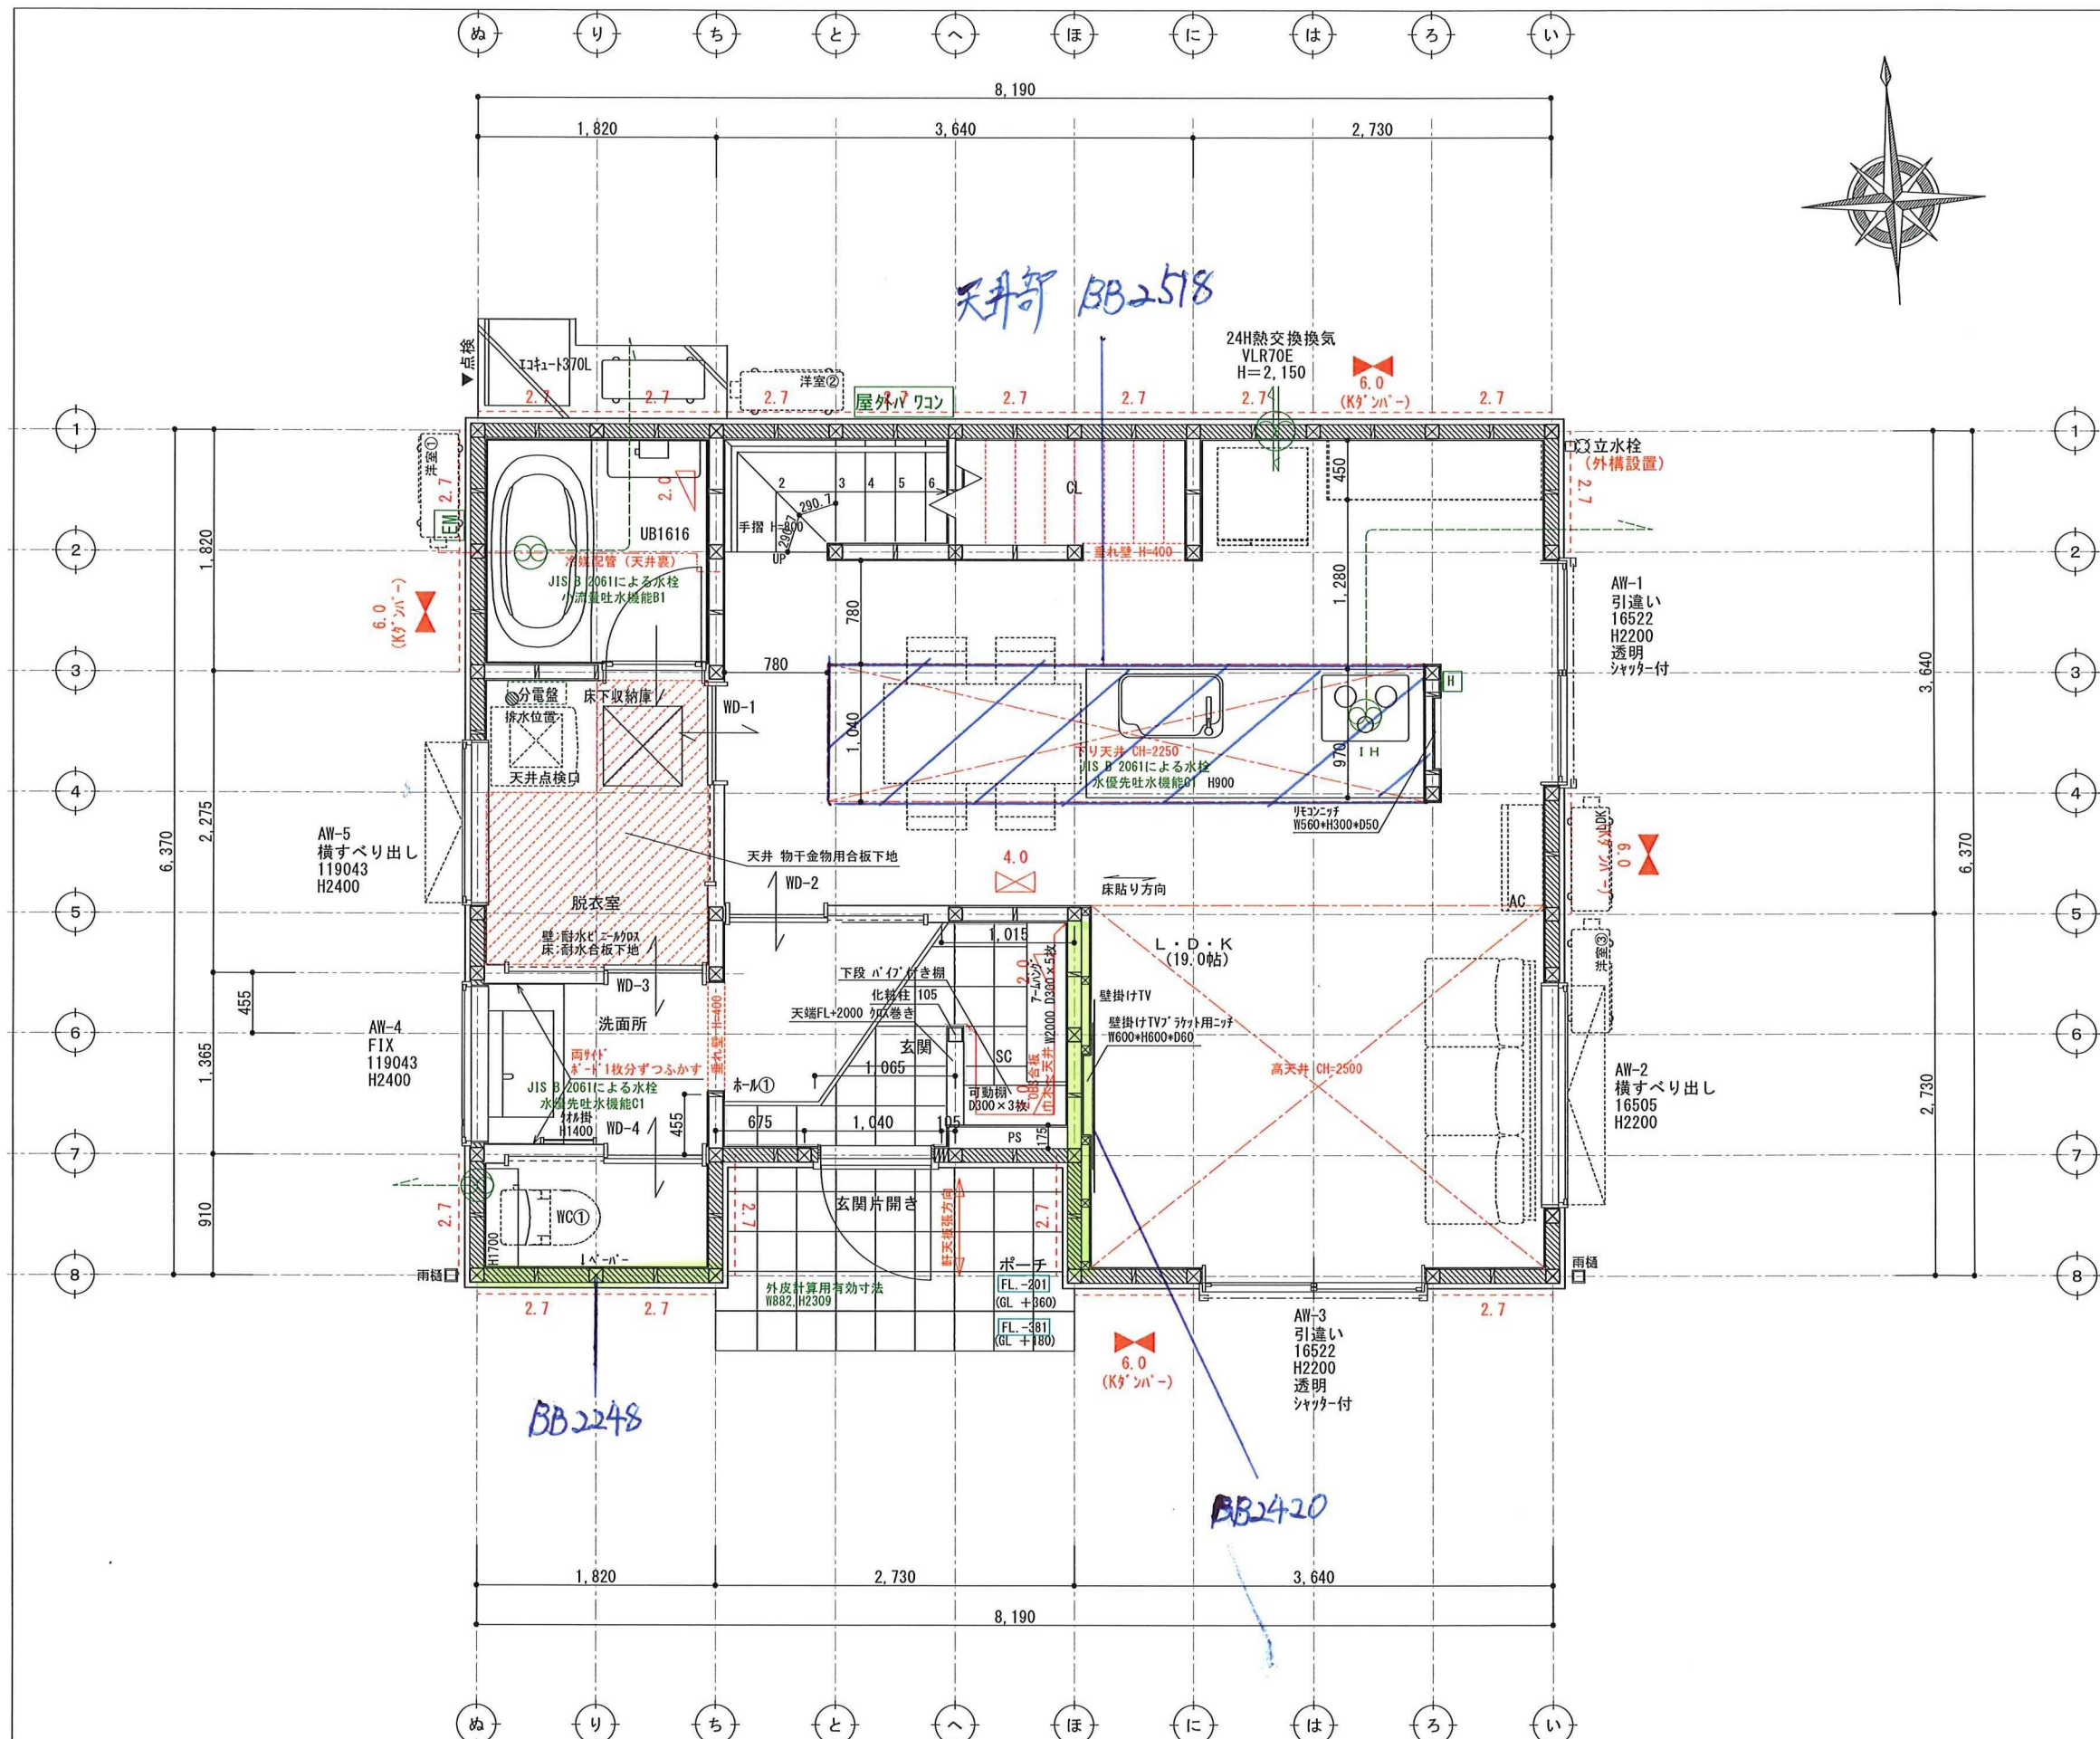

G2


壁付け 住宅用火災報知器			数量
[H] 熱感知	熱感知器	電池式(単独型)	1
	露出型		
壁付け 住宅用火災報知器			数量
[S] 煙感知	煙感知器	電池式(単独型)	
	露出型		

※ 煙感知器は壁・梁より600mm以上離す
壁に取付ける場合、
天井から150mm以上500mm以内離す
換気扇・エアコン吹出口から1500mm以上離す
※ 全室LED照明とする。
※ 標準天井高さ2,400
※ 特記無きガラスは型ガラス

- * 凡例
- ☒ 管柱 (105×105)
 - ≡ K'ンバ (3.30倍 FRM-0641)
 - △ 片筋違い (2.00倍 45×90)
(例 左:柱脚 右:柱頭)
 - ⊠ たすき掛筋違い (4.00倍 45×90)
 - 構造用合板 (2.70倍)
(t=9 タイプ-EXM/A-)
 - 床点検口
 - ⊞ 天井点検口
 - ⊕ 換気扇
 - ⊕ 熱交換換気扇VLR-70

※ 全室LED照明とし、調光制御を採用する。
※ 非居室の照明は人感センサーを採用する。
※ 階段寸法
蹴上: 207.14 (2900÷14段)
踏面: 227.5
有効幅: 780
手摺出幅100mm以下

決定図

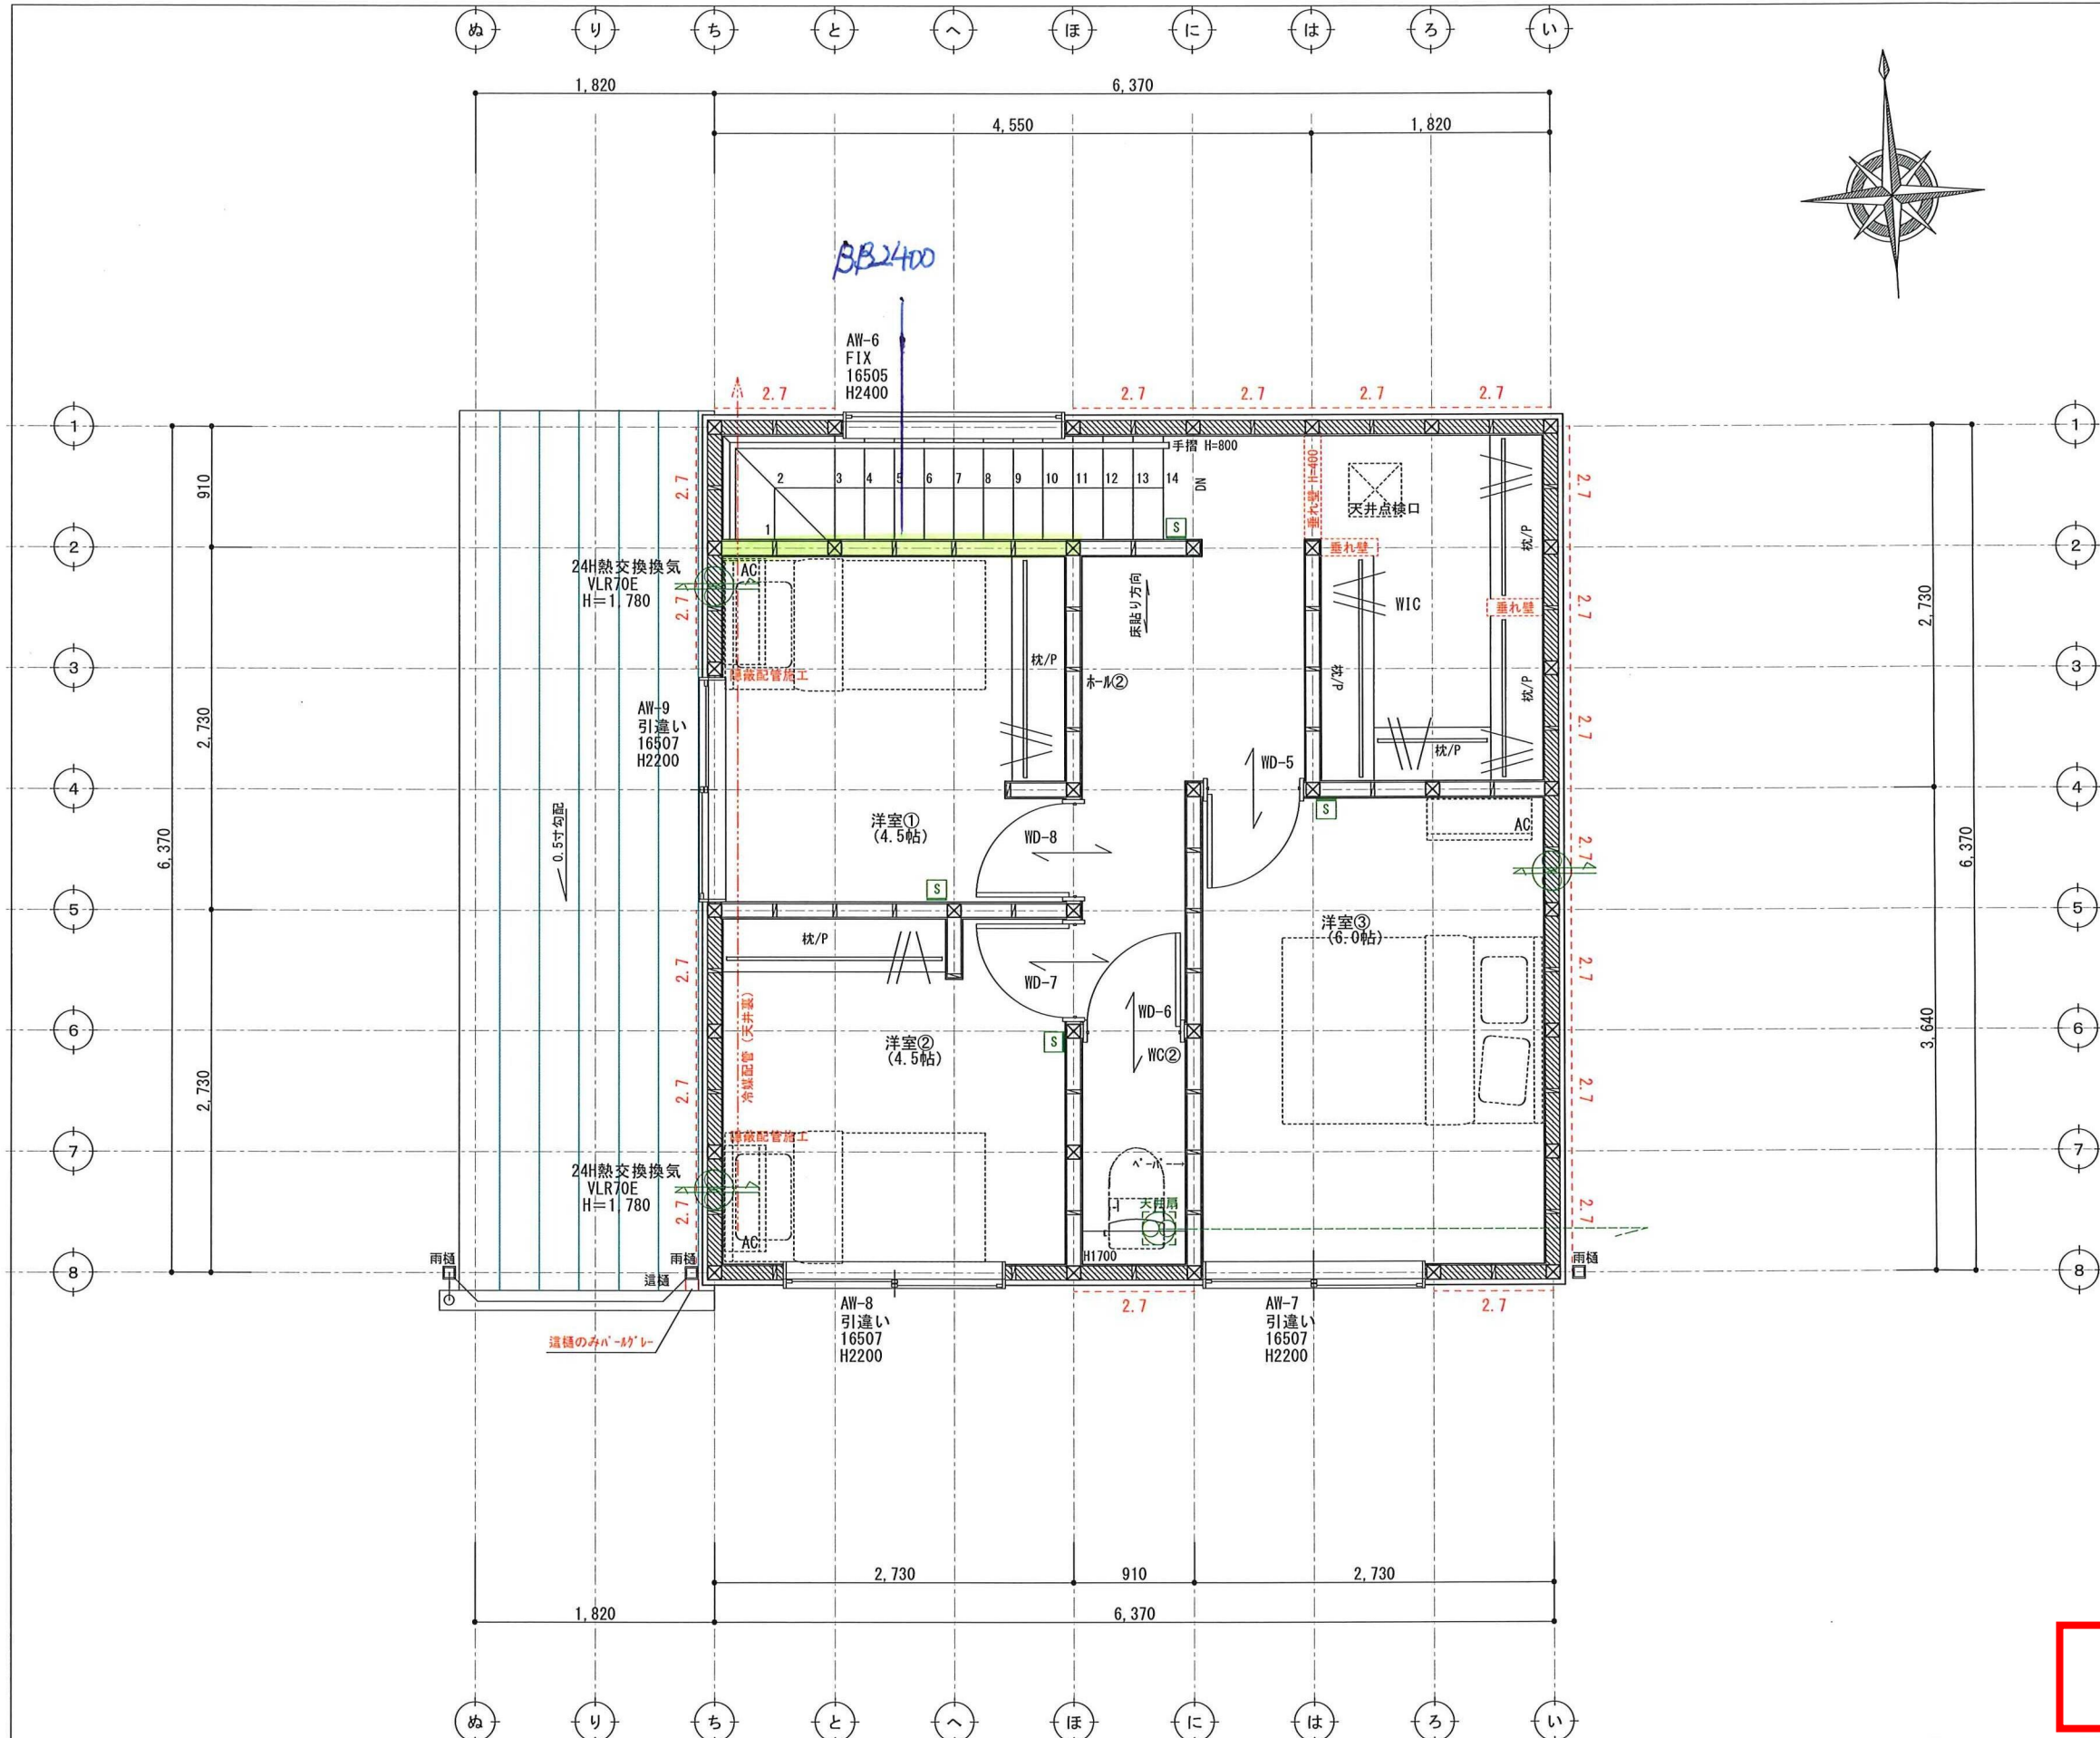

G2

壁付け 住宅用火災報知器			数量
H 熱感知	電池式(単独型)		
	露出型		
壁付け 住宅用火災報知器			数量
S 煙感知	電池式(単独型)		4
	露出型		

- ※ 煙感知器は壁・梁より600mm以上離す壁に取付ける場合、天井から150mm以上500mm以内離す換気扇・エアコン吹出口から1500mm以上離す
- ※ 全室LED照明とする。
- ※ 標準天井高さ2,400
- ※ 特記無きガラスは型ガラス

* 凡例

- ☒ 管柱 (105×105)
- ◀▶ K9' ヴァー (3.30倍 FRM-0641)
- △ 片筋違い (2.00倍 45×90) (例 左:柱脚 右:柱頭)
- ◻ たすき掛筋違い (4.00倍 45×90)
- 構造用合板 (2.70倍) (t=9 9' -EXNIN-)
- ⬆ 床点検口
- ⬆ 天井点検口
- ⊕ 換気扇
- ⊕ 熱交換換気扇VLR-70

- ※ 全室LED照明とし、調光制御を採用する。
- ※ 非居室の照明は人感センサーを採用する。

アドバンスシリーズ	
スマートデザイン (外部)	
凡例	
①	コンセント 1ヶ所
②	コンセント 2ヶ所
③	コンセント 3ヶ所
①ET	コンセント1ヶ所接地ターミナル付
②ET	コンセント2ヶ所接地ターミナル付
WP	コンセント 防水型
⊕	エアコン用コンセント
⊕	200V用コンセント
WP	防雨入線プレート
●	スイッチ
●3	3路スイッチ
●4	4路スイッチ
⊕	直結電源
TV	テレビ取出口
TEL	電話取出口 (テレホンガイド)
LAN	LAN取出口 (テレホンガイド)
⊕	壁照明
⊕	リモコン (給湯関係・ルフロ)
⊕	メーター
⊕	分電盤
⊕	チャイム

- ※ACコンセント天井付け
- ※TVアンテナ工事
- ※スイッチはFL+1100、コンセントはFL+200

決定図