
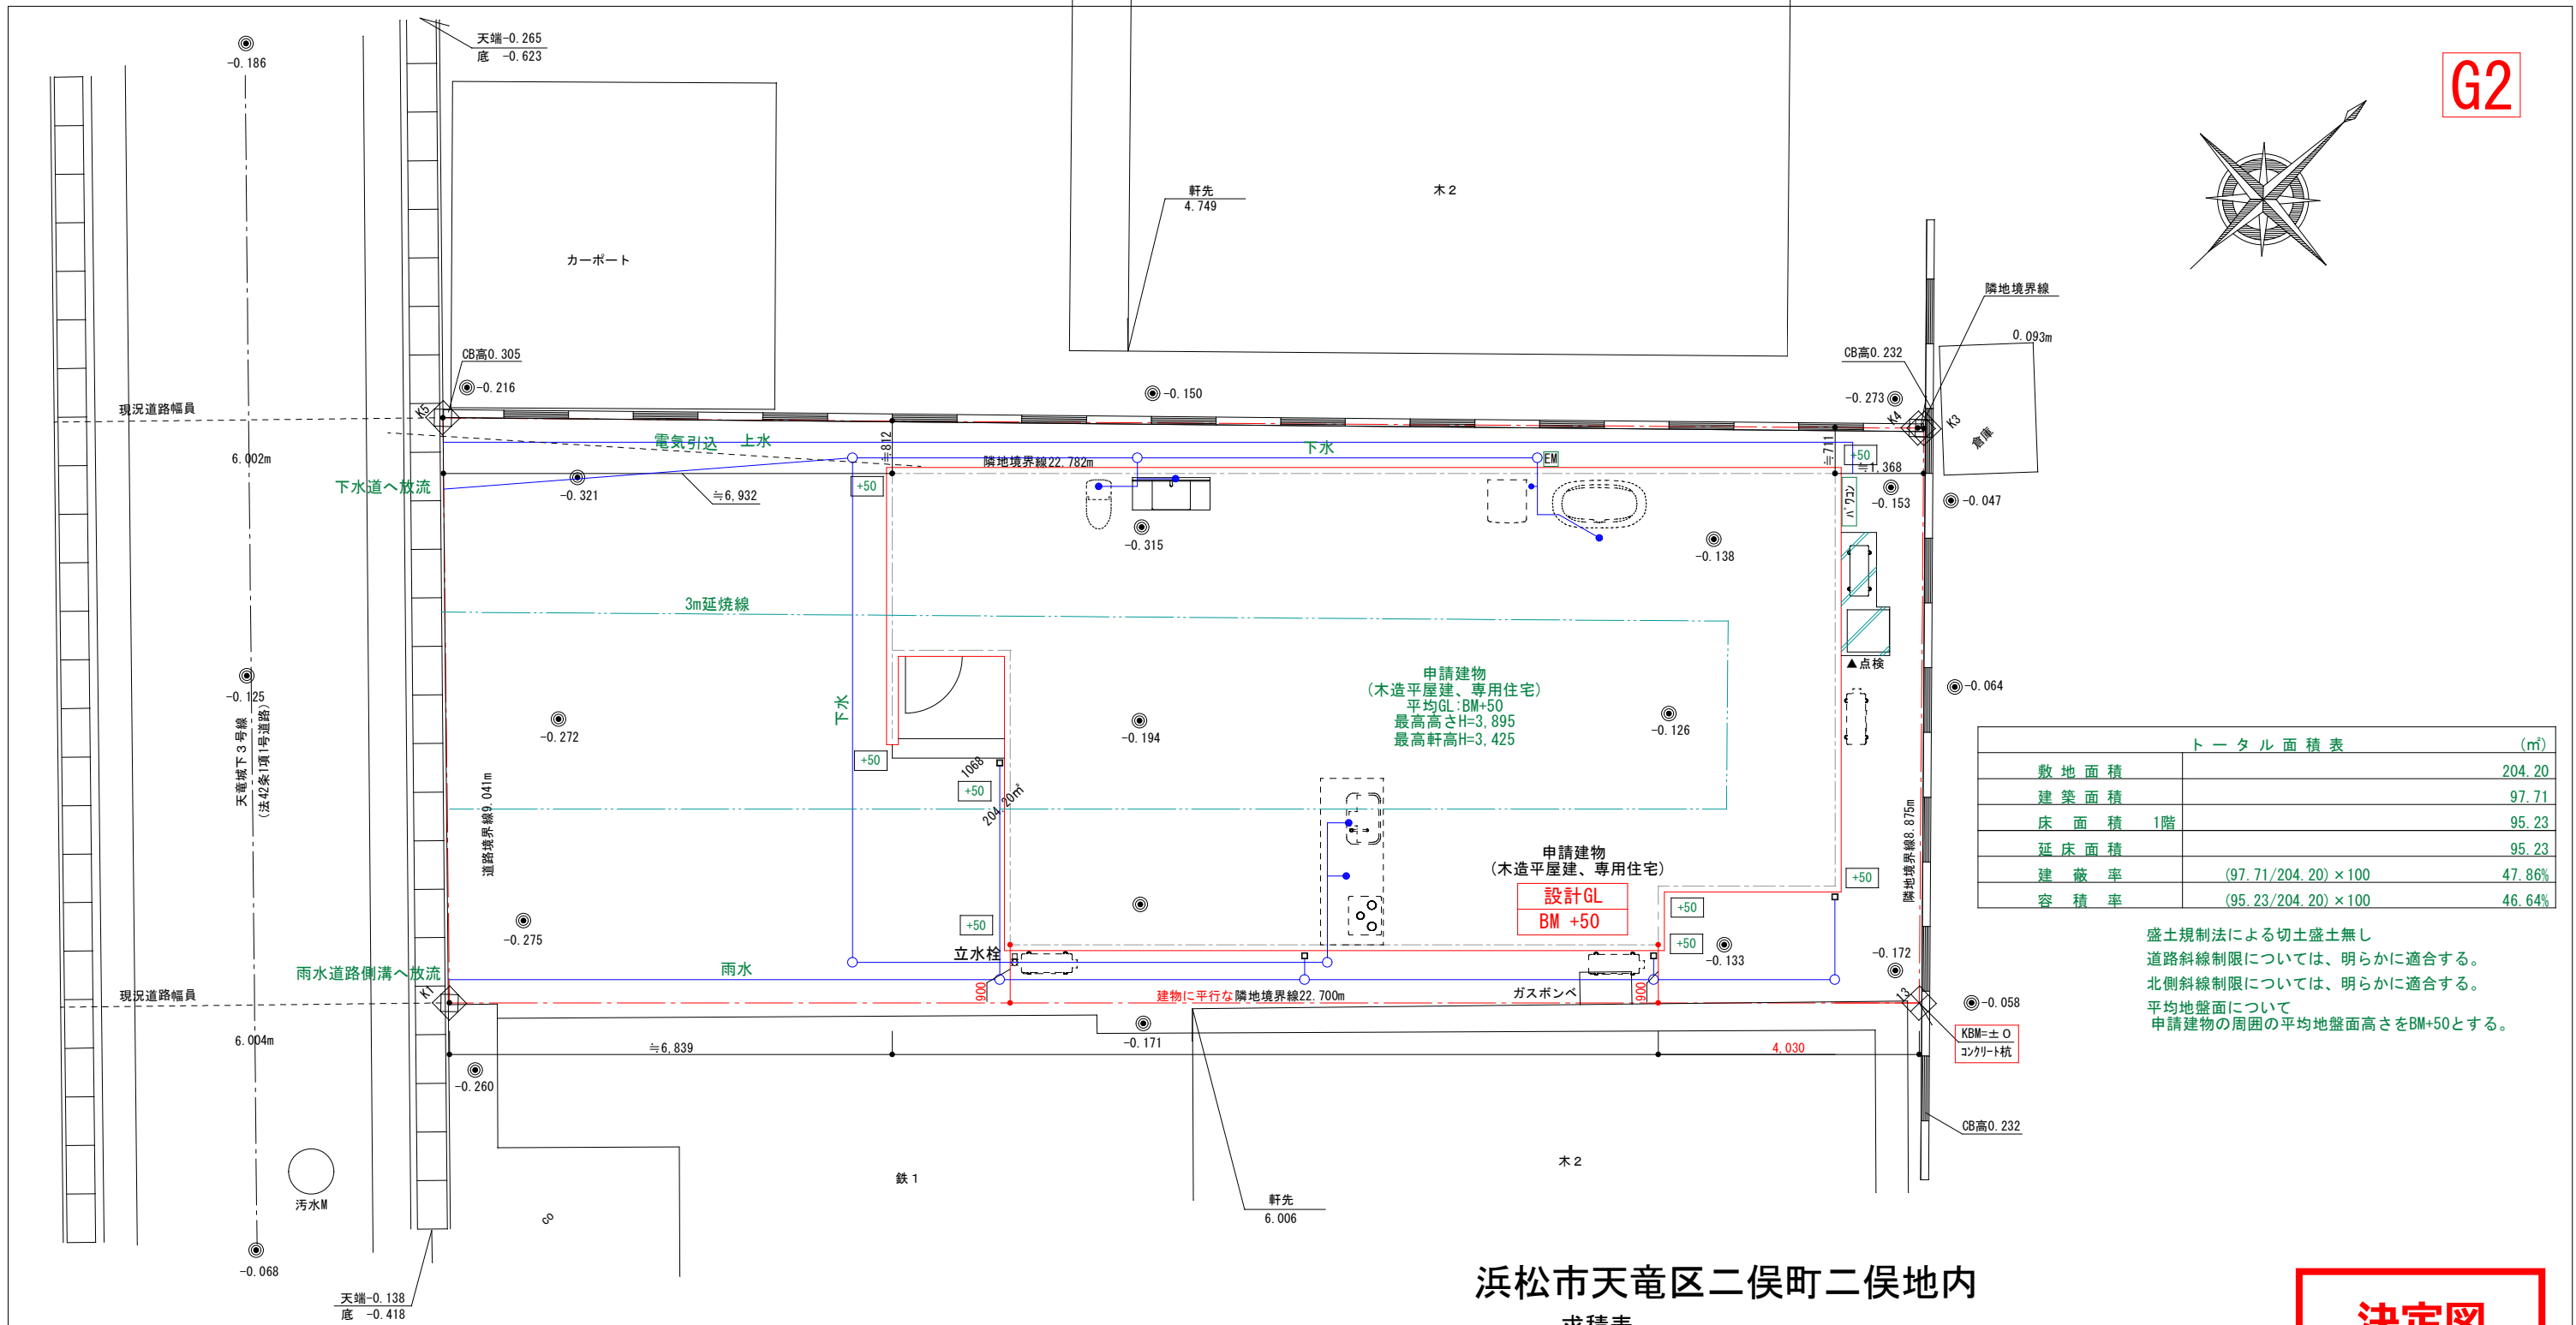



G2

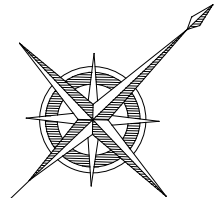

トータル面積表		(㎡)
敷地面積		204.20
建築面積		97.71
床面積 1階		95.23
延床面積		95.23
建蔽率	$(97.71/204.20) \times 100$	47.86%
容積率	$(95.23/204.20) \times 100$	46.64%

盛土規制法による切土盛土無し
道路斜線制限については、明らかに適合する。
北側斜線制限については、明らかに適合する。
平均地盤面について
申請建物の周囲の平均地盤面高さをBM+50とする。

求積図 (1/250)

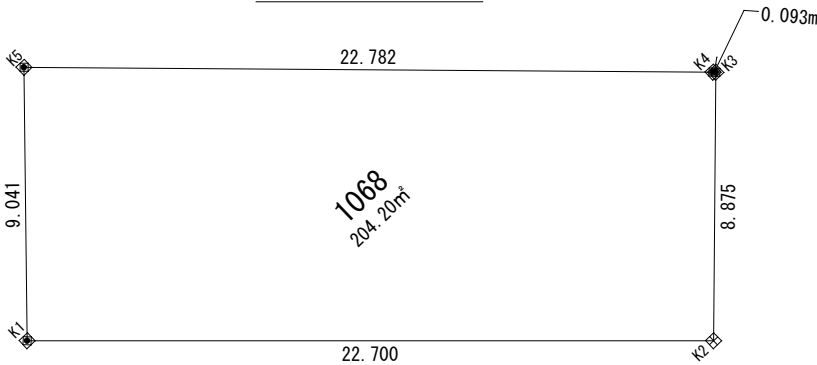

浜松市天竜区二俣町二俣地内
求積表

地番	1068				
NO	X _n	Y _n	Y _{n+1} - Y _{n-1}	X _n × (Y _{n+1} - Y _{n-1})	
K1	-5.585	-4.018	10.221	-57.084285	
K2	-21.281	12.381	22.589	-480.716509	
K3	-14.920	18.571	6.127	-91.414840	
K4	-14.851	18.508	-16.411	243.719761	
K5	1.017	2.160	-22.526	-22.908942	
合計				-408.404815	
合計面積				204.2024075	
地積				204.20 m ²	

決定図