




A面

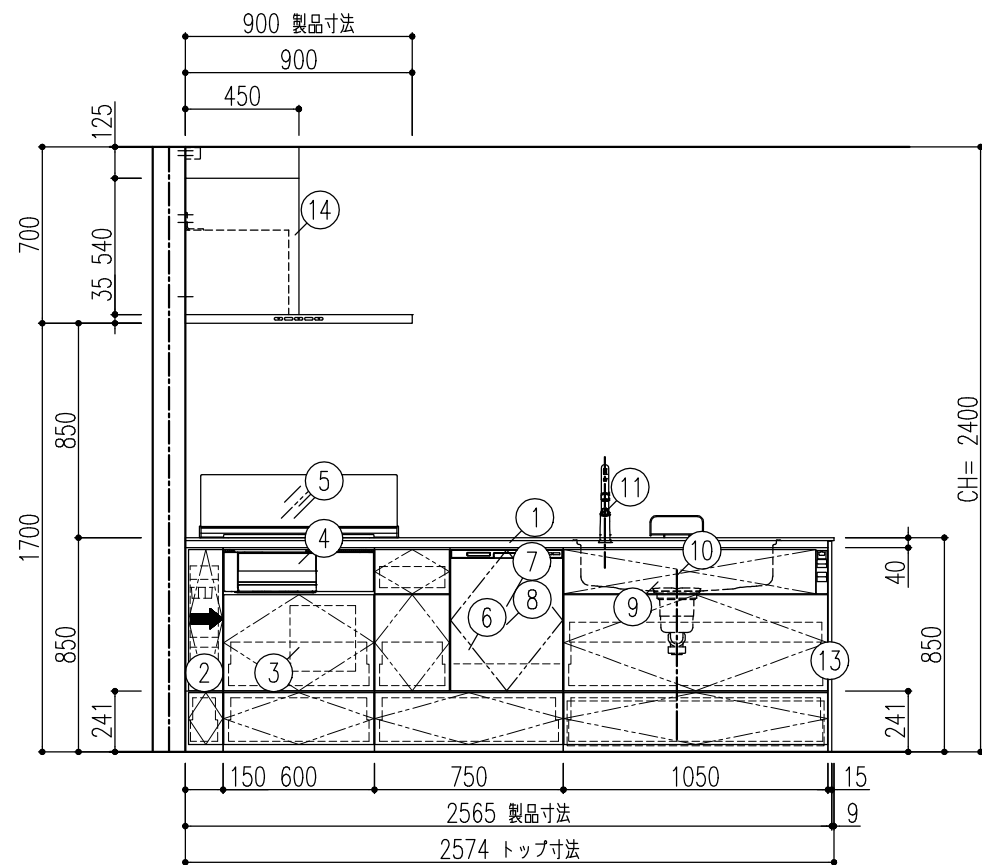


B面

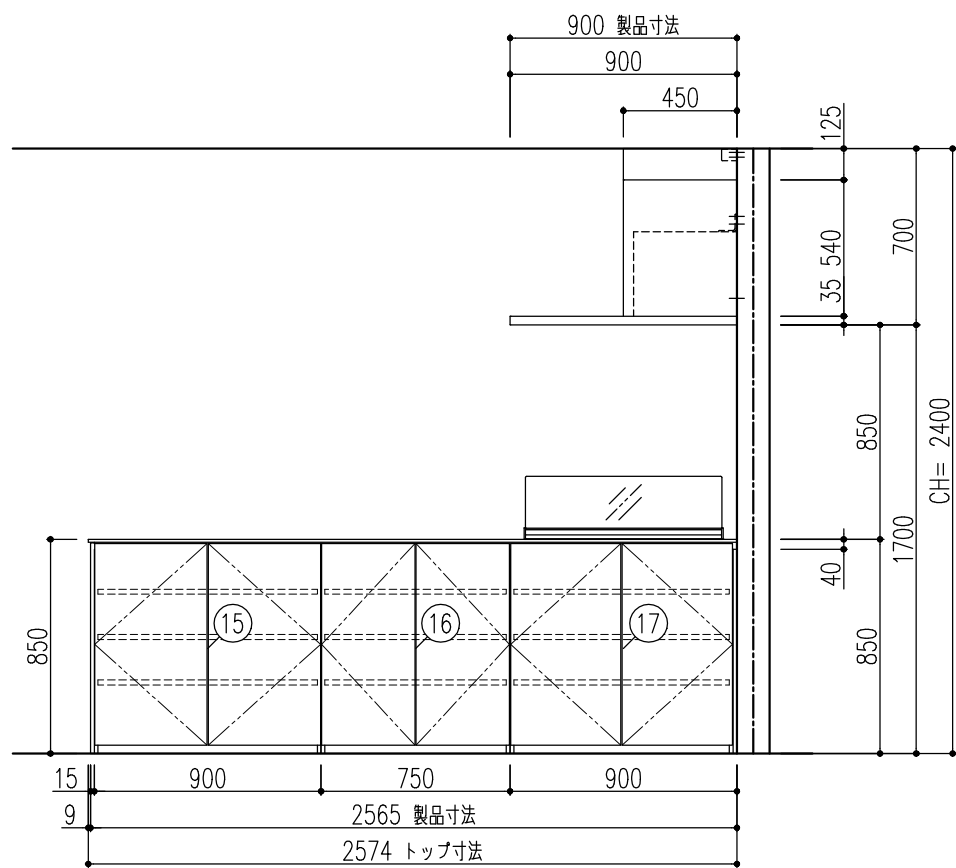


C面

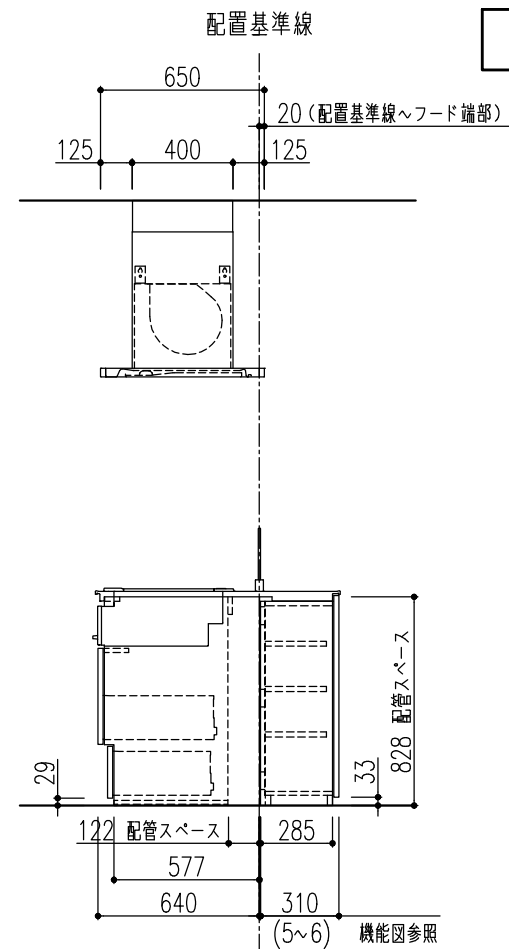

D面

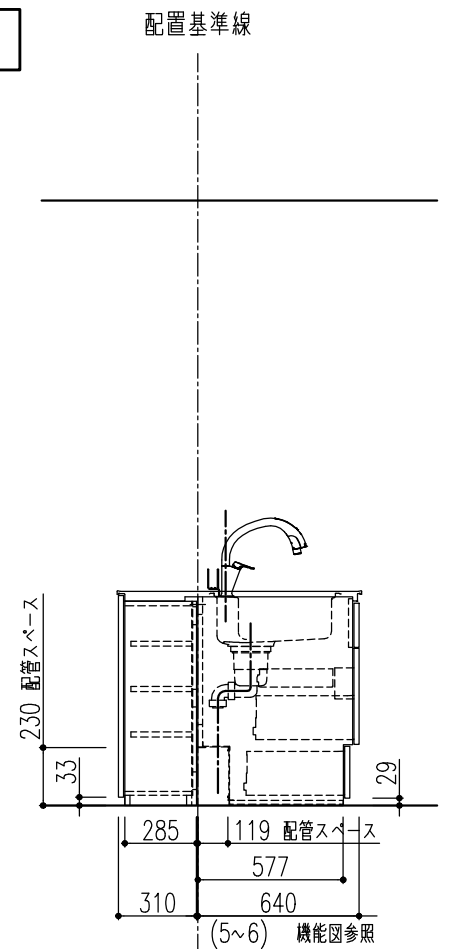

特記事項 扉色 KK5:ブラックスタック 取手 [M]スリム取手 (ブラック) ワークトップカラー 【LE】シルフィィグレー	物件名	三室司 様邸	案件No.	図面名	担当	図面	図番
			A2511DDD0EX74W	レイアウト図	栗野 友仁		株式会社 LIXIL
	仕様	ES21	見積No.	縮尺	日付		
			M25119283857-009-2	1/30	2026.01.13		

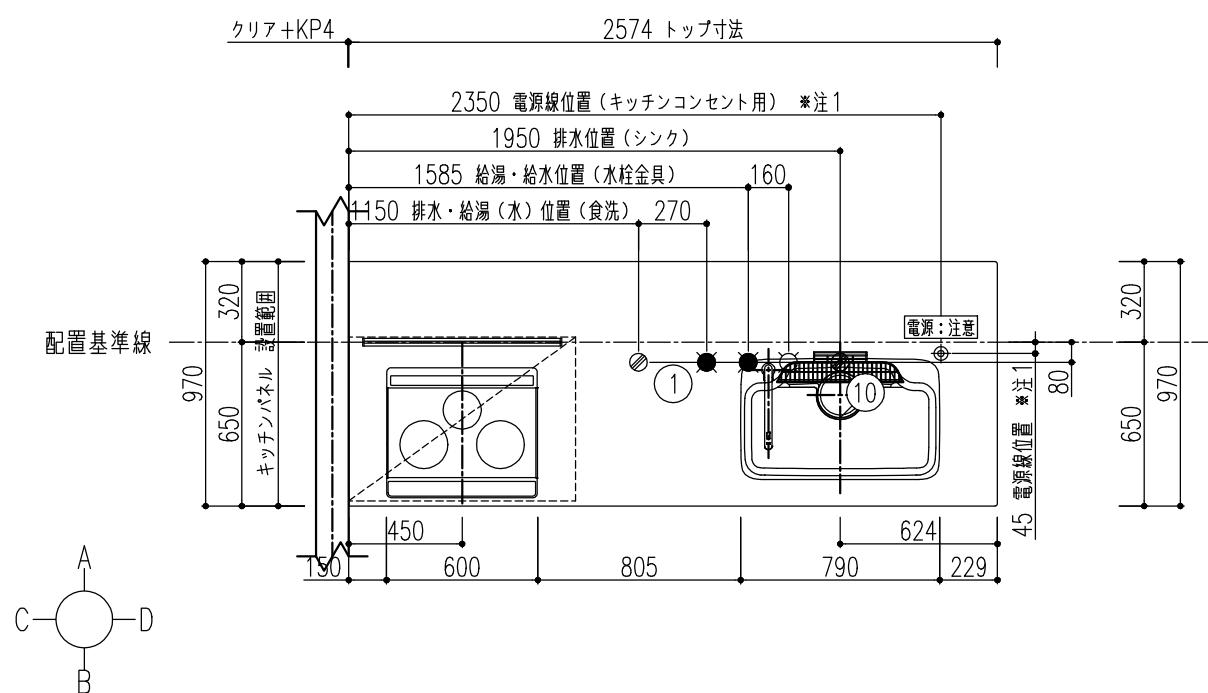[illegible]

注1) 100V・15A 電源線取出し推奨位置(3.0M出し)【専用】※配管スペース内であれば他位置でも可
【ご注意】



- 記載のキャビネット寸法は扉前面までの呼び寸法です。キャビネット本体の寸法・扉厚み等は商品ガイドの巻末資料をご確認ください。
- 記載のワークトップ、カウンター、エンドパネル、サイドパネルの寸法は呼び寸法です。詳細寸法は商品ガイドの巻末資料をご確認ください。
- 電気・ガス・給排水・換気等は法令・規定に従って有資格者が行ってください。
- 水道工事は排水配管工事となります。
- 取付・設置に際し、各製品の取付・設置説明書や図面の機能図を必ずお読み下さい。
- 内線規程上、各機器のプラグ仕様に関わらず建築側には接地極付コンセントを推奨しています。
- レンジフード電源プラグ仕様：3芯電源プラグ（アース工事が必要です。）
- 食器洗い乾燥機配管は、給水接続か給湯接続かお客様に確認したうえで施工願います。
- 食洗機内配管の詳細については必ず別添の機能図をご確認ください。
- VVFケーブルの太さにつきましては、内線規程に準じてください。
- スライドバスケットキャビ内バルーン上部の黒塗り矢印(→)は 取出し側を示します。

特記事項 扉色 KK5:ブラックスタック 取手 [M]スリム取手 (ブラック) ワークトップカラー 【LE】シルフィーグレー	物件名	三室司 様邸	案件No.	図面名	担当	図面	図番 : 株式会社 LIXIL
			A2511DDD0EX74W	納まり図	栗野 友仁		
	仕様	ES21	見積No.	縮尺	日付		
			M25119283857-009-2	1/30	2026.01.13		

A面

B面



- 注2) 125V・15A 2極接地極付アースターミナル付コンセント 【専用】
注3) 125V・15A 2極接地極付コンセント (側板取付)
注4) 250V・30A 2極接地極付コンセント (側板取付) 【専用】
注5) レンジフード総高さ (600~900) の時 ダクトカバー範囲 (25~325)

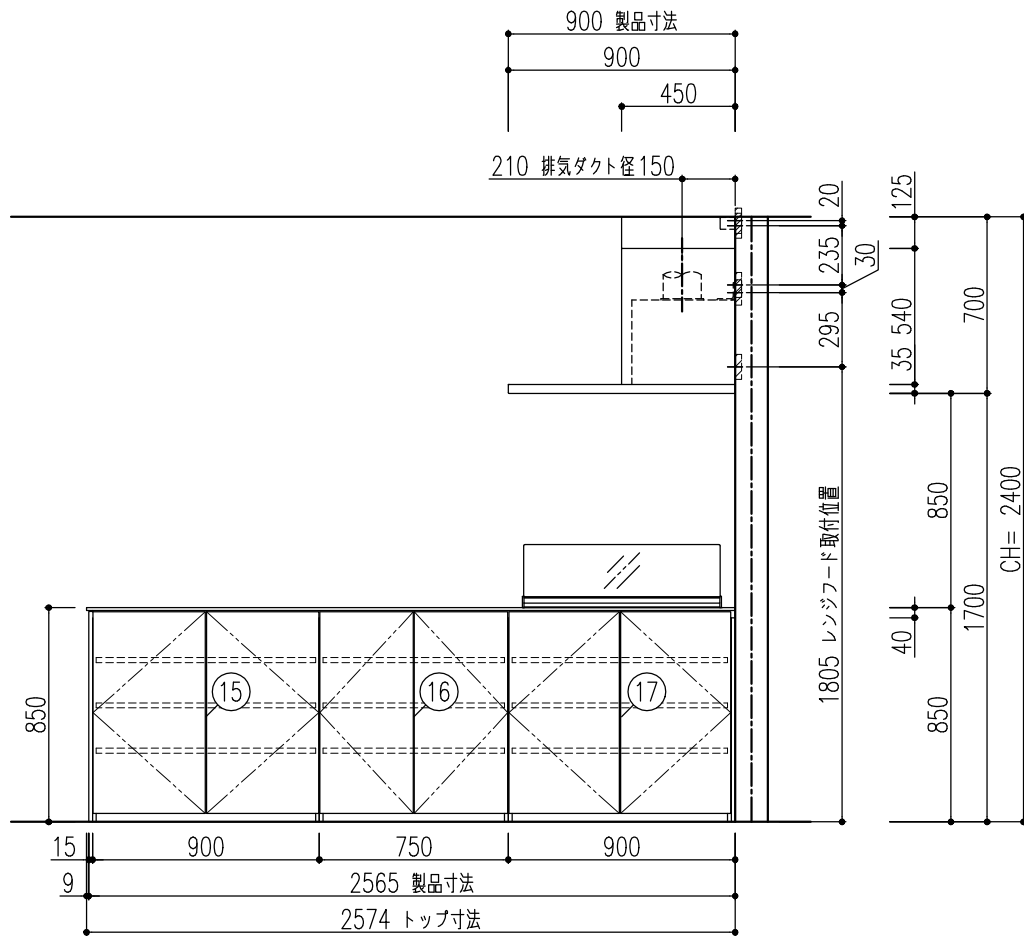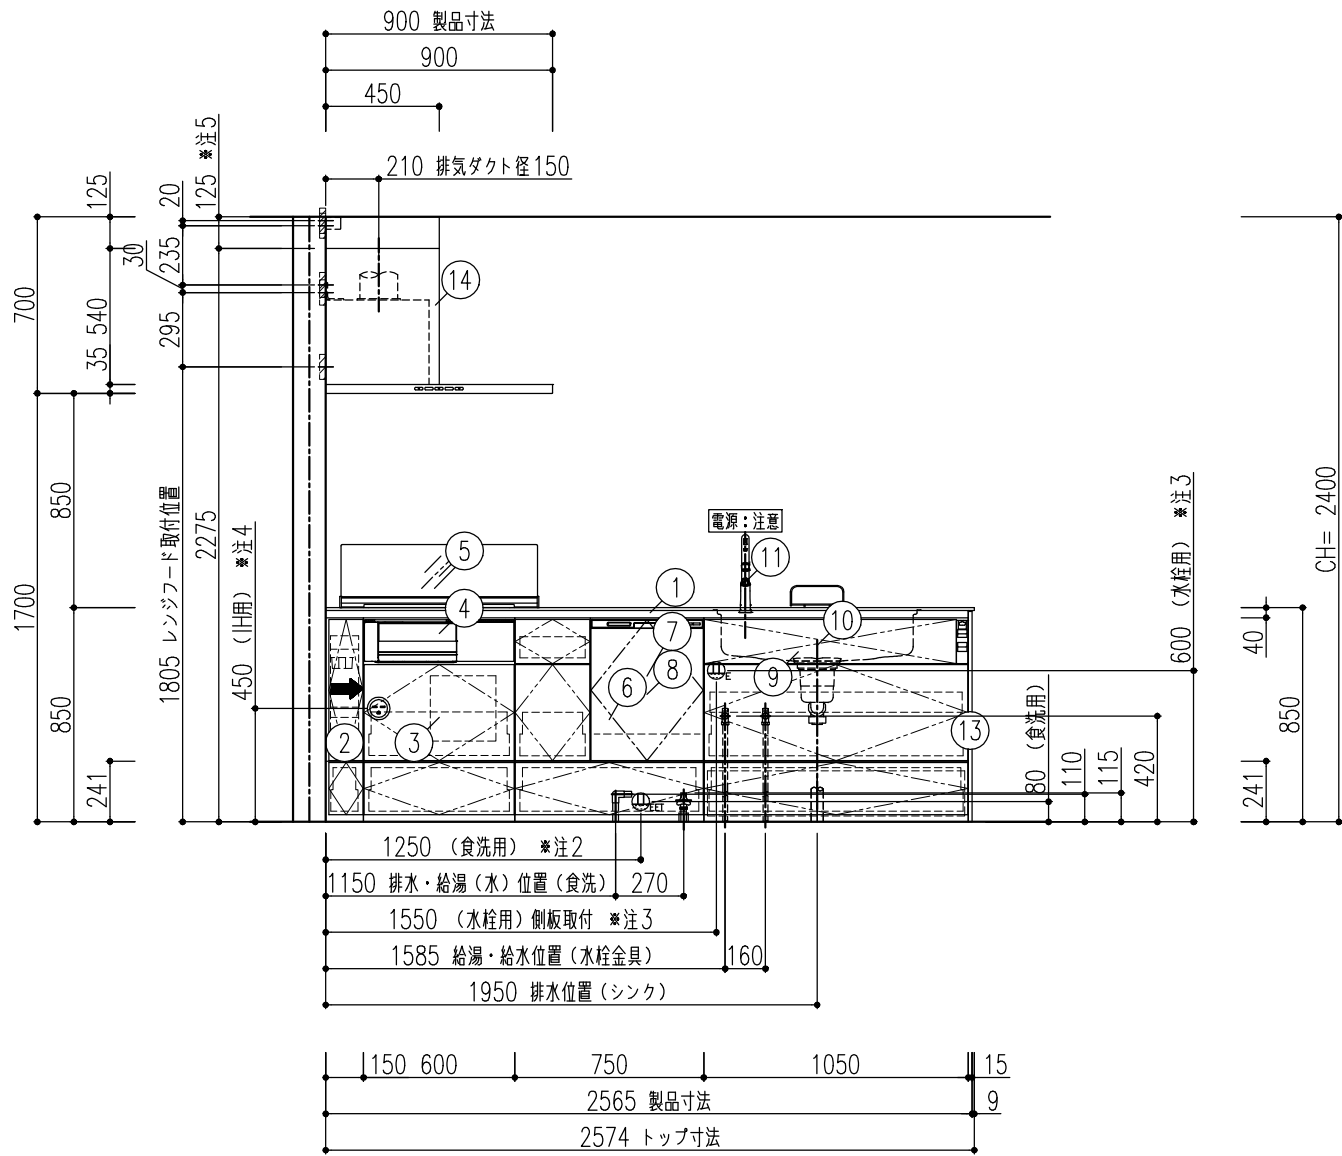

C面

D面

注6) 125V・15A 2極接地極付アースターミナル付コンセント 【専用】(フード用)

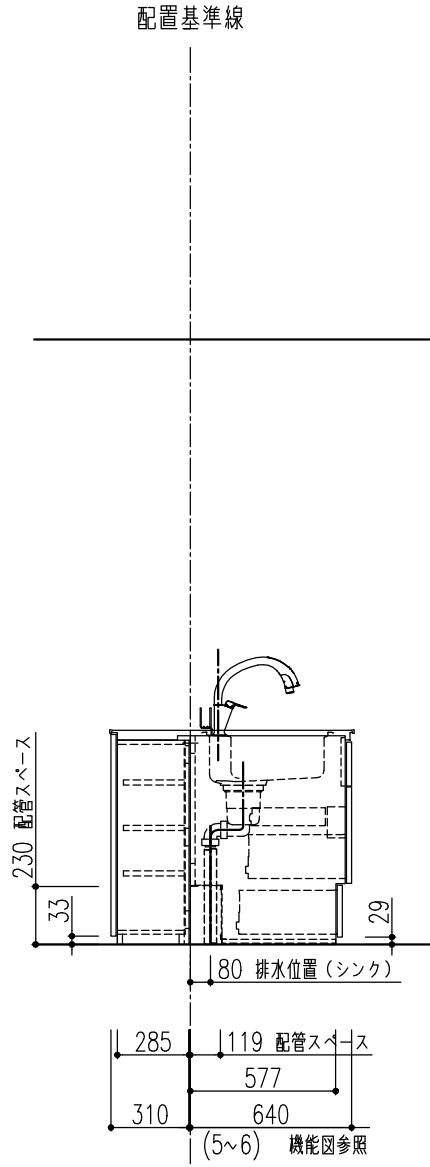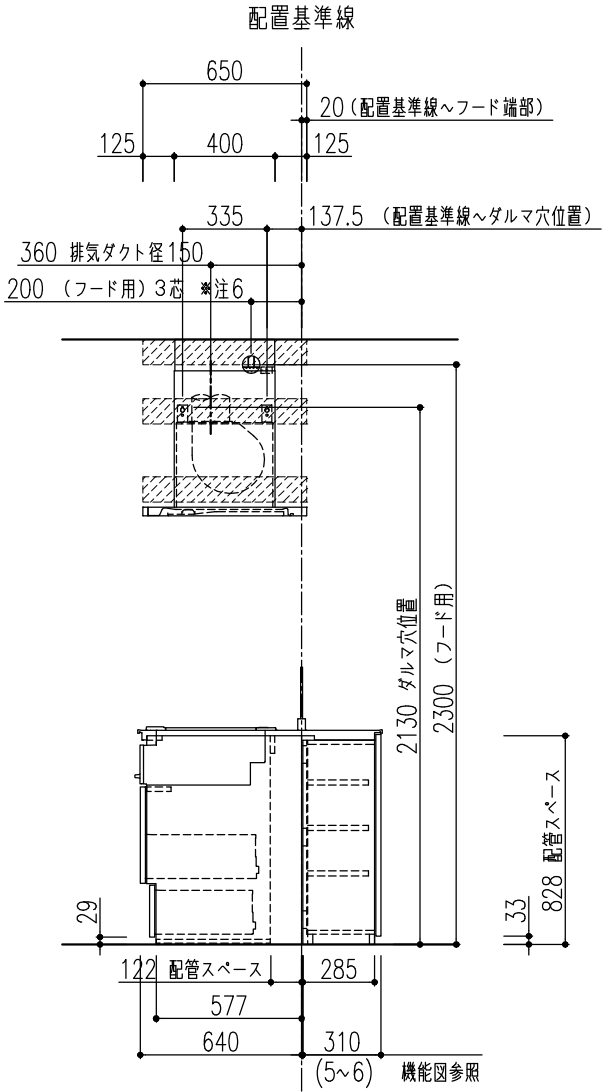

特記事項 原色 KK5:ブラックスタッコ 取手 [M]スリム取手(ブラック) ワークトップカラー 【LE】シルフィィーグレイ	物件名	三室司 様邸	案件No.	図面名	担当	図面	図番 : 株式会社 LIXIL
			A2511DDD0EX74W	納まり図	栗野 友仁		
	仕様	ES21	見積No.	縮尺	日付		
			M25119283857-009-2	1/30	2026.01.13		

■ 床の不陸に関して

床の不陸は、7mm以下に抑えるようにしてください。不陸が大きい場合は、現場責任者に床の修正を依頼してください。
※キャビネット取付時には不陸調整スペーサー等で水平になるように設置してください。

■ 裏面キャビネット納まりについて

(キッチン側キャビネット背面) 配置基準▽

キッチン側 ダイニング側

スリムデザイントップ

ワークトップアンダーモール前面とキャビネット側板前面をあわせるように設置してください。

標準框トップ

ワークトップ前面から側板前面を29mmの位置にあわせてに設置してください。

■ レンジフード取付注意事項（壁面取付時）

レンジフードを取付ける場合は下地の材が厚み30mm以上、幅100mm以上、ビス固定位置が材の端部から25mm以上であることを確認してください。
また、壁強度などの詳細は「レンジフード設置説明書」を必ず事前に確認してください。

取付位置については、取付設置図を確認してください。

参考図_CLS. SER. NST. ASR. ADR. RVJ. GSR. BFRS. TARシリーズ
(※RVJ. GSRシリーズの場合はレンジフードパネルの取付下地は不要です。)

【正面】 【側面】

参考図_NBHシリーズ

【正面】 【側面】

■ SMHVRフード

特性表

型名	定格電圧 (V)	定格周波数 (Hz)	消費電力 (W)	風量 (m³/h) OPg	騒音 (dB) 100Pa	製品質量 (Kg)	
SMHVR-93*	100	強	50	70	530	48	26.5
		中	50	28	370	39	
		弱	50	11	220	28	
		常時	50	7	155	22	
		50	7	155	22		

電動機形式 8極DC ブラシレスモーター 絶縁抵抗 10MΩ以上 (500V分) 前電圧 AC100V 1分置 絶縁区分 E種

風量値はJIS C9603 4次元法による

静圧・風量 曲線

静圧・風量 曲線

付属品

座付ねじ (φ5.1×45) 10本
化粧ねじ (M4×8) 2本
トラスねじ (M4×10) 2本
ソフトテープ 1本

品番

SMHVR-93*SL (R/L) シルバー塗装
SMHVR-93*SW (R/L) ホワイト塗装

色調

シルバー塗装
ホワイト塗装

※付部詳細図 (S=1/2)

4. 製品名の末尾の () には材質/サイズによって記号が入る場合があります。
3. 電動シャッター (HDS150) (別売) を使用時は、中継ユニットを外して取り付けてください。
2. 赤外線連動型レンジフードです。単独でも使用できます。
注) 1. 排気方向は側方 (L型) 外使用: 別売) と上方向です。

物件名

三室司 様邸

仕様

ES21

案件No.

A2511DDD0EX74W

図面名

機能図

担当

栗野 友仁

図面

図番

見積No.

M25119283857-009-2

縮尺

日付

2026.01.13


株式会社 LIXIL

A3

20260113ML6Z-01

- ※ コンセントはキャビネットの奥側（背板より65 mm）に取り付けてください。
- ※ コンセントや電源プラグが、引き出しおよびIHヒーター用仕切板（オプション）に接触しないように注意してください。
- ※ ロングスライドキャビネットの場合は、電源コードが引き出しおよびIHヒーター用仕切板（オプション）に接触しないように、キャビネットに付属の固定バンドで背板に固定してください。

※ () 内はD650/3□IHゲリルレスの場合

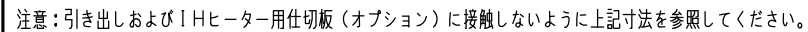

※給水接続か給湯接続かお客様に確認したうえで施工願います。 ※イラスト表記の事前配管部材は現地手配

⑤HTエルボ






○水栓がシンク右側の場合、電源位置は左右対象の位置にしてください。
○水栓がシンク中央の場合、電源位置は左右どちらでも構いません。
○＜ ＞内寸法はワークトップ高さ80cmの場合、[]内寸法はワークトップ高さ90cmの場合。

20260113ML6Z-01

■ キッチン取付者さま向け 動画コンテンツ ■

商品取付けの注意点を2次元コードでご視聴いただけます。
取付日より前に、是非ご確認ください。

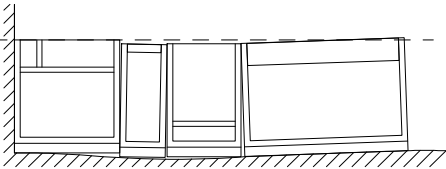荷扱い・搬入	カウンター開梱搬入「養生ツール」	不陸の確認と調整	マグネットキッチンパネル
荷扱い・搬入	カウンター開梱搬入「養生ツール」のご紹介		マグネット キッチンパネル「取付・設置」ポイント
作成日：2024年10月01日	作成日：2024年10月01日	作成日：2024年02月07日	作成日：2024年03月06日




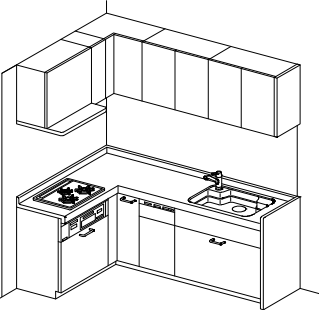
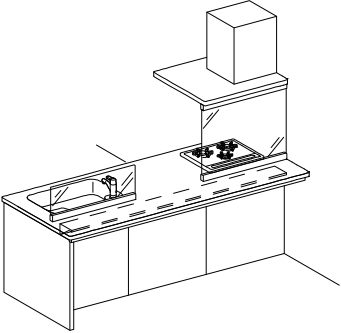
人造大理石カウンターL型キッチン	センターキッチン（ペニンシュラ型）		
			
作成日：2024年02月07日	作成日：2024年02月07日		

--	--	--	--

特記事項 扉色 KK5:ブラックスタック 取手 [M]スリム取手（ブラック） ワークトップカラー 【LE】シルフィーグレー	物件名	三室司 様邸	案件No.	図面名	担当	図面	図番
	仕様	ES21	A2511DDD0EX74W	機能図	栗野 友仁		株式会社 LIXIL
			見積No.	縮尺	日付		
			M25119283857-009-2		2026.01.13		

■ キッチン取付者さま向け 動画コンテンツ ■

商品取付けの注意点を2次元コードでご視聴いただけます。
取付日より前に、是非ご確認ください。

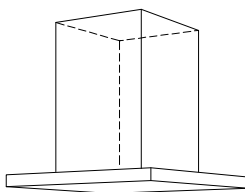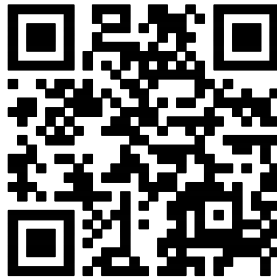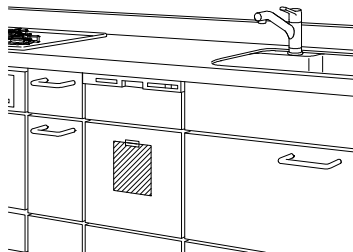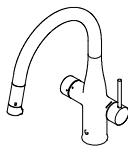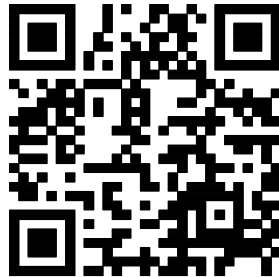センターフード型レンジフード (天吊りフード)  作成日：2024年06月03日 		I H加熱機器関連 I H加熱機器 仕切り板 作成日：2024年02月07日 		食器洗い乾燥機  作成日：2024年02月07日 		ミネラル浄水栓 Greentap  作成日：2024年06月03日 	
	特記事項 扉色 KK5:ブラックスタッコ 取手 [M]スリム取手 (ブラック) ワークトップカラー 【LE】シルフィーグレー	物件名 三室司 様邸 仕様 ES21	案件No.	図面名	担当	図面	図番
			A2511DDD0EX74W	機能図	栗野 友仁		株式会社 LIXIL
			見積No.	縮尺	日付		
			M25119283857-009-2		2026.01.13		