



面

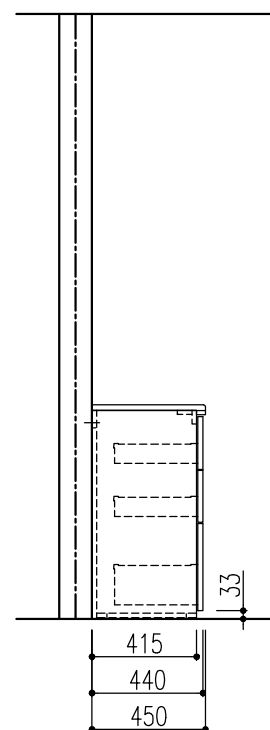

【 ご注意 】

- 記載のキャビネット寸法は扉前面までの呼び寸法です。キャビネット本体の寸法・扉厚み等は商品ガイドの巻末資料をご確認ください。
- 記載のワークトップ、カウンター、エンドパネル、サイドパネルの寸法は呼び寸法です。詳細寸法は商品ガイドの巻末資料をご確認ください。

A3 20260113ML6W-0

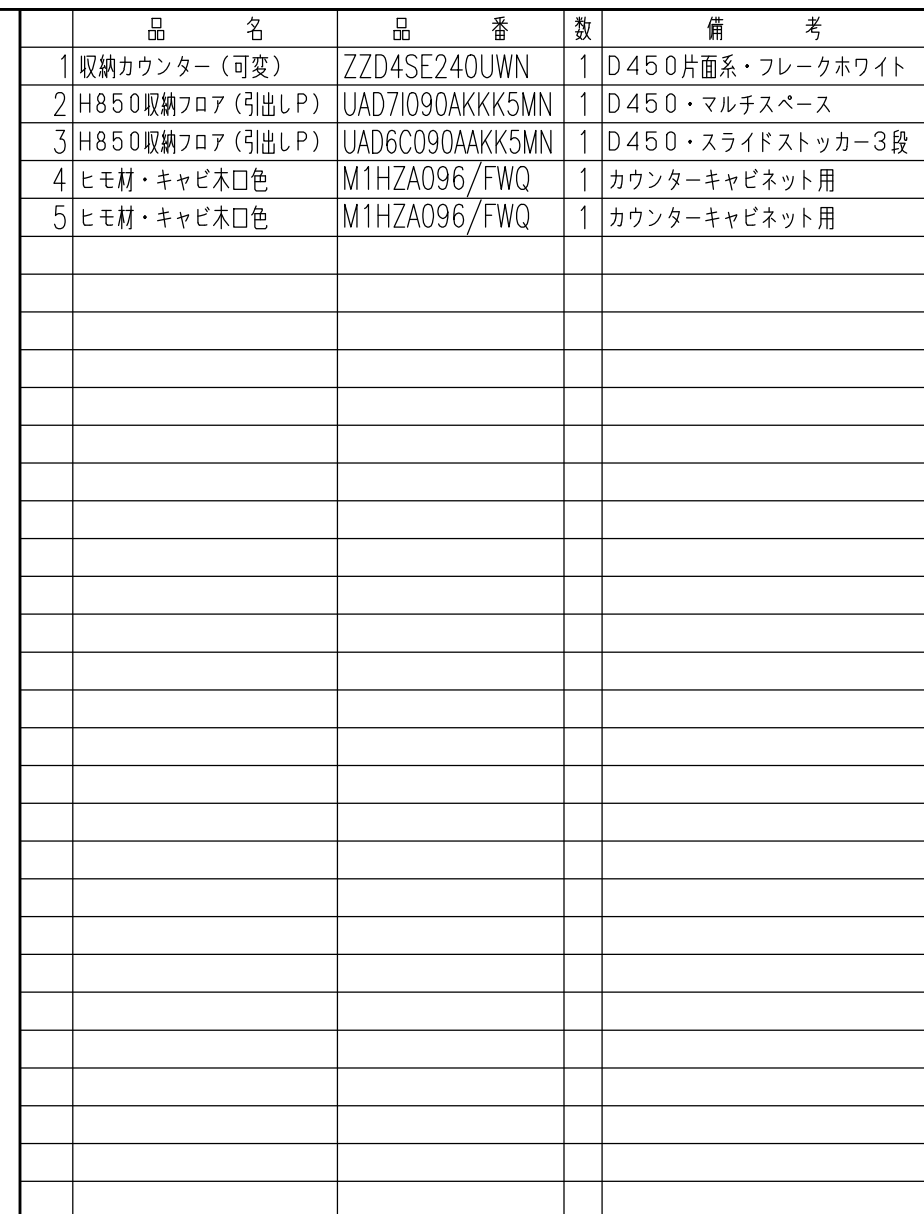



【ご注意】

- 記載のキャビネット寸法は扉前面までの呼び寸法です。キャビネット本体の寸法・扉厚み等は商品ガイドの巻末資料をご確認ください。
- 記載のワークトップ、カウンター、エンドパネル、サイドパネルの寸法は呼び寸法です。詳細寸法は商品ガイドの巻末資料をご確認ください。
- 取付・設置に際し、各製品の取付・設置説明書や図面の機能図を必ずお読み下さい。

特記事項 扉色 KK5:ブラックスタック 取手 [M]スリム取手（ブラック）	物件名	三室司 様邸	案件No.	図面名	担当	図面	図番 : 株式会社 LIXIL
			A2511DDDOEX74W	納まり図	栗野 友仁		
	仕様	ES21	見積No.	縮尺	日付		
			M25119283857-009-3	1/30	2026.01.13		


B面

B面

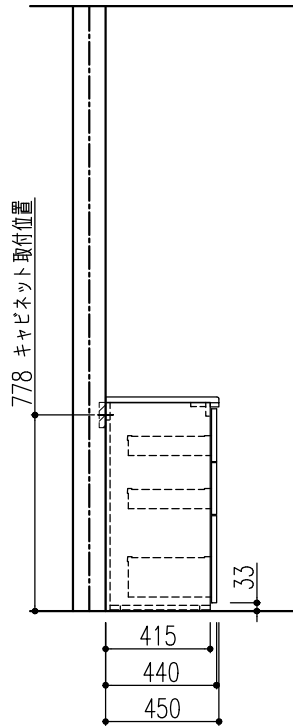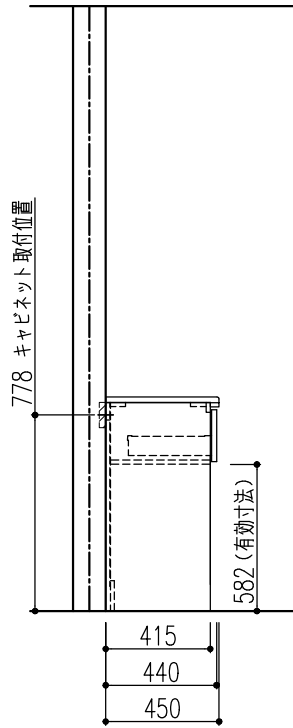

特記事項 扉色 KK5:ブラックスタック 取手 [M]スリム取手 (ブラック)	物件名	三室司 様邸	案件No.	図面名	担当	図面	図番
	仕様	ES21	A2511DDD0EX74W	納まり図	栗野 友仁		株式会社 LIXIL
			見積No.	縮尺	日付		
			M25119283857-009-3	1/30	2026.01.13		

■ 床の不陸に関して

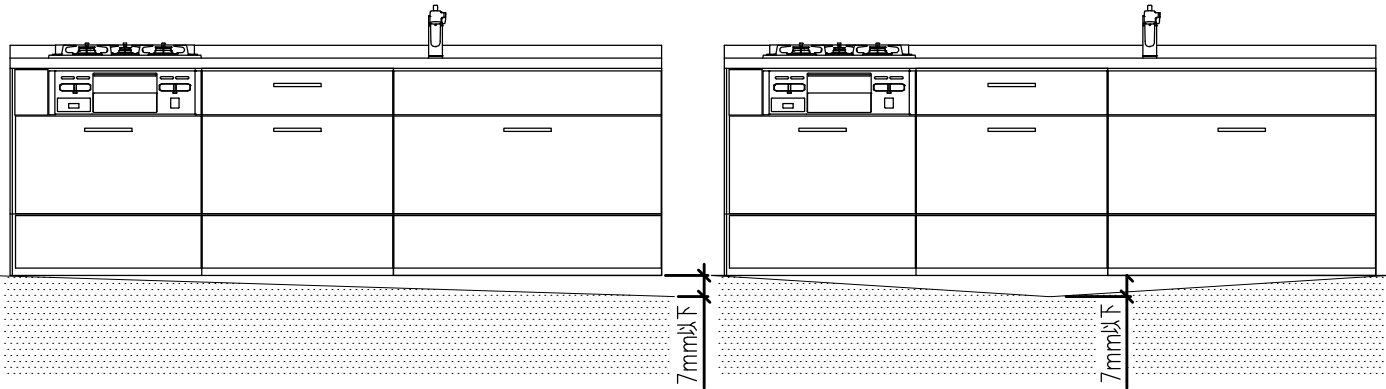

床の不陸は、7 m m 以下に抑えるようにしてください。不陸が大きい場合は、現場責任者に床の修正を依頼してください。
※キャビネット取付時には不陸調整スペーサー等で水平になるように設置してください。

特記事項 扉色 KK5:ブラックスタック 取手 [M]スリム取手（ブラック）	物件名	三室司 様邸	案件No.	図面名	担当	図面	図番
			A2511DDD0EX74W	機能図	栗野 友仁		株式会社 LIXIL
	仕様	ES 2 1	見積No.	縮尺	日付		
			M25119283857-009-3		2026.01.13		

■ キッチン取付者さま向け 動画コンテンツ ■


商品取付けの注意点を2次元コードでご視聴いただけます。

取付日より前に、是非ご確認ください。

1  — 

荷扱い・搬入


荷扱い・搬入

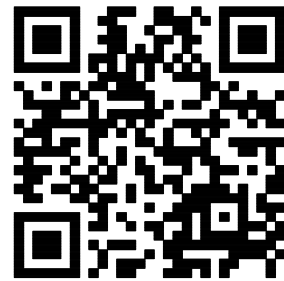

作成日：2024年10月01日



カウンター開梱搬入「養生ツール」

カウンター開梱搬入 「養生ツール」のご紹介

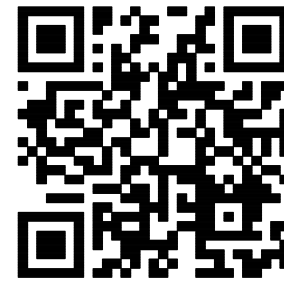

作成日：2024年10月01日

不陸の確認と調整

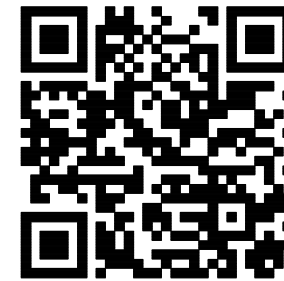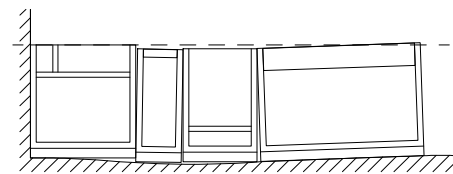

作成日：2024年02月07日



マグネットキッチンパネル

マグネット キッチンパネル 「取付・設置」ポイント





作成日：2024年03月06日

人造大理石カウンターL型キッチン

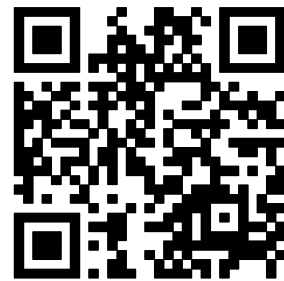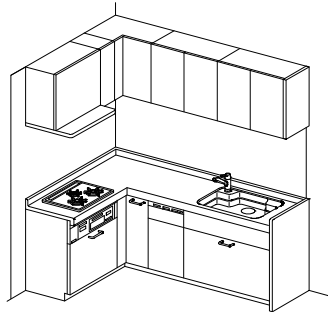

作成日：2024年02月07日

センターキッチン（ペニンシュラ型）



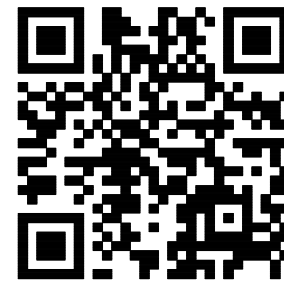
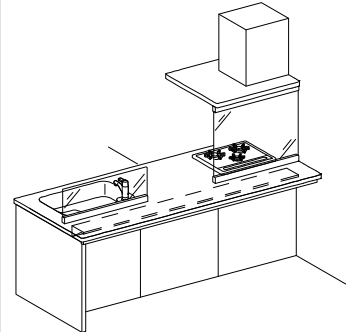


作成日：2024年02月07日

特記事項 扉色 KK5:ブラックスタック 取手 [M]スリム取手（ブラック）	物件名	三室司 様邸	案件No.	図面名	担当	図面	図番 :
			A2511DDD0EX74W	機能図	栗野 友仁		
	仕様	ES21	見積No.	縮尺	日付		株式会社 LIXIL
			M25119283857-009-3		2026.01.13		

■ キッチン取付者さま向け 動画コンテンツ ■

商品取付けの注意点を2次元コードでご視聴いただけます。
取付日より前に、是非ご確認ください。

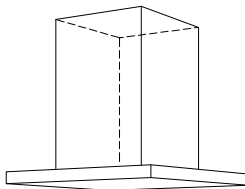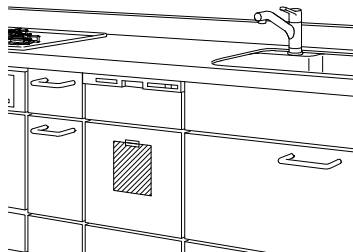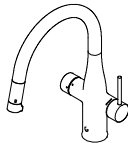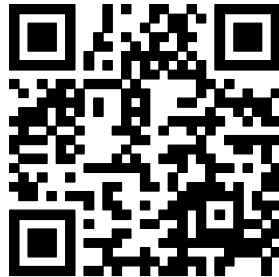センターフード型レンジフード (天吊りフード)  作成日：2024年06月03日 		I H加熱機器関連 I H加熱機器 仕切り板 作成日：2024年02月07日 		食器洗い乾燥機  作成日：2024年02月07日 		ミネラル浄水栓 Greentap  作成日：2024年06月03日 		
	特記事項 扉色 KK5:ブラックスタッコ 取手 [M]スリム取手 (ブラック)	物件名 仕様	三室司 様邸	案件No.	図面名	担当	図面	図番 : 株式会社 LIXIL
				A2511DDD0EX74W	機能図	栗野 友仁		
			ES21	見積No.	縮尺	日付		
				M25119283857-009-3		2026.01.13		