


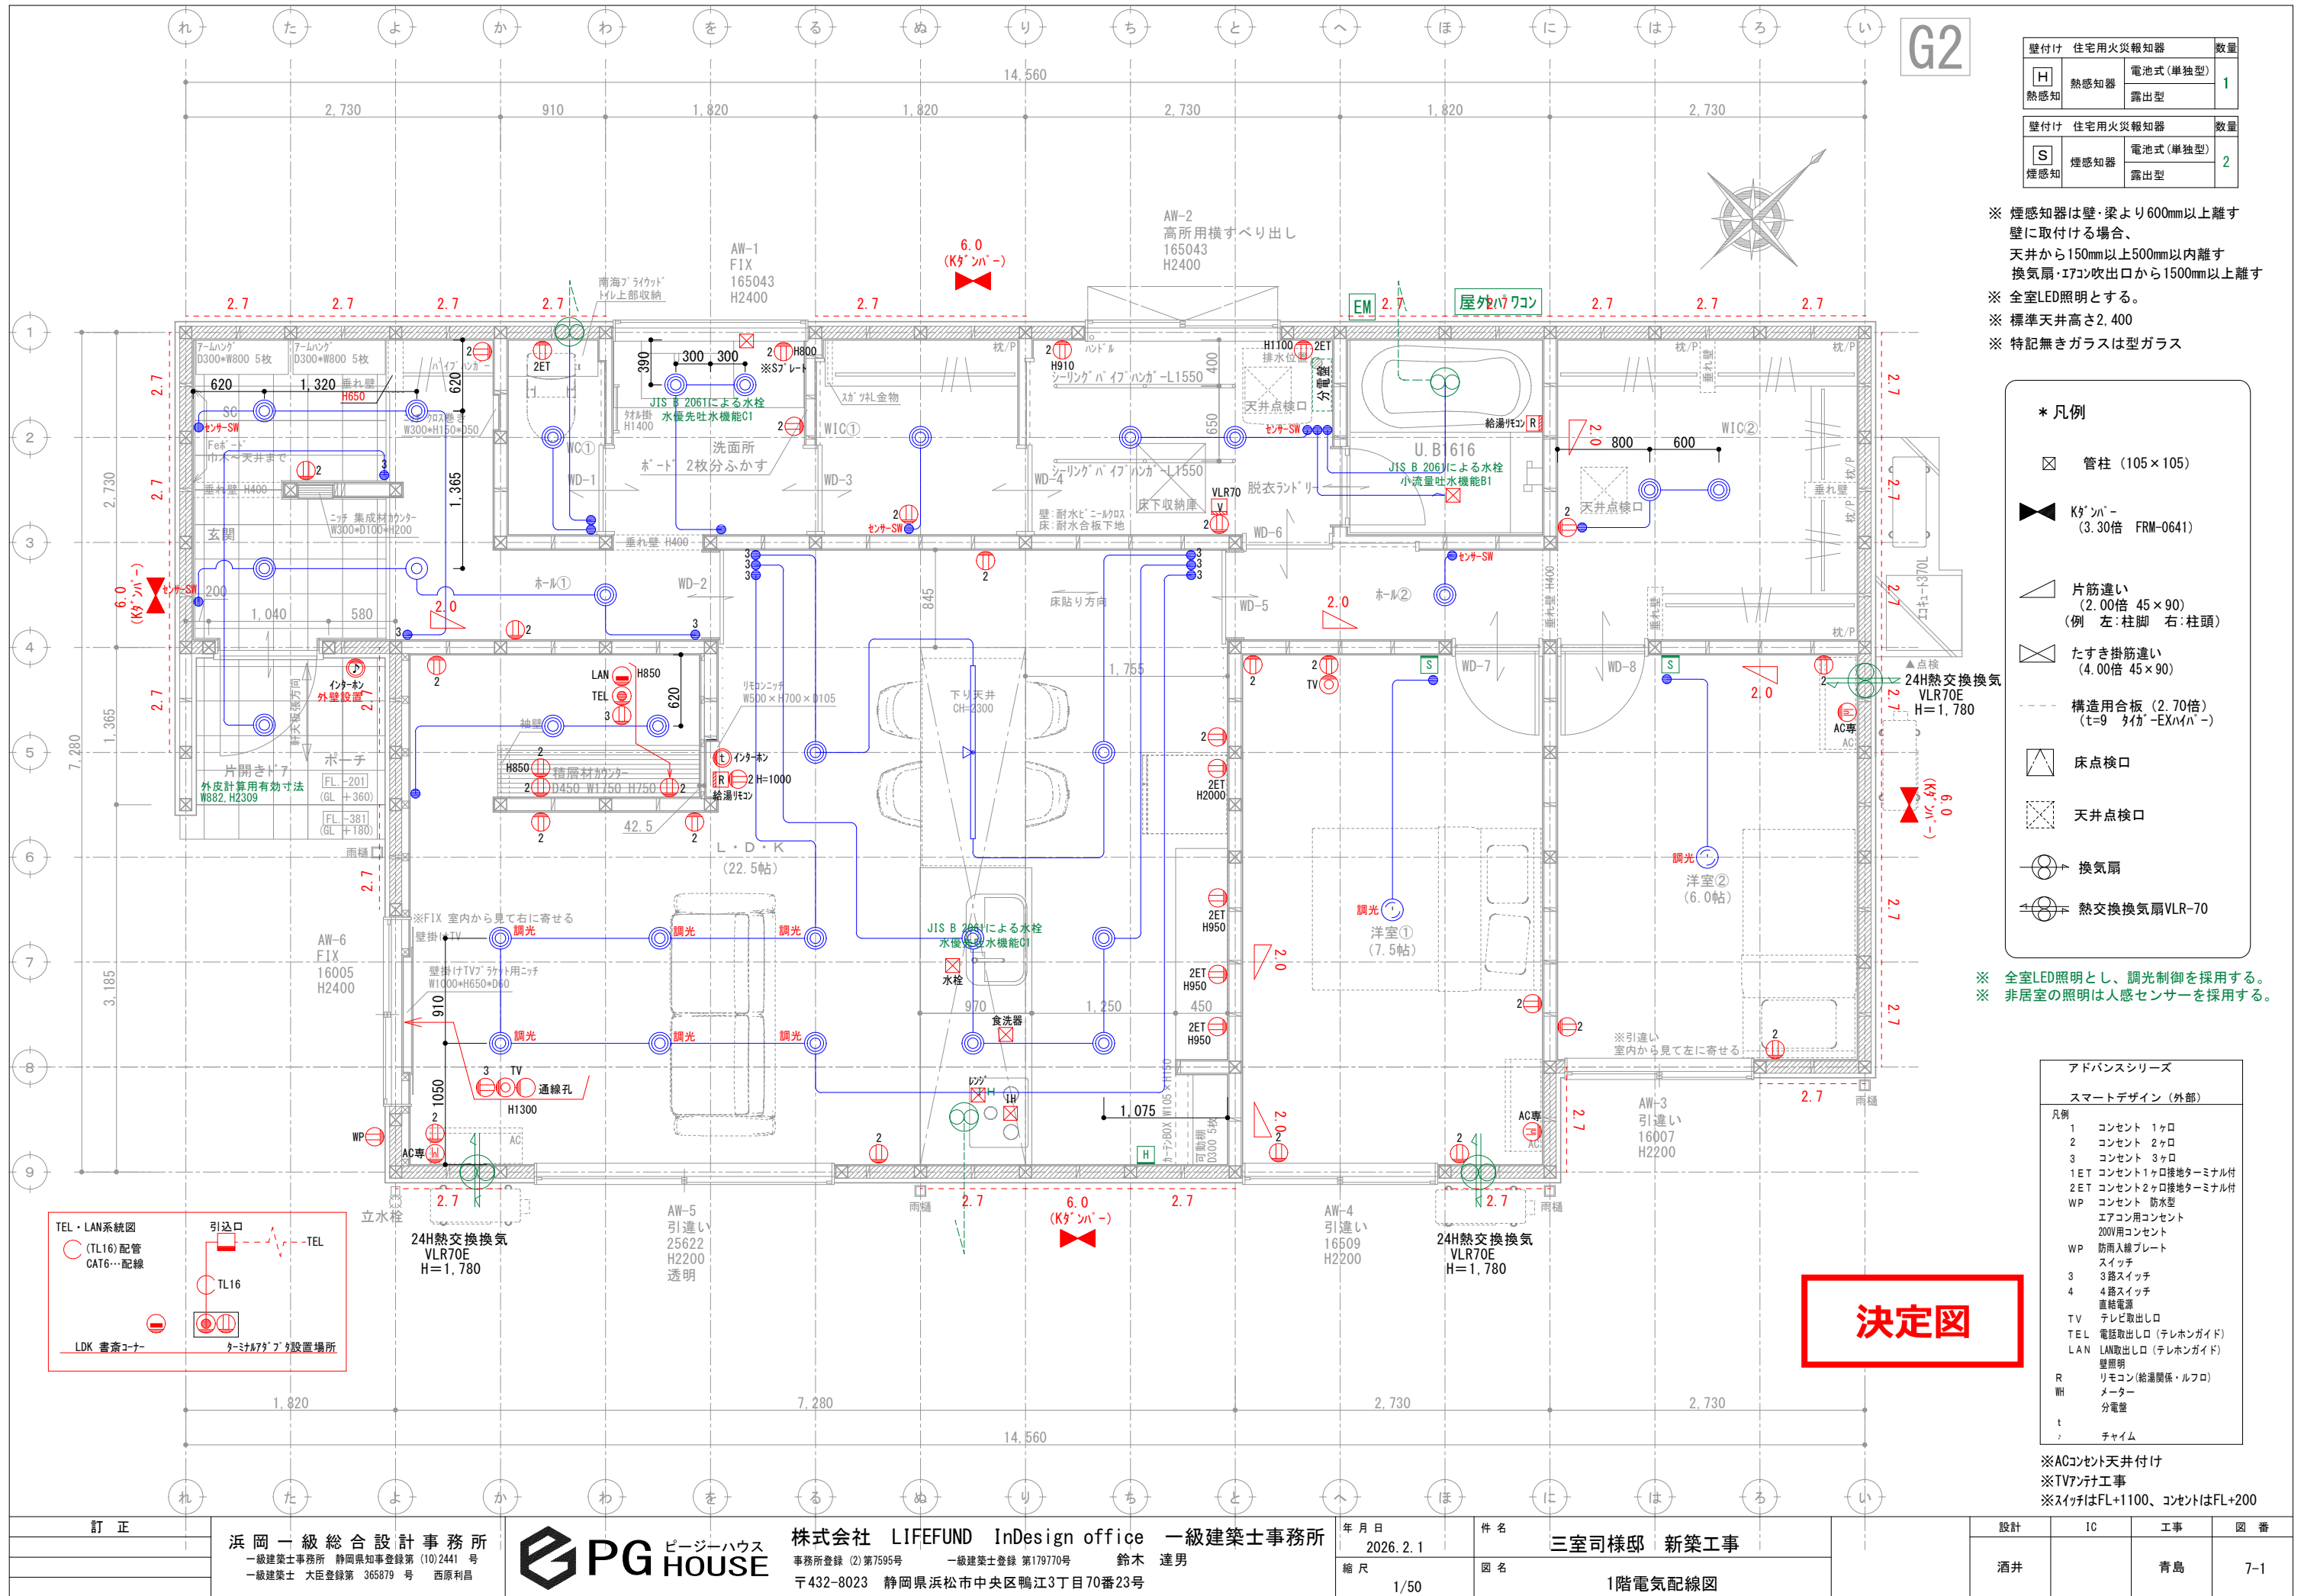

壁付け 住宅用火災報知器			数量
H	熱感知器	電池式 (単独型)	1
	露出型		
壁付け 住宅用火災報知器			数量
S	煙感知器	電池式 (単独型)	2
	露出型		

- ※ 煙感知器は壁・梁より600mm以上離す
壁に取付ける場合、
天井から150mm以上500mm以内離す
換気扇・エアコン吹出口から1500mm以上離す
- ※ 全室LED照明とする。
- ※ 標準天井高さ2,400
- ※ 特記無きガラスは型ガラス

- * 凡例**
- 管柱 (105×105)
 - Kダクト (3.30倍 FRM-0641)
 - 片筋違い (2.00倍 45×90)
(例 左:柱脚 右:柱頭)
 - たすき掛筋違い (4.00倍 45×90)
 - 構造用合板 (2.70倍)
(t=9 材種 EXハイバー)
 - 床点検口
 - 天井点検口
 - 換気扇
 - 熱交換換気扇VLR-70

- ※ 全室LED照明とし、調光制御を採用する。
- ※ 非居室の照明は人感センサーを採用する。

アドバンスシリーズ		
スマートデザイン (外部)		
凡例	1	コンセント 1ヶ所
	2	コンセント 2ヶ所
	3	コンセント 3ヶ所
	1ET	コンセント1ヶ所接地ターミナル付
	2ET	コンセント2ヶ所接地ターミナル付
	WP	コンセント 防水型
		エアコン用コンセント
		200V用コンセント
	WP	防雨入線プレート
		スイッチ
	3	3路スイッチ
	4	4路スイッチ
		直結電源
	TV	テレビ取出口
	TEL	電話取出口 (テレホンガイド)
	LAN	LAN取出口 (テレホンガイド)
	R	壁照明
	WH	リモコン (給湯関係・ルフロ)
	t	メーター
		分電盤
		チャイム

- ※ACコンセント天井付け
- ※TVアンテナ工事
- ※スイッチはFL+1100、コンセントはFL+200