

■ 仕 様			■ HEAT20 G2		
断熱工事		■ 床:カネライトフォーム t90 ■ 土間床等の外周:スタイロフォームAT t50 ■ 壁:アクアフォームLITE吹付 t90 ■ 天井:アクファフォームLITE吹付 t220			
床下換気		■ 基礎パッキン JOTO (玄関・UB周り:気密基礎パッキン)			
防虫防蟻		■ 土壌処理・木部 ガントナーMC			
■ 外 部 仕 上 表			■ 22条地域		
部位		仕上・仕様・メーカー		色番・品番	
屋根		■ ガルバリウム鋼板(t0.35)UK立平 ニスクカラーPro GH 軒先通気金物 日本住環境株式会社【REV-15】		GHK01 Sブラック	
パラペット笠木		■ なし			
破風・鼻隠		■ なし			
雨樋	(軒樋)	■ Panasonic サーフeskエアFS-I型		ブラック	
	(縦樋)	■ Panasonic S30角樋		ブラック	
軒天	屋根軒	■ なし			
	ポーチ軒	■ 神島化学 アルテザード		ウォルナットダーク	
	バルコニー軒	■ なし			
オーバーハング水切り		■ ガルバリウム鋼板 ※外壁合わせ JOTO:HF-A3550		ブラック	
外壁	通気金物(15mm)	■メイン	Knewエクセレージ・シマンフラット	光セラ	
	※下地面材:タイガーEXハイパー	■アクセントA	なし		
	防火認定 PC030BE-4028	■アクセントB	なし		
玄関ポーチ		■ 床 玄関に同じ		-	
基礎		■ 立上り巾木: モルタル刷毛引き		-	
基礎水切り金物		■ JOTO鋼板製 防鼠材付き水切り JOTO:WMF-N35		ブラック	
バルコニー	床・内壁	■ なし		-	
	笠木	■ なし			
外部建具		■ LIXIL EW(アルゴンガス高遮熱仕様LowEトリプルガラス クリア) ・SD、TSは、メーカー設定によるが、オペレーターハンドル優先とする ・オペレーター付サッシの場合は固定網戸とする ・グレモンハンドル式サッシの場合は可動網戸とする		外観 ブラック 内観 シェードオークforDesign ※樹脂パッキン・網戸付	
シャッター		■ なし			
軒天通気金物					
玄関扉		■ LIXIL ジエスタ2 K2仕様 LIXILファミロック タグキー×3 (電池式)		ドア型: M17 型 ドア色: ブラックウォールナット ハンドル: S型ハンドル 色 ブラック	
外部物干し金物		■			
換気フード		■ 局所換気扇(トイレ 浴室 キッチンフード) 防火ダンパー無		外気フード: ブラック	
		■ ダクトレス熱交換換気システム (日本スティーベル株式会社) VLR-70E 防火ダンパー無		外気フード: B ブラック 室内パネル マットグレー	



■ 構 造 概 要					
基礎	■ RCベタ基礎コンクリート				
通し柱・管柱	■ 構造用集成材 105×105		間柱	■ 集成材	
土台	■ 桧 105×105	大引き	■ 桧 90*90	筋交い	■ 構造用製材 火打梁 ■ 鋼製火打(当社基準により米松あり)
桁・梁	■ 構造用製材及び集成材		制震装置	■ Kダンパー (株)アイ・エム・エー	
■ 設 備 装 着 品					
住宅設備	部位	メーカー	商品名 ※ 詳細は見積り、プレゼン参照	見積りNo.	(日付)
	キッチン	LIXIL	■ ES I 型	見積り番号 : M25119283857-010-2	(日付) 2026.01.13
	バックカウンタ ※オプション	LIXIL	■ ES L1800(W900スライドストッカー+マルチスペース)	見積り番号 : M25119283857-010-3	(日付) 2026.01.13
	浴室	LIXIL	■ AX1616 PGハウス標準仕様	見積り番号 : M25119283857-010-1	(日付) 2026.01.13
	1Fトイレ	LIXIL	■ ベーシアシャワートイレ 白 ● タオル掛け: なし(支給品取付) タンク手洗 無し ● 紙巻き器: なし(支給品取付)	見積り番号 : M25119283857-010-5	(日付) 2026.01.13
	洗面台	LIXIL	■ カスタム バニティ	見積り番号 : M25119283857-010-4	(日付) 2026.01.13
			その他 ● タオル掛け: なし(支給品取付)		
給排水設備	給湯器	■ エコキュート370L Panasonic Sシリーズ スタンダードモデル 追い焚きフルオート			
	排水	■ 下水			
	外水栓	■ 1 カ所 (平面図参照)		■ 外部立栓柱: GM3-AL50BH3	
	外部ガーデンパン	■ 無し			
	その他	■ 洗濯機用単水栓: 緊急止水弁付 ■ 洗濯機用排水: トラップ金物(標準) ■ 排水さや管(長期優良住宅仕様)			
ガス配管設備	■ なし (配置図・平面図参照) ■ガス使用器具				
電気設備	インターホン	■ パナソニック VL-SE31XL			
	TVアンテナ	■ UHF + BS・110度CS/CSアンテナ [2K・4K・8K対応] ■ブラック ※電波状況によりホワイトになる可能性あり			
	エアコン	■ 設置場所:			
	ソーラー ※標準搭載	■ あり(Qセルズ) 12 枚 5.28 KW Re.RISE-NBC 440 (1722×1134×30) ※メーカーのモデルチェンジ等で後継品に変更される可能性あり ■ 屋外パワコン エネルギーマネジメントシステム Cube J			
その他					

決定図

決定図

	浜 岡 一 級 総 合 設 計 事 務 所 一級建築士事務所 静岡県知事登録第 (10)2441 号 一級建築士 大臣登録第 365879 号 西原利昌	 株式会社 LIFEFUND InDesign office 一級建築士事務所 事務所登録 (2)第7595号 一級建築士登録 第179770号 鈴木 達男 〒432-8023 静岡県浜松市中央区鴨江3丁目70番23号	年 月 日	2026.2.1	件名	三室司 様邸 新築工事		設計	IC	工務	図 番
			縮尺		図面	仕上表 1		酒井		青島	1-1


G2

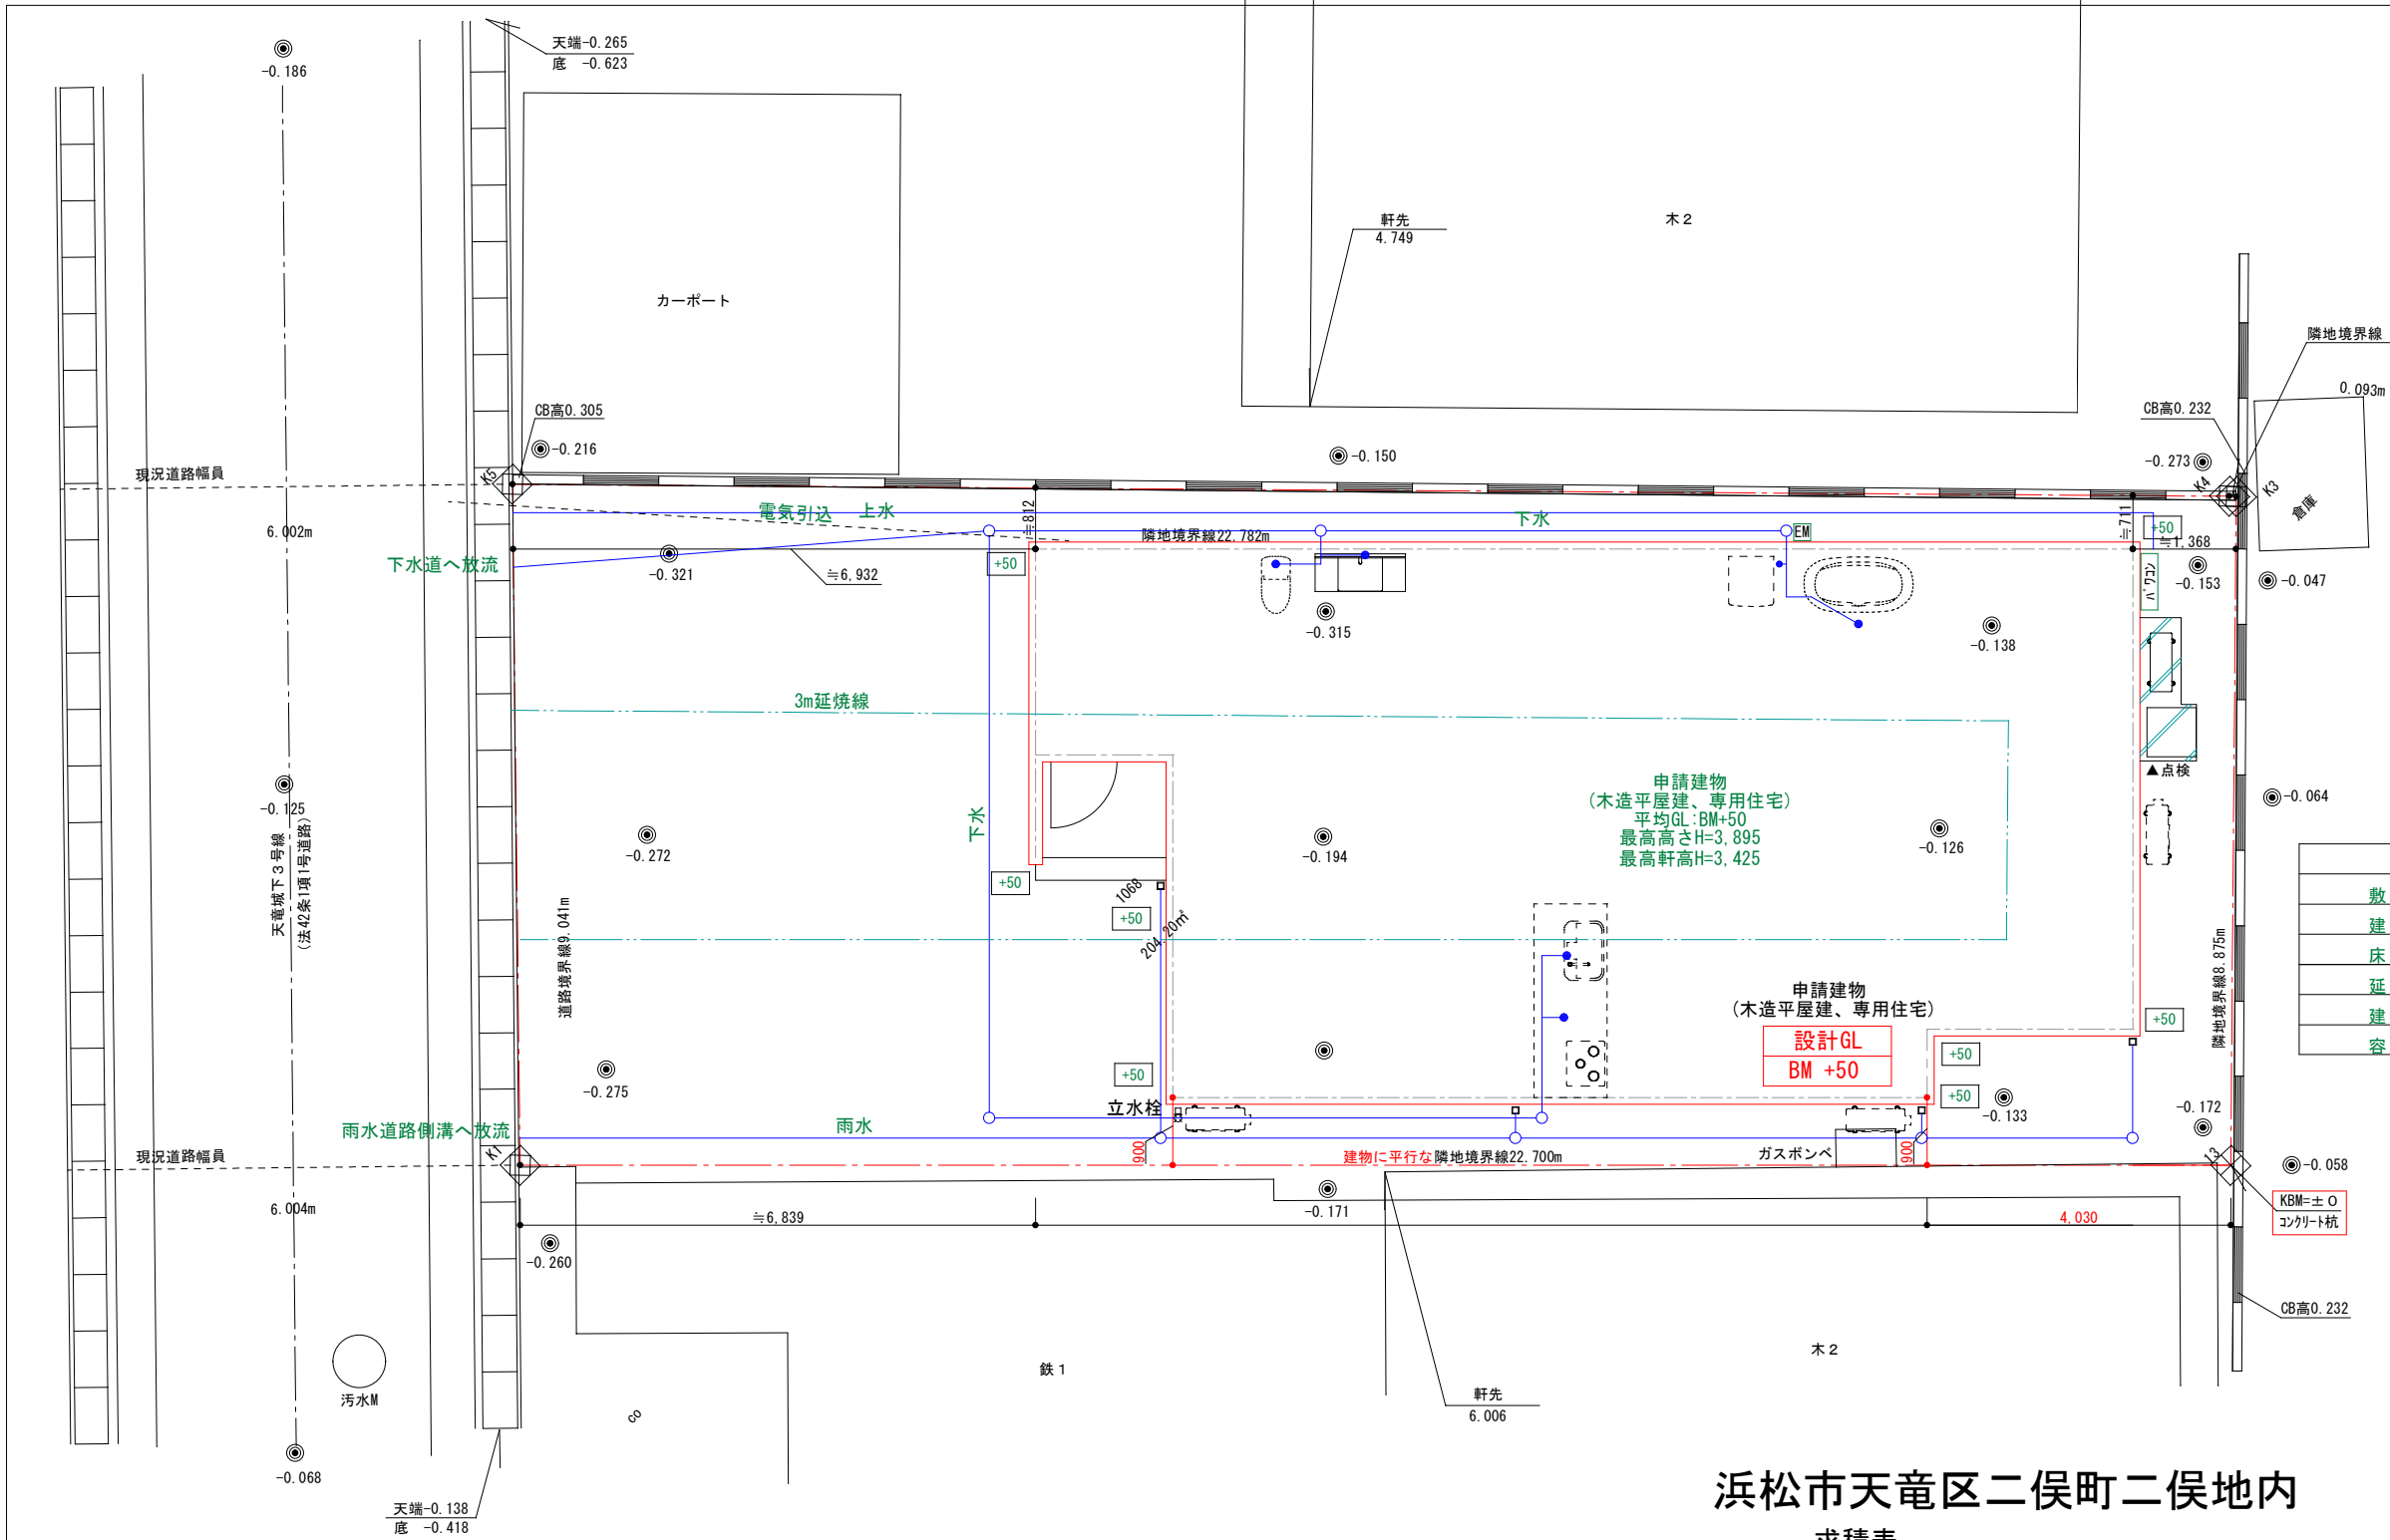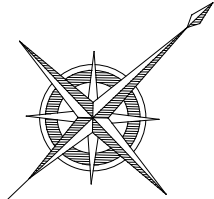

トータル面積表		(㎡)
敷地面積		204.20
建築面積		97.71
床面積 1階		95.23
延床面積		95.23
建蔽率	$(97.71/204.20) \times 100$	47.86%
容積率	$(95.23/204.20) \times 100$	46.64%

盛土規制法による切土盛土無し
道路斜線制限については、明らかに適合する。
北側斜線制限については、明らかに適合する。
平均地盤面について
申請建物の周囲の平均地盤面高さをBM+50とする。


求積図 (1/250)

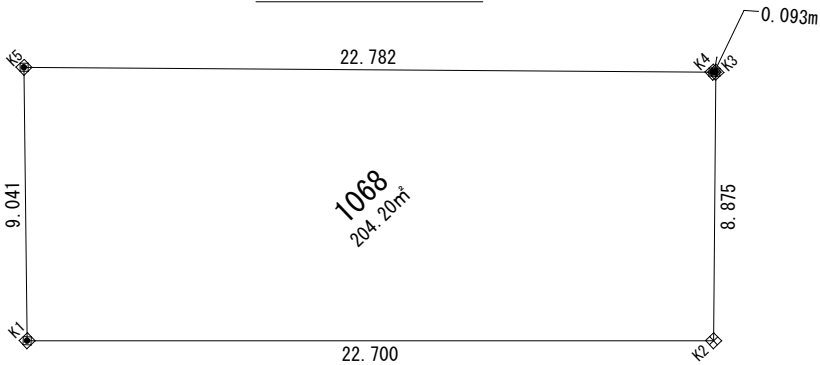

浜松市天竜区二俣町二俣地内
求積表

地番	1068			
NO	X _n	Y _n	Y _{n+1} - Y _{n-1}	X _n × (Y _{n+1} - Y _{n-1})
K1	-5.585	-4.018	10.221	-57.084285
K2	-21.281	12.381	22.589	-480.716509
K3	-14.920	18.571	6.127	-91.414840
K4	-14.851	18.508	-16.411	243.719761
K5	1.017	2.160	-22.526	-22.908942
合計				-408.404815
合計面積				204.2024075
地積				204.20 m ²

決定図

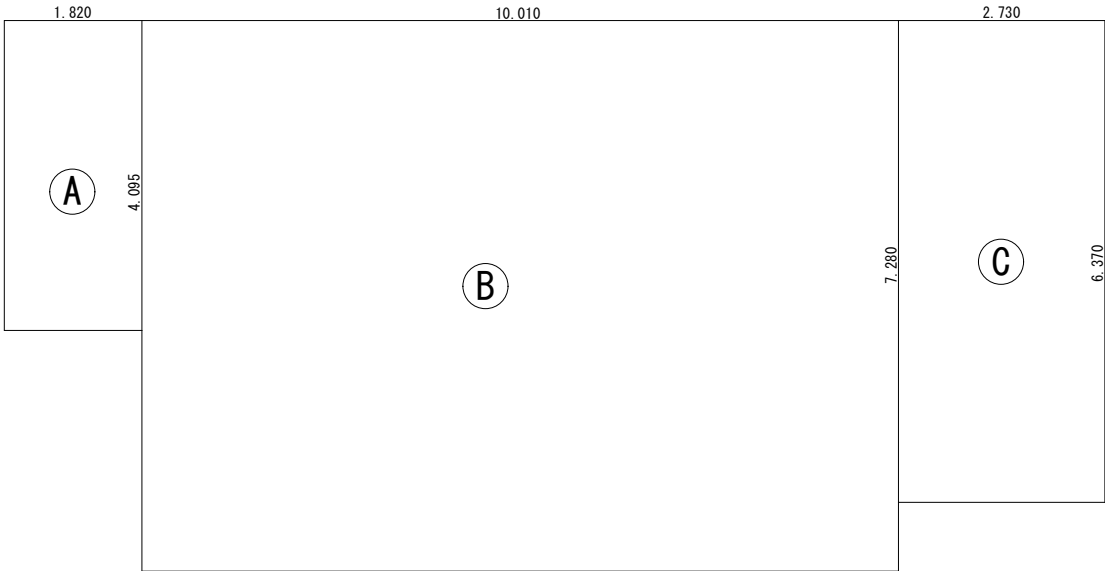


建築面積求積図 S=1/100

建築面積求積表

番号	計算式	(m)	面積 (㎡)
Ⓐ	1.820 × 4.095		7.4529
Ⓑ	10.010 × 7.280		72.8728
Ⓑ	2.730 × 6.370		17.3901
合計			97.7158 97.71 (29.5坪)

1階床面積求積表

番号	計算式	(m)	面積 (㎡)
①	1.820 × 2.730		4.9686
②	10.010 × 7.280		72.8728
③	2.730 × 6.370		17.3901
合計			95.2315 95.23 (28.8坪)

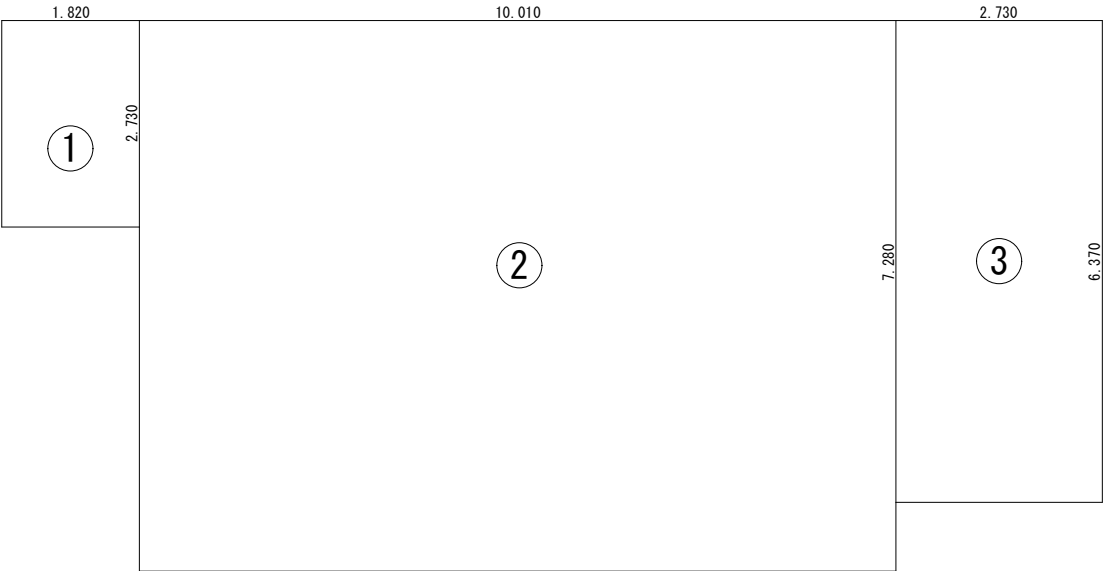


1階床面積図 S=1/100

延べ床面積表

	番号	(m)	面積 (㎡)
1階床面積	① ② ③		95.23
2階床面積			
合計			95.23 (28.8坪)

決定図

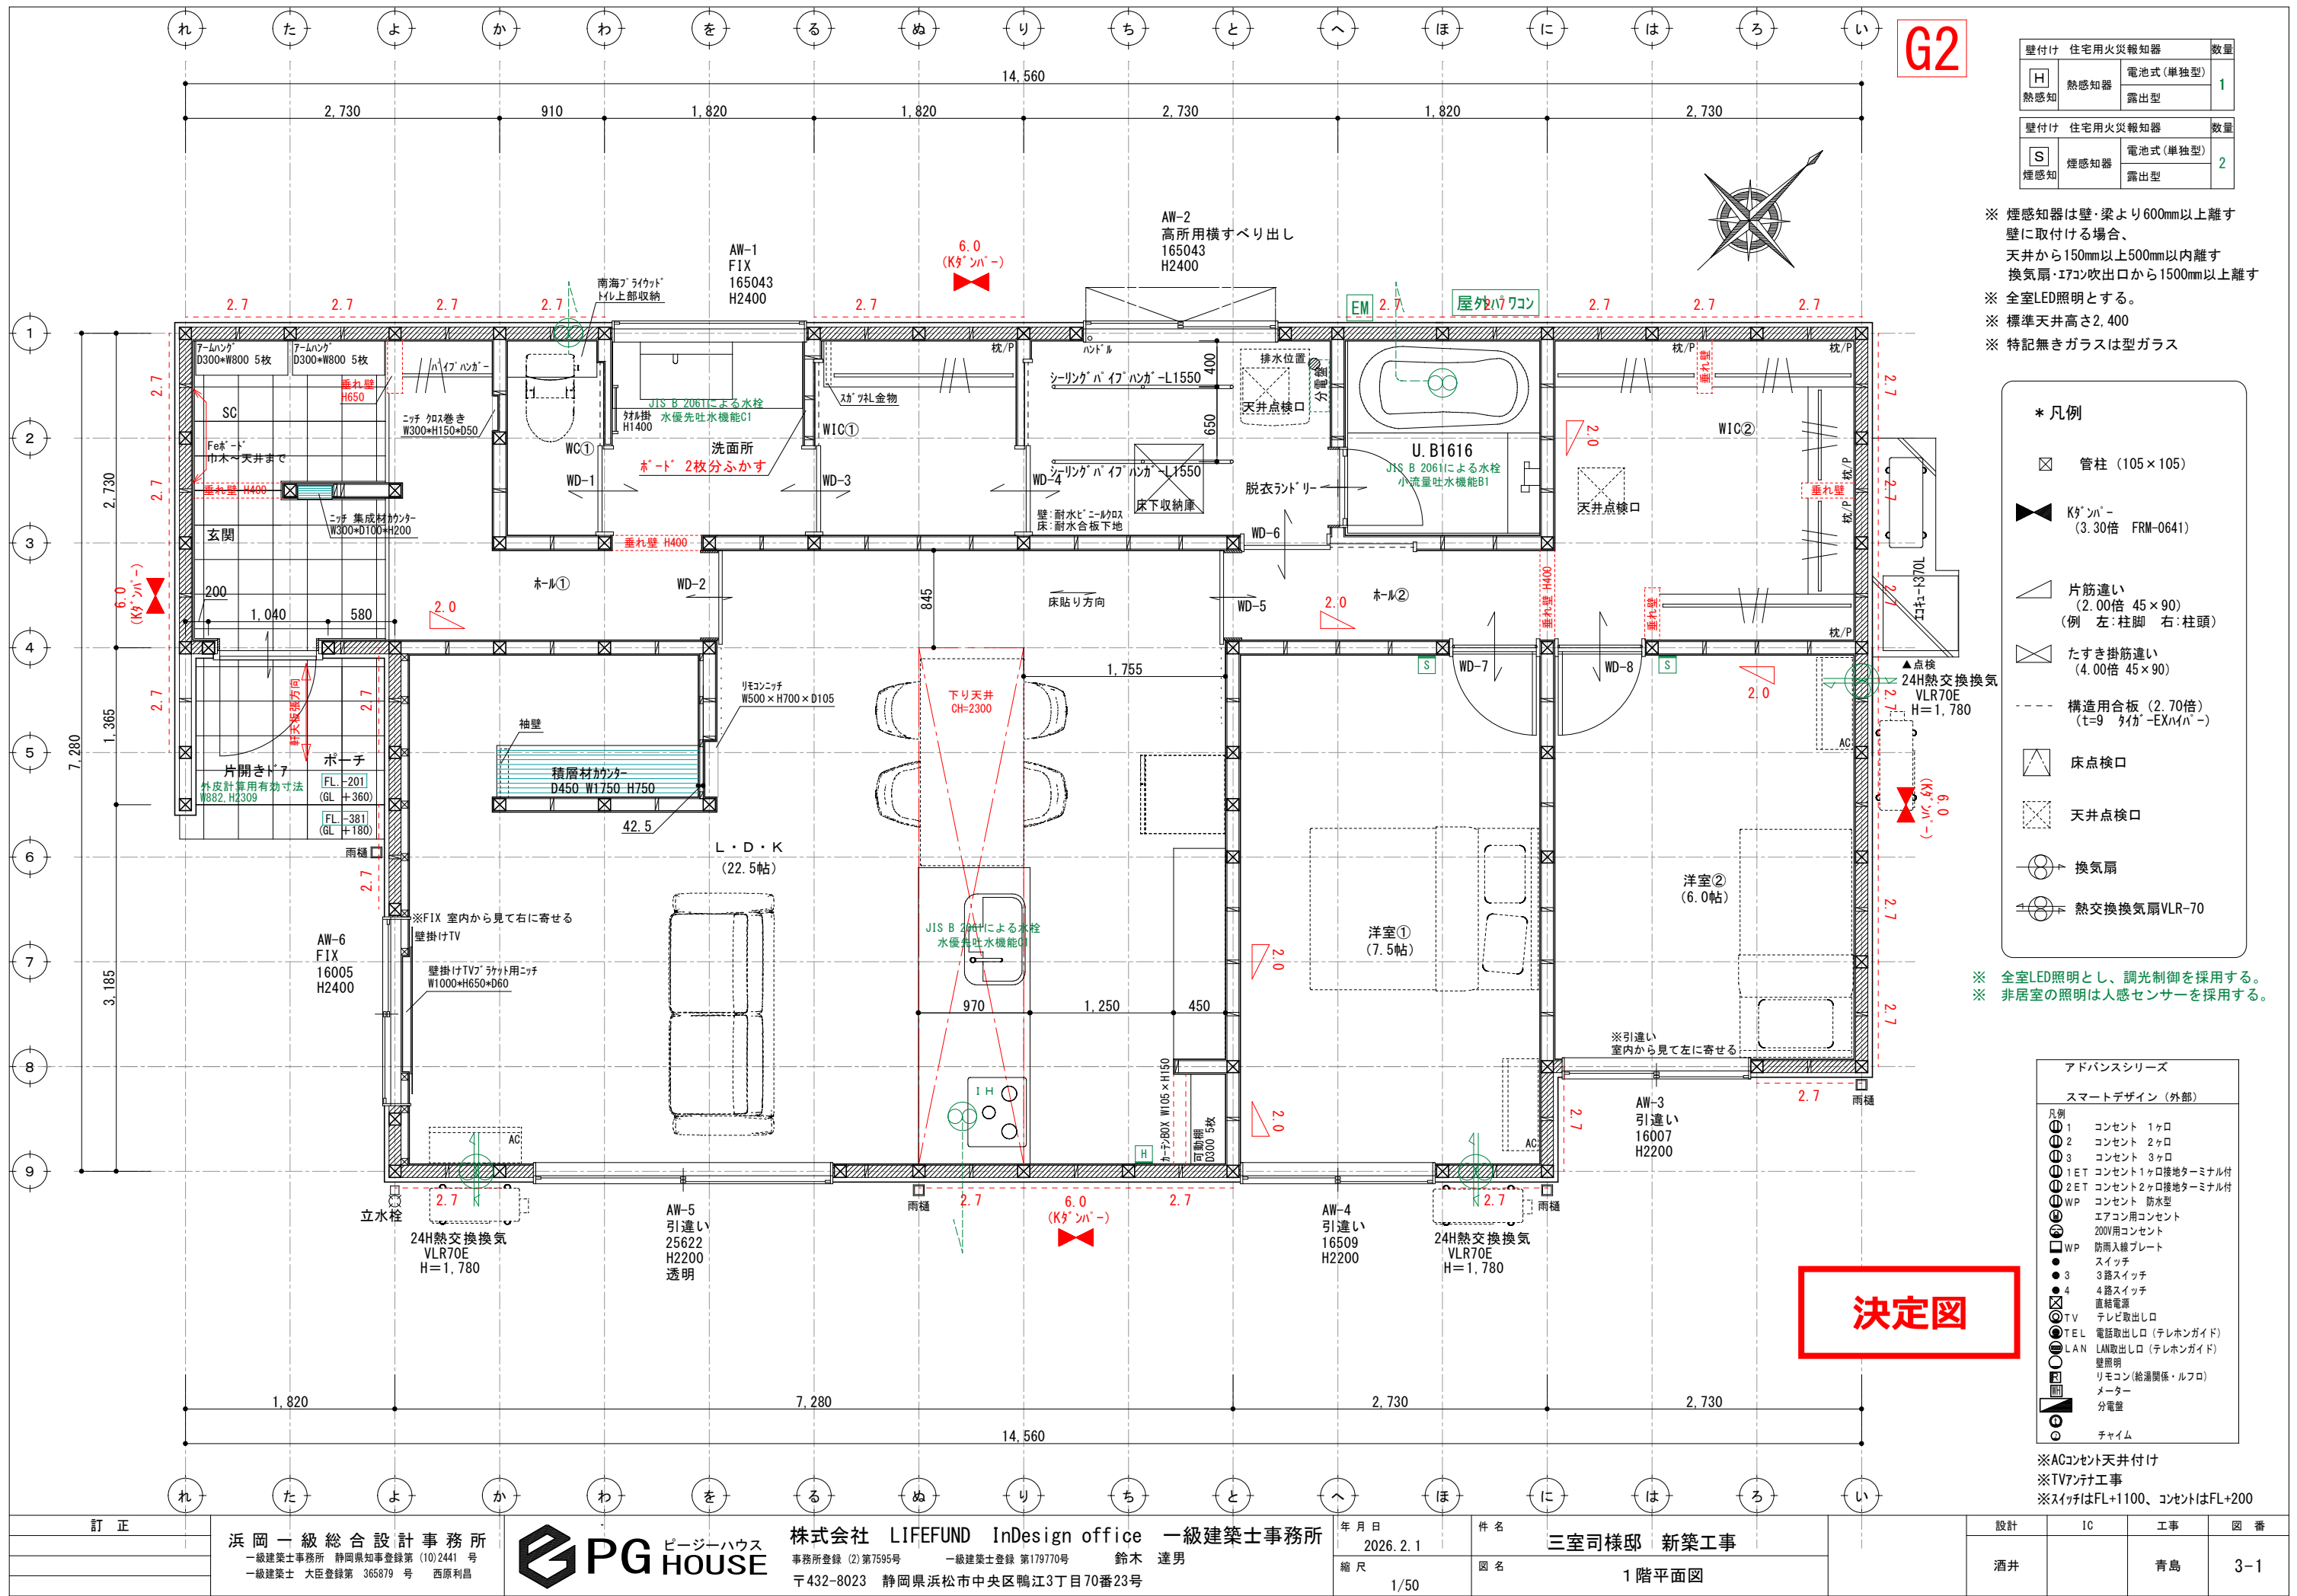

壁付け 住宅用火災報知器			数量
H	熱感知器	電池式(単独型)	1
	露出型		
壁付け 住宅用火災報知器			数量
S	煙感知器	電池式(単独型)	2
	露出型		

※ 煙感知器は壁・梁より600mm以上離す壁に取付ける場合、天井から150mm以上500mm以内離す換気扇・エアコン吹出口から1500mm以上離す

※ 全室LED照明とする。

※ 標準天井高さ2,400

※ 特記無きガラスは型ガラス

- * 凡例**
- 管柱 (105×105)
 - Kダクト (3.30倍 FRM-0641)
 - 片筋違い (2.00倍 45×90) (例: 左: 柱脚 右: 柱頭)
 - たすき掛筋違い (4.00倍 45×90)
 - 構造用合板 (2.70倍) (t=9 材質: EXハイパー)
 - 床点検口
 - 天井点検口
 - 換気扇
 - 熱交換換気扇 VLR-70

※ 全室LED照明とし、調光制御を採用する。

※ 非居室の照明は人感センサーを採用する。

アドバンスシリーズ	
スマートデザイン (外部)	
凡例	
1	コンセント 1ヶ所
2	コンセント 2ヶ所
3	コンセント 3ヶ所
1 ET	コンセント1ヶ所接地ターミナル付
2 ET	コンセント2ヶ所接地ターミナル付
WP	コンセント 防水型
	エアコン用コンセント
	200V用コンセント
WP	防雨入線プレート
	スイッチ
3	3路スイッチ
4	4路スイッチ
	直結電源
TV	テレビ取出口
TEL	電話取出口 (テレホンガイド)
LAN	LAN取出口 (テレホンガイド)
	壁照明
	リモコン (給湯関係・ルフロ)
	メーター
	分電盤
	チャイム


※ACコンセント天井付け

※TVアンテナ工事

※スイッチはFL+1100、コンセントはFL+200



GX住宅 (Cube J付)

太陽光あり

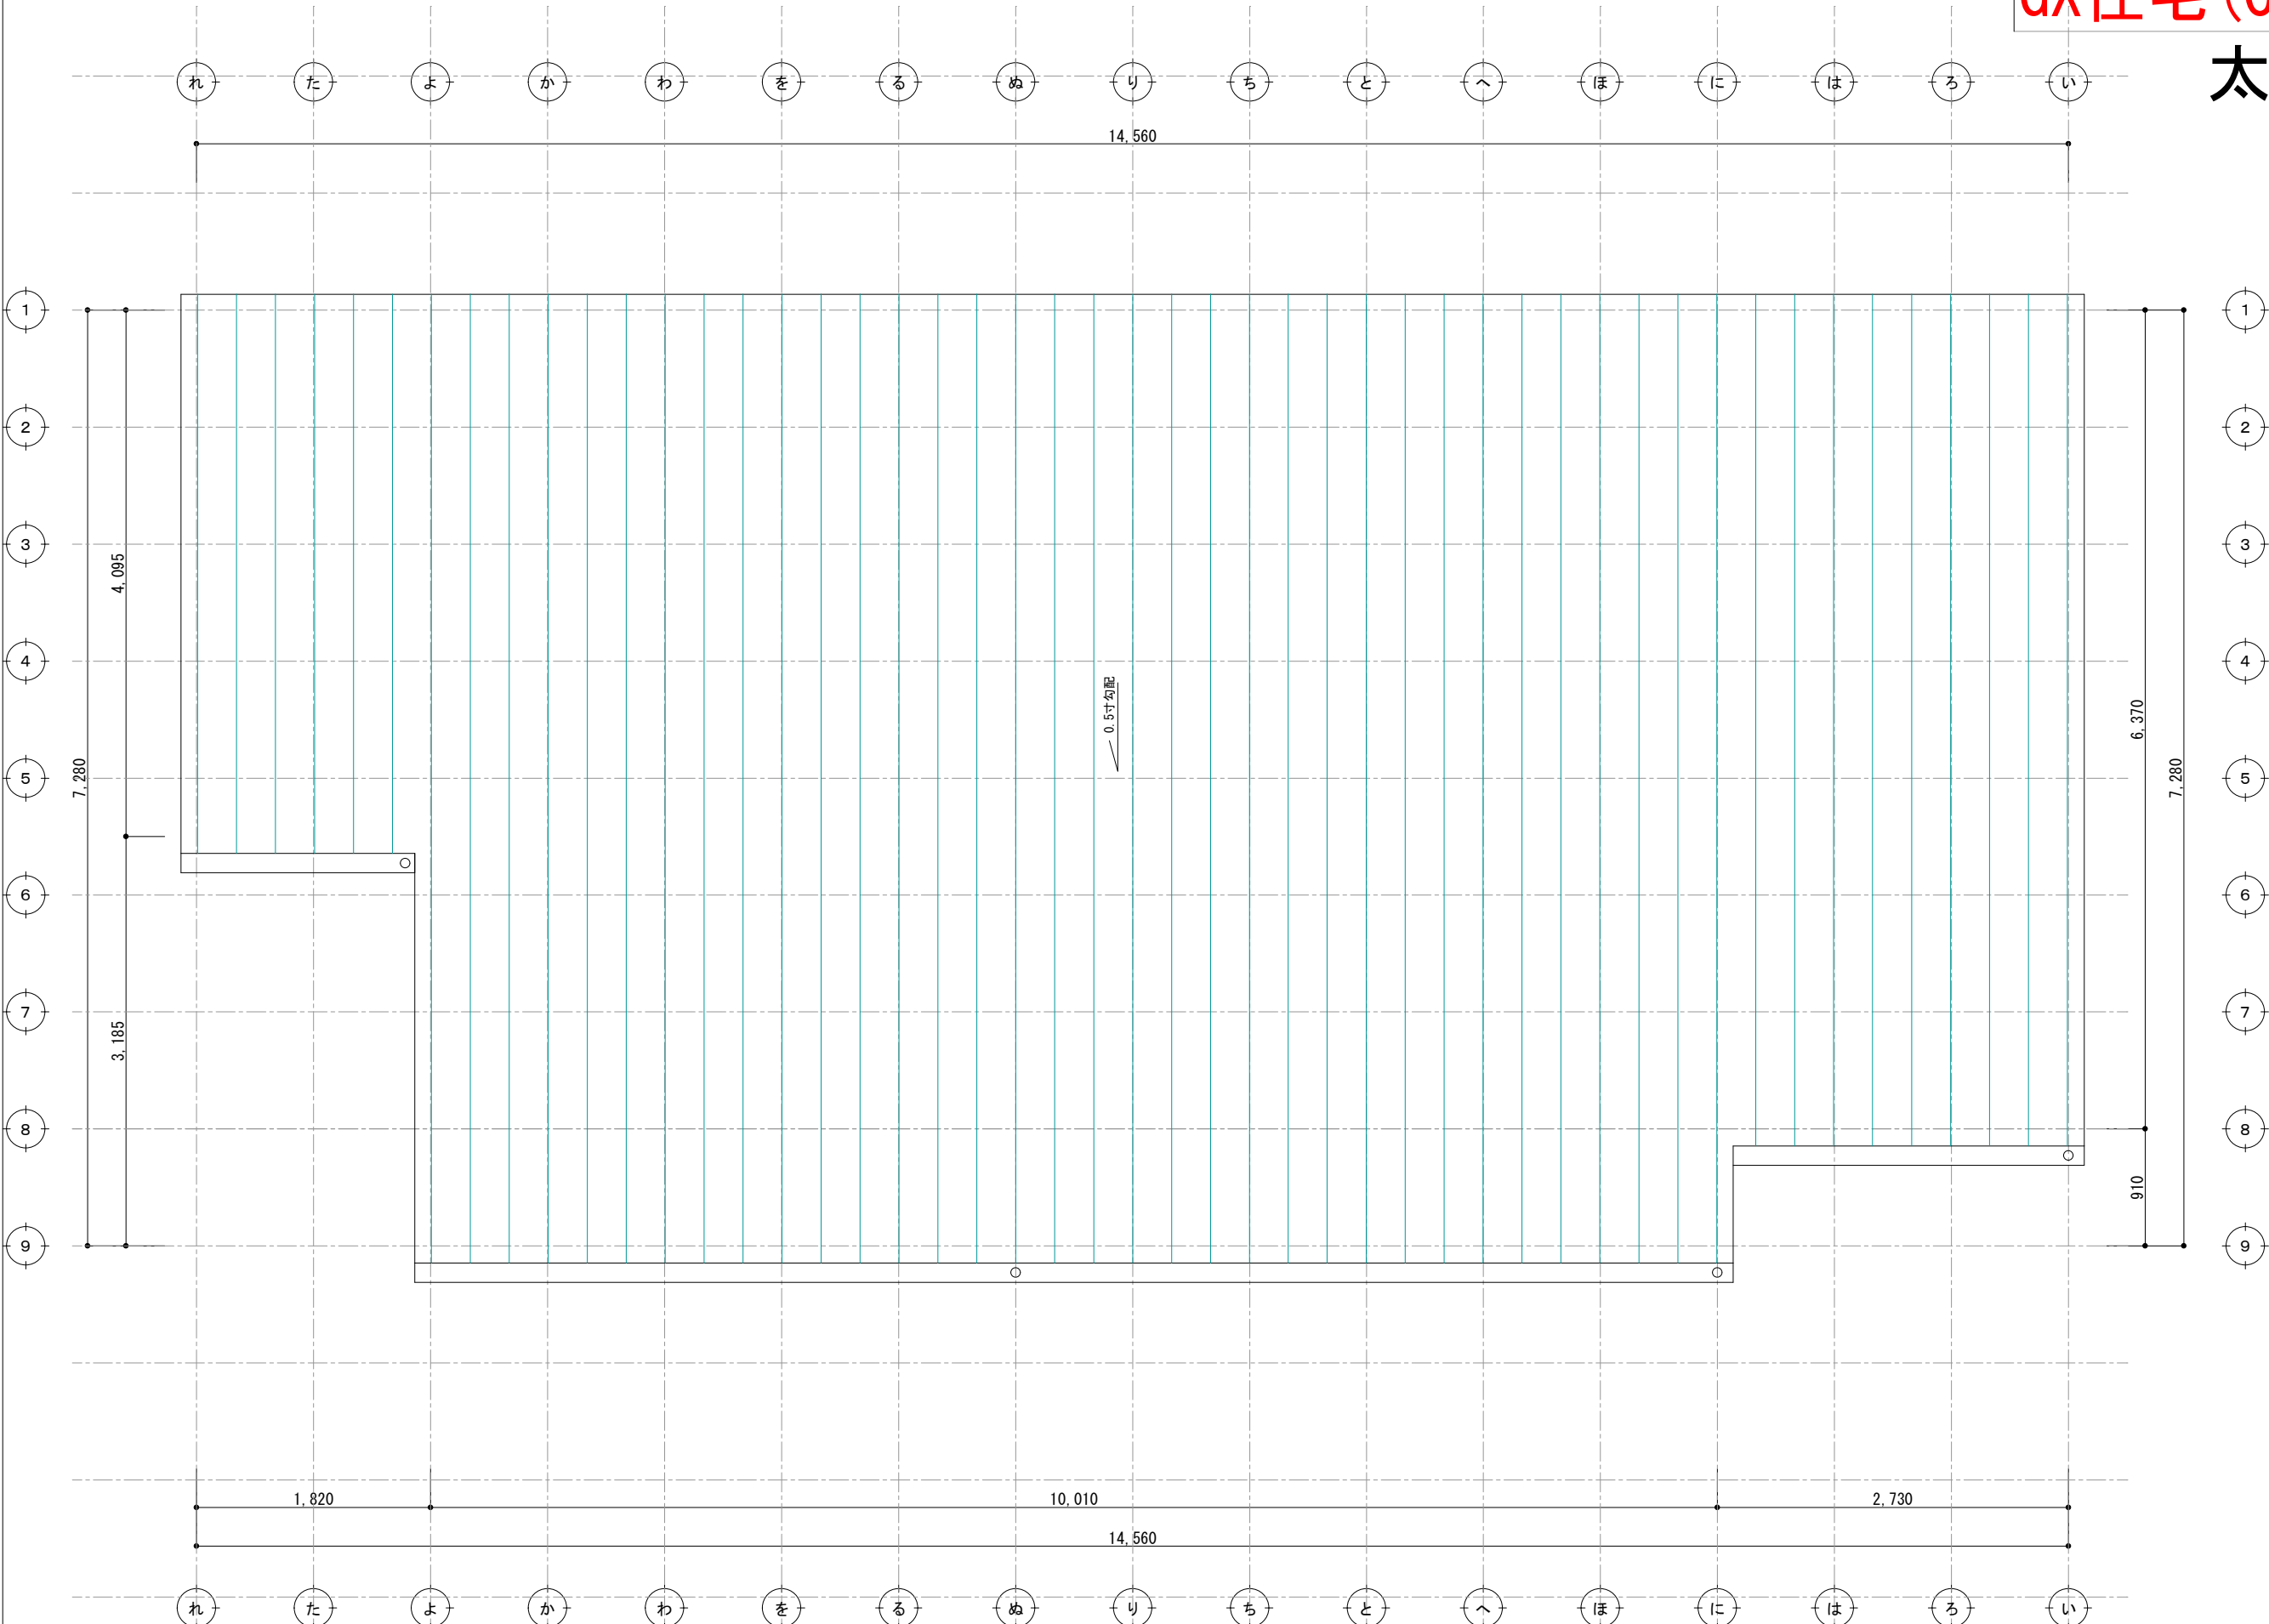

決定図

訂 正	浜 岡 一 級 総 合 設 計 事 務 所			株式会社 LIFEFUND InDesign office 一級建築士事務所		年 月 日	件 名		設計	IC	工事	図 番
	一級建築士事務所 静岡県知事登録第 (10)2441 号			事務所登録 (2) 第7595号 一級建築士登録 第179770号 鈴木 達男		2026. 2. 1	三室司様邸 新築工事					
	一級建築士 大臣登録第 365879 号 西原利昌			〒432-8023 静岡県浜松市中央区鴨江3丁目70番23号		縮 尺	図 名					
				1/100	屋根伏図							












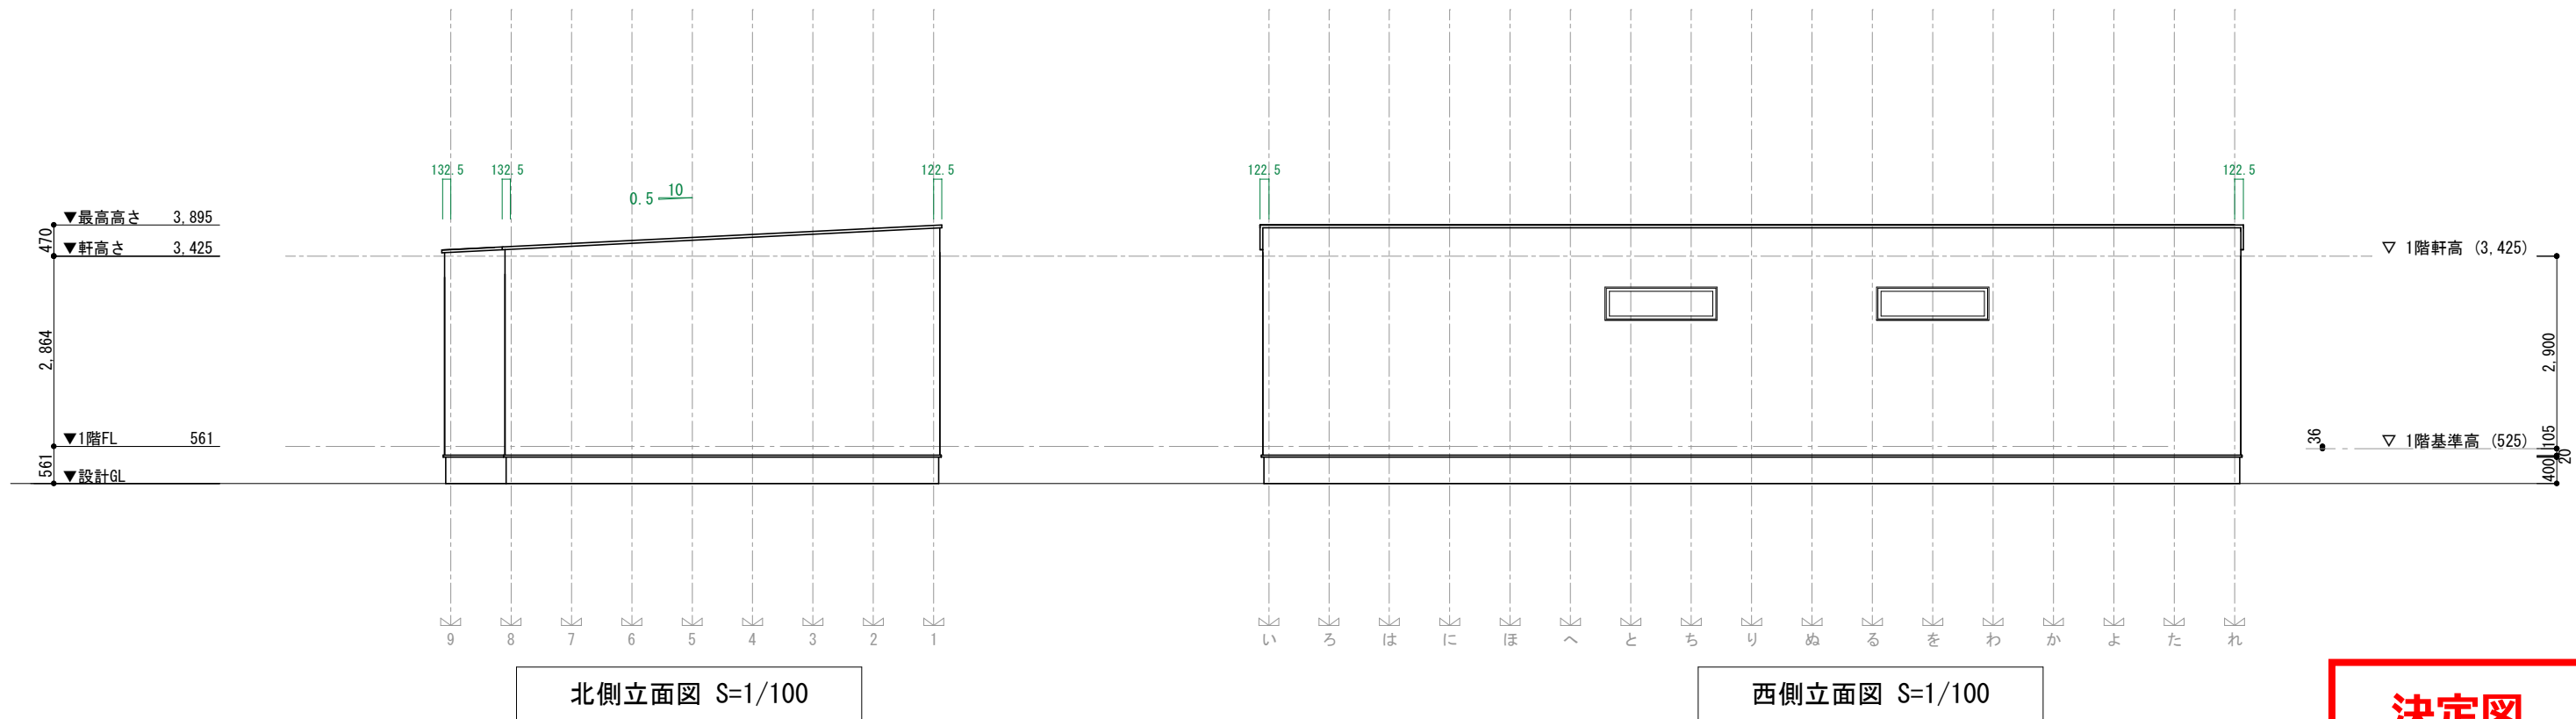
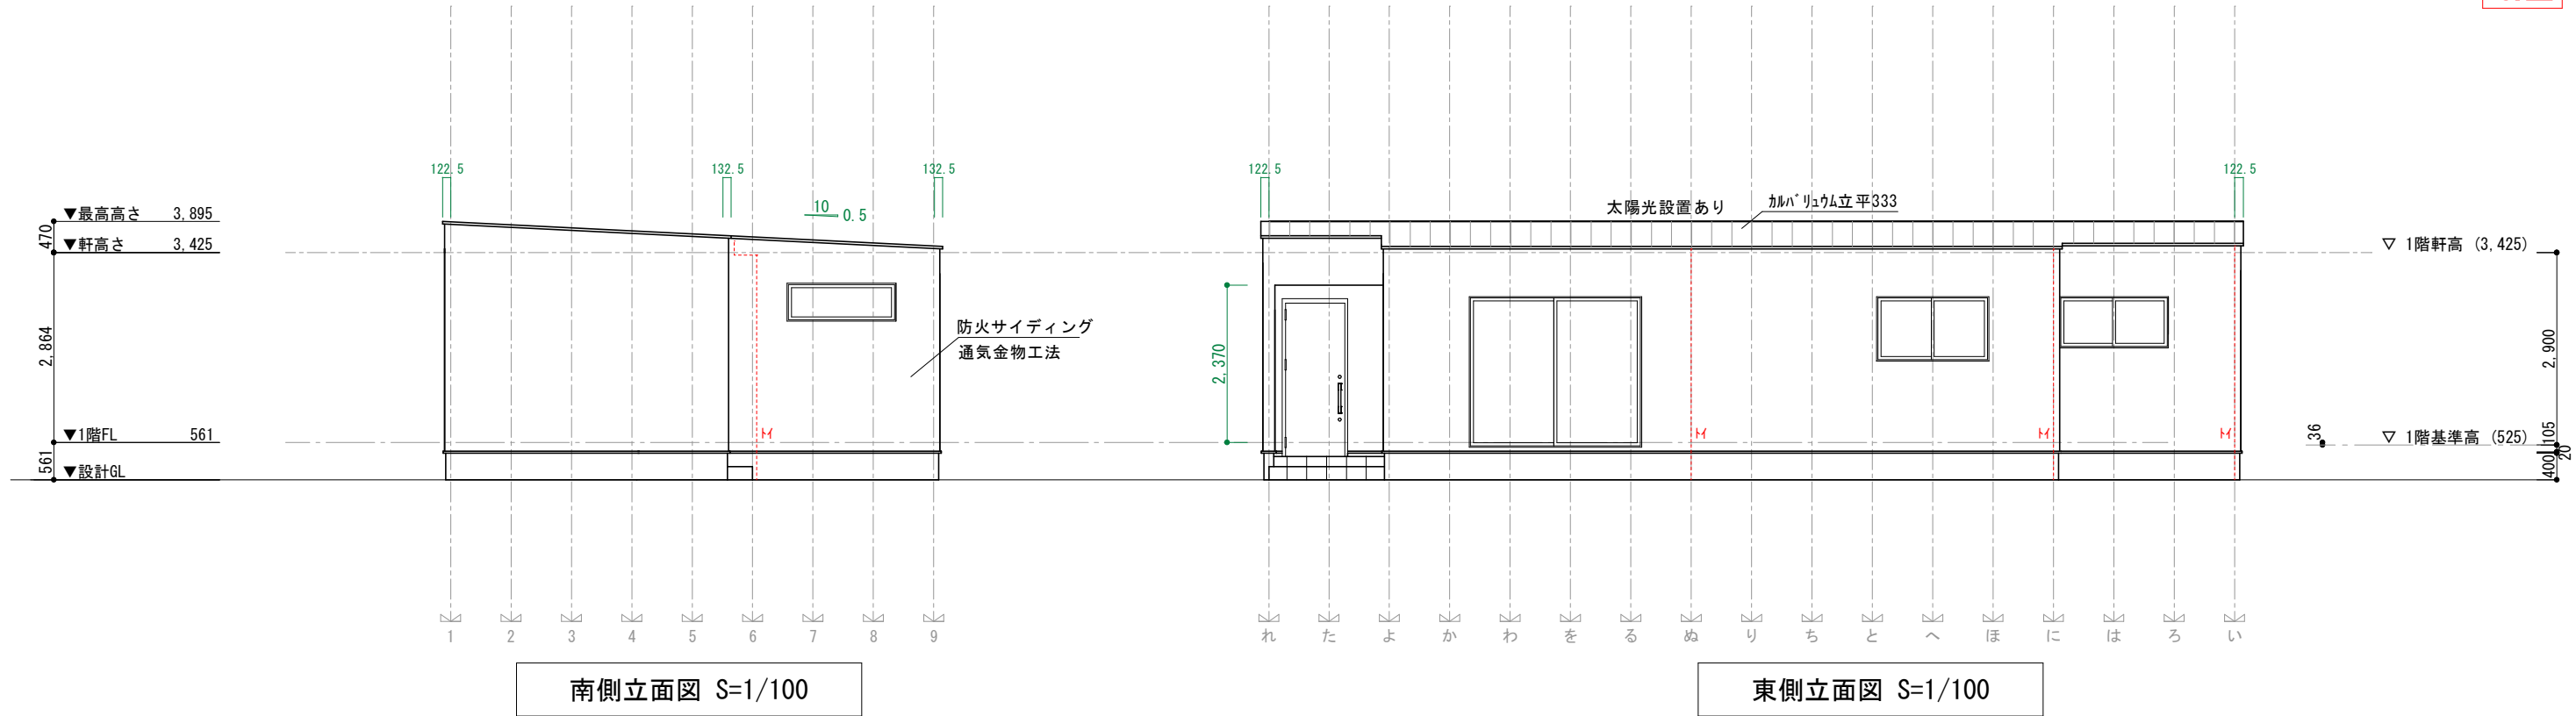


決定図

訂 正	浜 岡 一 級 総 合 設 計 事 務 所 一級建築士事務所 静岡県知事登録第 (10)2441 号 一級建築士 大臣登録第 365879 号 西原利昌		株式会社 LIFE FUND InDesign office 一級建築士事務所 事務所登録 (2) 第7595号 一級建築士登録 第179770号 鈴木 達男 〒432-8023 静岡県浜松市中央区鴨江3丁目70番23号	年 月 日	件 名		設計	IC	工事	図 番
				2026. 2. 1	三室司様邸 新築工事					
				縮 尺	図 名					
				1/100	立面図		酒井		青島	4




訂 正	浜 岡 一 級 総 合 設 計 事 務 所 一級建築士事務所 静岡県知事登録第 (10)2441 号 一級建築士 大丘登録第 365879 号 西原利昌		株式会社 LIFEFUND InDesign office 一級建築士事務所 事務所登録 (2)第7595号 一級建築士登録 第179770号 鈴木 達男 〒432-8023 静岡県浜松市中央区鴨江3丁目70番23号	年 月 日	件 名	設計	IC	工事	図 番
				2026. 2. 1	三室司様 邸新築工事				
				縮 尺	図 名				
				1/30	矩計図				

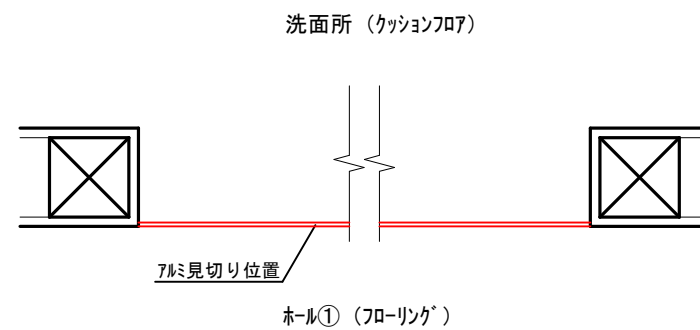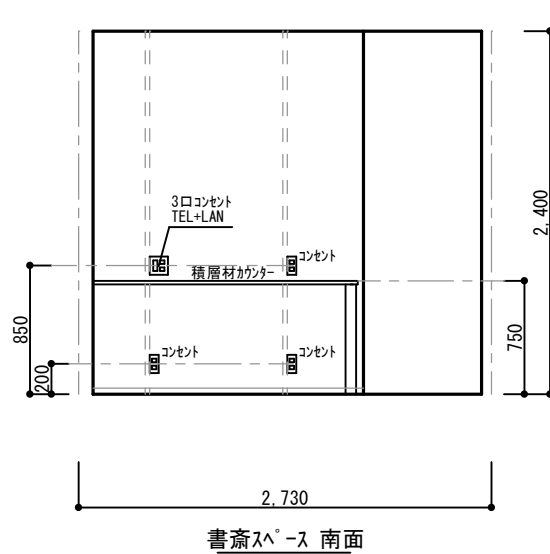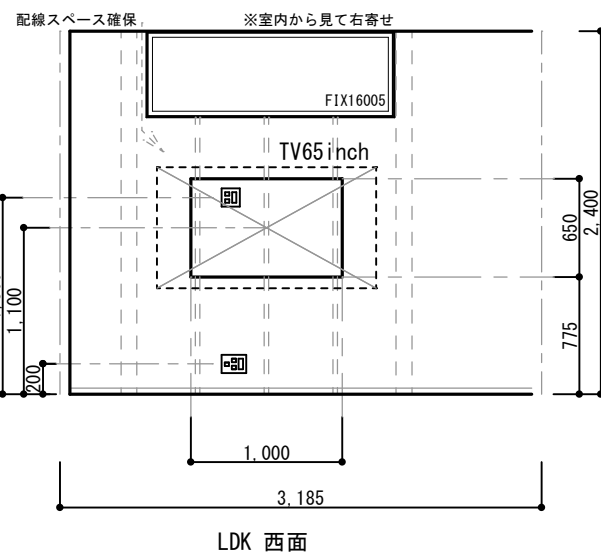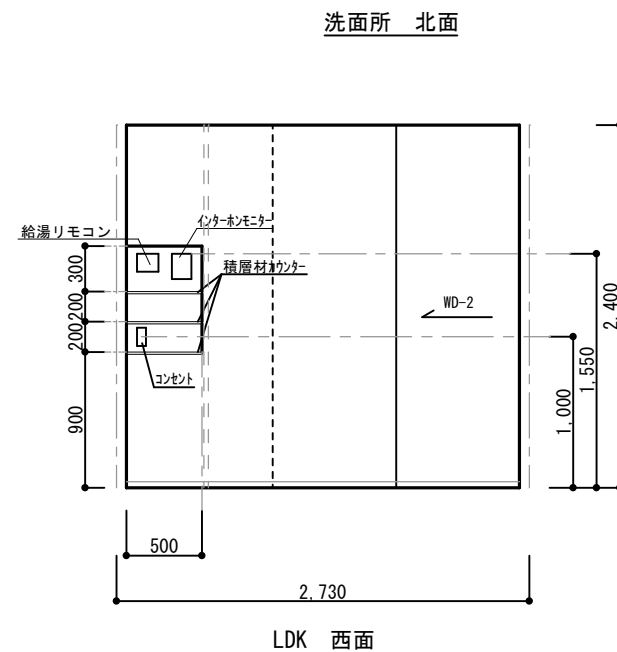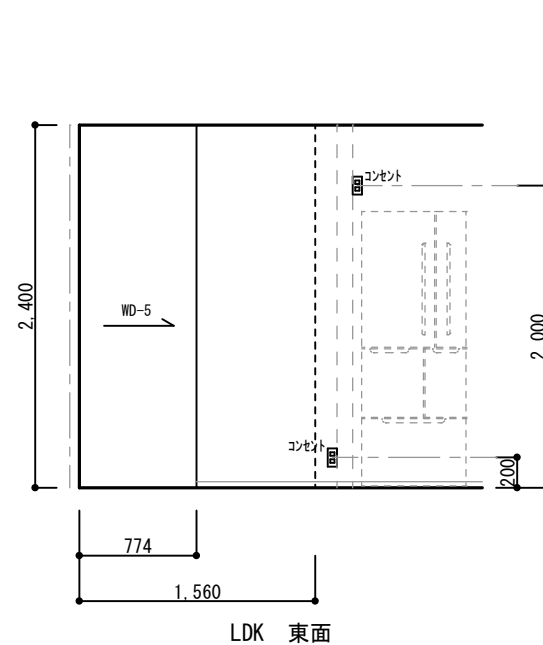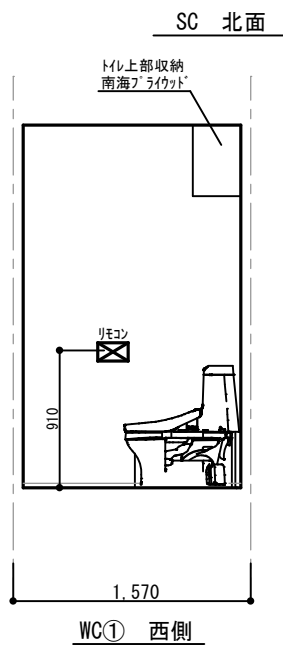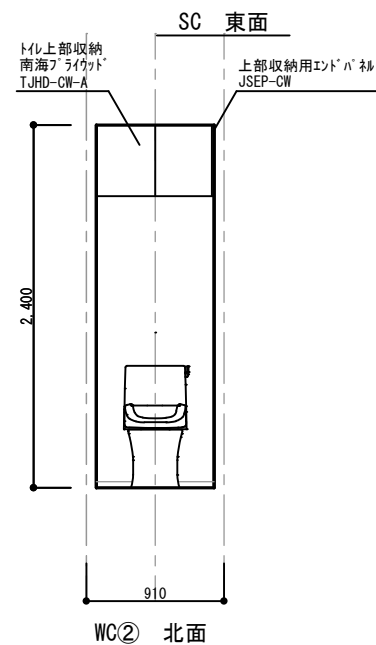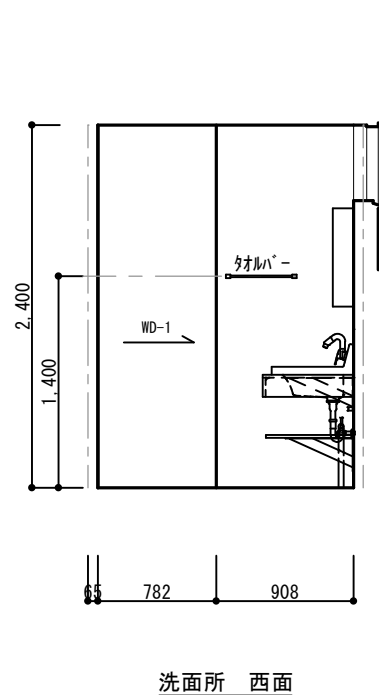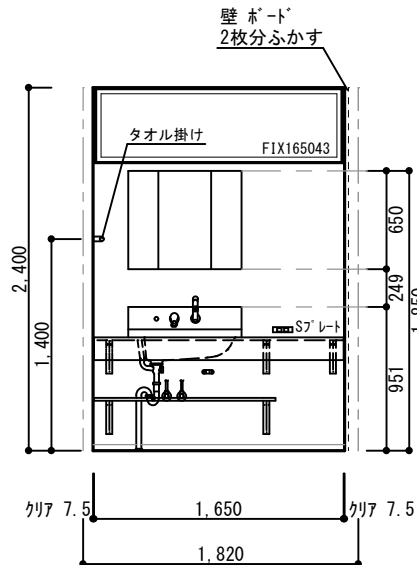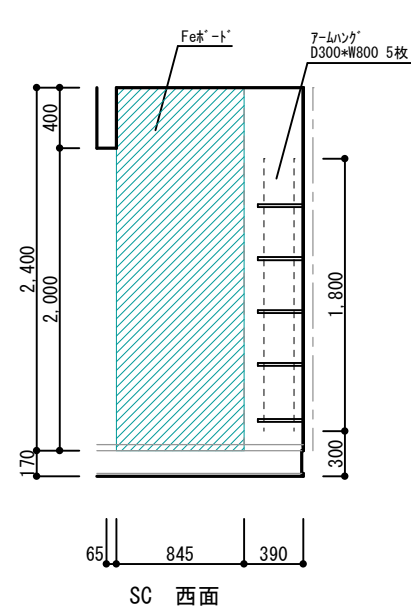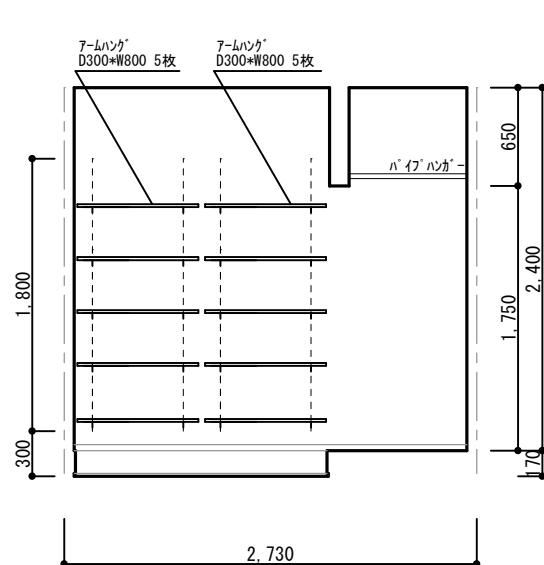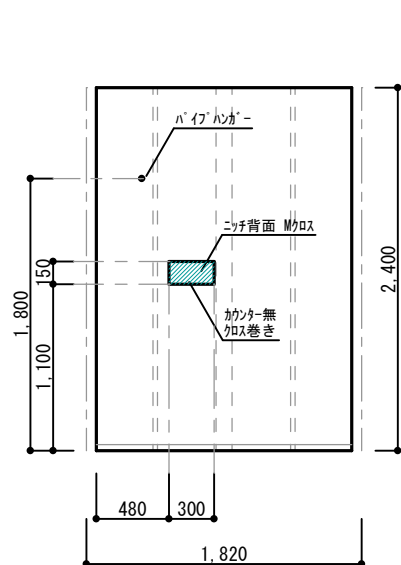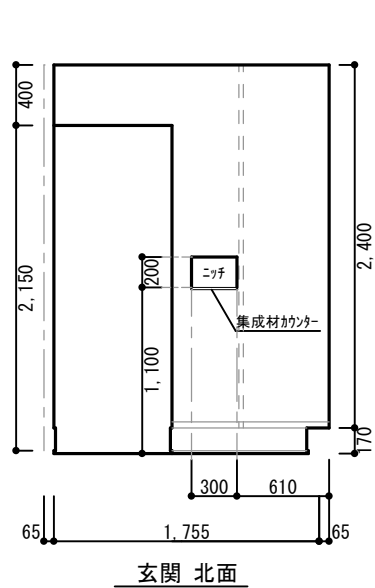

決定図

訂正	浜岡一級総合設計事務所 一級建築士事務所 静岡県知事登録第 (10)2441 号 一級建築士 大田登録第 365879 号 西原利昌	LIFEFUND PG HOUSE	株式会社 LIFEFUND InDesign office 一級建築士事務所 事務所登録 (2) 第7595号 一級建築士登録 第179770号 鈴木 達男 〒432-8023 静岡県浜松市中央区鴨江3丁目70番23号	年月日 2026.2.1	件名 三室司様 邸新築工事	設計 酒井	IC	工事 青島	図番 6-1
縮尺 1/50	図名 展開図-1	ホール①⇄洗面所 7ルに見切り位置							

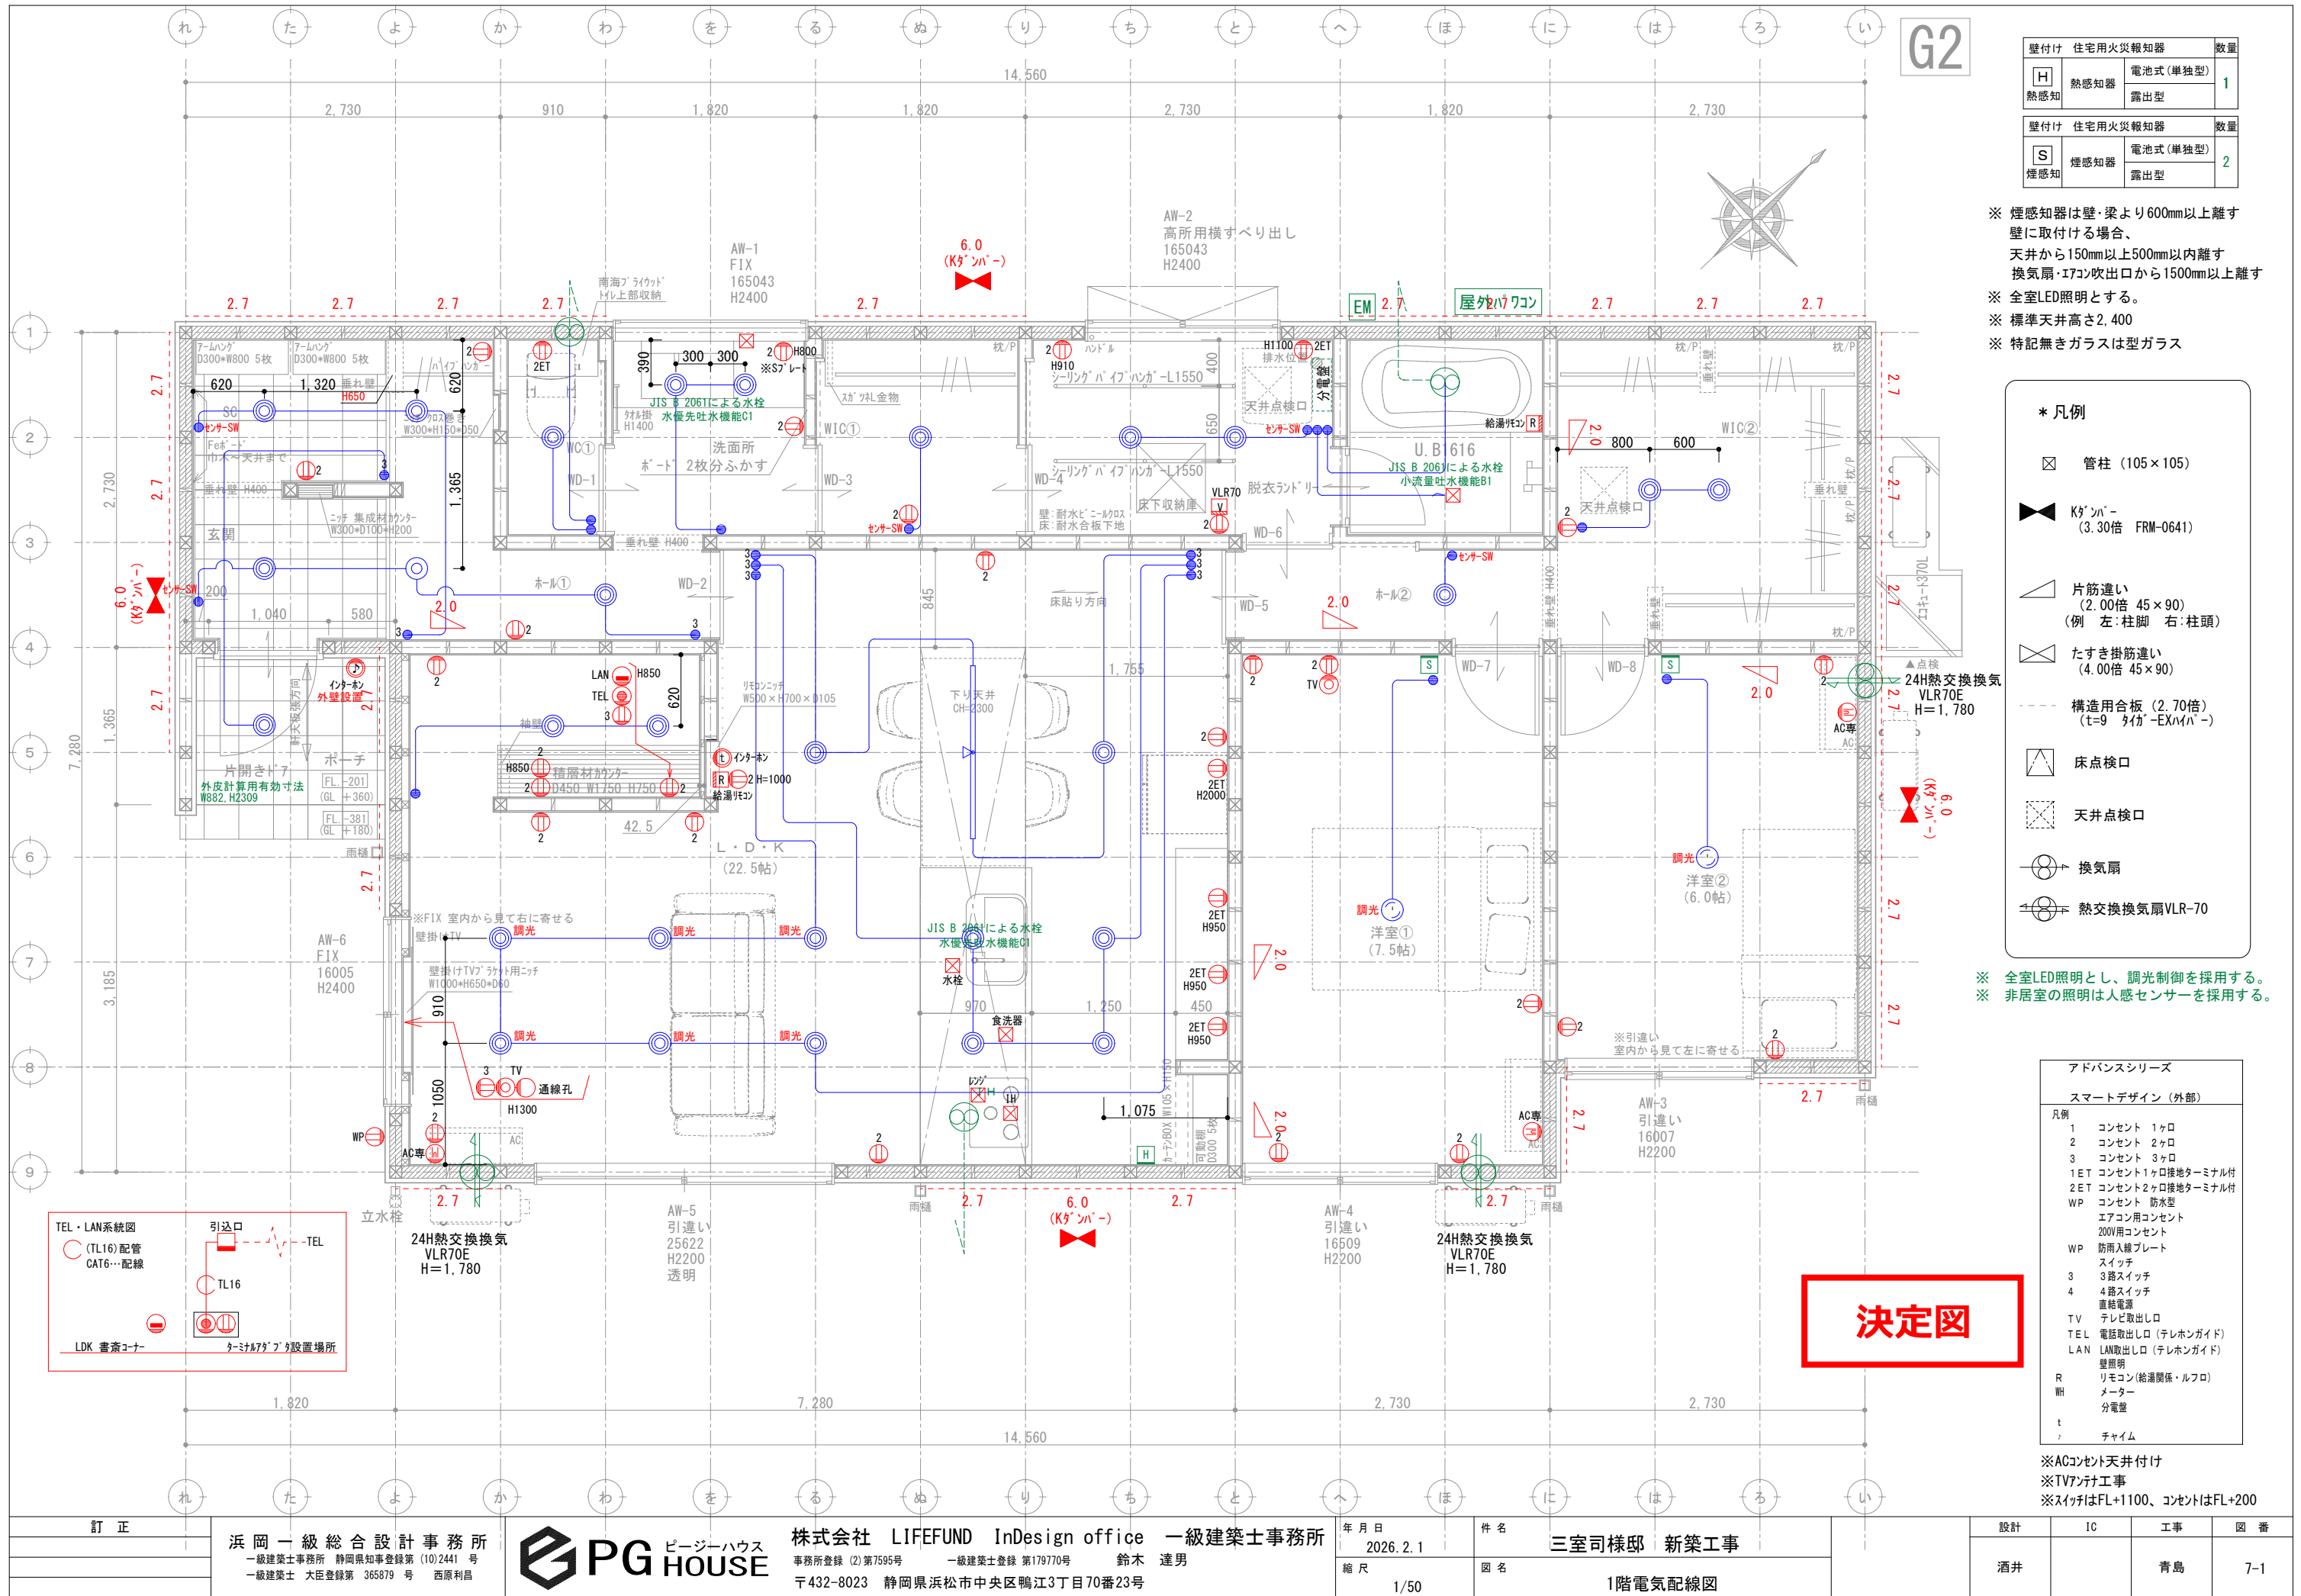

壁付け 住宅用火災報知器			数量
H	熱感知器	電池式(単独型)	1
	熱感知器	露出型	
壁付け 住宅用火災報知器			数量
S	煙感知器	電池式(単独型)	2
	煙感知器	露出型	

- ※ 煙感知器は壁・梁より600mm以上離す
壁に取付ける場合、
天井から150mm以上500mm以内離す
換気扇・エアコン吹出口から1500mm以上離す
- ※ 全室LED照明とする。
- ※ 標準天井高さ2,400
- ※ 特記無きガラスは型ガラス


* 凡例

- 管柱 (105×105)
- ▲ Kダクト (3.30倍 FRM-0641)
- △ 片筋違い (2.00倍 45×90)
(例 左:柱脚 右:柱頭)
- △ たすき掛筋違い (4.00倍 45×90)
- 構造用合板 (2.70倍)
(t=9 材:EXハイパー)
- △ 床点検口
- △ 天井点検口
- 換気扇
- 熱交換換気扇VLR-70

- ※ 全室LED照明とし、調光制御を採用する。
- ※ 非居室の照明は人感センサーを採用する。

アドバンスシリーズ		
スマートデザイン (外部)		
凡例	1	コンセント 1ヶ所
	2	コンセント 2ヶ所
	3	コンセント 3ヶ所
	1ET	コンセント1ヶ所接地ターミナル付
	2ET	コンセント2ヶ所接地ターミナル付
	WP	コンセント 防水型
		エアコン用コンセント
		200V用コンセント
	WP	防雨入線プレート
		スイッチ
	3	3路スイッチ
	4	4路スイッチ
		直結電源
	TV	テレビ取出口
	TEL	電話取出口 (テレホンガイド)
	LAN	LAN取出口 (テレホンガイド)
	R	壁照明
	WH	リモコン (給湯関係・ルフロ)
	t	メーター
		分電盤
		チャイム

- ※ACコンセント天井付け
- ※TVアンテナ工事
- ※スイッチはFL+1100、コンセントはFL+200

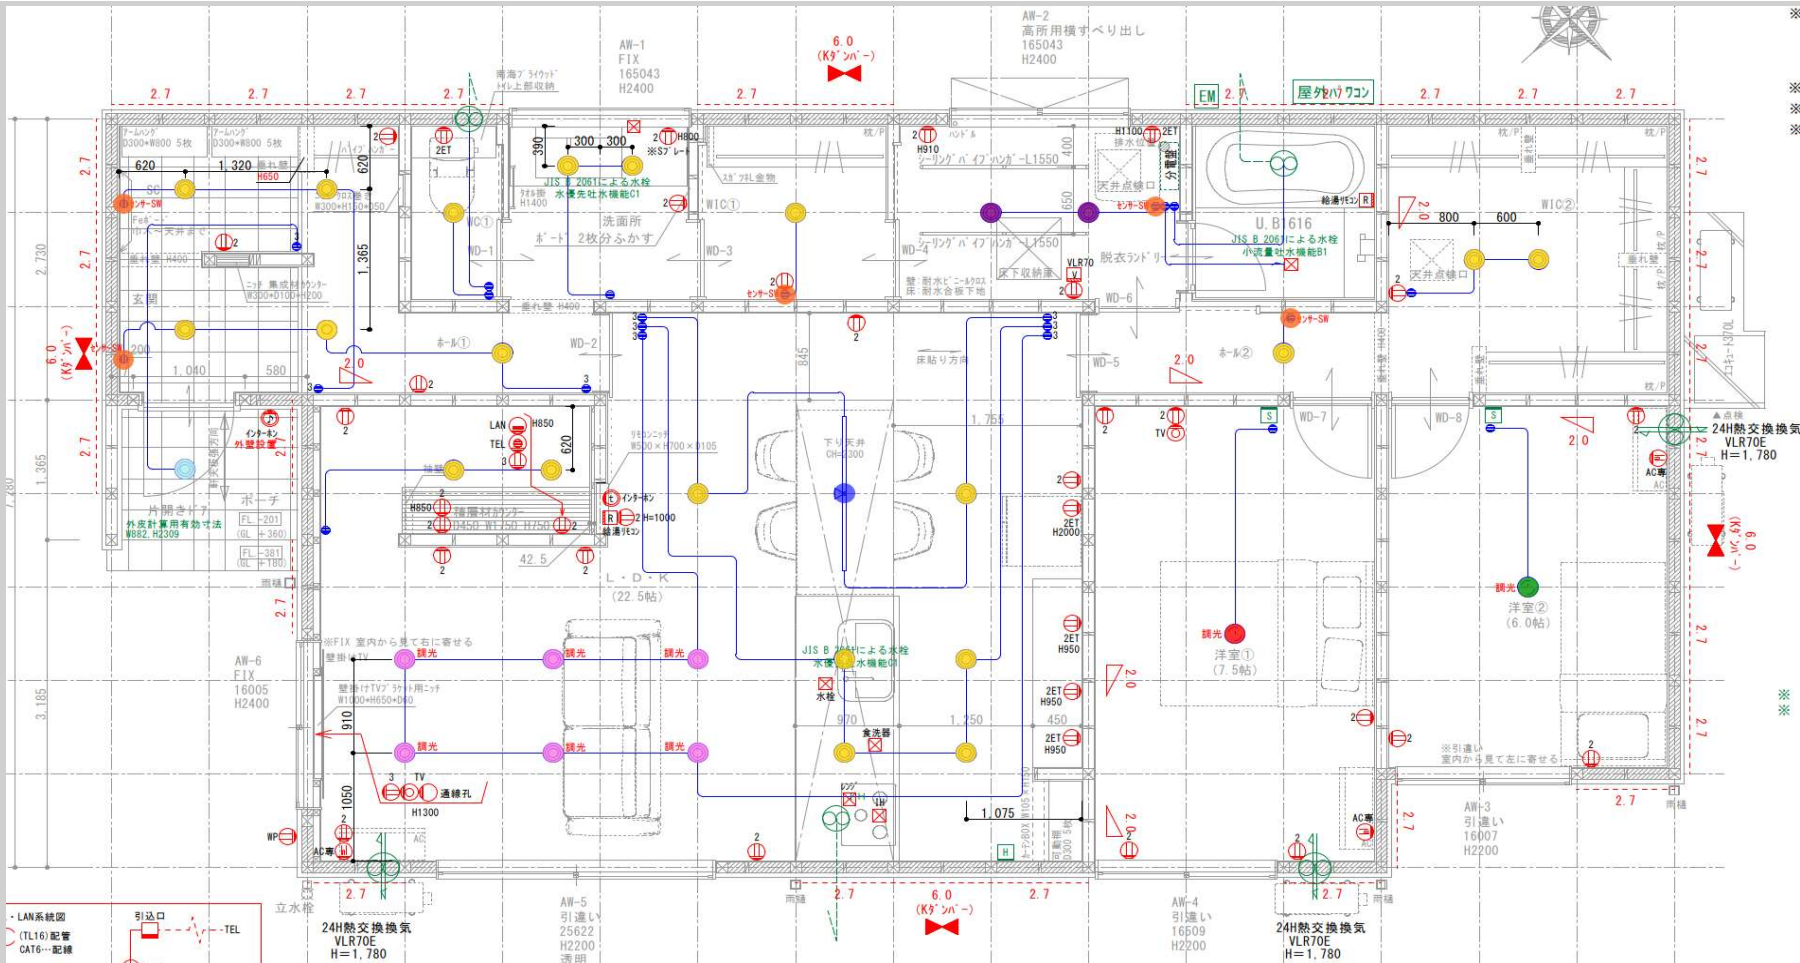

1階

ドアホン：VL-SE31XL
(Panasonic)



内部SW：アドバンス
マットグレー



ポーチ灯

×1

センサー付きダウナイト

DDL_6259YB

基本照明ダウナイト

×20

DDL_6132YB

脱衣ランドリー

×2

ダウナイト

DDL_6132AB

LDK

×6

調光ダウナイト

DDL_6032YBG

洋室①

×1

シーリングライト

DCL_42122

洋室②

×1

シーリングライト

DCL_42121

玄関、SC、WIC①、脱衣ランドリー、ホール②

×5

センサーSW

WTA_14119H

LDK

×1

レール照明

DP_02915K



高気密SB形 | 人感センサー
連動マルチタイプ

DDL-6259 YB
電球色 / 2700K Ra93(クラス2)

415 lm 7.7 W 53.8 lm/W

¥21,800(税抜) (LED内蔵)

LED LED 7.7W 白熱灯60W相当
●銅板 黒塗装
●アルミダイカスト 黒塗装
●アクリル 乳白(マット)
●径φ116 埋込穴φ100 埋込深75mm 0.5kg
●14VA
●点灯角度調節機能付(暗・明切)
●点灯保持時間(1分)
●拡散バネル付
●AC100V
●光束維持時間40,000時間
●取付可能天井厚5~25mm
●調光器併用不可

【連動器具について】
LED調光タイプ60VAまで
LED非調光タイプ不可 蛍光灯不可
白熱灯60Wまで

強制ON
ソフトオフ
60°
0.1m
遮断天井 100
遮込必要高 80
準耐火
LED交換 不可
防雨形
温度保護 機能付



COBタイプ | 高気密SB形

DDL-6132 YB
電球色 / 2700K Ra93(クラス2)

370 lm 4.6 W 80.4 lm/W

¥3,600(税抜) (LED内蔵)

LED LED 4.6W 白熱灯60W相当
●銅板 黒塗装
●アクリル 乳白(マット)
●径φ116 埋込穴φ100 埋込深70mm 0.3kg
●8VA
●拡散バネル付
●AC100V
●光束維持時間60,000時間
●取付可能天井厚5~25mm
●調光器併用不可

LED交換 不可
非調光
防雨形
60°
0.1m
遮断天井 100
遮込必要高 70
準耐火
LED交換 不可
防雨形
温度保護 機能付



COBタイプ | 高気密SB形

DDL-6132 AB
温白色 / 3500K Ra93(クラス2)

400 lm 4.6 W 86.9 lm/W

¥3,600(税抜) (LED内蔵)

LED LED 4.6W 白熱灯60W相当
●銅板 黒塗装
●アクリル 乳白(マット)
●径φ116 埋込穴φ100 埋込深70mm 0.3kg
●8VA
●拡散バネル付
●AC100V
●光束維持時間60,000時間
●取付可能天井厚5~25mm
●調光器併用不可

LED交換 不可
非調光
防雨形
60°
0.1m
遮断天井 100
遮込必要高 70
準耐火
LED交換 不可
防雨形
温度保護 機能付



COBタイプ | 高気密SB形

DDL-6032 YBG
電球色 / 2700K Ra93(クラス2)

370 lm 5.8 W 63.7 lm/W

¥4,600(税抜) (LED内蔵)

LED LED 5.8W 白熱灯60W相当
●銅板 黒塗装
●アクリル 乳白(マット)
●径φ116 埋込穴φ100 埋込深71mm 0.3kg
●7VA
●拡散バネル付
●AC100V
●調光可能(1%~100%)
●光束維持時間60,000時間
●取付可能天井厚5~25mm

LED交換 不可
調光
防雨形
60°
0.1m
遮断天井 100
遮込必要高 80
準耐火
LED交換 不可
防雨形
温度保護 機能付



タイマー付リモコンブルレス | 調色調光タイプ

DCL-42122
昼光色 / 6500K~電球色 / 2700K Ra93

LED LED S1.1W 4299 lm 31.1 W 138.2 lm/W

¥26,000(税抜) (LED内蔵)

●再生アクリル 乳白(マット)
●径φ110 高さ138mm 1.4kg
●フルレリースイッチ付(金灯・赤点灯・常夜灯)
●消灯時の調色調光状態
●調色機能付(6500K~2700K) ●調光機能付(5%~100%)
●常夜灯6段階調光 ●AC100V ●光束維持時間40,000時間
●調光器併用不可 ●シーンコントロールは使用できません。
※定格光束、消費電力、固有エネルギー消費効率は
昼白色での値です。

調色調光
8段階
LED交換 不可
防雨形
45°
遮断天井 45°
遮込必要高 DP-42432
準耐火 DP-42433



タイマー付リモコンブルレス | 調色調光タイプ

DCL-42121
昼光色 / 6500K~電球色 / 2700K Ra93

LED LED 27.1W 3699 lm 27.1 W 136.4 lm/W

¥22,000(税抜) (LED内蔵)

●再生アクリル 乳白(マット)
●径φ110 高さ138mm 1.4kg
●フルレリースイッチ付(金灯・赤点灯・常夜灯)
●消灯時の調色調光状態
●調色機能付(6500K~2700K) ●調光機能付(5%~100%)
●常夜灯6段階調光 ●AC100V ●光束維持時間40,000時間
●調光器併用不可 ●シーンコントロールは使用できません。
※定格光束、消費電力、固有エネルギー消費効率は
昼白色での値です。

調色調光
6段階
LED交換 不可
防雨形
45°
遮断天井 45°
遮込必要高 DP-42432
準耐火 DP-42433



3線 / 4線式

WTA14119H

希望小売価格 11,400円(税抜)
※掲載の価格には消費税は含まれていません。

【壁取付】熱線センサ付自動スイッチ(親器)
(検知後連続動作時間 約10秒~30分可変形)
(明るさセンサ・手動スイッチ付)(マットグレー)

3A 100V AC

プレート別売



フィードインボックス・エンドキャップセット


ダクトレール1.5m用

DP-02915 K

¥8,800(税抜)

●アルミ型材 黒アルマイト
●φ33 ダクト長1500 全長1603 高19mm
●2P 15A 125V
●フィードインボックス・エンドキャップ1個付

外部：スマートデザインシリーズ
ブラック

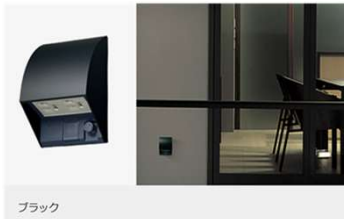

照明器具
施主手配

決定図


PG House






三室司 様邸新築工事

Lighting Plan







2026.2.1

(図面 7-3)

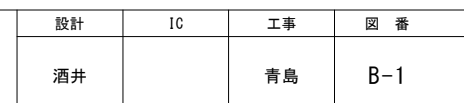


 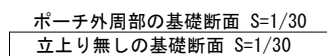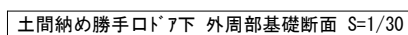  

※注意：基礎伏図に特記のない内部基礎の場合

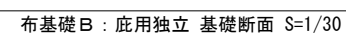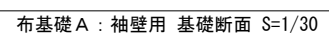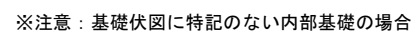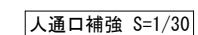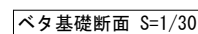 

決定図

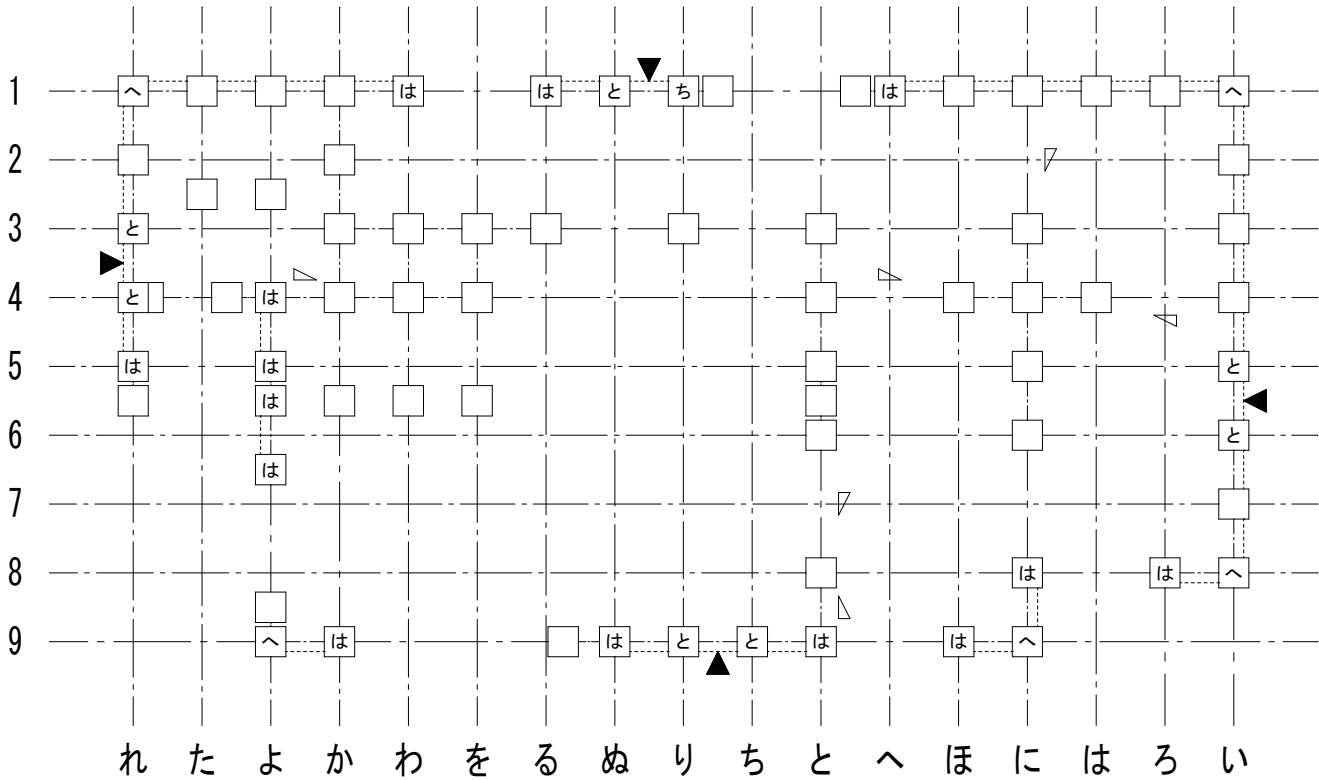

1 階柱壁伏図

接合部凡例				*接合部凡例はユーザ設定されたものです。	
記号	仕様（カナイ金物）		N	倍率	
SBCP	スリムビルドコーナー75, チビクリCK (化粧柱の場合)		0.00	1.00	
SBCP	スリムビルドコーナー75, チビクリCK (化粧柱の場合)		0.65	1.00	
SBCP	は	スリムビルドコーナー75	1.00	1.00	
ARCG	に	アレントコーナー合板用	1.40	2.20	
ARCG	ほ	アレントコーナー合板用	1.60	2.20	
ARCG	へ	アレントコーナー合板用	1.80	2.20	
HD15	と	ブレイブホールダウン B-HD15	2.80	3.60	
HD20	ち	ブレイブホールダウン B-HD20	3.70	4.70	
HD25	り	ブレイブホールダウン B-HD25	4.70	4.80	
HD30	ぬ	ブレイブホールダウン B-HD30	5.60	7.20	
J1	る	腰掛け蟻若しくは大入れ蟻掛け+羽子板*ルト、短冊金物		1.90	梁継手・仕口用 梁継手・仕口用
J2	を	腰掛け蟻若しくは大入れ蟻掛け+羽子板*ルト、短冊金物×2		3.00	

※表示なき金物は「は」とする。


接合部凡例				*接合部凡例はユーザ設定されたものです。	
記号	仕様（タナカ金物）		N	倍率	
FCP	フックコーナー, チビクリCK (化粧柱の場合)		0.00	1.00	
FCP	フックコーナー, チビクリCK (化粧柱の場合)		0.65	1.00	
FCP	は	フックコーナー	1.00	1.00	
CCP	に	シナコーナー	1.40	2.20	
CCP	ほ	シナコーナー	1.60	2.20	
CCP	へ	シナコーナー	1.80	2.20	
HD15	と	ビス止めホールダウンU HD15	2.80	3.60	
HD20	ち	ビス止めホールダウンU HD20	3.70	4.70	
HD25	り	ビス止めホールダウンU HD25	4.70	4.80	
HD30	ぬ	ビス止めホールダウンU HD15×2 (HD35)	5.60	7.20	
J1	る	腰掛け蟻若しくは大入れ蟻掛け+羽子板*ルト、短冊金物		1.90	梁継手・仕口用 梁継手・仕口用
J2	を	腰掛け蟻若しくは大入れ蟻掛け+羽子板*ルト、短冊金物×2		3.00	

※表示なき金物は「は」とする。

筋かいの種類に応じた筋かいの端部の接合部の仕様		
	筋かいの種類	接合部の仕様（構造方法）
イ	鉄筋φ9	柱又は横架材を貫通し、三角座金を介してナット締め、又は鋼板添え板を用い鋼板を柱及び横架材にCN90, 8本平打ち
ロ	筋かい:15×90	柱・横架材を欠き込み、柱・横架材双方に対してN65, 5本平打ち
ハ	筋かい:30×90	鋼板添え板t=1.6mmを筋かいに対してボルトφ12及びCN65, 3本平打ち、柱に対してCN65, 3本平打ち、横架材に対してCN65, 4本平打ち。筋かいプレートBP同等品
ニ	筋かい:45×90	鋼板添え板t=2.3mmを筋かいに対してボルトφ12及びスクリュー釘φ4.5L50, 7本平打ち、柱及び横架材に対してスクリュー釘φ4.5L50, 5本平打ち。筋かいプレートBP-2同等品
ホ	筋かい:90×90	柱又は横架材にボルトφ12mmを用いて一面剪断接合

胴差と通し柱の接合部の仕様		
	胴差と通し柱の条件	仕口
T1	通し柱の片側に胴差が来る場合	胴差を柱にかたぎ大入れ短ほぞ差しの上、羽子板ボルト、かね折り金物又は同等以上の仕口
T2	通し柱の両側に胴差が来る場合	胴差を柱にかたぎ大入れ短ほぞ差しの上、短冊金物又は、同等以上の仕口で胴差相互を緊結
T3	通し柱と胴差の接合部の近くに90×90以上の筋かいが来る場合 (通し柱が建物の出隅にあるか、筋かい壁が外壁と直交して接する場合)	胴差を通し柱に、15KN用引き寄せ金物を水平に用いて緊結

決定図

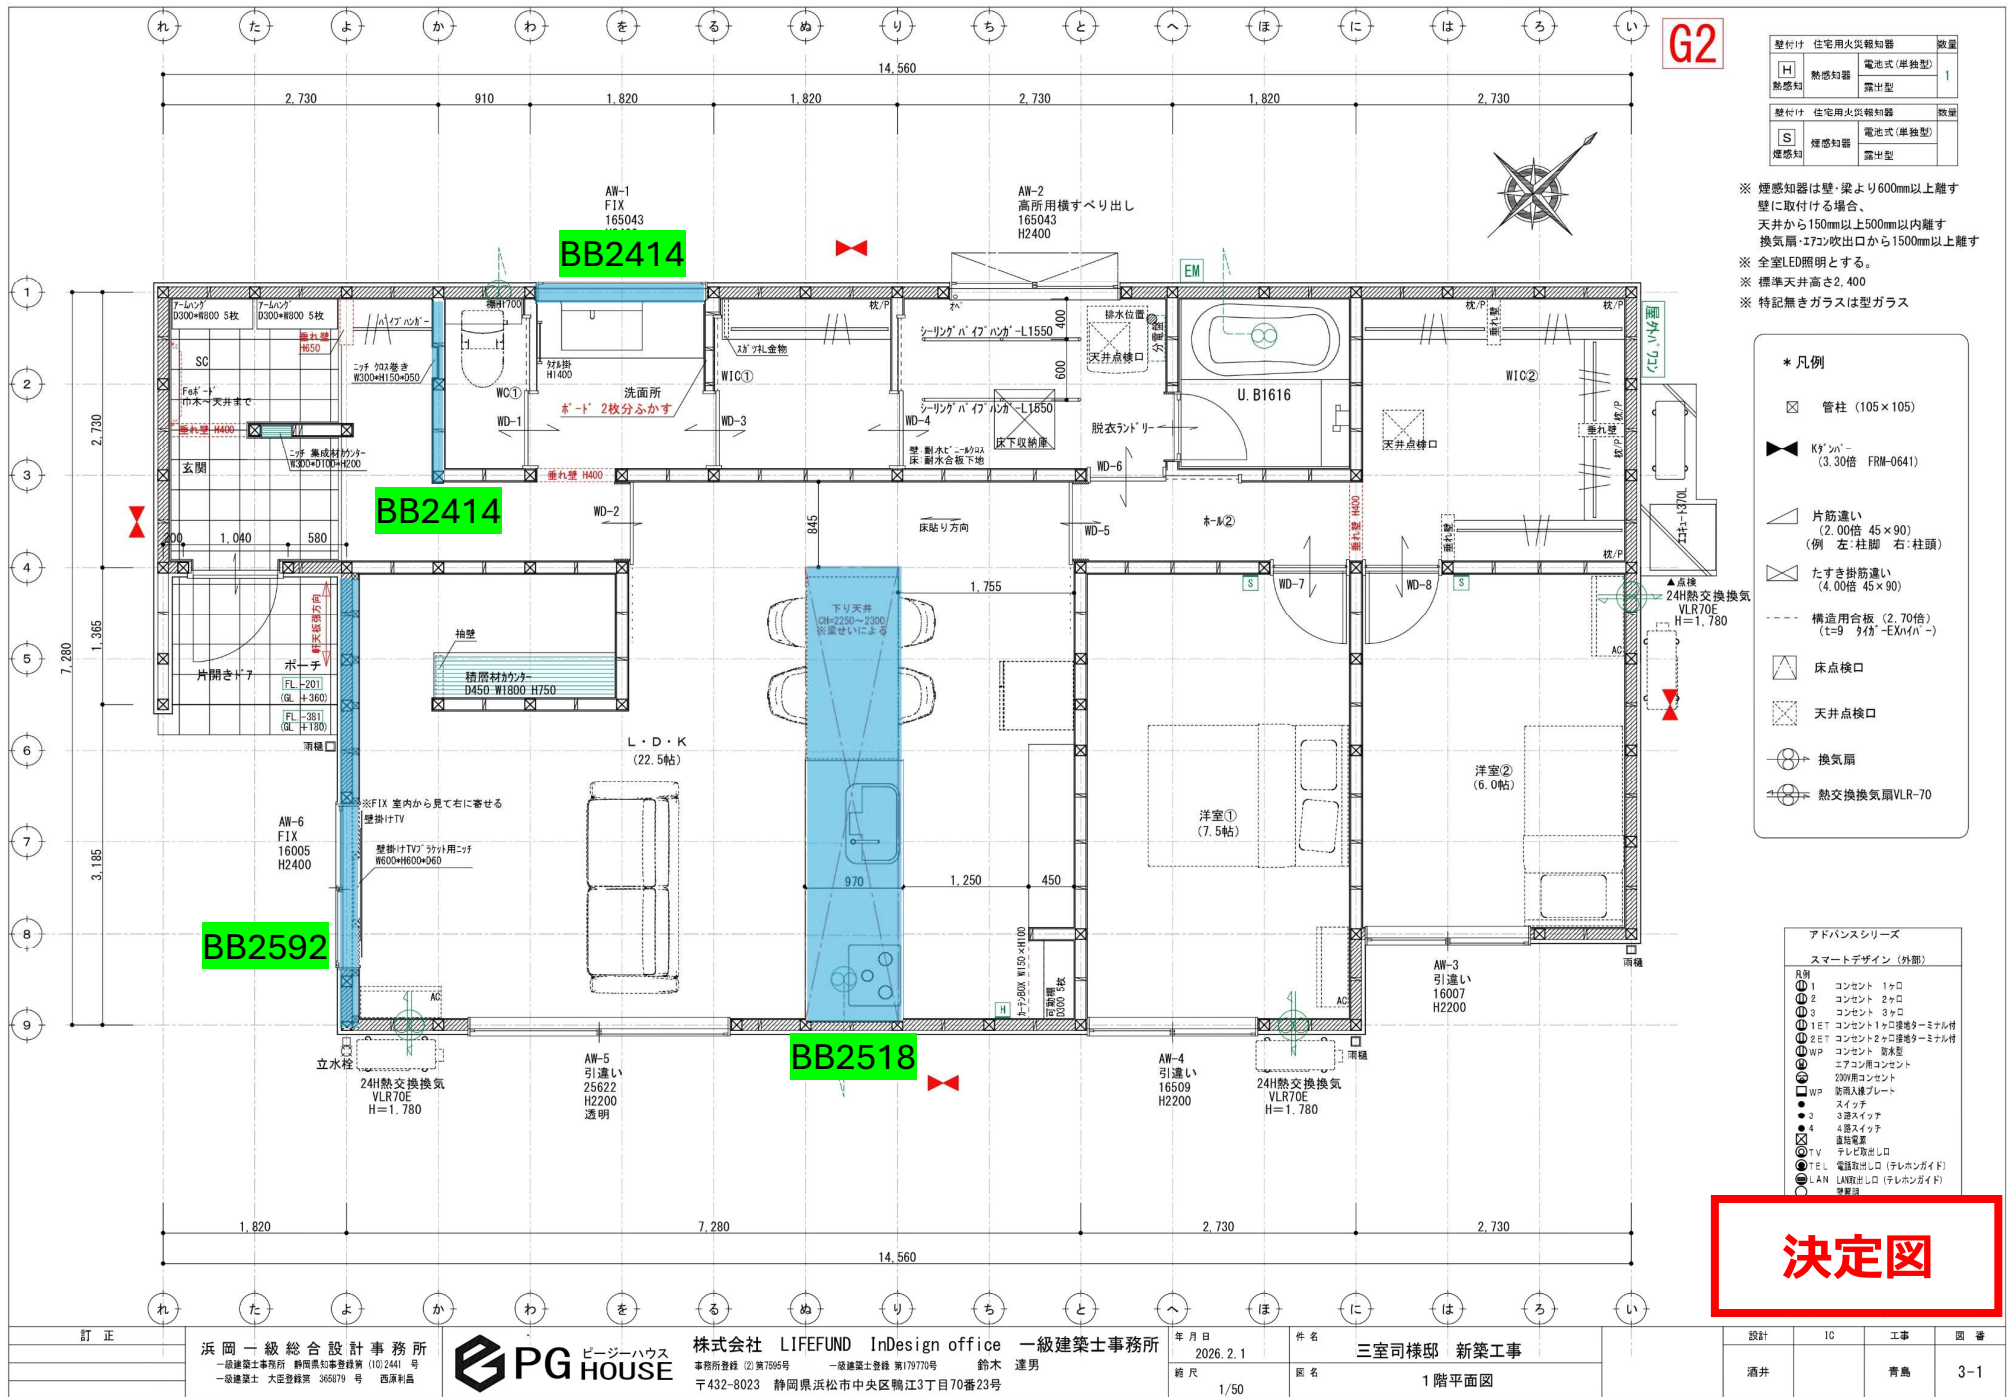

決定図

訂正

浜岡一級総合設計事務所
一級建築士事務所 新築用和室設計
一級建築士 大庭登輔 36579号 西原利昌

PG HOUSE
ピージーハウス

株式会社 LIFEFUND InDesign office 一級建築士事務所
事務所登録 (2) 第7995号 一級建築士登録 第179770号 鈴木 達男
〒432-8023 静岡県浜松市中央区鶴江3丁目70番23号

年月日
2026.2.1
縮尺
1/50

件名
三室司様邸 新築工事
図名
1階平面図

設計	IC	工事	図番
酒井		青島	3-1