
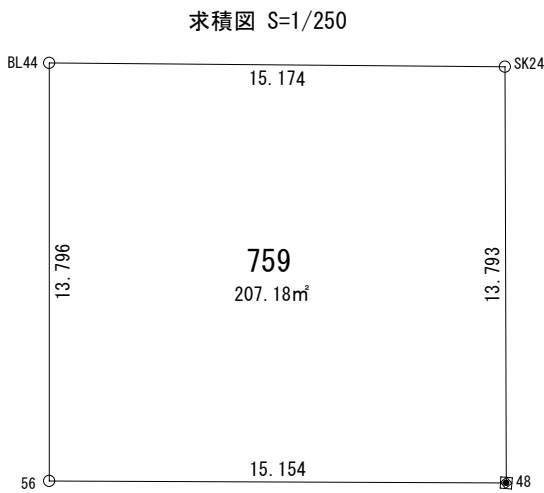


浜松市中央区神原町地内

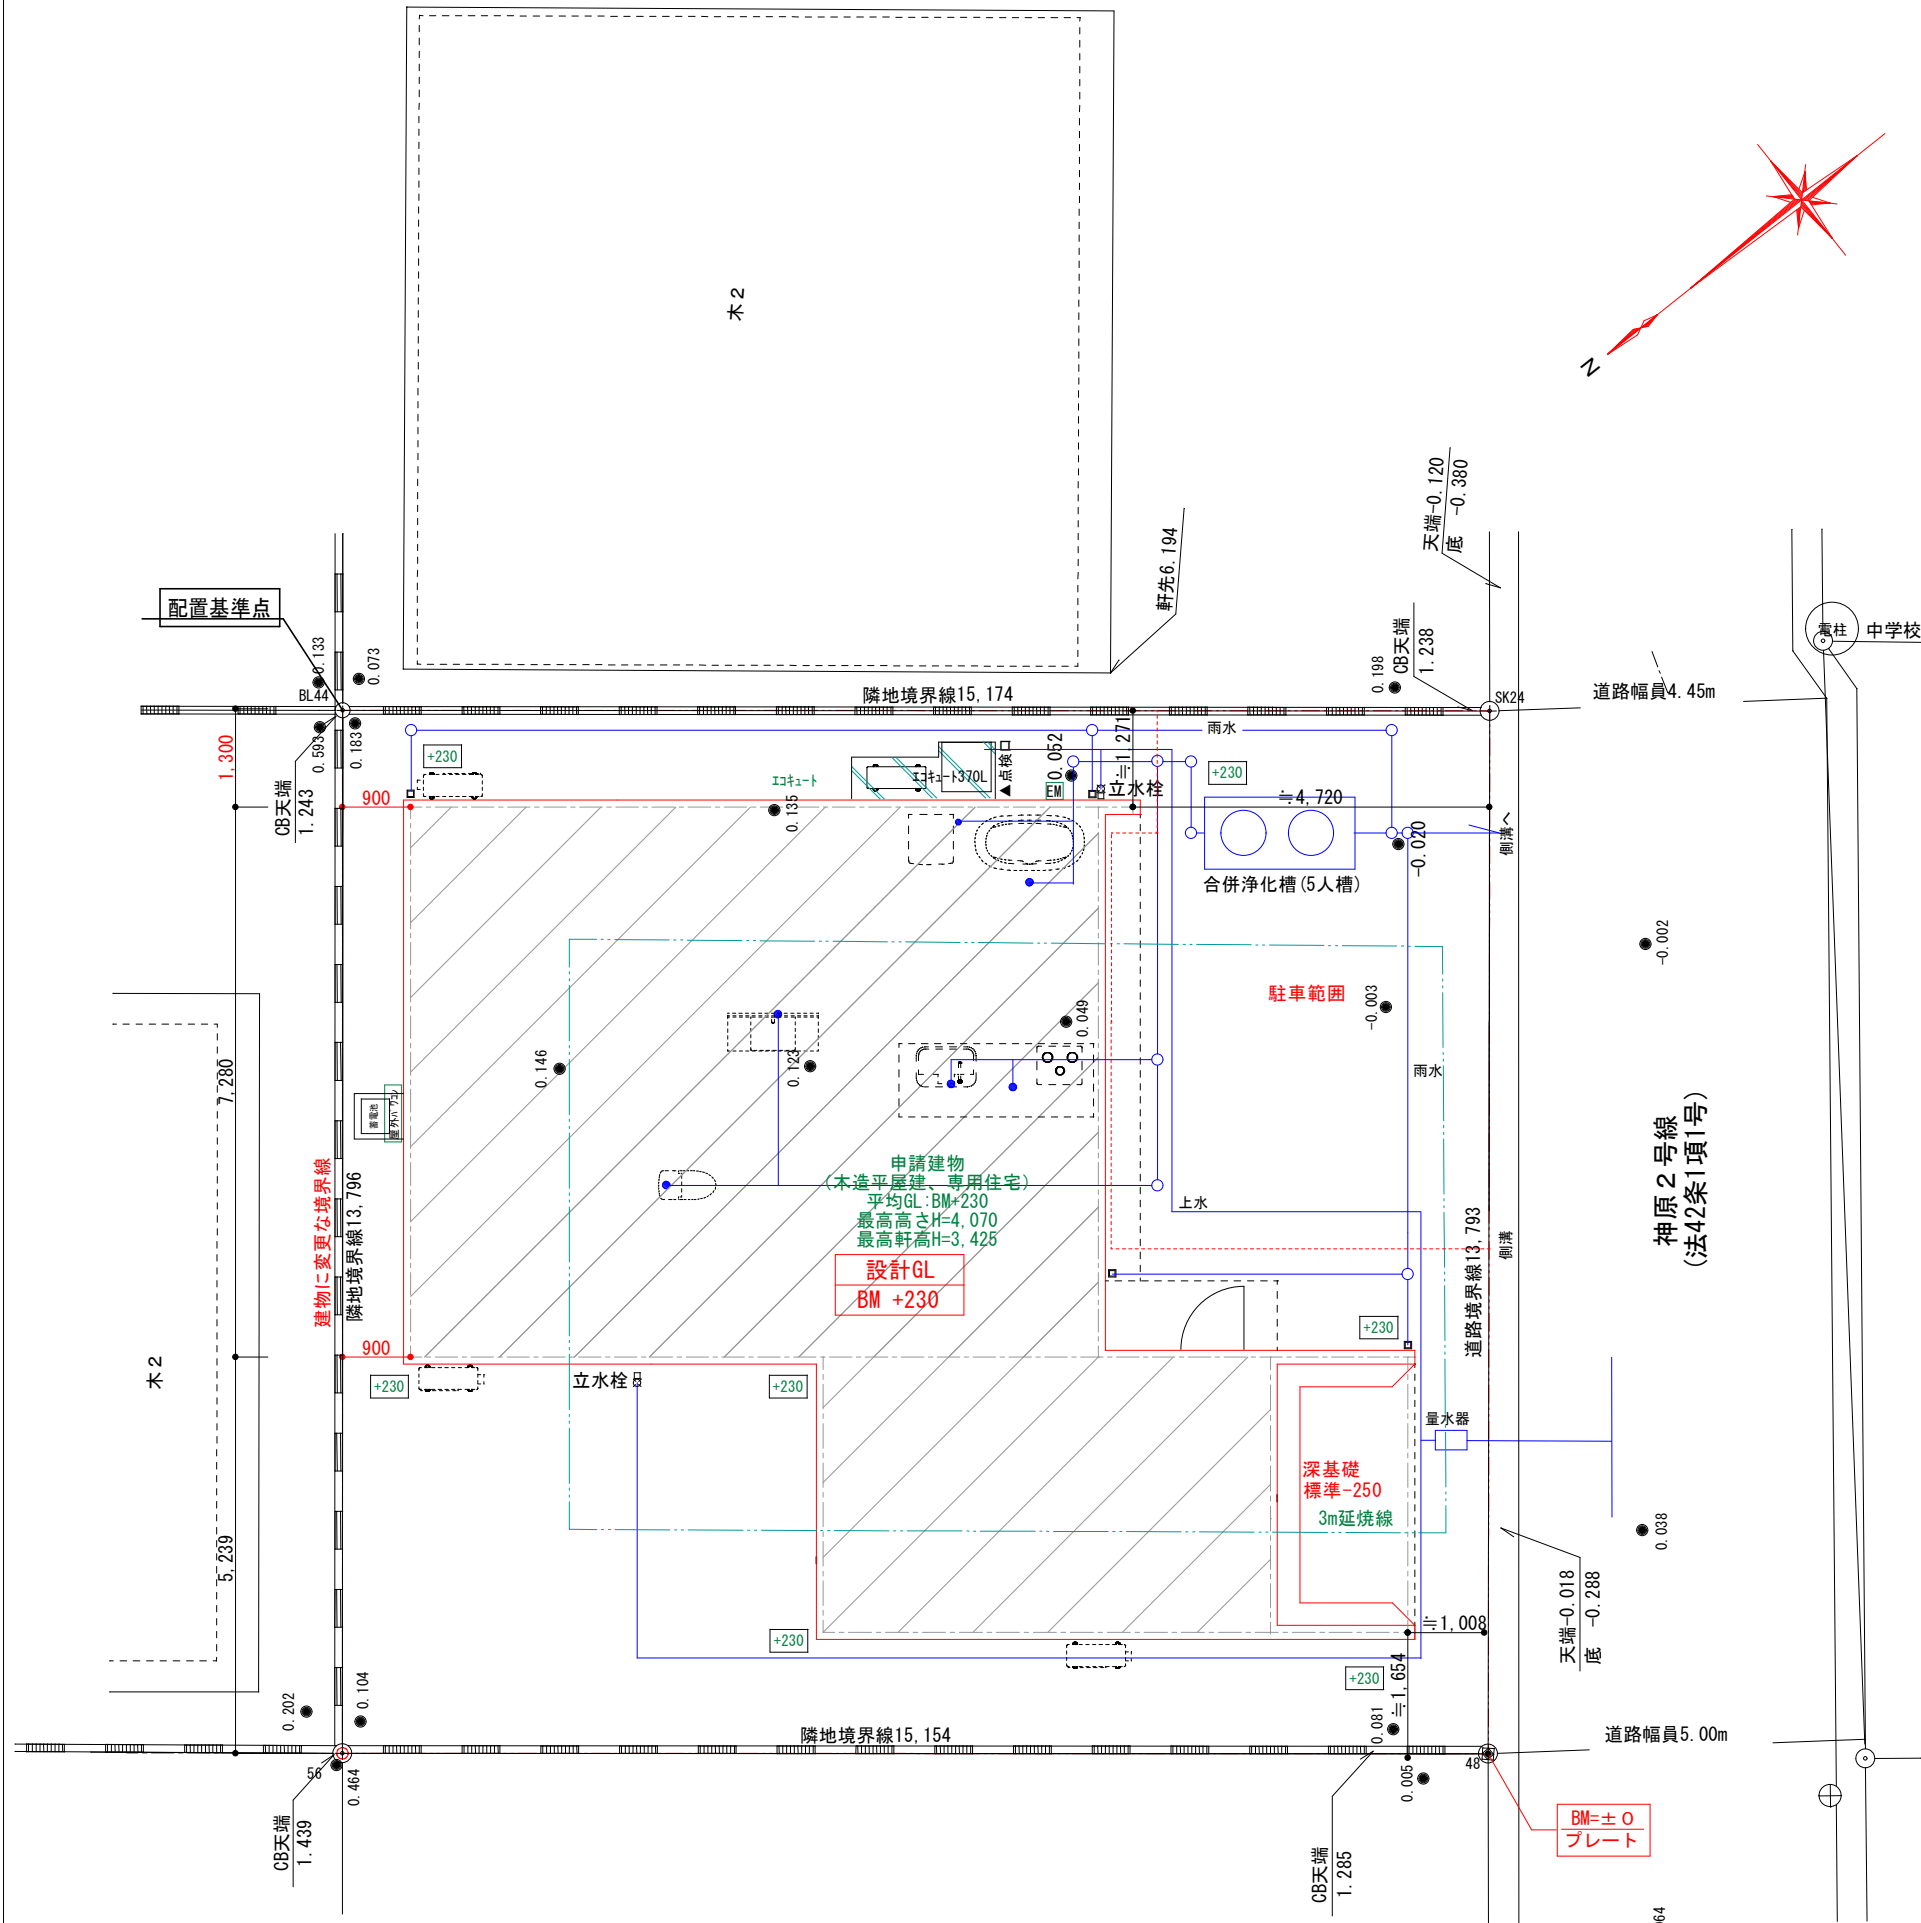

座 標 求 積 表

(任意座標)

地 番	759			
測 点	Xn	Yn	(Xn+1 - Xn-1) Yn	距 離
56	549.857	484.334	7239.824632	15.154
48	551.052	469.227	-5890.675758	13.793
SK24	537.303	468.122	-6997.487656	15.174
BL44	536.104	483.249	6066.707946	13.796
	倍 面 積		418.369164	
	面 積		209.1845820	
	地 積		209.18	

解体後、北側・西側・東側C B 2 段予定

トータル面積表 (㎡)	
敷地面積	209.18
建築面積	97.71
床面積 1階	87.77
延床面積	87.77
建蔽率	(97.71/209.18) × 100 46.72%
容積率	(87.77/209.18) × 100 41.96%

道路斜線制限については、明らかに適合する。
隣地斜線制限については、明らかに適合する。
平均地盤面について
申請建物の周囲の平均地盤面高さをBM+260とする。
盛土規制法の許可対象となる工事なし。

決定図