


【 ご注意 】


- 記載のキャビネット寸法は扉前面までの呼び寸法です。キャビネット本体の寸法・扉厚み等は商品ガイドの巻末資料をご確認ください。
- 記載のワークトップ、カウンター、エンドパネル、サイドパネルの寸法は呼び寸法です。詳細寸法は商品ガイドの巻末資料をご確認ください。
- レンジフード電源プラグ仕様：3芯電源プラグ（アース工事が必要です。）

A3 20260227NFRT-01


A面

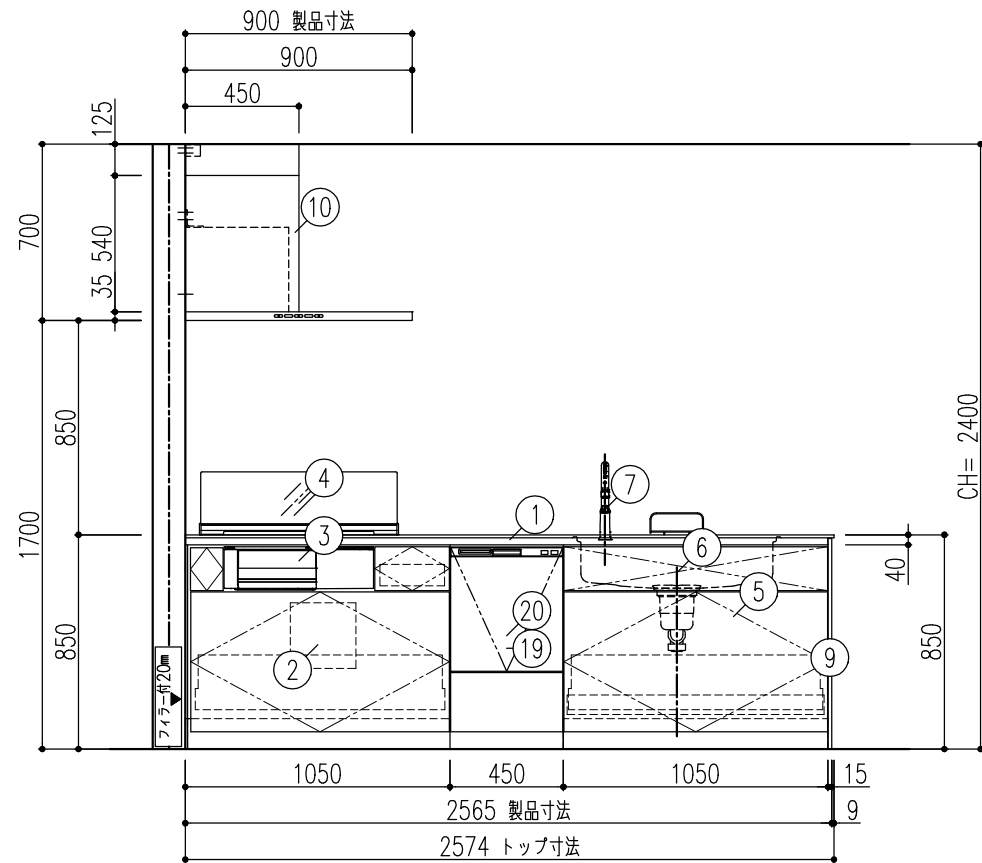


B面

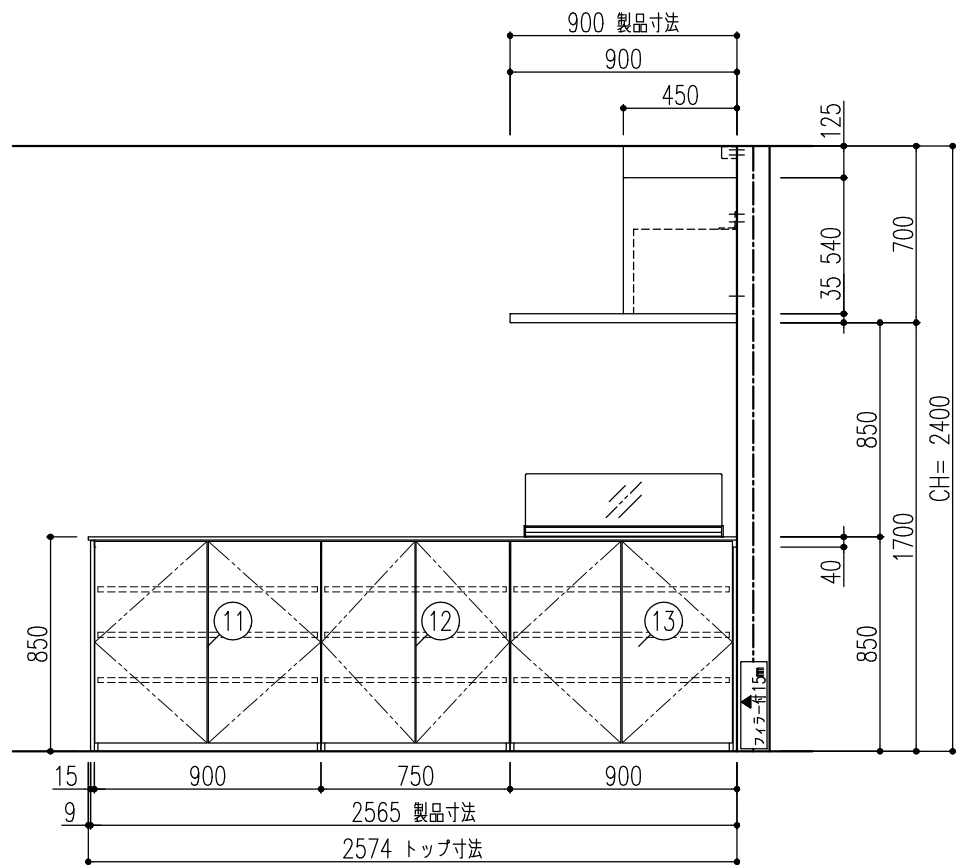

C面

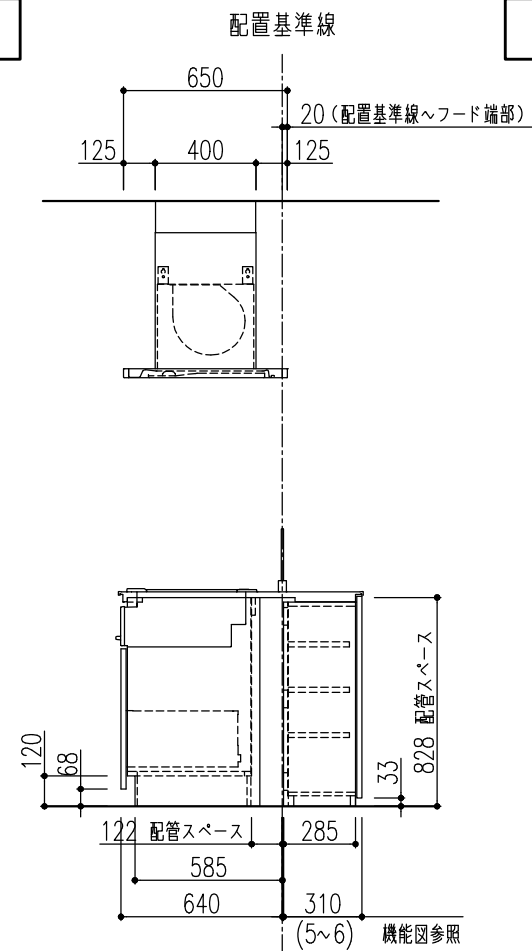

D面

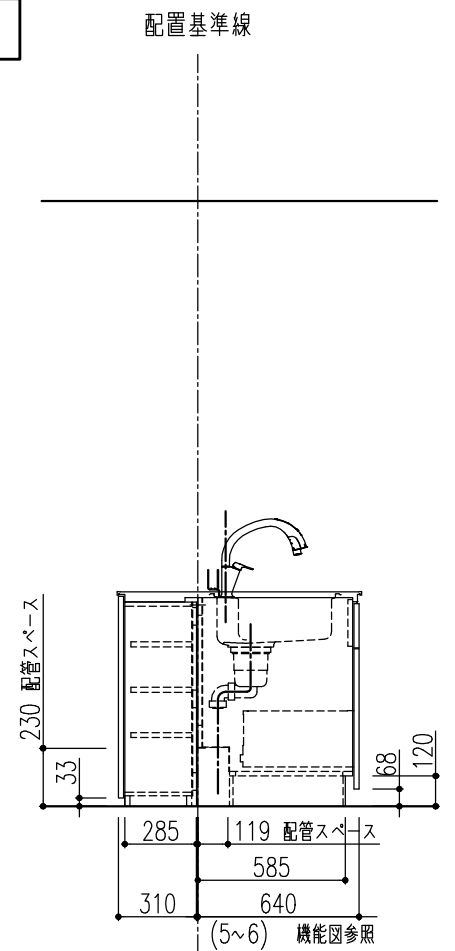



|                                                                          |     |         |                    |        |            |    |            |
|--------------------------------------------------------------------------|-----|---------|--------------------|--------|------------|----|------------|
| 特記事項<br>扉色 VK5:グレージュスタッコ<br>取手 [M]スリム取手 (ブラック)<br>ワークトップカラー 【DW】ソルティホワイト | 物件名 | 小林大樹 様邸 | 案件No.              | 図面名    | 担当         | 図面 | 図番         |
|                                                                          |     |         | A2511DDDOEXLYQ     | レイアウト図 | 栗野 友仁      |    | 株式会社 LIXIL |
|                                                                          | 仕様  | ES21    | 見積No.              | 縮尺     | 日付         |    |            |
|                                                                          |     |         | M25119238165-007-2 | 1/30   | 2026.02.27 |    |            |



A面

B面

- 注1) 125V・15A 2極接地極付アースターミナル付コンセント 【専用】  
注2) 125V・15A 2極接地極付コンセント (側板取付)  
注3) 250V・30A 2極接地極付コンセント (コンセントベース固定) 【専用】  
注4) レンジフード総高さ (600~900) の時 ダクトカバー範囲 (25~325)

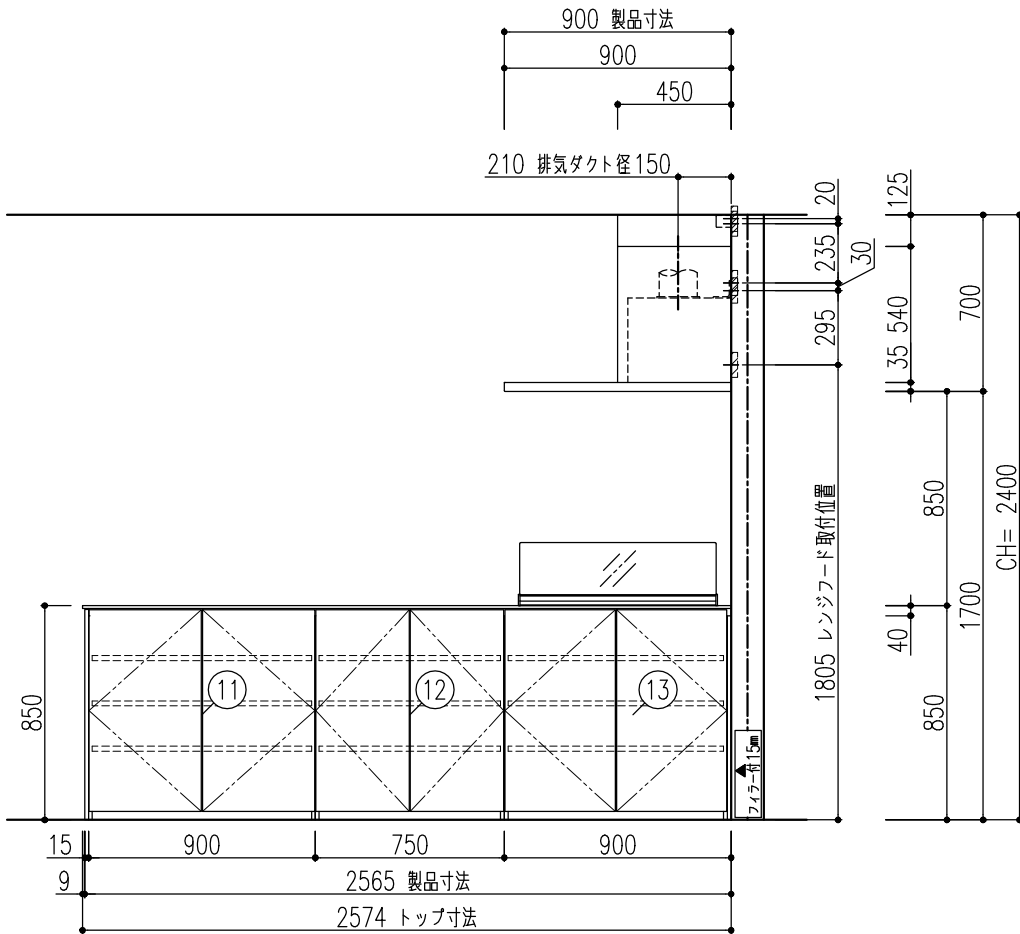
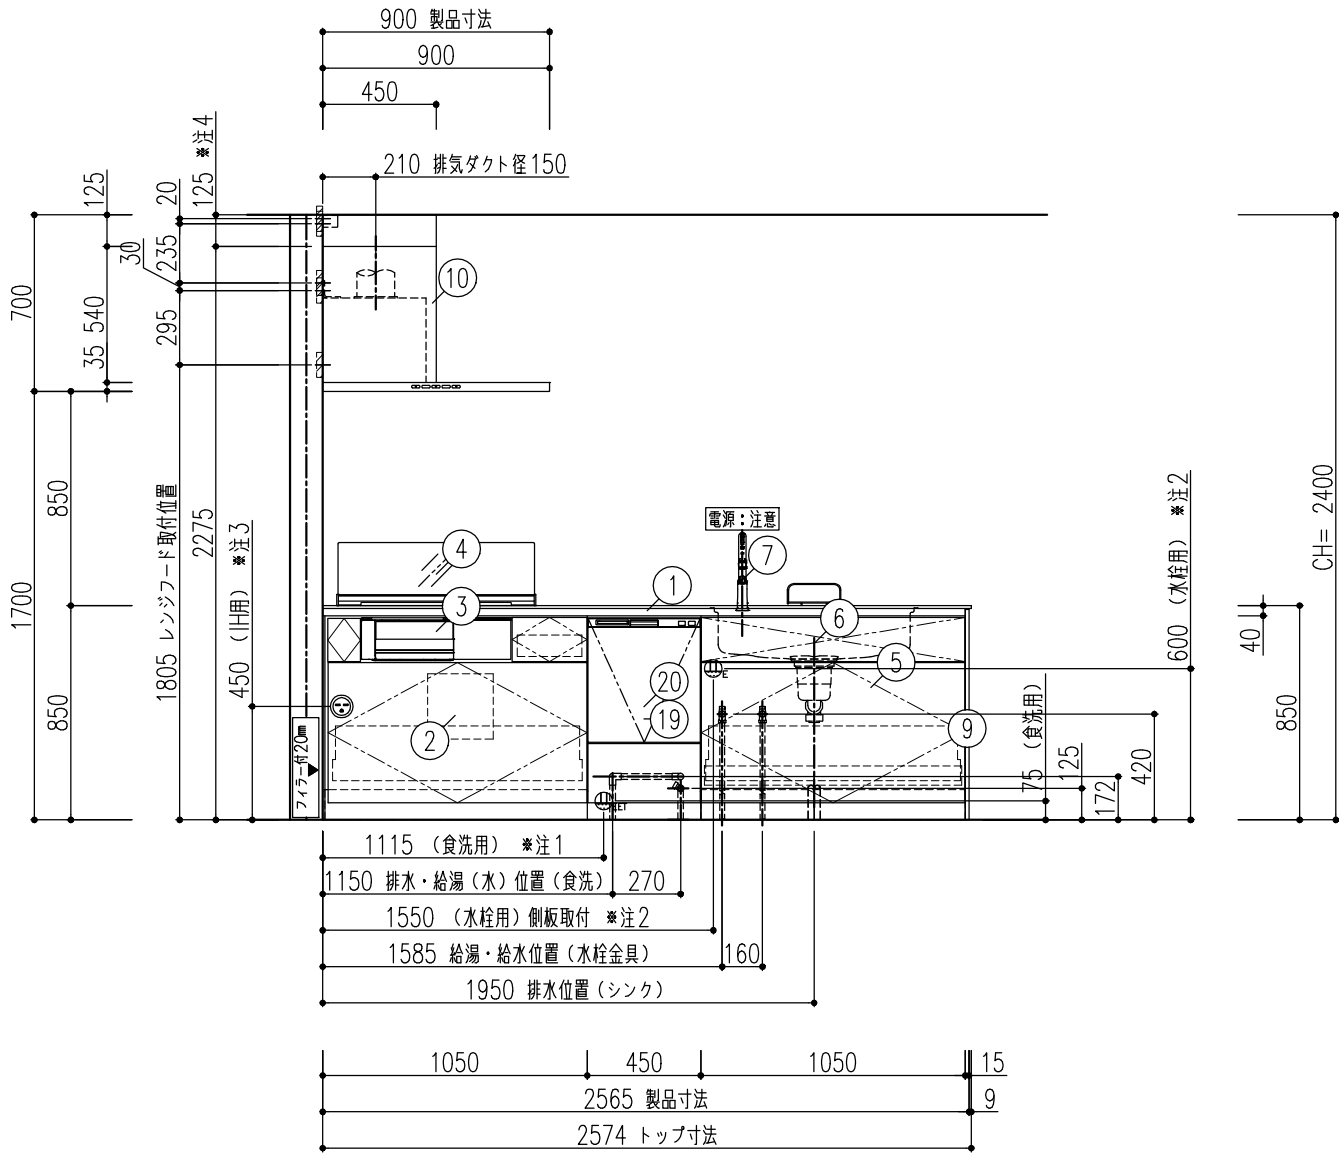


|                                                                           |     |         |                    |      |            |    |            |
|---------------------------------------------------------------------------|-----|---------|--------------------|------|------------|----|------------|
| 特記事項<br>扉色 VK5:グレージュスタッコ<br>取手 【M】スリム取手 (ブラック)<br>ワークトップカラー 【DW】 ソルティホワイト | 物件名 | 小林大樹 様邸 | 案件No.              | 図面名  | 担当         | 図面 | 図番         |
|                                                                           | 仕様  | ES21    | A2511DDD0EXLYQ     | 納まり図 | 栗野 友仁      |    | 株式会社 LIXIL |
|                                                                           |     |         | 見積No.              | 縮尺   | 日付         |    |            |
|                                                                           |     |         | M25119238165-007-2 | 1/30 | 2026.02.27 |    |            |

C面


D面

注3) 250V・30A 2極接地極付コンセント（コンセントベース固定）【専用】  
注5) 125V・15A 2極接地極付アースターミナル付コンセント 【専用】（フード用）

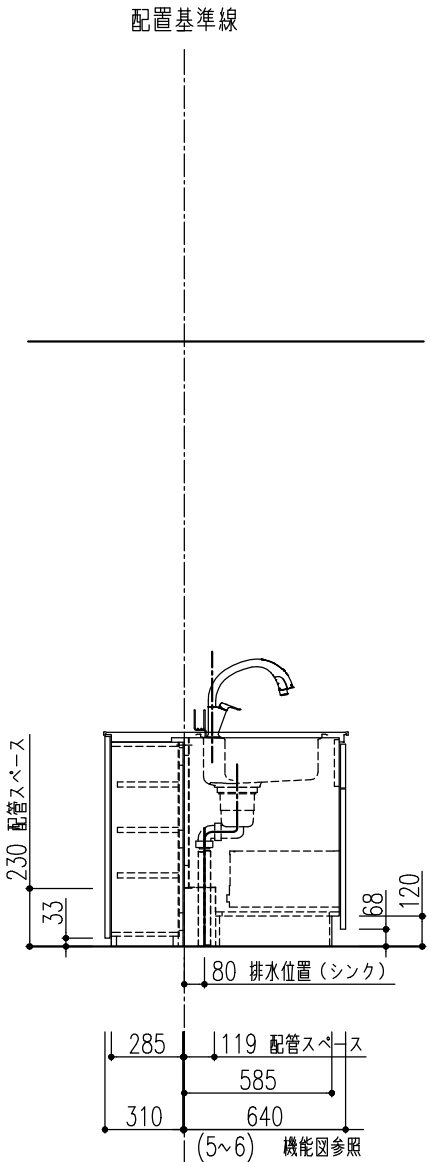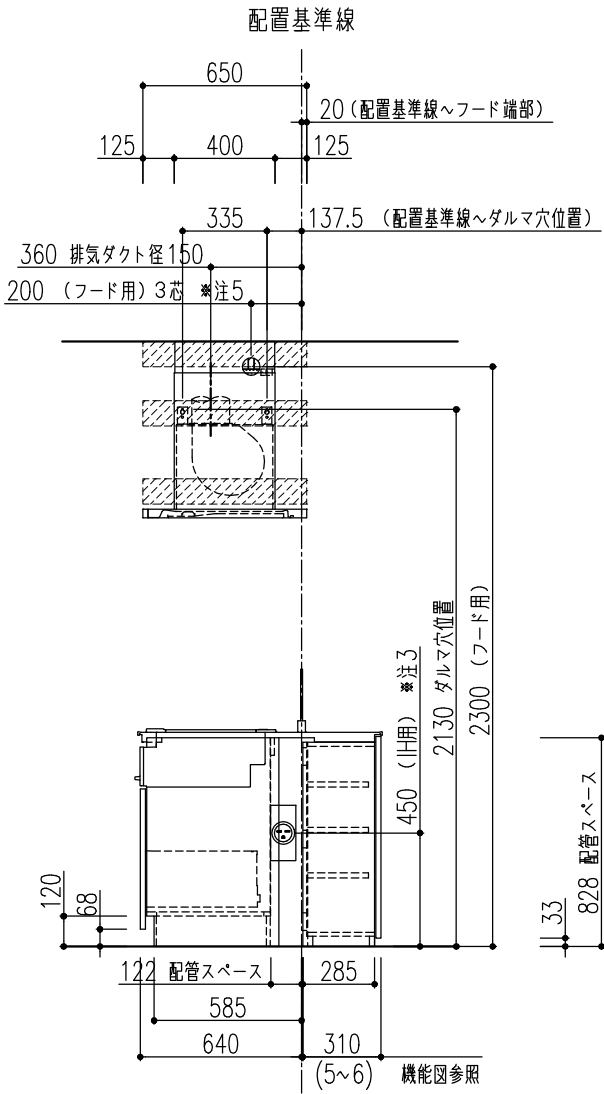

|                                                                         |     |         |                    |      |            |    |            |
|-------------------------------------------------------------------------|-----|---------|--------------------|------|------------|----|------------|
| 特記事項<br>扉色 VK5:グレージュスタック<br>取手 【M】スリム取手（ブラック）<br>ワークトップカラー 【DW】ソルティホワイト | 物件名 | 小林大樹 様邸 | 案件No.              | 図面名  | 担当         | 図面 | 図番         |
|                                                                         | 仕様  | ES21    | A2511DDD0EXLYQ     | 納まり図 | 栗野 友仁      |    | 株式会社 LIXIL |
|                                                                         |     |         | 見積No.              | 縮尺   | 日付         |    |            |
|                                                                         |     |         | M25119238165-007-2 | 1/30 | 2026.02.27 |    |            |



■ 床の不陸に関して

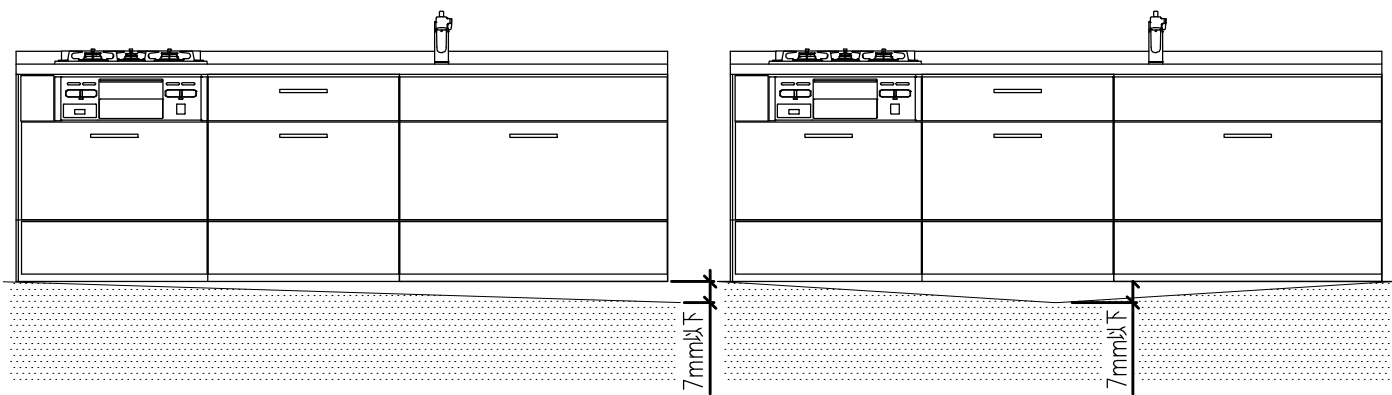

床の不陸は、7mm以下に抑えるようにしてください。不陸が大きい場合は、現場責任者に床の修正を依頼してください。  
※キャビネット取付時には不陸調整スペーサー等で水平になるように設置してください。

■ 裏面キャビネット納まりについて

(キッチン側キャビネット背面) 配置基準▽

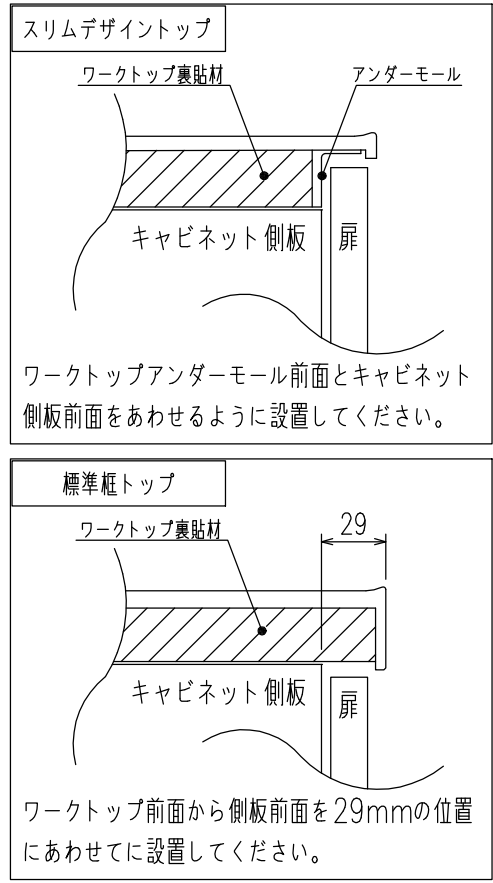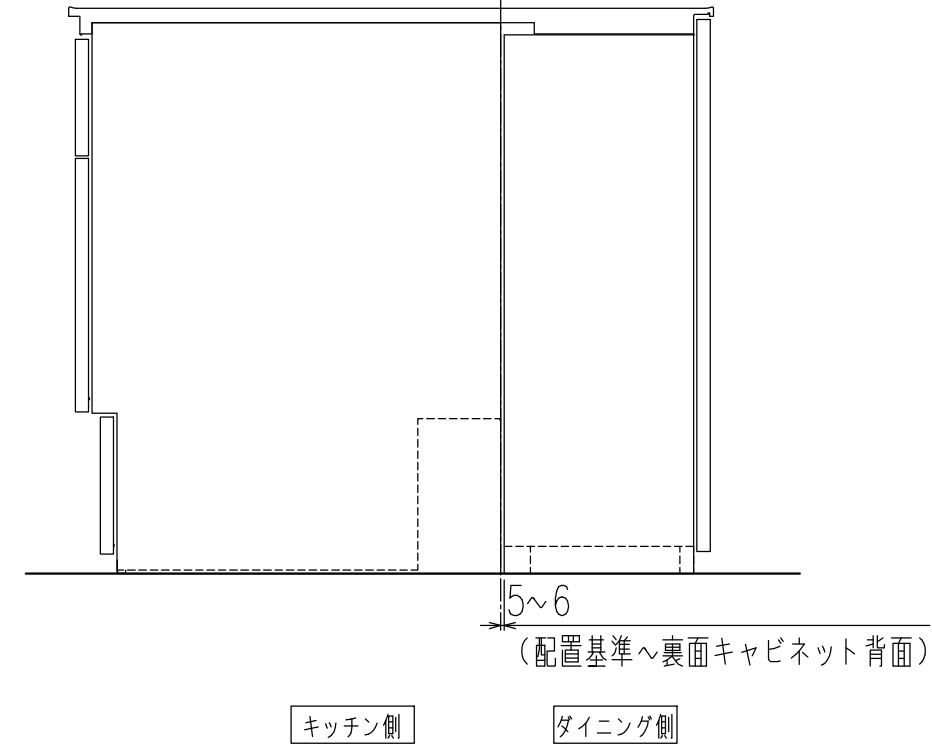

■ 食器洗い乾燥機内配管図 床立上げ配管例


※給水接続か給湯接続かお客様に確認したうえで施工願います。

給水（給湯の場合は耐熱配管）

- ①アングル型止水栓（ドライバー式）
- ②硬質塩化ビニルライニング鋼管相当品
- ③Rc1/2エルボ
- ④断熱材（Φ48）

排水（耐熱塩ビ使用のこと）

- ⑤排水パイプHT20相当品
- ⑥HT20エルボ

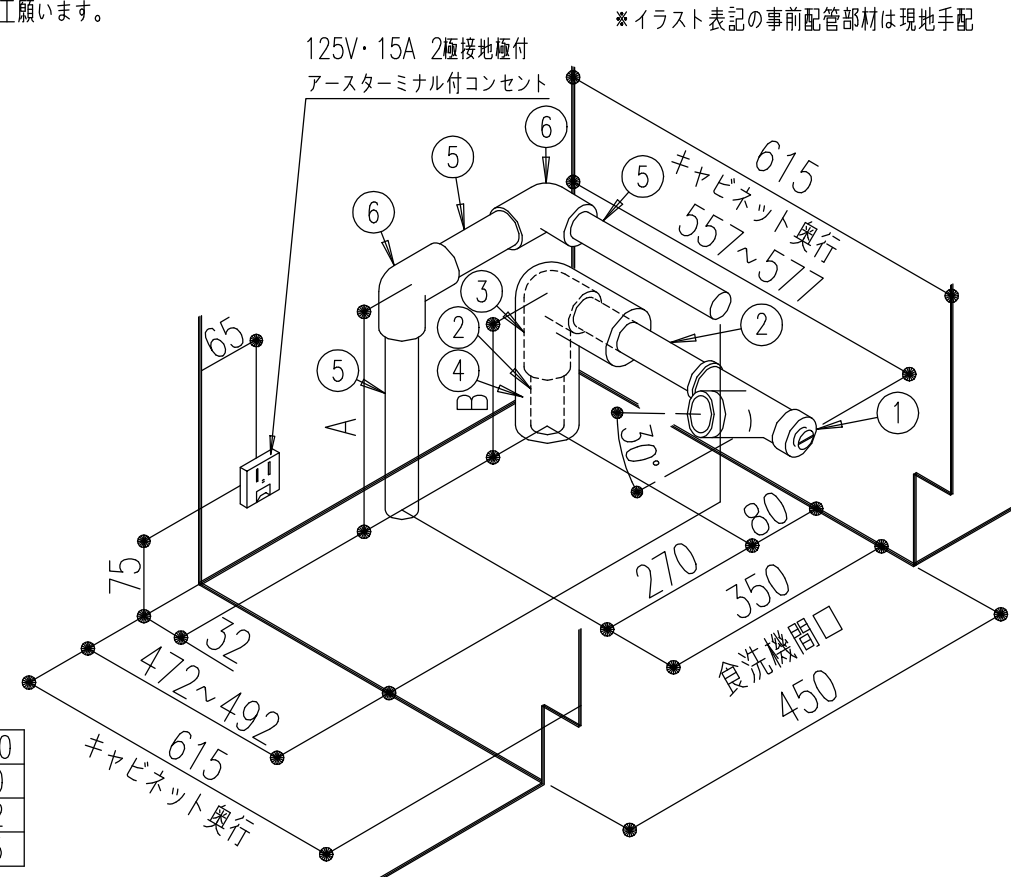


|        |      |      |      |      |
|--------|------|------|------|------|
| キッチン高さ | H825 | H850 | H875 | H900 |
| 本体高さ   | 775  | 800  | 825  | 850  |
| A      | 147  | 172  | 197  | 222  |
| B      | 100  | 125  | 150  | 175  |

■ レンジフード取付注意事項（壁面取付時）


レンジフードを取付ける場合は下地の材が厚み30mm以上、幅100mm以上、ビス固定位置が材の端部から25mm以上であることを確認してください。また、壁強度などの詳細は「レンジフード設置説明書」を必ず事前に確認してください。

取付位置については、取付設置図を確認してください。


参考図\_CLS. SER. NST. ASR. ADR. RVJ. GSR. BFRS. TARシリーズ  
（※RVJ. GSRシリーズの場合はレンジフードパネルの取付下地は不要です。）

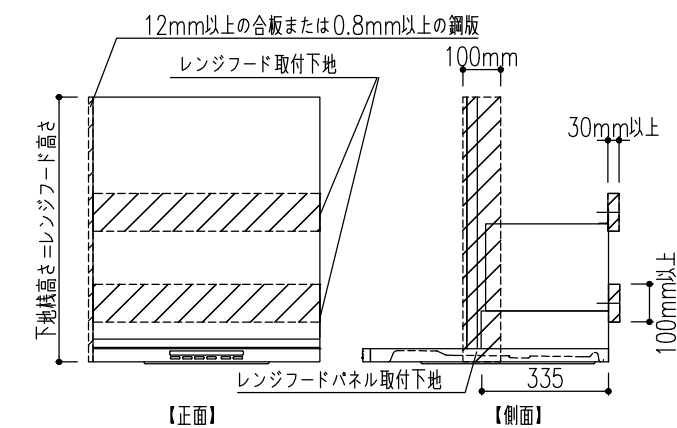

参考図\_FED. HVR. NSDシリーズ（サイドマントルタイプ）

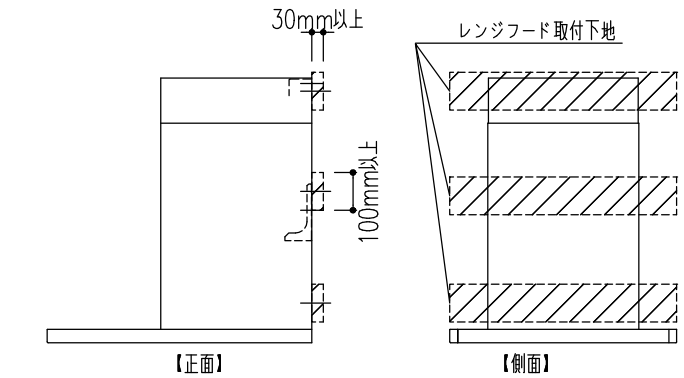


参考図\_NBHシリーズ

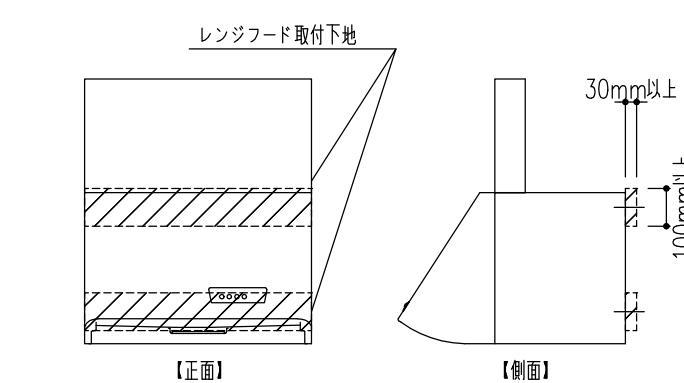



■ SMHVRフード

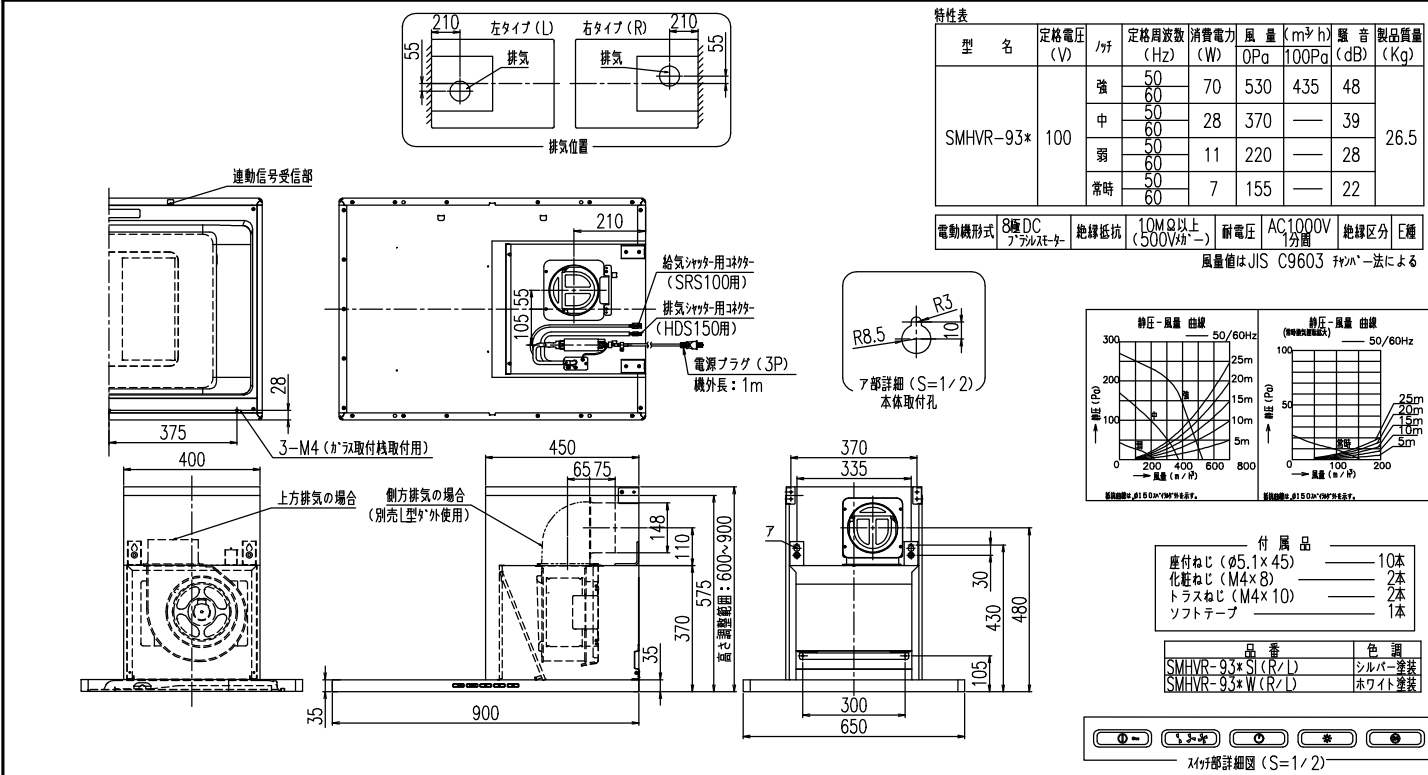


4. 製品名の末尾の ( ) にはワザンリスによって記号が入る場合があります。  
5. 電動シャッター (HDS150) (別売) を使用時は、中継コトを外して取り付けてください。  
6. 赤外線連動型リモコンです。単独でも使用できます。  
注) 1. 排気方向は側方 (L型) 外使用: 別売) と上方です。

■ IHヒーター用コンセント推奨位置図 / 側面設置の場合


※コンセントや電源プラグが、引き出しおよびIHヒーター用仕切板 (オプション) に接触しないように注意してください。  
※木製キッチンの配管スペース付キャビネットは、キャビネット内にコンセントを取り付けるスペースがありませんので、別売のコンセントベース (W-SOCKET-B) などを使用して配管スペース内にコンセントを設置してください。

| キッチン高さ | コンセント下端高さ | コンセントセンター高さ |
|--------|-----------|-------------|
| 800    | 355       | 400         |
| 850    | 405       | 450         |
| 900    | 455       | 500         |

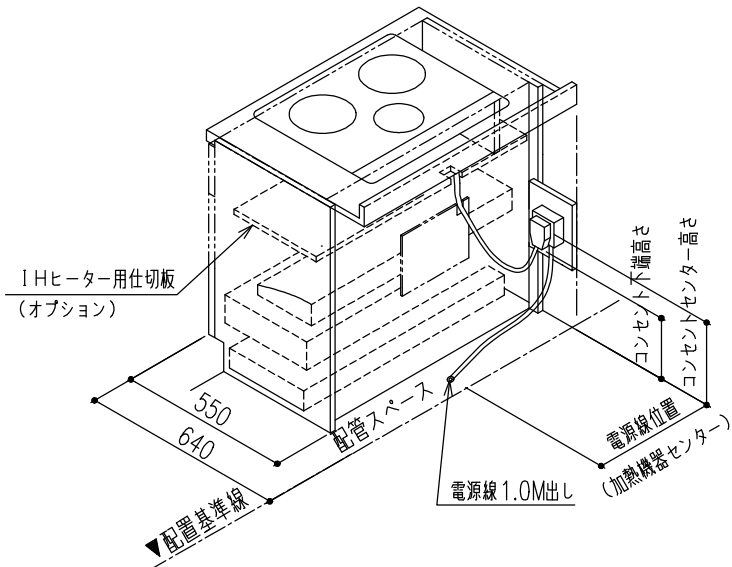


注意: 引き出しおよびIHヒーター用仕切板 (オプション) に接触しないように上記寸法を参照してください。

■ 止水栓図 (床立上げ)

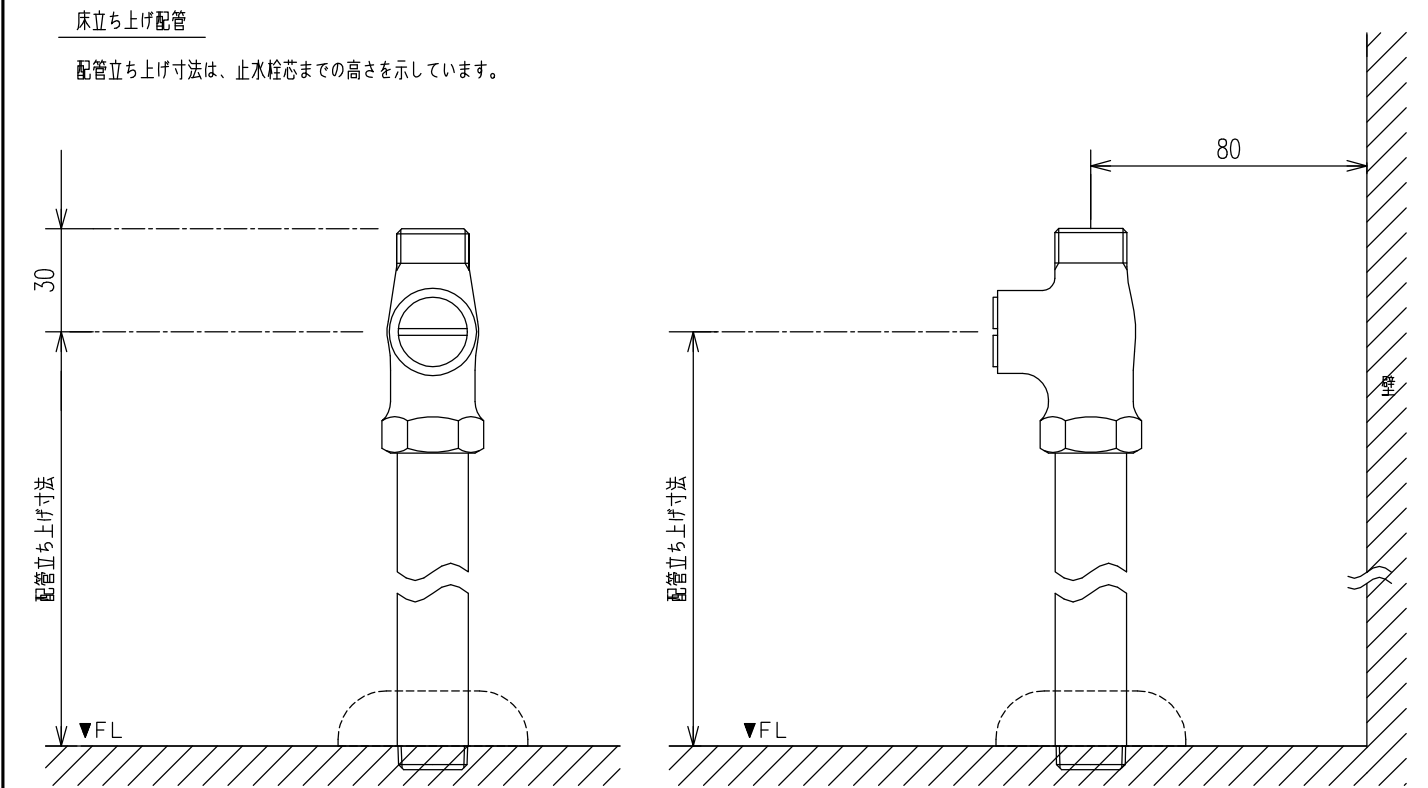

■ タッチレス水栓ナビッシュ 推奨電源位置図

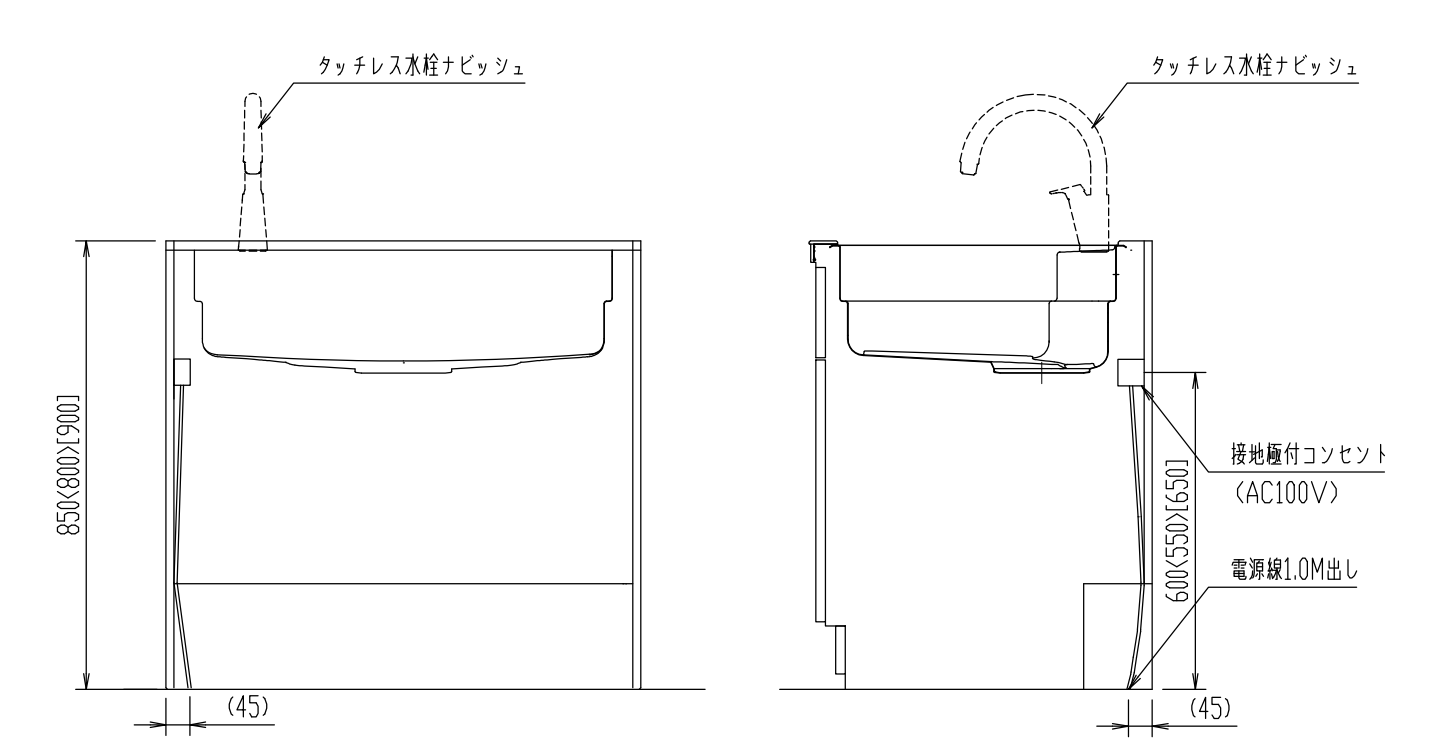




- 水栓がシンク右側の場合、電源位置は左右対象の位置にしてください。  
○水栓がシンク中央の場合、電源位置は左右どちらでも構いません。  
○< >内寸法はワークトップ高さ80cmの場合、[ ]内寸法はワークトップ高さ90cmの場合。

|                                                                          |               |                     |       |     |    |    |   |
|--------------------------------------------------------------------------|---------------|---------------------|-------|-----|----|----|---|
| 特記事項<br>扉色 VK5:グレイジュスタック<br>取手 [M]スリム取手 (ブラック)<br>ワークトップカラー 【DW】ソルティホワイト | 物件名<br><br>仕様 | 小林大樹 様邸<br><br>ES21 | 案件No. | 図面名 | 担当 | 図面 | 図番 :<br><br><br><br><br><br><br><br><br><br><br><br><br><br><br><br><br><br><br><br><br><br><br><br><br><br><br><br><br><br><br><br><br><br><br><br><br><br><br><br><br><br><br><br><br><br><br><br><br><br><br><br><br><br><br><br><br><br><br><br><br><br><br><br><br><br><br><br><br><br><br><br><br><br><br><br><br><br><br><br><br><br><br><br><br><br><br><br><br><br><br><br><br><br><br><br><br><br><br><br><br><br><br><br><br><br><br><br><br><br><br><br><br><br><br><br><br><br><br><br><br><br><br><br><br><br><br><br><br><br><br><br><br><br><br><br><br><br><br><br><br><br><br><br><br><br><br><br><br><br><br><br><br><br><br><br><br><br><br><br><br><br><br><br><br><br><br><br><br><br><br><br><br><br><br><br><br><br><br><br><br><br><br><br><br><br><br><br><br><br><br><br><br><br><br><br><br><br><br><br><br><br><br><br><br><br><br><br><br><br><br><br><br><br><br><br><br><br><br><br><br><br><br><br><br><br><br><br><br><br><br><br><br><br><br><br><br><br><br><br><br><br><br><br><br><br><br><br><br><br><br><br><br><br><br><br><br><br><br><br><br><br><br><br><br><br><br><br><br><br><br><br><br><br><br><br><br><br><br><br><br><b|--------------------------------------------------------------------------|---------------|---------------------|-------|-----|----|----|---|

■ キッチン取付者さま向け 動画コンテンツ ■

商品取付けの注意点を2次元コードでご視聴いただけます。  
取付日より前に、是非ご確認ください。
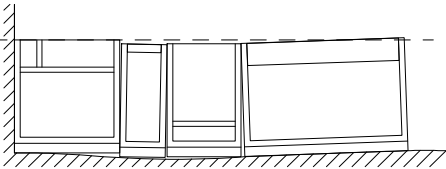
|                 |                                    |                                                                                     |                          |
|-----------------|------------------------------------|-------------------------------------------------------------------------------------|--------------------------|
| 荷扱い・搬入          | カウンター開梱搬入「養生ツール」                   | 不陸の確認と調整                                                                            | マグネットキッチンパネル             |
| 荷扱い・搬入          | カウンター開梱搬入「養生ツール」のご紹介               |  | マグネット キッチンパネル「取付・設置」ポイント |
| 作成日：2024年10月01日 | 作成日：2024年10月01日<br>改定日：2025年12月11日 | 作成日：2024年02月07日                                                                     | 作成日：2024年03月06日          |


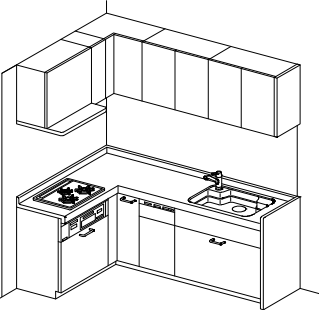
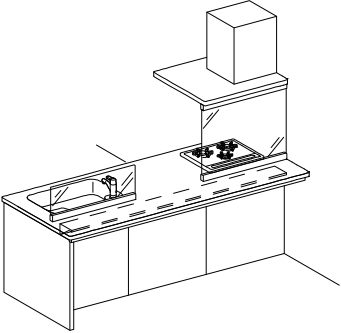
|                                                                                    |                                                                                     |  |  |
|------------------------------------------------------------------------------------|-------------------------------------------------------------------------------------|--|--|
| 人造大理石カウンターL型キッチン                                                                   | センターキッチン（ペニンシュラ型）                                                                   |  |  |
|  |  |  |  |
| 作成日：2024年02月07日                                                                    | 作成日：2024年02月07日                                                                     |  |  |

|  |                                                                         |                |         |  |                    |  |       |  |            |    |    |            |
|--|-------------------------------------------------------------------------|----------------|---------|--|--------------------|--|-------|--|------------|----|----|------------|
|  |                                                                         |                |         |  |                    |  |       |  |            |    |    |            |
|  | 特記事項<br>扉色 VK5:グレージュスタッコ<br>取手 [M]スリム取手（ブラック）<br>ワークトップカラー 【DW】ソルティホワイト | 物件名            | 小林大樹 様邸 |  | 案件No.              |  | 図面名   |  | 担当         | 図面 | 図番 | 株式会社 LIXIL |
|  |                                                                         | A2511DDD0EXLYQ |         |  | 機能図                |  | 栗野 友仁 |  |            |    |    |            |
|  |                                                                         | 仕様             | ES21    |  | 見積No.              |  | 縮尺    |  | 日付         |    |    |            |
|  |                                                                         |                |         |  | M25119238165-007-2 |  |       |  | 2026.02.27 |    |    |            |



■ キッチン取付者さま向け 動画コンテンツ ■

商品取付けの注意点を2次元コードでご視聴いただけます。  
取付日より前に、是非ご確認ください。
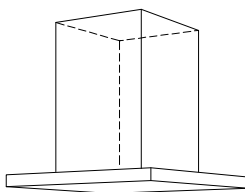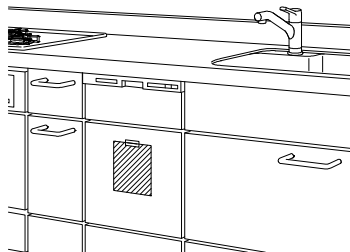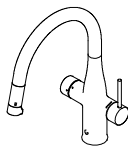
|   |  |                                                         |  |   |  |   |  |     |            |    |            |
|---|--|---------------------------------------------------------|--|---|--|---|--|-----|------------|----|------------|
| センターフード型レンジフード<br>(天吊りフード)<br><br><br>作成日：2024年06月03日 |  | I H加熱機器関連<br><br>I H加熱機器<br>仕切り板<br><br>作成日：2024年02月07日 |  | 食器洗い乾燥機<br><br><br>作成日：2024年02月07日 |  | ミネラル浄水栓 Greentap<br><br><br>作成日：2024年06月03日 |  |     |            |    |            |
|   |  |                                                         |  |   |  |   |  |     |            |    |            |
|   |  |                                                         |  |   |  |   |  |     |            |    |            |
|   |  |                                                         |  |   |  |   |  |     |            |    |            |
| <div>特記事項</div> <div>扉色 VK5:グレージュスタック</div> <div>取手 [M]スリム取手 (ブラック)</div> <div>ワークトップカラー 【DW】ソルティホワイト</div>                            |  | <div>物件名</div> <div>仕様</div>                            |  | 小林大樹 様邸<br><br>ES21                                                                                                   |  | 案件No.   |  | 図面名 | 担当         | 図面 | 図番         |
|   |  |                                                         |  |   |  | A2511DDD0EXLYQ   |  | 機能図 | 栗野 友仁      |    | 株式会社 LIXIL |
|   |  |                                                         |  |   |  | 見積No.   |  | 縮尺  | 日付         |    |            |
|   |  |                                                         |  |   |  | M25119238165-007-2   |  |     | 2026.02.27 |    |            |