

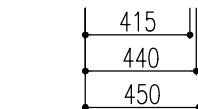



面

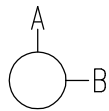

A面

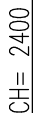


面

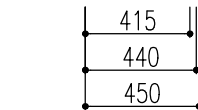[illegible]

【 ご注意 】

- 記載のワークトップ、カウンター、エンドパネル、サイドパネルの寸法は呼び寸法です。詳細寸法は商品ガイドの巻末資料をご確認ください。

特記事項 扉色 VK5:グレイジュスタッコ 取手 [M]スリム取手(ブラック)	物件名	小林大樹 様邸	案件No.	図面名	担当	図面	図番 : 株式会社 LIXIL
			A2511DDDOEXLYQ	レイアウト図	葉野 友仁		
	仕様	ES21	見積No.	縮尺	日付		
			M25119238165-007-3	1/30	2026.02.27		

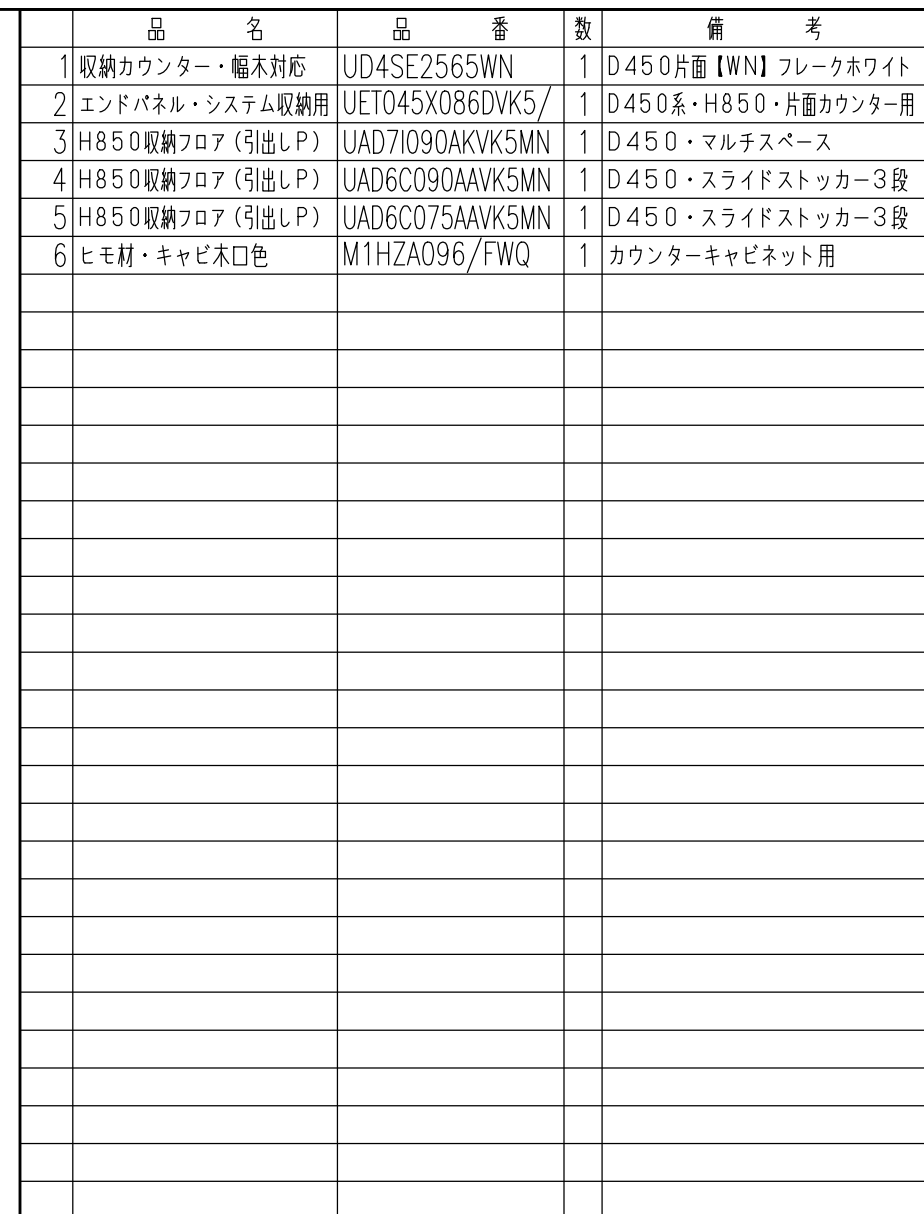

特記事項
扉色 VK5:グレージュスタッコ
取手 [M]スリム取手(ブラック)

物件名	仕様
-----	----



小林大樹 様邸

ES21

案件No.	図面名	担当	図面	図番
511DDDOEXLYQ	納まり図	栗野 友仁		株式会社 LIXIL
見積No.	縮尺	日付		
19238165-007-3	1/30	2026.02.27		


B面

B面

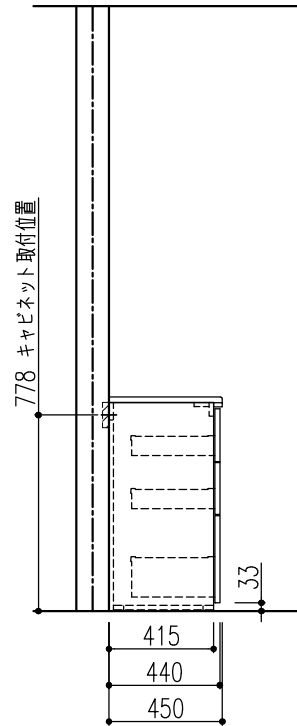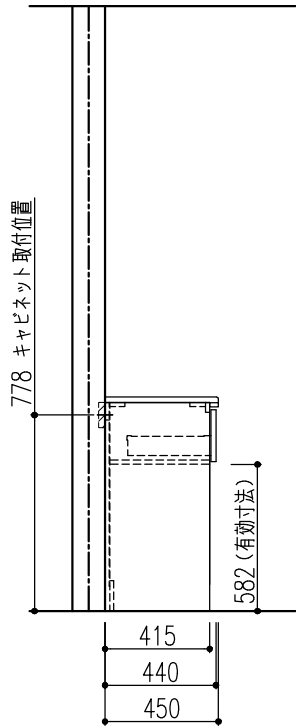

特記事項 扉色 VK5:グレージュスタック 取手 [M]スリム取手（ブラック）	物件名	小林大樹 様邸	案件No.	図面名	担当	図面	図番
			A2511DDD0EXLYQ	納まり図	栗野 友仁		株式会社 LIXIL
	仕様	ES 2 1	見積No.	縮尺	日付		
			M25119238165-007-3	1/30	2026.02.27		

■ 床の不陸に関して

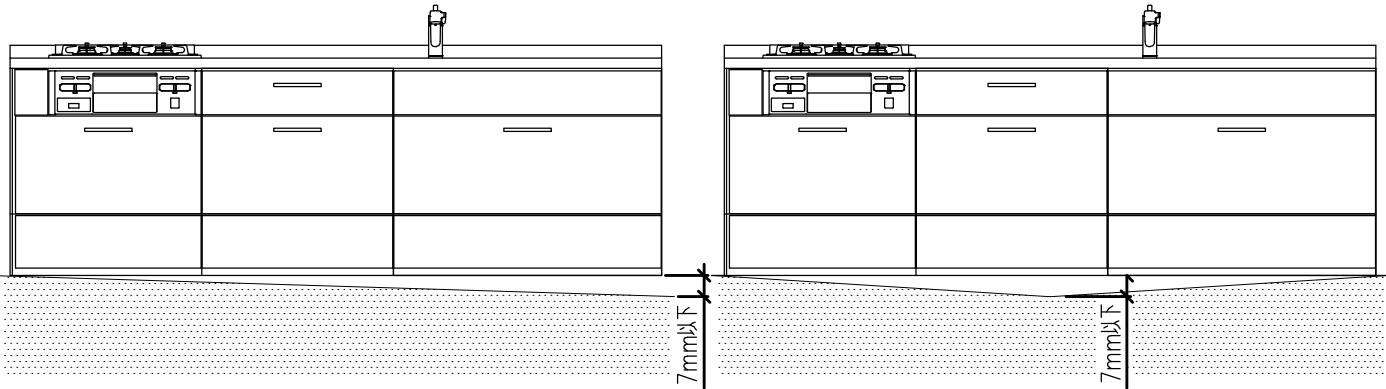

床の不陸は、7 m m 以下に抑えるようにしてください。不陸が大きい場合は、現場責任者に床の修正を依頼してください。
※キャビネット取付時には不陸調整スペーサー等で水平になるように設置してください。

	特記事項 扉色 VK5:グレージュスタック 取手 [M]スリム取手（ブラック）	物件名	小林大樹 様邸	案件No.	図面名	担当	図面	図番
				A2511DDD0EXLYQ	機能図	栗野 友仁		株式会社 LIXIL
		仕様	ES 2 1	見積No.	縮尺	日付		
				M25119238165-007-3		2026.02.27		

■ キッチン取付者さま向け 動画コンテンツ ■
商品取付けの注意点を2次元コードでご視聴いただけます。
取付日より前に、是非ご確認ください。

1 ページ目

■ キッチン取付者さま向け 動画コンテンツ ■
商品取付けの注意点を2次元コードでご視聴いただけます。
取付日より前に、是非ご確認ください。

1 ページ目

■ キッチン取付者さま向け 動画コンテンツ ■

商品取付けの注意点を2次元コードでご視聴いただけます。
取付日より前に、是非ご確認ください。

1 ページ目

荷扱い・搬入

荷扱い・搬入



作成日：2024年10月01日

荷扱い・搬入

荷扱い・搬入



作成日：2024年10月01日



荷扱い・搬入

荷扱い・搬入



作成日：2024年10月01日

カウンター開梱搬入「養生ツール」

カウンター開梱搬入 「養生ツール」のご紹介



作成日：2024年10月01日
改定日：2025年12月11日

カウンター開梱搬入「養生ツール」

カウンター開梱搬入 「養生ツール」のご紹介



作成日：2024年10月01日
改定日：2025年12月11日




カウンター開梱搬入「養生ツール」

カウンター開梱搬入 「養生ツール」のご紹介





作成日：2024年10月01日
改定日：2025年12月11日


不陸の確認と調整

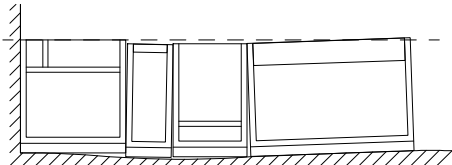

作成日：2024年02月07日

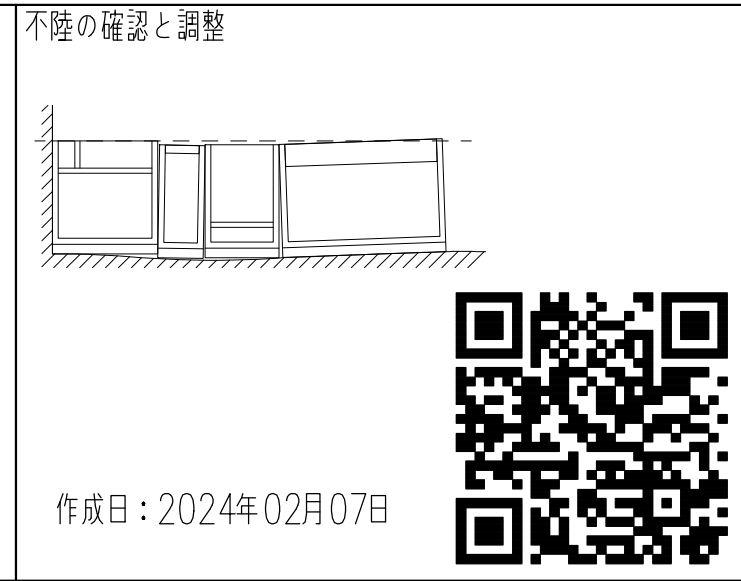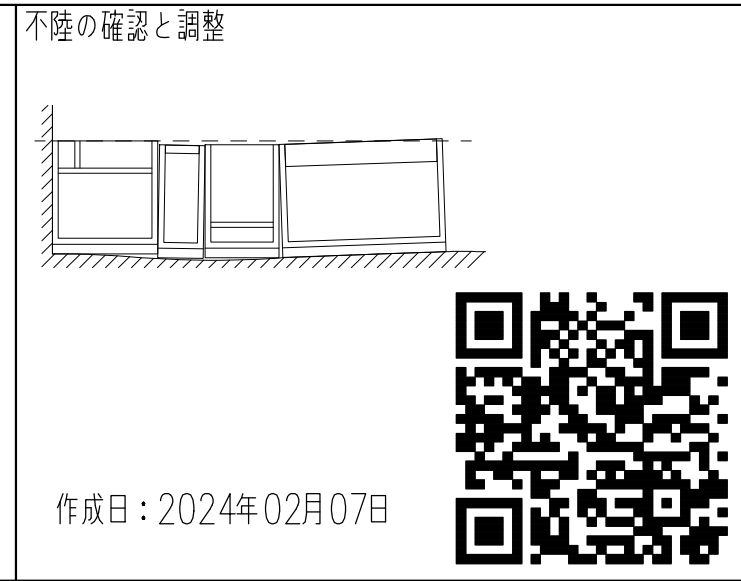

不陸の確認と調整

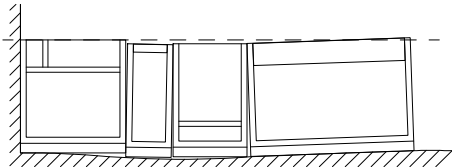

作成日：2024年02月07日



マグネットキッチンパネル

マグネット キッチンパネル 「取付・設置」ポイント



作成日：2024年03月06日

マグネットキッチンパネル

マグネット キッチンパネル 「取付・設置」ポイント



作成日：2024年03月06日



マグネットキッチンパネル


マグネット キッチンパネル

「取付・設置」ポイント



作成日：2024年03月06日


人造大理石カウンターL型キッチン

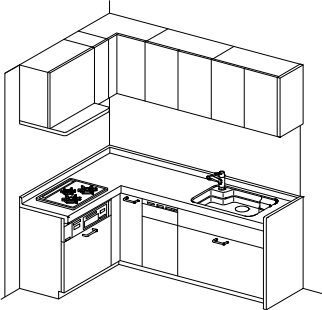

作成日：2024年02月07日




人造大理石カウンターL型キッチン

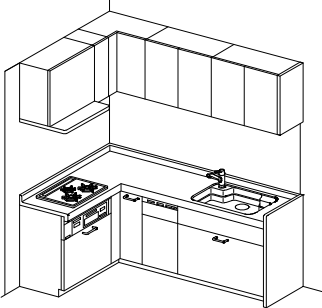



作成日：2024年02月07日




センターキッチン（ペニンシュラ型）

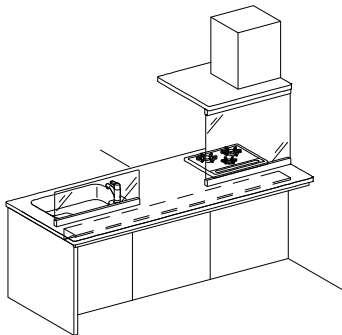

作成日：2024年02月07日

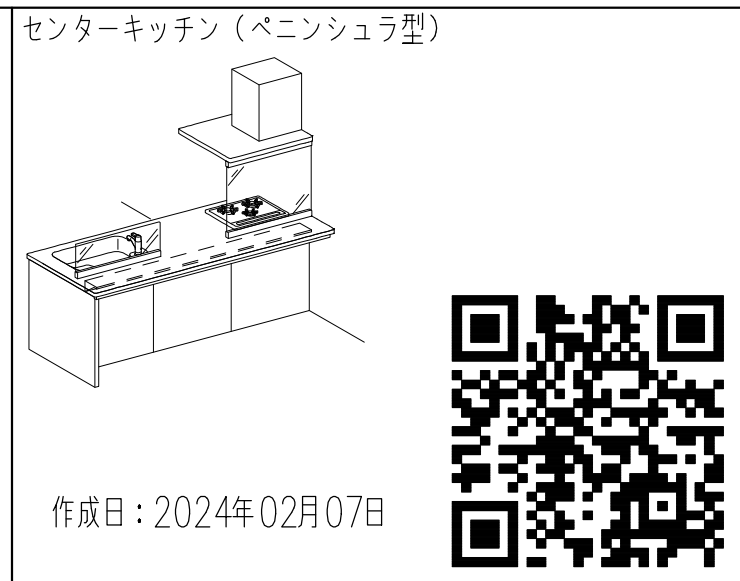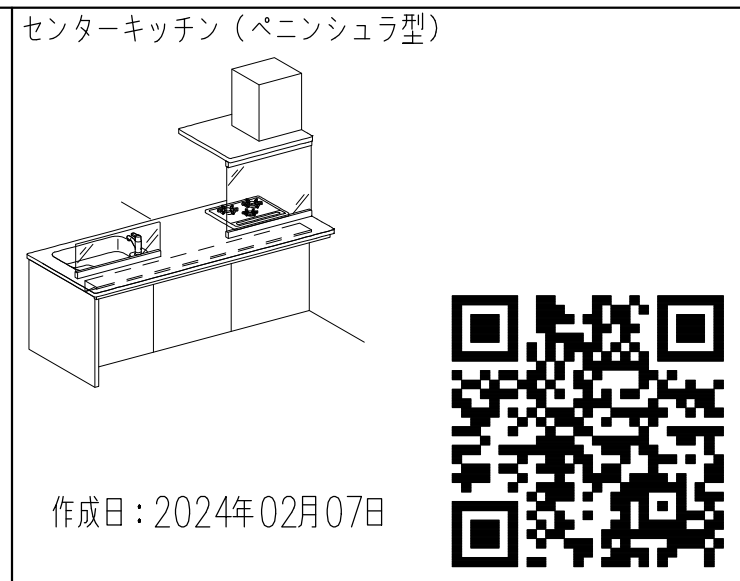

センターキッチン（ペニンシュラ型）

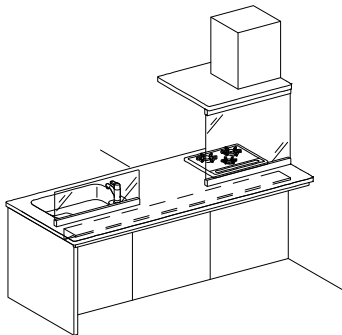




作成日：2024年02月07日



		特記事項 扉色 VK5:グレージュスタック 取手 [M]スリム取手（ブラック）	物件名 仕様	小林大樹 様邸 E S 2 1	案件No.	図面名	担当	図面	図番 ： 株式会社 LIXIL	
					A2511DDD0EXLYQ	機能図	栗野 友仁			
					見積No.	縮尺	日付			
					M25119238165-007-3		2026.02.27			

■ キッチン取付者さま向け 動画コンテンツ ■

商品取付けの注意点を2次元コードでご視聴いただけます。
取付日より前に、是非ご確認ください。

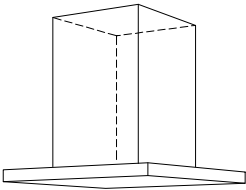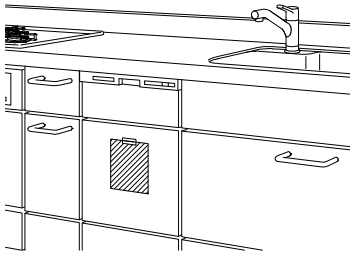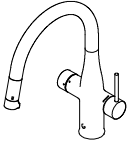センターフード型レンジフード (天吊りフード)  作成日：2024年06月03日 	I H加熱機器関連 I H加熱機器 仕切り板 作成日：2024年02月07日 	食器洗い乾燥機  作成日：2024年02月07日 	ミネラル浄水栓 Greentap  作成日：2024年06月03日 
---	--	--	---

--	--	--	--

--	--	--	--

特記事項 扉色 VK5:グレージュスタック 取手 [M]スリム取手（ブラック）	物件名	小林大樹 様邸	案件No.	図面名	担当	図面	図番
	仕様	ES21	A2511DDD0EXLYQ	機能図	栗野 友仁		株式会社 LIXIL
			見積No.	縮尺	日付		
			M25119238165-007-3		2026.02.27		