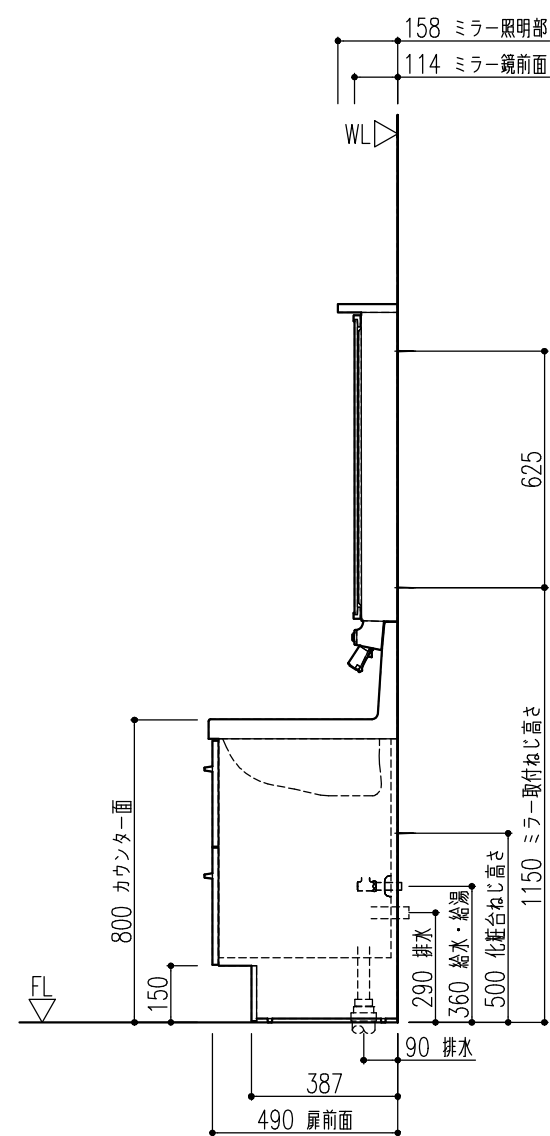
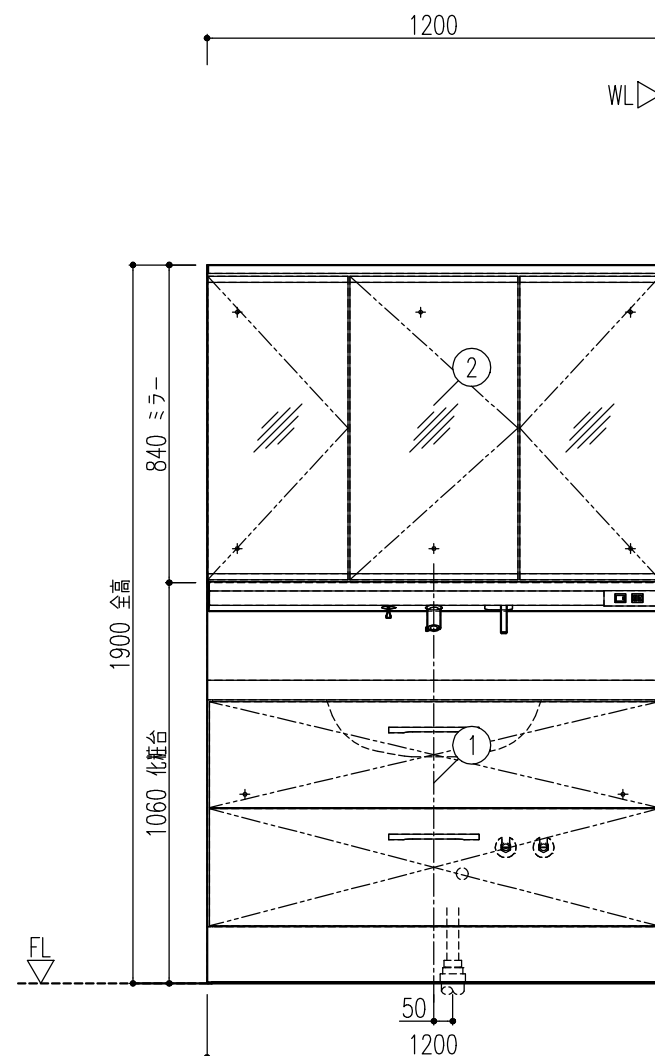
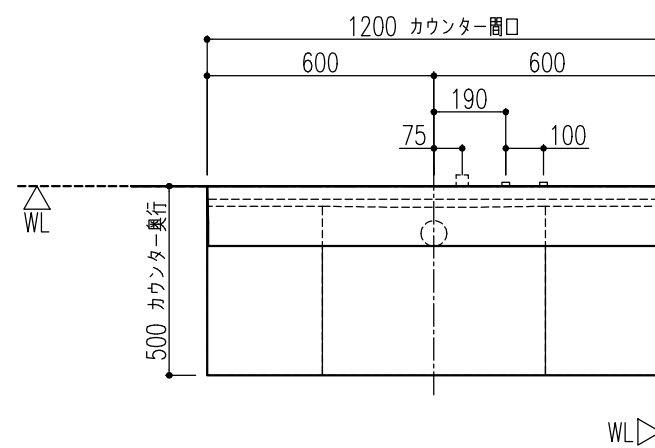


[illegible]

※部品の表の「図面」列に○がないものは図面表示されません。

- ・止水栓は左側が給湯位置、右側が給水位置を示します。
- ・排水管VP・VU50管の立上寸法は、F.L.より、  
20mm～30mmの範囲内で立ち上げてください。
- ・排水管VP・VU40管の立上寸法は、F.L.より、  
35mm～45mmの範囲内で立ち上げてください。
- ・給水、給湯接続はR1/2

※「ねじ固定位置」には必ず補強木（幅90mm×厚み30mm以上）または、  
取付壁全面に厚み12mm以上（※床面に接地されないカウンターやキャビネットは、厚み24mm以上）のJAS規格品合板を強固に取り付けてください。

※止水栓は別途手配してください。

※壁排水のときは、市販の排水アダプターをご使用ください。

※ミラーキャビネットはシリコンシーリングが出来ません。（シリコンが付きません。）

■化粧台本体仕様

扉カラー：YS2 グロスホワイト 材質：DAP化粧板

カウンターカラー：H プレーンネオホワイト 人造大理石（ポリエステル系樹脂）

洗面器容量：16L

水栓金具：シングルレバーシャワー水栓（ホース収納式/吐水切替付）エコハンドル（節湯C1）

排水器具：ポップアップ排水栓（てまなし排水口）・ヘアキャッチャー付・フタ着脱式

排水トラップ：床排水・壁排水兼用ボルトトラップ（フレキホース・呼び径32mm）

■ミラーキャビネット仕様

照明（定格消費電力）：LED照明（6.5W）

くもり止めコート仕様（中央鏡）・トレイ15個付

コンセント3個（外付1個・内部2個） コンセント許容電力合計1300W以下（内部コンセント含む）

プラグ式電源仕様 電源コード長さ：2.1m ※取出可能長さは機能図参照の事

|     |                                                                     |                    |         |            |    |            |
|-----|---------------------------------------------------------------------|--------------------|---------|------------|----|------------|
| 物件名 | 小林大樹 様邸                                                             | 案件No.              | 図面名     | 担当         | 図面 | 図番         |
|     |                                                                     | A2511DDDOEXLYQ     | 簡易取付設置図 | 栗野 友仁      |    |            |
| 仕様  | EV/奥行500タイプ/23モデル/フルスライドタイプ/シングルレバーシャワー水栓<br>LED照明(スリムLED)/3面鏡(全収納) | 見積No.              | 縮尺      | 日付         |    | 株式会社 LIXIL |
|     |                                                                     | M25119238165-007-4 | 1/20    | 2026.02.27 |    |            |


■参考取付図【排水金具】

＜壁床排水兼用のマルチボルトトラップ仕様について＞

マルチボルトトラップは、フレキホース仕様のため壁、床排水の両方に対応できるトラップです。


※マルチボルトトラップ（床排水）は、住宅品質確保促進法「維持管理対策等級」2または3に対応しています。

＜マルチボルトトラップの接続＞

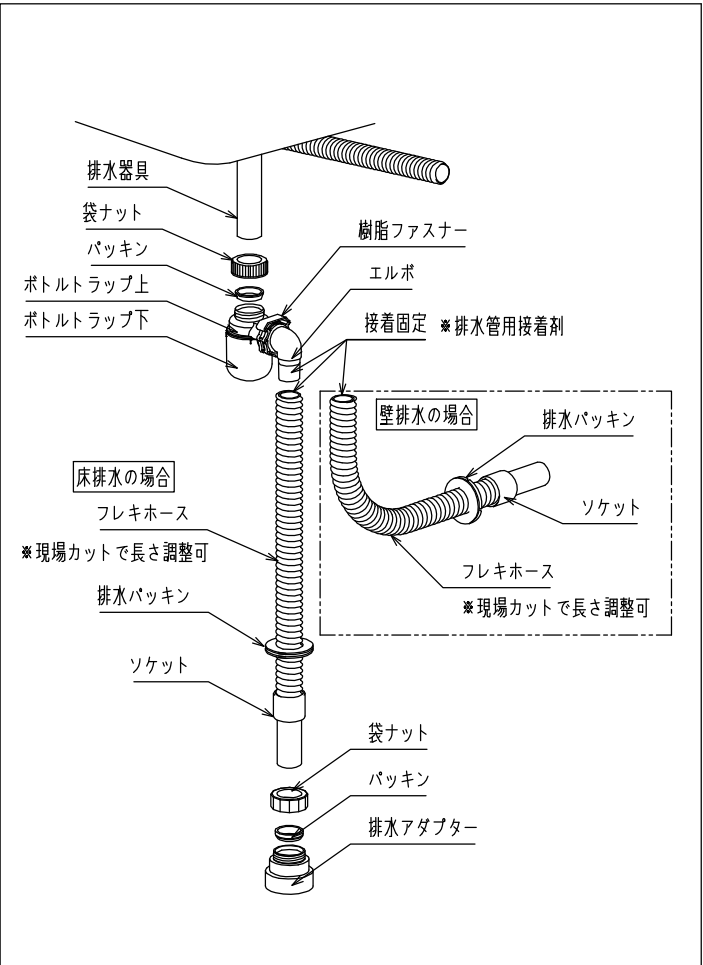

＜フレキホースの接続可能範囲＞

ハッチング範囲内の建築側排水管であれば接続可能です。  
フレキホースは建築側排水管の真上から接続してください。

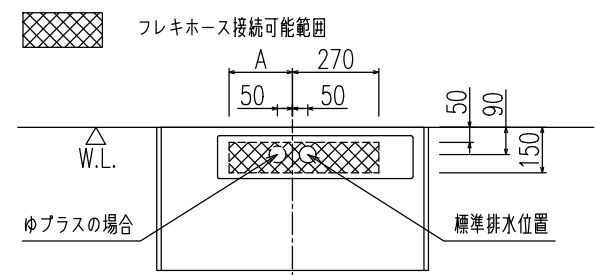

| 引出しタイプ |     | フルスライドタイプ |     | 扉タイプ |     |
|--------|-----|-----------|-----|------|-----|
| 間口     | A   | 間口        | A   | 間口   | A   |
| 750    | 24  | 750       | 130 | 750  | 210 |
| 900    | 99  | 900       | 130 | 900  | 210 |
| 1000   | 149 | 1000      | 130 |      |     |
| 1200   | 210 | 1200      | 130 |      |     |

注意

フレキホース取り回しの際は最小曲げR120以下にならないこと。  
※ホースの折れ、つぶれ等が発生する恐れがあります


最小曲げR120

△ 注意

- ・建築側排水管VP・VU50管の立上寸法は、F.L.より20～30mmの範囲内で、VP・VU40管の立上寸法は、F.L.より35～45mmの範囲で立ち上げてください。（右図参照）  
※立上寸法が足りないと接着できなくなります。
- ・配管の接着は接着面全面に塩ビ管用接着剤を十分に塗り、奥まで十分に押し込み接着してください。
- ・接着には耐熱塩ビ管（HT管）用接着剤を使用しないでください。  
※漏水し、家財などを濡らす拡大損害発生 の恐れがあります。
- ・壁排水の場合は、市販の排水アダプターをご使用ください。
- ・建築側排水管と化粧台開口部に隙間がある場合、シリコンでシーリングしてください。


△ 注意

- ・バッキンの向きに注意してください。
- ・管は奥に当たるまで差し込んでください。
- ・袋ナットはしっかり締めてください。  
※漏水し、家財などを濡らす拡大損害発生 の恐れがあります。

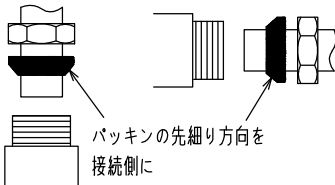


VP・VU50の場合

VP・VU40の場合

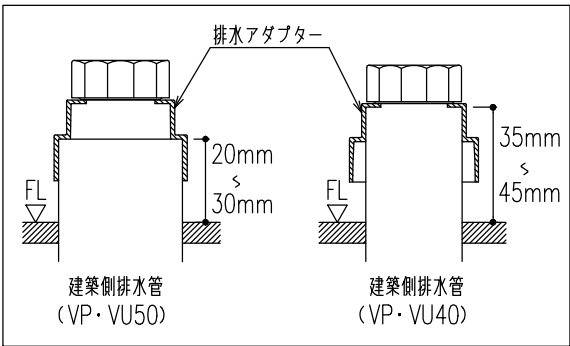

■カウンター・キャビネットを取付可能な壁面


【乾式壁の場合】

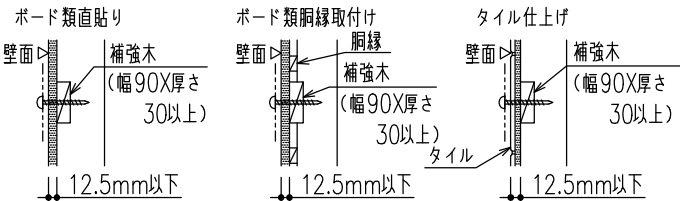

- 「ねじ固定位置」には必ず補強木（幅90mm X 厚み30mm以上）を設けてください。
- 補強木は必ず柱・間柱・縦杭などの建築躯体に固定してください。  
※補強木の固定は、キャビネットの固定強度と同等以上になるよう、種類・数を選定してください。
- 壁固定ねじを補強木に届かせるため、壁仕上げの総厚さは12.5mm以下にしてください。


【壁面に補強木が取り付けられない場合】

- 取付壁全面に厚み12mm以上のJAS規格品合板を強固に取り付けてください。【建築工事】  
※床面に接地されないカウンターやキャビネットは、厚み24mm以上のJAS規格品合板を強固に取り付けてください。

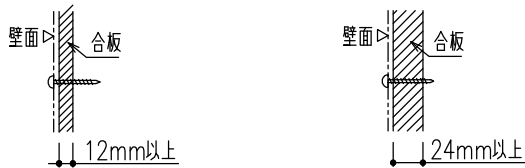

床面に接地されないカウンターやキャビネット

【湿式壁の場合】

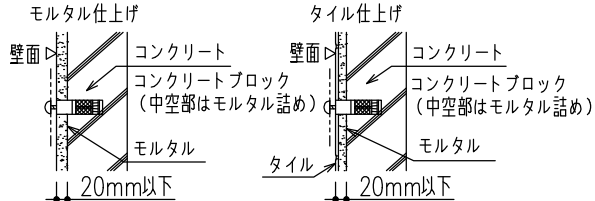

- ※AYボルト取付穴：φ7.5mm深さ60mm以上
- ※プラグ取付穴：φ6mm以上深さ50mm以上

【AYボルト・プラグセット品番】※別途手配品


| 標準の壁固定ねじの種類     | 対応AYボルト・プラグセット品番 | セット内容                          |
|-----------------|------------------|--------------------------------|
| タッピンねじトラス       | #KB-4X60T (AY)   | M4X60mmトラス2本入り                 |
| 平頭タッピンねじ        | #KB-4X60WT (AY)  | M4X60mmなべ2本入り、ワッシャー2個入り        |
| 平頭タッピンねじ化粧キャップ付 | #KB-4X60SC (AY)  | 化粧キャップ（白）、皿ワッシャー、M4X60mm皿各2個入り |
| 製品同梱ねじ使用        | #MIL-T8          | 樹脂性プラグ2個入り                     |
| タッピンねじトラス       | AY-24 (1P)       | M6X65mmトラス1本                   |

- 壁固定ねじに合ったAYボルトを使用してください。
- ※AYボルトを壁本体に届かせるため、壁仕上げの総厚さは20mm以下にしてください。
- ※AYボルト・プラグの種類、必要数はキャビネットにより異なります。
- 詳しくは取付説明書または洗面化粧台特注マニュアルでご確認ください。

【コンクリートブロック壁の場合】

- ブロック中空部はモルタル詰めする。

■底板詳細図

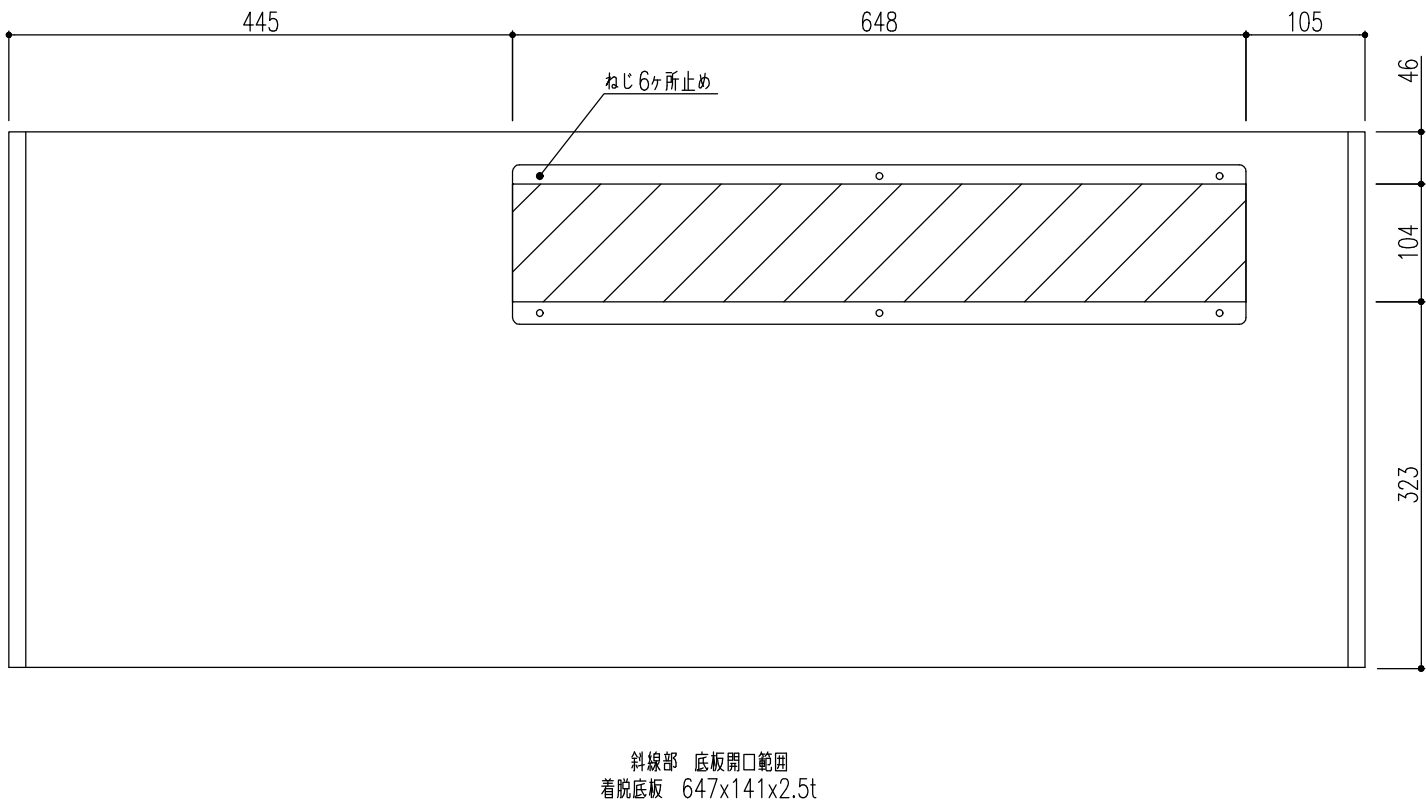

斜線部 底板開口範囲  
着脱底板 647x141x2.5t

特記事項

取り付けに関わる情報は機能図に記載しています。  
必ず機能図を出力の上ご確認ください。  
詳細仕様の確認は、単品図をご参照ください。

物件名

小林大樹 様邸

仕様

EVノ奥行500タイプノ23モデルノフルスライドタイプノシングルレバーシャワー水栓LED照明（スリムLED）ノ3面鏡（全収納）

案件No.

A2511DDDOEXLYQ

図面名

機能図

担当

栗野 友仁

図面

図番

株式会社 LIXIL

■電源コード取出位置 【3面鏡】

- ※ 1.コード有効長さ：ミラーキャビネット 取出口からの実際のコード寸法です。
- ※ 2.右図は参考図のため、実際のプランとは異なります。
- ※ 3.W キャビネット本体開口は、ミラーキャビネットの開口調整材を含まない寸法です。

【コンセント仕様について】

- 電源は過電流遮断器（110V、15Aまたは20A）の設置された専用の回路からとってください。

【全収納タイプ】LED照明


| ※ 3キャビネット本体開口 | ※ 1キャビネット外<br>（コード有効長さ） |     |     | コード取出位置 |      |
|---------------|-------------------------|-----|-----|---------|------|
| W             | A                       | B   | C   | D       | E    |
| 750           | 1400                    | 950 | 800 | 150     | 1110 |
| 900           | 1400                    | 900 | 800 | 225     | 1110 |
| 1000          | 1250                    | 750 | 700 | 225     | 1110 |
| 1200          | 1150                    | 650 | 700 | 225     | 1110 |

【全収納タイプ】スタンダードLED

| ※ 3キャビネット本体開口 | ※ 1キャビネット外<br>（コード有効長さ） |     |     | コード取出位置 |      |
|---------------|-------------------------|-----|-----|---------|------|
| W             | A                       | B   | C   | D       | E    |
| 750           | 1400                    | 950 | 800 | 150     | 1110 |
| 900           | 1400                    | 900 | 800 | 225     | 1110 |
| 1000          | 1350                    | 850 | 800 | 225     | 1110 |
| 1200          | 1250                    | 750 | 800 | 225     | 1110 |

【スマートポケット付き全収納タイプ】LED照明

| ※ 3キャビネット本体開口 | ※ 1キャビネット外<br>（コード有効長さ） |     |     | コード取出位置 |      |
|---------------|-------------------------|-----|-----|---------|------|
| W             | A                       | B   | C   | D       | E    |
| 750           | 1400                    | 950 | 900 | 150     | 1210 |
| 900           | 1400                    | 900 | 900 | 225     | 1210 |
| 1000          | 1350                    | 850 | 900 | 225     | 1210 |
| 1200          | 1250                    | 750 | 900 | 225     | 1210 |

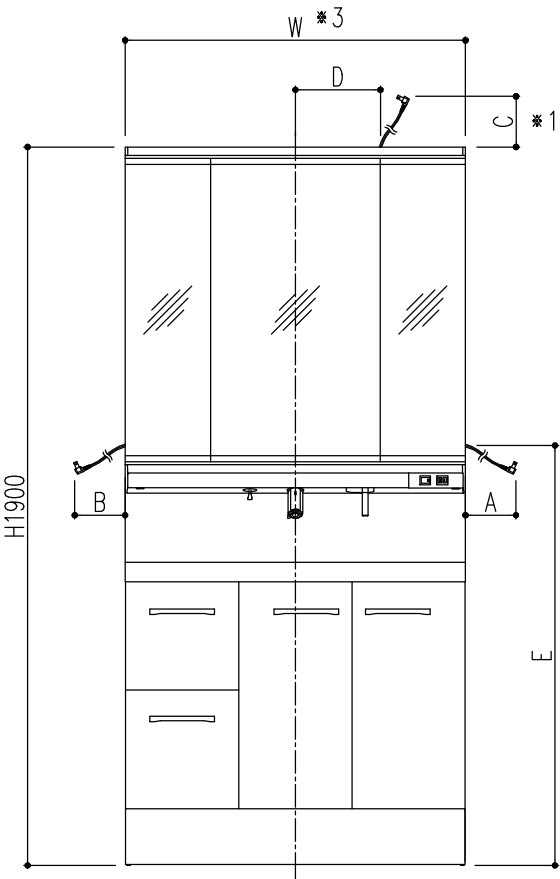

特記事項

取り付けに関わる情報は機能図に記載しています。  
必ず機能図を出力の上ご確認ください。  
詳細仕様の確認は、単品図をご参照ください。

物件名

小林大樹 様邸

仕様

EVノ奥行500タイプノ23モデルノフルスライドタイプノシングルレバーシャワー水栓  
LED照明（スリムLED）ノ3面鏡（全収納）

案件No.

A2511DDD0EXLYQ

図面名

機能図

担当

栗野 友仁

図面

図番

：

見積No.

M25119238165-007-4

縮尺

日付

2026.02.27

株式会社 LIXIL