
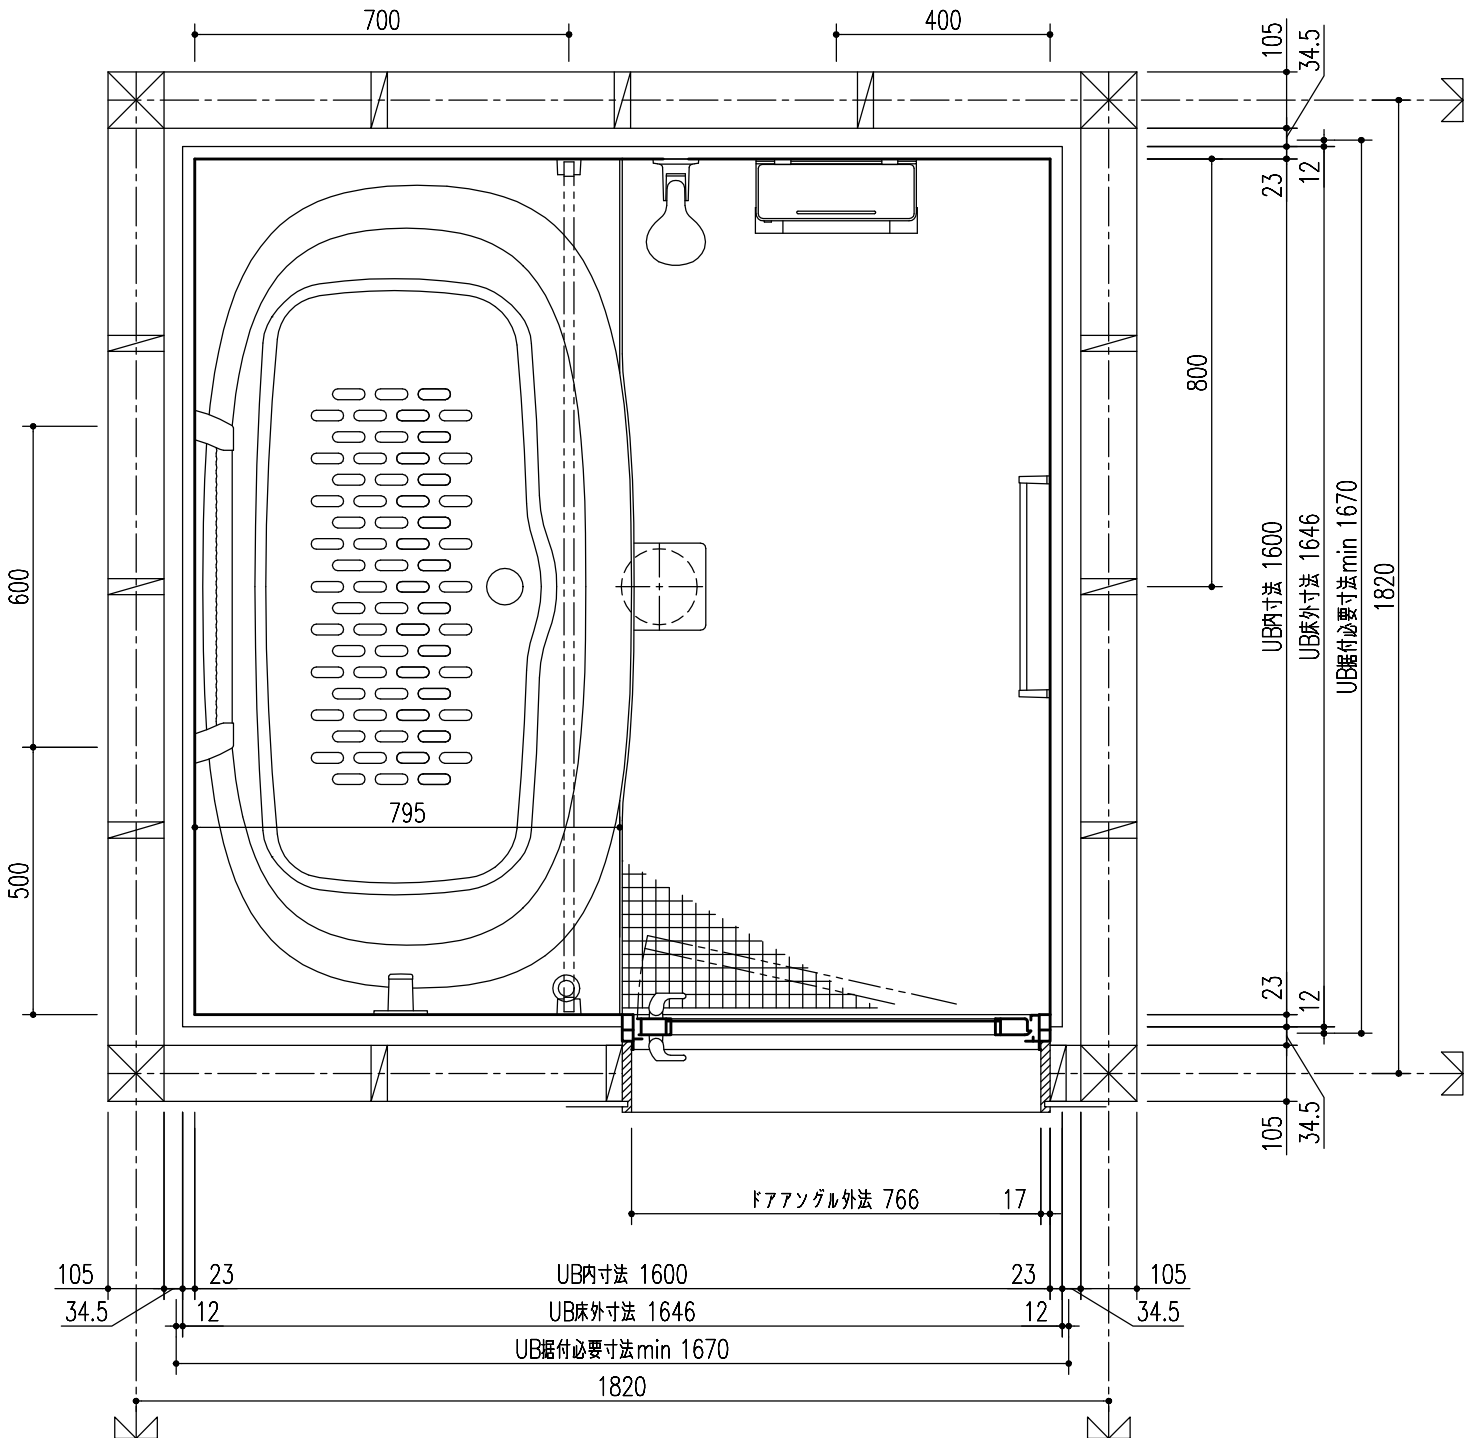
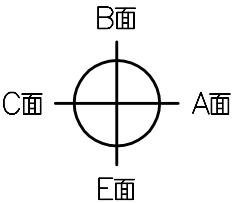


BMUS-1616LBZ-B


部位／項目	仕様（寸法単位：mm）	備考（色柄・品番等）	壁穴加工
床	FRP 単色 バックりんボイ排水口	N86	
壁	アクセントパネル（器具面）：Lパネル（ハイクラス） ベースパネル：Lパネル（ベーシッククラス）	HN987,LE301	
天井	化粧鋼板複合パネル	UE103	
ドア	開き戸：アルミアルマイト処理（キレイドア） 面 材：型板調樹脂板 ハンドル：プッシュプル	UDY-8002006UR(29)/WM-P2-WM	
浴槽	FRP ミナモ浴槽（浴槽内法 1501W×802D×480H） プッシュフソウェイ排水栓（メタル調） サーモバスS（浴槽保温材・薄型保温2枚組蓋＜ホワイト＞） マグネット組蓋フック＜ホワイト＞ エプロン＜ホワイト＞	NW1	
水栓金具	洗い場側：壁付サーモ水栓（LS）＜ホワイト＞ シャワー：スイッチ付エコアクアシャワー＜メタル調－ホワイト＞ メタル調ホース	BF-BD147TX-J12PU/FW1. A-10315-PU BF-SL6MBGE(1.7)-PU/FW1	
シャワーフック	マグネットシャワーフック（角度調節式）＜ホワイト＞1個	SWH(4)/FW1	
シャワーホースフック	マグネットシャワーホースホルダー＜グレー＞	SHH-4/N55	
照明	パネルダウンライト（防湿型） 電球色LED 2灯	LE-D1-10A(1.3M)/1L	
タオル掛	アルミパイプ L400 ブラケット：樹脂製	TB-400E-K	現場開口
鏡	防湿型化粧鏡 300W×600H	KGM-3060(1)S	
収納	マグネットシェルフ 300W＜ホワイト＞ ※強度上、ポンプボトルのポンプを棚上で押さないでください。	NT-300A(2)-1S/FW1	
換気扇	100V 換気乾燥暖房機 浴室外リモコン付 アルミダクトホース付	UFD-112A	
ランドリーパイプ	ステンレス製＜ホワイト＞ 1本セット	LAP-1582-W（×1本）	現場開口
給水管	PJ1/2 おねじ止		
給湯管	PJ1/2 おねじ止		
雑排水管	塩ビ管 VU50		
追いだき	浴槽穴加工φ50 水受けトレイ付		
保温仕様	洗い場床防水バン保温 床気密材セット トラップ保温 エプロン保温		
握りバー	型（ホワイト）L600 1本	8928-BTYPE-L600/W	現場開口

天井見上げ図

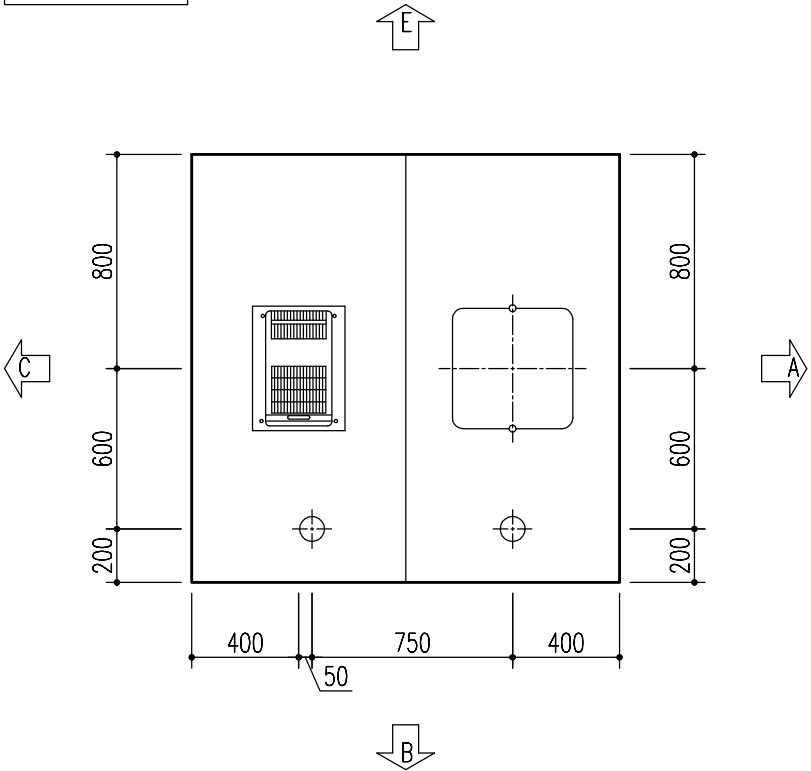

- ※ UB据付必要寸法はドア部の寸法を含みません。ドア部の寸法は詳細図のドア取合をご確認ください。
- ※ 取付けの機器により、UB据付必要寸法は異なります。
詳しくは、カタログの「工務店さまへ（取付け前の確認事項）」をご確認ください。
- ※ プラスオプションの追加マグネットアイテムは仕様図には表示されません。

特記事項	受領印	物件名	図面	担当	検図	図番
		小林大樹 様邸		栗野 友仁		日付 2026.02.27
		仕様図 BMUS-1616LBZ-B+H,RL	縮尺	株式会社 LIXIL		

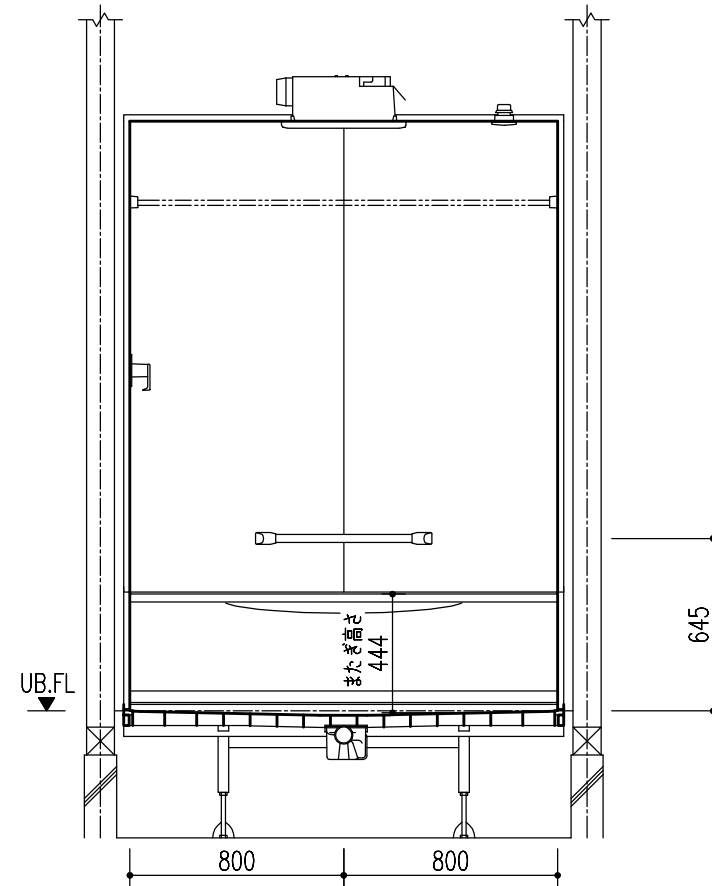

特記事項	受領印	物件名	図面	担当	検図	図番
		小林大樹 様邸		薬野 友仁		
		品名	縮尺	株式会社 LIXIL		
		仕様図 BMUS-1616LBZ-B+H,RL				
						日付 2026.02.27

配管接続部詳細図


配管の接続をスムーズに行うためにユニットバス取付前に下記の準備をお願いします。

(1)給水、給湯、排水の一次側は所定の位置に立ち上げておいてください。


(2)排水を脱衣室側(ドア下等)へ抜く場合は、基礎部に開口を設けるか、束構造にして排水管を抜いてください。

シャワーの種類により水栓金具の入口での必要給湯圧力が異なります。詳細はカタログを確認してください。

給水給湯配管立上げ位置 点検口止め

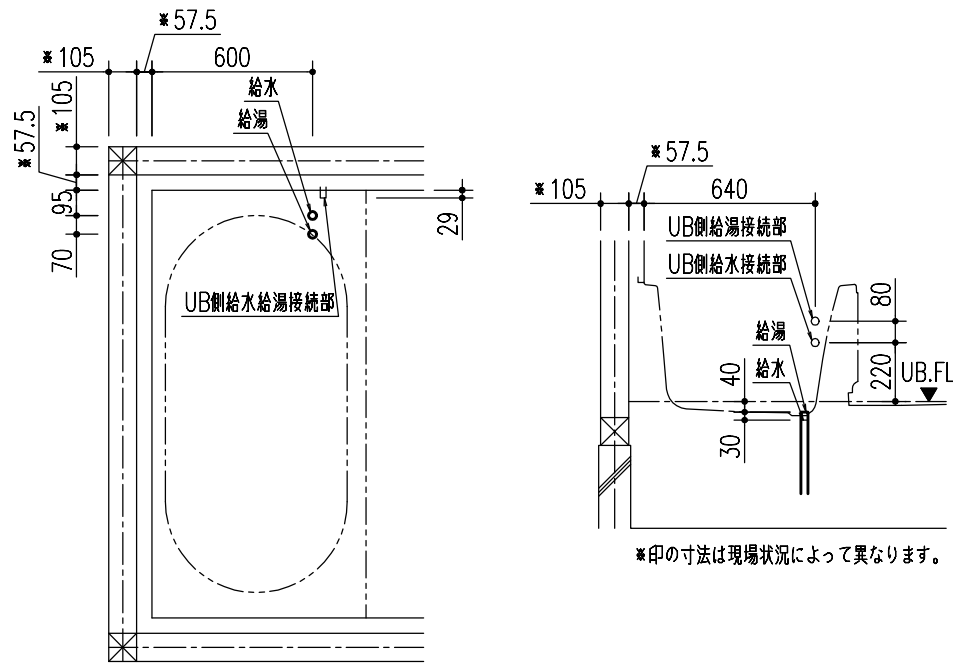

追いだき配管立上位置図

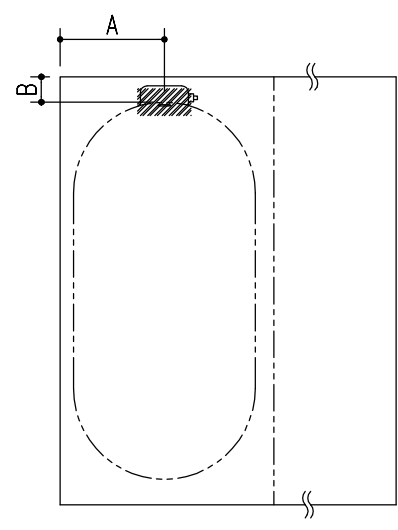


浴槽	A	B	H
ミナモトイド浴槽	506	231	113
1600フイド浴槽	589	247	113
1600ミナモ浴槽	374	231	113
1600エコベンチ浴槽	389	456	103
1600ストレートライン浴槽	369	252	113
1600ロング浴槽	355	194	113
1300ミナモ浴槽	384	132	113
1300ストレートライン浴槽	369	160	113
1200ミナモ浴槽	387	130	113
1150ミナモ浴槽	387	130	113

※図はR勝手の場合です。L勝手の場合は左右反転になります。

※追いだき循環アダプターは現場手配になります。



雑排水管

浴槽側の配管持出し位置・排水管立上位置は専用の配管キット(オプション)を使用した場合の位置です。

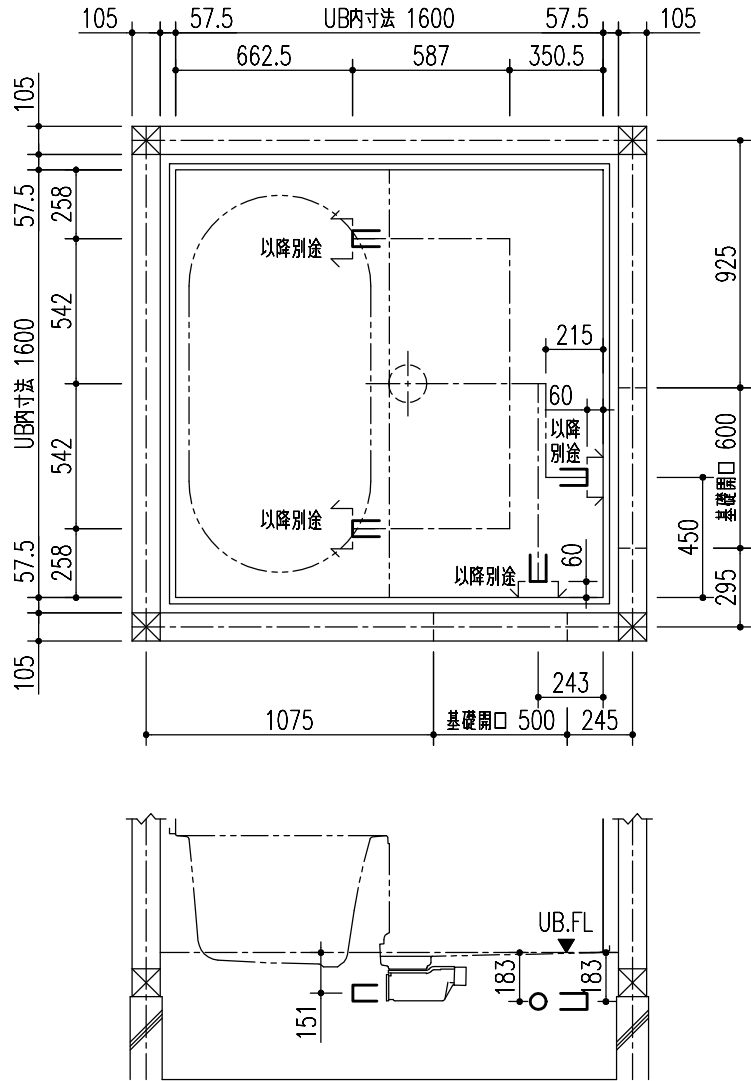


標準持出し位置

給水給湯接続部

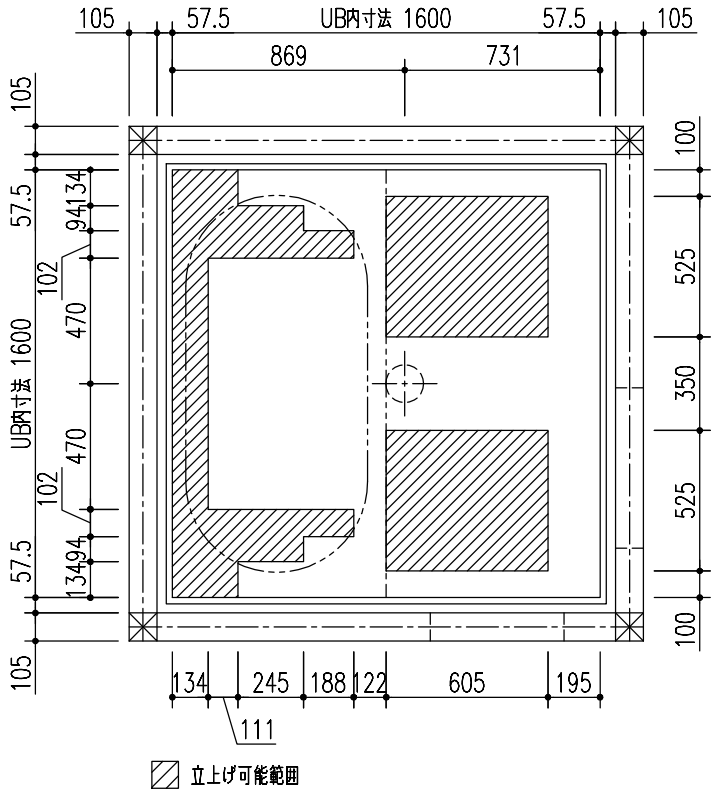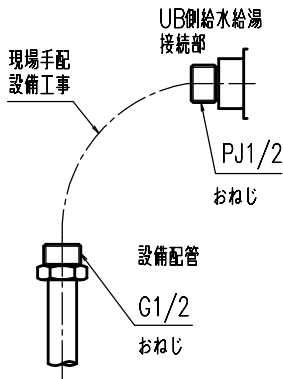

立上げ推奨位置


床支持位置

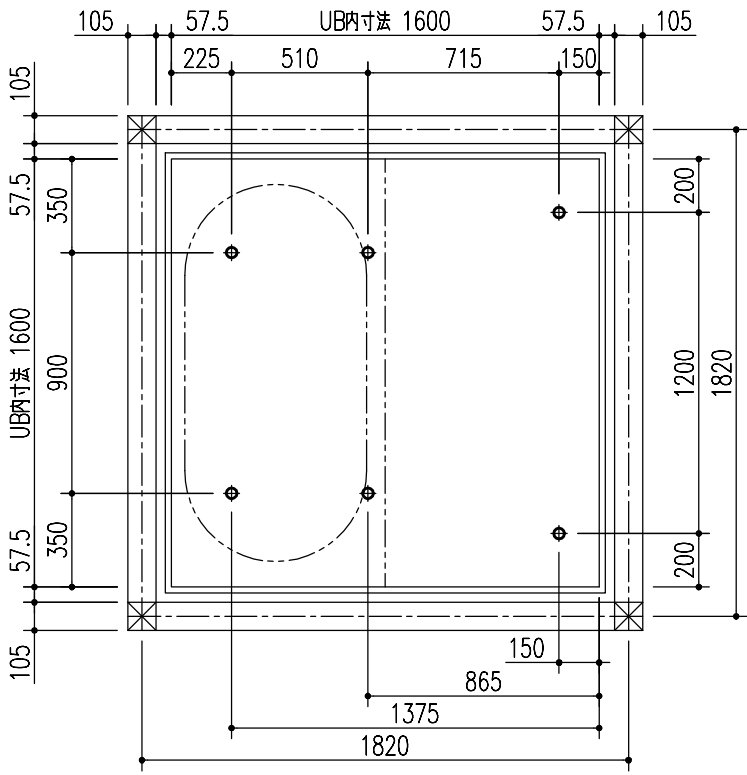

特記事項	受領印	物件名	図面	担当	検図	図番
		小林大樹 様邸		栗野 友仁		日付 2026.02.27
		詳細図	縮尺	株式会社 LIXIL		
		BMUS-1616LBZ-B+H,RL				
		名				


ドア取合

有効幅員:683mm

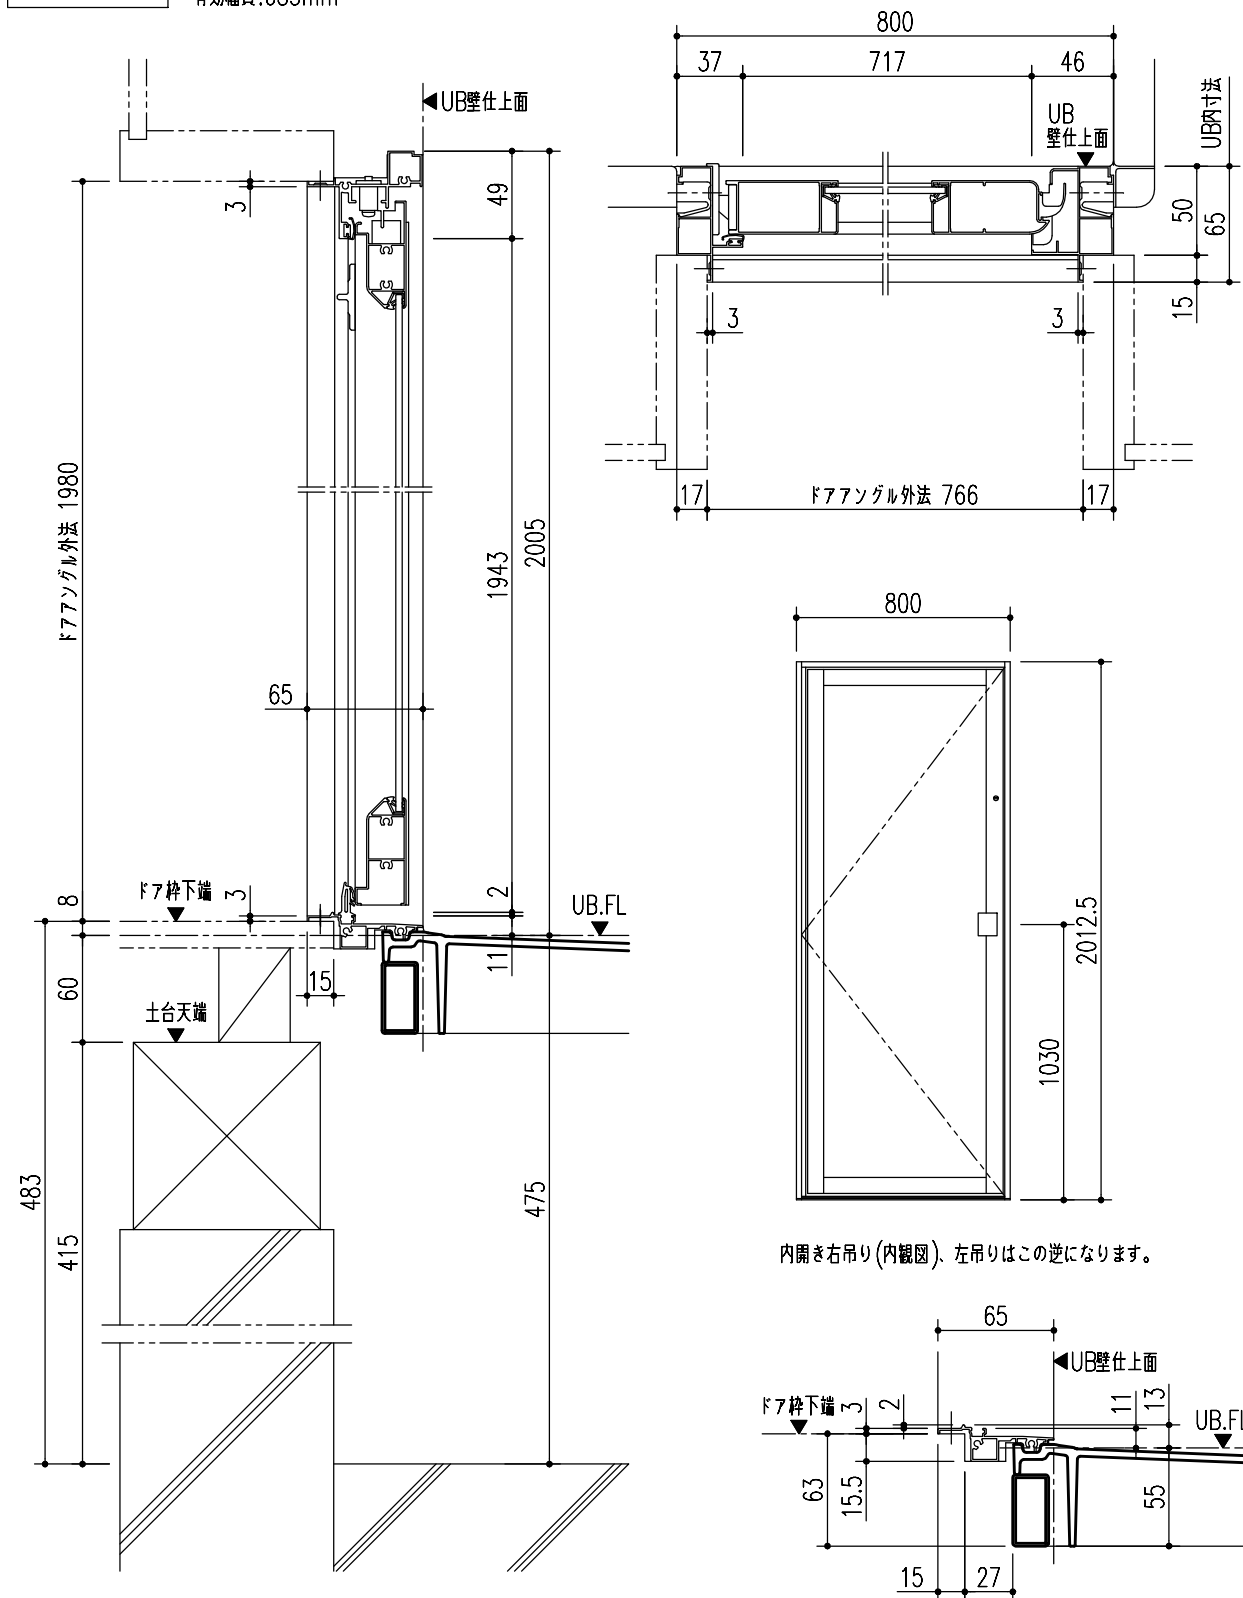

ドア横の管柱、間柱について

ドアが管柱、固柱にあたらないように十分考慮してください。
寸法はユニットサイズやドア位置ずらし、固柱切りユニットの有無
によって異なる場合があります。仕様図でご確認ください。

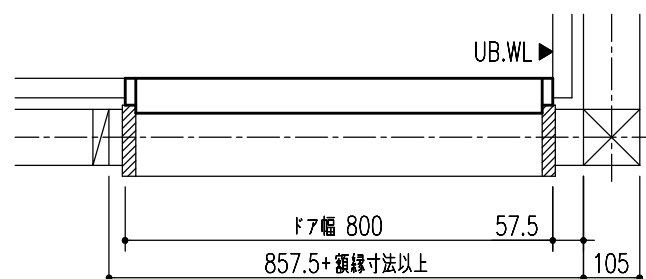


窓開口位置


現場の状況や窓により窓開口位置を設定する場合、以下の範囲で決めてください。

- ※ 壁幅いっぱい大きさの窓の場合は、パネル左右のスペースを0としてください。
- ※ () 内の寸法とする場合は、壁パネルの強度上、柱木等を使用し補強を行ってください。


＜1枚のパネルに納まる場合＞

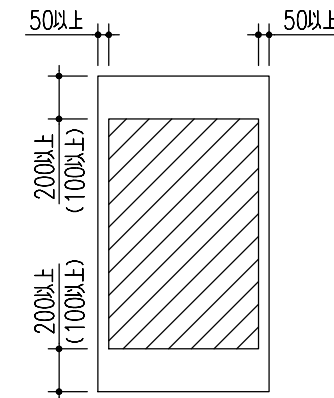 開口可能範圍

＜2枚のパネルにまたがる場合＞


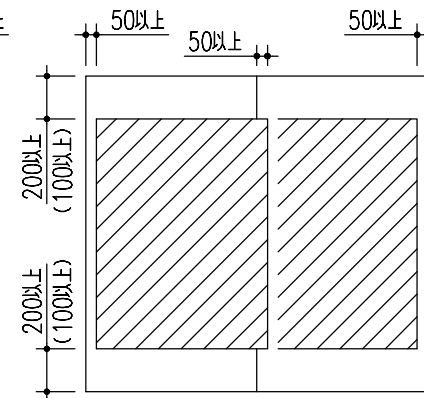


＜器具とのクリアランス＞

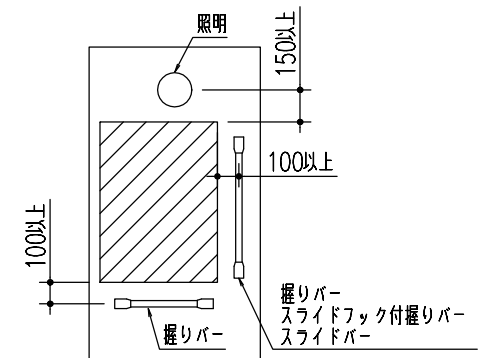

特記事項	受領印	物 件 名	図面	担当	検図	図 番
		小林大樹 様邸		栗野 友仁		日付 2026.02.27
		品	縮尺	株式会社 LIXIL		
		詳細図 BMUS-1616LBZ-B+H,RL				
		名				

照明

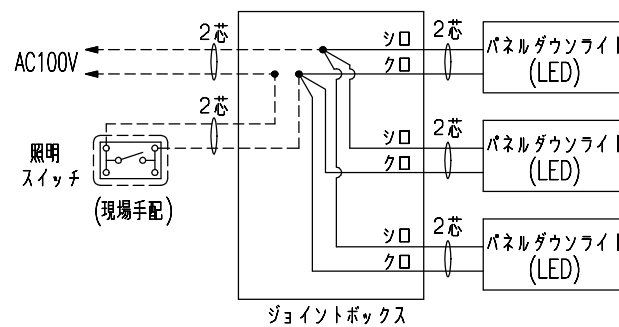
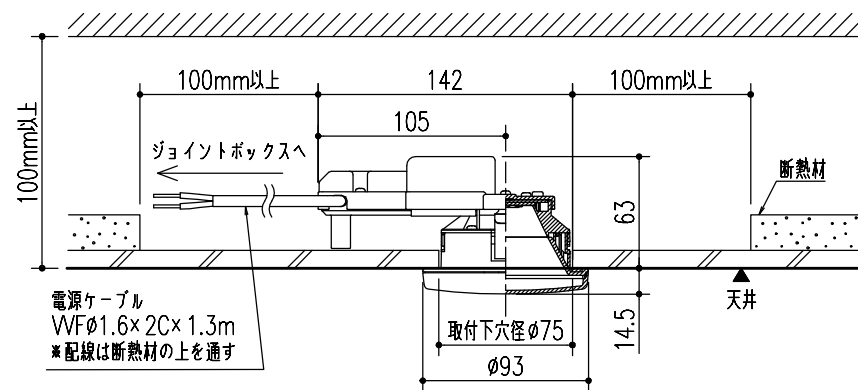


※浴室サイズ等により照明の数は異なります。

- 結線箇所(電気工事)
- ――配線(現場手配・電気工事)

換氣乾燥暖房機

UFD-112A • UFD-112PWA

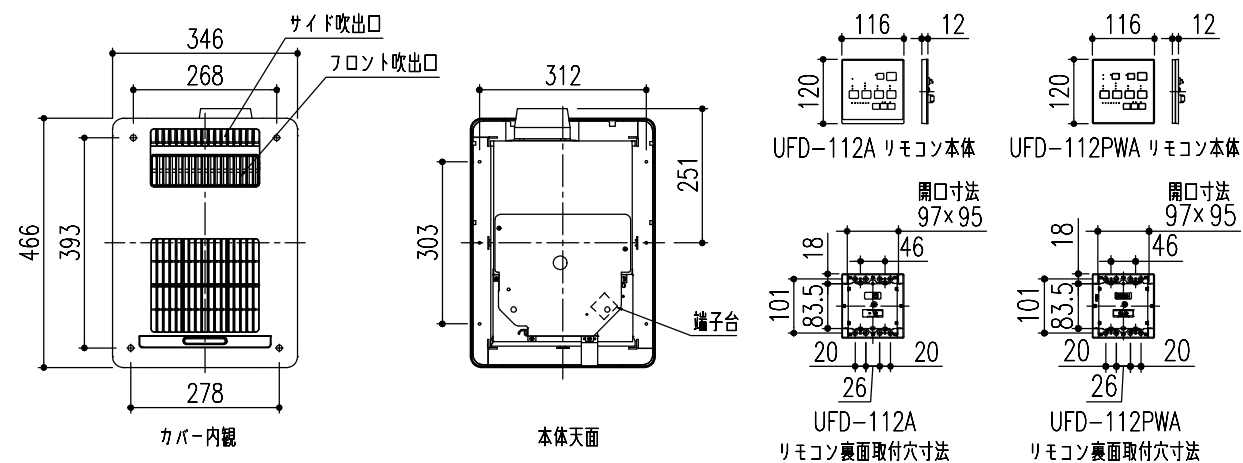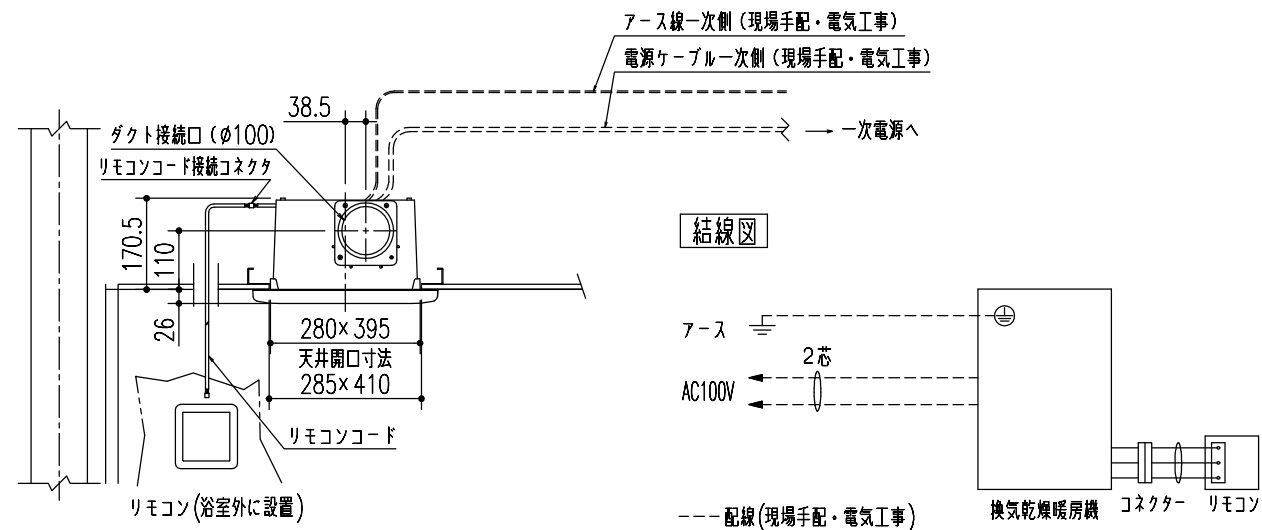

- 注1) 電源ケーブル・アース線は付属していません。電気工事において一次側の電源ケーブル・アース線を端子台に接続してください。
- 注2) 一次側電源線・アース線との結線工事、それ以降の配線工事、リモコン取付・接続工事は電気工事業者さまの作業範囲となります。
- 注3) 一次電源側に漏電遮断器を必ず設置してください。アース工事はD種接地工事を行ってください。
- 注4) 最大消費電力は1250W、運転電流は12.5Aです。また、運転初期に突入電流が発生しますので、暖房機単独でAC100V、20Aの専用回路に接続してください。
- また、配線の途中にスイッチを設けないでください。
- 注5) 大きな窓がある場合、室温が上昇しにくいことがあります。
- 注6) 標準ではランドリーパイプは1本となります。2本にした場合は乾燥時間に差が出る場合があります。
- 注7) 排気方向は180°回転可能です。その際、本体とフロントパネルを180°回転させて取り付けます。
- 注8) 点検口との間に中間梁などの障害物がある場合はスペース確保にご注意ください。
- 注9) 1616サイズよりも大きなサイズでは、使用条件(地域、断熱材の有無、窓など)による影響を受けにくくするため、暖房能力に余裕のあるUFD-212シリーズをおすすめします。


警告

- 電気工事は電気設備技術基準、内線規程など関連する法令・規程にしたがって、必ず「電気工事士」が行ってください。
- 電線相互の接続は銅線用圧着管スリーブを用いる等確実に工事してください。絶対に「手より」接続しないでください。
※電気工事が不適切な場合、火災や漏電の恐れがあります。
- 電源線など各配線に、以下のことをしないでください。 ※火災、漏電や故障の恐れがあります。
 - 傷つける、無理に曲げる、無理な力を加える、束ねる、重いものを載せる、挟み込む
- 一次側に必ず漏電遮断器を設置してください。 ※感電する恐れがあります。

特記事項	受領印	物 件 名 品 名	図面	担当	検図	図 番
		小林大樹 様邸		栗野 友仁		日付 2026.02.27
		詳細図 BMUS-1616LBZ-B+H,RL	縮尺	株式会社 LIXIL		

注意）配線図の  は電気工事による接続箇所を示します。搭載する電気機器は配線図中の  に  と記入し、また不要な電気機器は斜線で消してください。

< 電気工事範囲 >

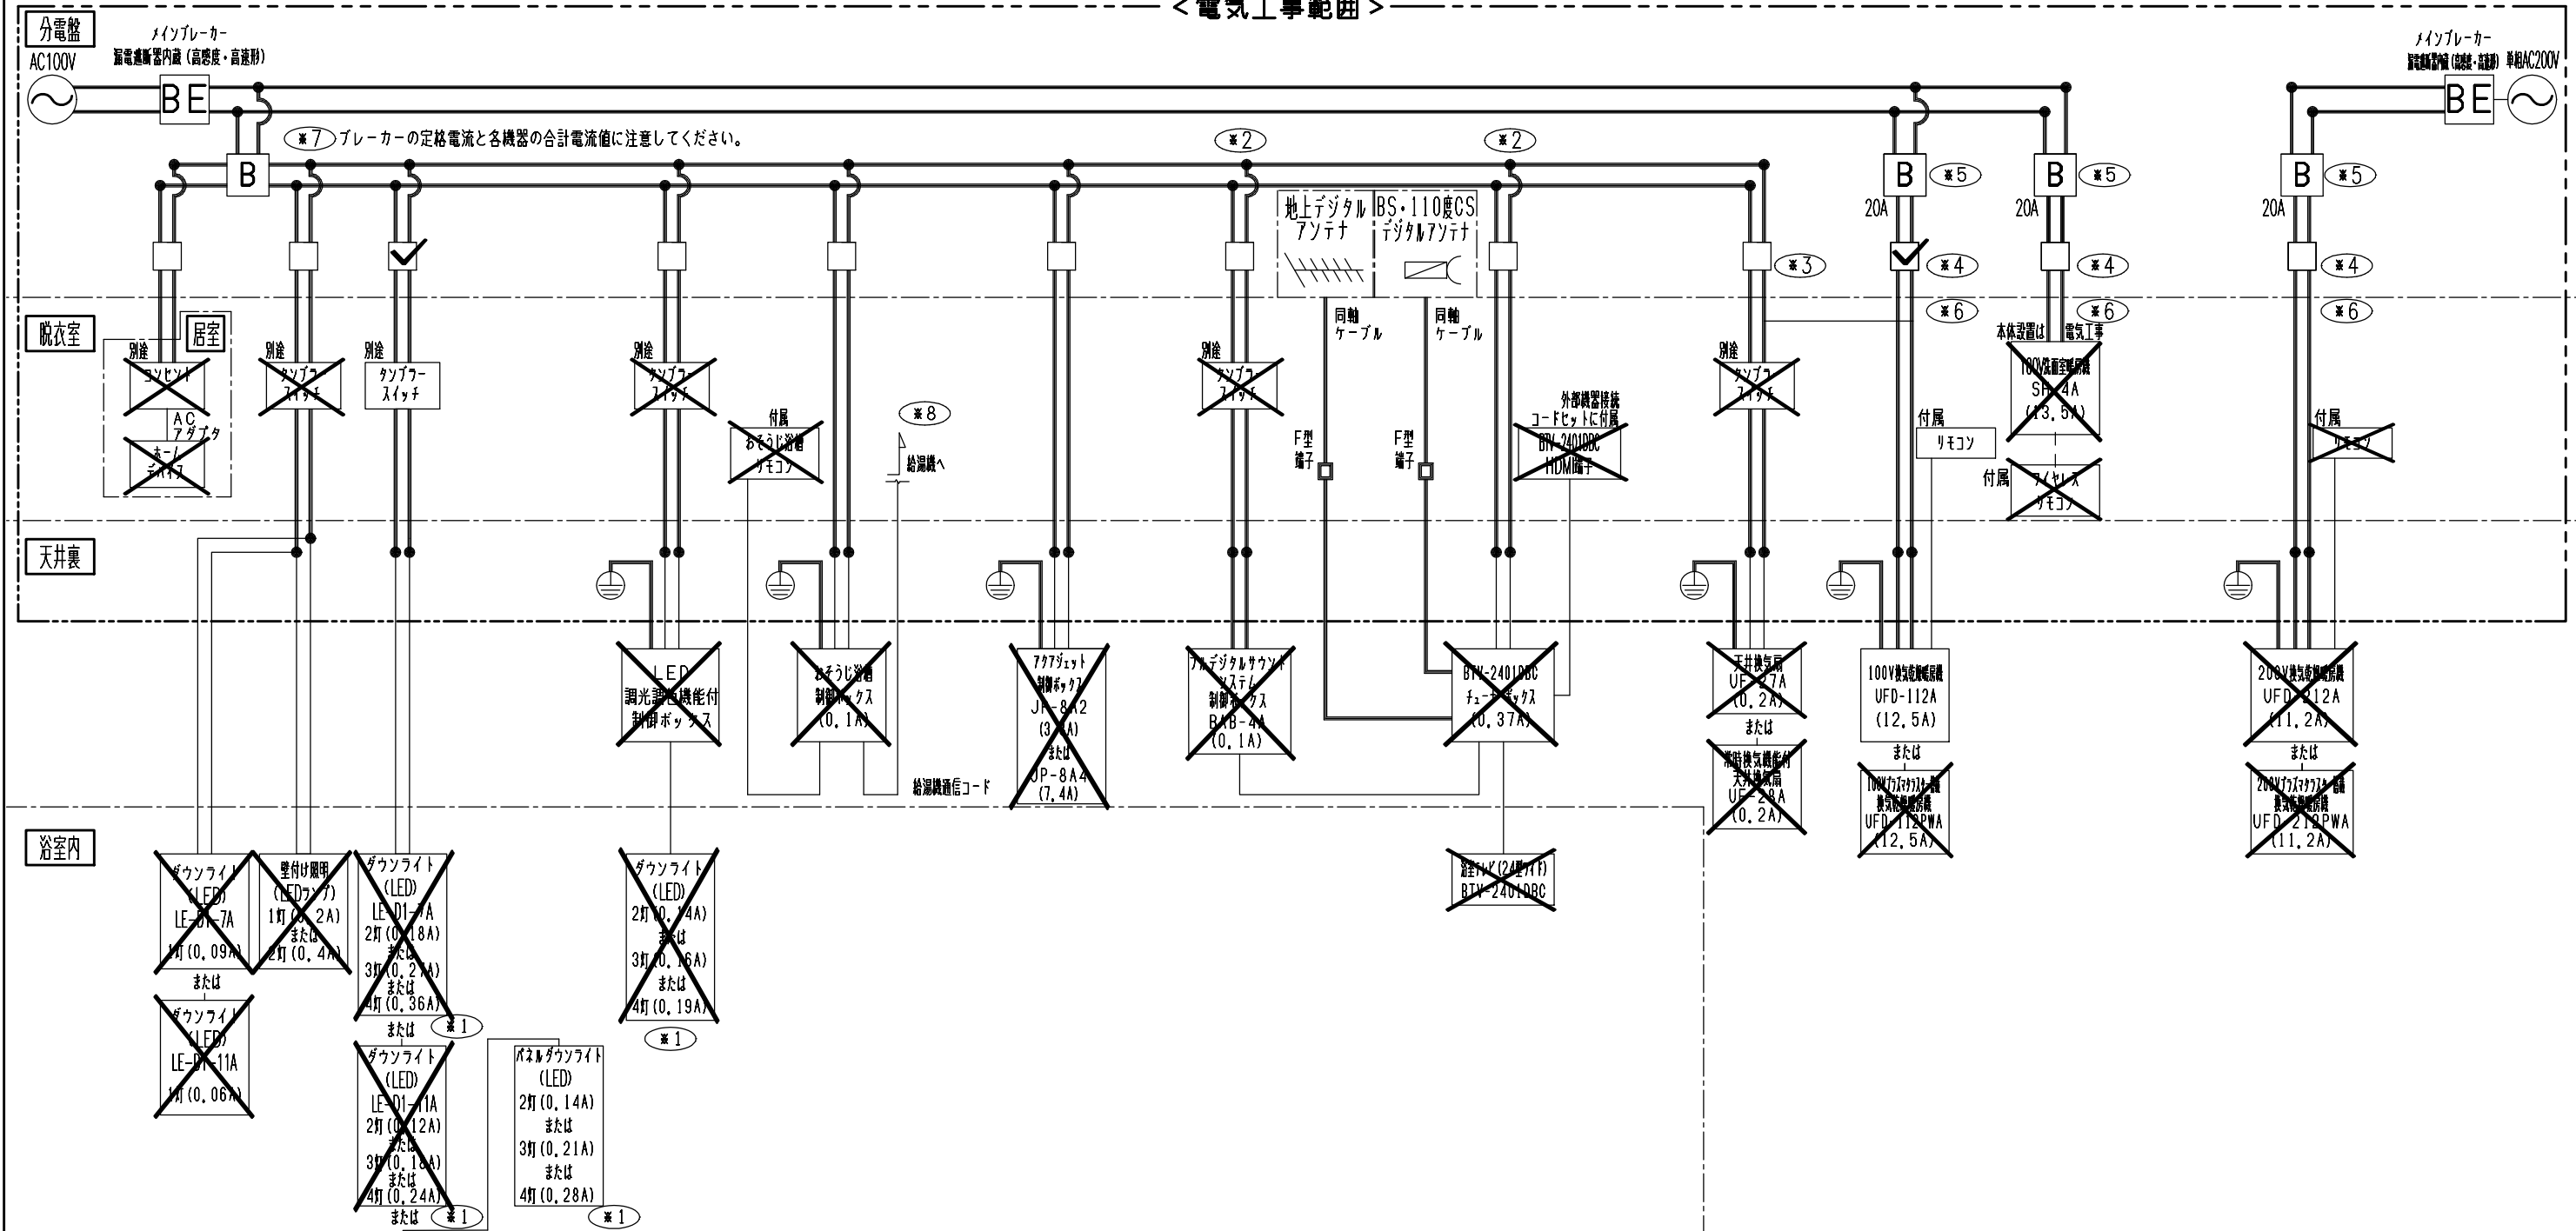

区分	照明	おそうじ浴槽	気泡浴槽	テレビ・サウンドシステム	換気設備	暖房設備・換気乾燥暖房機
----	----	--------	------	--------------	------	--------------

- ※1：選択されたユニットサイズ、タイプ、オプションによって灯数が異なります。
- ※2：化粧台など浴室以外の照明器具との配線を分けてください。
※照明のon/offによってフルデジタルサウンドシステムへノイズが乗る可能性があります。
- ※3：換気扇を単独で設置する（換気乾燥暖房機を設置しない）場合を示します。
- ※4：換気乾燥暖房機を設置する場合、※3の経路はありません。
- ※5：運転初期に突入電流が発生しますので、換気乾燥暖房機単独で20Aの専用回路としてください。
※電気工事が不適切な場合、火災や漏電の恐れがあります。
- ※6：専用の配線用遮断機から配線し、途中にスイッチを設けないでください。
※誤った配線工事は、火災や漏電、故障の恐れがあります。
- ※7：ブレーカーの定格電流と各機器の合計電流値に注意してください。
- ※8：給湯機器と連動する場合に必要となります。

※以下のものは、システムバス取付作業に含まれておりません
・電源線、アース線の一次側配線工事、D種接地工事、漏電遮断器の調達および設置工事。
・各電気機器の電源線およびアース線と一次側配線との接続工事。
・脱衣室に設置するスイッチ（別途の表記があるもの）の調達。
・脱衣室に設置するスイッチの配線接続および設置工事（別途、付属とも）。

⚠ 警告


- 電気工事は電気設備技術基準、内線規程など関連する法令・規程に従って、必ず電気工事士の資格を有する者が適切な方法で行ってください。 ※無資格者の工事や、電気工事士による不適切な工事は、火災や漏電を引き起こす恐れがあるほか、関係法令により処罰等されることがあります。
- 電線相互の接続は銅線用裸圧着スリーブや差込形コネクタを用いる等確実に工事してください。絶対に「手より」接続しないでください。
※電気工事が不適切な場合、火災や漏電の恐れがあります。
- アース工事が必要な電気機器はD種接地工事を施した接地線と確実に接続してください。
※漏電や故障の際に、感電する恐れがあります。
- 電源線など各配線に、以下のことをしないでください。
・傷つける、無理に曲げる、無理な力を加える、束ねる、重いものを載せる、挟み込む ※火災、漏電や故障の恐れがあります。
- 電源線、アース線やリモコンコード等の配線は、照明器具（ダウンライト等）や暖房機など熱器具から離して設置してください。
※器具の熱で配線が溶断し、火災や漏電の恐れがあります。
- 一次側に必ず漏電遮断器（高感度・高速形）を設置してください。 ※感電する恐れがあります。
- 一次側の電源線、アース線、スイッチ配線と電気機器配線の結線部は、必ずジョイントボックス内に収めてください。
システムバスルームに同梱されているジョイントボックスを使用してください。 ※ほこり等により火災の恐れがあります。

特記事項	受領印	物件名	図面	担当	検図	図番
各電気機器の詳細については各々のオプション詳細図を参照ください。		小林大樹 様邸		栗野 友仁		日付 2026.02.27
		電気機器配線図 BMUS-1616LBZ-B+H,RL	縮尺	株式会社 LIXIL		

排水管接続の注意点
浴槽排水時には最大約1.2L/sの流量が発生します。排水管の経路や、管内の状態によっては正しく排水されない場合があります。設計・取付の際は次の各項目を確認して下さい。

■ダブルトラップ
浴室以降の排水管経路上に、トラップが無いことを確認してください。（ダブルトラップの禁止）
ダブルトラップになっていると、「排水が流れない」「異臭がする（封水切れ）」などの異常につながります。
ダブルトラップは配管接続前に解消してください。
システムバスルーム設置後はダブルトラップの解除ができません。


【ダブルトラップの例】

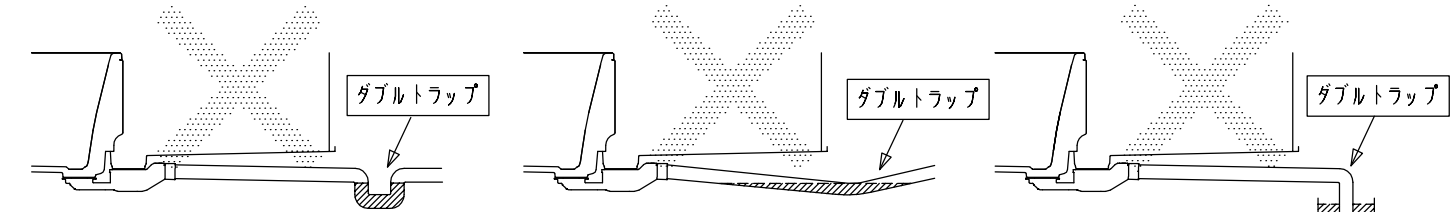

下に曲がった配管部分が、トラップになっている
横引き配管がたわみ、トラップになっている
配管の先が排水ます溜水内にあり、トラップになっている


■排水管内の詰まり
接続する排水管が、汚れなどで詰まっていないことを確認してください。
配管が細かったり、配管内が汚れ等で詰まっていると、「排水が流れない」「洗い場排水口から浴槽排水が溢れてくる」といった異常につながります。
汚れが付着して詰まっている場合、配管を接続する前に洗浄し汚れを取り除いてください。

【悪い例】

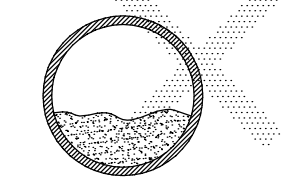

配管内に汚れなどの詰まりがある



【良い例】

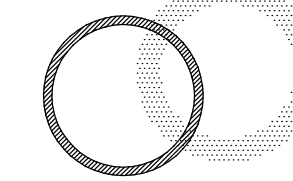

配管内に汚れなどの詰まりは取り除く

■排水管経路
排水管の経路によっては、排水異常となる場合があります。
次の事項にご注意のうえ設備業者さまと十分な事前打合せをお願い致します。


- ① システムバスルーム以降で排水管を縦方向に落とす場合
通気を設けるか、配管径を拡張、もしくは90°曲げ部に大曲リエルボ（LL）を使用する事をおすすめします。

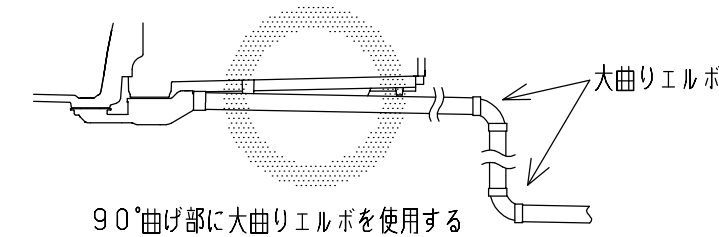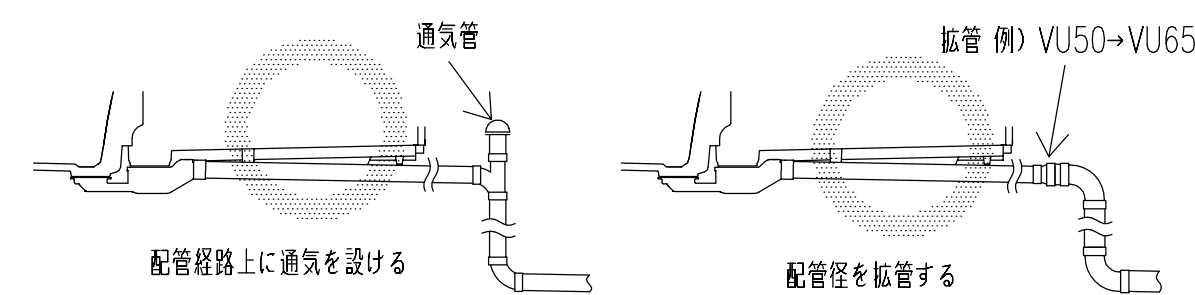

90°曲げ部に大曲リエルボを使用する



※浴槽排水時に排水口から「ゴボゴボ」と音が発生することがありますが、異常ではありません。

- ② システムバスルーム以降の横引き配管について
90°曲げ部に大曲リエルボ（LL）を使用するか、システムバスルームに近い位置で配管径を拡張する事をおすすめします。


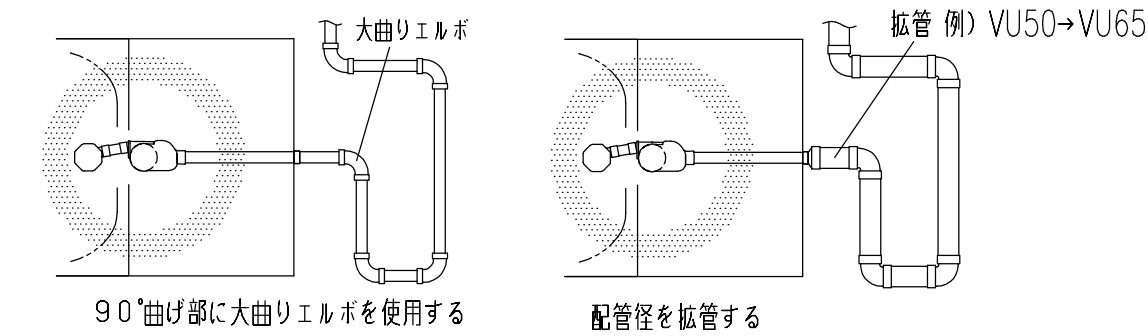


- ③ システムバスルーム床下の排水管経路について



- トラップ出口には同梱の継口配管を接続してください
 - 継口配管を使用しない場合
 - ・大曲リエルボを使用してください
 - ・1620-2サイズの場合、トラップ出口に接続する配管には、必ず切断長さ250mm以上の横引き経路を設けてください
- ※洗い場パントの干渉回避や浴槽排水の流れを妨げないため

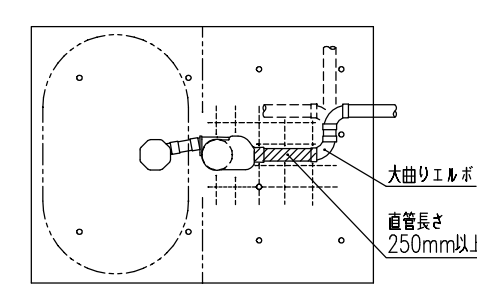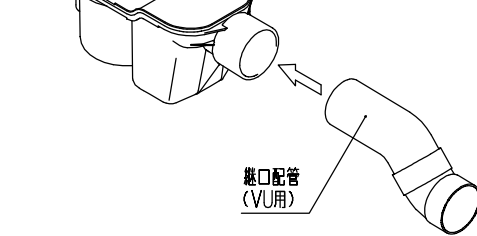




【排水管経路の悪い例】
十分な長さの横引き配管を設けずに曲げを繰り返したり、縦方向に落としている

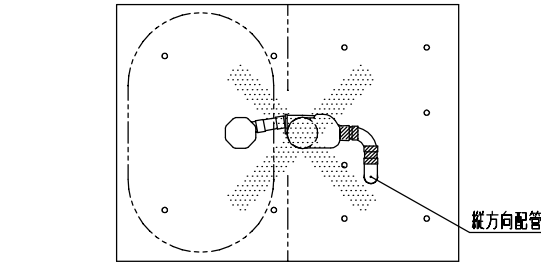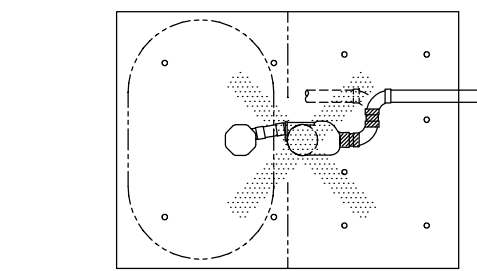

【排水管経路の良い例】
トラップから2曲がりまでの間に十分な長さの横引き経路を設けている

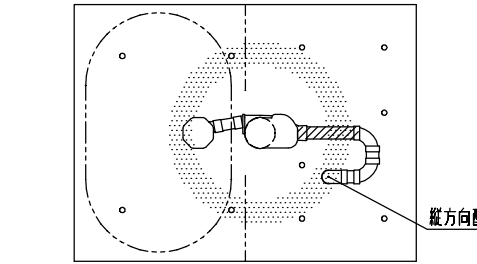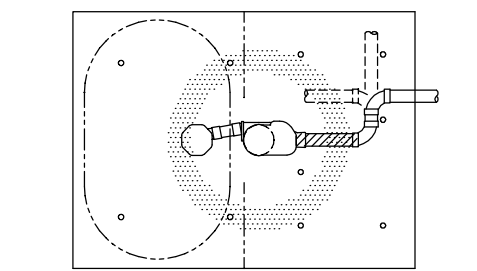

特記事項	受領印	物件名	図面	担当	検図	図番
		品名				日付
		排水管経路条件図	縮尺	株式会社 LIXIL		
		AX				

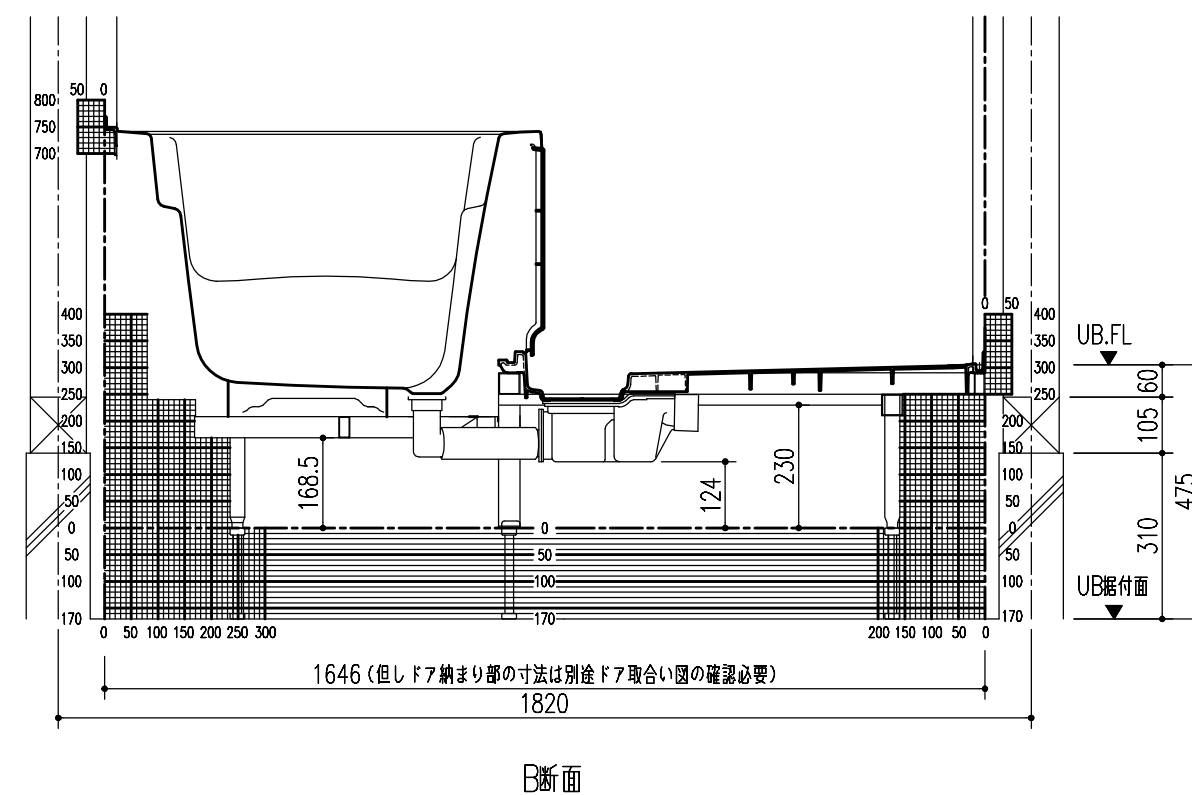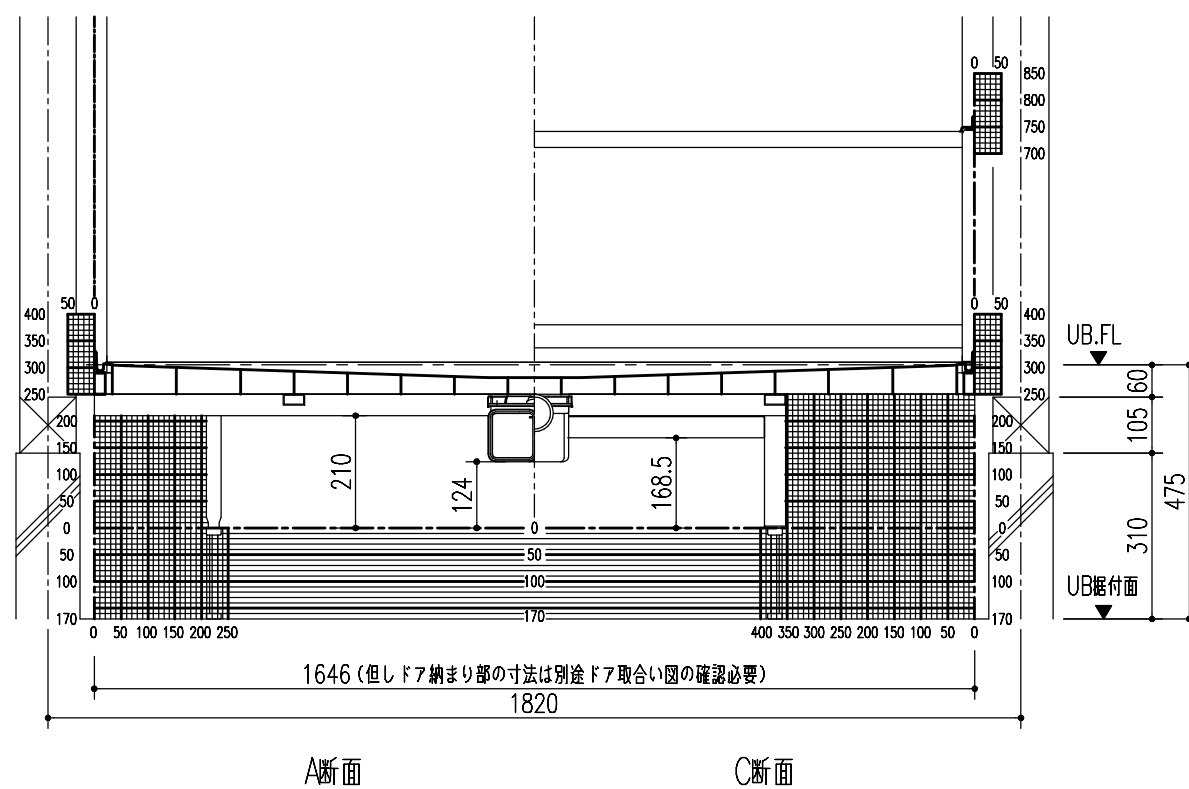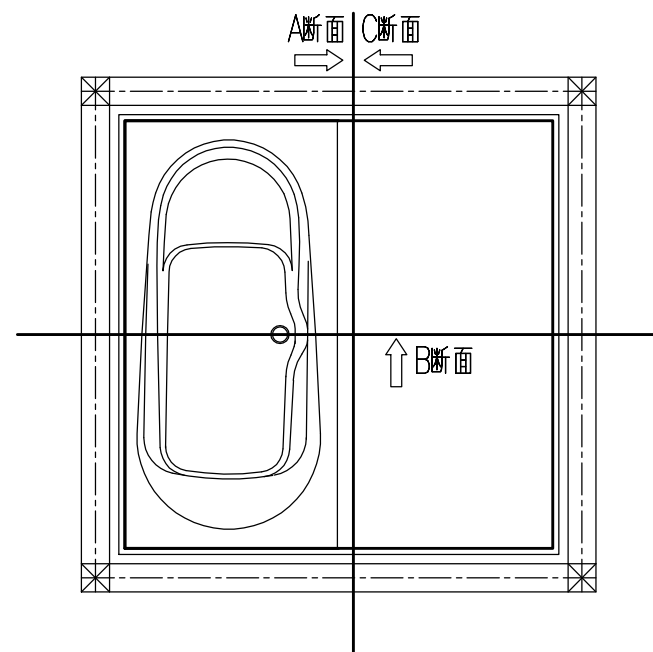

※ 本図はRタイプを示します。Lタイプは本図を左右反転したものになります。

特記事項	受領印	物	図面	担当	検図	図	
		件				番	
		名				日付	
		品	床下納まり	縮尺	株式会社 LIXIL		
			AX				
		名	1616サイズ(浴槽パンなし・ボルト脚仕様H475)				