


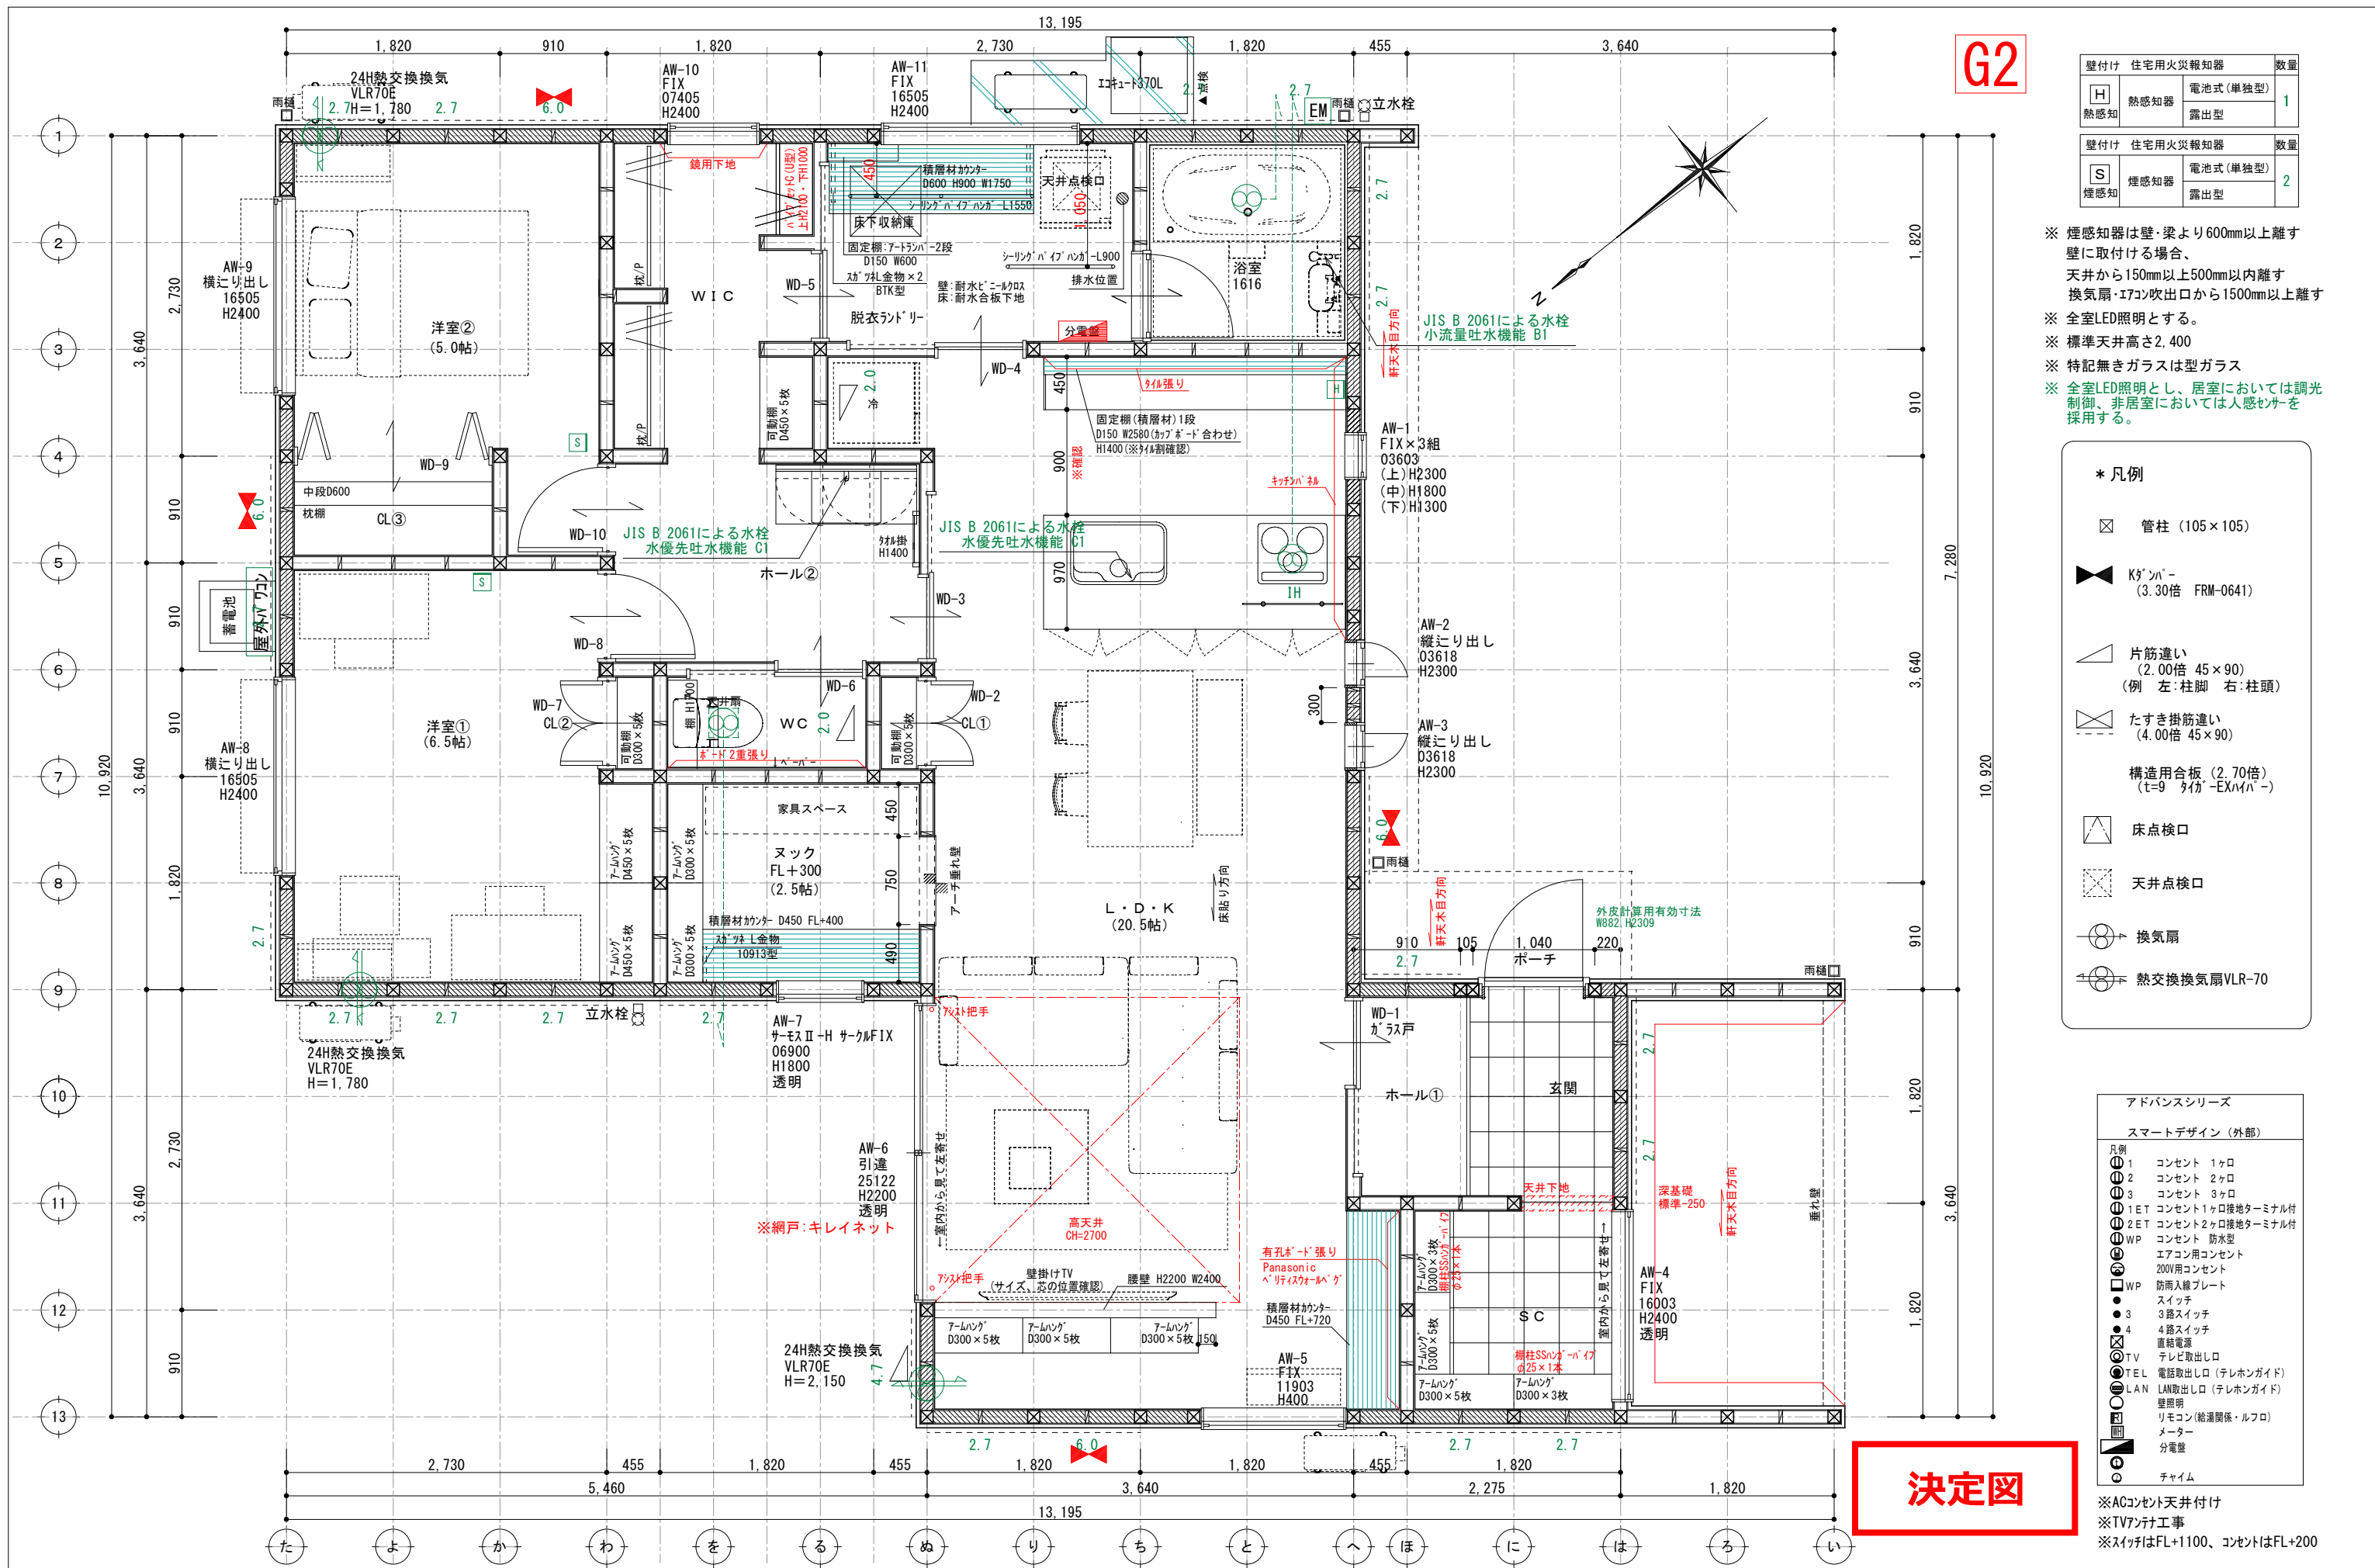

壁付け 住宅用火災報知器			数量
H	熱感知器	電池式(単独型)	1
	熱感知	露出型	
壁付け 住宅用火災報知器			数量
S	煙感知器	電池式(単独型)	2
	煙感知	露出型	

※ 煙感知器は壁・梁より600mm以上離す
壁に取付ける場合、
天井から150mm以上500mm以内離す
換気扇・エアコン吹出口から1500mm以上離す
※ 全室LED照明とする。
※ 標準天井高さ2,400
※ 特記無きガラスは型ガラス
※ 全室LED照明とし、居室においては調光
制御、非居室においては人感センサーを
採用する。

* 凡例	
	管柱 (105×105)
	K's Pan (3.30倍 FRM-0641)
	片筋違い (2.00倍 45×90) (例 左:柱脚 右:柱頭)
	たすき掛筋違い (4.00倍 45×90)
	構造用合板 (2.70倍) (t=9 2枚-EXハイパー)
	床点検口
	天井点検口
	換気扇
	熱交換換気扇VLR-70

アドバンスシリーズ	
スマートデザイン (外部)	
凡例	1 コンセント 1ヶロ
2	コンセント 2ヶロ
3	コンセント 3ヶロ
1ET	コンセント1ヶロ接地ターミナル付
2ET	コンセント2ヶロ接地ターミナル付
WP	コンセント 防水型
	エアコン用コンセント
	200V用コンセント
WP	防雨入線プレート
	スイッチ
●	3路スイッチ
●	4路スイッチ
●	直結電源
●	テレビ取出口
●	TEL 電話取出口 (テレホンガイド)
●	LAN 取出口 (テレホンガイド)
●	壁照明
●	リモコン (給湯関係・ルフロ)
●	メーター
●	分電盤
●	チャイム

※ACコンセント天井付け
※TVアンテナ工事
※スイッチはFL+1100、コンセントはFL+200