


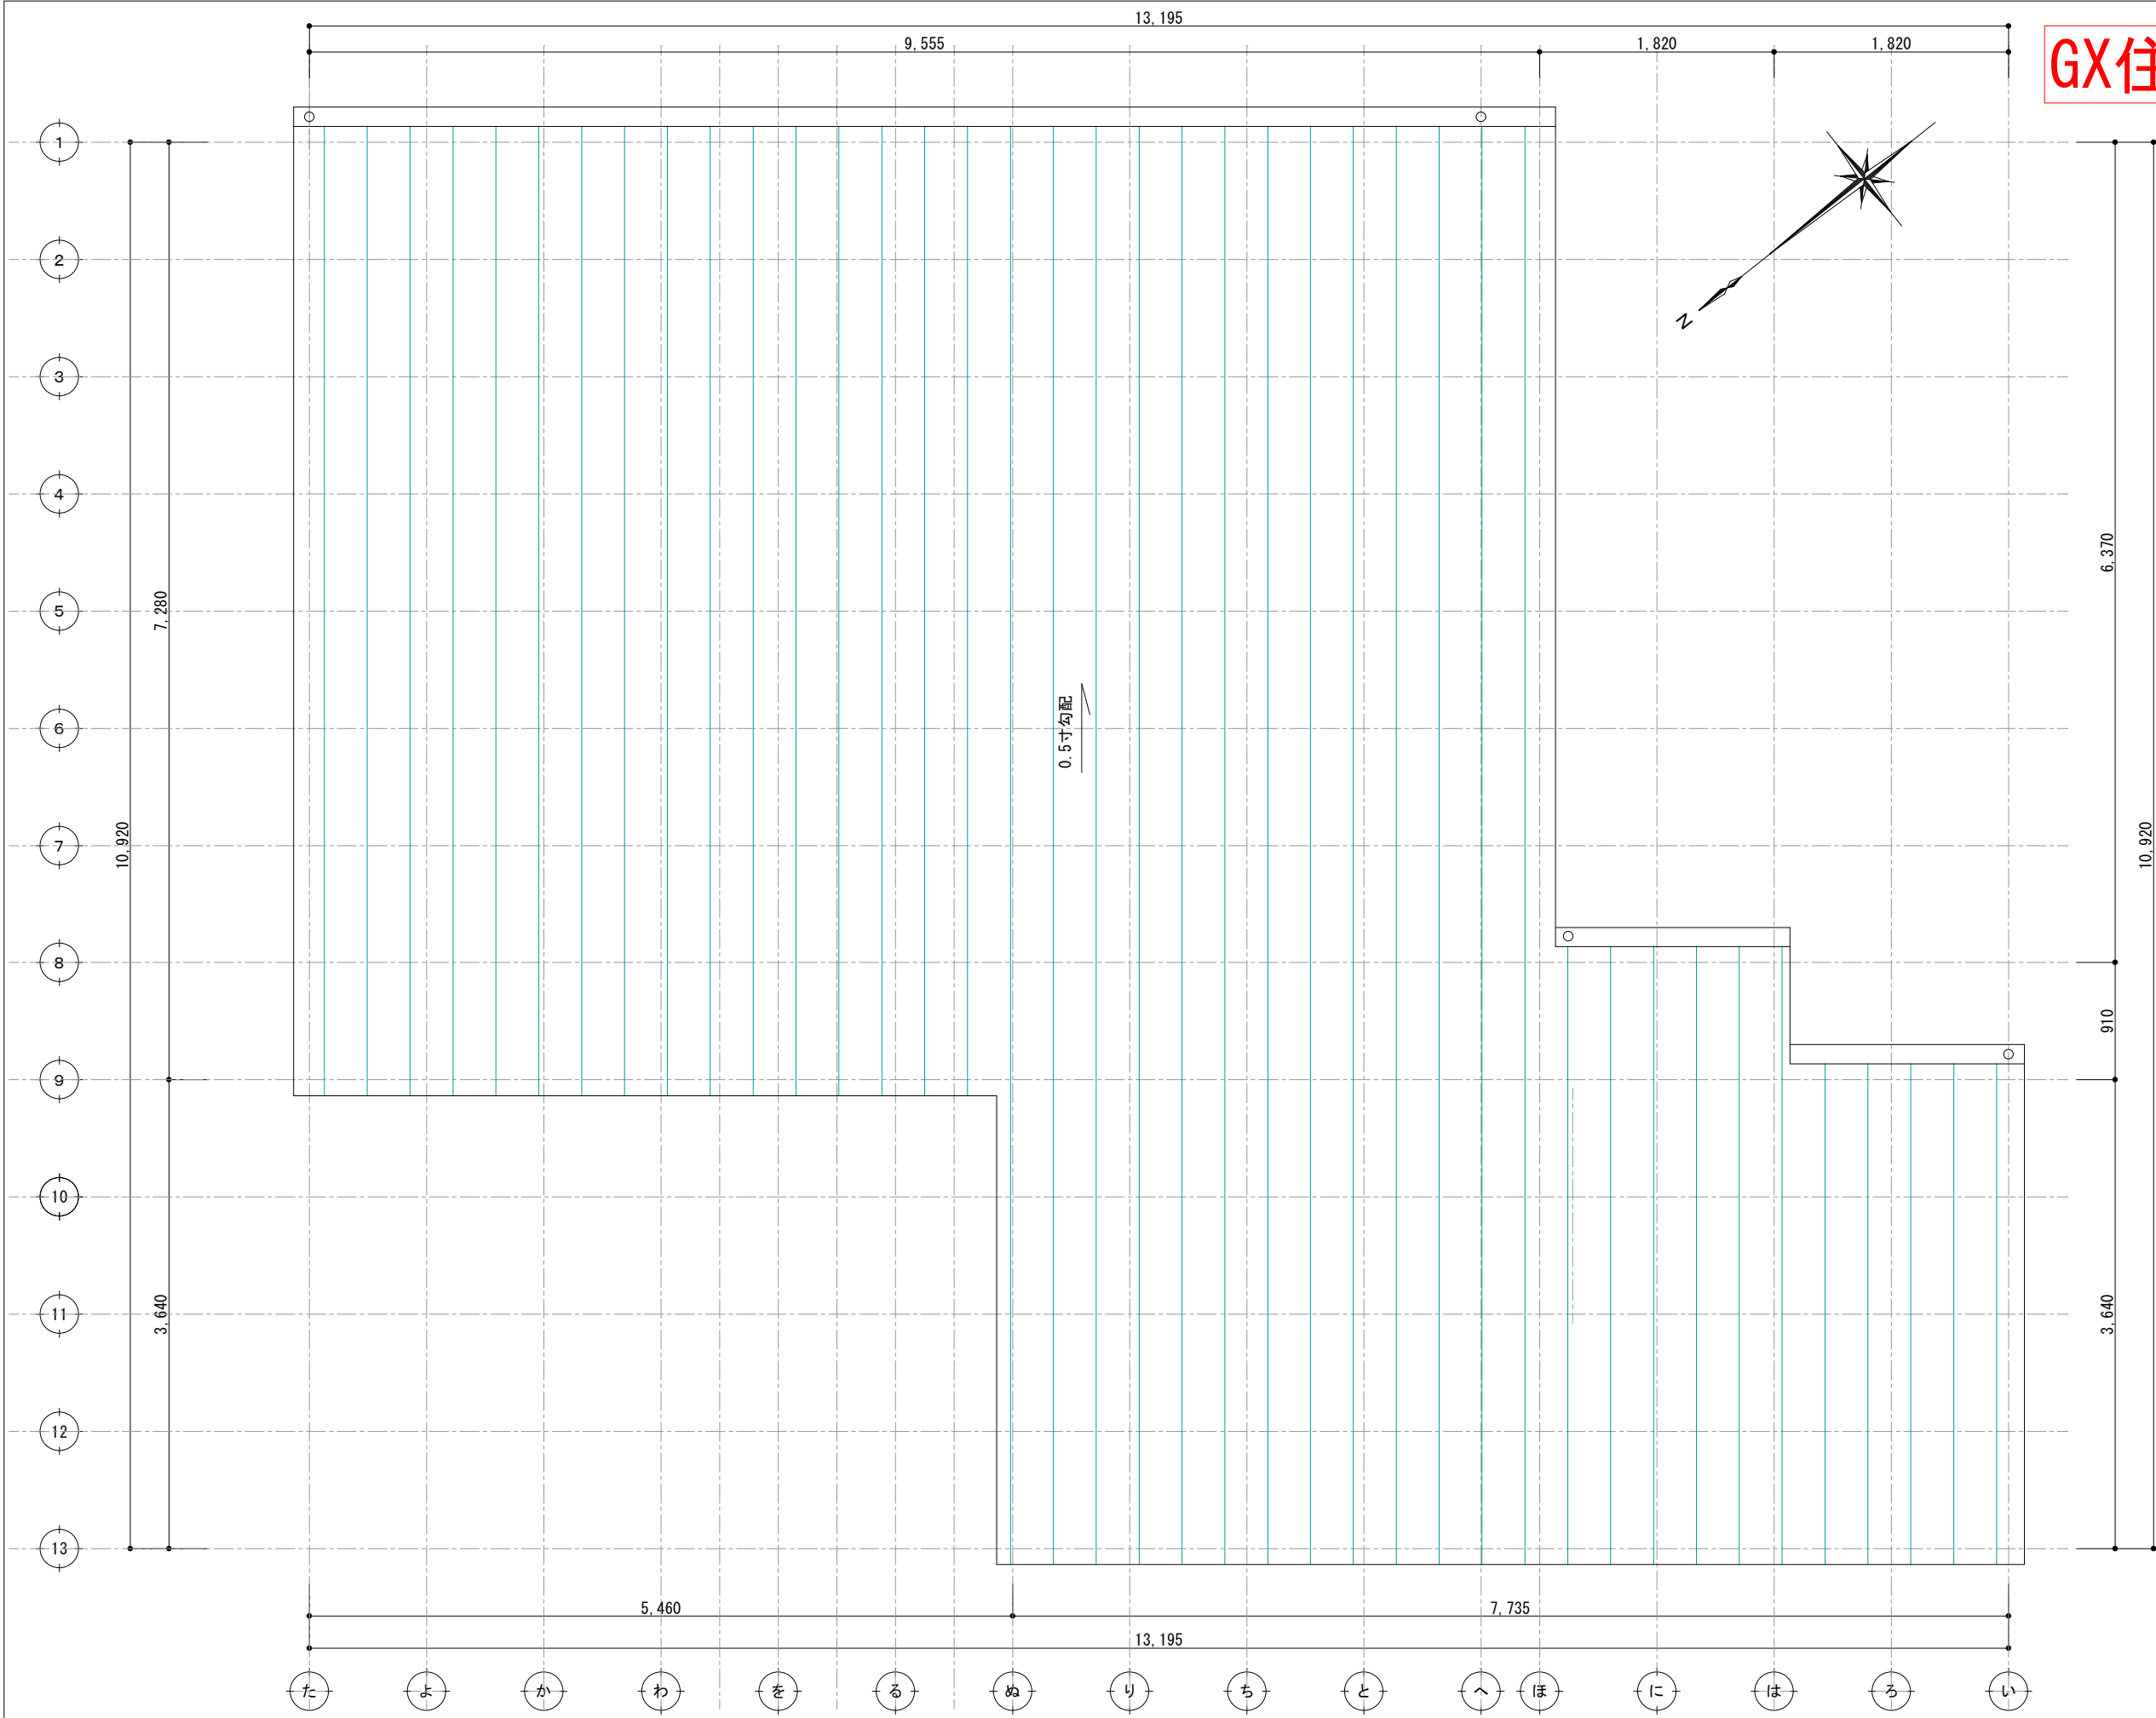

GX住宅 (Cube J付)

太陽光あり

決定図

|     |                                                                                    |                                                                                      |   |            |             |  |      |    |    |     |
|-----|------------------------------------------------------------------------------------|--------------------------------------------------------------------------------------|---|------------|-------------|--|------|----|----|-----|
| 訂 正 | 浜 岡 一 級 総 合 設 計 事 務 所<br>一級建築士事務所 静岡県知事登録第 (10)2441 号<br>一級建築士 大臣登録第 365879 号 西原利昌 |  | 株式会社 LIFEFUND InDesign office 一級建築士事務所<br>事務所登録 (2)第7595号 一級建築士登録 第179770号 鈴木 達男<br>〒432-8023 静岡県浜松市中央区鴨江3丁目70番23号 | 2026. 3. 1 | 小林大樹様邸 新築工事 |  | 設計   | IC | 工事 | 図 番 |
|     |                                                                                    |                                                                                      |   | 縮 尺        |             |  | 図 名  | 角谷 |    | 青島  |
|     |                                                                                    |                                                                                      |   |            | 1/50        |  | 屋根伏図 |    |    |     |