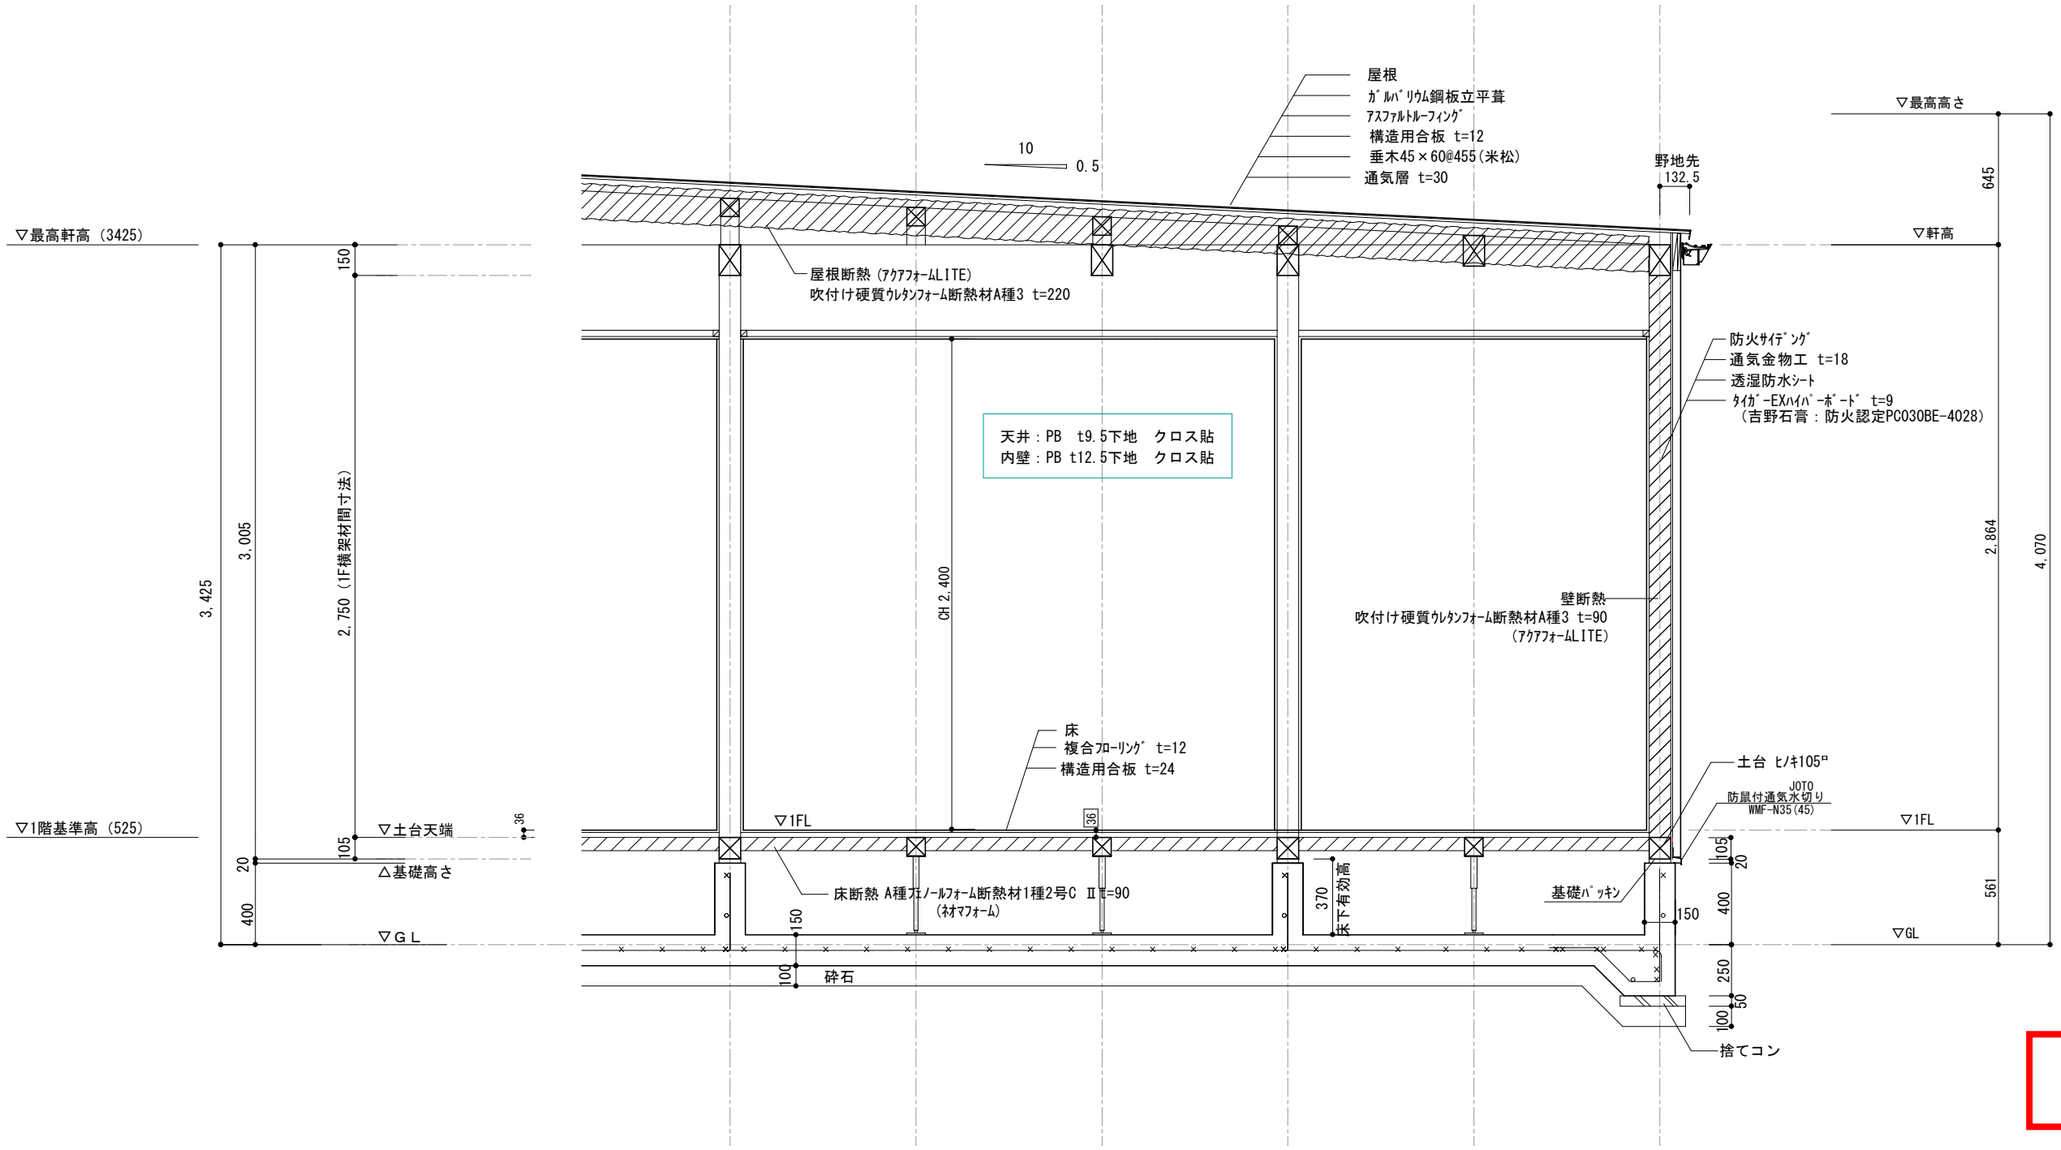

決定図

訂正	浜岡一級総合設計事務所 一級建築士事務所　静岡県知事登録第 (10)2441 号 一級建築士　大臣登録第 365879 号　西原利昌	PG HOUSE ピージーハウス 株式会社 LIFEFUND InDesign office 一級建築士事務所 事務所登録 (2)第7595号　一級建築士登録 第179770号　鈴木 達男 〒432-8023 静岡県浜松市中央区鴨江3丁目70番23号	年月日 2026.3.1	件名 小林大樹様 邸新築工事		設計	IC	工事	図番
			縮尺 1/30	図名 矩計図		角谷		青島	5