
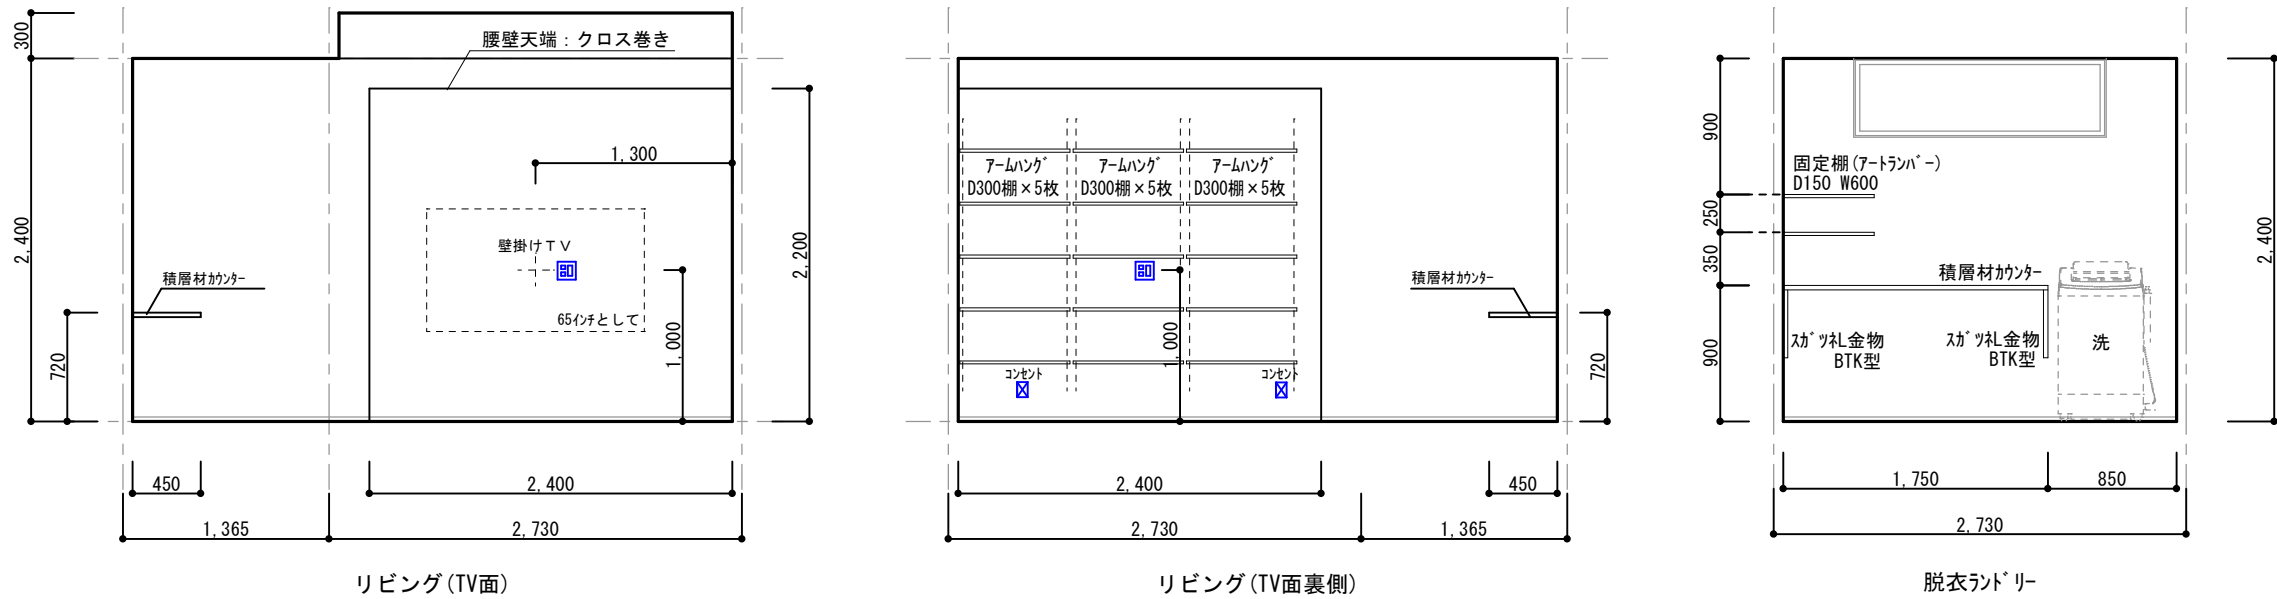
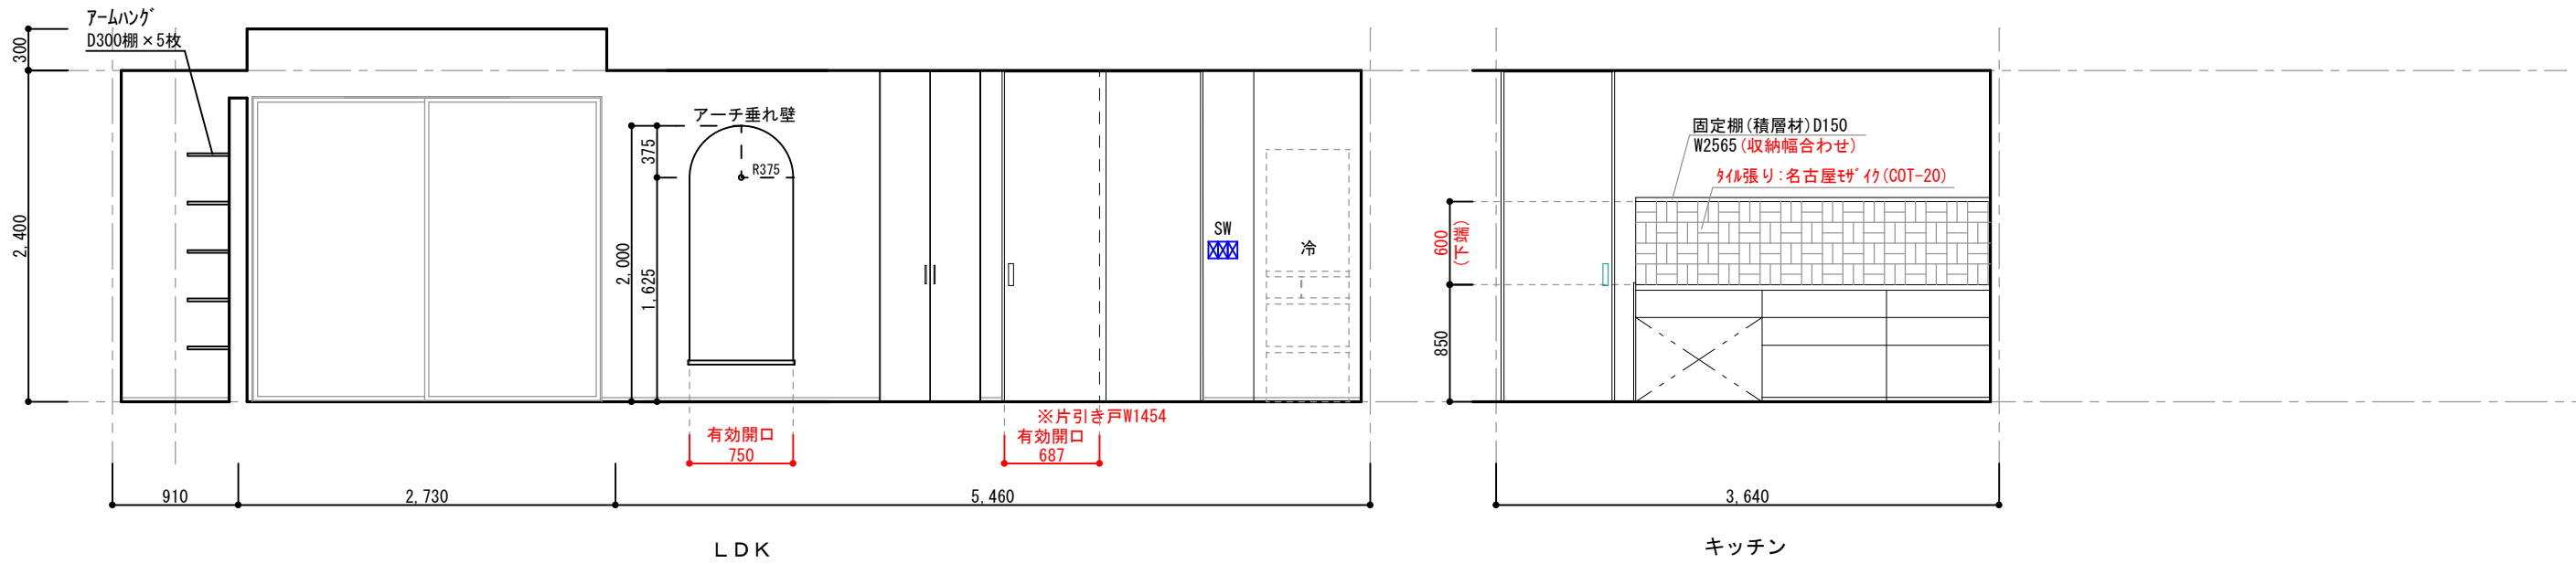


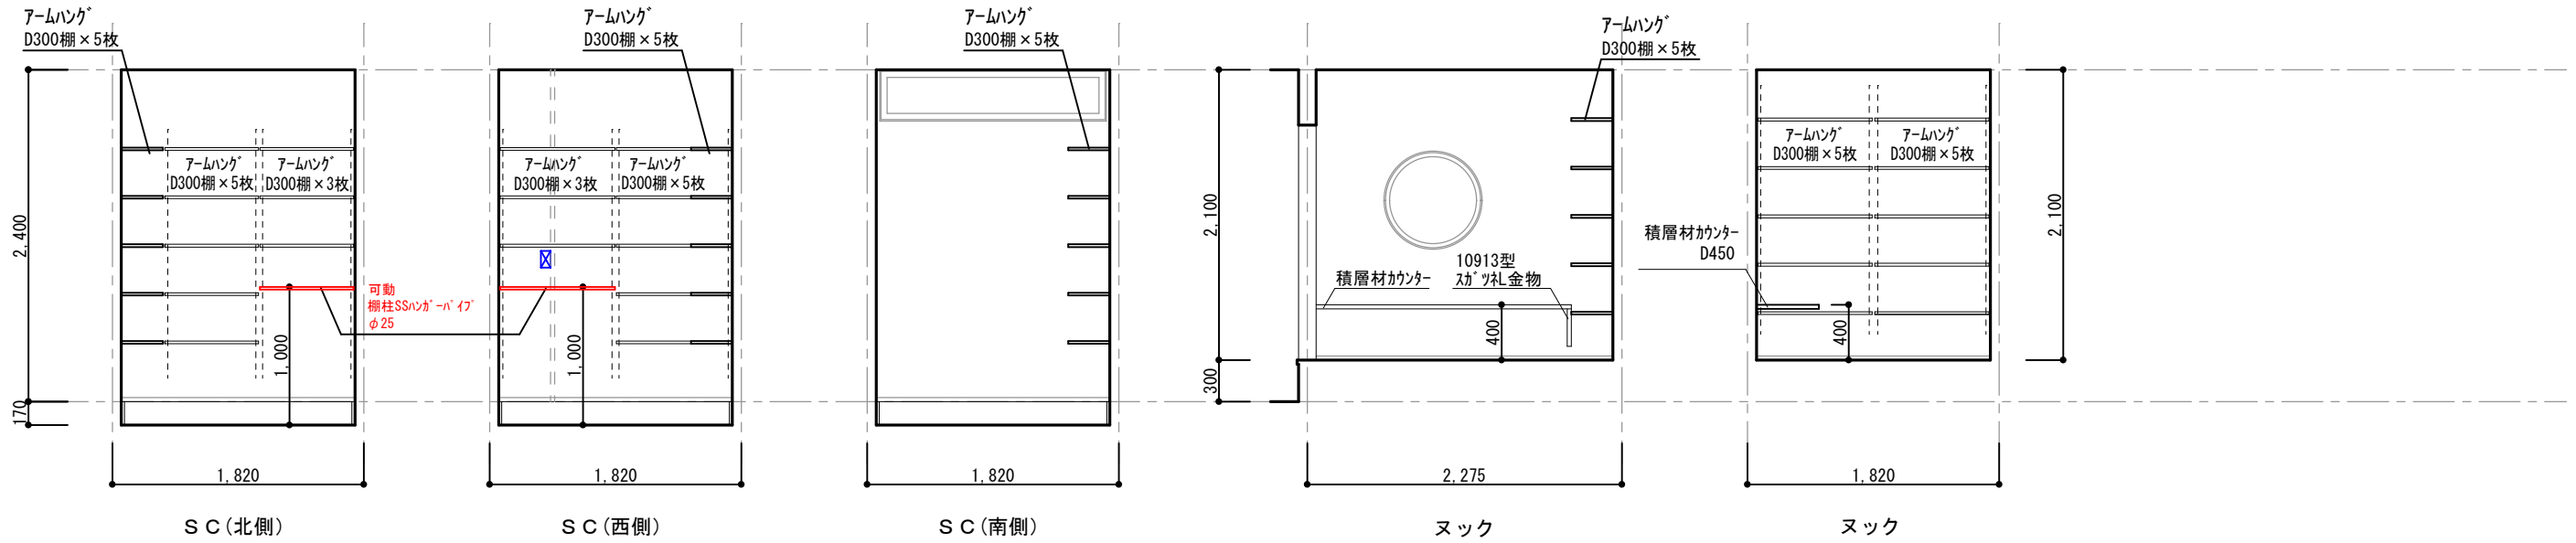

決定図

訂正	浜岡一級総合設計事務所 一級建築士事務所 静岡県知事登録第 (10)2441 号 一級建築士 大臣登録第 365879 号 西原利昌	LIFEFUND PG HOUSE	株式会社 LIFEFUND InDesign office 一級建築士事務所 事務所登録 (2) 第7595号 一級建築士登録 第179770号 鈴木 達男 〒432-8023 静岡県浜松市中央区鶴江3丁目70番23号	年月日 2026.3.1	件名 小林大樹様 新築工事	設計 IC 工事 図番	設計 角谷	IC 青島	工事 青島	図番 6-1
				縮尺 1/50	図名 展開図-1					