


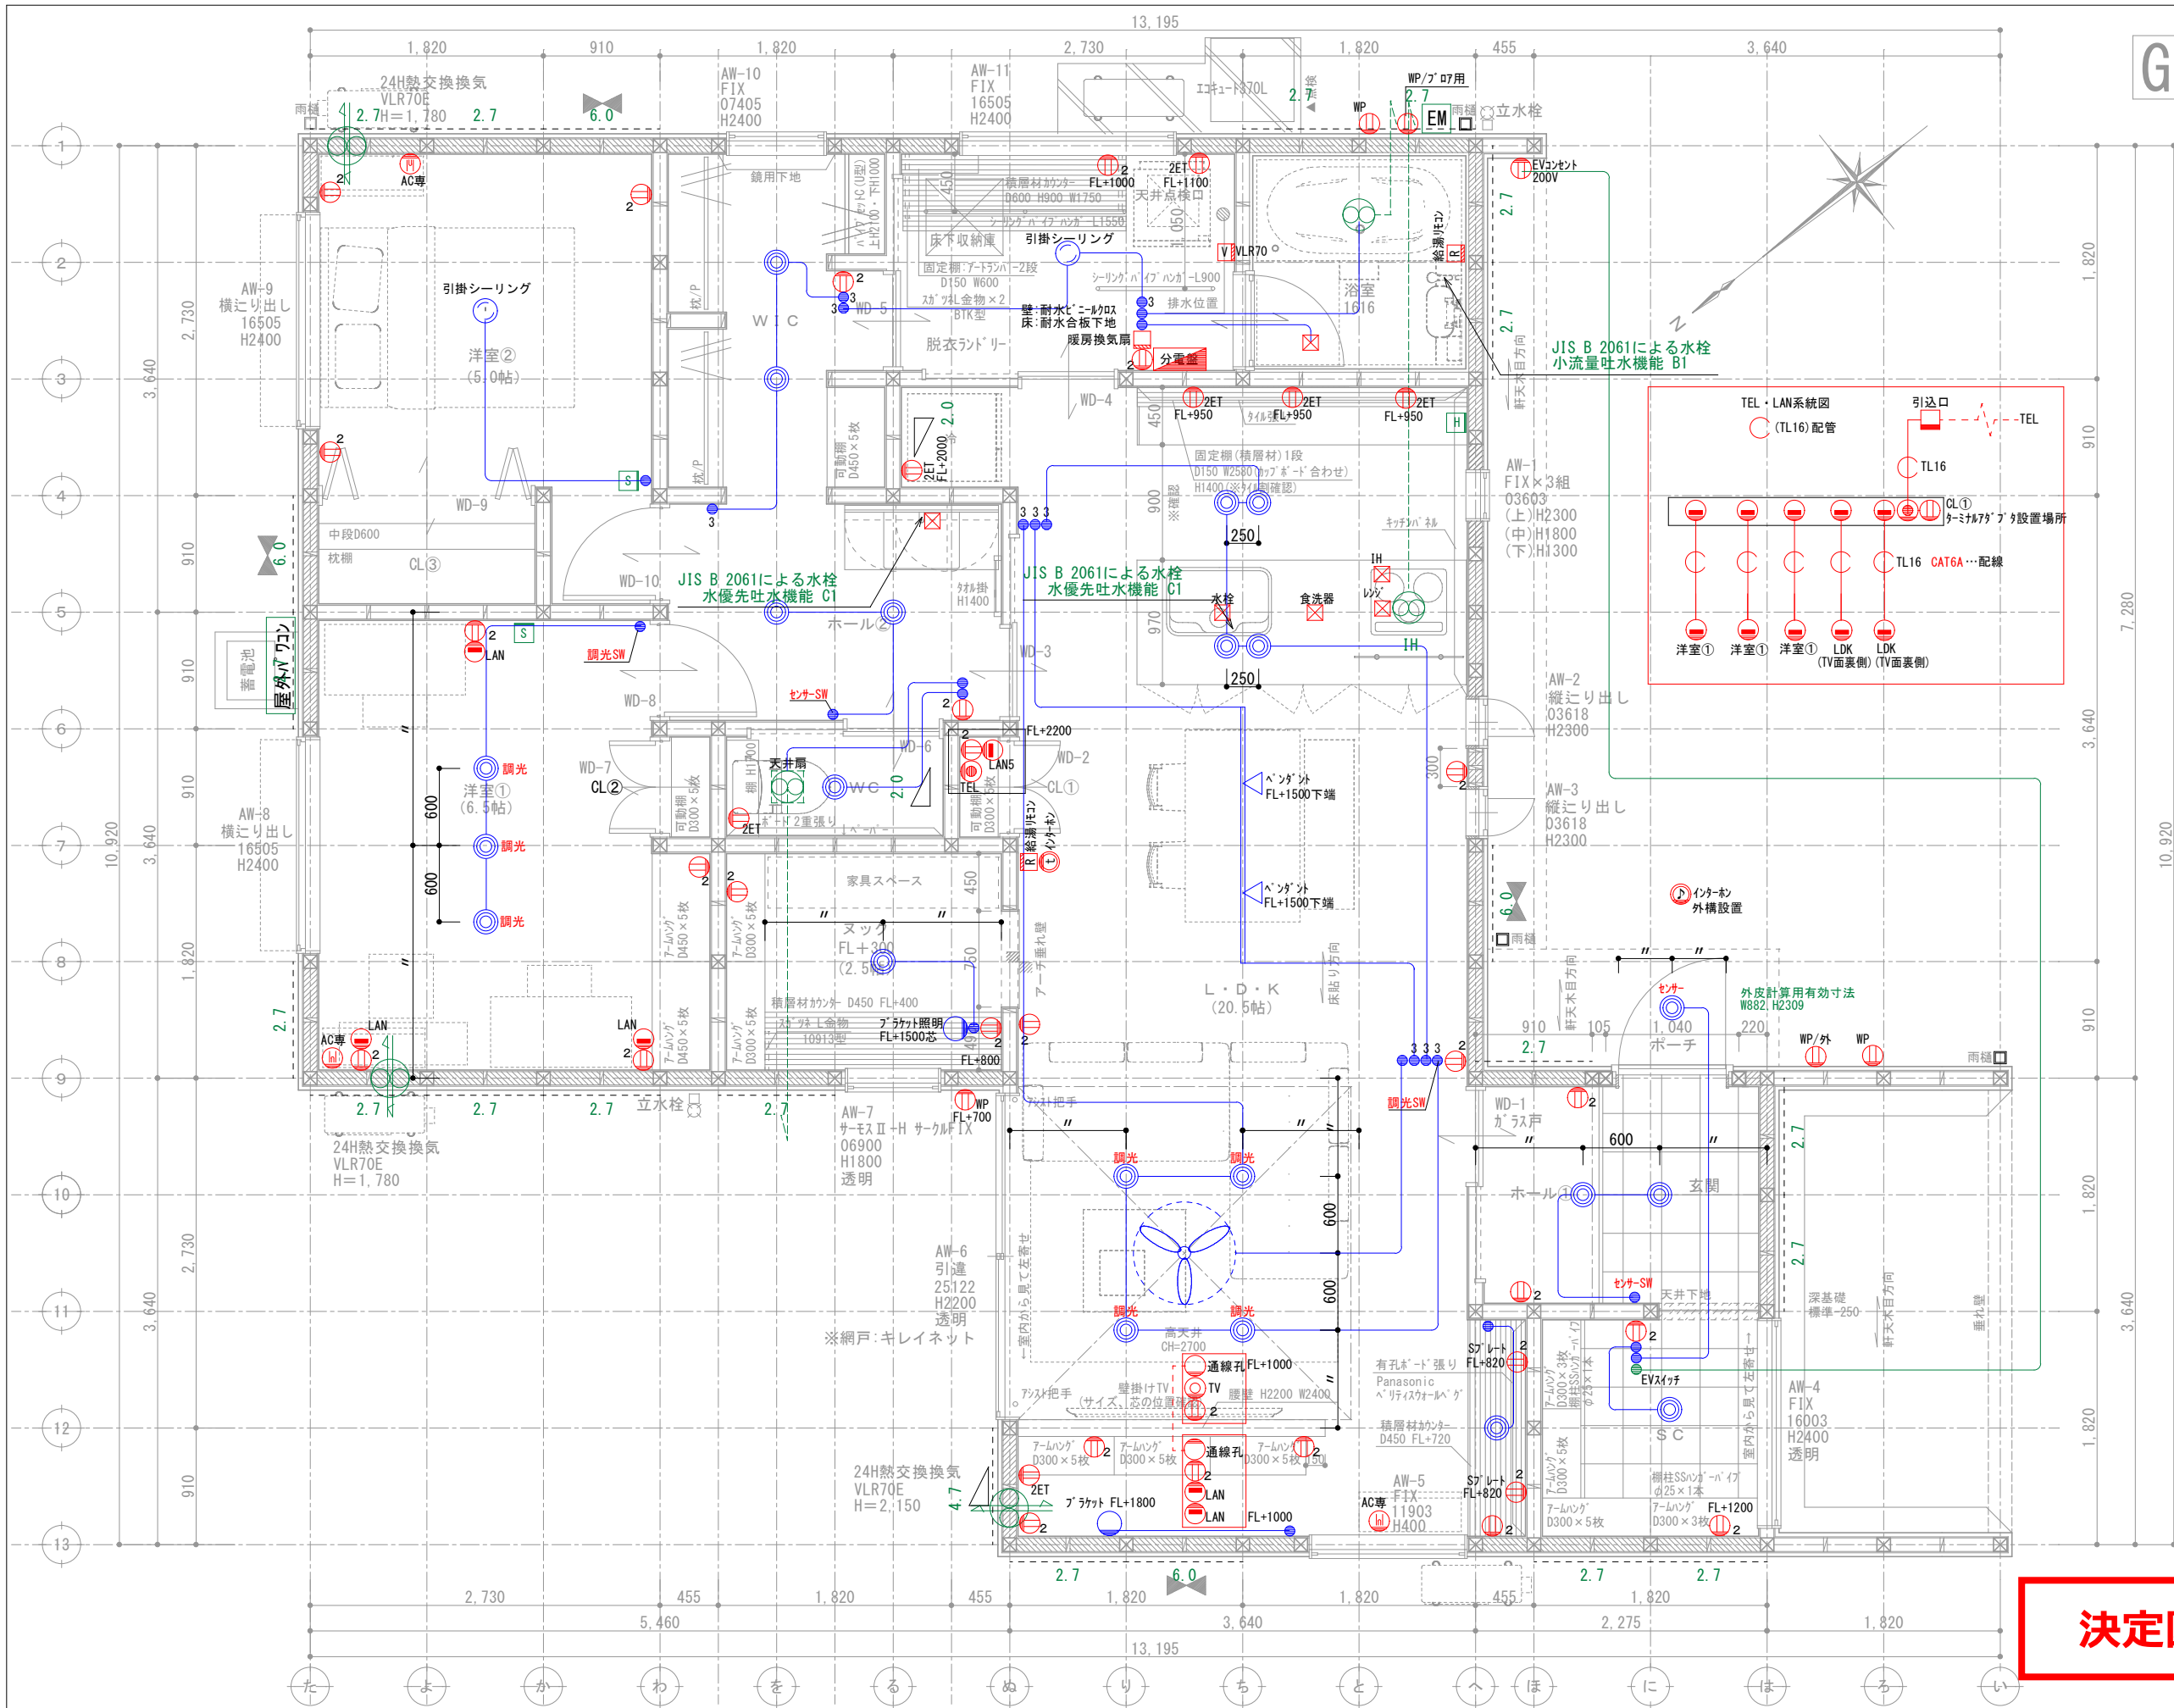

G2

壁付け 住宅用火災報知器			数量
H 熱感知	熱感知器	電池式(単独型)	1
		露出型	
壁付け 住宅用火災報知器			数量
S 煙感知	煙感知器	電池式(単独型)	2
		露出型	

※ 煙感知器は壁・梁より600mm以上離す
壁に取付ける場合、
天井から150mm以上500mm以内離す
換気扇・エアコン吹出口から1500mm以上離す

※ 全室LED照明とする。

※ 標準天井高さ2,400

※ 特記無きガラスは型ガラス

※ 全室LED照明とし、居室においては調光制御、非居室においては人感センサーを採用する。

*** 凡例**

- 管柱 (105×105)
- K's'パネ (3.30倍 FRM-0641)
- 片筋違い (2.00倍 45×90)
(例 左:柱脚 右:柱頭)
- たすき掛筋違い (4.00倍 45×90)
- 構造用合板 (2.70倍)
(t=9 材種=EXハイバー)
- 床点検口
- 天井点検口
- 換気扇
- 熱交換換気扇VLR-70

アドバンスシリーズ	
スマートデザイン (外部)	
凡例	
①	コンセント 1ヶロ
②	コンセント 2ヶロ
③	コンセント 3ヶロ
①ET	コンセント1ヶロ接地ターミナル付
②ET	コンセント2ヶロ接地ターミナル付
③ET	コンセント3ヶロ接地ターミナル付
WP	防水型
④	エアコン用コンセント
⑤	200V用コンセント
WP	防雨入線プレート
⑥	スイッチ
⑦	3路スイッチ
⑧	4路スイッチ
⑨	直結電源
⑩	テレビ取出口
TEL	電話取出口 (テレホンガイド)
LAN	LAN取出口 (テレホンガイド)
⑪	壁照明
⑫	リモコン (給湯関係・ルフロ)
⑬	メーター
⑭	分電盤
⑮	チャイム

※ACコンセント天井付け
※TVアンテナ工事
※スイッチはFL+1100、コンセントはFL+200

決定図