



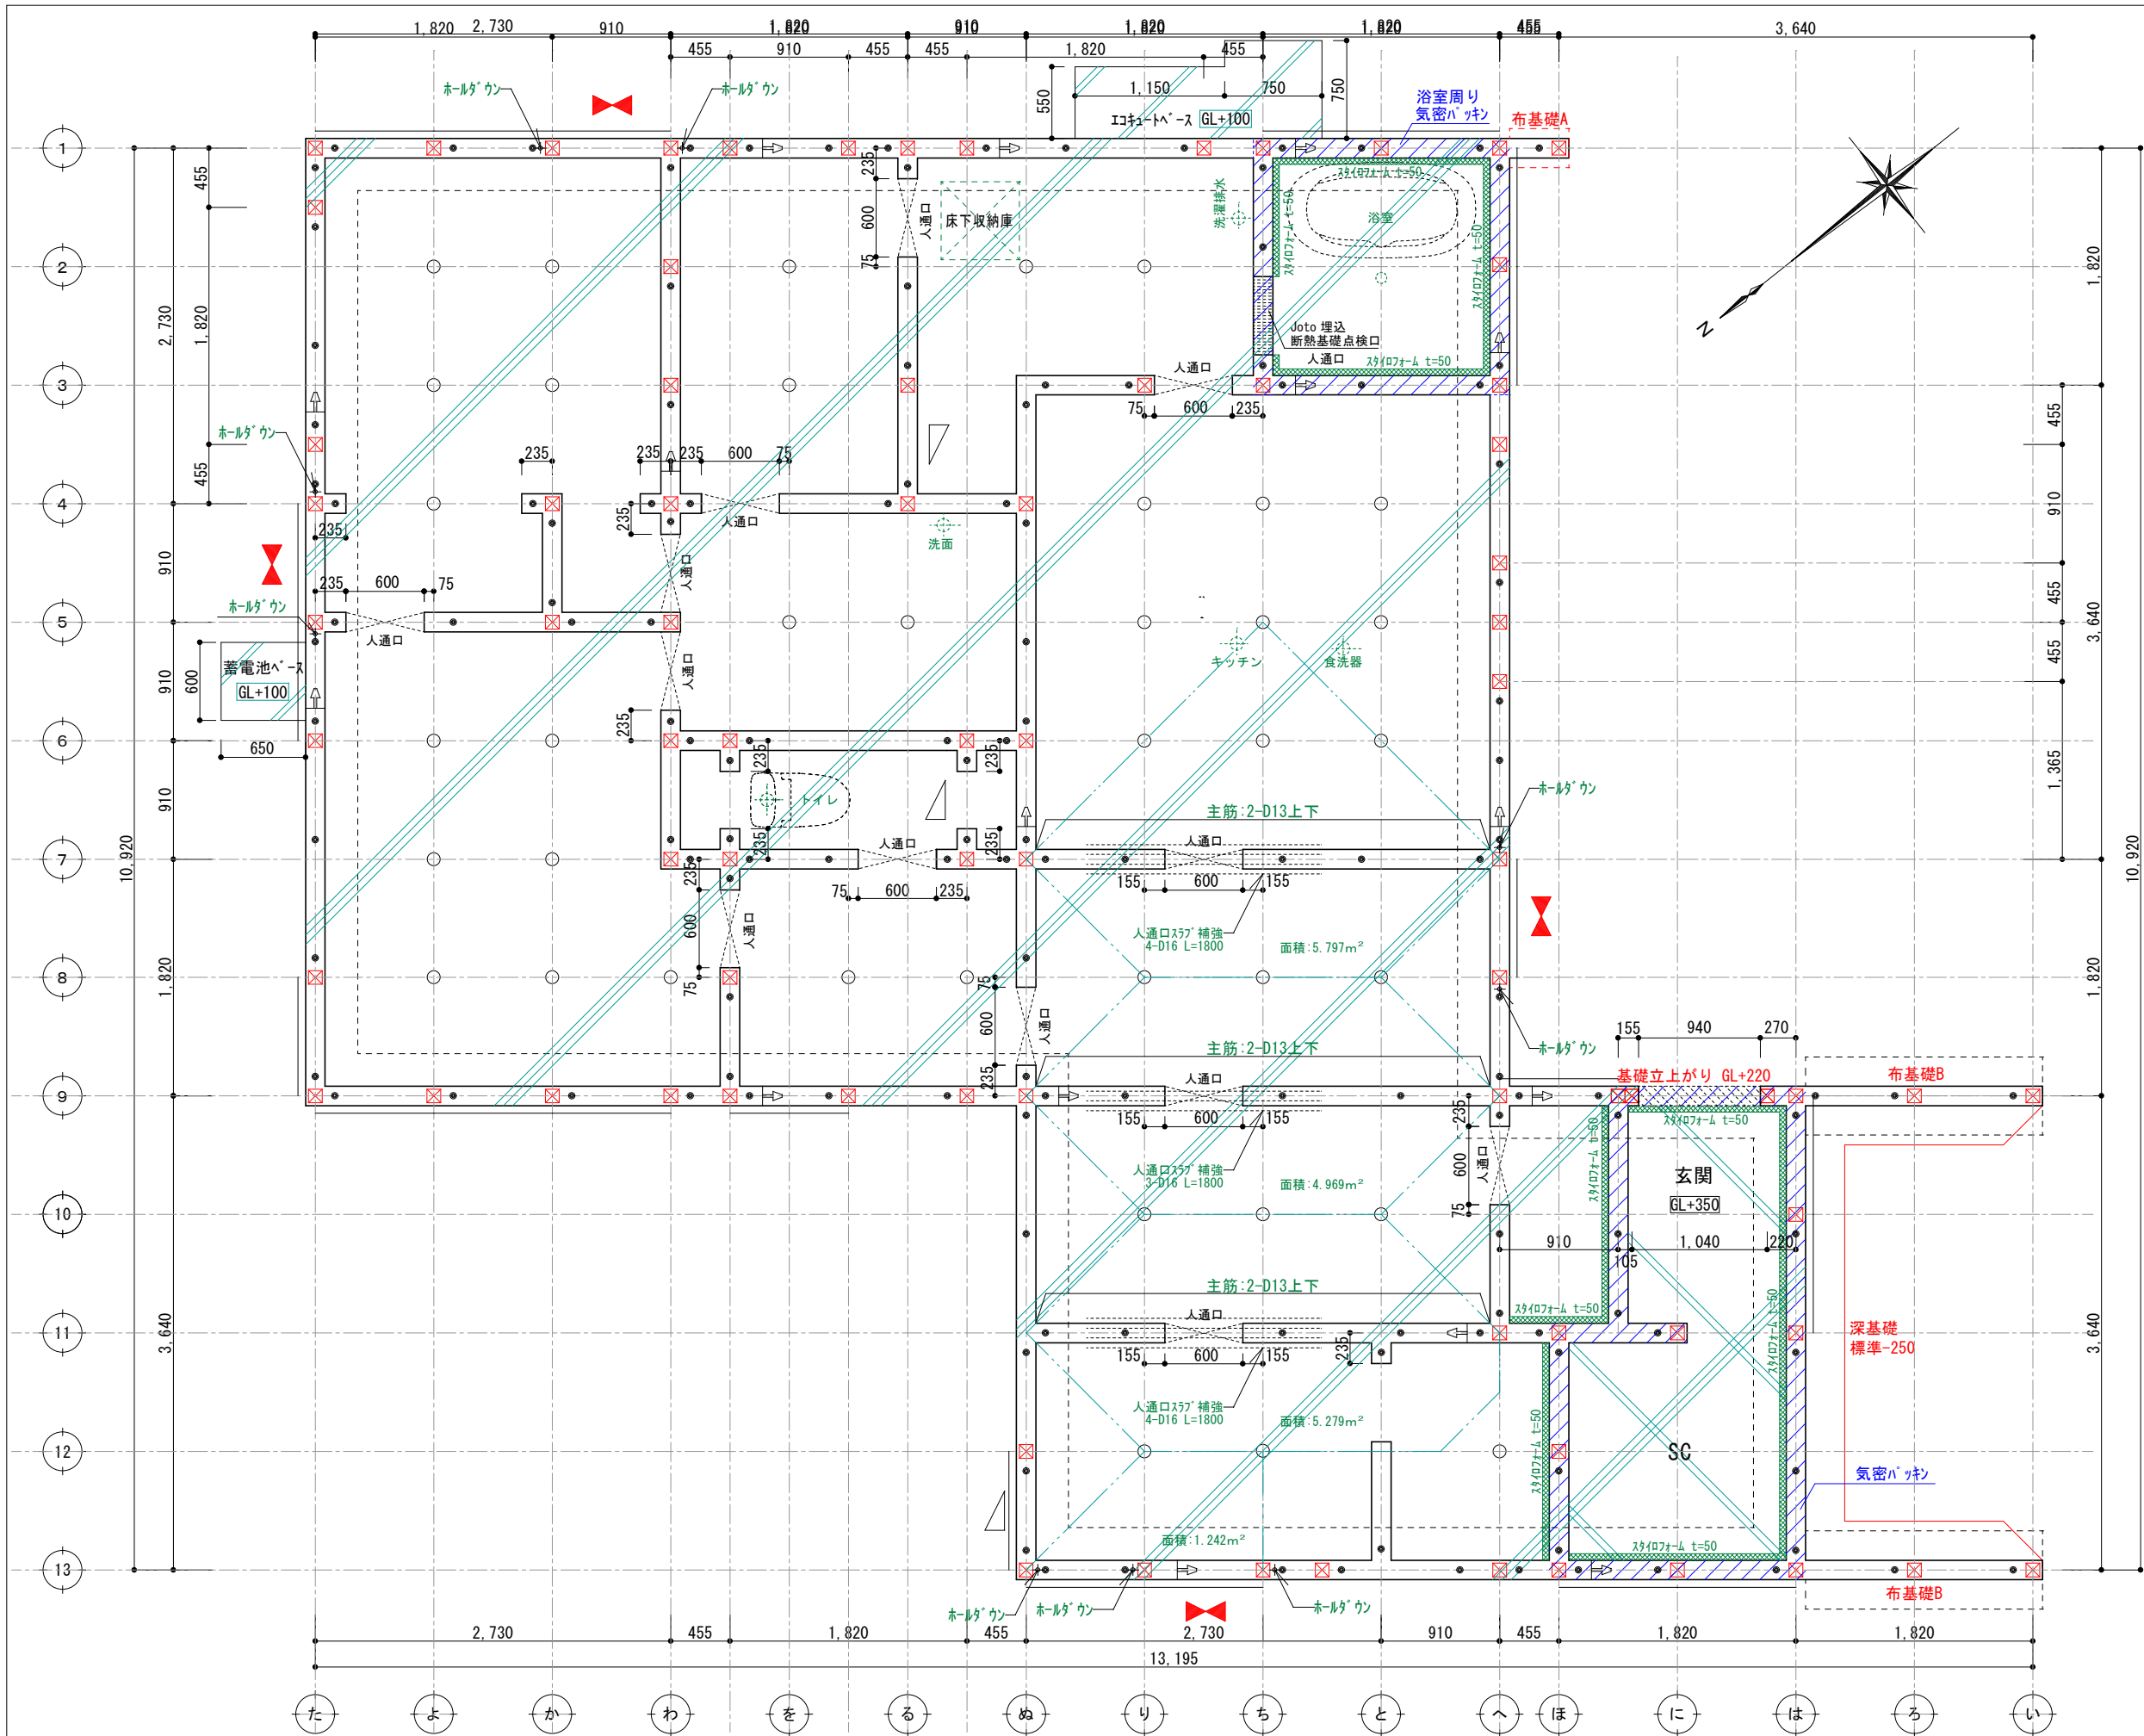

構造体ベースコンクリート t=150

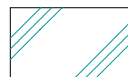


後打ち土間コン



アンカーボルトの配置
土台切れの箇所より150mm
土台の継手及び仕口の端部より150mm
耐力壁の端部、筋交いの脚部より150mm
1.82m以下の間隔
250mm以上埋込み
基礎天端より120mm

筋かい凡例
柱脚 柱頭 片筋かい
たすき掛け筋かい
構造用パネル

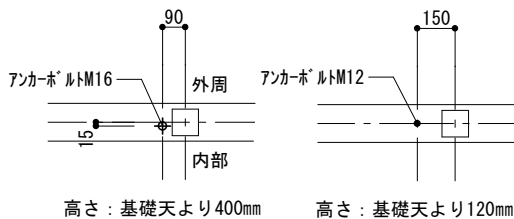

ホールダウン用アンカーボルト配置

アンカーボルト配置

- 凡例
- 通し柱 (105*105) 管柱 (105*105)
 - アンカーボルト M12 L=400
 - ✦ ホールダウンアンカー M16 L=800
柱芯より90mm 280mm以上埋め込み
(カナフイストアンカーボルト M16)
 - ⊕ 鋼製束
 - 土台ジョイント
 - ▨ ベースコンクリート (t=150)
 - ▨ 後打ちコンクリート

- 基礎伏図について特記なき場合に限り下記による。
1. コンクリート：呼び強度 21N/mm²
 2. 鉄筋：SD295A
 3. 設計地耐力：fe=20kN/m²
地耐力計測後、不足の場合は相当の改良を行い、満たすものとする。
 4. 基礎の位置は、芯振分けとする。
 5. 玄関・S/C・UB周囲の基礎天端は気密パッキン施工（網掛け部）とし、その他の基礎天端は基礎パッキン施工とする。
 6. 設備配管の屋内への取り入れは基礎立上り部のスリーブによる。

決定図

訂正	浜岡一級総合設計事務所 一級建築士事務所 静岡県知事登録第 (10)2441 号 一級建築士 大臣登録第 365879 号 西原利昌	 ピージーハウス	株式会社 LIFEFUND InDesign office 一級建築士事務所 事務所登録 (2) 第7595号 一級建築士登録 第179770号 鈴木 達男 〒432-8023 静岡県浜松市中央区鶴江3丁目70番23号	2026. 3. 1 縮尺 1/50	図名 小林大樹様邸 新築工事 基礎伏図	設計	IC	工事	図番
						角谷		青島	B-1