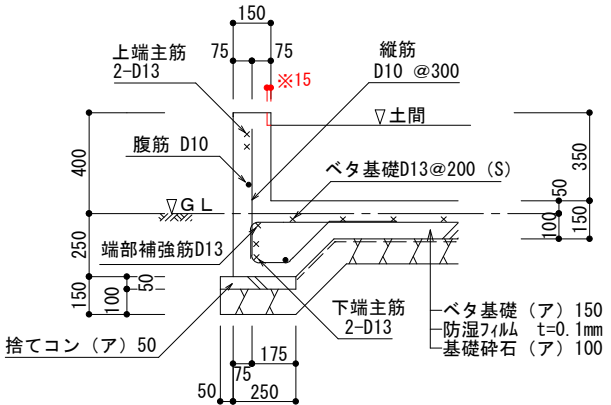
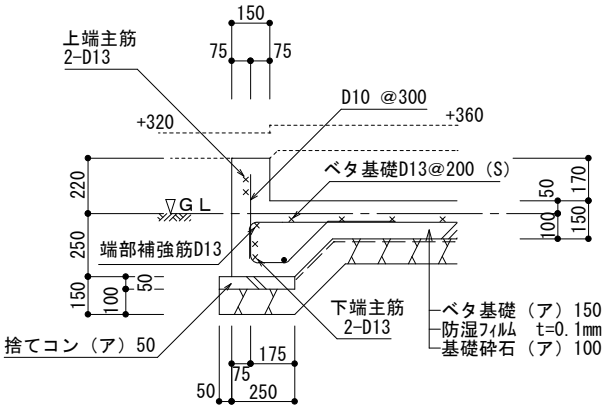
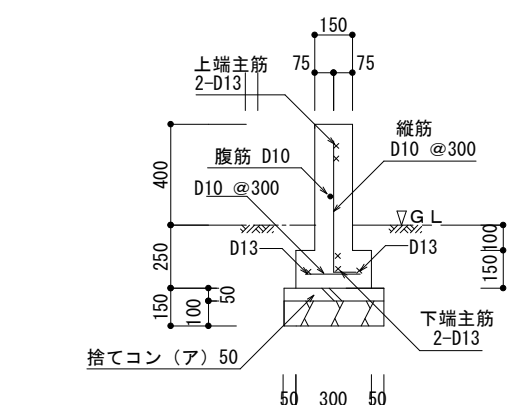
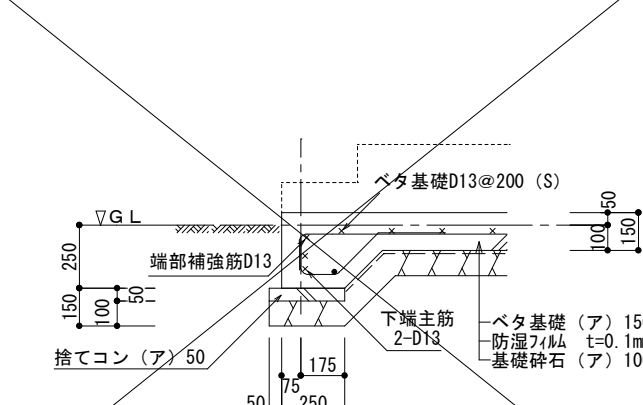
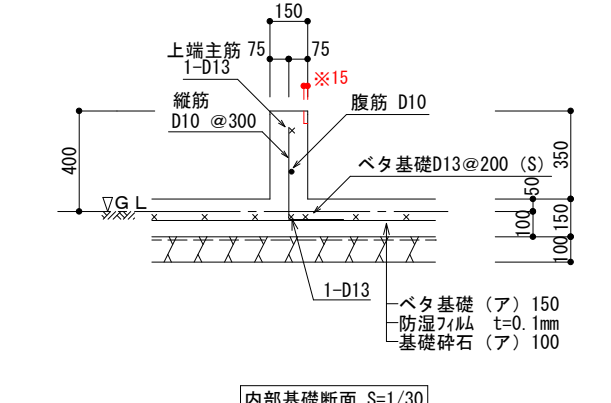
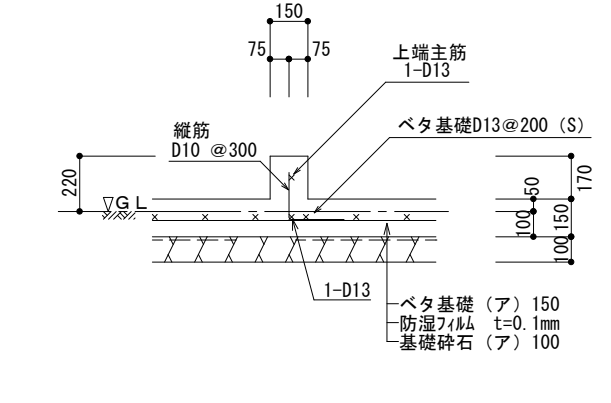
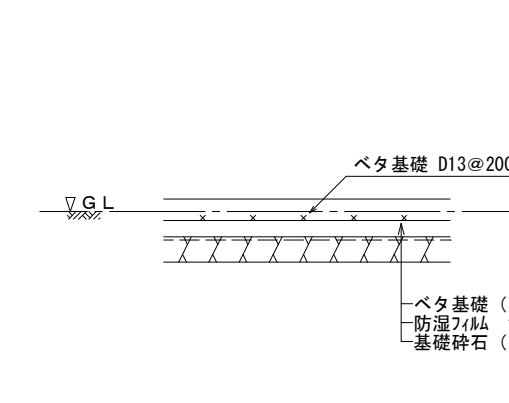
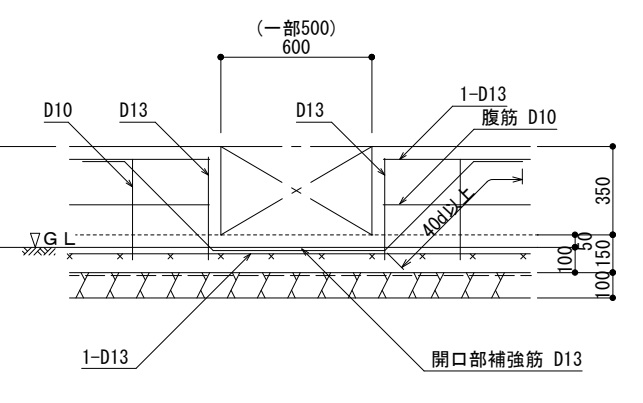
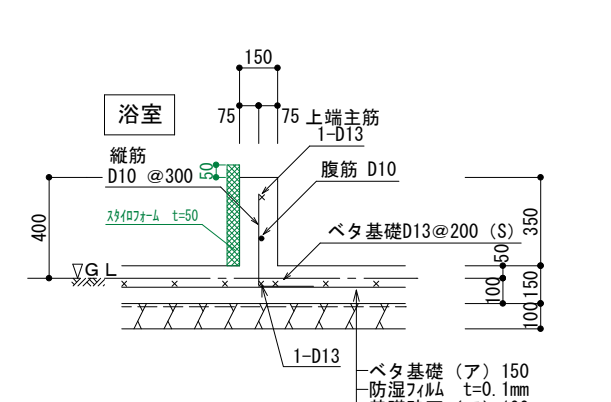
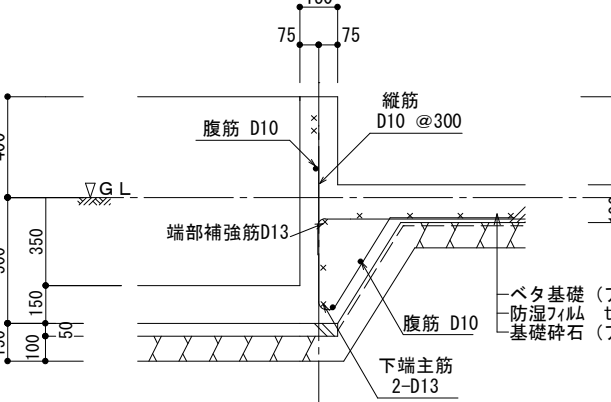
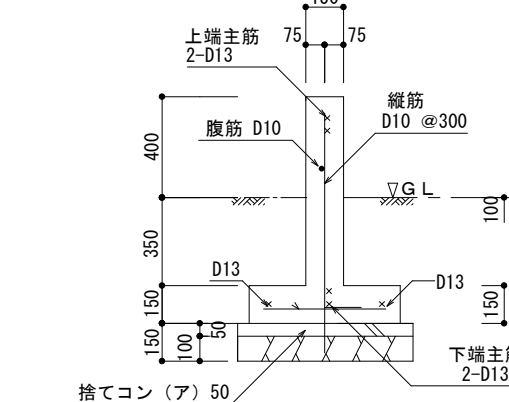


 外周基礎断面 S=1/30 ※玄関内土間部分のみ15mm欠き込み	 ポーチ下 外周部基礎断面 S=1/30 倉庫ドア下 外周部基礎断面 S=1/30	 布基礎A：袖壁用 基礎断面 S=1/30	 ポーチ外周部の基礎断面 S=1/30 立上り無しの基礎断面 S=1/30							
 内部基礎断面 S=1/30 ※玄関内土間部分のみ15mm欠き込み ※注意：基礎伏図に特記のない内部基礎の場合	 ポーチ下 内周部基礎断面 S=1/30 玄関ドア下 内周部基礎断面 S=1/30 玄関＝SC布基礎断面 S=1/30	 ベタ基礎断面 S=1/30	 人通口補強 S=1/30							
 浴室内部基礎断面 S=1/30 ※注意：基礎伏図に特記のない内部基礎の場合	 外周深基礎/布基礎B 断面 S=1/30 深基礎(標準-250)	 布基礎B 断面 S=1/30	基礎の寸法 及び 配筋の検証方法 基礎立上り配筋は、 (財)日本住宅・木材技術 センター発行のスパン表 (増補版)による。 ベタ基礎スラブ配筋は、 まもりすまい保険設計施工 基準同解説のベタ基礎配筋表 による。具体的な寸法・配 筋は基礎詳細図参照。 鉄筋断面表記 ●・・・D10を示す。 ×・・・D13を示す。 ※使用しない断面は×を記入。 決定図							
訂正	浜岡一級総合設計事務所 一級建築士事務所 静岡県知事登録第(10)2441号 一級建築士 大臣登録第365879号 西原利昌	PG HOUSE	株式会社 LIFEFUND InDesign office 一級建築士事務所 事務所登録(2)第7595号 一級建築士登録第179770号 鈴木 達男 〒432-8023 静岡県浜松市中央区鴨江3丁目70番23号	年月日 2026.3.1 縮尺 1/30	件名 小林大樹様 邸新築工事 図名 基礎断面リスト		設計 角谷	IC 青島	工務 青島	図番 B-2