

■ 仕 様		■ HEAT20 G2
断熱工事	■ 床:カネライトフォーム t90 ■ 土間床等の外周:スタイロフォームAT t50 ■ 壁:アクアフォームLITE吹付 t90 ■ 天井:アクアフォームLITE吹付 t220	
床下換気	■ 基礎パッキン JOTO (玄関・UB周り:気密基礎パッキン)	
防虫防蟻	■ 土壌処理・木部 ガントナーMC	


■ 外 部 仕 上 表			■ 22条地域
部位	仕上・仕様・メーカー		色番・品番
屋根	■ ガルバリウム鋼板(t0.35)UK立平 ニスクカラーPro GH 軒先通気金物 日本住環境株式会社【REV-15】		GHK01 Sブラック
パラペット笠木	■ なし		
破風・鼻隠	■ なし		
軒天	屋根軒	■ ニチハ軒天5 木目調 910×1820×5	ライト
	ポーチ軒	■ ニチハ軒天5 木目調 910×1820×5	ライト
	バルコニー軒	■ なし	
オーバーハンク水切り		■ ガルバリウム鋼板 ※外壁合わせ JOTO:HF-A3550	アンバーグレー
外壁 ※下地面材:タイガーEXハイパー 防火認定 PC030BE-4028	■メイン	ニチハ モエンエクセラード16 Vシリーズ ルビドフラットV	ヘイジグレー
	■アクセントA	なし	
	■アクセントB	なし	
玄関ポーチ		■ 床 玄関に同じ	-
基礎		■ 立上り巾木: モルタル刷毛引き	-
基礎水切り金物		■ JOTO鋼板製 防鼠材付き水切り JOTO:WMF-N35	アンバーグレー
バルコニー	床・内壁	■ なし	-
	笠木	■ なし	
外部建具		■ LIXIL EW(アルゴンガス高遮熱仕様LowEトリプルガラス クリア) ※スツックのみサーモスⅡ-H(アルゴンガスLowEペアガラス クリア) ・SD、TSは、メーカー設定によるが、オペレーターハンドル優先とする ・オペレーター付サッシの場合は固定網戸とする ・グレモンハンドル式サッシの場合は可動網戸とする	外観 ホワイト 内観 ホワイト ※樹脂パッキン・網戸付
シャッター		■ なし	
軒天通気金物		■ なし	
玄関扉		■ LIXIL ジェスタ2 K2仕様 LIXILファミロック タグキー×3 (電池式) ※標準キー収納リモコン×2	ドア型: M17 型 ドア色: チーク浮造 ハンドル: S型ハンドル 色: ブラック
外部物干し金物		■ なし	
換気フード	■ 局所換気扇(トイレ 浴室 キッチンフード) 防火ダンパー無		外気フード: シルバー
	■ ダクトレス熱交換換気システム (日本スティーベル株式会社) VLR-70E 防火ダンパー無		外気フード: S シルバー 室内パネル: ホワイト

■ 構 造 概 要			
基礎	■ RCベタ基礎コンクリート		
通し柱・管柱	■ 構造用集成材 105×105	間柱	■ 集成材
土台	■ 桧 105×105 大引き ■ 桧 90*90	筋交い	■ 構造用製材 火打梁 ■ 鋼製火打(当社基準により米松あり)
桁・梁	■ 構造用製材及び集成材		制震装置 ■ Kダンパー (株)アイ・エム・エー


■ 設 備 装 着 品				
住宅設備	部位	メーカー	商品名 ※ 詳細は見積り、プレゼン参照	見積りNo. (日付)
	キッチン	LIXIL	■ ES	見積り番号 : M25119238165-008-2 (日付) 2026.2.28
	バックカウンタ ※オプション	LIXIL	■ ES L2580(スライドストッカー×2+マルチスペース)	見積り番号 : M25119238165-008-3 (日付) 2026.2.28
	浴室	LIXIL	■ AX1616 PGハウス標準仕様	見積り番号 : M25119238165-008-1 (日付) 2026.2.28
	1Fトイレ	LIXIL	■ ベーシアハーモJタイプ 白 ● タオル掛け:無し タンク手洗 無し ● 紙巻き器: CF-AA22H /WA	見積り番号 : M25119238165-008-5 (日付) 2026.2.28
	洗面台	LIXIL	■ EV W1200(D500タイプ) 扉:グロスホワイト その他 ● タオル掛け:KF-AA71D(ハーフ)	見積り番号 : M25119238165-008-4 (日付) 2026.2.28
給排水設備	給湯器		■ エコキュート370L Panasonic Sシリーズ スタンダードモデル 追い焚きフルオート	
	排水		■ 合併浄化槽 5人槽 ポンプアップ無	
	外水栓		■ 2カ所 (平面図参照) ■ 外部立栓柱: PVC製 水栓柱12型アイホリー【前澤化成工業】	
	外部ガーデンパン		■ 無し	
	その他		■ 洗濯機用単水栓: 緊急止水弁付 ■ 洗濯機用排水:トラップ金物(標準) ■ 排水さや管(長期優良住宅仕様)	
ガス配管設備			■ なし (配置図・平面図参照) ■ ガス使用器具	
電気設備	インターホン		■ パナソニック VL-SE31XL	
	TVアンテナ		■ UHF + BS・110度CS／CSアンテナ [2K・4K・8K対応] ■ブラック ※電波状況によりホワイトになる可能性あり	
	エアコン		■ 設置場所:	
	ソーラー ※標準搭載		■ あり(Qセルズ) 12 枚 5.28 KW Re.RISE-G3 440 (1722×1134×30) ※メーカーのモデルチェンジ等で後継品に変更される可能性あり ■ 屋外パワコン エネルギーマネジメントシステム Cube J ■ 蓄電池 QREADY-B77-1	
その他				決定図

	浜 岡 一 級 総 合 設 計 事 務 所 一級建築士事務所 静岡県知事登録第 (10)2441 号 一級建築士 大臣登録第 365879 号 西原利昌	 株式会社 LIFEFUND InDesign office 一級建築士事務所 事務所登録 (2) 第7595号 一級建築士登録 第179770号 鈴木 達男 〒432-8023 静岡県浜松市中央区鴨江3丁目70番23号	年 月 日	件名	設計 IC 工務 図 番 角谷 青島 1-1
			2026.3.1	小林大樹 様邸 新築工事	
			縮尺	図面 仕上表 1	

浜松市中央区神原町地内

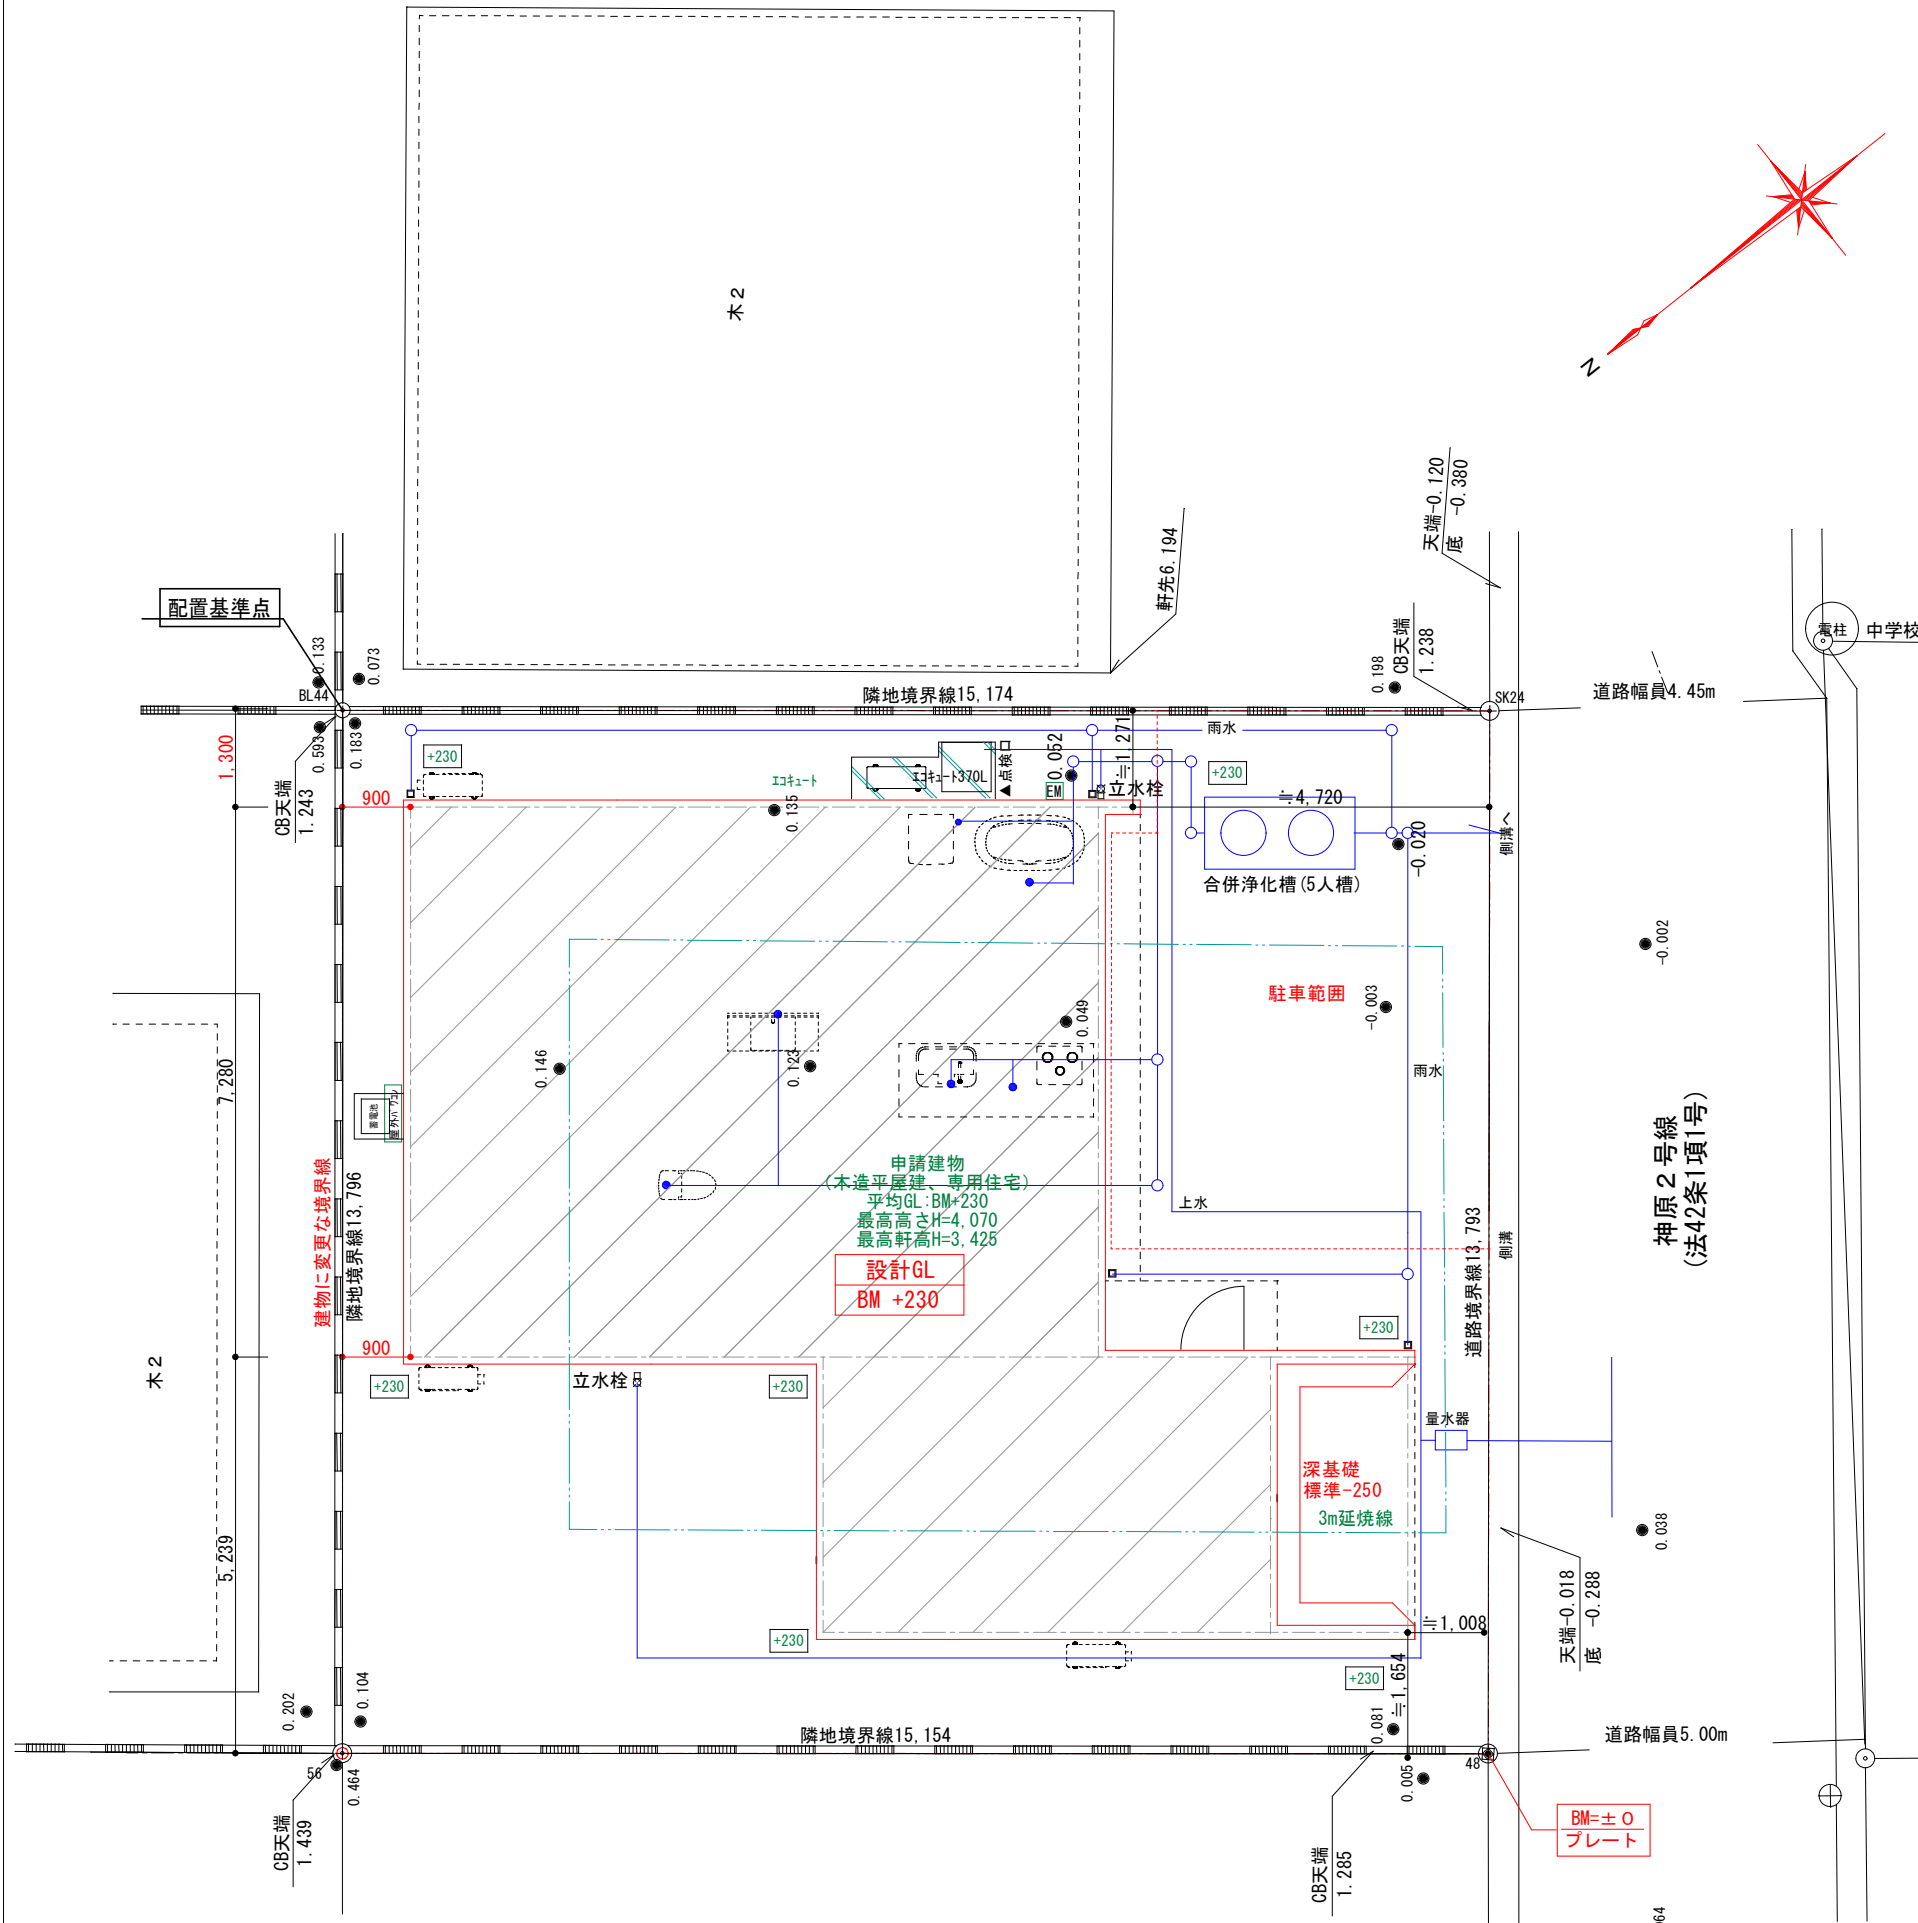

求積図 S=1/250

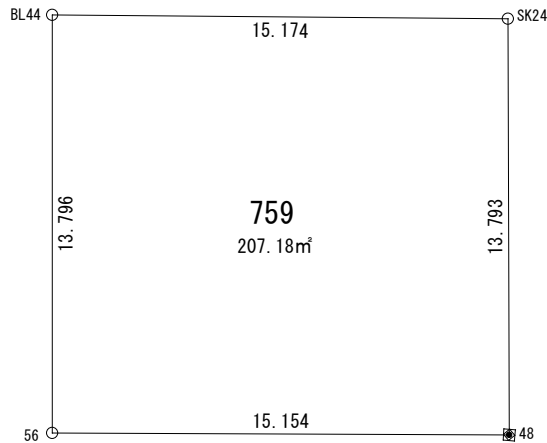

座 標 求 積 表

(任意座標)

地 番	759			
測 点	Xn	Yn	(Xn+1 - Xn-1) Yn	距 離
56	549.857	484.334	7239.824632	15.154
48	551.052	469.227	-5890.675758	13.793
SK24	537.303	468.122	-6997.487656	15.174
BL44	536.104	483.249	6066.707946	13.796
	倍 面 積		418.369164	
	面 積		209.1845820	
	地 積		209.18	


解体後、北側・西側・東側C B 2段予定

トータル面積表 (㎡)

敷地面積	209.18
建築面積	97.71
床面積 1階	87.77
延床面積	87.77
建蔽率	(97.71/209.18) × 100
容積率	(87.77/209.18) × 100

道路斜線制限については、明らかに適合する。
隣地斜線制限については、明らかに適合する。
平均地盤面について
申請建物の周囲の平均地盤面高さをBM+260とする。
盛土規制法の許可対象となる工事なし。

決定図

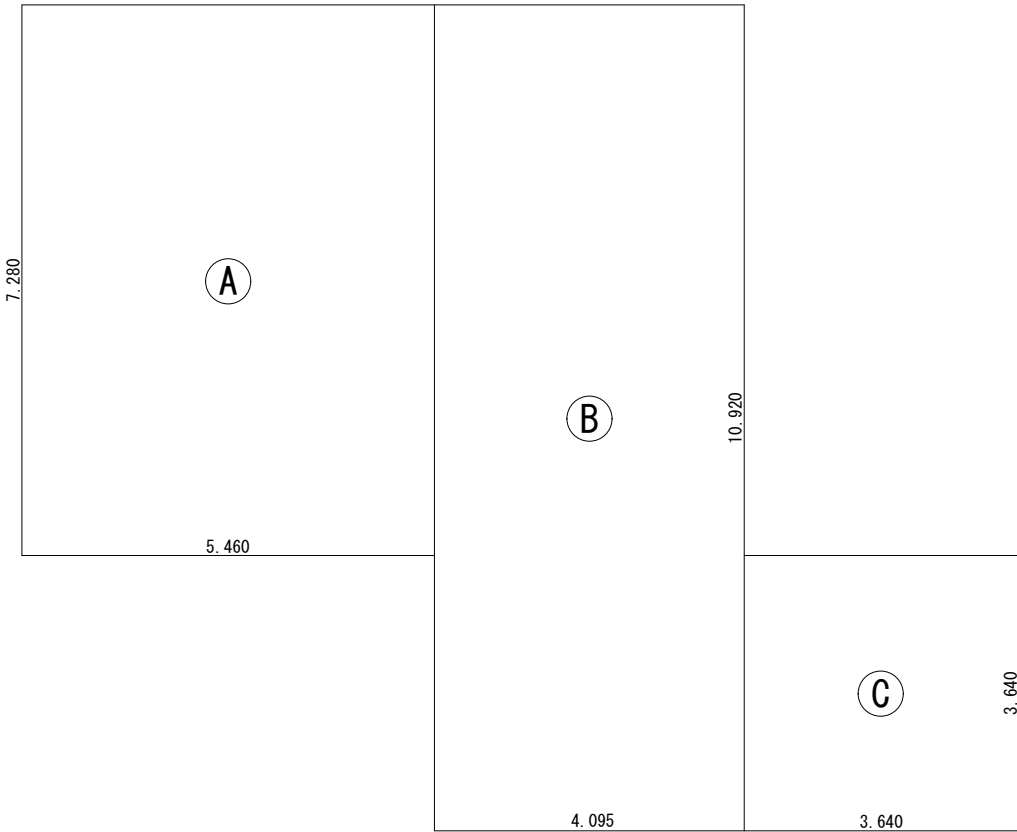


建築面積求積図 S=1/100

建築面積求積表

番号	計算式 (m)	面積 (㎡)
Ⓐ	5.460 × 7.280	39.7488
Ⓑ	4.095 × 10.920	44.7174
Ⓒ	3.640 × 3.640	13.2496
合計 ≡		97.7158 97.71

(29.5坪)

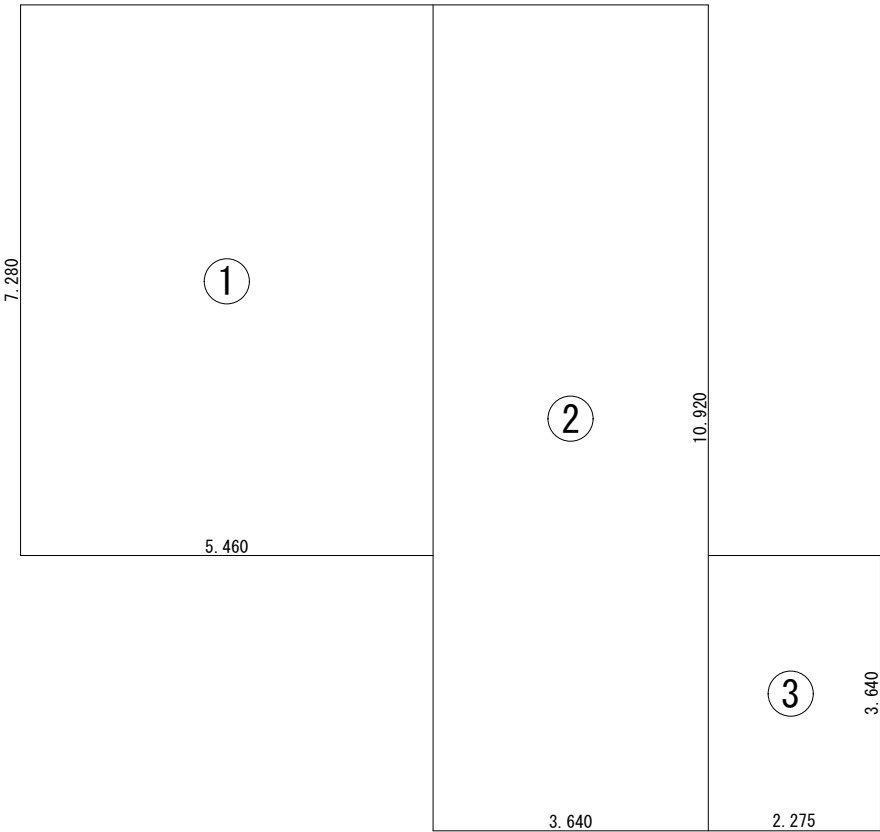


1階床面積図 S=1/100

1階床面積求積表

番号	計算式 (m)	面積 (㎡)
①	5.460 × 7.280	39.7488
②	3.640 × 10.920	39.7488
③	2.275 × 3.640	8.2810
合計 ≡		87.7786 87.77

(26.5坪)

決定図

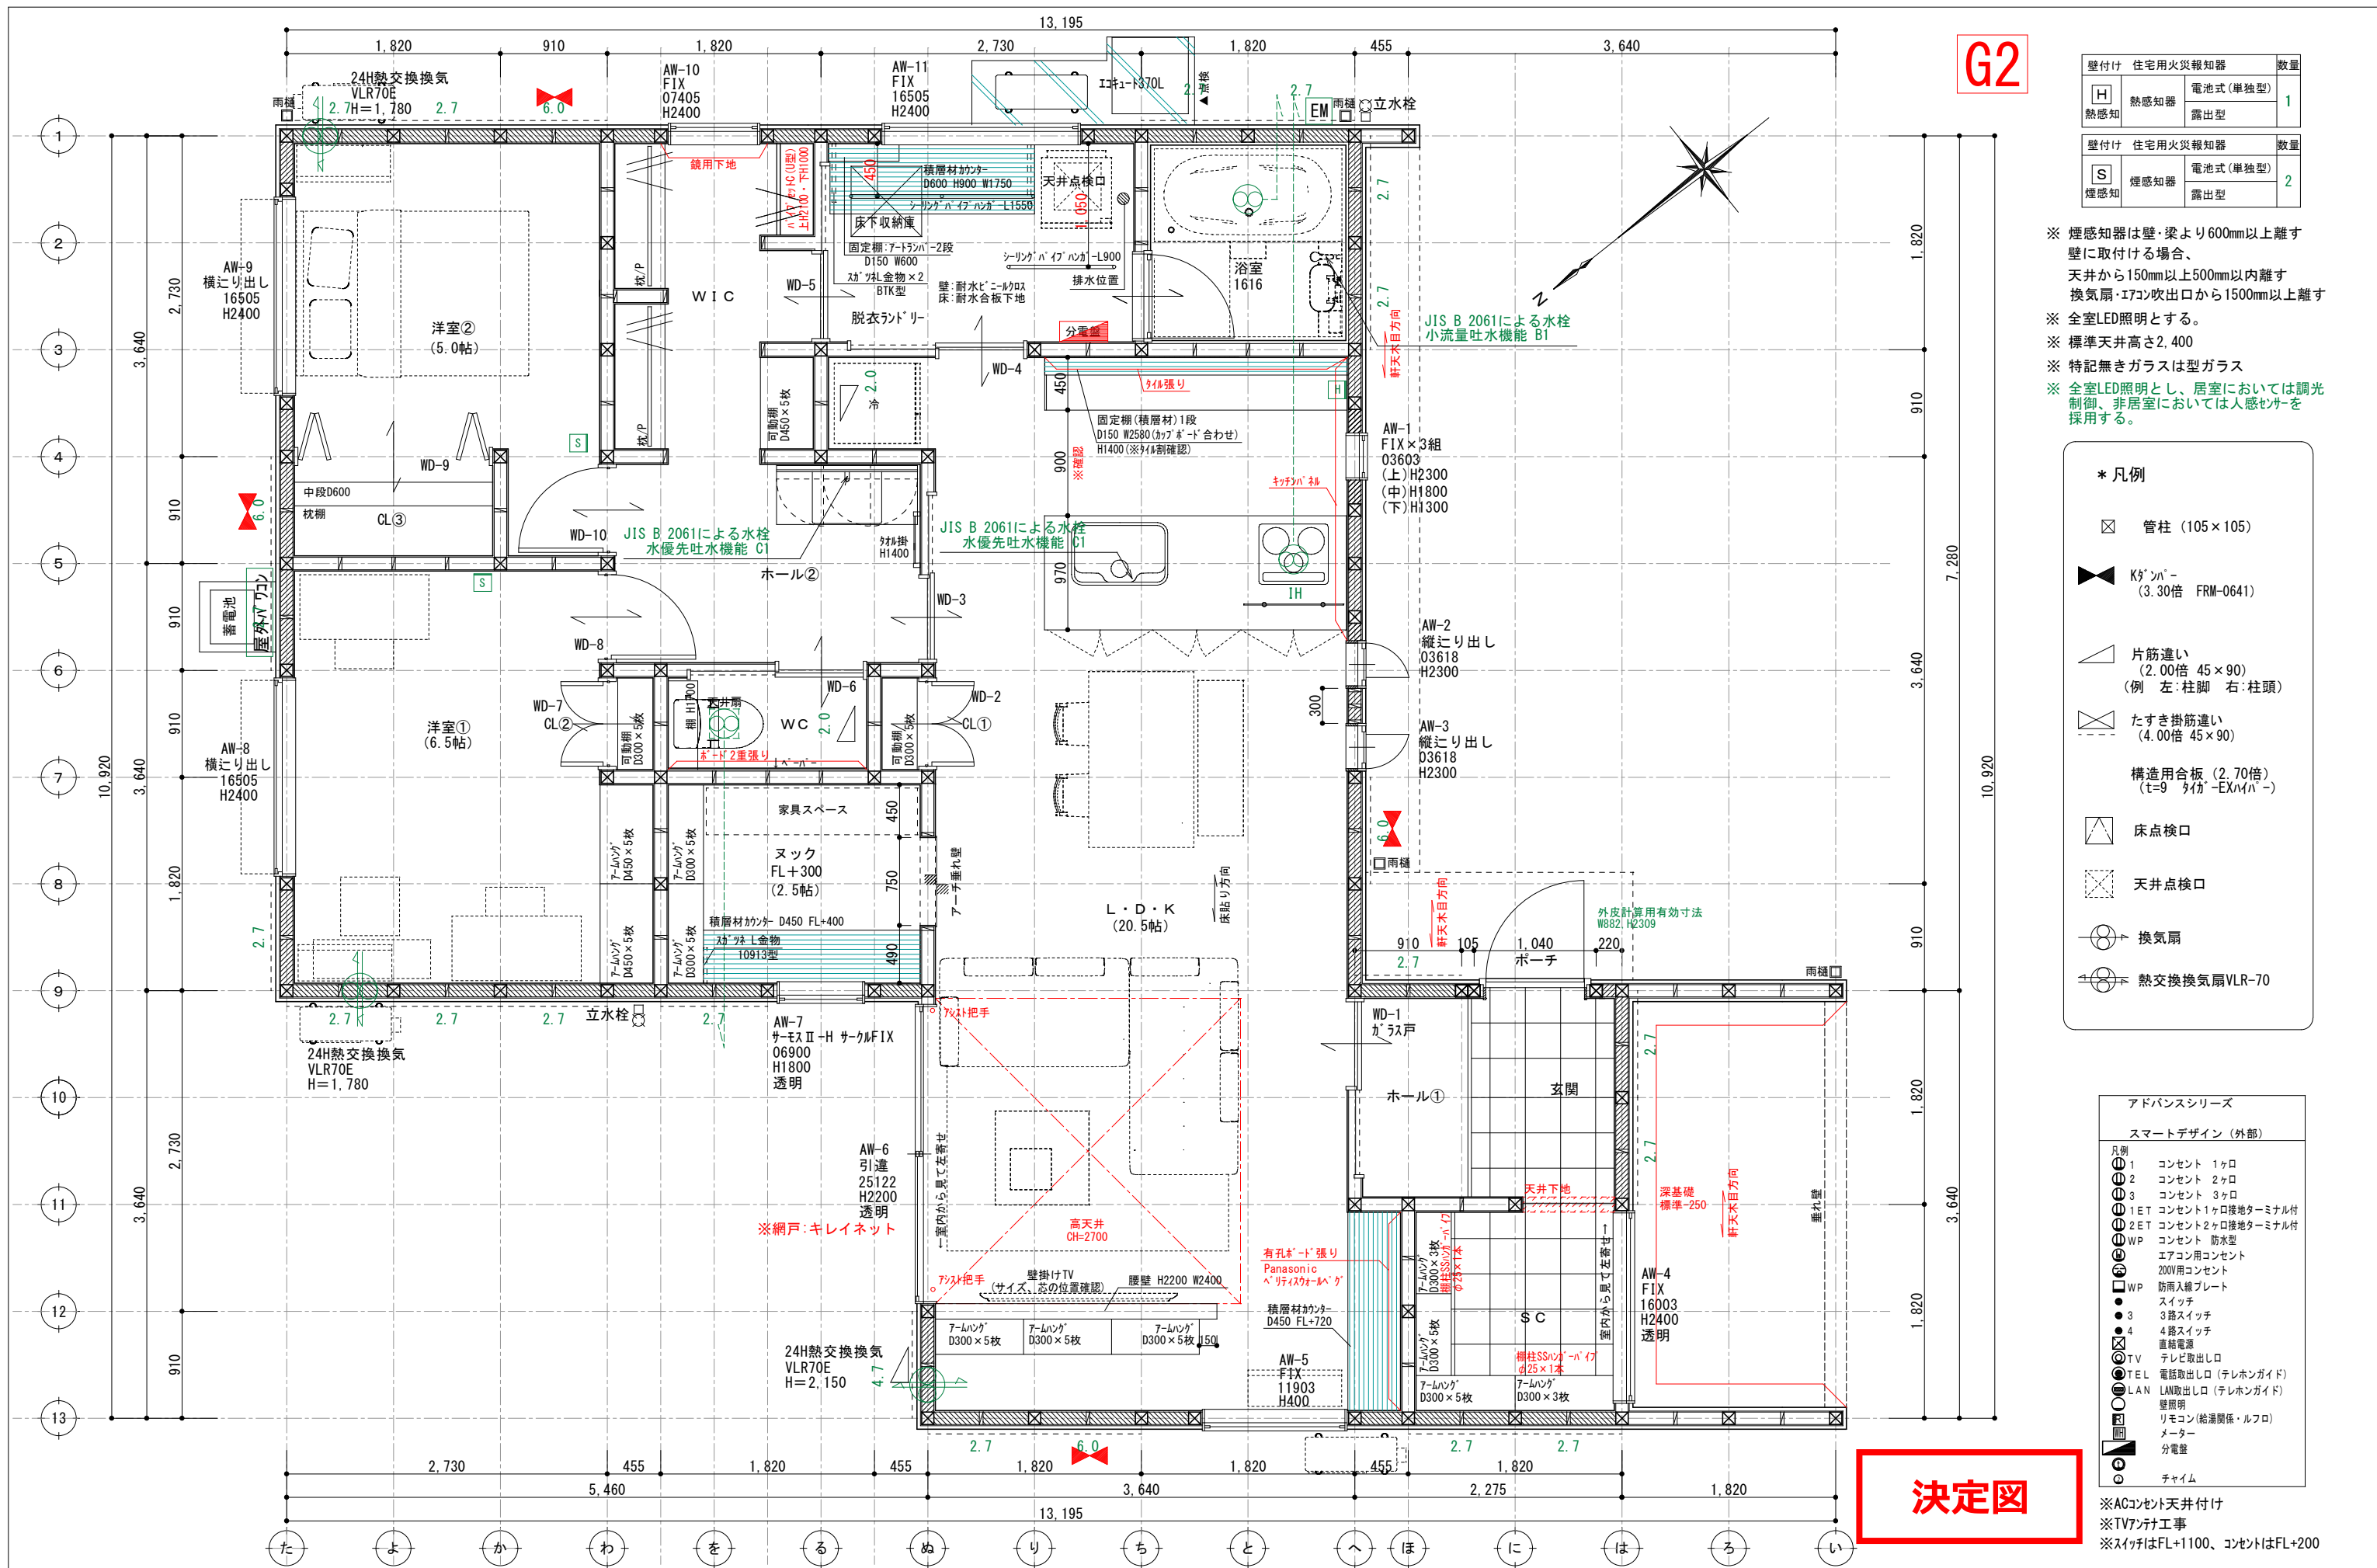

壁付け 住宅用火災報知器			数量
H	熱感知器	電池式(単独型)	1
	熱感知	露出型	
壁付け 住宅用火災報知器			数量
S	煙感知器	電池式(単独型)	2
	煙感知	露出型	

※ 煙感知器は壁・梁より600mm以上離す
壁に取付ける場合、
天井から150mm以上500mm以内離す
換気扇・エアコン吹出口から1500mm以上離す

※ 全室LED照明とする。

※ 標準天井高さ2,400

※ 特記無きガラスは型ガラス

※ 全室LED照明とし、居室においては調光制御、非居室においては人感センサーを採用する。

*** 凡例**

管柱 (105×105)

K's'パネ (3.30倍 FRM-0641)

片筋違い (2.00倍 45×90)
(例 左:柱脚 右:柱頭)

たすき掛筋違い (4.00倍 45×90)

構造用合板 (2.70倍)
(t=9 2枚-EXハイパー)

床点検口

天井点検口

換気扇


熱交換換気扇VLR-70

アドバンスシリーズ		
スマートデザイン (外部)		
凡例	1	コンセント 1ヶロ
②	2	コンセント 2ヶロ
③	3	コンセント 3ヶロ
①ET	1ヶロ	コンセント1ヶロ接地ターミナル付
②ET	2ヶロ	コンセント2ヶロ接地ターミナル付
WP		コンセント 防水型
②		エアコン用コンセント
②		200V用コンセント
WP		防雨入線プレート
②		スイッチ
③		3路スイッチ
④		4路スイッチ
②		直結電源
TV		テレビ取出口
TEL		電話取出口 (テレビホンガイド)
LAN		LAN取出口 (テレビホンガイド)
②		壁照明
②		リモコン (給湯関係・ルフロ)
②		メーター
②		分電盤
②		チャイム

※ACコンセント天井付け

※TVアンテナ工事


※スイッチはFL+1100、コンセントはFL+200

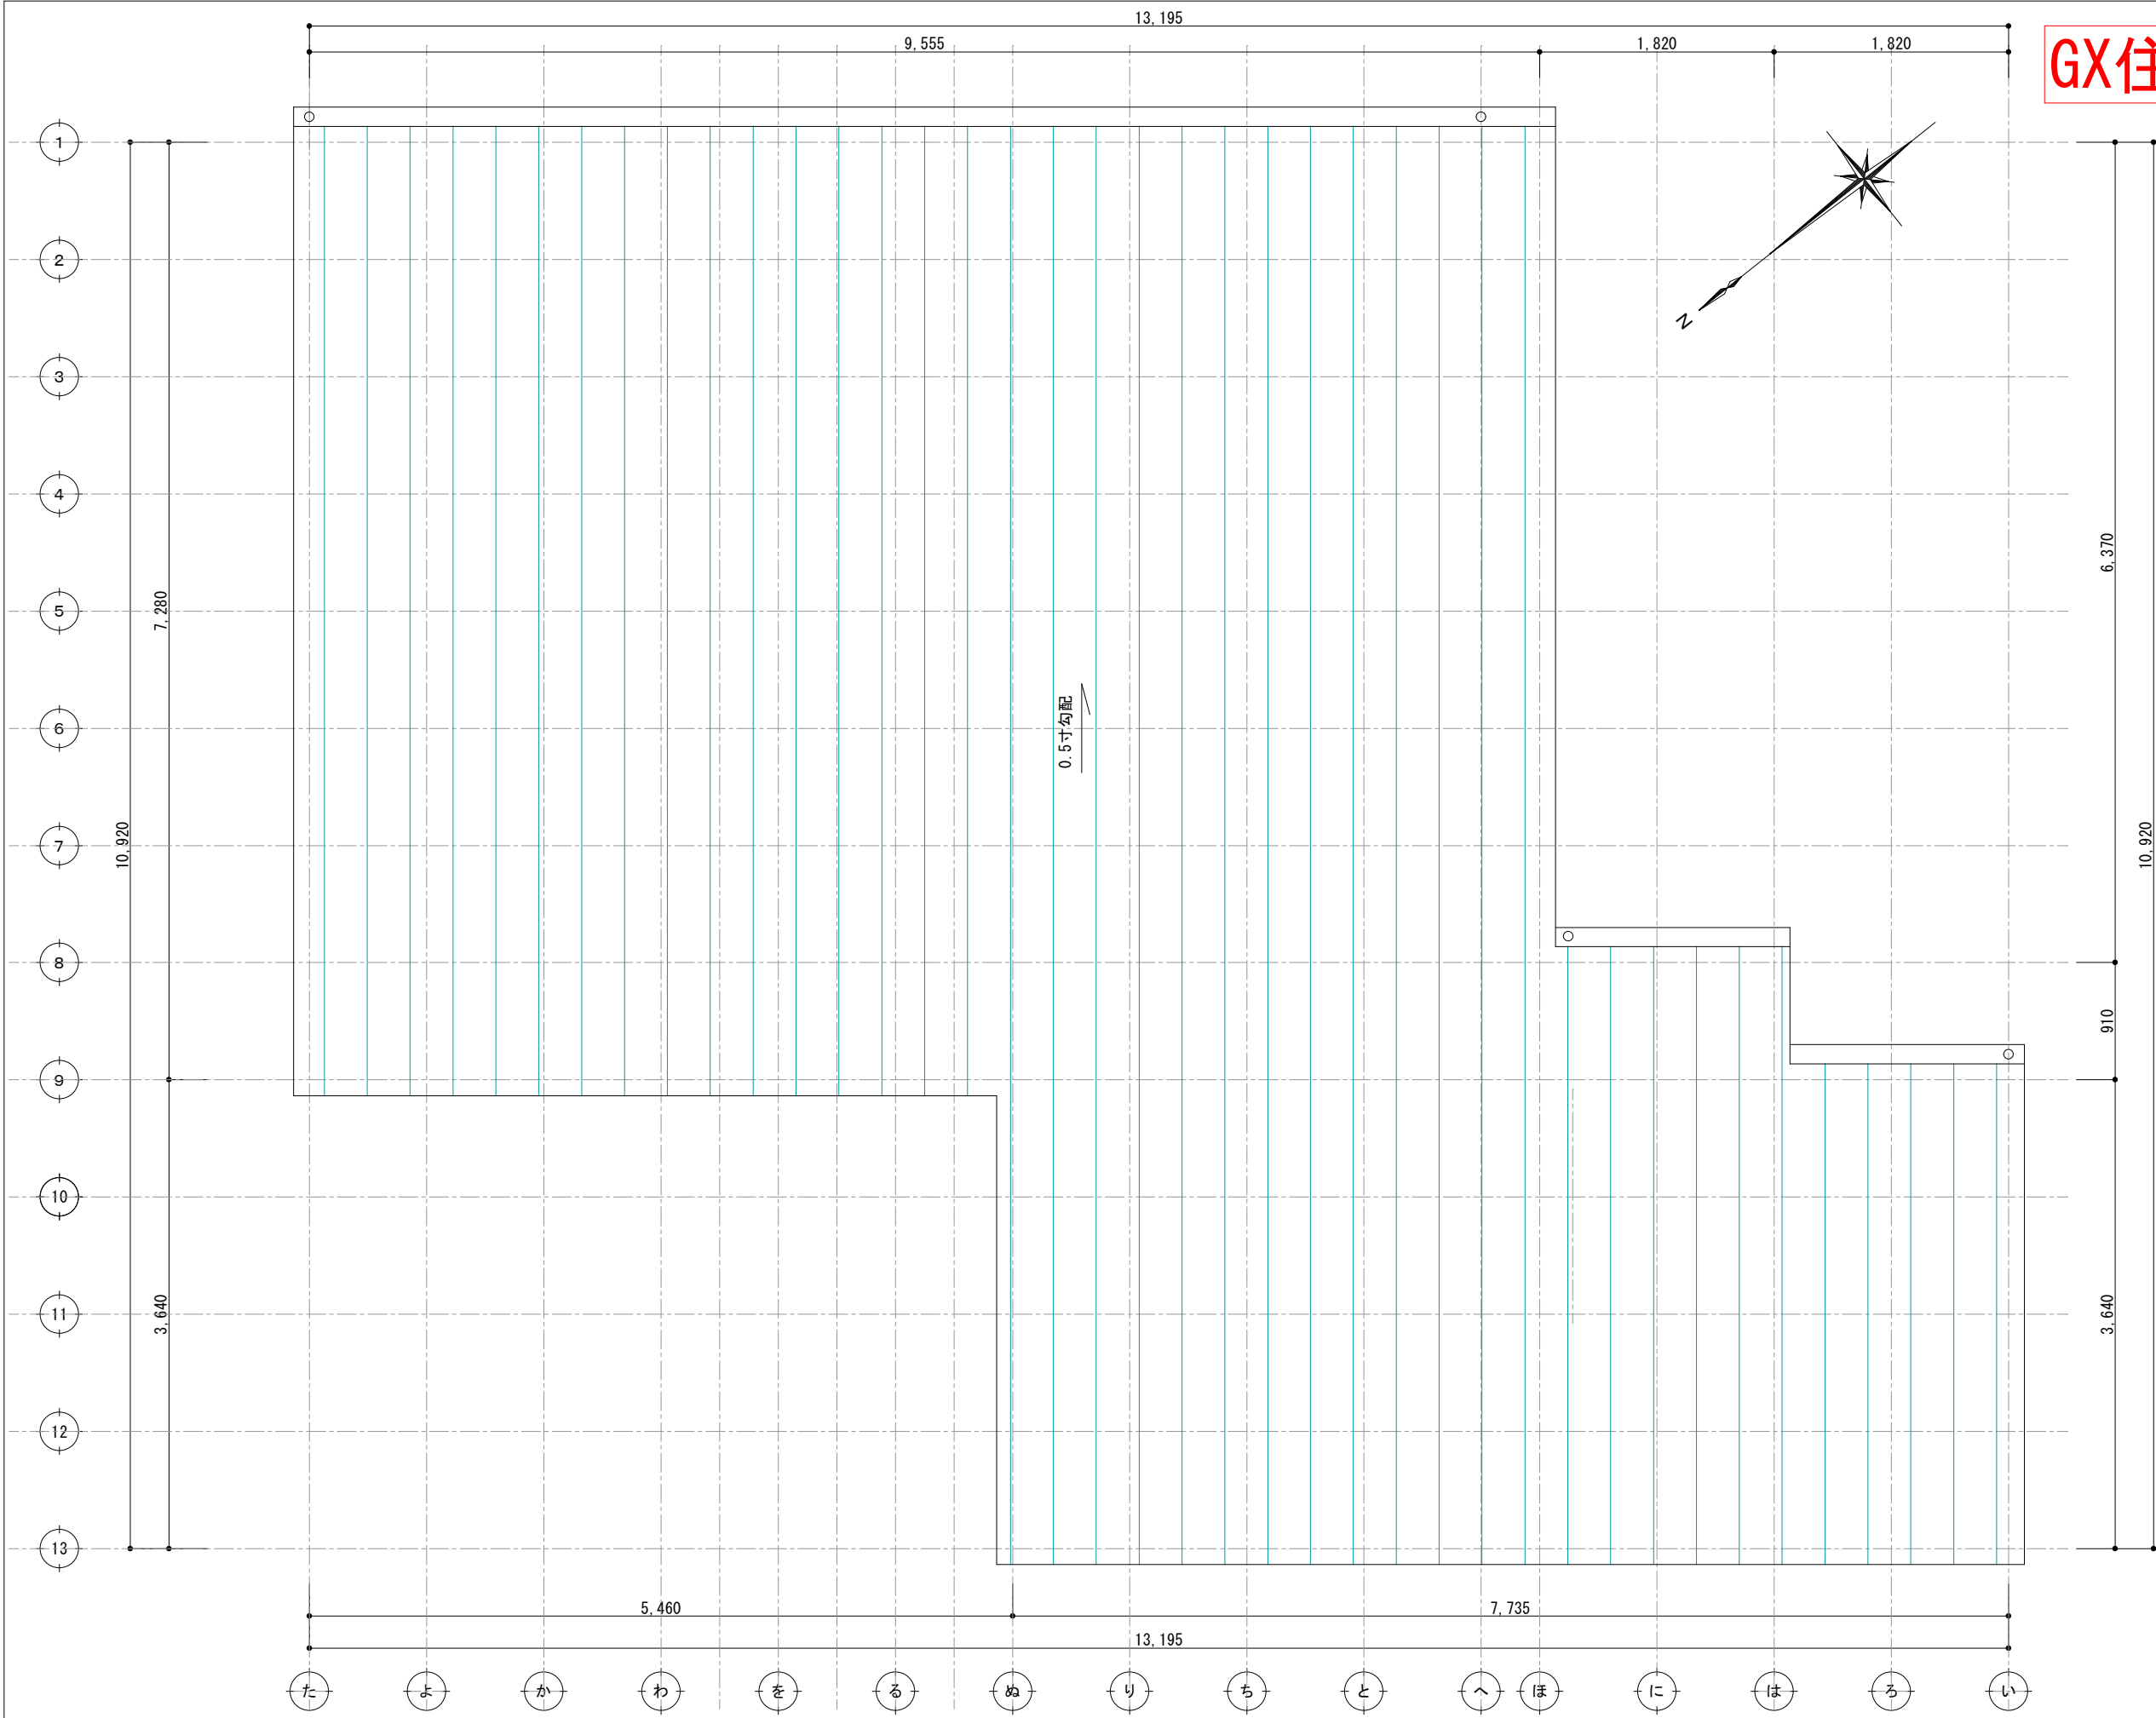

GX住宅 (Cube J付)
太陽光あり


決定図

訂正	浜岡一級総合設計事務所 一級建築士事務所 静岡県知事登録第 (10)2441 号 一級建築士 大臣登録第 365879 号 西原利昌	 ピージーハウス	株式会社 LIFEFUND InDesign office 一級建築士事務所 事務所登録 (2) 第7595号 一級建築士登録 第179770号 鈴木 達男 〒432-8023 静岡県浜松市中央区鴨江3丁目70番23号	2026. 3. 1	図名 小林大樹様邸 新築工事 屋根伏図		設計	IC	工事	図番
				縮尺 1/50			角谷		青島	3-3

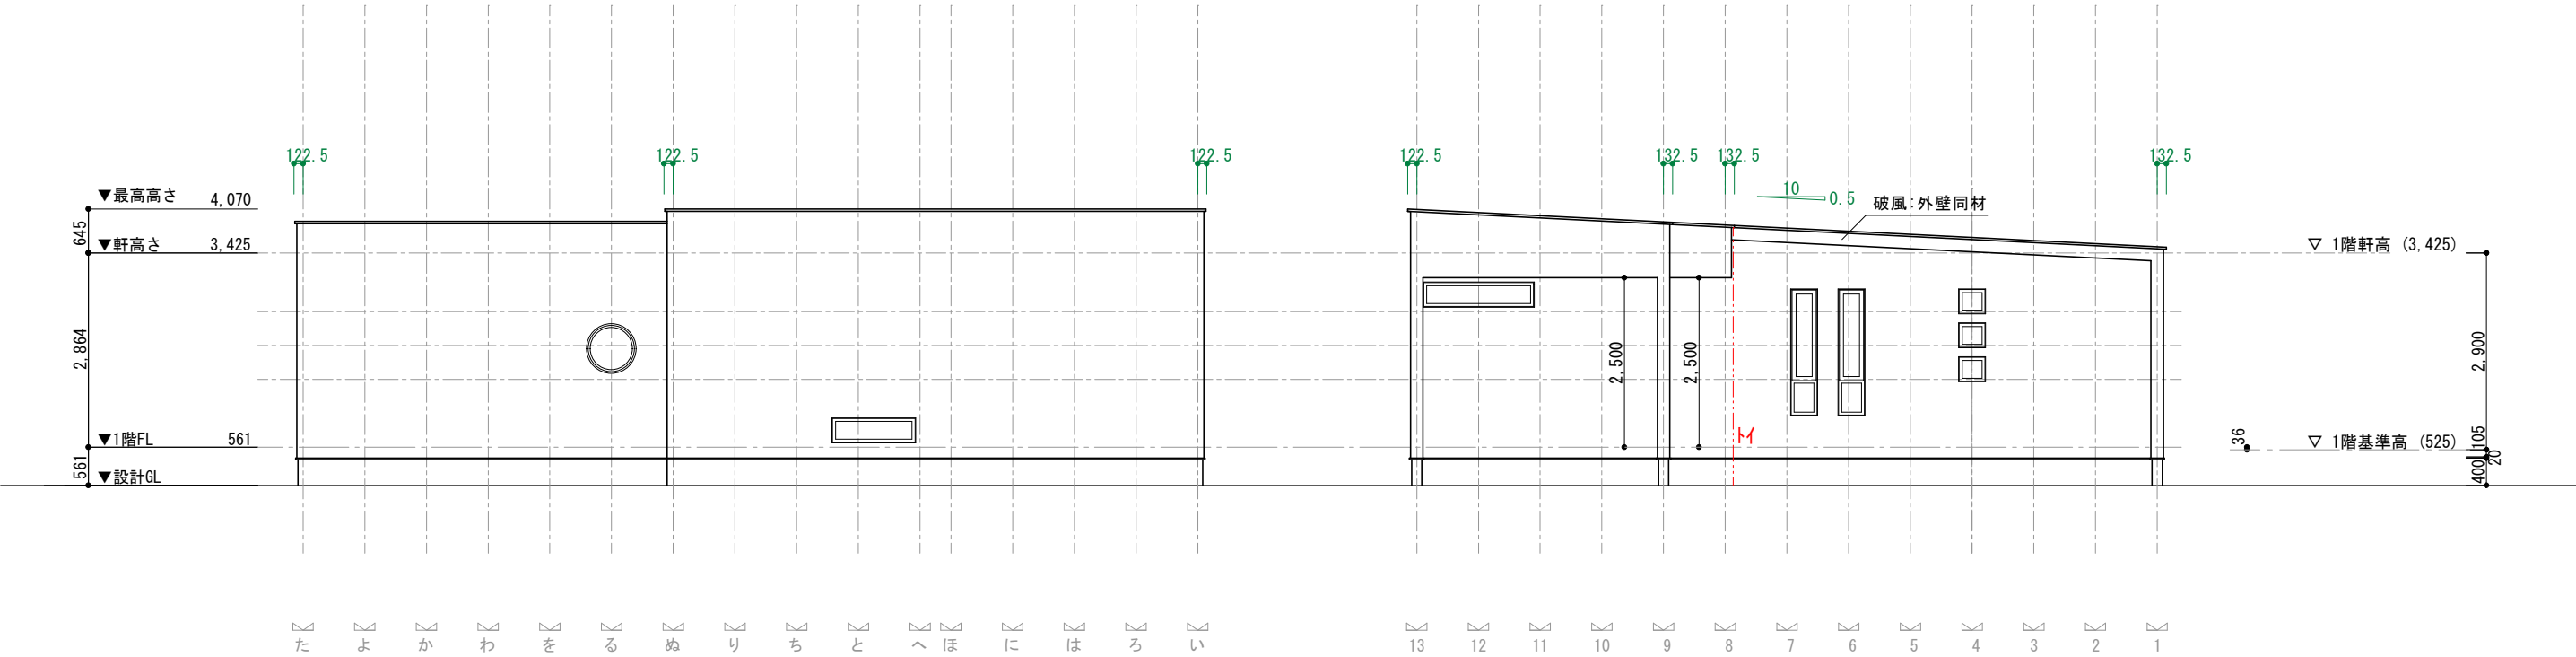

西側立面図 S=1/100

南側立面図 S=1/100

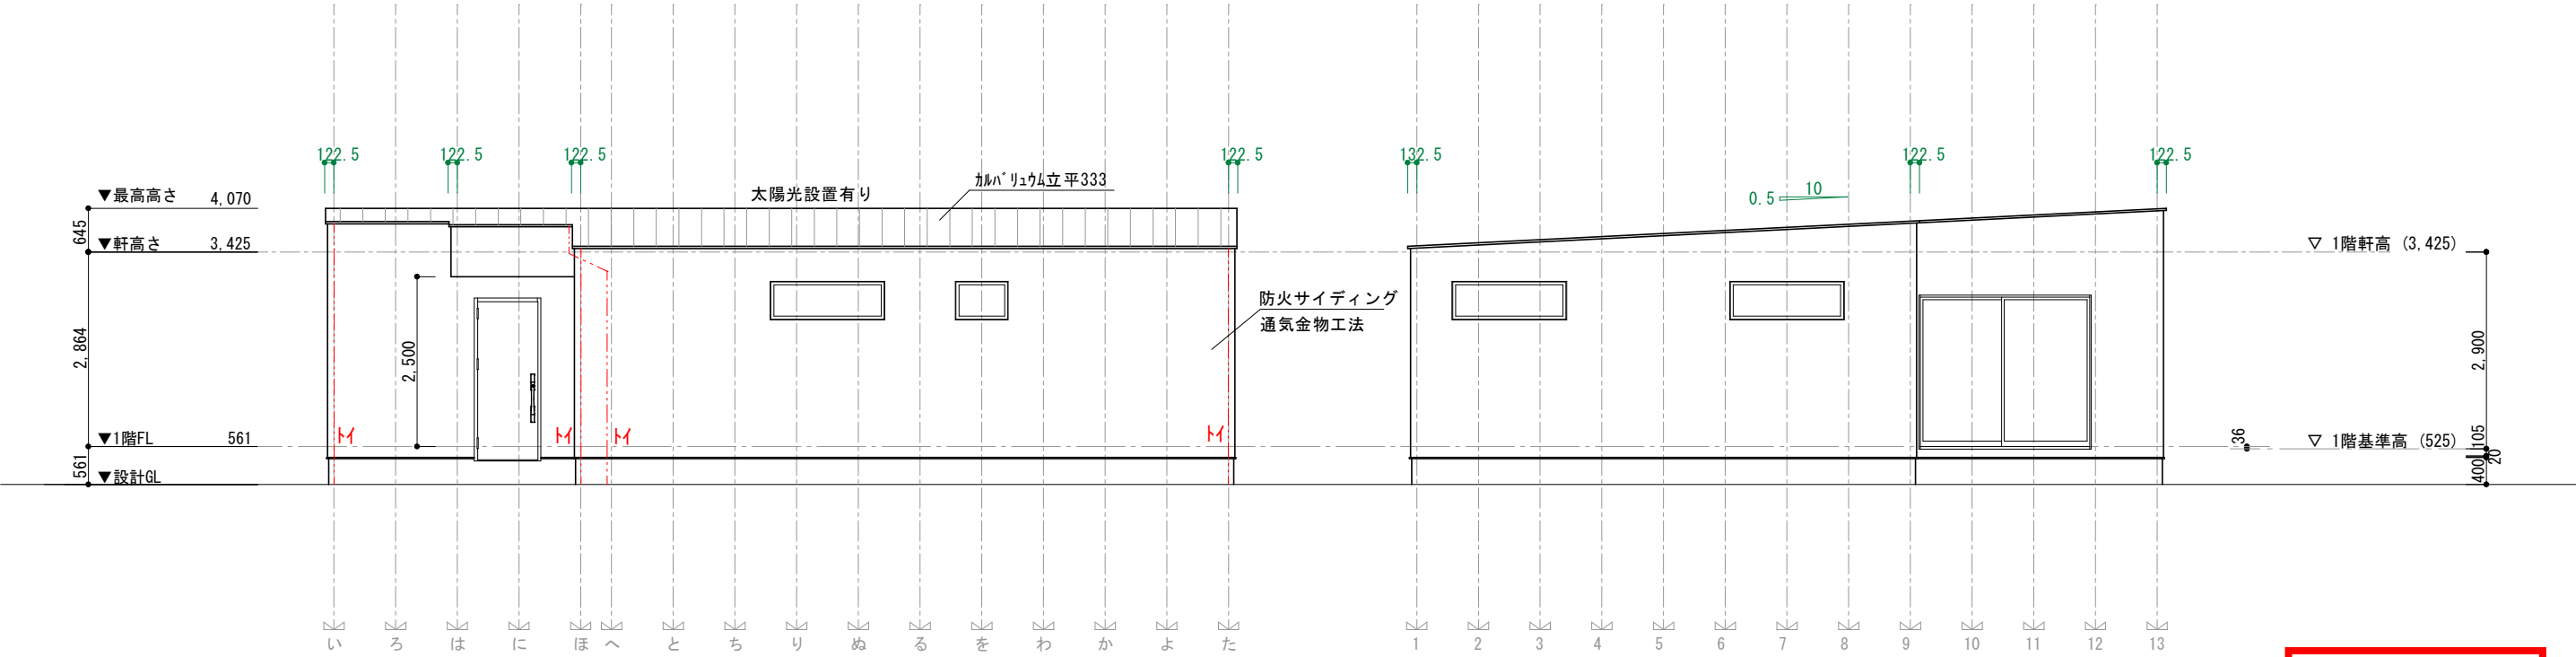




東側立面図 S=1/100

北側立面図 S=1/100

決定図




訂 正	浜 岡 一 級 総 合 設 計 事 務 所 一級建築士事務所 静岡県知事登録第 (10)2441 号 一級建築士 大臣登録第 365879 号 西原利昌	 PG HOUSE ピージーハウス	株式会社 LIFEFUND InDesign office 一級建築士事務所 事務所登録 (2) 第7595号 一級建築士登録 第179770号 鈴木 達男 〒432-8023 静岡県浜松市中央区鴨江3丁目70番23号	年 月 日 2026. 3. 1	件 名 小林大樹様 邸新築工事	設計 角谷	IC	工事 青島	図 番 5
				縮 尺 1/30	図 名 矩計図				

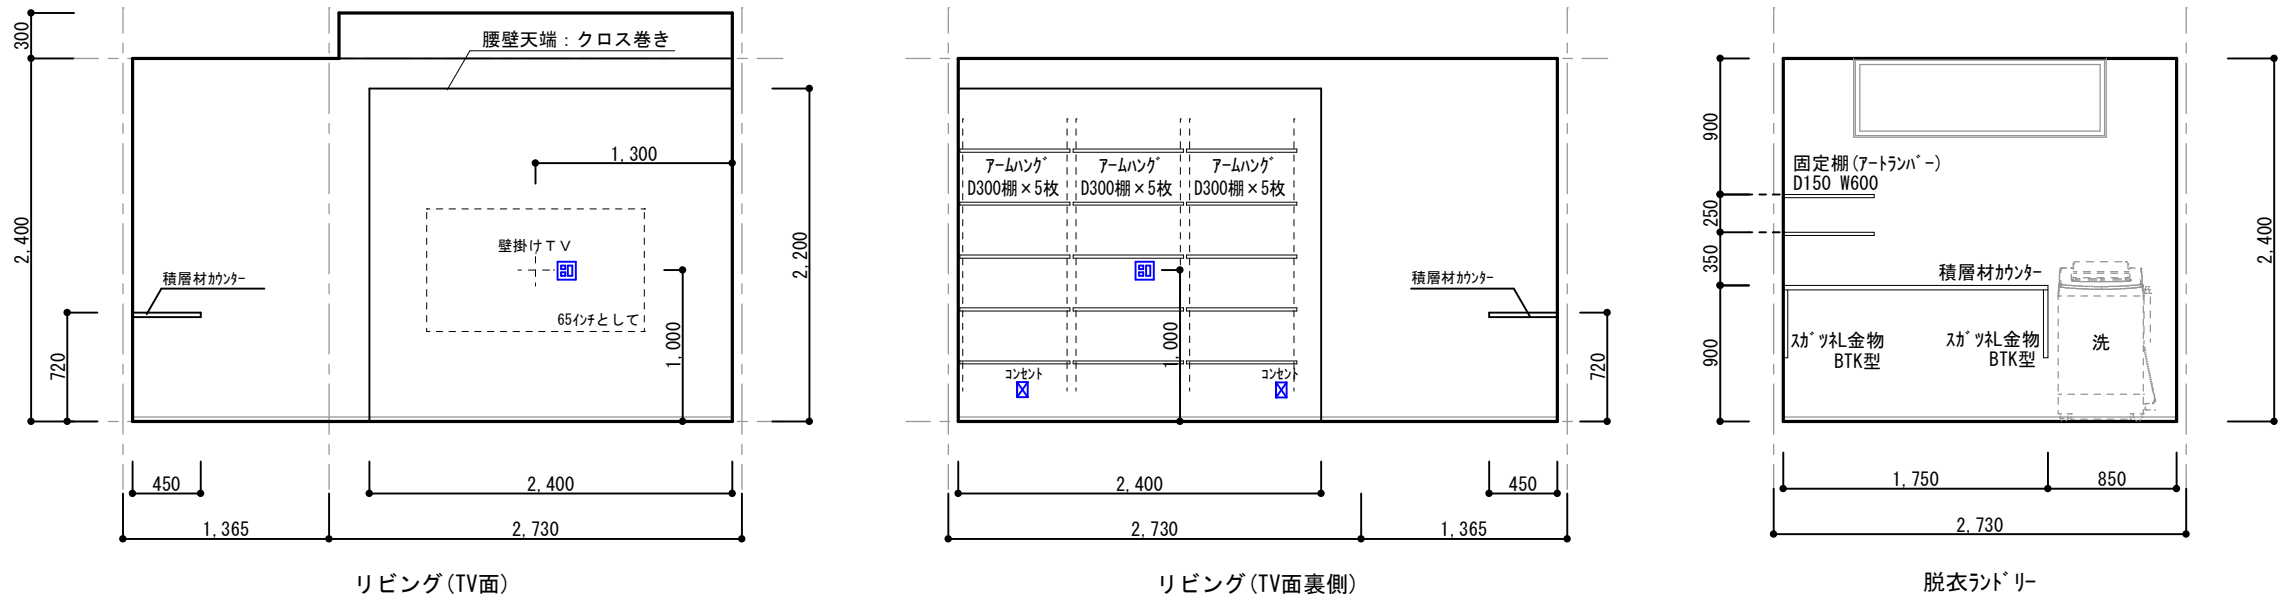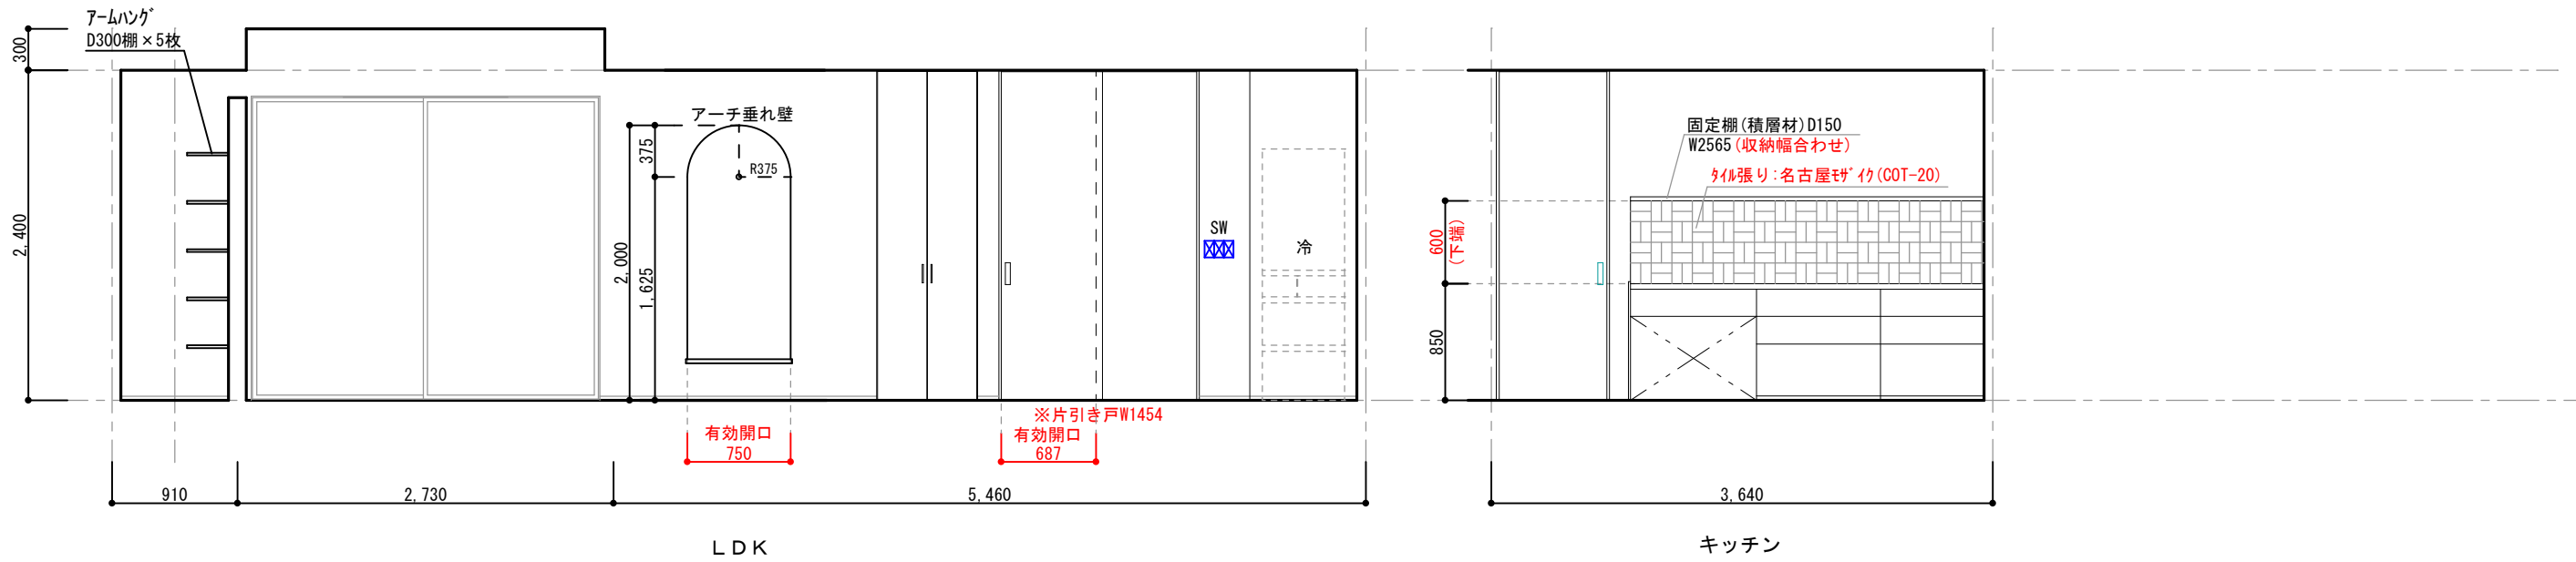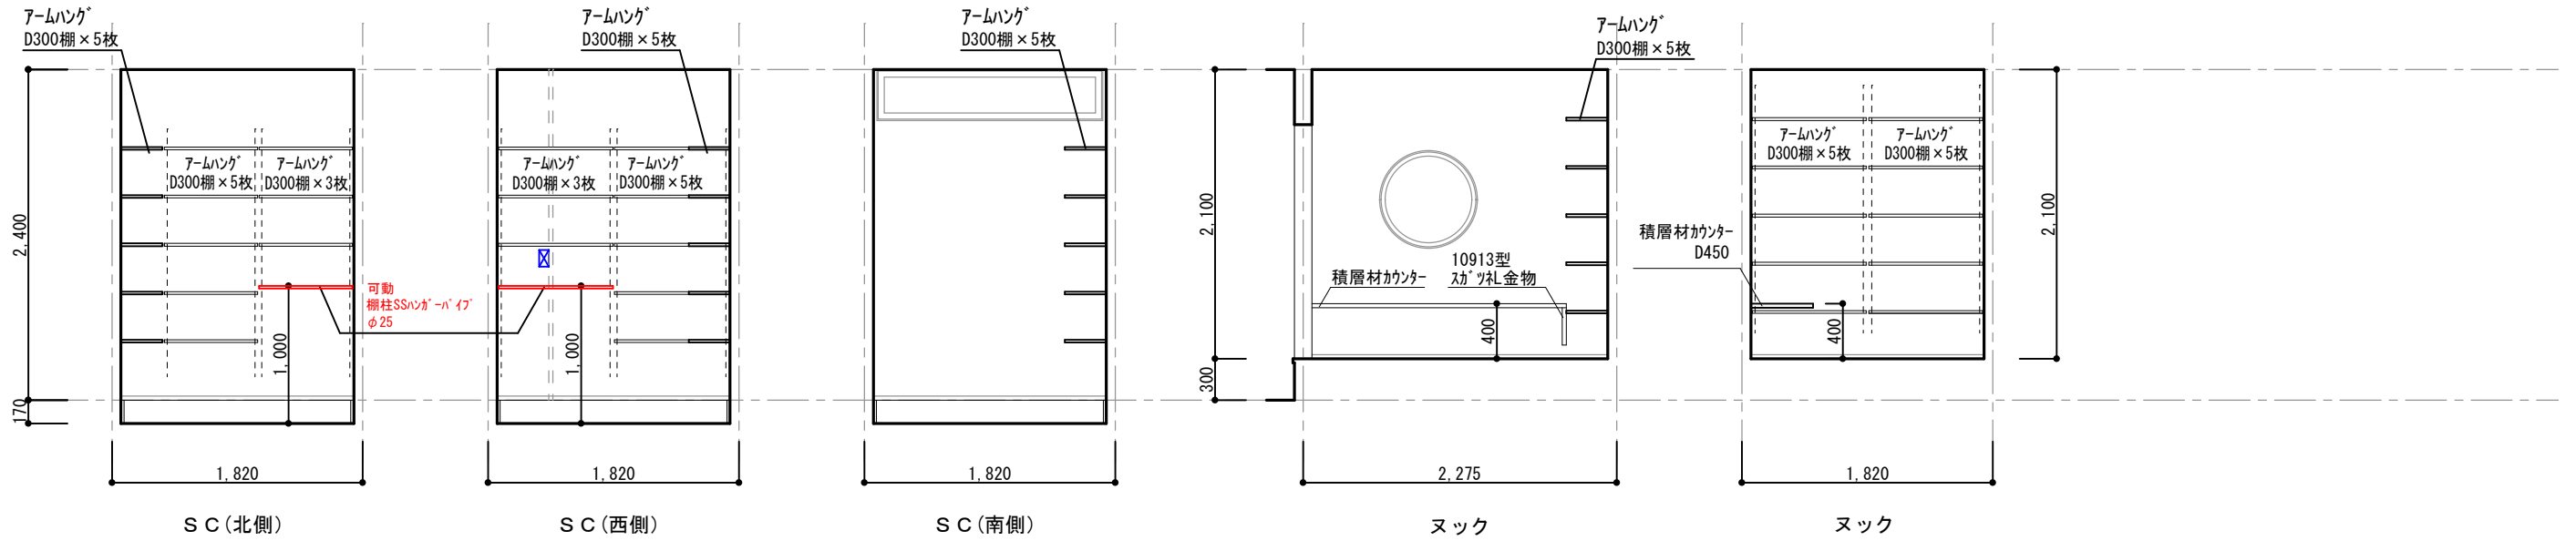


決定図


訂正	浜岡一級総合設計事務所 一級建築士事務所 静岡県知事登録第 (10)2441 号 一級建築士 大臣登録第 365879 号 西原利昌	LIFEFUND PG HOUSE	株式会社 LIFEFUND InDesign office 一級建築士事務所 事務所登録 (2) 第7595号 一級建築士登録 第179770号 鈴木 達男 〒432-8023 静岡県浜松市中央区鶴江3丁目70番23号	年月日 2026.3.1	件名 小林大樹様 新築工事	設計 IC 工事 青島	図番 6-1
				縮尺 1/50	図名 展開図-1		

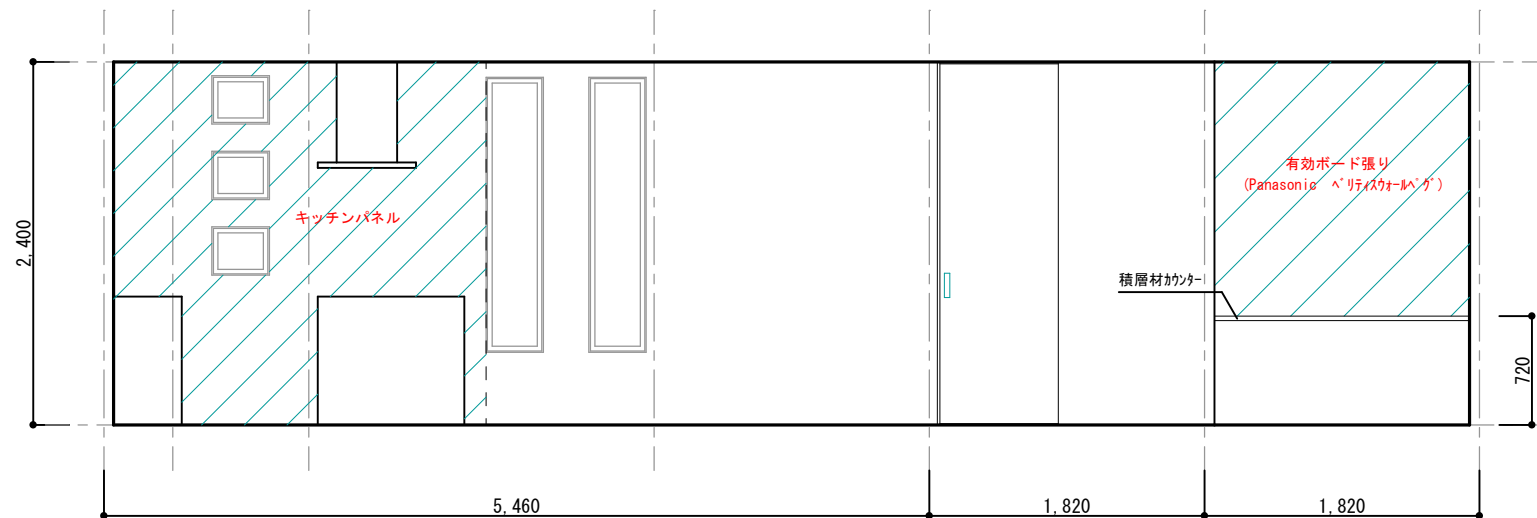


LDK

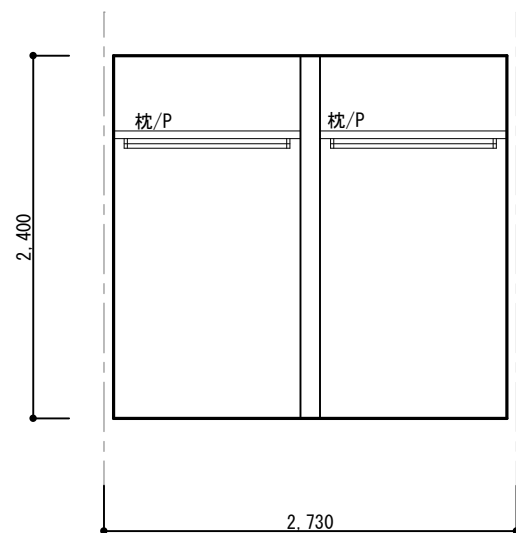

WIC

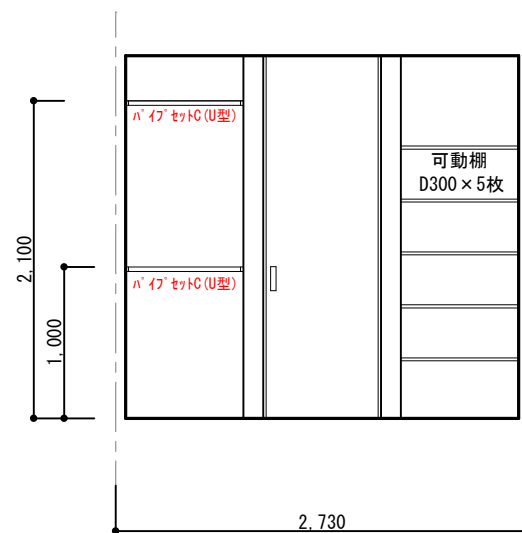


WIC

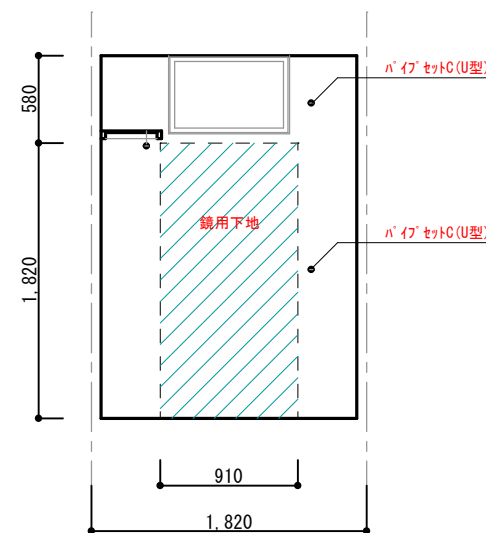

WIC

決定図

訂正	浜岡一級総合設計事務所 一級建築士事務所 静岡県知事登録第(10)2441号 一級建築士 大臣登録第 365879号 西原利昌	LIFEFUND PG HOUSE	株式会社 LIFEFUND InDesign office 一級建築士事務所 事務所登録(2)第7595号 一級建築士登録 第179770号 鈴木 達男 〒432-8023 静岡県浜松市中央区鴨江3丁目70番23号	年月日 2026.3.1	件名 小林大樹様 新築工事		設計	IC	工事	図番
				縮尺 1/50	図名 展開図-2		角谷		青島	6-2

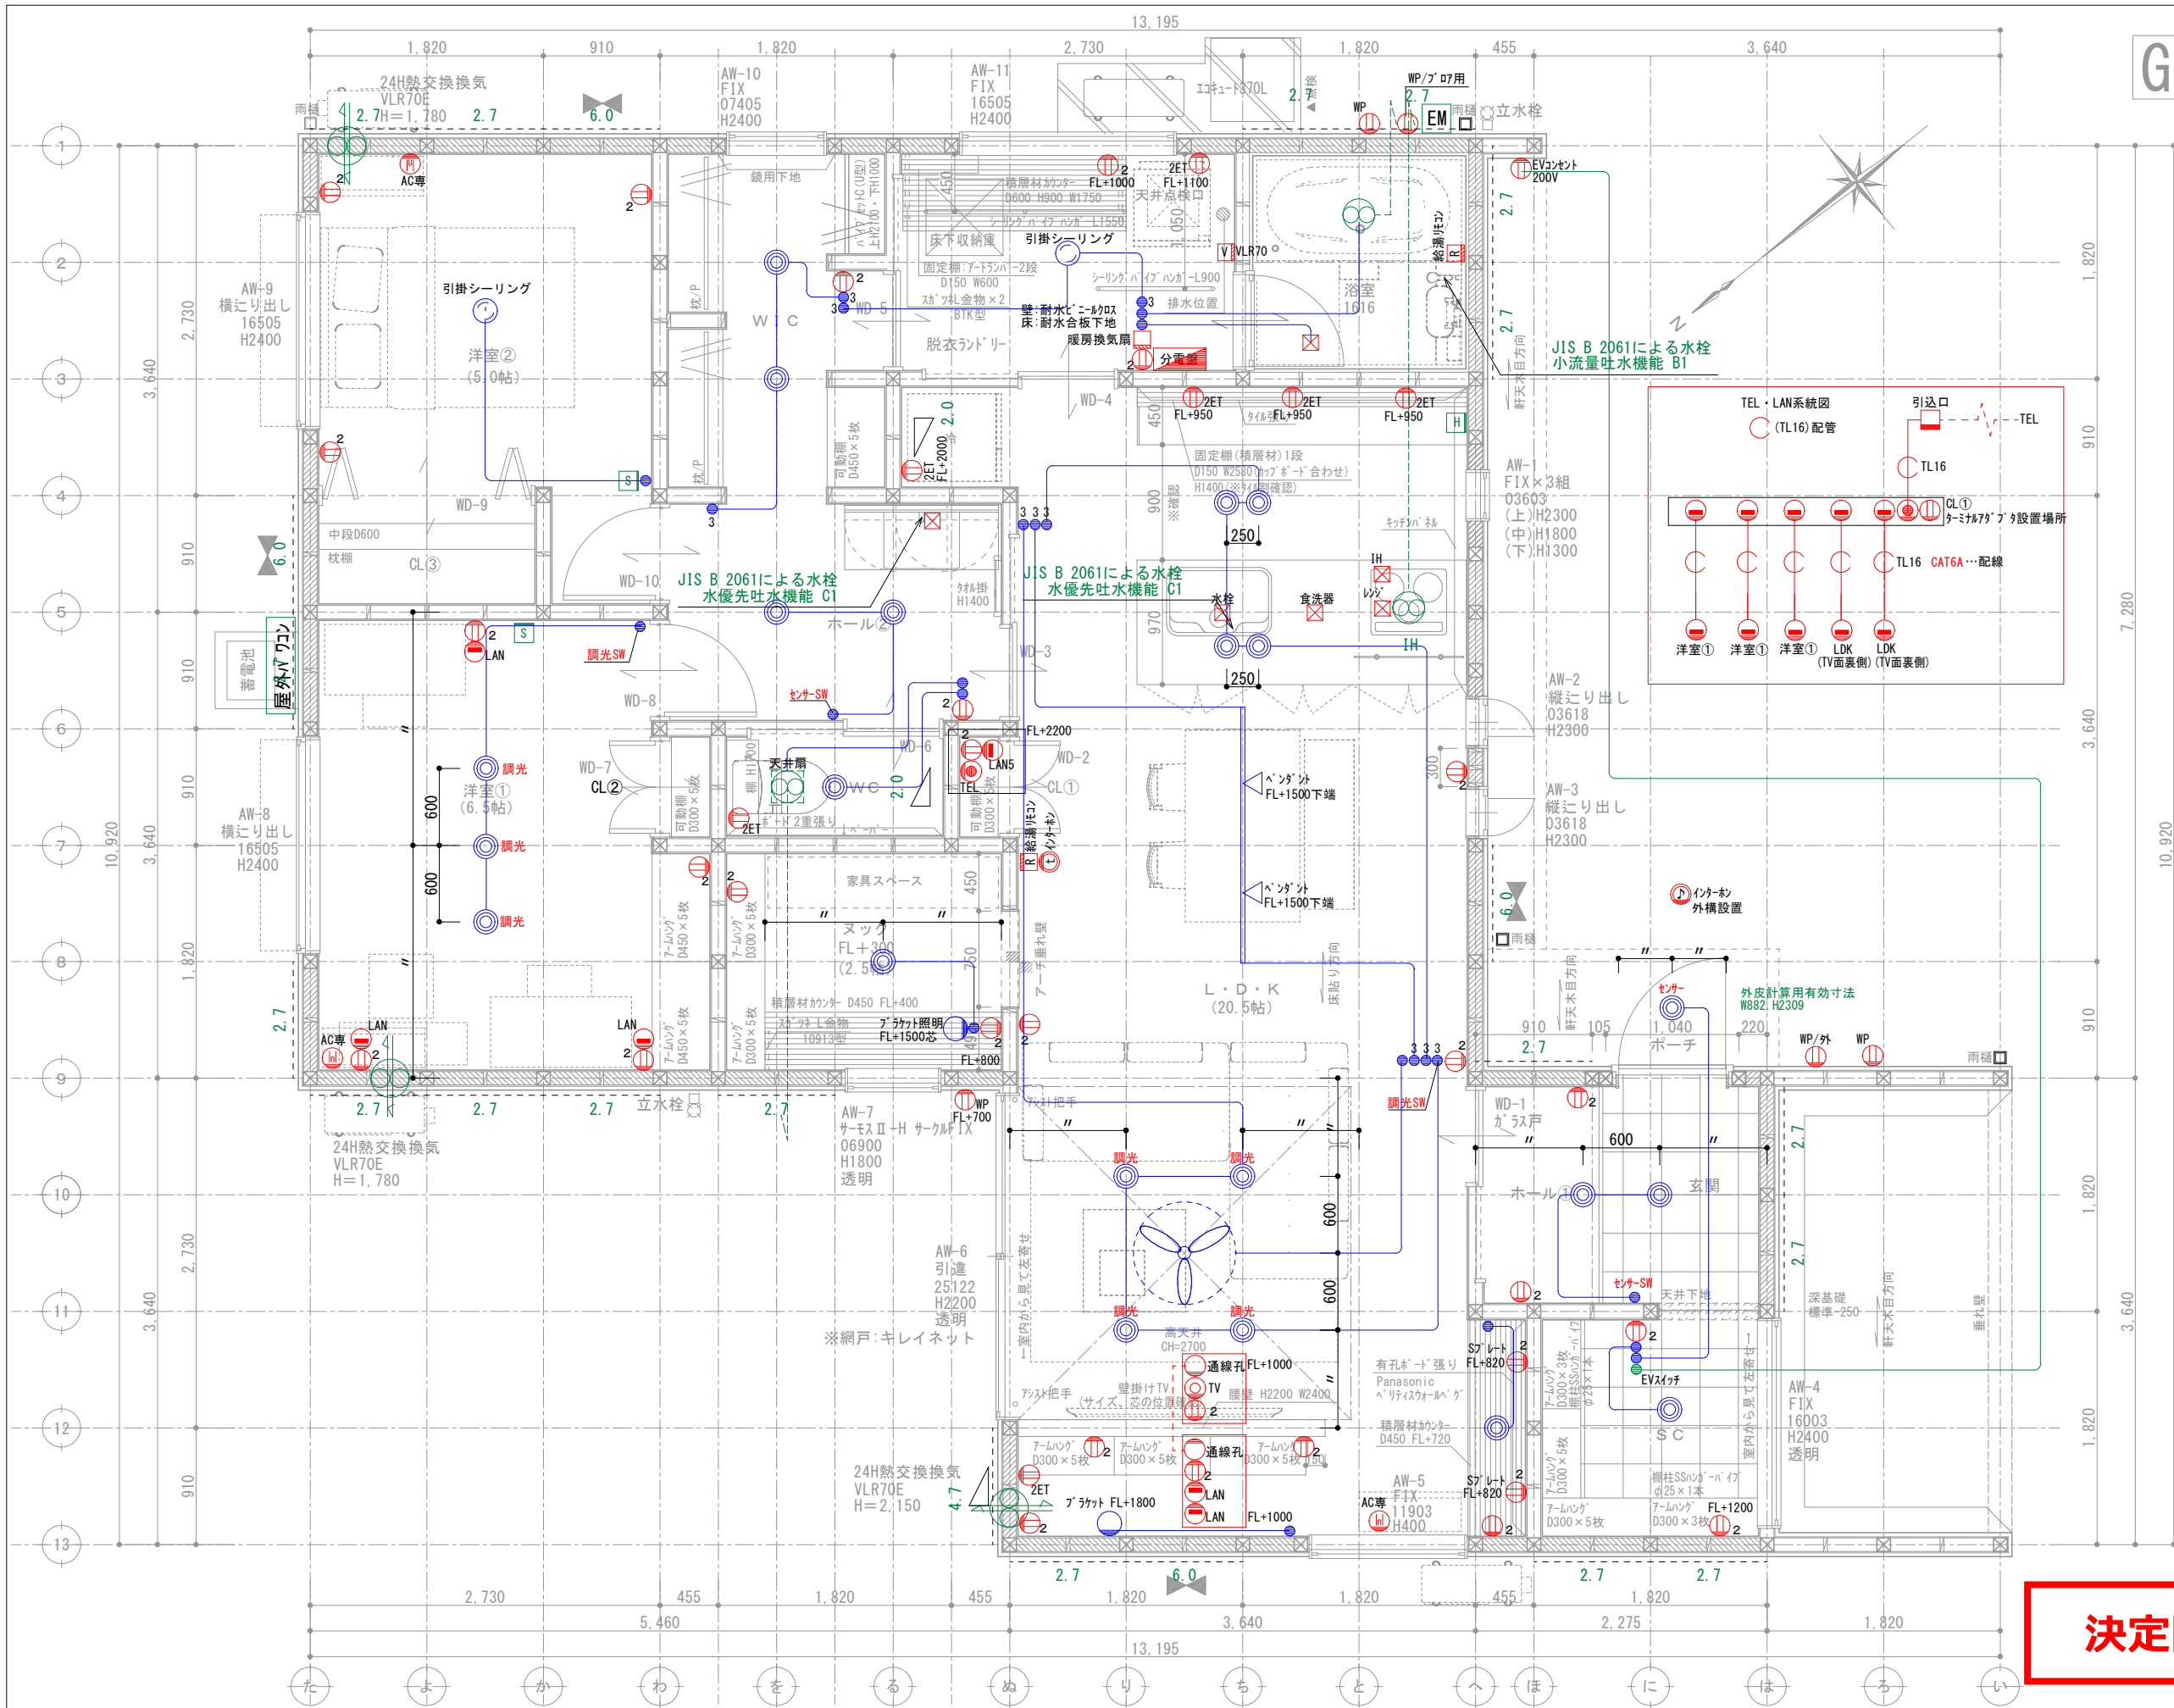

G2

壁付付 住宅用火災報知器			数量
H 熱感知	熱感知器	電池式(単独型)	1
		露出型	
壁付付 住宅用火災報知器			数量
S 煙感知	煙感知器	電池式(単独型)	2
		露出型	

※ 煙感知器は壁・梁より600mm以上離す
壁に取付ける場合、
天井から150mm以上500mm以内離す
換気扇・エアコン吹出口から1500mm以上離す

※ 全室LED照明とする。

※ 標準天井高さ2,400

※ 特記無きガラスは型ガラス

※ 全室LED照明とし、居室においては調光制御、非居室においては人感センサーを採用する。


*** 凡例**

- 管柱 (105×105)
- K's'パネ (3.30倍 FRM-0641)
- 片筋違い (2.00倍 45×90)
(例 左:柱脚 右:柱頭)
- たすき掛筋違い (4.00倍 45×90)
- 構造用合板 (2.70倍)
(t=9 材種=EXハイバー)
- 床点検口
- 天井点検口
- 換気扇
- 熱交換換気扇VLR-70

アドバンスシリーズ	
スマートデザイン (外部)	
凡例	
①	コンセント 1ヶ所
②	コンセント 2ヶ所
③	コンセント 3ヶ所
①ET	コンセント1ヶ所接地ターミナル付
②ET	コンセント2ヶ所接地ターミナル付
③ET	コンセント3ヶ所接地ターミナル付
WP	防水型
EA	エアコン用コンセント
200V	200V用コンセント
WP	防雨入線プレート
スイッチ	スイッチ
③	3路スイッチ
④	4路スイッチ
直結電源	直結電源
TV	テレビ取出口
TEL	電話取出口 (テレホンガイド)
LAN	LAN取出口 (テレホンガイド)
壁照明	壁照明
リモコン	リモコン (給湯関係・ルフロ)
メーター	メーター
分電盤	分電盤
①	チャーム

※ACコンセント天井付け
※TVアンテナ工事
※スイッチはFL+1100、コンセントはFL+200

決定図

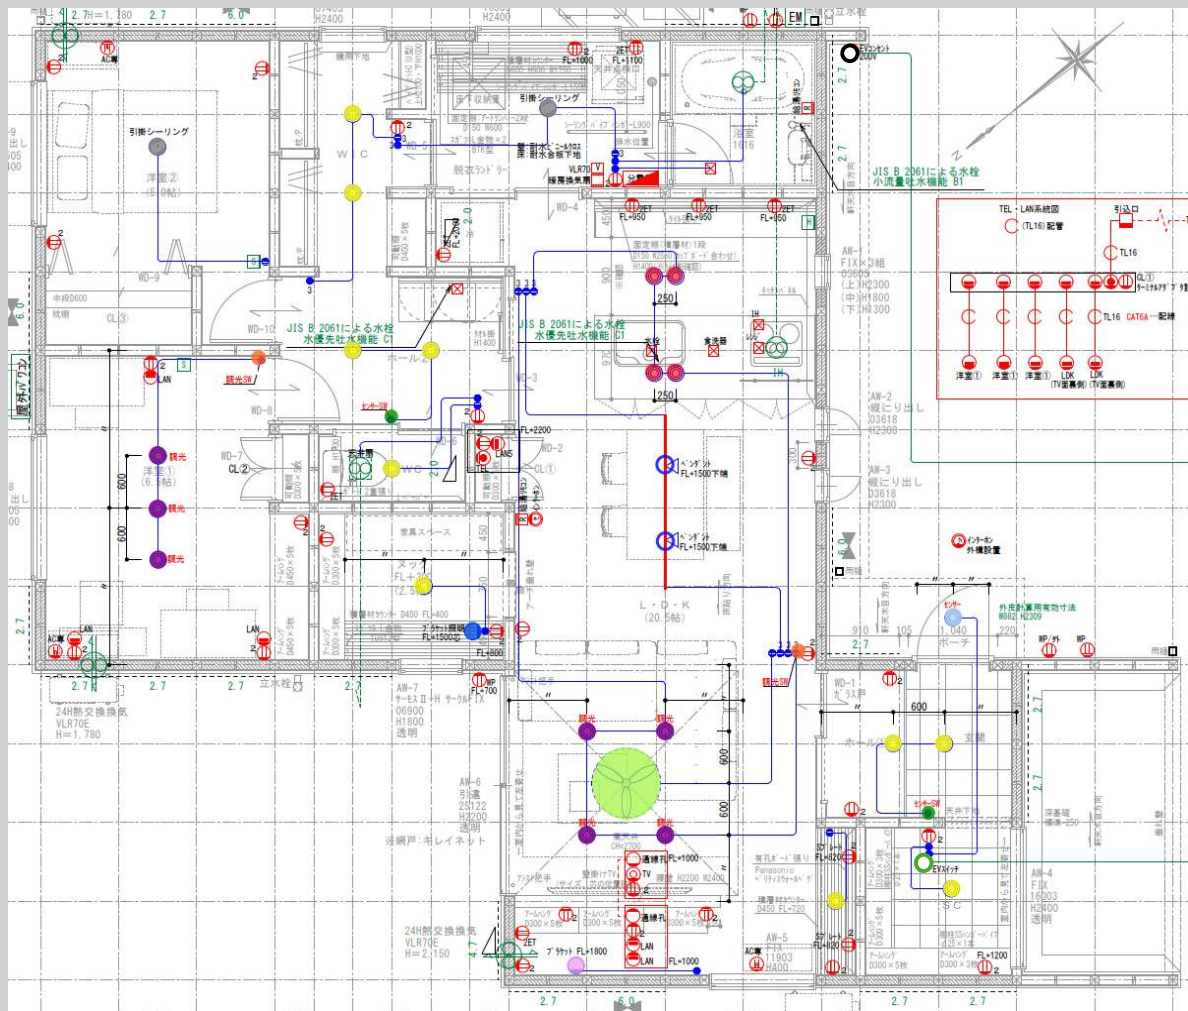

ポーチ灯

● × 1

センサー付きダウナイト

DDL_6259YW

基本照明ダウナイト

● × 10

DDL_6132AW

LDK・洋室①

● × 7

調光ダウナイト

DBK_39359A

キッチン

● × 4

ダウナイト

DDL_6134AW

ダイニング

○ × 2

ペンダントライト

DPN-41592G

ダイニング

— × 1

ダクトレール

DP-00292W

テレビ裏バックヤード

● × 1

ブラケット

DBK_39359A

ヌック

● × 1

スポットライト

DBK_42022AG

玄関・ホール②

● × 2

センサー-SW

WTA_14119W

LDK・洋室①

● × 2

調光SW

WTA_57583WK

LDK

● × 1

シーリングファン

DP-41996

EVスイッチ：アドバンス

○ × 1

マットホワイト

WTA52631WK01



WTA52631WK01

希望小売価格 3,670円(税抜)

※掲載の価格には消費税は含まれていません。

アドバンスシリーズ 埋込「入」「切」表示スイッチセット (両切・20A) (シングル用) (EVロゴマーク表示) (マットホワイト)

プレート別売

WTA7101WK

希望小売価格 350円(税抜)

※掲載の価格には消費税は含まれていません。

アドバンスシリーズ スイッチプレート(1連用) (マットホワイト)

EVコンセント

○ × 1

ホワイトシルバー

WK4322S



WK4322S

希望小売価格 6,050円(税抜)

※掲載の価格には消費税は含まれていません。

EV・PHEV充電用 15A・20A兼用接地屋外コンセント (露出・埋込両用) (200V用) (ホワイトシルバー)

ドアホン：VL-SE31XL(Panasonic)



内部SW：アドバンス

マットホワイト



外部：スマートデザインシリーズ

ホワイトシルバー



エコキュートリモコン







24時間換気 VLR-70



引っ掛けシーリング

● × 2

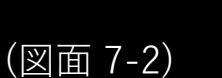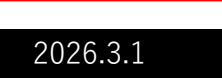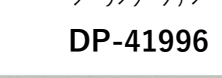

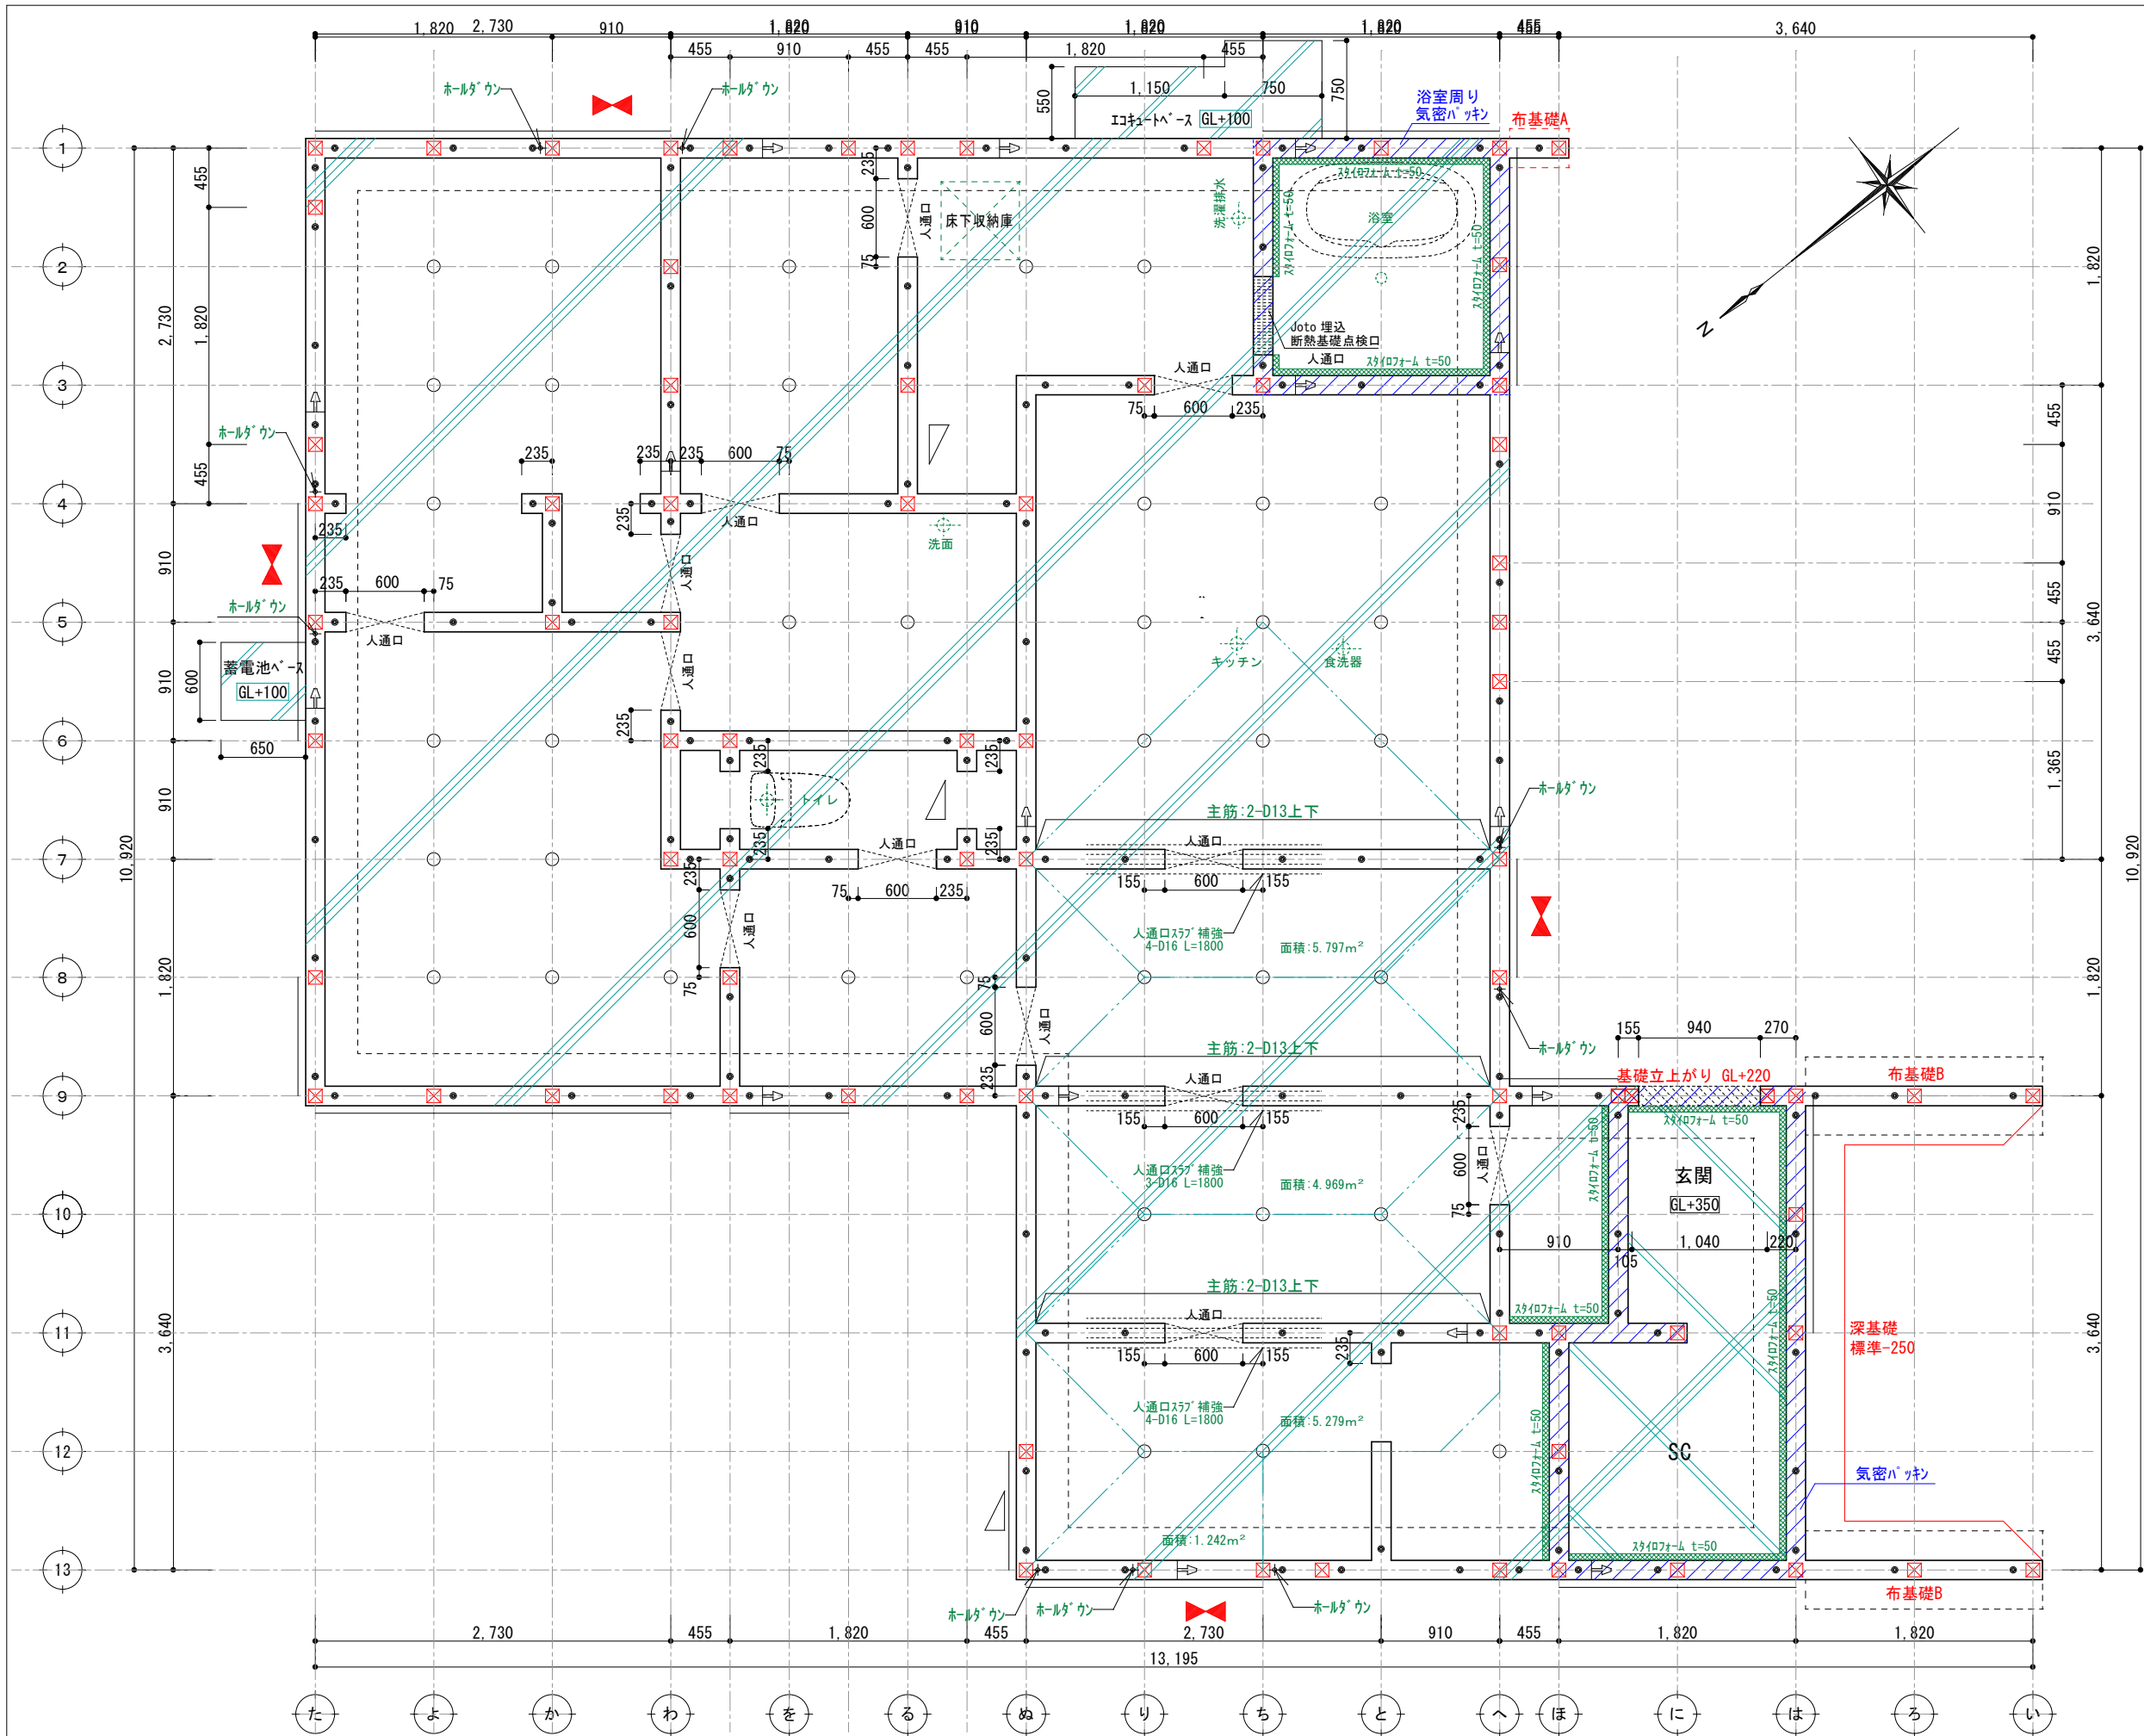

構造体ベースコンクリート t=150




後打ち土間コン



アンカーボルトの配置
土台切れの箇所より150mm
土台の継手及び仕口の端部より150mm
耐力壁の端部、筋交いの脚部より150mm
1.82m以下の間隔
250mm以上埋込み
基礎天端より120mm

筋かい凡例
柱脚 柱頭 片筋かい
たすき掛け筋かい
構造用パネル

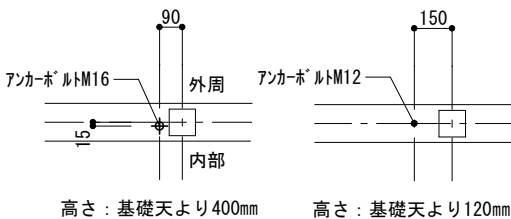

ホールダウン用アンカーボルト配置

アンカーボルト配置












凡例
通し柱(105*105) 管柱(105*105)
● アンカーボルトM12 L=400
+ ホールダウンアンカーM16 L=800
柱芯より90mm 280mm以上埋め込み
(カナフイストアンカーボルトM16)
⊕ 鋼製束
土台ジョイント
ベースコンクリート(t=150)
後打ちコンクリート

基礎伏図について特記なき場合に限り下記による。

1. コンクリート：呼び強度 21N/mm²
2. 鉄筋：SD295A
3. 設計地耐力：fe=20kN/m²
地耐力計測後、不足の場合は相当の改良を行い、満たすものとする。
4. 基礎の位置は、芯振分けとする。
5. 玄関・S/C・UB周囲の基礎天端は気密パッキン施工(網掛け部)とし、その他の基礎天端は基礎パッキン施工とする。
6. 設備配管の屋内への取り入れは基礎立上り部のスリーブによる。

決定図

訂正	浜岡一級総合設計事務所 一級建築士事務所 静岡県知事登録第(10)2441号 一級建築士 大臣登録第365879号 西原利昌	PG HOUSE ピージーハウス	株式会社 LIFEFUND InDesign office 事務所登録(2)第7595号 一級建築士登録 第179770号 鈴木 達男 〒432-8023 静岡県浜松市中央区鶴江3丁目70番23号	一級建築士事務所	2026.3.1 縮尺 1/50	図名 小林大樹様邸 新築工事 基礎伏図	設計 角谷 IC 工事 青島 図番 B-1
----	--	---------------------	--	----------	---------------------	------------------------	--------------------------------

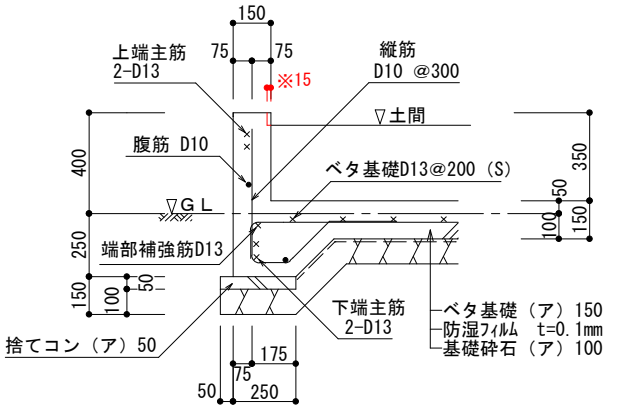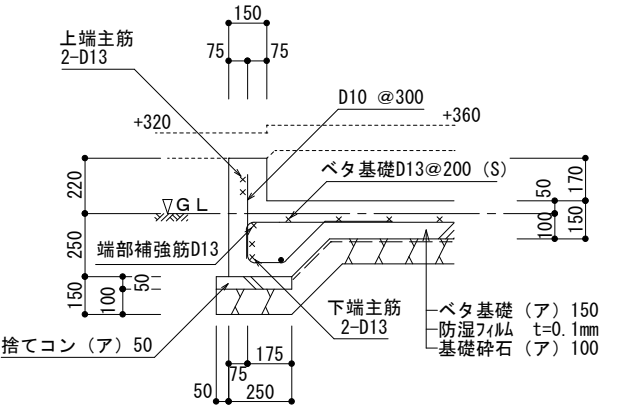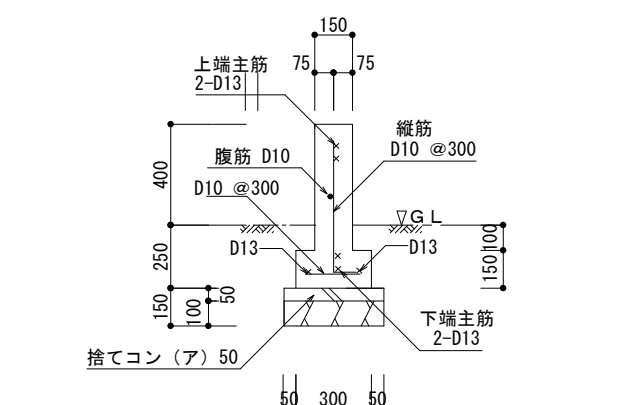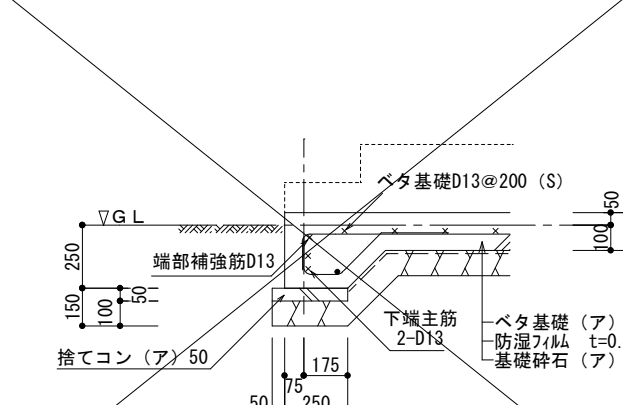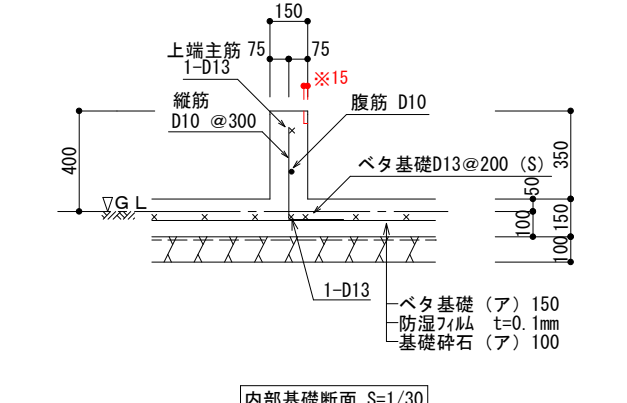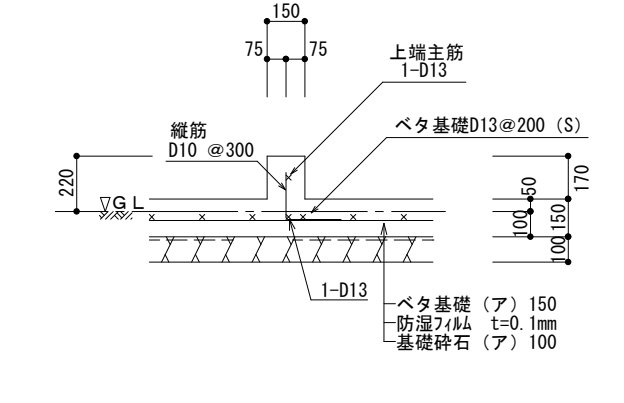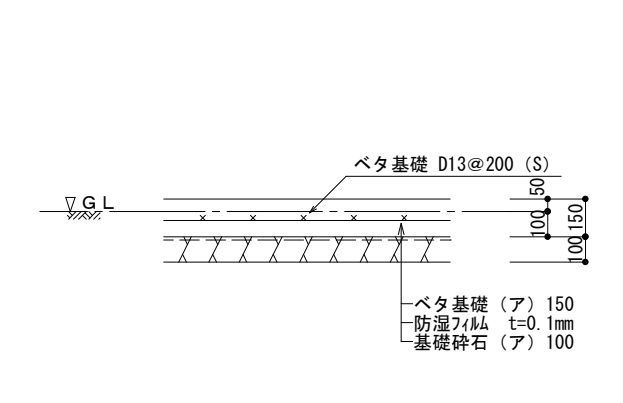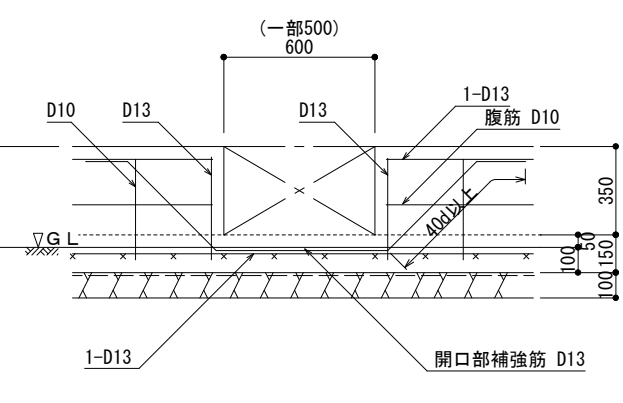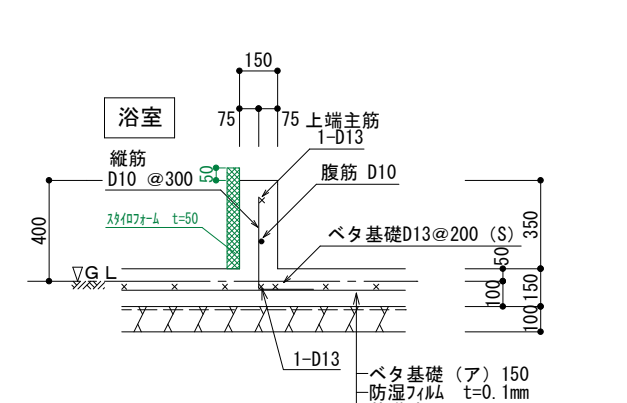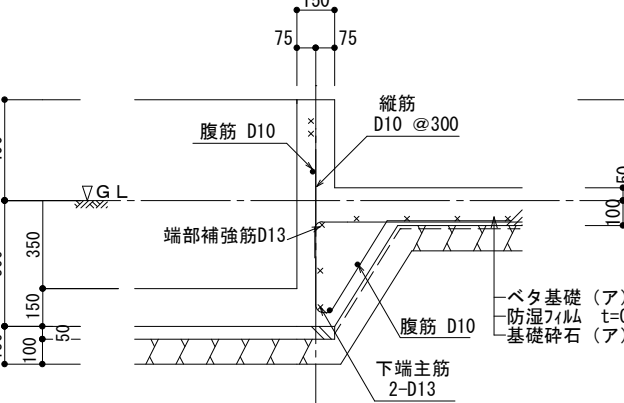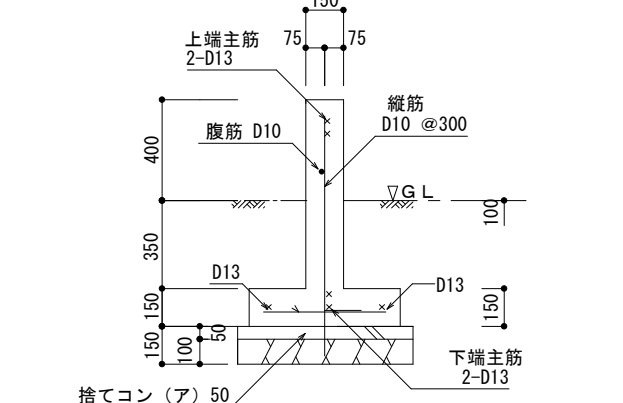 外周基礎断面 S=1/30 ※玄関内土間部分のみ15mm欠き込み	 ポーチ下 外周部基礎断面 S=1/30 倉庫ドア下 外周部基礎断面 S=1/30	 布基礎A：袖壁用 基礎断面 S=1/30	 ポーチ外周部の基礎断面 S=1/30 立上り無しの基礎断面 S=1/30							
 内部基礎断面 S=1/30 ※玄関内土間部分のみ15mm欠き込み ※注意：基礎伏図に特記のない内部基礎の場合	 ポーチ下 内周部基礎断面 S=1/30 玄関ドア下 内周部基礎断面 S=1/30 玄関＝SC布基礎断面 S=1/30	 ベタ基礎断面 S=1/30	 人通口補強 S=1/30							
 浴室内部基礎断面 S=1/30 ※注意：基礎伏図に特記のない内部基礎の場合	 外周深基礎/布基礎B 断面 S=1/30 深基礎(標準-250)	 布基礎B 断面 S=1/30	基礎の寸法 及び 配筋の検証方法 基礎立上り配筋は、 (財)日本住宅・木材技術 センター発行のスパン表 (増補版)による。 ベタ基礎スラブ配筋は、 まもりすまい保険設計施工 基準同解説のベタ基礎配筋表 による。具体的な寸法・配 筋は基礎詳細図参照。 鉄筋断面表記 ●・・・D10を示す。 ×・・・D13を示す。 ※使用しない断面は×を記入。 決定図							
訂正	浜岡一級総合設計事務所 一級建築士事務所 静岡県知事登録第 (10)2441 号 一級建築士 大臣登録第 365879 号 西原利昌	PG HOUSE	株式会社 LIFEFUND InDesign office 一級建築士事務所 事務所登録 (2)第7595号 一級建築士登録 第179770号 鈴木 達男 〒432-8023 静岡県浜松市中央区鴨江3丁目70番23号	年月日 2026.3.1 縮尺 1/30	件名 小林大樹様 邸新築工事 図名 基礎断面リスト		設計 角谷	I C	工務 青島	図番 B-2

37セントクロス 指示書

