


37セントクロス指示書

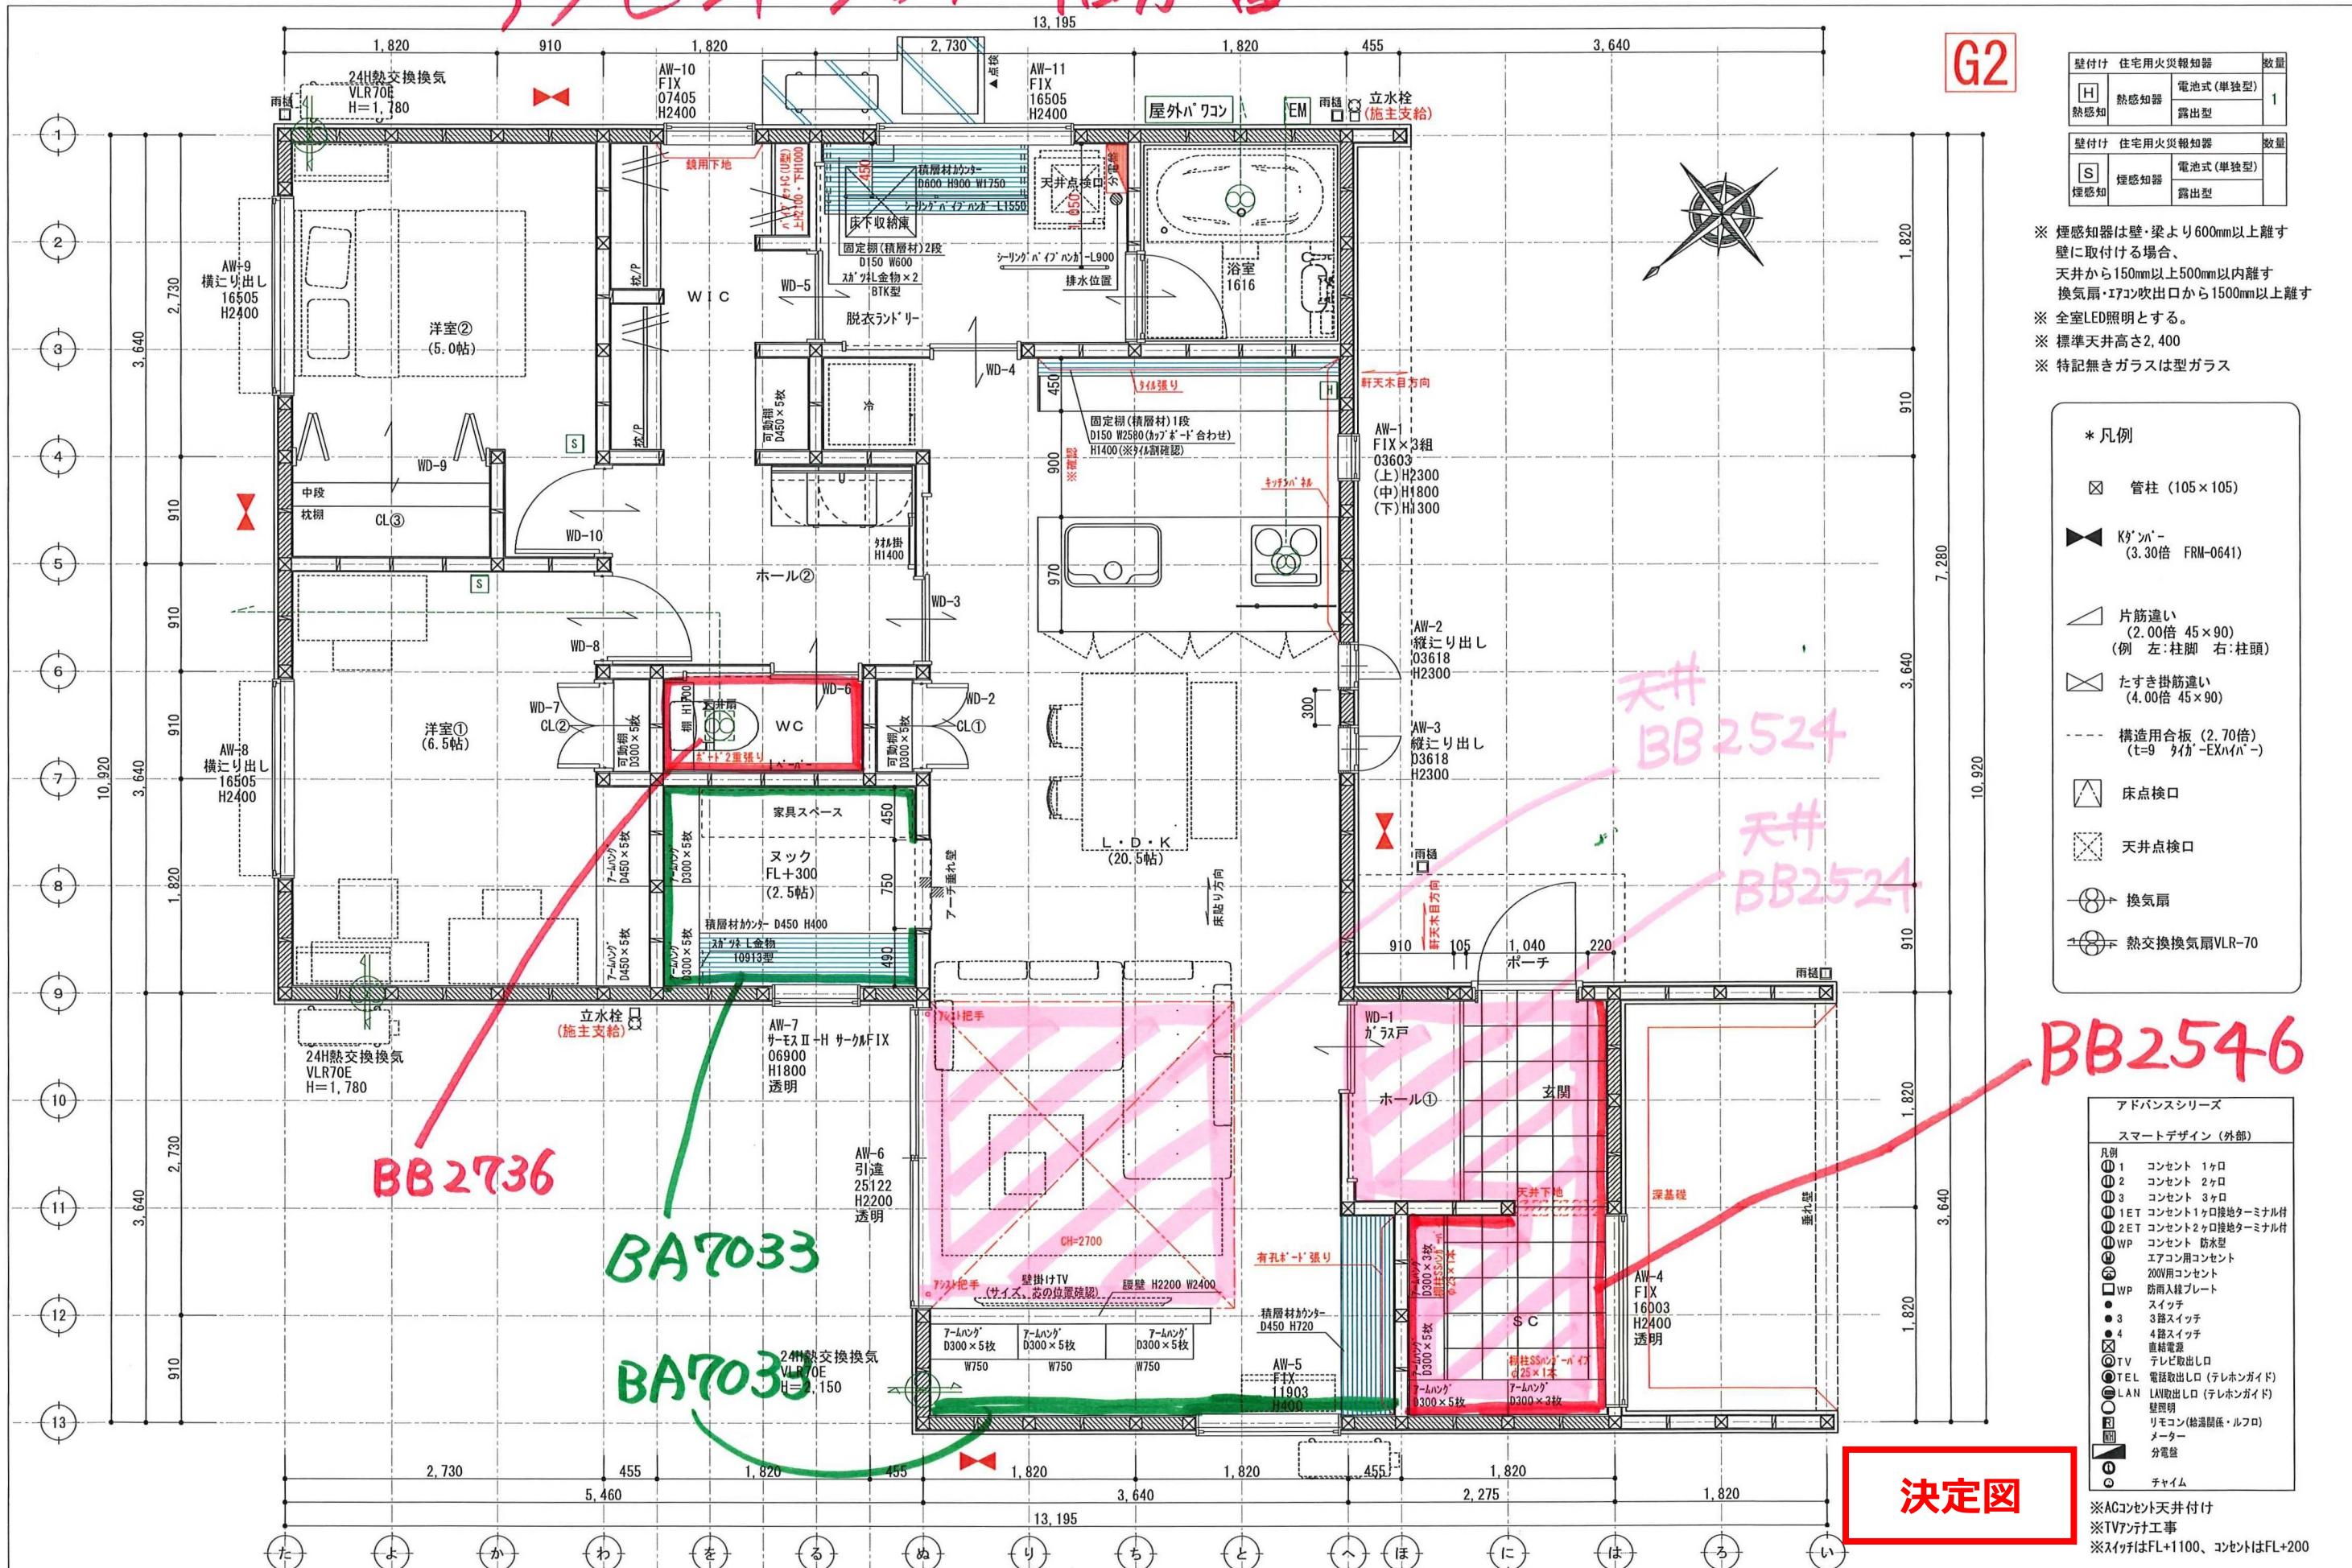

G2

壁付け 住宅用火災報知器			数量
[H] 熱感知	電池式(単独型)		1
	露出型		
壁付け 住宅用火災報知器			数量
[S] 煙感知	電池式(単独型)		
	露出型		

- ※ 煙感知器は壁・梁より600mm以上離す
- ※ 壁に取付ける場合、天井から150mm以上500mm以内離す
- ※ 換気扇・エアコン吹出口から1500mm以上離す
- ※ 全室LED照明とする。
- ※ 標準天井高さ2,400
- ※ 特記無きガラスは型ガラス

* 凡例

- ☒ 管柱 (105×105)
- ◀▶ K'ア'ン' (3.30倍 FRM-0641)
- △ 片筋違い (2.00倍 45×90) (例 左:柱脚 右:柱頭)
- ⊠ たすき掛筋違い (4.00倍 45×90)
- 構造用合板 (2.70倍) (t=9 タイ EXNIN)
- △ 床点検口
- ⊠ 天井点検口
- ⊕ 換気扇
- ⊕ 熱交換換気扇VLR-70

アドバンスシリーズ		
スマートデザイン (外部)		
凡例	1	コンセント 1ヶ所
②	2	コンセント 2ヶ所
③	3	コンセント 3ヶ所
1ET	コンセント1ヶ所接地ターミナル付	
2ET	コンセント2ヶ所接地ターミナル付	
WP	コンセント 防水型	
④	エアコン用コンセント	
⑤	200V用コンセント	
WP	防雨入換プレート	
⑥	スイッチ	
⑦	3路スイッチ	
⑧	4路スイッチ	
⑨	直結電源	
TV	テレビ取出口	
TEL	電話取出口 (テレホンガイド)	
LAN	LAN取出口 (テレホンガイド)	
⑩	壁照明	
⑪	リモコン (給湯関係・ルフロ)	
⑫	メーター	
⑬	分電盤	
⑭	チャイム	

- ※ACコンセント天井付け
- ※TVアンテナ工事
- ※スイッチはFL+1100、コンセントはFL+200

決定図