



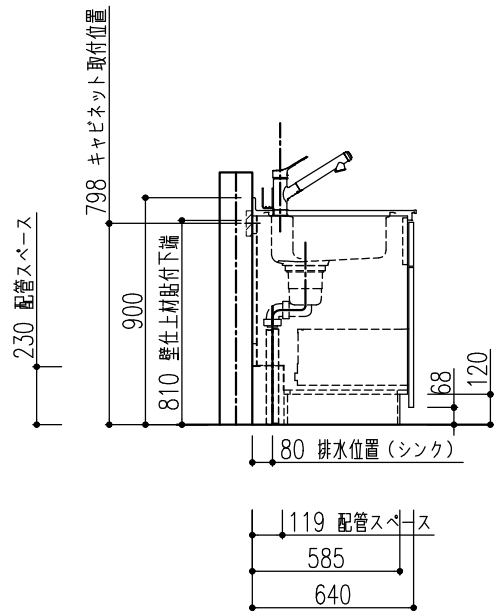

B面

C面

注4) 125V・15A 2極接地極付アースターミナル付コンセント 【専用】（フード用）

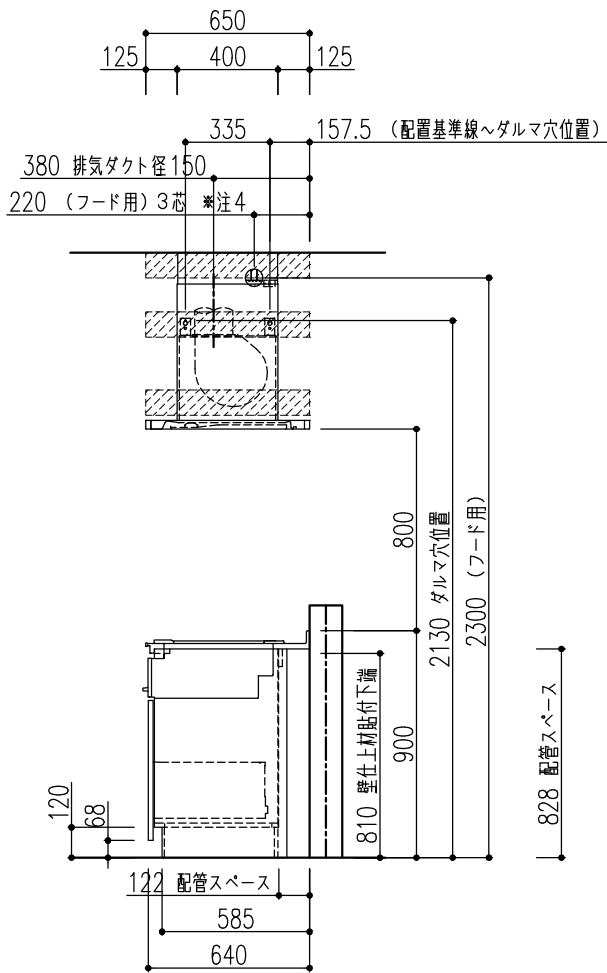


特記事項 扉色 IK8:ブリーチドウッド 取手 [R]スリム取手（シャインニッケル） ワークトップカラー 【DW】ソルティホワイト	物件名	小長井祐希 様邸	案件No.	図面名	担当	図面	図番
	仕様	ES21	A2507DDD0EPN6Q	納まり図	栗野 友仁		株式会社 LIXIL
			見積No.	縮尺	日付		
			M25078034870-003-2	1/30	2025.07.28		

■壁面仕上材（キッチンパネル、タイルなど）取付注意事項〔貼付下端位置〕

●キッチンパネルの貼付下端位置

キッチンパネルの貼付下端位置にご注意ください。

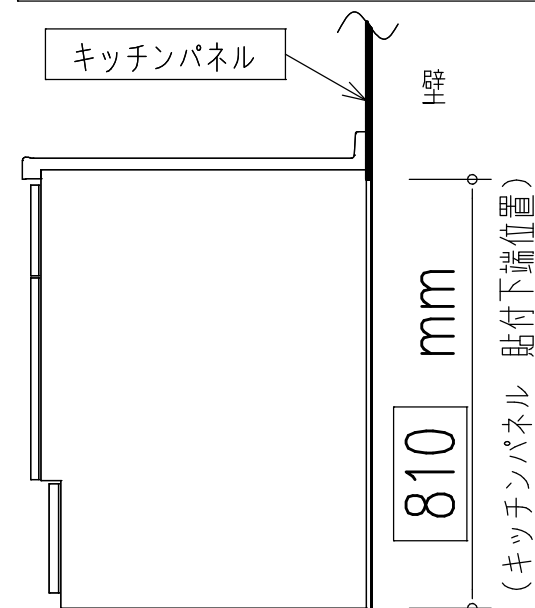


ワークトップ高さ：850mm以外の場合は、
下表を参照してください。

ワークトップ高さ	キッチンパネル 貼付下端位置
900	860
875	835
825	785
800	760

●上表はキッチンパネルの場合です。ステンレスパネルの場合は、キッチンパネルの「取付・設置説明書」を参照してください。

《ワークトップ高さ：850mmの場合》

■ 床の不陸に関して

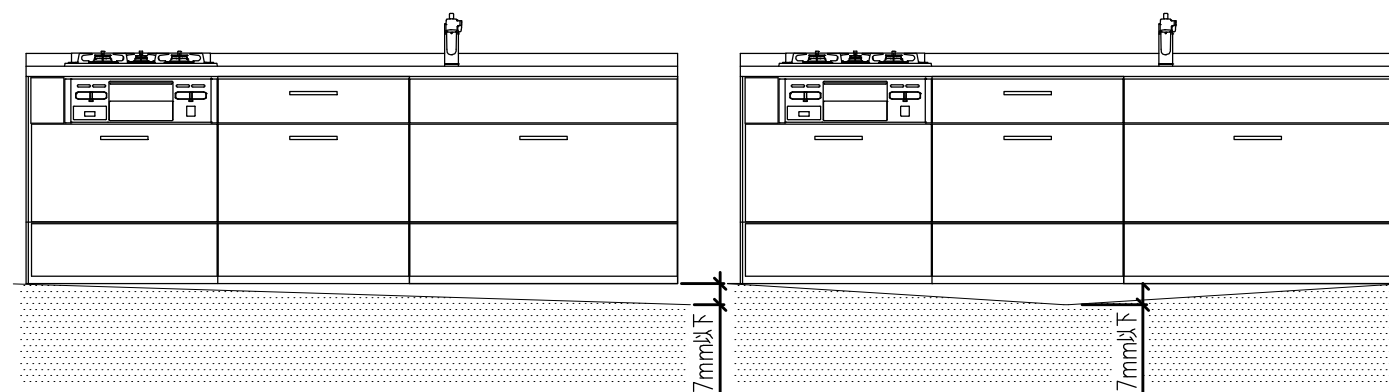


床の不陸は、7 mm 以下に抑えるようにしてください。不陸が大きい場合は、現場責任者に床の修正を依頼してください。

※キャビネット取付時には不陸調整スペーサー等で水平になるように設置してください。

■壁面仕上材（キッチンパネル）取付注意事項〔貼付向き〕

●キッチンパネルの貼付向き

キッチンパネルの貼付向きにご注意ください。

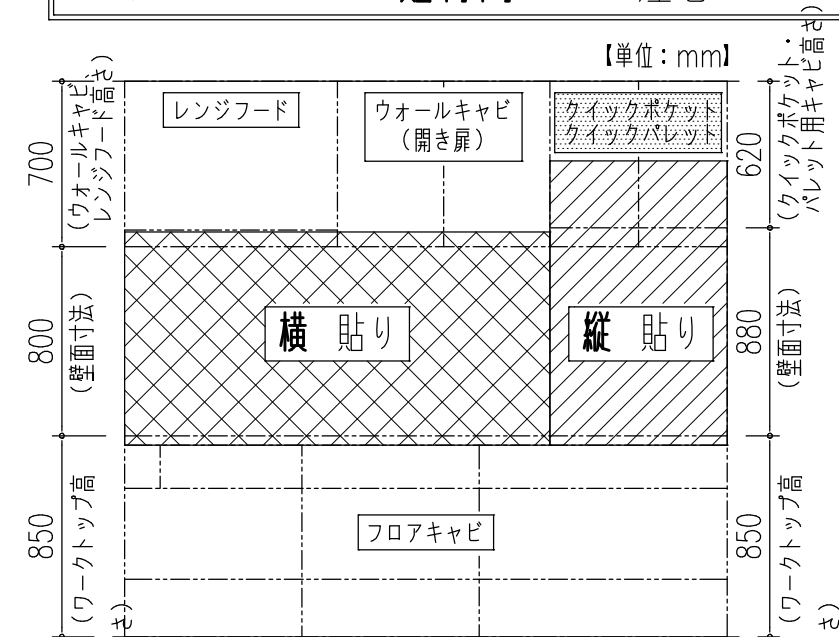

《バックガード：なし、ワークトップ高さ：850mm、ウォールキャビ高さ：700mmの場合》

《キッチンパネル 貼付方向》

総高さ：2350mmの場合

	ウォールキャビ		
	開き扉		クイックボケット クイックパレット
	H700	H600 H500	H700 (620) H600 (520)
キッチンパネル 貼付方向	横	縦	


【ご注意】
リシエル以外のクイックパレットは、
キャビネットの背板高さがショート
（-80mm）してありませんので、
『開き扉』のキッチンパネル貼付方向
に合せてください。

■レンジフード取付注意事項（壁面取付時）


レンジフードを取付ける場合は下地の桟が厚み30mm以上、幅100mm以上、
ビス固定位置が桟の端部から25mm以上であることを確認してください。
また、壁強度などの詳細は「レンジフード設置説明書」を必ず事前に確認してください。

取付位置については、取付設置図を確認してください。


参考図 FED、HVR、NSDシリーズ（サイドマントルタイプ）

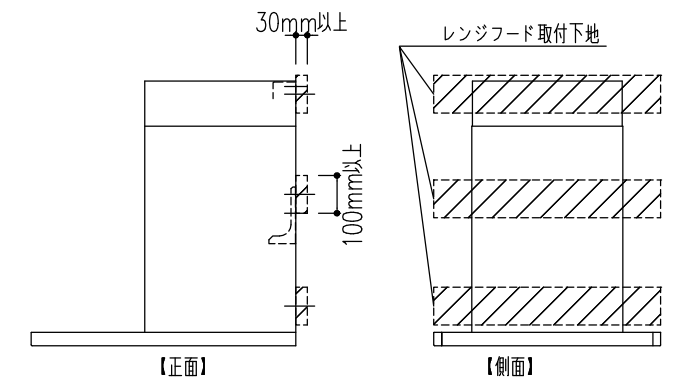

参考図_CLS, SER, NST, ASR, ADR, RVJ, GSR, BFRS, TARシリーズ
(※RVJ, GSRシリーズの場合はレンジフードパネルの取付下地は不要です。)

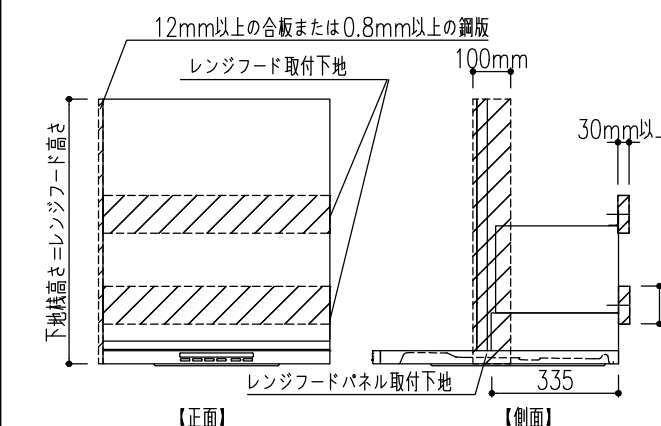


参考図 NBHシリーズ

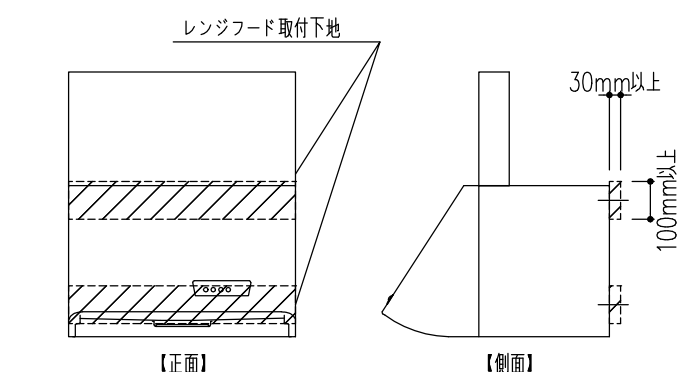

特記事項 扉色 IK8:ブリーチドウッド 取手 「R」スリム取手（シャインニッケル） ワークトップカラー 【DW】ソルティホワイト	物件名	小長井祐希 様邸	案件No.	図面名	担当	図面	図番 : 株式会社 LIXIL
			A2507DDDOEPN6Q	機能図	栗野 友仁		
	仕様	ES21	見積No.	縮尺	日付		
			M25078034870-003-2		2025.07.28		

■ SMHVRフード

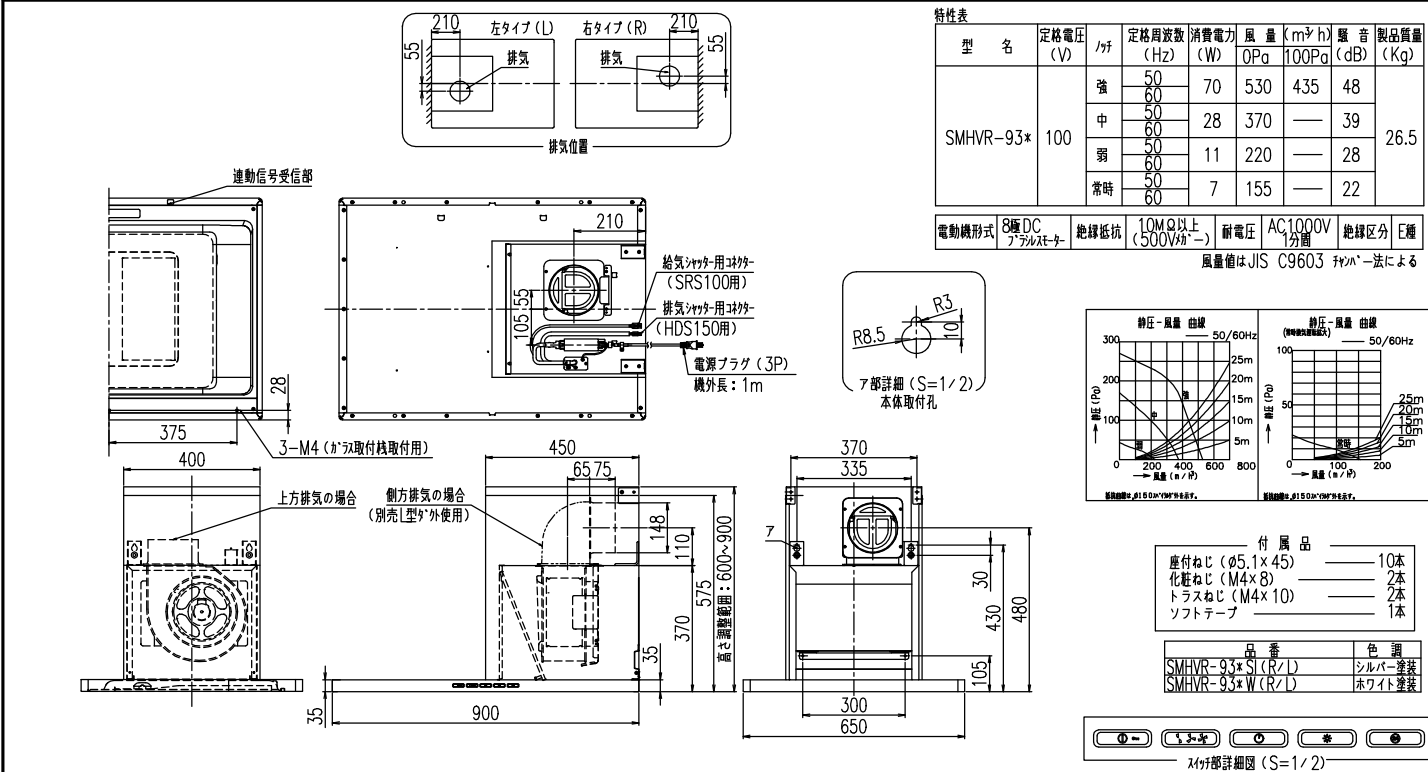


4. 製品名の末尾の () にはワザシズによって記号が入る場合があります。
5. 電動シャッター (HDS150) (別売) を使用時は、中継コトを外して取り付けてください。
2. 赤外線連動型オプションです。単独でも使用できます。
注) 1. 排気方向は側方 (L型) 外使用: 別売) と上向きです。

■ IHヒーター用コンセント推奨位置図 / 壁付設置の場合


※コンセントや電源プラグが、引き出しおよびIHヒーター用仕切板 (オプション) に接触しないように注意してください。
※木製キャビネットの配管スペース付キャビネットを使用する場合は、点検口裏の配管スペース内にコンセントを設置してください。

キッチン高さ	電源線高さ
800	400
850	450
900	500

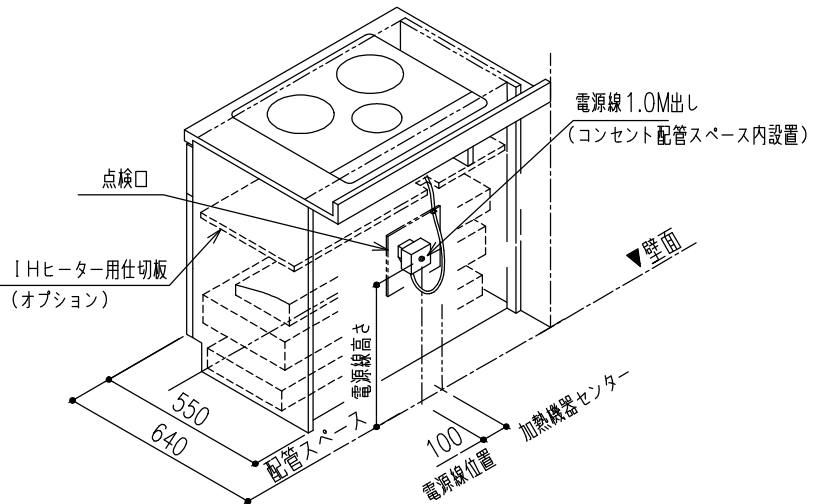

注意: 引き出しおよびIHヒーター用仕切板 (オプション) に接触しないように上記寸法を参照してください。

■ 食器洗い乾燥機内配管図 床立上げ配管例

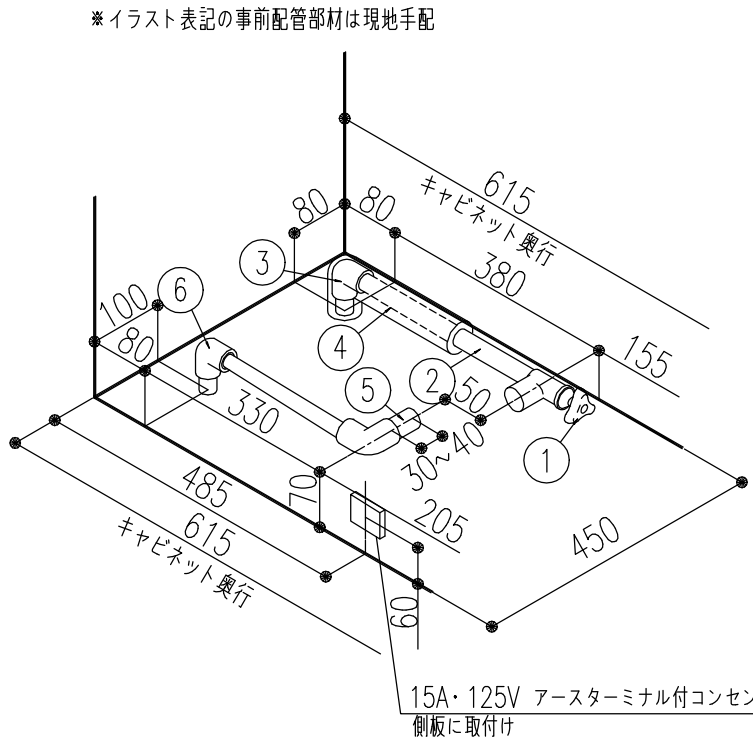


注意: 配管立ち上げ位置は必ず本図の位置に立ち上げて下さい。

※給水接続か給湯接続かお客様に確認したうえで施工願います。


- 給水 (給湯の場合は耐熱配管)
- ①アングル型止水栓 (ハンドル式・固定ゴマタイプ)
※必ず固定ゴマタイプをご使用ください。
落としゴマタイプを使用すると、水栓内でコマが移動し、ゴトゴト音を生じる恐れがあります。
 - ②硬質塩化ビニルライニング鋼管 (相当品)
 - ③RC1/2ソケット
 - ④断熱材 (Φ48)
- 排水 (耐熱塩ビ使用のこと)
- ⑤排水パイプHT20
 - ⑥HTエルボ
- ※配水管先端のエルボを上向きにしないでください。
キャビネットに当たるため、排水ホース折れの原因になります。



■ 止水栓図 (床立上げ)

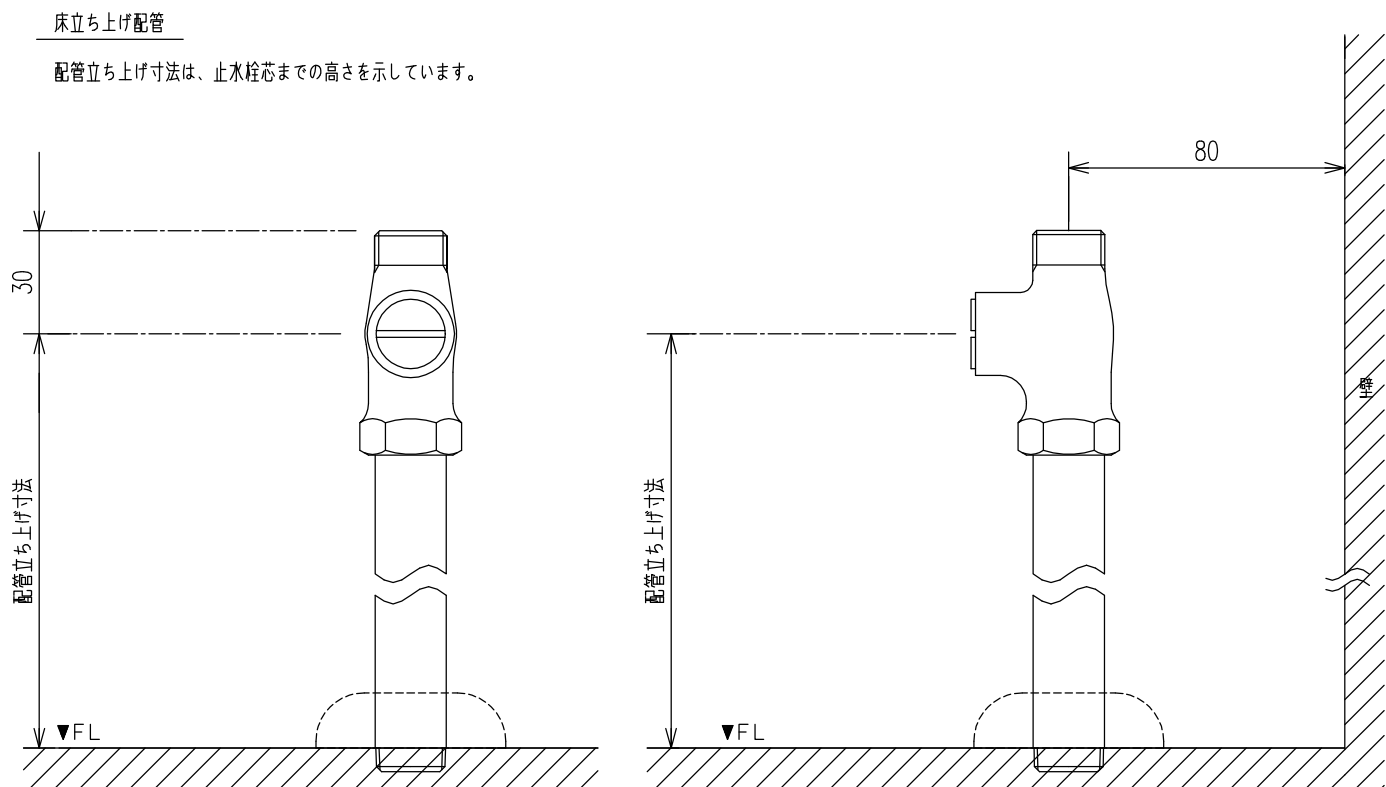

■ キッチン取付者さま向け 動画コンテンツ ■

商品取付けの注意点を2次元コードでご視聴いただけます。
取付日より前に、是非ご確認ください。

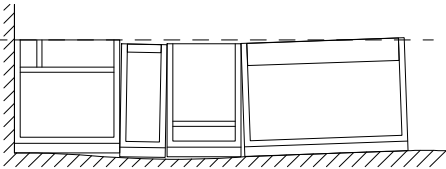荷扱い・搬入	カウンター開梱搬入「養生ツール」	不陸の確認と調整	マグネットキッチンパネル
荷扱い・搬入	カウンター開梱搬入「養生ツール」のご紹介		マグネット キッチンパネル「取付・設置」ポイント
作成日：2024年10月01日	作成日：2024年10月01日	作成日：2024年02月07日	作成日：2024年03月06日


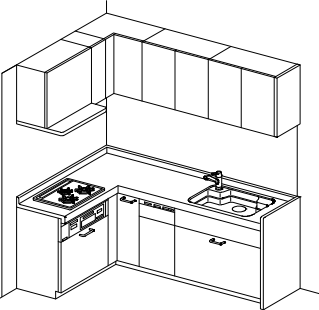
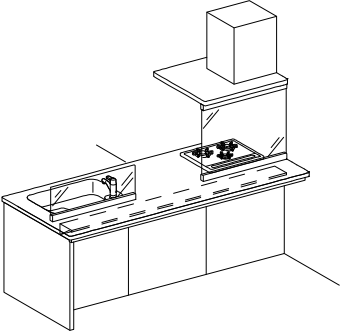
人造大理石カウンターL型キッチン	センターキッチン（ペニンシュラ型）		
			
作成日：2024年02月07日	作成日：2024年02月07日		

--	--	--	--

特記事項 扉色 IK8:ブリーチドウッド 取手 [R]スリム取手（シャインニッケル） ワークトップカラー 【DW】ソルティホワイト	物件名	小長井祐希 様邸	案件No.	図面名	担当	図面	図番
	仕様	ES21	A2507DDD0EPN6Q	機能図	栗野 友仁		株式会社 LIXIL
			見積No.	縮尺	日付		
			M25078034870-003-2		2025.07.28		

■ キッチン取付者さま向け 動画コンテンツ ■

商品取付けの注意点を2次元コードでご視聴いただけます。
取付日より前に、是非ご確認ください。

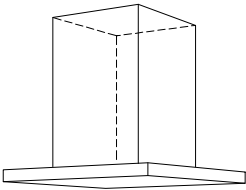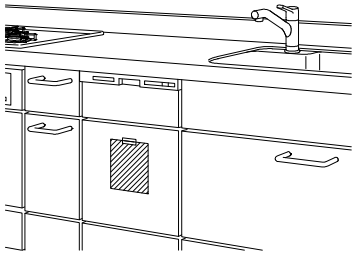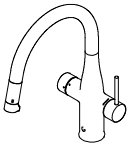センターフード型レンジフード (天吊りフード)  作成日：2024年06月03日 	I H加熱機器関連 I H加熱機器 仕切り板 作成日：2024年02月07日 	食器洗い乾燥機  作成日：2024年02月07日 	ミネラル浄水栓 Greentap  作成日：2024年06月03日 
---	--	--	---

--	--	--	--

--	--	--	--

特記事項 扉色 IK8:ブリーチドウッド 取手 [R]スリム取手 (シャインニッケル) ワークトップカラー 【DW】ソルティホワイト	物件名	小長井祐希 様邸	案件No.	図面名	担当	図面	図番
	仕様	ES21	A2507DDD0EPN6Q	機能図	栗野 友仁		株式会社 LIXIL
			見積No.	縮尺	日付		
			M25078034870-003-2		2025.07.28		