
[illegible]

【ご注意】

- 記載のキャビネット寸法は扉前面までの呼び寸法です。キャビネット本体の寸法・扉厚等商品は商品ガイドの巻末資料をご確認ください。
- 記載のワークトップ、カウンター、エンドパネル、サイドパネルの寸法は呼び寸法です。詳細寸法は商品ガイドの巻末資料をご確認ください。

特記事項 扉色 IK8:ブリーチドウッド 取手 [R]スリム取手(シャインニッケル)	物件名 小長井祐希 様邸	案件No. A2507DDD0EPN6Q	図面名 レイアウト図	担当 葉野 友仁	図面 	図番 : 株式会社 LIXIL
		見積No. M25078034870-003-3	縮尺 1/30	日付 2025.07.28		
	仕様 ES21					

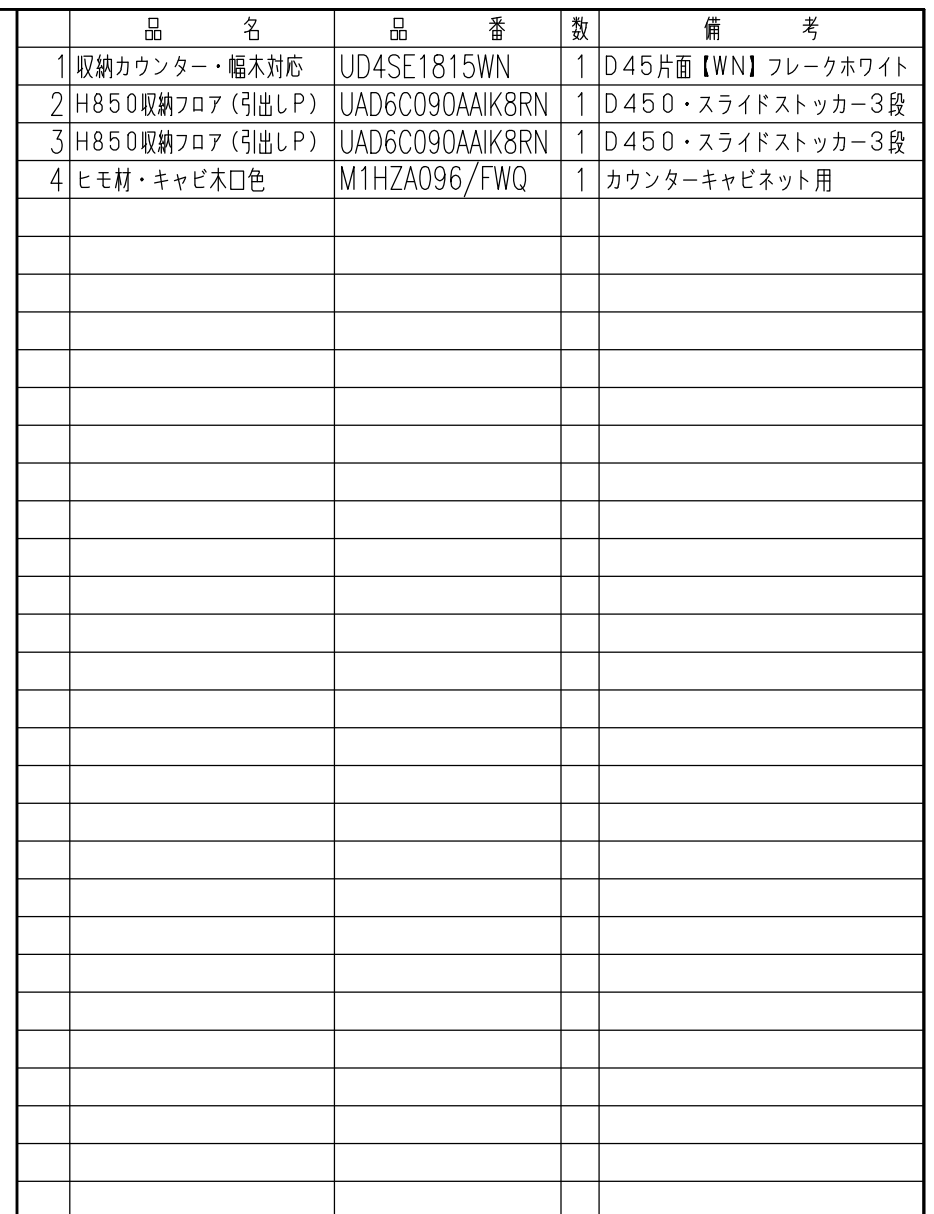


特記事項	
扉色	IK8:ブリーチドウッド
取手	[R]スリム取手（シャインニッケル）

物件名	小長井祐希 様邸
仕様	E S 2 1

案件No.	図面名	担当	図面
A2507DDDD0EPN6Q	納まり図	栗野 友仁	
見積No.	縮尺	日付	
M25078034870-003-3	1/30	2025.07.28	

図番	:
株式会社 LIXIL	

■ 床の不陸に関して

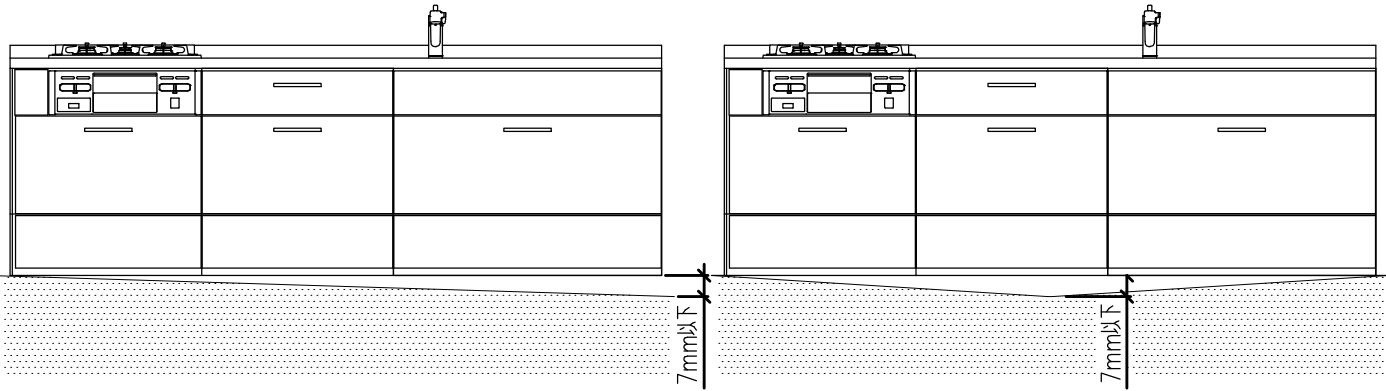

床の不陸は、7 m m 以下に抑えるようにしてください。不陸が大きい場合は、現場責任者に床の修正を依頼してください。
※キャビネット取付時には不陸調整スペーサー等で水平になるように設置してください。

	特記事項 扉色 IK8:ブリーチドウッド 取手 [R]スリム取手（シャインニッケル）	物件名	小長井祐希 様邸	案件No.	図面名	担当	図面	図番
				A2507DDD0EPN6Q	機能図	栗野 友仁		株式会社 LIXIL
		仕様	ES 2 1	見積No.	縮尺	日付		
				M25078034870-003-3		2025.07.28		

■ キッチン取付者さま向け 動画コンテンツ ■
商品取付けの注意点を2次元コードでご視聴いただけます。
取付日より前に、是非ご確認ください。

1 ページ目

■ キッチン取付者さま向け 動画コンテンツ ■
商品取付けの注意点を2次元コードでご視聴いただけます。
取付日より前に、是非ご確認ください。

1 ページ目

■ キッチン取付け者さま向け 動画コンテンツ ■

商品取付けの注意点を2次元コードでご視聴いただけます。
取付日より前に、是非ご確認ください。

1 ページ目

■ キッチン取付け者さま向け 動画コンテンツ ■
商品取付けの注意点を2次元コードでご視聴いただけます。
取付日より前に、是非ご確認ください。

1 ページ目

荷扱い・搬入


荷扱い・搬入



作成日：2024年10月01日

荷扱い・搬入

荷扱い・搬入

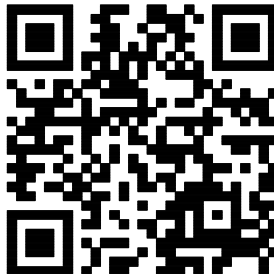

作成日：2024年10月01日



荷扱い・搬入

荷扱い・搬入



作成日：2024年10月01日

カウンター開梱搬入「養生ツール」

カウンター開梱搬入 「養生ツール」のご紹介



作成日：2024年10月01日

カウンター開梱搬入「養生ツール」

カウンター開梱搬入 「養生ツール」のご紹介



作成日：2024年10月01日



カウンター開梱搬入「養生ツール」



カウンター開梱搬入 「養生ツール」のご紹介




作成日：2024年10月01日

不陸の確認と調整

作成日：2024年02月07日

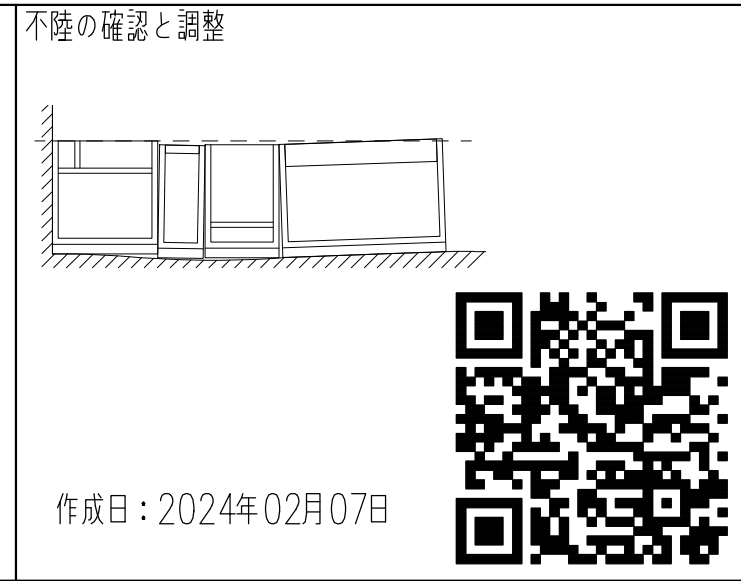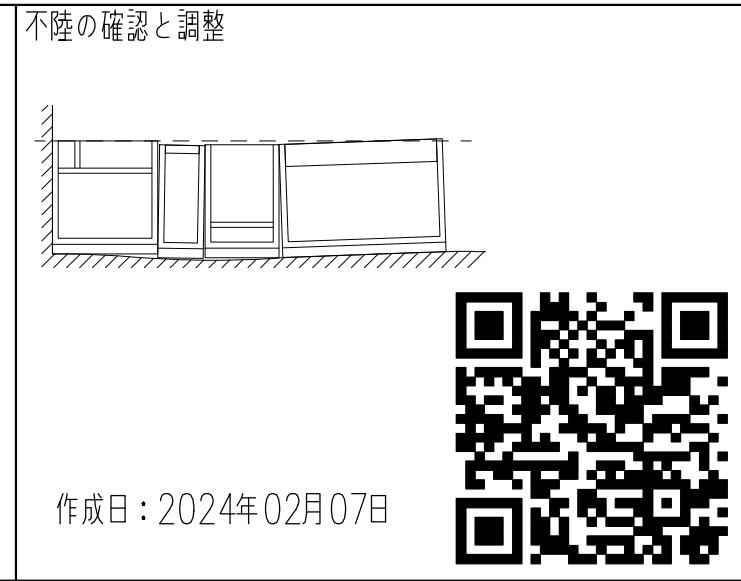

不陸の確認と調整

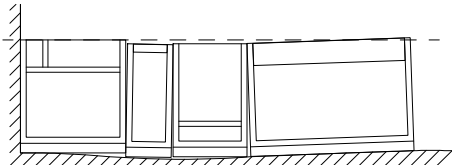

作成日：2024年02月07日



マグネット キッチンパネル

マグネット キッチンパネル 「取付・設置」ポイント



作成日：2024年03月06日

マグネット キッチンパネル

マグネット キッチンパネル 「取付・設置」ポイント



作成日：2024年03月06日




マグネット キッチンパネル

マグネット キッチンパネル 「取付・設置」ポイント



作成日：2024年03月06日


人造大理石カウンターL型キッチン

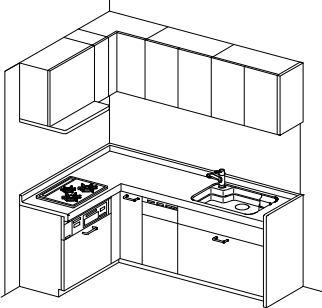

作成日：2024年02月07日




人造大理石カウンターL型キッチン

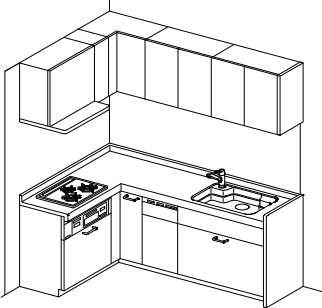



作成日：2024年02月07日




センターキッチン（ペニンシュラ型）

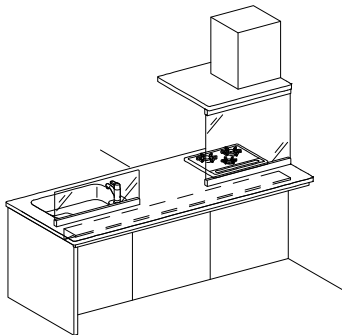

作成日：2024年02月07日

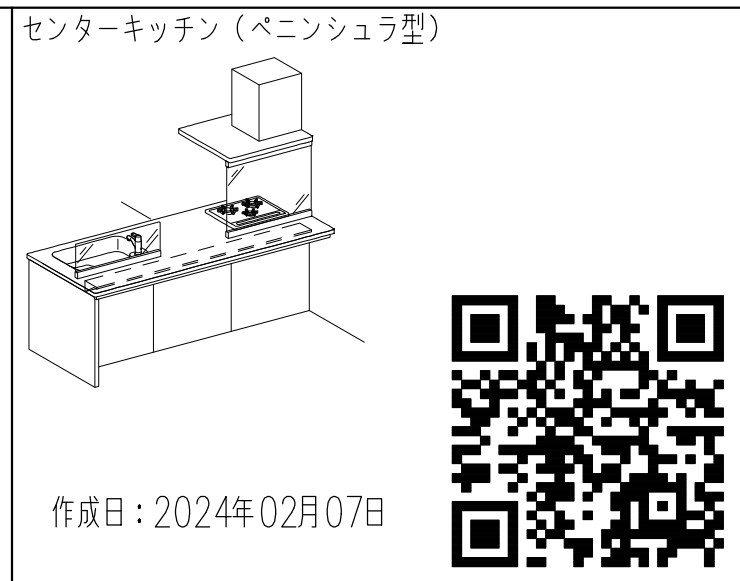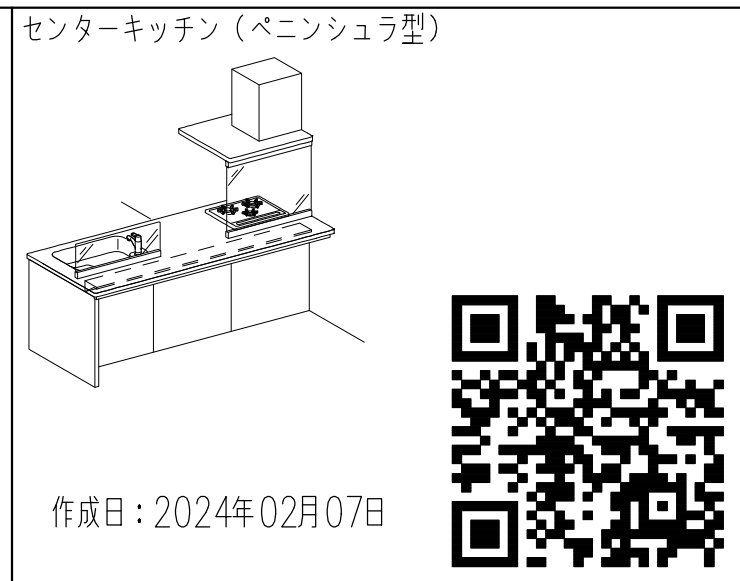

センターキッチン（ペニンシュラ型）

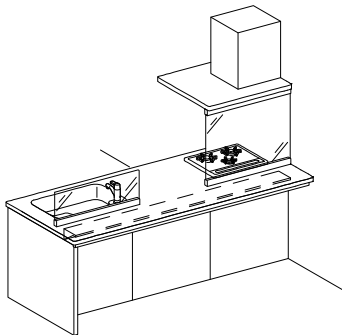





作成日：2024年02月07日



		特記事項 扉色 IK8:フリーチドウッド 取手 [R]スリム取手（シャインニッケル）	物件名 仕様	小長井祐希 様邸 E S 2 1	案件No.	図面名	担当	図面	図番 : 株式会社 LIXIL	
					A2507DDD0EPN6Q	機能図	栗野 友仁			
					見積No.	縮尺	日付			
					M25078034870-003-3		2025.07.28			

■ キッチン取付者さま向け 動画コンテンツ ■

商品取付けの注意点を2次元コードでご視聴いただけます。
取付日より前に、是非ご確認ください。

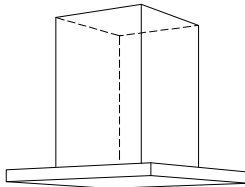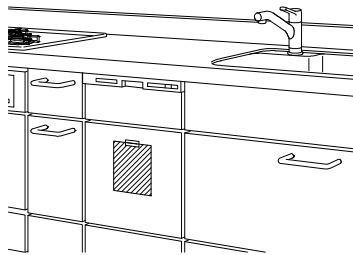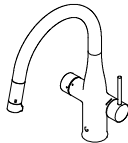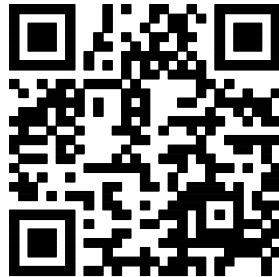センターフード型レンジフード (天吊りフード)  作成日：2024年06月03日 		I H加熱機器関連 I H加熱機器 仕切り板 作成日：2024年02月07日 		食器洗い乾燥機  作成日：2024年02月07日 		ミネラル浄水栓 Greentap  作成日：2024年06月03日 			
	特記事項 扉色 IK8:ブリーチドウッド 取手 [R]スリム取手 (シャインニッケル)	物件名 仕様	小長井祐希 様邸		案件No.	図面名	担当	図面	図番 : 株式会社 LIXIL
					A2507DDD0EPN6Q	機能図	栗野 友仁		
			ES21		見積No.	縮尺	日付		
					M25078034870-003-3		2025.07.28		