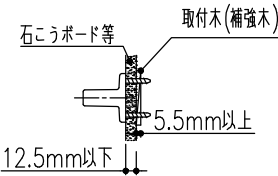
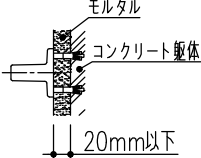
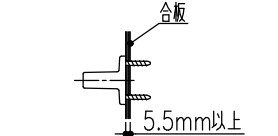
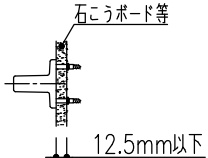
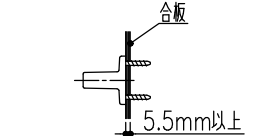
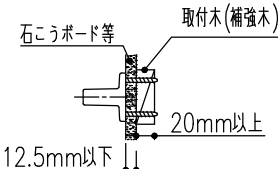
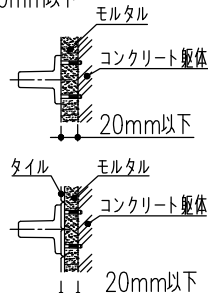
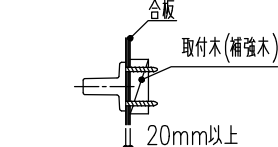
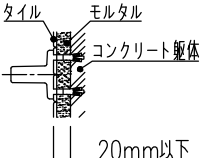
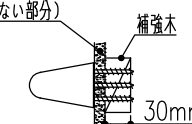
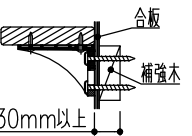
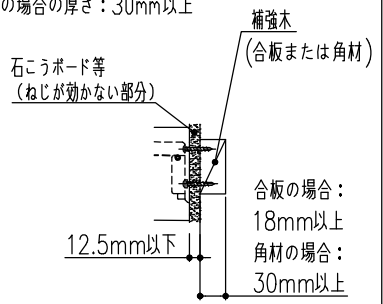
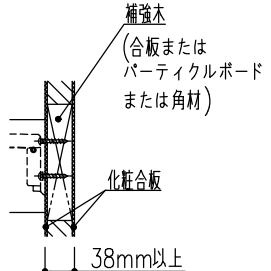
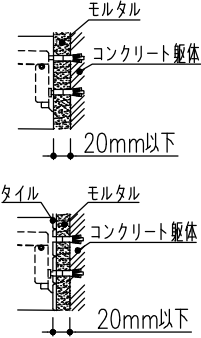
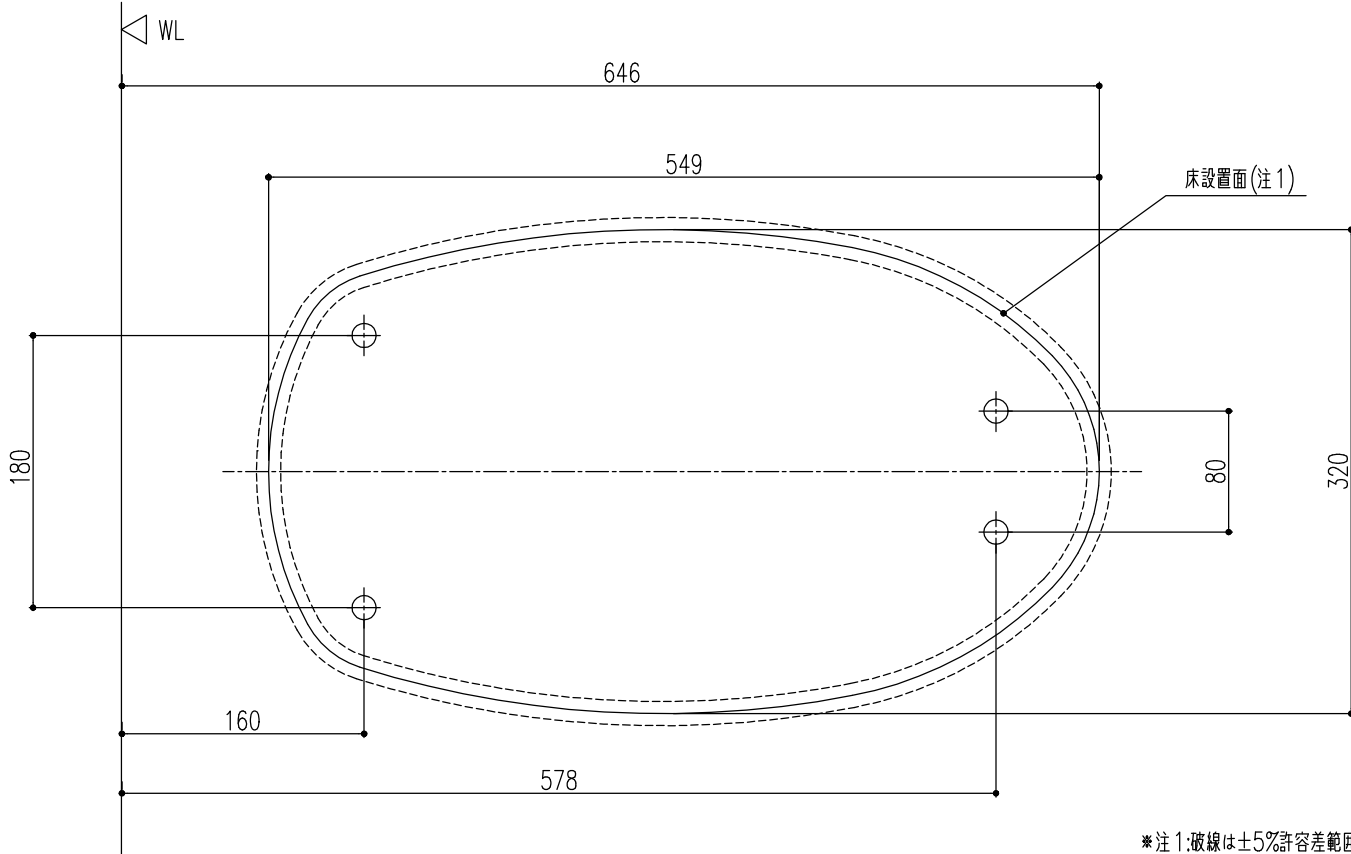
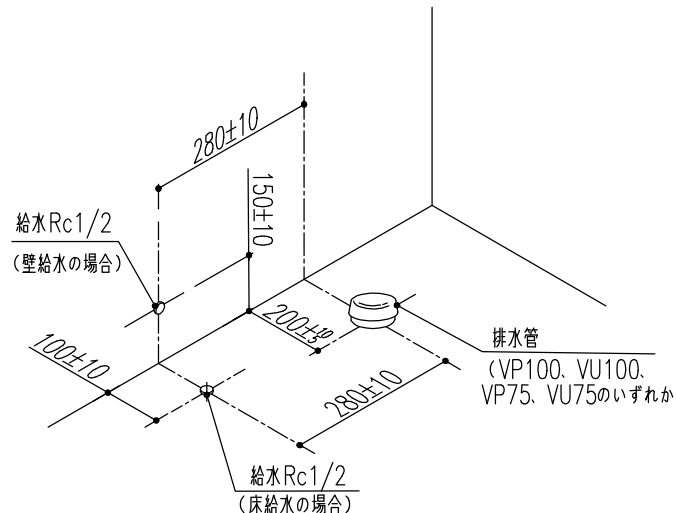
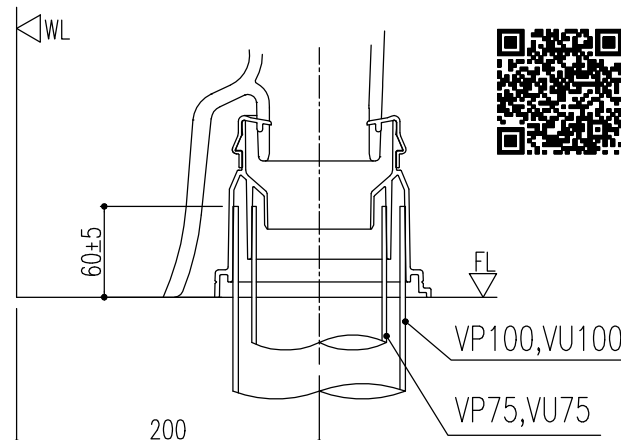
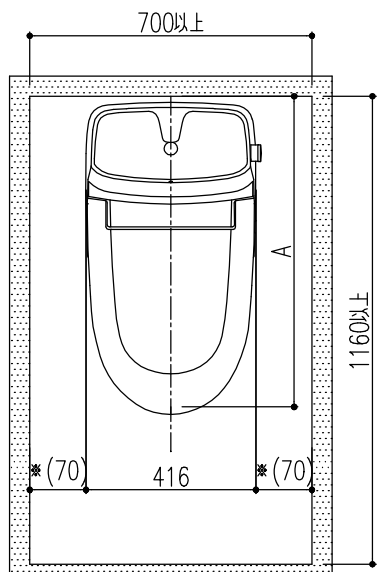
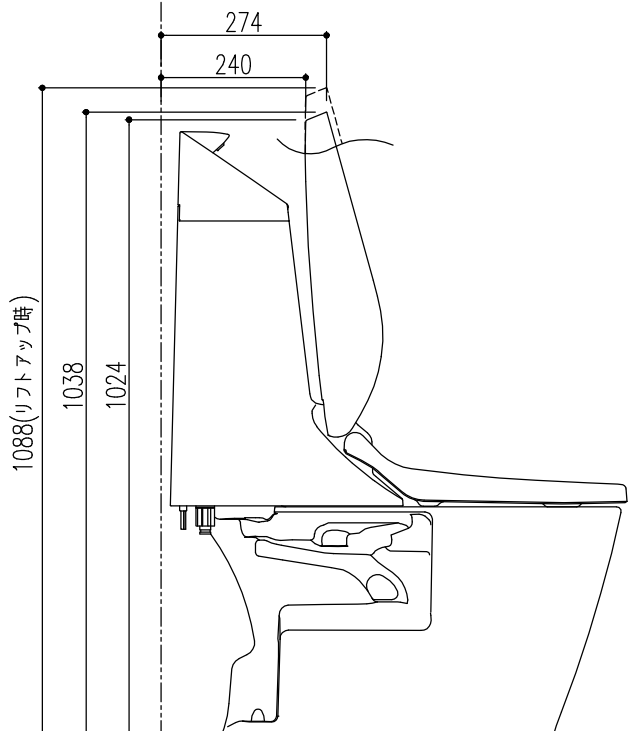


●アクセサリー 施工要領図

壁取付アクセサリーの落下事故防止のため、取付部材（木ねじ、AYボルト等）の固定強度（種類・数）については十分配慮を行っておりますが、壁面の構造についても配慮いただくことが不可欠です。

アクセサリー種類	乾 式 壁			湿 式 壁	
	木 ね じ	木ねじ+プラスチックプラグ	パ ー テ ー シ ョ ン 壁	A Y ボ ル ト	木ねじ+プラスチックプラグ
紙巻器 化粧鏡 石けん入れ	ねじ込み深さ：5.5mm以上 	取付不可	取付不可	壁仕上材厚さ：20mm以下 	取付不可
化粧鏡		石こうボード壁厚：9.5mm以上 12.5mm以下 			
紙巻器 石けん入れ					
紙巻器	ねじ込み深さ：20mm以上 	取付不可			壁仕上材厚さ：20mm以下 
フック タオル掛 化粧棚 紙巻器 タオルリング 化粧鏡 スベアペーパーホルダー サニタリーボックス					取付不可
アクセサリーパー 棚手すり 紙巻器 タオル棚 手すり 照明付鏡	ねじ込み深さ：30mm以上 石こうボード等 （ねじが効かない部分）  				
棚付二連紙巻器 横2連ストック付紙巻器 横4連ストック付紙巻器	合板の場合の厚さ：18mm以上 角材の場合の厚さ：30mm以上 		パーテーション （化粧合板+補強木）の厚さ：38mm以上 	壁仕上材厚さ：20mm以下 	

待記事項	物件名	小長井祐希 様邸	案件No.	図面名	担当	図面	図番
			A2507DDD0EPN6Q	機能図	栗野 友仁		株式会社 LIXIL
		仕様	ベーシアシャワートイレ／ECO5 床排水 一般地	見積No.	縮尺	日付	
				M25078034870-003-6		2025.07.28	

●便器床設置面寸法・固定穴寸法				●給排水の位置決めと取出し				●排水塩ビ管の接続			
				給水管、排水管を取り出します。 ※ 給水管、排水管を施工寸法通りに取り出します。 誤って排水管を壁寄りに取り出した場合は、タンクと壁が干渉して施工できない恐れがあります。 				※ 接続は、塩ビ接着剤にて確実に行なって下さい。 ※ 排水管の立ち上げ高さは、必ず60±5mmの位置で切断してください。 施工方法詳細の動画を以下から読み取ることができます。 ・ 通信料はお客様のご負担となります。 ・ お使いの環境・端末によっては、閲覧できない場合があります。 ・ 実物と動画のデザインが異なる場合があります。 ・ 動画内に表示される商品名と品番・デザインが異なる場合がありますが、施工手順に影響ありません。  ※注…立ち上げ寸法が60mm以下の場合は 既設配管に合った、市販の60mm立ち上げ用部材(持ち出しニップル)を別途手配ください。 ※注…防振シートを組み合わせる場合は5mm高くしてください。			
●取付最小スペース		●便フタ開時寸法									
※ 最小スペースはA寸法(前出寸法) + 400となり、便器排水方向や既設配管により、異なります。 A寸法は、床排水・床上排水(後抜き)の場合760mm、床上排水(横抜き)の場合860mmとなります。 ご確認ください。 ※ 右図の空間寸法は、衣服の着脱などの行為に必要な最低寸法です。 手すりや紙巻器などの機器を併設する場合は、必要に応じた広い空間が必要になります。 ※ 便器に向かって左右共に70mm以上の空間を確保してください。 		 ※ 上図は代表商品のイメージ図です。 ※ 防振シートを組み合わせる場合は、全体が5mm高くなります。									
特記事項		物件名	小長井祐希 様邸		案件No.	図面名	担当	図面	図番：		
		仕様	ベージャシャワートイレノECO5 床排水 一般地		A2507DDD0EPN6Q	機能図	栗野 友仁		株式会社 LIXIL		
					見積No.	縮尺	日付				
					M25078034870-003-6		2025.07.28				