



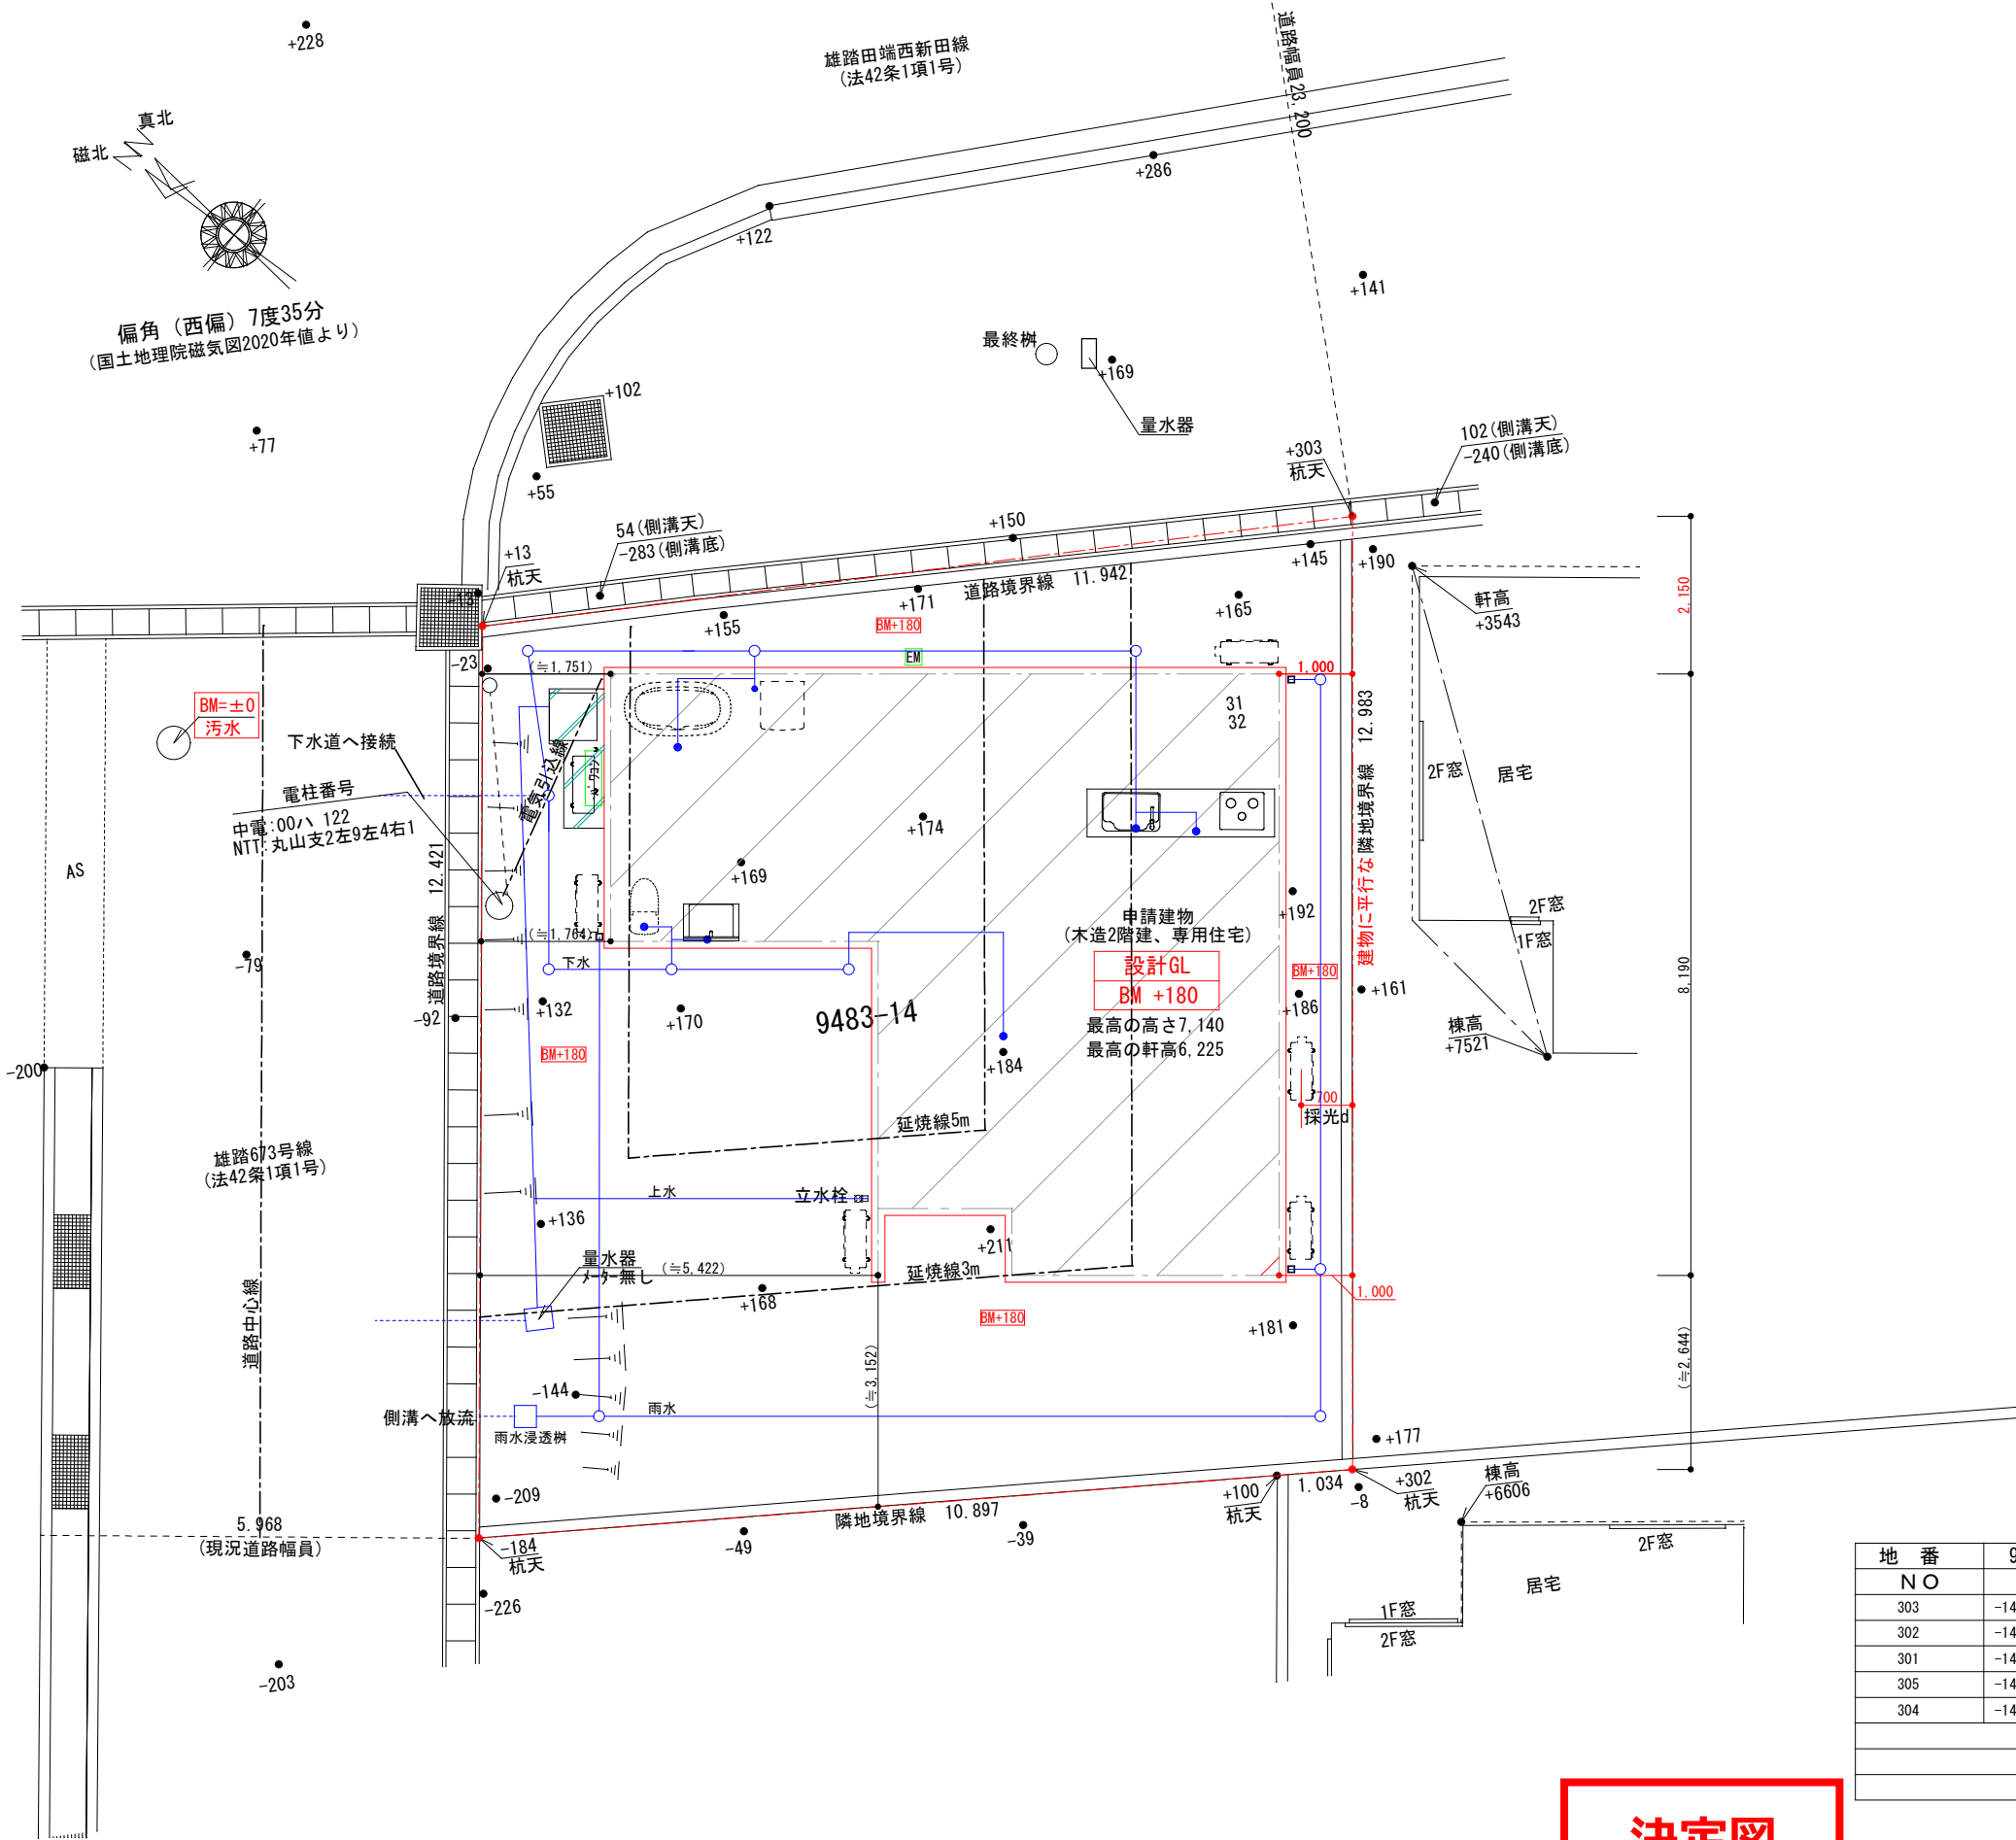

- ・設計GL+0=KBM+180
- ・ KBMからの設計地盤高さ
- ・ KBMからの現況地盤高さ
- ・隣地斜線・道路斜線 支障なし
- ・絶対高さ・日影規制 支障なし
- ・北側斜線 7m+1.25d 支障なし
- ・高度地区 有り
- ・盛土規制法の許可に係る盛土・切土無し

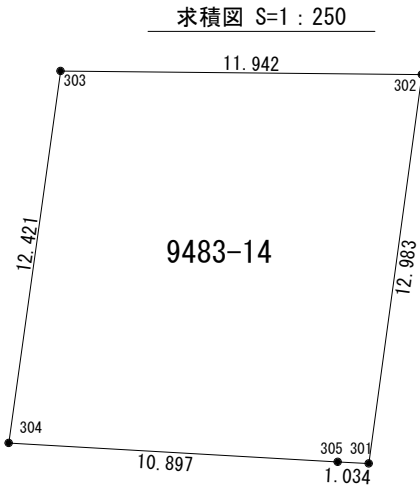

求積表

地番	9483-14			
NO	X _n	Y _n	Y _{n+1} - Y _{n-1}	X _n × (Y _{n+1} - Y _{n-1})
303	-143113.429	-79770.758	18.283	-2616542.822407
302	-143120.979	-79761.505	-0.152	21754.388808
301	-143129.930	-79770.910	-10.175	1456347.037750
305	-143129.239	-79771.680	-8.878	1270701.383842
304	-143121.958	-79779.788	0.922	-131958.445276
合計			301.542717	
合計面積			150.7713585	
地積			150.77 m ²	

決定図

※この図面は、現地の杭・構造物及び周辺建物を簡易測量し、
法務局備付地積測量図の成果を座標変換し、重ねたものです。