


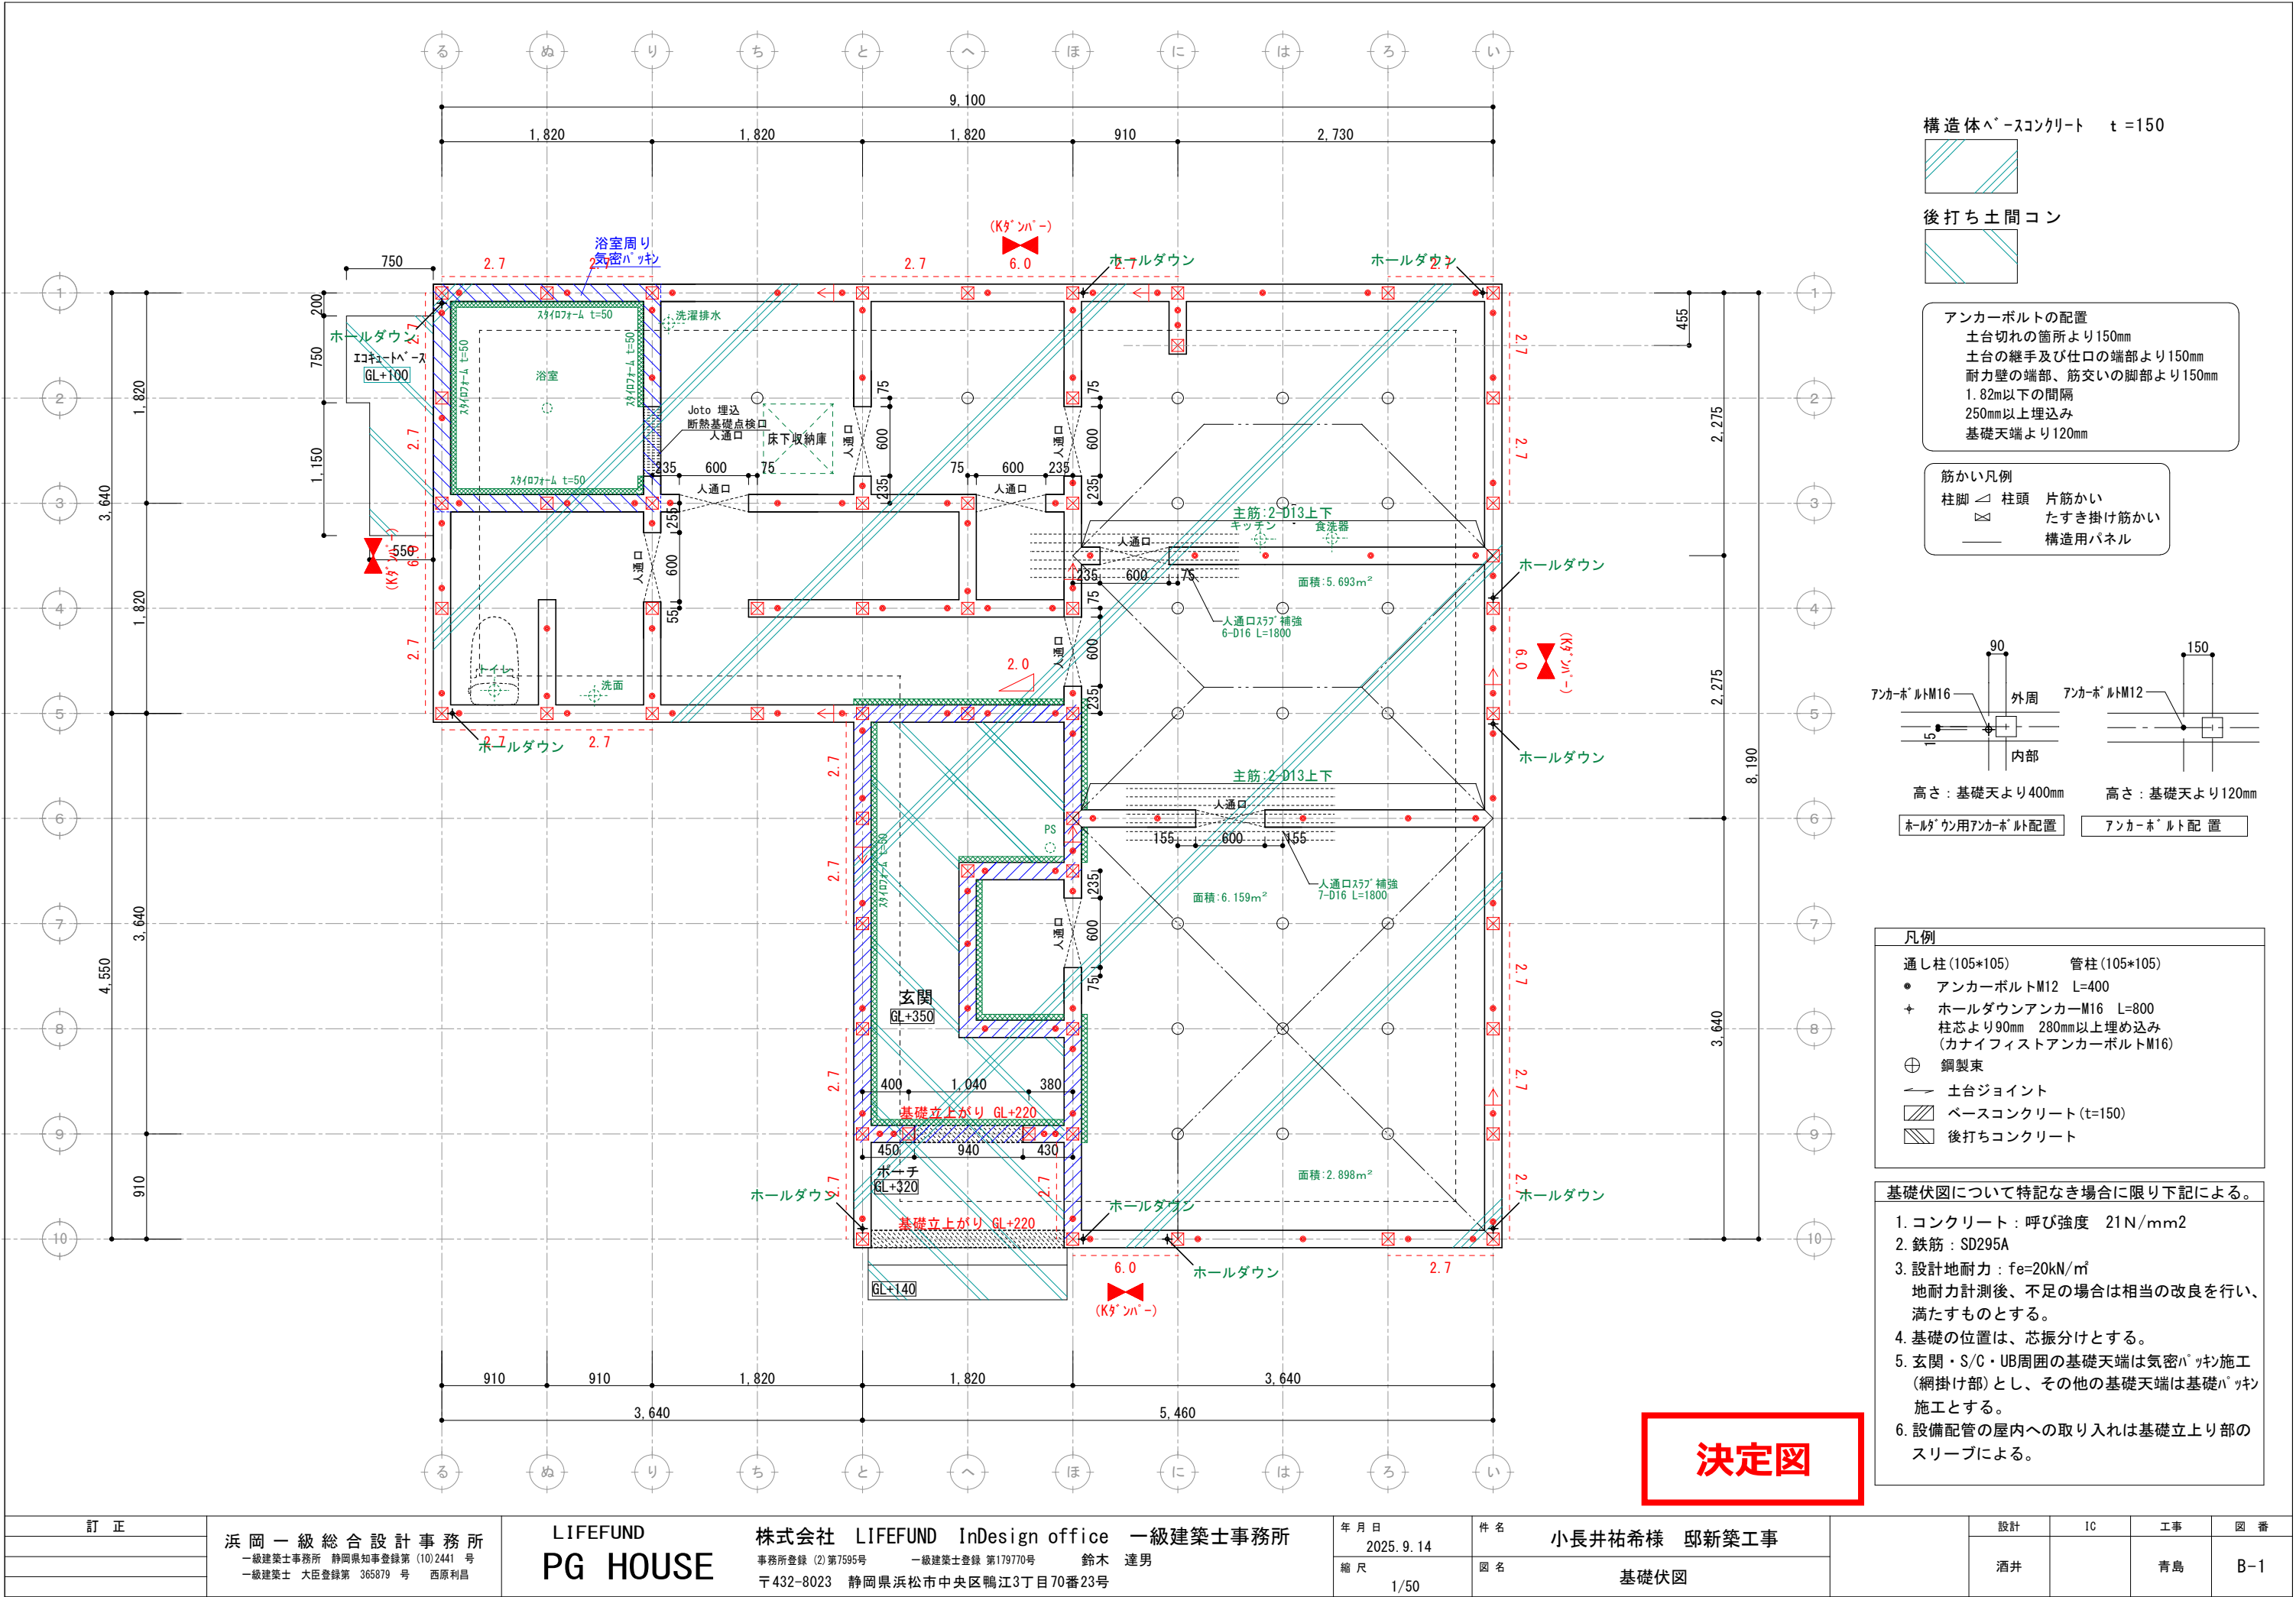


構造体ベースコンクリート t=150

後打ち土間コン

アンカーボルトの配置
土台切れの箇所より150mm
土台の継手及び仕口の端部より150mm
耐力壁の端部、筋交いの脚部より150mm
1.82m以下の間隔
250mm以上埋込み
基礎天端より120mm

筋かい凡例
柱脚 柱頭 筋かい
たすき掛け筋かい
構造用パネル

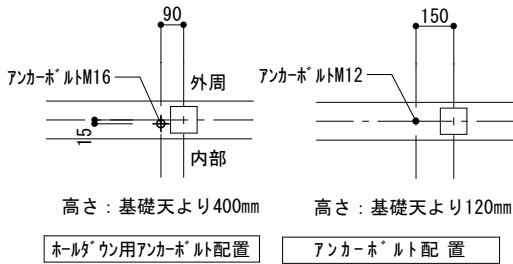

- 凡例
- 通し柱 (105*105) 管柱 (105*105)
 - アンカーボルト M12 L=400
 - + ホールダウンアンカー M16 L=800
柱芯より90mm 280mm以上埋め込み
(カナダファイストアンカーボルト M16)
 - ⊕ 鋼製束
 - 土台ジョイント
 - ベースコンクリート (t=150)
 - 後打ちコンクリート

- 基礎伏図について特記なき場合に限り下記による。
1. コンクリート：呼び強度 21N/mm²
 2. 鉄筋：SD295A
 3. 設計地耐力：fe=20kN/m²
地耐力計測後、不足の場合は相当の改良を行い、満たすものとする。
 4. 基礎の位置は、芯振分けとする。
 5. 玄関・S/C・UB周囲の基礎天端は気密パッキン施工（網掛け部）とし、その他の基礎天端は基礎パッキン施工とする。
 6. 設備配管の屋内への取り入れは基礎立上り部のスリーブによる。