

■ 仕 様				■ HEAT20 G2	
断熱工事		■ 床:カネライトフォーム t90		■ 土間床等の外周:スタイロフォームAT t50	
		■ 壁:アクアフォームLITE吹付 t90		■ 天井:アクファフォームLITE吹付 t220	
床下換気		■ 基礎パッキン JOTO (玄関・UB周り:気密基礎パッキン)			
防虫防蟻		■ 土壌処理・木部 ガントナーMC			
■ 外 部 仕 上 表				■ 22条地域	
部位		仕上・仕様・メーカー		色番・品番	
屋根		■ ガルバリウム鋼板(t0.35)UK立平 ニスクカラーPro GH 軒先通気金物 日本住環境株式会社【REV-15】		GHK01 Sブラック	
パラペット笠木		■ なし			
破風・鼻隠		■ なし			
雨樋	(軒樋)	■ Panasonic サーフeskエアFS-I型		ミルクホワイト	
	(縦樋)	■ Panasonic S30角樋		ミルクホワイト	
軒天	屋根軒	■ なし			
	ポーチ軒	■ ニチハ軒天5 木目調 910×1820×5		ライト	
	バルコニー軒	■ なし			
オーバーハング水切り		■			
外壁	通気金物(15mm)	■メイン	エクセレーション 光セラ15 ひより15	ミルクチタンホワイト	
	※下地面材:タイガーEXハイパー	■アクセントA	なし		
	防火認定 PC030BE-4028	■アクセントB	なし		
玄関ポーチ		■ 床 玄関タイルに同じ		-	
基礎		■ 立上り巾木: モルタル刷毛引き		-	
基礎水切り金物		■ JOTO鋼板製 防鼠材付き水切り JOTO:WMF-N35		ホワイト	
バルコニー	床・内壁	■ なし		-	
	笠木	■ なし			
外部建具		■ LIXIL EW(アルゴンガス高遮熱仕様LowEトリプルガラス クリア) ・SD、TSは、メーカー設定によるが、オペレーターハンドル優先とする ・オペレーター付サッシの場合は固定網戸とする ・グレモンハンドル式サッシの場合は可動網戸とする		外観 ホワイト 内観 ホワイト ※樹脂パッキン・網戸付	
シャッター		■ 手動シャッター(LDK掃き出し窓)			
軒天通気金物					
玄関扉		■ LIXIL ジエスタ2 K2仕様 LIXILファミロック タグキー×3 (電池式)		ドア型: M17 型 ドア色: チーク浮造 ハンドル: S型ハンドル 色 ブラック	
外部物干し金物		■ 川口技研RK型-55 外壁付		ピュアホワイト	
換気フード		■ 局所換気扇(トイレ 浴室 キッチンフード) 防火ダンパー無		外気フード: ホワイト	
		■ ダクトレス熱交換換気システム (日本スティーベル株式会社) VLR-70E 防火ダンパー無		外気フード: W ホワイト 室内パネル ホワイト	

■ 構 造 概 要					
基礎	■ RCベタ基礎コンクリート				
通し柱・管柱	■ 構造用集成材 105×105		間柱	■ 集成材	
土台	■ 桧 105×105	大引き	■ 桧 90*90	筋交い	■ 構造用製材 火打梁 ■ 鋼製火打(当社基準により米松あり)
桁・梁	■ 構造用製材及び集成材		制震装置	■ Kダンパー (株)アイ・エム・エー	
■ 設 備 装 着 品					
住宅設備	部位	メーカー	商品名 ※ 詳細は見積り、プレゼン参照	見積りNo.	(日付)
	キッチン	LIXIL	■ ES I型 扉 ブリーチドウッド 天板 人造大理石(ソルティホワイト) キッチンパネル フレッシュホワイト 深型食洗器 標準IH, サイドフード HVR(ホワイト) スリム取手 シャインニッケル	見積り番号 : M25078034870-004-2	(日付) 2025.07.28
	バックカウンタ ※オプション	LIXIL	■ ES L1800(W900スライドストッカー×2)	見積り番号 : M25078034870-004-3	(日付) 2025.07.28
	浴室	LIXIL	■ AX1616 PGハウス標準仕様 エコベンチ浴槽 開き戸 アクセント壁: マーフィルベージュ 浴槽 ホワイト 床 ベージュ マグネットシェフ: ホワイト	見積り番号 : M25078034870-004-1	(日付) 2025.07.28
	1Fトイレ	LIXIL	■ ベアシアシャワートイレ 白 ● タオル掛け: KF-AA70D(リング) タンク手洗 無し ● 紙巻き器: なし(支給品取付)	見積り番号 : M25078034870-004-5	(日付) 2025.07.28
	2Fトイレ	LIXIL	■ ベアシアシャワートイレ 白 ● タオル掛け: KF-AA70D(リング) タンク手洗 有り ● 紙巻き器: なし(支給品取付)	見積り番号 : M25078034870-004-6	(日付) 2025.07.28
	洗面台	LIXIL	■ EV W750(D500タイプ) 扉:クリエモカ [引出しタイプ シングルハンドシャワー スタンダードLED三面鏡 その他 ● タオル掛け: KF-AA71D(バー)	見積り番号 : M25078034870-004-4	(日付) 2025.07.28
給排水設備	給湯器	■ エコキュート370L Panasonic Sシリーズ スタンダードモデル 追い焚きフルオート			
	排水	■ 下水			
	外水栓	■ 1 カ所 (平面図参照)	■ 外部立栓柱: PVC製 水栓柱12型【前澤化成工業】		
	外部ガーデンパン	■ 無し			
	その他	■ 洗濯機用単水栓: 緊急止水弁付 ■ 洗濯機用排水: トラップ金物(標準) ■ 排水さや管(長期優良住宅仕様)			
ガス配管設備	■ なし (配置図・平面図参照)				
電気設備	インターホン	■ パナソニック VL-SE31XL			
	TVアンテナ	■ UHF + BS・110度CS／CSアンテナ [2K・4K・8K対応] ■ ホワイト			
	エアコン	■ 設置場所:			
	ソーラー	■ あり(Qセルズ) 12 枚 5.28 KW Re.RISE-G3 440 (1722×1134×30)			
	※標準搭載	※メーカーのモデルチェンジ等で後継品に変更される可能性あり ■ 屋外パワコン			
その他					

決定図

決定図


内 部 仕 上 表 （壁下地:石膏ボード12.5mm/天井下地:9.5mm）※脱衣室:床合板特類 下地									
階		床	巾木	壁	品番	廻 縁	天 井	品番	特記事項
1F	ポーチ	LIXILパセオ300/PSO-FIO 4							
	玄関	LIXILパセオ300/PSO-FIO 4	ライン巾木(W)	ビニルクロス	SLP-252	突付	ビニルクロス	SLP-252	
	ホール①	イタ銘木フロアーラステックt12 ナラ桎3P	ライン巾木(W)	ビニルクロス	SLP-252	突付	ビニルクロス	SLP-252	
	ホール②	イタ銘木フロアーラステックt12 ナラ桎3P	ライン巾木(W)	ビニルクロス	SLP-252	突付	ビニルクロス	SLP-252	
	LDK	イタ銘木フロアーラステックt12 ナラ桎3P	ライン巾木(W)	ビニルクロス	SLP-252	突付	ビニルクロス	SLP-252	シンコール SLP391
	WIC①	イタ銘木フロアーラステックt12 ナラ桎3P	ライン巾木(W)	ビニルクロス	SLP-252	突付	ビニルクロス	SLP-252	
	脱衣ランドリー	フロアタイルt2.3 サンゲツIS-2070	H40ソフト巾木W97	ビニルクロス	SLP-252	突付	ビニルクロス	SLP-252	シンコール SLP401
2F	WC①	フロアタイルt2.3 サンゲツIS-2070	H40ソフト巾木W97	ビニルクロス	SLP-252	突付	ビニルクロス	SLP-252	シンコール BB2736
	洋室①	イタ銘木フロアーラステックt12 ナラ桎3P	ライン巾木(W)	ビニルクロス	SLP-252	突付	ビニルクロス	SLP-252	シンコール TRM15004
	洋室②	イタ銘木フロアーラステックt12 ナラ桎3P	ライン巾木(W)	ビニルクロス	SLP-252	突付	ビニルクロス	SLP-252	シンコール SLP401
	洋室③	イタ銘木フロアーラステックt12 ナラ桎3P	ライン巾木(W)	ビニルクロス	SLP-252	突付	ビニルクロス	SLP-252	シンコール SLP401
	洋室④	イタ銘木フロアーラステックt12 ナラ桎3P	ライン巾木(W)	ビニルクロス	SLP-252	突付	ビニルクロス	SLP-252	
	WC②	フロアタイルt2.3 サンゲツIS-2070	H40ソフト巾木W97	ビニルクロス	SLP-252	突付	ビニルクロス	SLP-252	シンコール BL2914
	WIC②	イタ銘木フロアーラステックt12 ナラ桎3P	ライン巾木(W)	ビニルクロス	SLP-252	突付	ビニルクロス	SLP-252	
	ホール③	イタ銘木フロアーラステックt12 ナラ桎3P	ライン巾木(W)	ビニルクロス	SLP-252	突付	ビニルクロス	SLP-252	
	吹抜け			ビニルクロス	SLP-252	突付	ビニルクロス		シンコール BB2503
物入・収納・CL etc		※接続する部屋と同仕様とする							

上 框 ※	■ LIXILラシッサS 上框のみ30×150	色:	クリエペール
階 段	■ LIXIL KA 階段	ササラ:	プレシャスホワイト
KA階段で対応できない場合、オプション	段板 :	クリエペール	蹴込板: プレシャスホワイト
にてラシッサS階段	ラウンド手摺:	クリエペール	手摺金物 プレシャスホワイト
	上段框:	クリエペール	長尺笠木156: LIXIL 段板同色
窓 枠	■ LIXIL スマート10	色	プレシャスホワイト
	※浴室ドア枠 フクビ3方枠 [ホワイト]		
キッチン笠木	■ ゴム集成カウンター(オスモカラー)	色	3062フロアークリアmatt
カウンター	形状 L型(ジョイント加工)		t=30
天井点検口	■ 天井アルミ点検口枠 450角 TAN45BW	フクビ化学工業 ミルキーホワイト	
床下収納庫	■ 高気密型床下点検口断熱型 SPF-R6060 城東テクノ	収納付	(脱衣室) ライトグレー(LG)
トイレ棚	■ 1,2階トイレ D250	アートランバー棚(シェルホワイト)	
室内物干し金物	■ 川口技研SPC型1セット		
	■ なし	色	
下足入	■ LIXILラシッサS	色	クリエペール
プッシュタイプ	サイズ: W800 D400	形状:	二の字型


支給品	■ 無し
備考	※付框は(30×150)プレシャスホワイト 可動棚アートランバー色 シェルホワイト 棚受金物類は全てホワイト 下足入 入隅 サイドパネルあり

内 部 建 具 表							
LIXIL		建具色：プレシャスホワイト		枠色 ： 扉同色		※その他、下記特記による	
ラフィス		把手 ： スクエアL（シャインニッケル） 丁番 固定枠（156） 外付戸当り ガイドピン床色合せ 引戸のみ上吊W70フタモーション					
階	No	室名	形式	枠外W サイズ	デザイン	枠色	特記事項
				枠外H サイズ	建具色	把手	
1	1	LDK	片引き戸	—	RAA	—	アウトセット
	WD			2400	—	—	
	2	LDK	片引き戸	—	RAA	—	アウトセット
	WD			2400	—	—	
	3	WC①	片引き戸	—	RAA	—	明り窓・表示錠
	WD			2400	—	—	
	4	脱衣ランドリー	片引き戸	—	RAA	—	明り窓・表示錠
	WD			2400	—	—	
	5	脱衣ランドリー	片引き戸	—	RAA	—	明り窓・表示錠
	WD			2400	—	—	
	6	段下物入	観音開	—	RAA	—	
	WD			2400	—	—	
7	パントリー	観音開	—	RAA	—		
WD			2400	—	—		
2	8	洋室②	片開き戸	—	RAA	—	
	WD			2400	—	—	
	9	洋室①	片開き戸	—	RAA	—	
	WD			2400	—	—	
	10	WC②	片引き戸	—	RAA	—	アウトセット 明り窓・表示錠
	WD			2400	—	—	
	11	洋室③	片開き戸	—	RAA	—	
	WD			2400	—	—	
	12	洋室④	片開き戸	—	RAA	—	
	WD			2400	—	—	

	浜 岡 一 級 総 合 設 計 事 務 所		株式会社 LIFEFUND InDesign office	一級建築士事務所	年 月 日	2025/9/14	件名	小長井祐希 様邸 新築工事				
	一級建築士事務所 静岡県知事登録第 (10)2441 号		事務所登録 (2) 第7595号	一級建築士登録 第179770号	鈴木 達男	縮尺		図面	仕上表 2			
	一級建築士 大臣登録第 365879 号 西原利昌		〒432-8023 静岡県浜松市中央区鴨江3丁目70番23号									
								設計	IC	工務	図 番	
								酒井		青島	1-2	

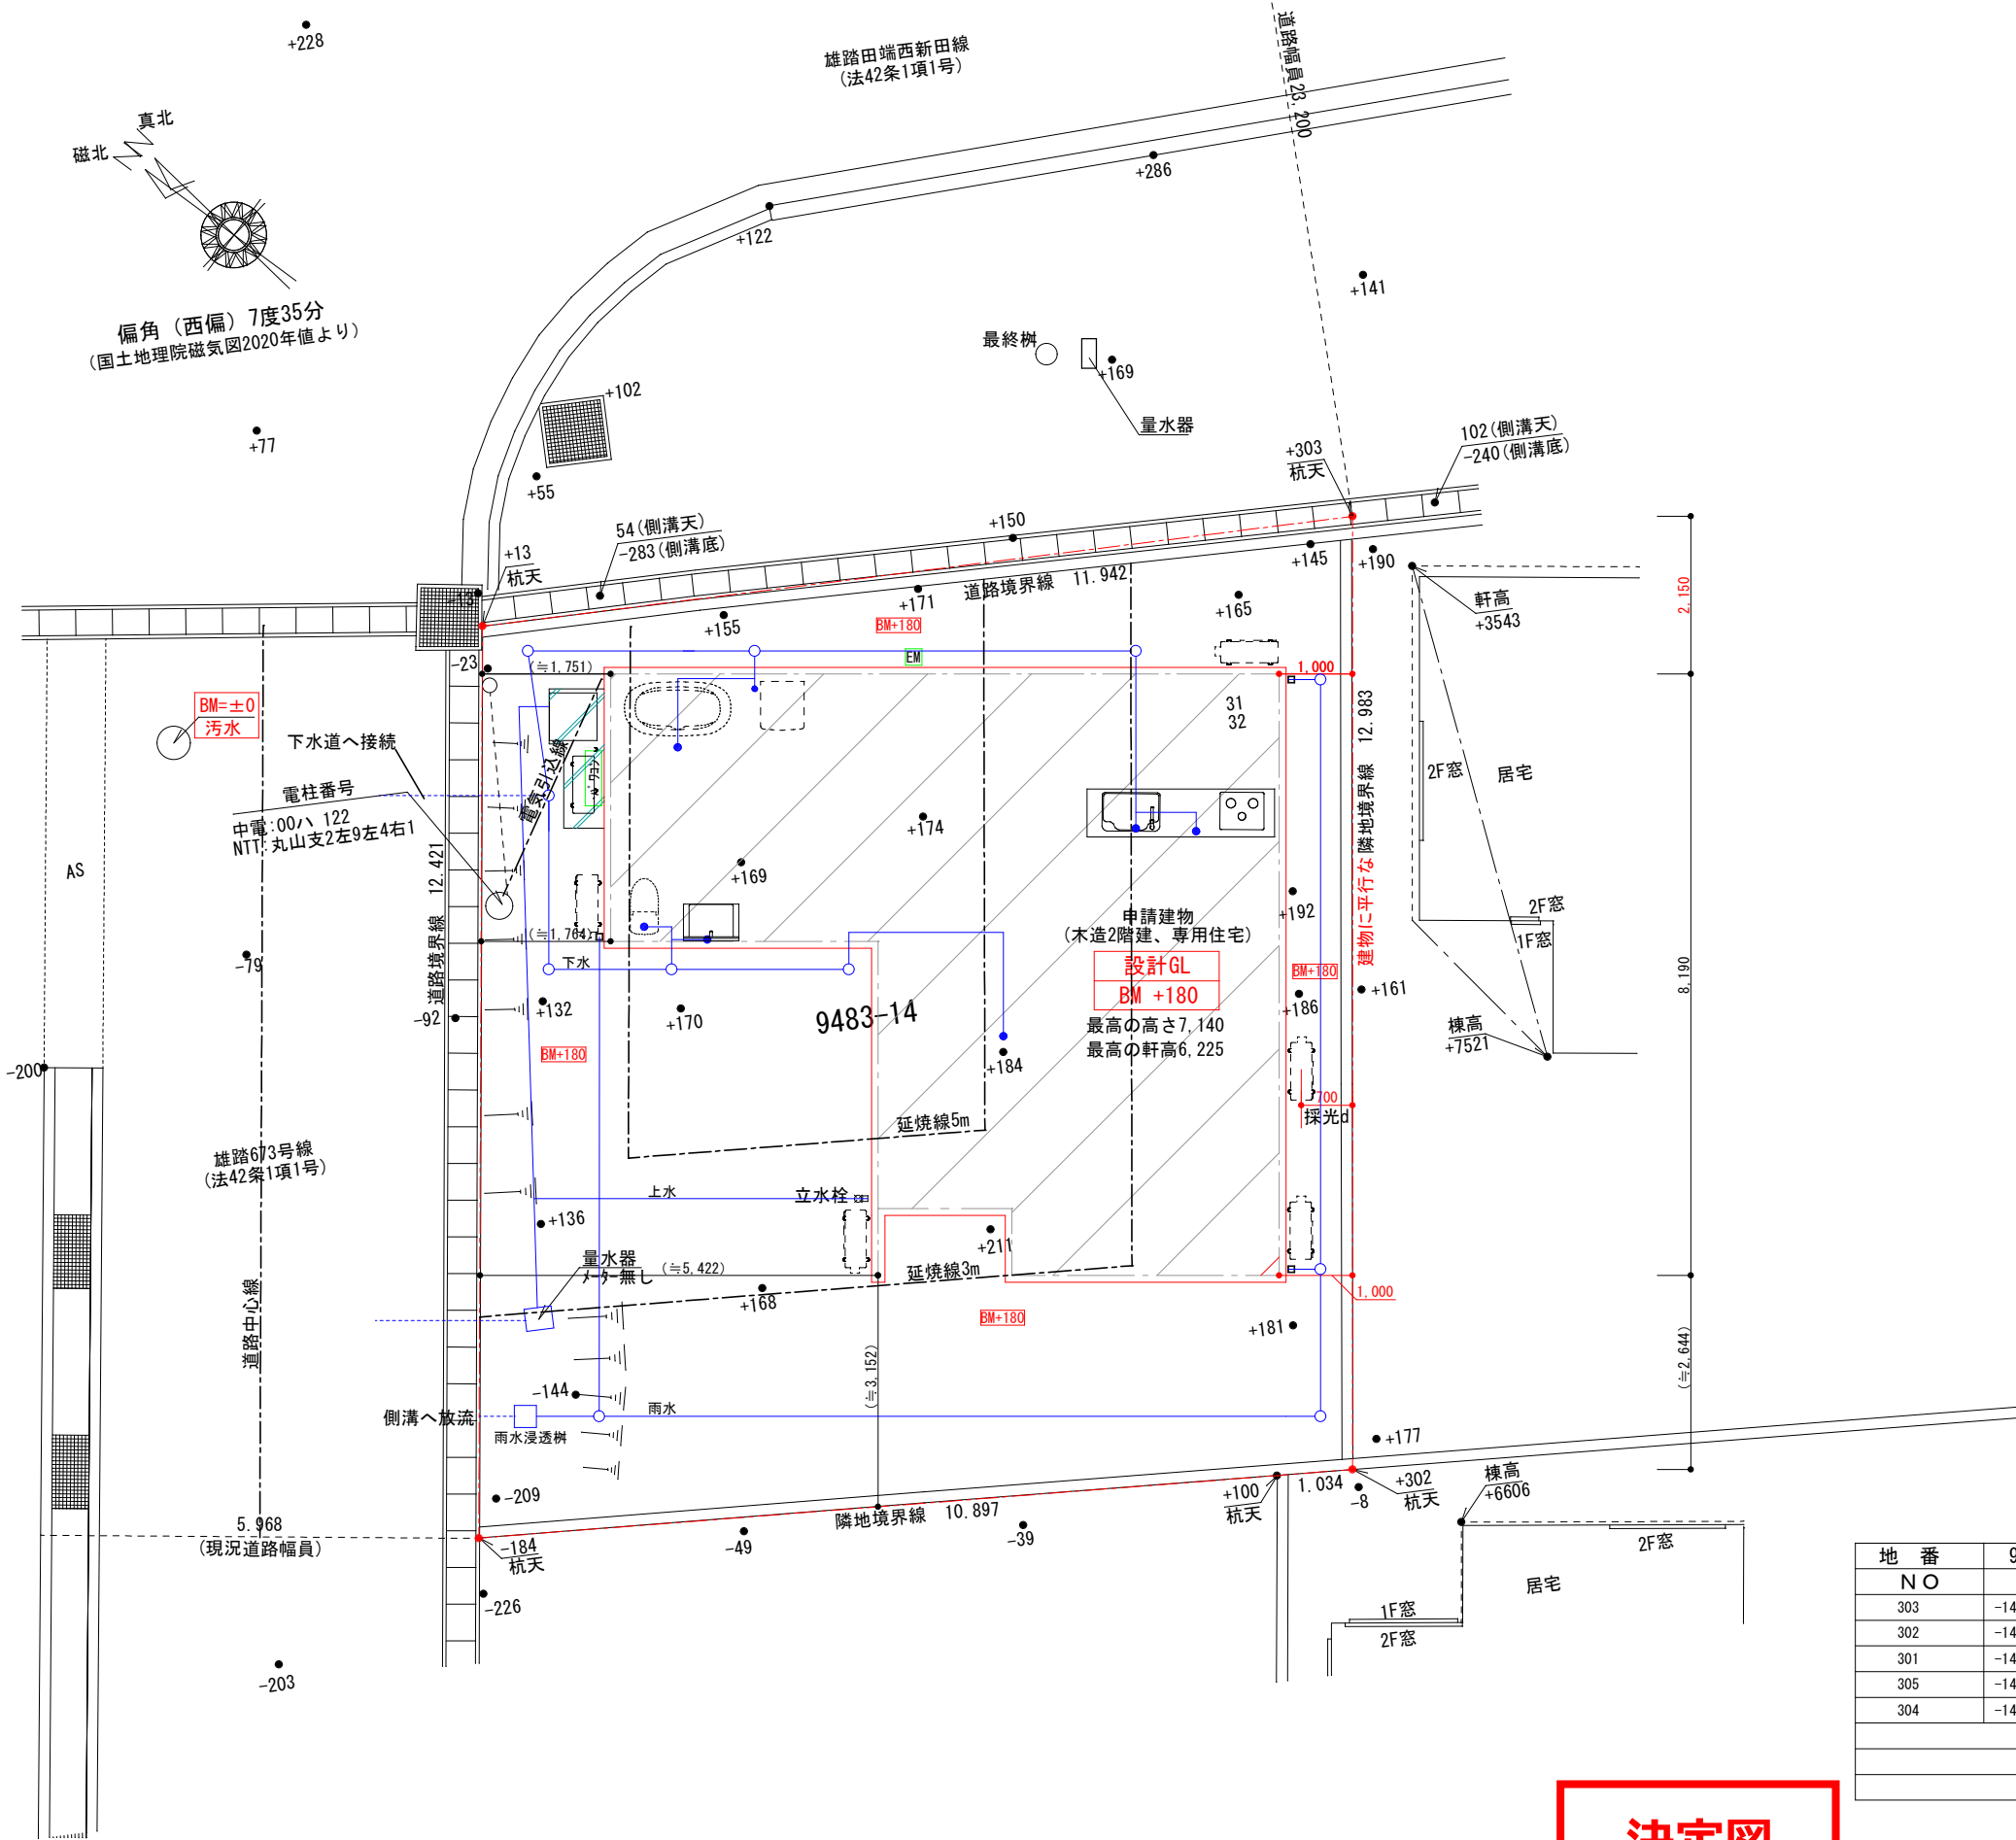

- ・設計GL+0=KBM+180
- ・ KBMからの設計地盤高さ
- ・ KBMからの現況地盤高さ
- ・隣地斜線・道路斜線 支障なし
- ・絶対高さ・日影規制 支障なし
- ・北側斜線 7m+1.25d 支障なし
- ・高度地区 有り
- ・盛土規制法の許可に係る盛土・切土無し

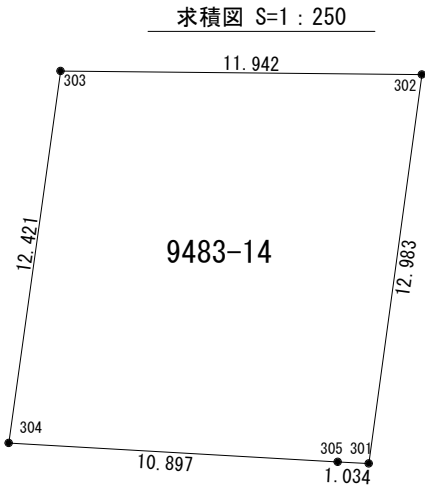


求積表

地番	9483-14				
NO	X _n	Y _n	Y _{n+1} - Y _{n-1}	X _n × (Y _{n+1} - Y _{n-1})	
303	-143113.429	-79770.758	18.283	-2616542.822407	
302	-143120.979	-79761.505	-0.152	21754.388808	
301	-143129.930	-79770.910	-10.175	1456347.037750	
305	-143129.239	-79771.680	-8.878	1270701.383842	
304	-143121.958	-79779.788	0.922	-131958.445276	
合計				301.542717	
合計面積				150.7713585	
地積				150.77 m ²	

決定図


※この図面は、現地の杭・構造物及び周辺建物を簡易測量し、
法務局備付地積測量図の成果を座標変換し、重ねたものです。

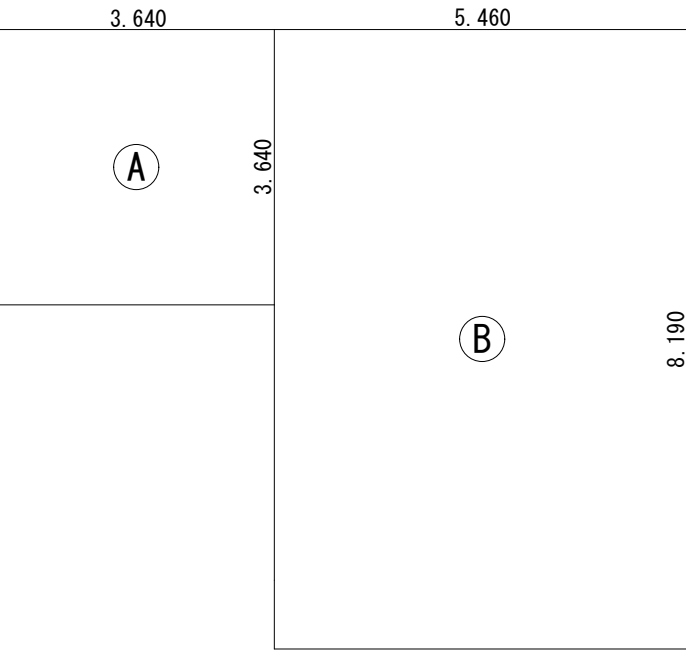

建築面積求積図 S=1/100

建築面積求積表


番号	計算式	(m)	面積 (㎡)
Ⓐ	3.640 × 3.640		13.2496
Ⓑ	5.460 × 8.190		44.7174
合計			57.9670 57.96 (17.5坪)

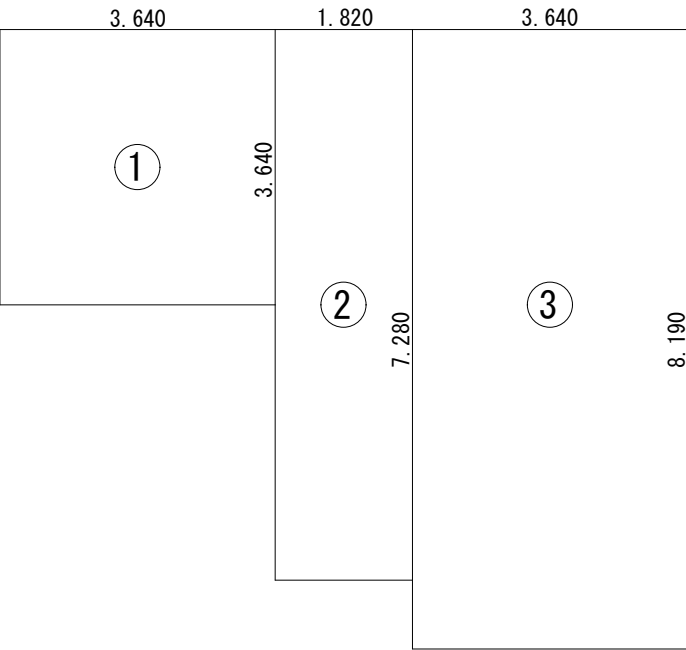

1階床面積図 S=1/100

1階床面積求積表

番号	計算式	(m)	面積 (㎡)
①	3.640 × 3.640		13.2496
②	1.820 × 7.280		13.2496
③	3.640 × 8.190		29.8116
合計			56.3108 56.31 (17.0坪)

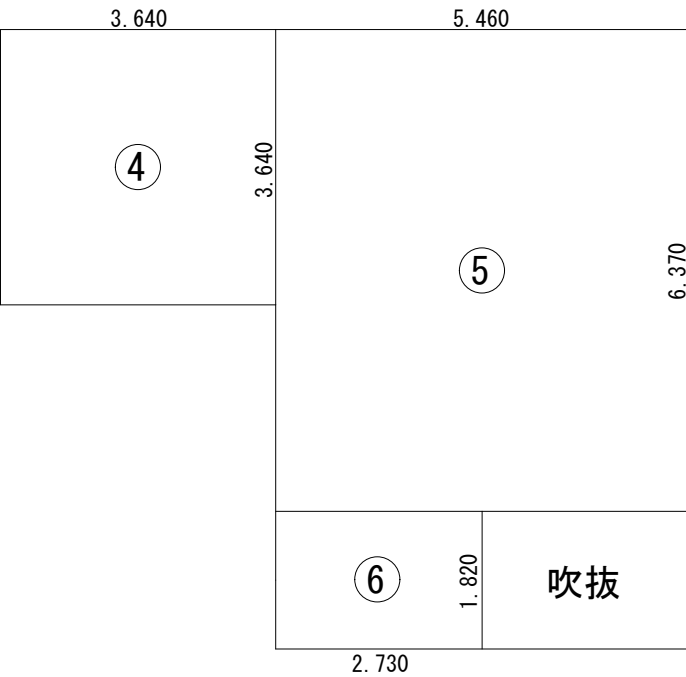

2階床面積図 S=1/100


2階床面積求積表

番号	計算式	(m)	面積 (㎡)
④	3.640 × 3.640		13.2496
⑤	5.460 × 6.370		34.7802
⑥	2.730 × 1.820		4.9686
合計			52.9984 52.99 (16.0坪)

延べ床面積表

	番号	(m)	面積 (㎡)
1階床面積	① ② ③		56.31
2階床面積	④ ⑤ ⑥		52.99
合計			109.30 (33.06坪)

決定図

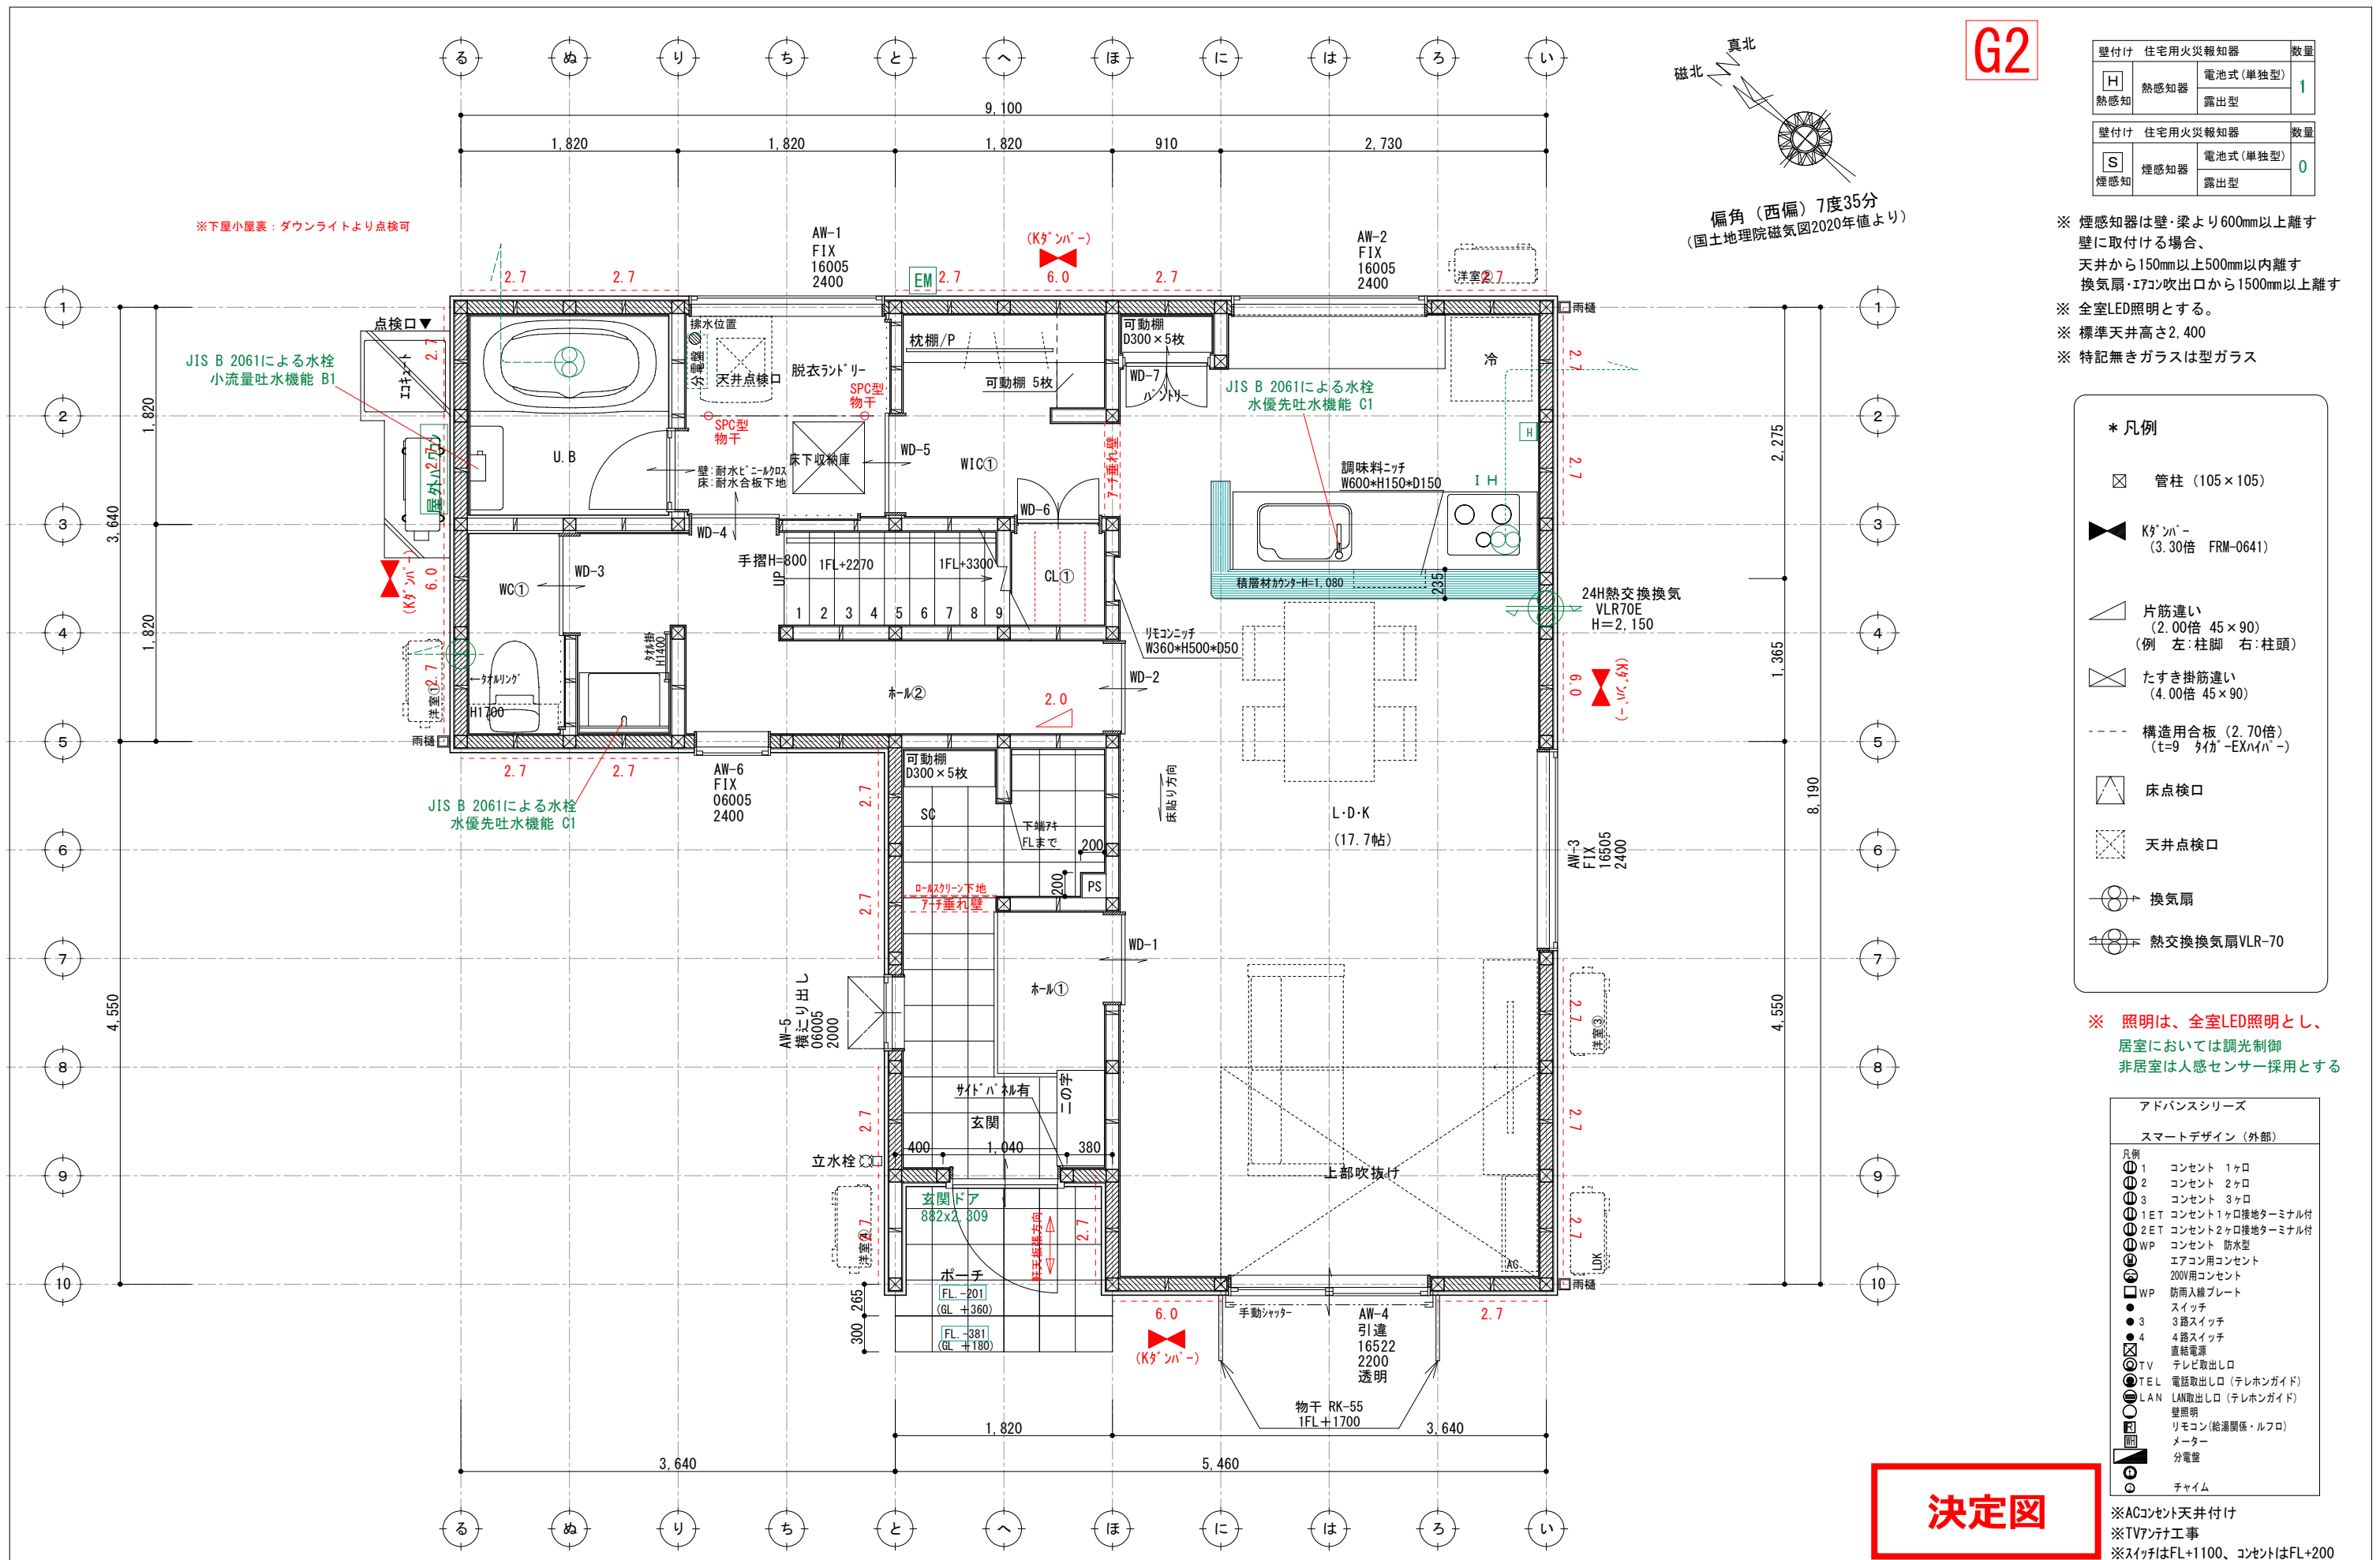

壁付け 住宅用火災報知器			数量
H	熱感知器	電池式(単独型)	1
	熱感知	露出型	
壁付け 住宅用火災報知器			数量
S	煙感知器	電池式(単独型)	0
	煙感知	露出型	

※ 煙感知器は壁・梁より600mm以上離す
壁に取付ける場合、
天井から150mm以上500mm以内離す
換気扇・エアコン吹出口から1500mm以上離す

※ 全室LED照明とする。

※ 標準天井高さ2,400


※ 特記無きガラスは型ガラス

- * 凡例**
- 管柱 (105×105)
 - Kダクト (3.30倍 FRM-0641)
 - 片筋違い (2.00倍 45×90)
(例 左:柱脚 右:柱頭)
 - たすき掛筋違い (4.00倍 45×90)
 - 構造用合板 (2.70倍)
(t=9 9材 EXハイバー)
 - 床点検口
 - 天井点検口
 - 換気扇
 - 熱交換換気扇VLR-70



※ 照明は、全室LED照明とし、
居室においては調光制御
非居室は人感センサー採用とする

アドバンスシリーズ			
スマートデザイン (外部)			
凡例	1	コンセント	1ヶ所
2	コンセント	2ヶ所	
3	コンセント	3ヶ所	
1ET	コンセント1ヶ所接地ターミナル付		
2ET	コンセント2ヶ所接地ターミナル付		
WP	コンセント 防水型		
エアコン	エアコン用コンセント		
200V	200V用コンセント		
WP	防雨入線プレート		
スイッチ	スイッチ		
3	3路スイッチ		
4	4路スイッチ		
直結電源	直結電源		
TV	テレビ取出口		
TEL	電話取出口 (テレホンガイド)		
LAN	LAN取出口 (テレホンガイド)		
壁照明	壁照明		
リモコン	リモコン (給湯関係・ルフロ)		
メーター	メーター		
分電盤	分電盤		
チャイム	チャイム		

※ACコンセント天井付け
※TVアンテナ工事
※スイッチはFL+1100、コンセントはFL+200

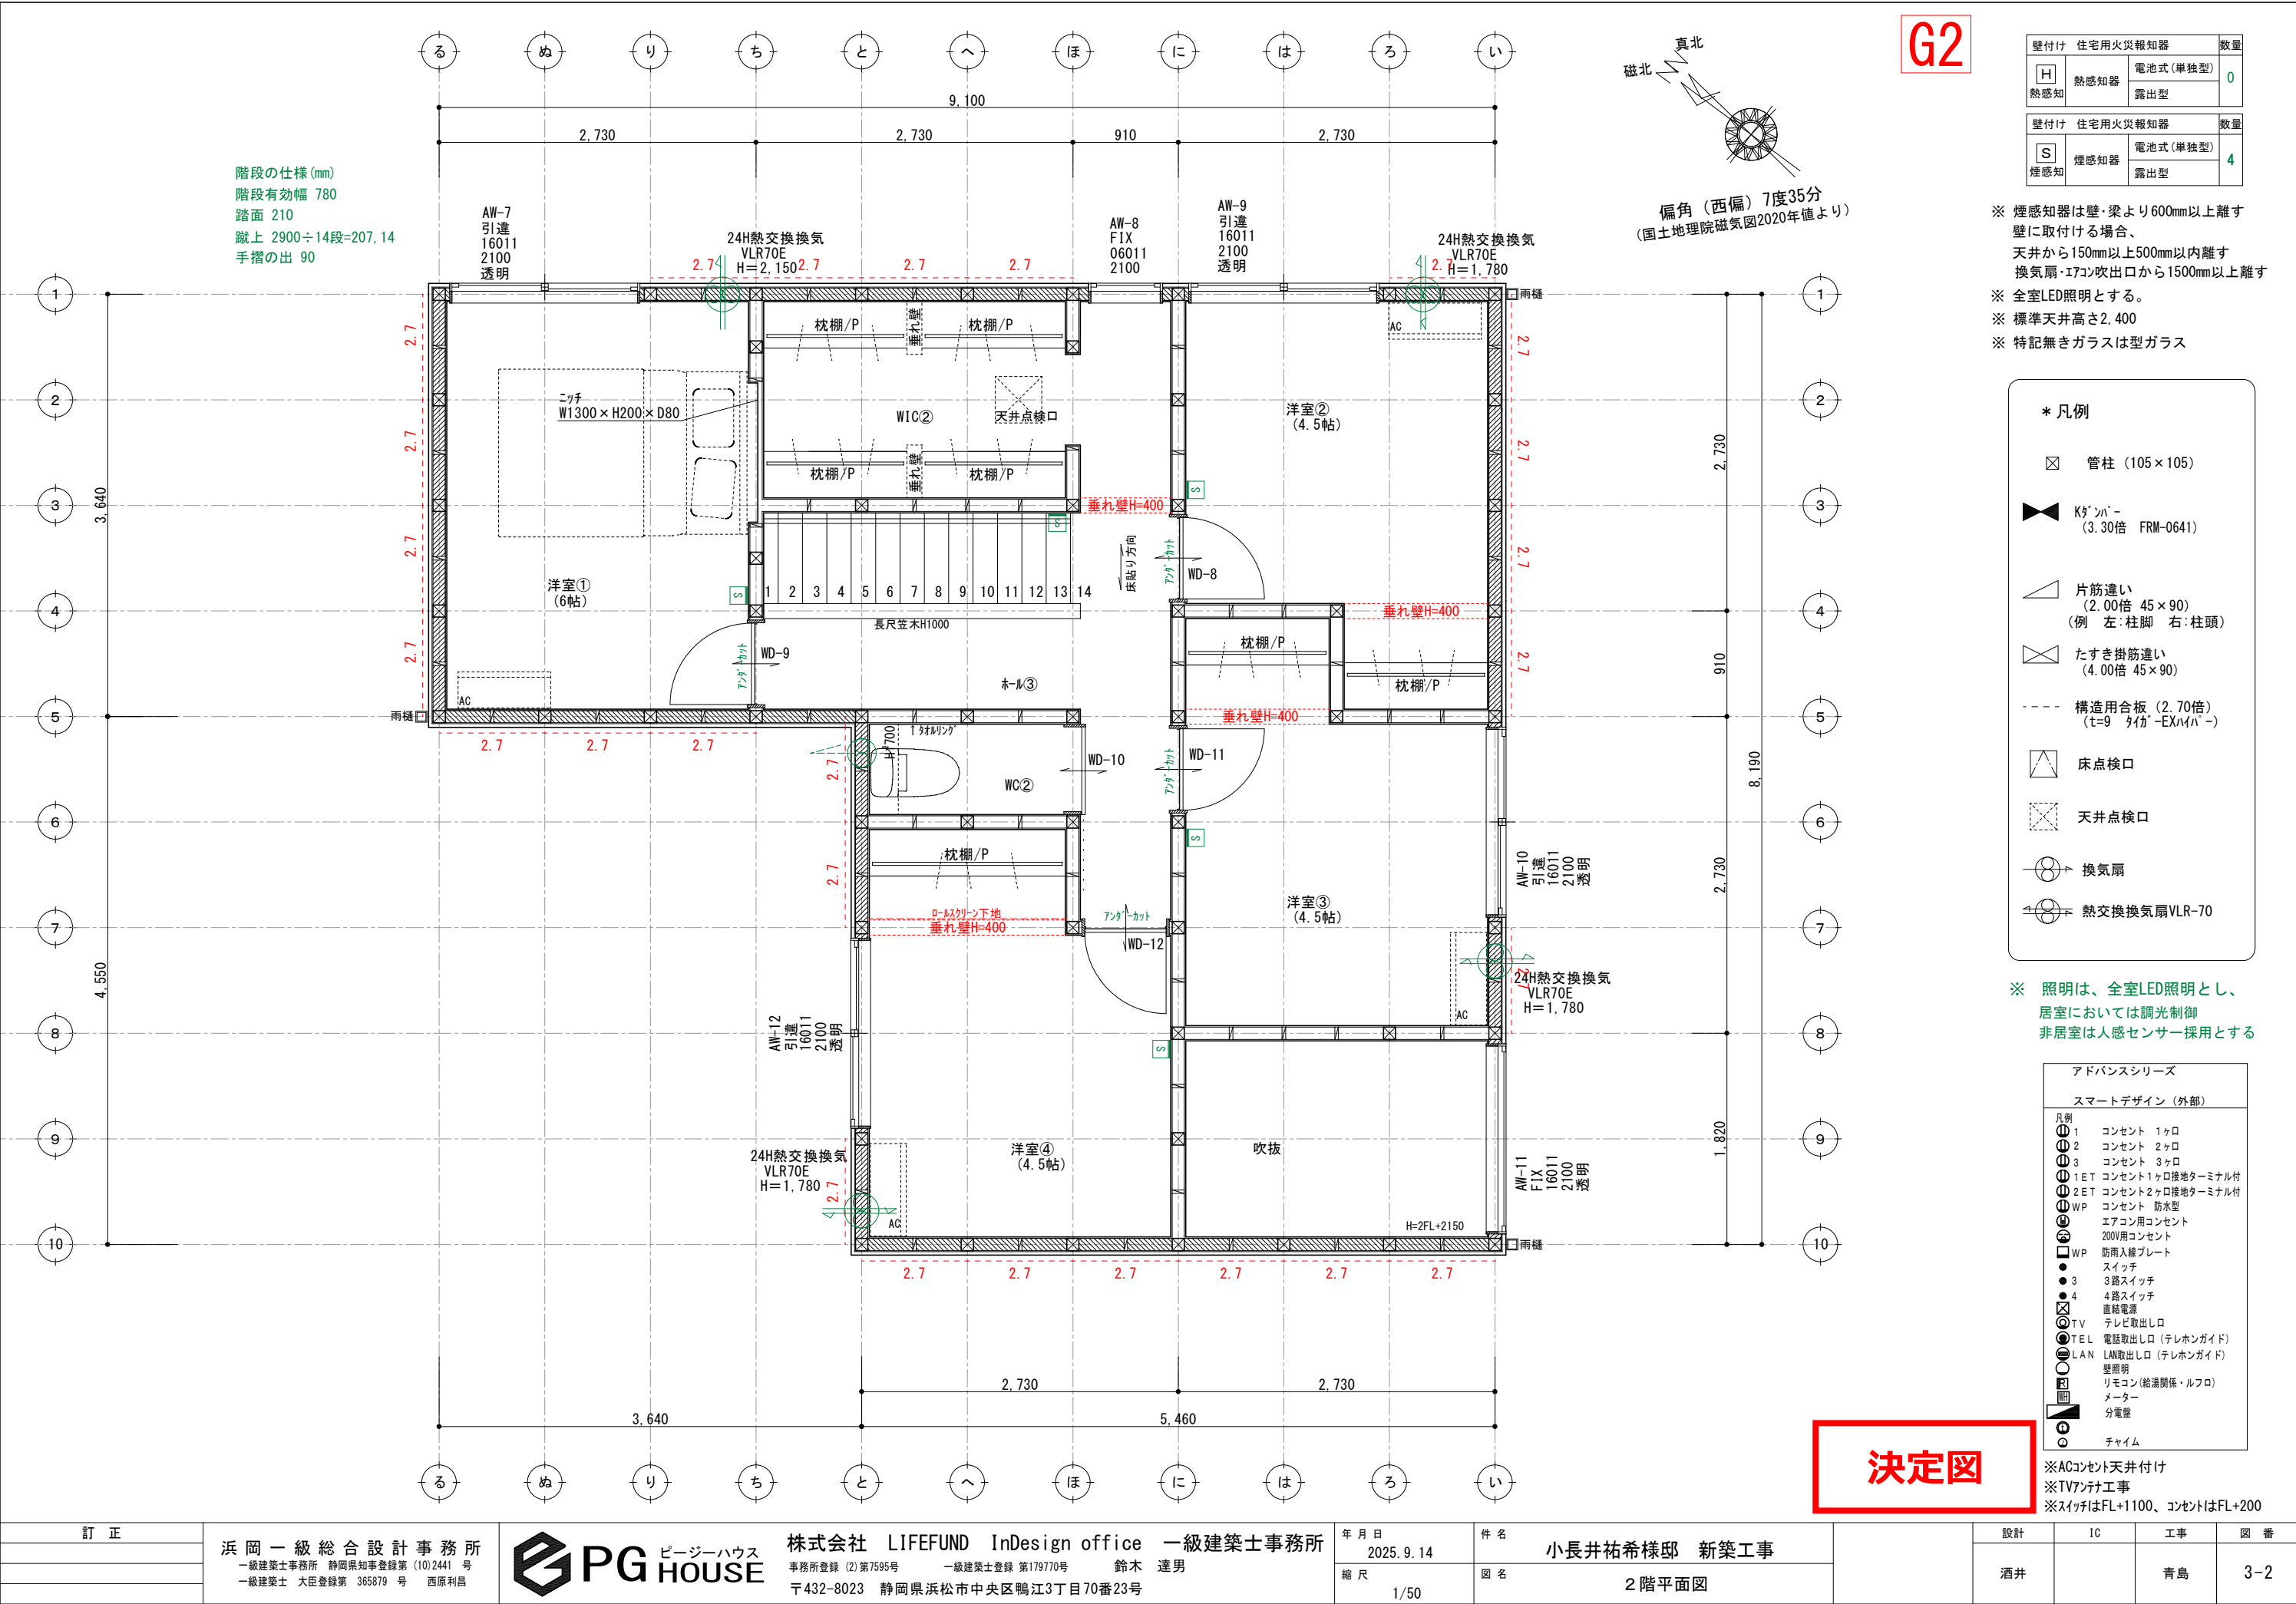



GX住宅 (Cube J付)
太陽光あり

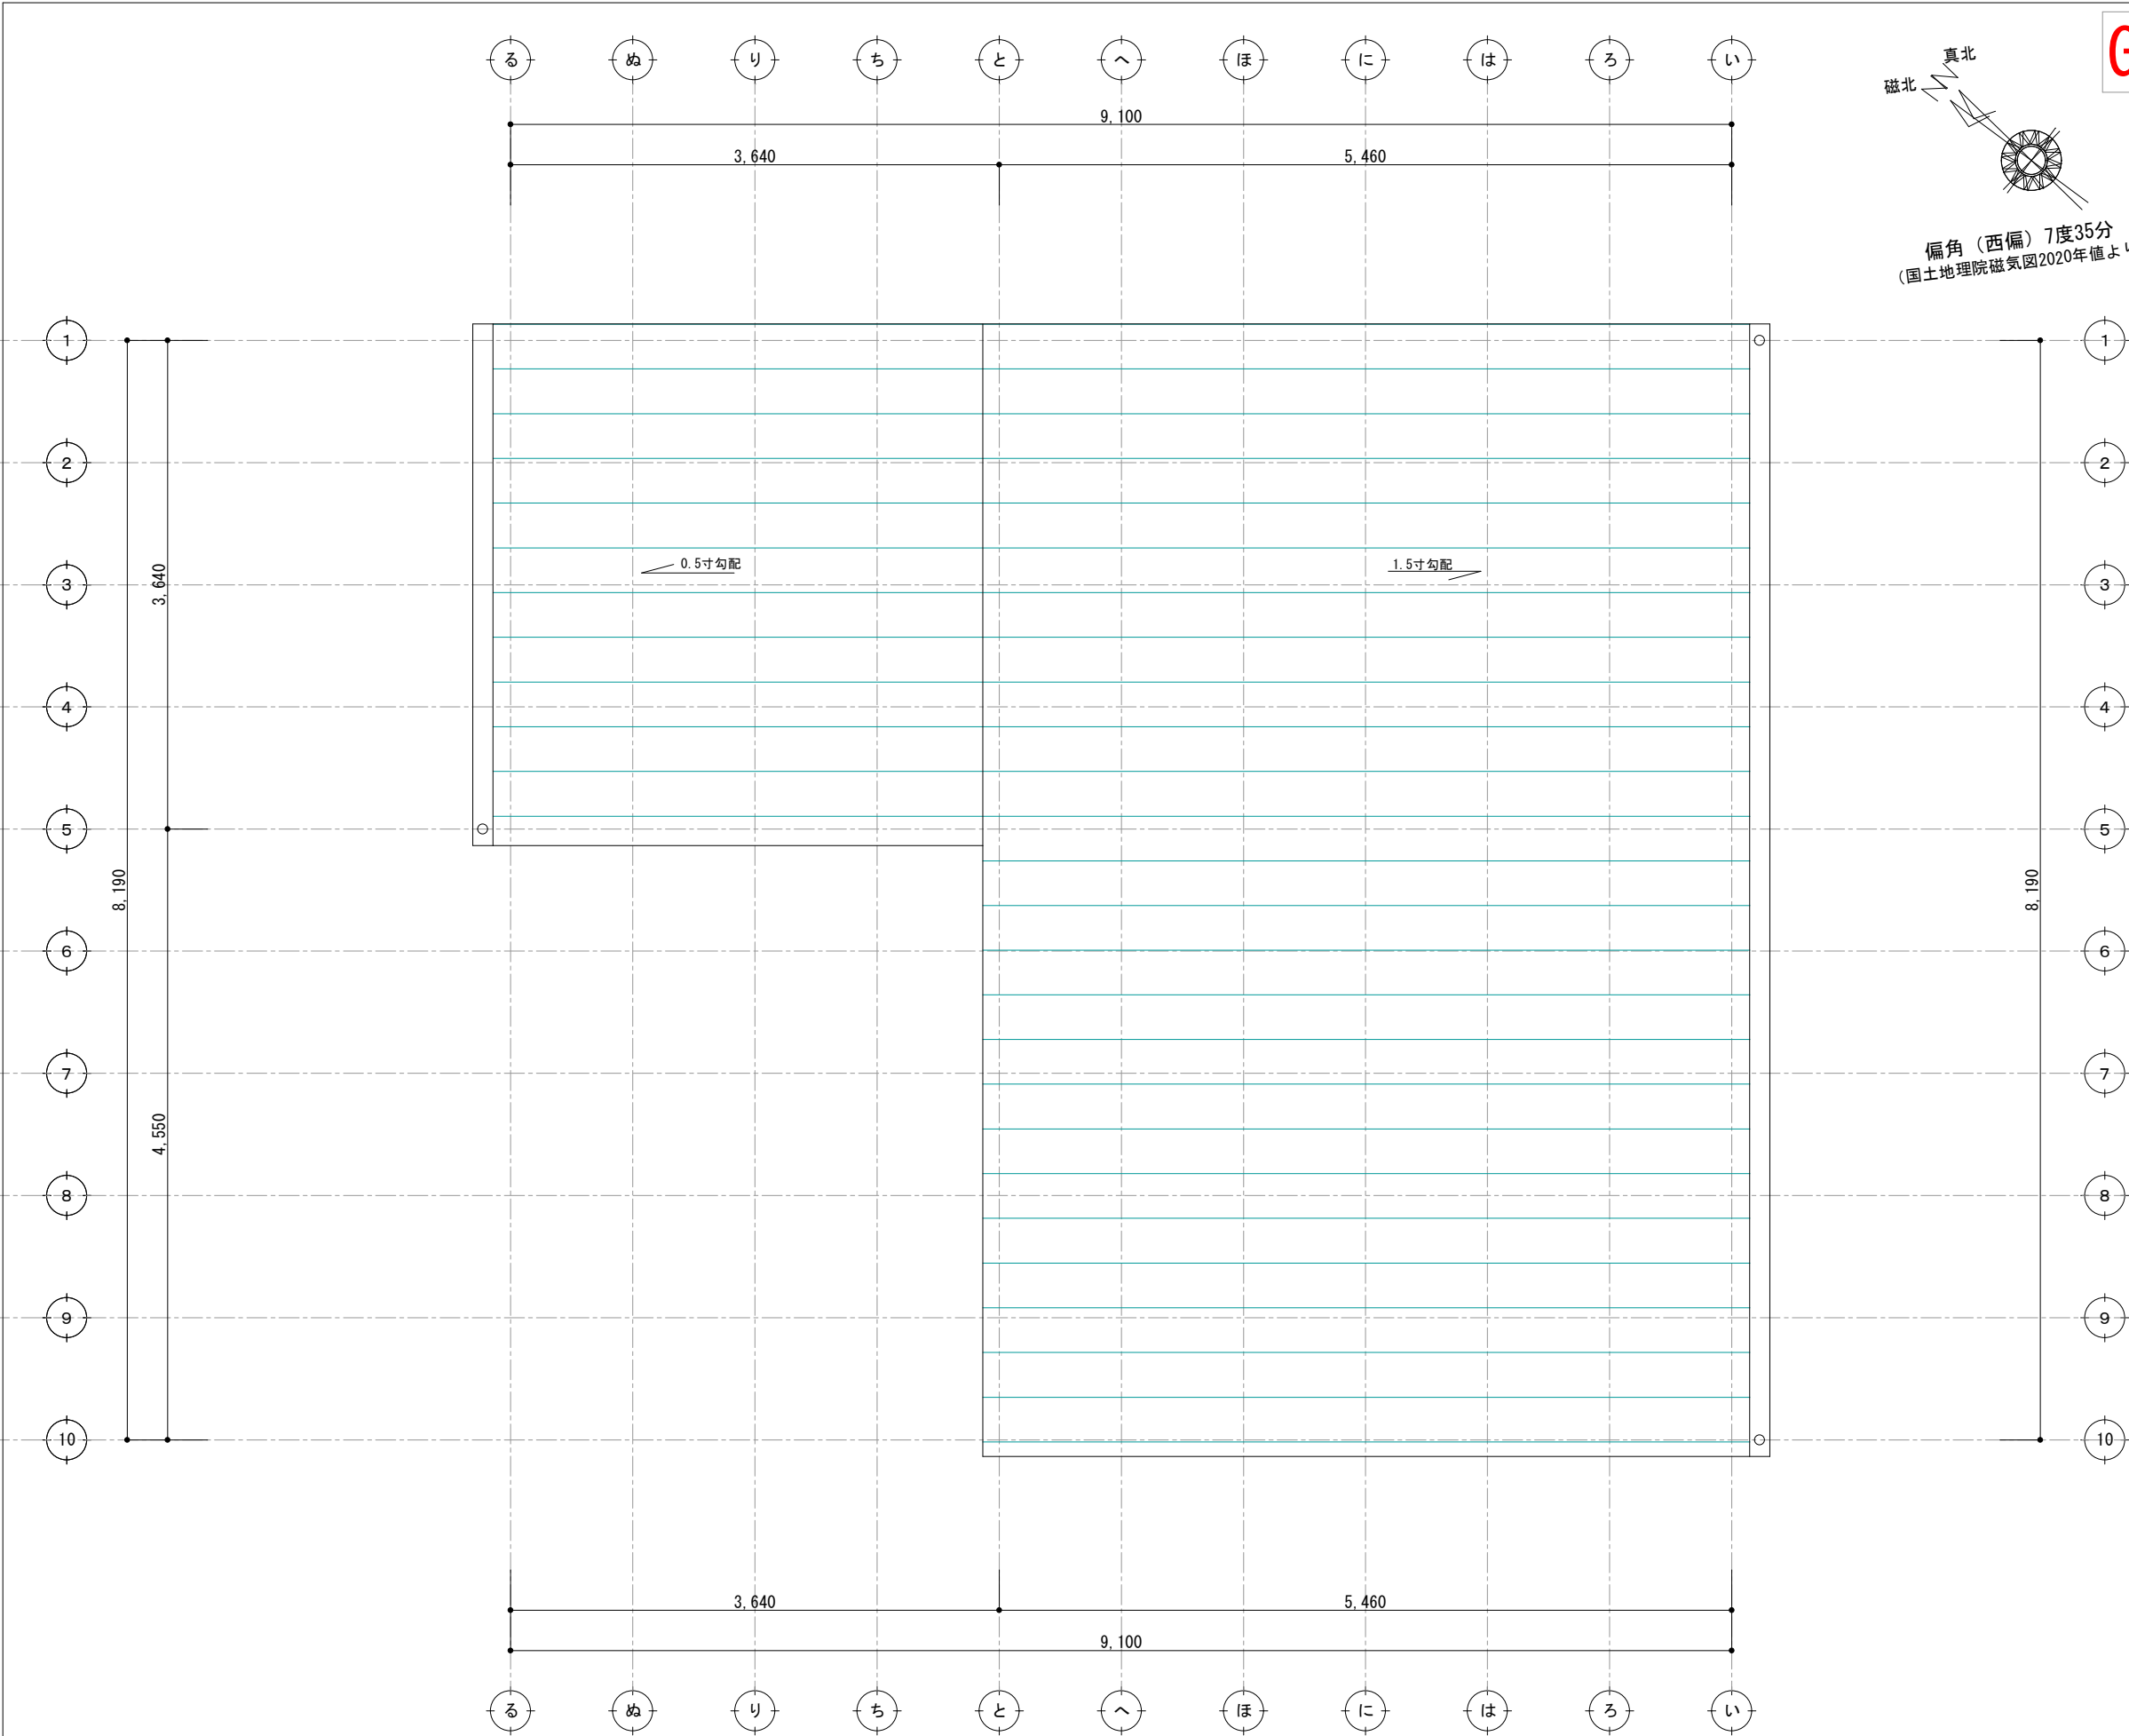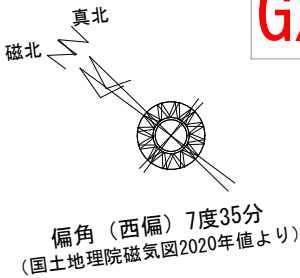

決定図

訂 正	浜 岡 一 級 総 合 設 計 事 務 所 一級建築士事務所 静岡県知事登録第 (10)2441 号 一級建築士 大臣登録第 365879 号 西原利昌		株式会社 LIFEFUND InDesign office 一級建築士事務所 事務所登録 (2) 第7595号 一級建築士登録 第179770号 鈴木 達男 〒432-8023 静岡県浜松市中央区鴨江3丁目70番23号	年 月 日 2025. 9. 14	件 名 小長井祐希様邸 新築工事		設計	IC	工事	図 番
				縮 尺 1/100	図 名 屋根伏図					

G2

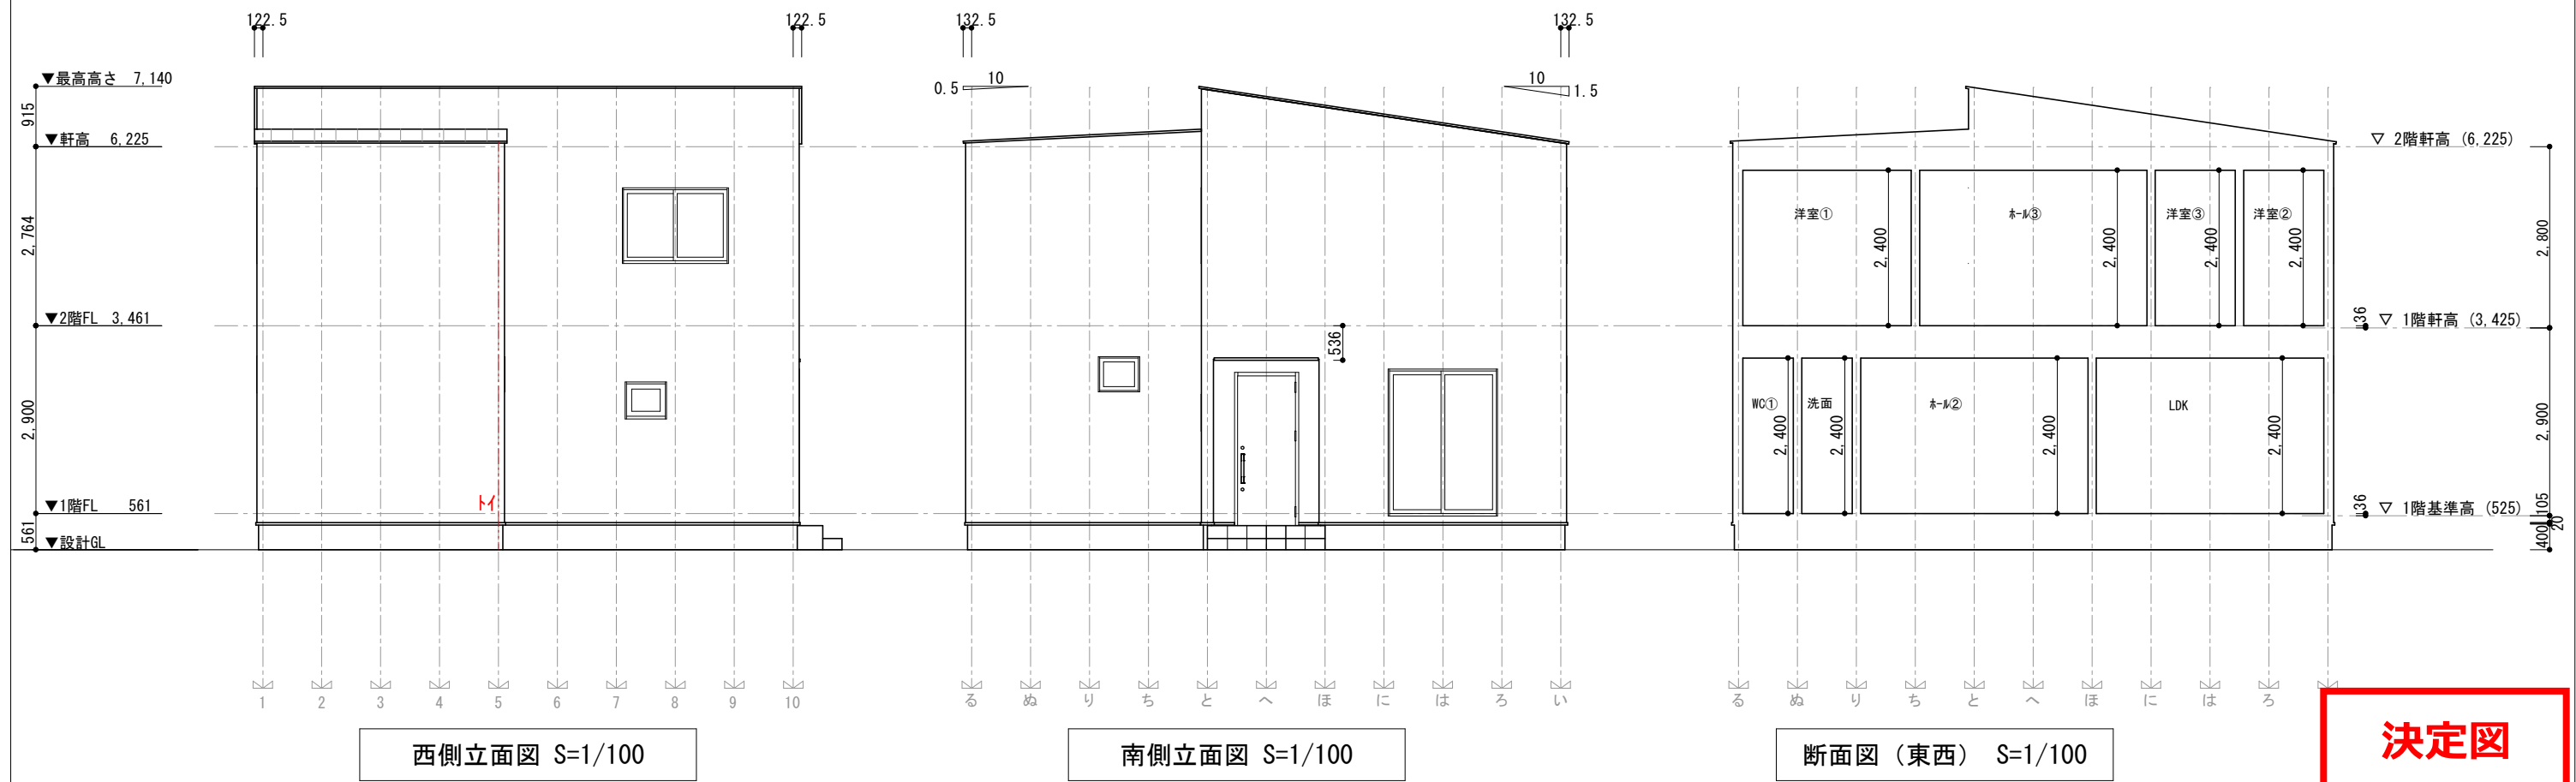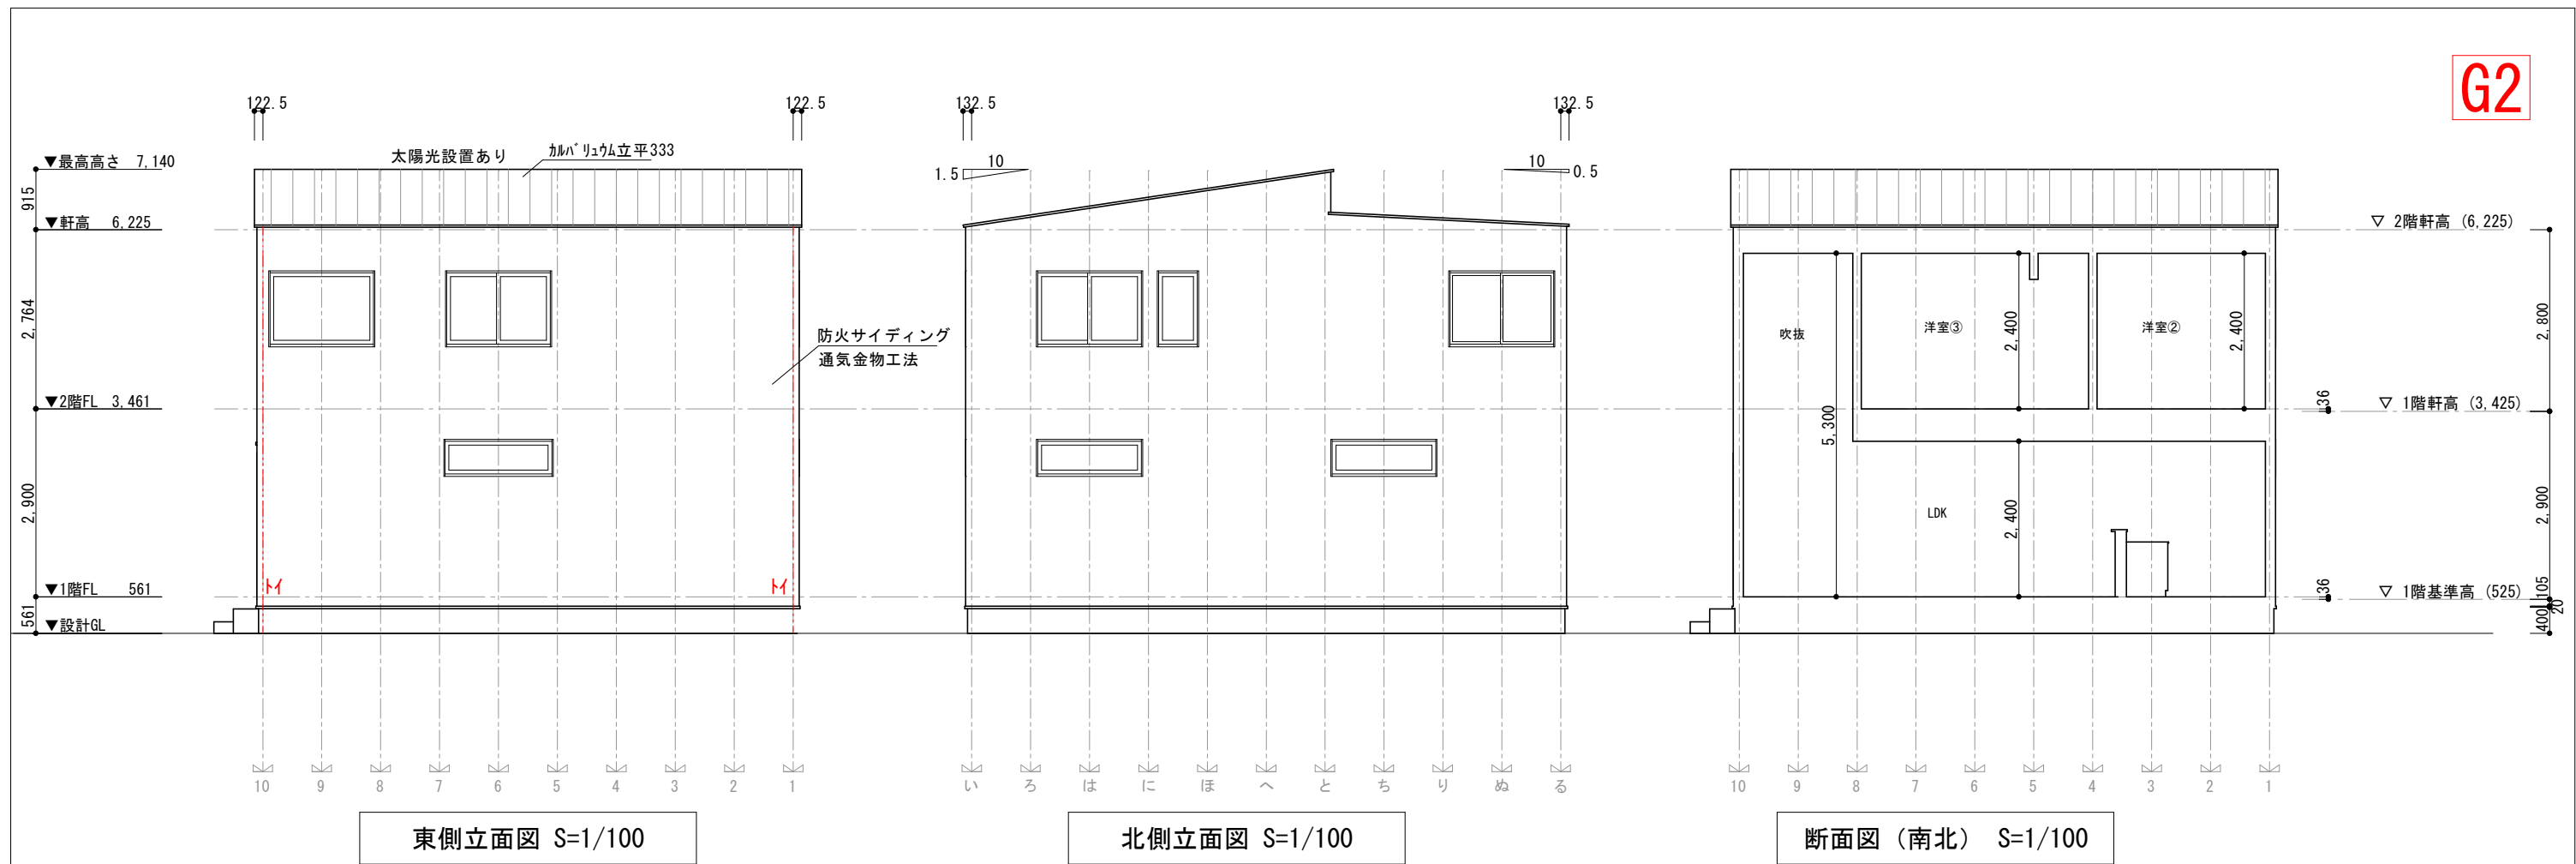











決定図

訂 正	浜 岡 一 級 総 合 設 計 事 務 所 一級建築士事務所 静岡県知事登録第 (10)2441 号 一級建築士 大臣登録第 365879 号 西原利昌		株式会社 LIFEFUND InDesign office 一級建築士事務所 事務所登録 (2)第7595号 一級建築士登録 第179770号 鈴木 達男 〒432-8023 静岡県浜松市中央区鴨江3丁目70番23号	年 月 日	件 名		設計	IC	工事	図 番
				2025. 9. 14	小長井祐希様邸 新築工事		酒井	青島	4	
				縮 尺	図 名					
				1/100	立面図					

G-2




訂 正	浜 岡 一 級 総 合 設 計 事 務 所 一級建築士事務所 静岡県知事登録第 (10)2441 号 一級建築士 大臣登録第 365879 号 西原利昌	 PG HOUSE ビージーハウス	株式会社 LIFEFUND InDesign office 一級建築士事務所 事務所登録 (2)第7595号 一級建築士登録 第179770号 鈴木 達男 〒432-8023 静岡県浜松市中央区鴨江3丁目70番23号	年 月 日 2025. 9. 14 縮 尺 1/30	件 名 小長井祐希様 邸新築工事 図 名 矩計図	設計 酒井	IC 青島	工事 青島	図 番 5
-----	--	--	--	-------------------------------------	-----------------------------------	----------	----------	----------	----------

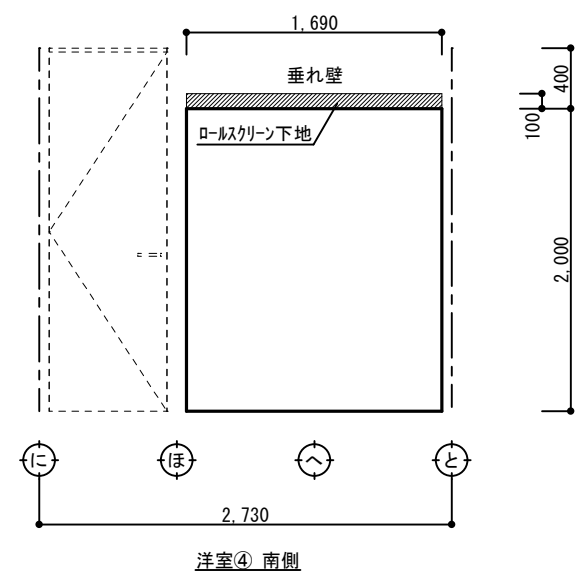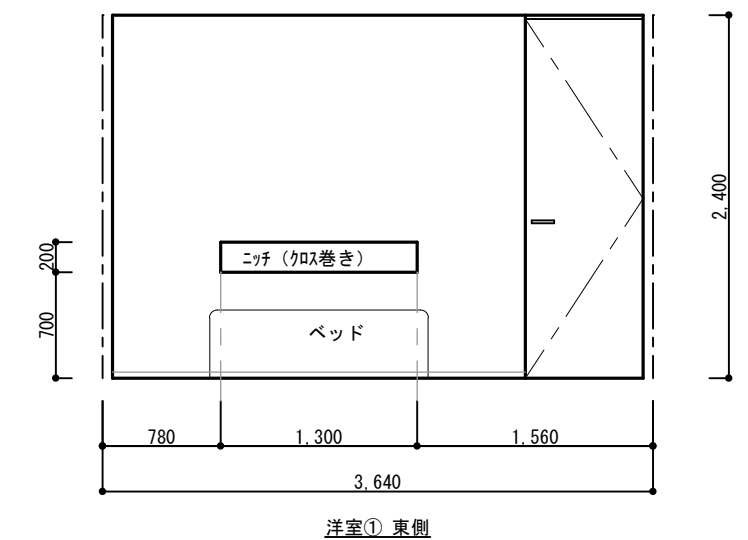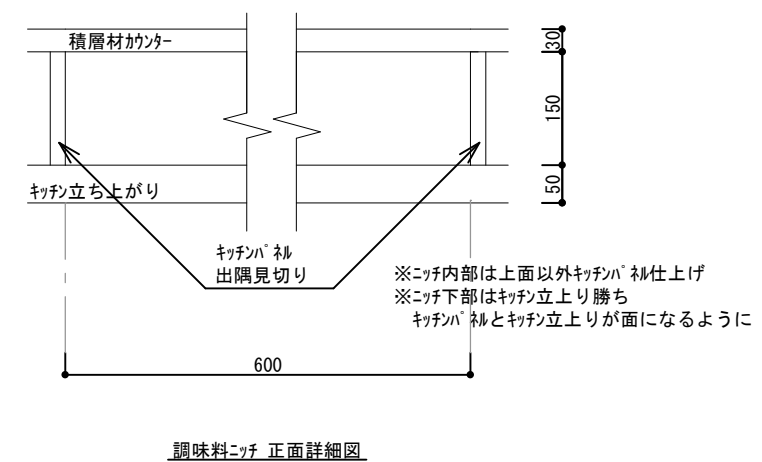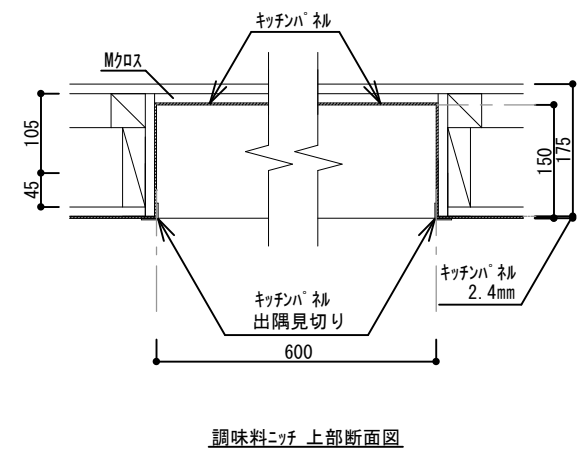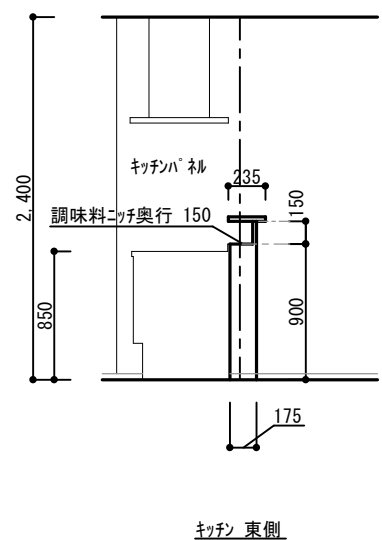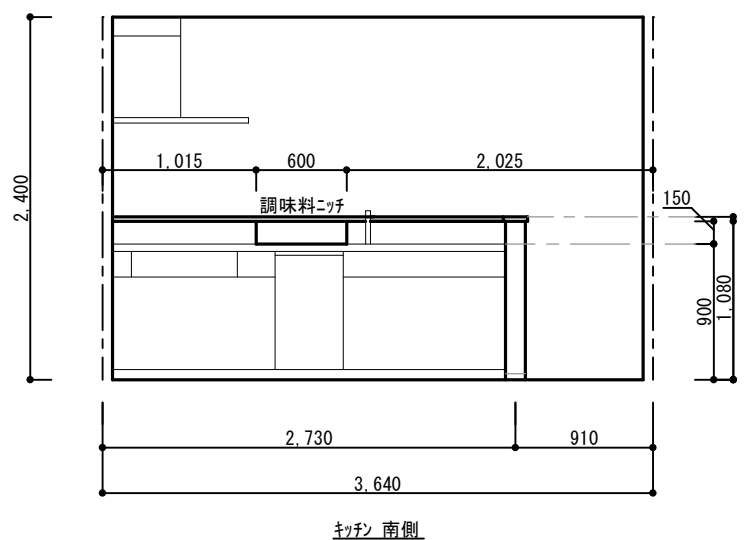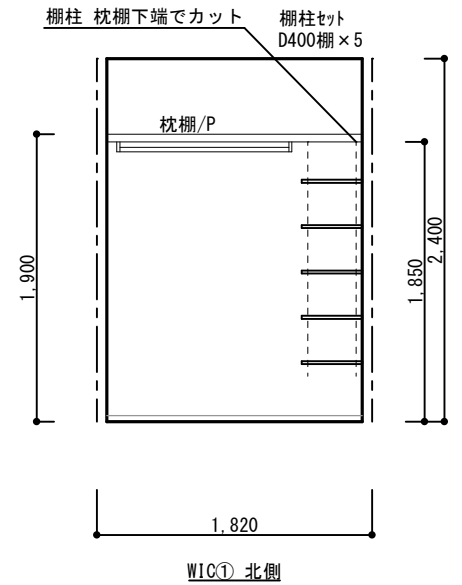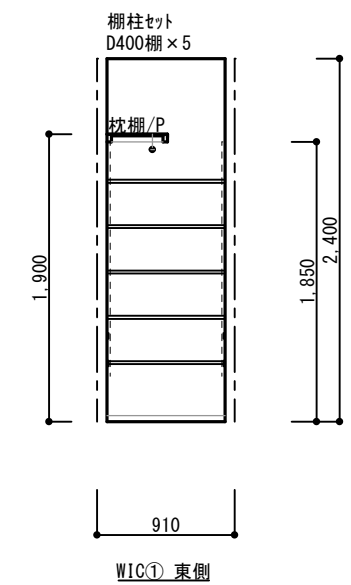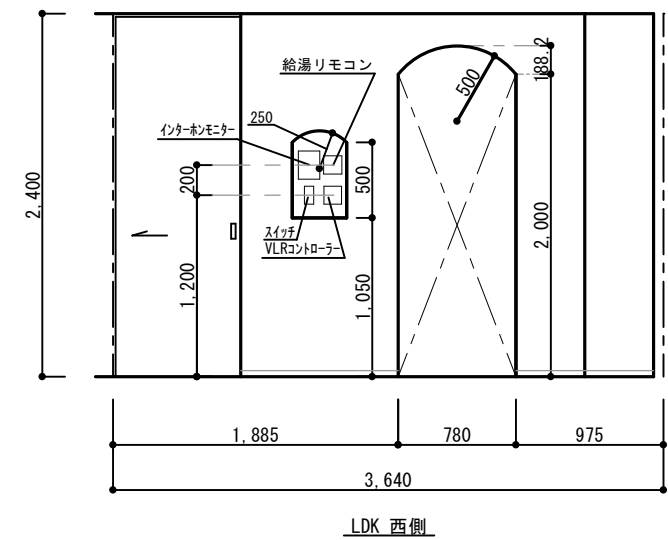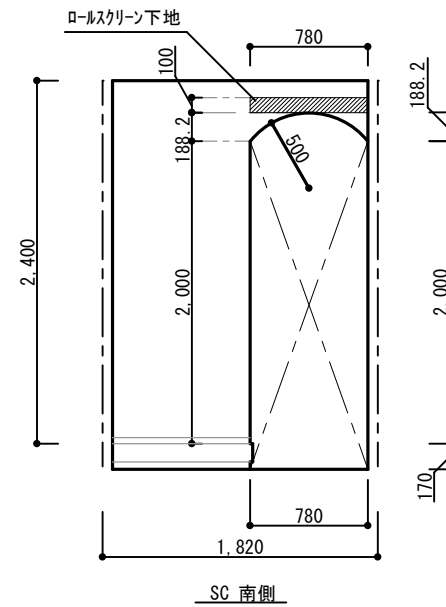

決定図

訂正	浜岡一級総合設計事務所 一級建築士事務所 静岡県知事登録第 (10)2441 号 一級建築士 大臣登録第 365879 号 西原利昌	LIFEFUND PG HOUSE	株式会社 LIFEFUND InDesign office 一級建築士事務所 事務所登録 (2) 第7595号 一級建築士登録 第179770号 鈴木 達男 〒432-8023 静岡県浜松市中央区鶴江3丁目70番23号	年月日 2025. 9. 14	件名 小長井祐希様 新築工事		設計 酒井	IC	工事 青島	図番 6-1
				縮尺 1/50	図名 展開図-1					

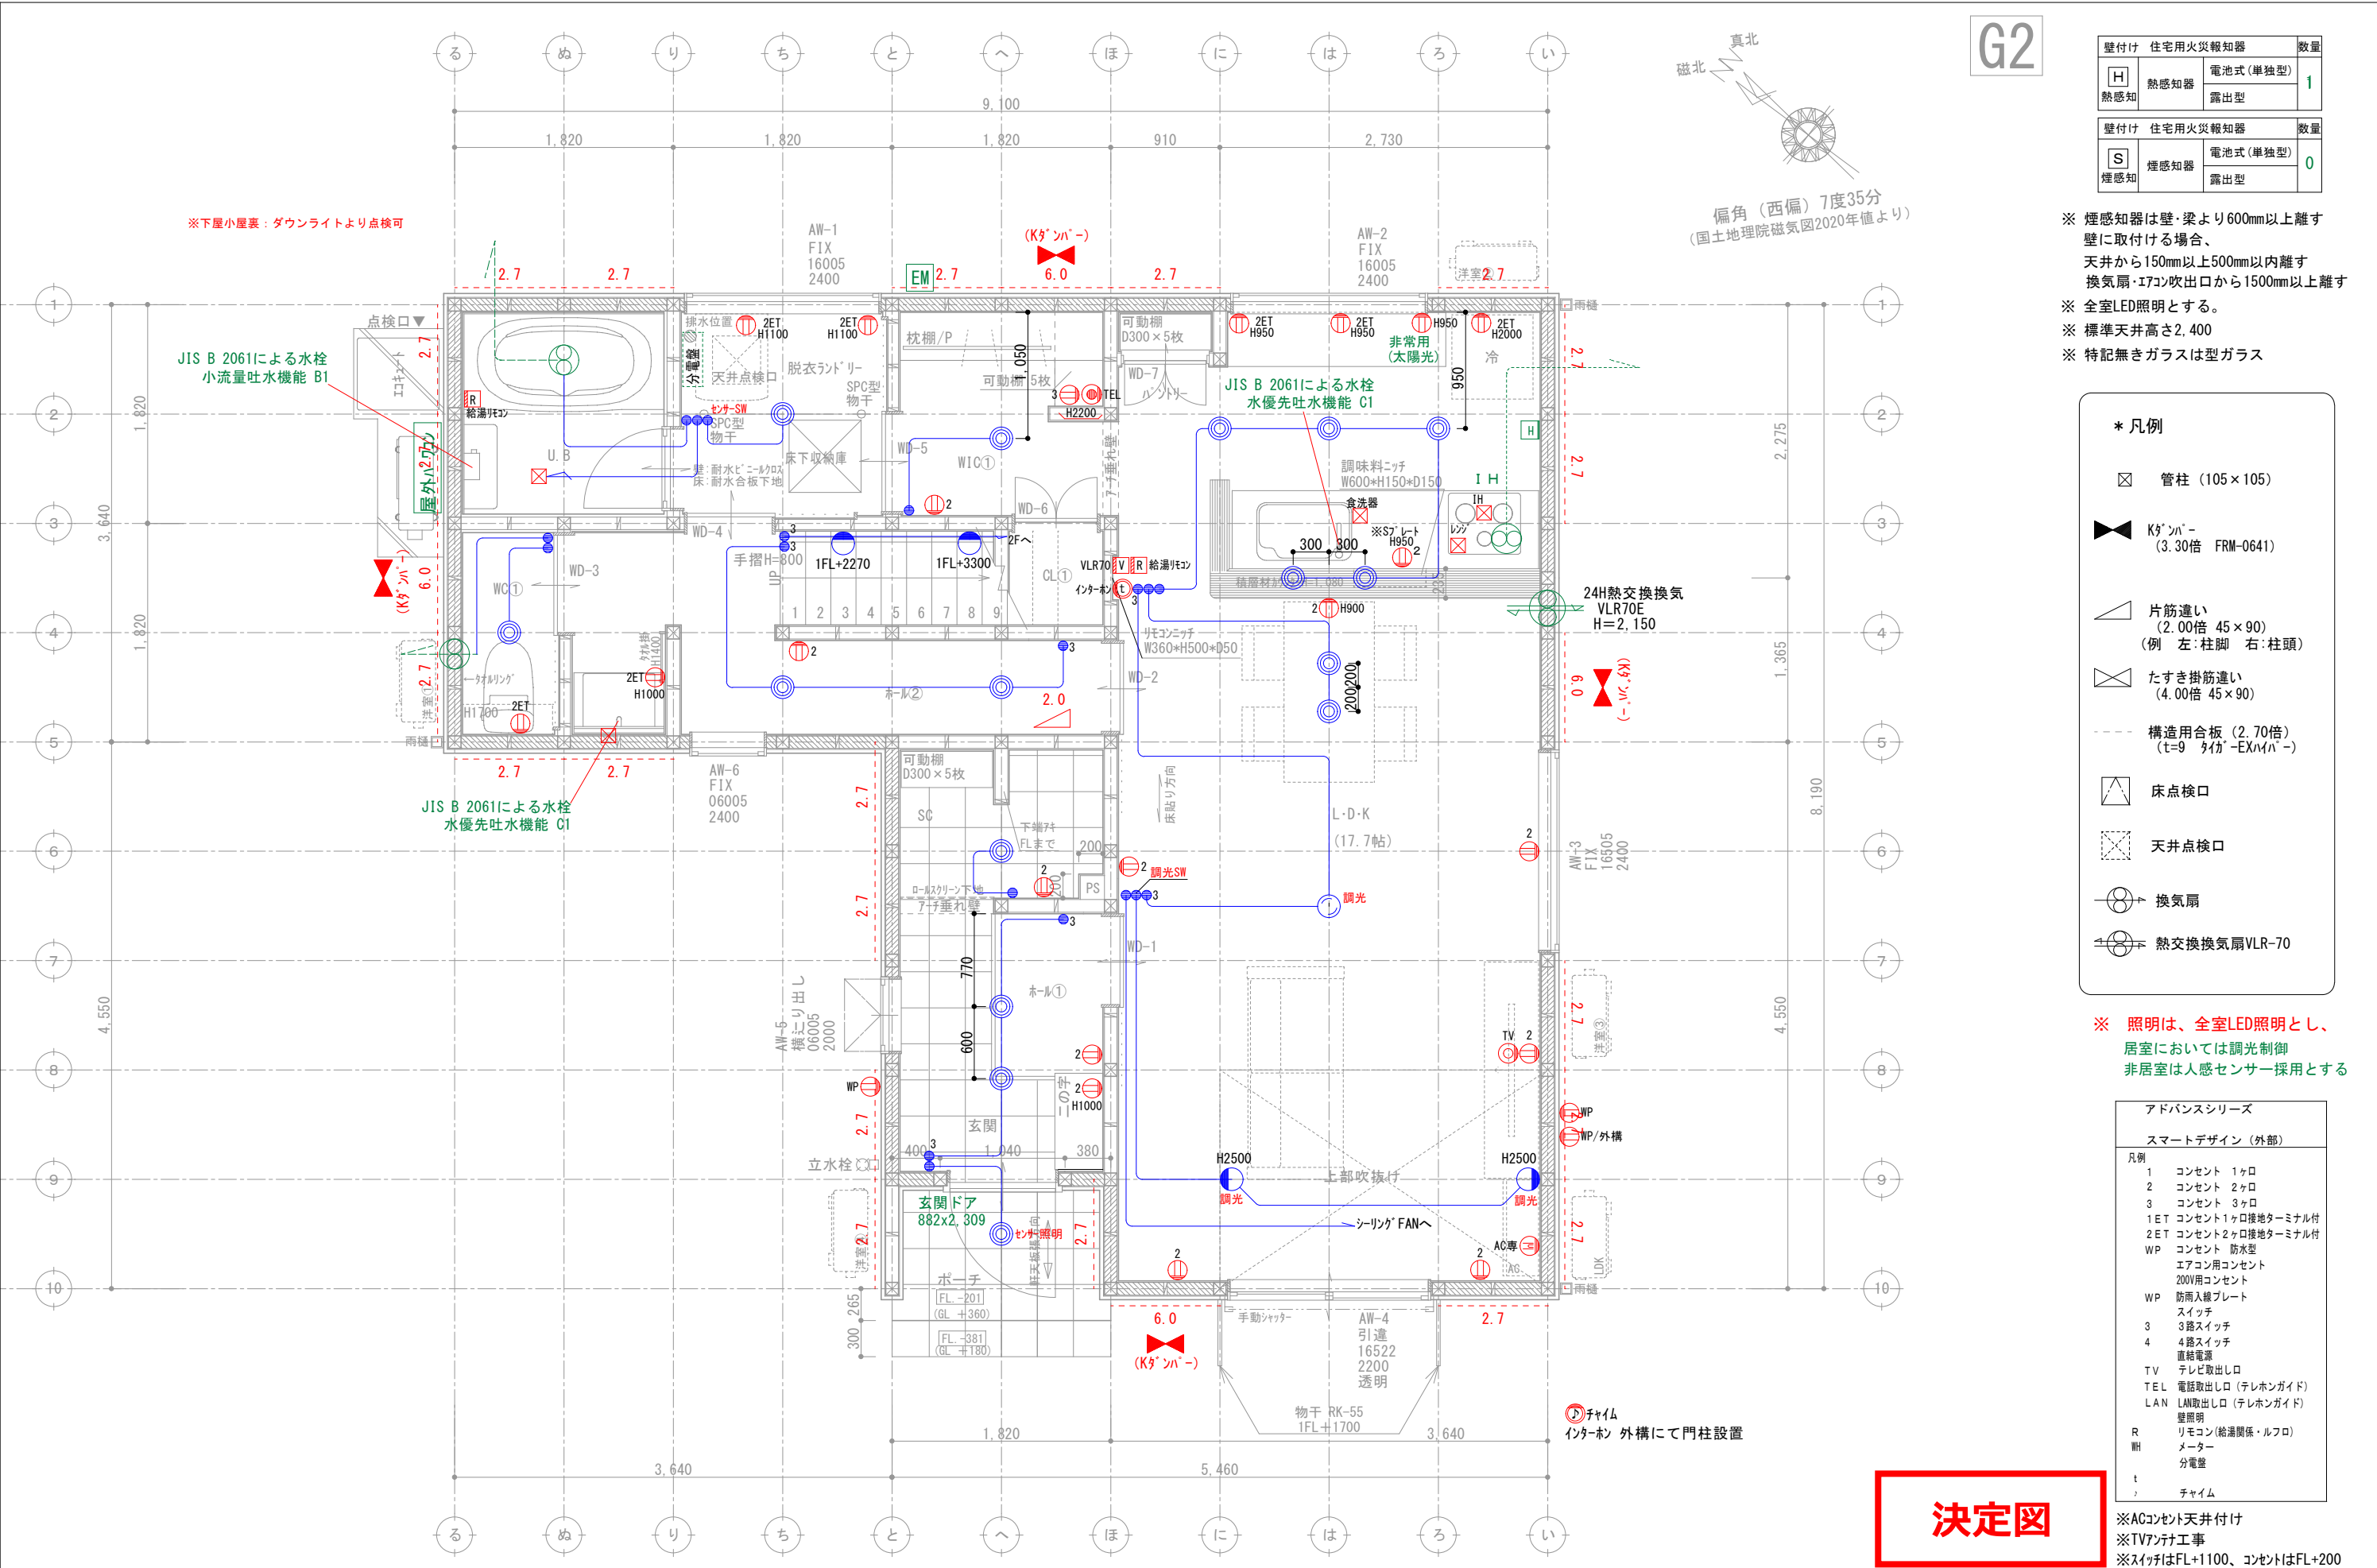

壁付け 住宅用火災報知器			数量
H 熱感知	電池式(単独型)		1
	露出型		
壁付け 住宅用火災報知器			数量
S 煙感知	電池式(単独型)		0
	露出型		

※ 煙感知器は壁・梁より600mm以上離す
壁に取付ける場合、
天井から150mm以上500mm以内離す
換気扇・エアコン吹出口から1500mm以上離す

※ 全室LED照明とする。

※ 標準天井高さ2,400

※ 特記無きガラスは型ガラス


* 凡例	
☒	管柱 (105×105)
◀▶	Kダクト (3.30倍 FRM-0641)
△	片筋違い (2.00倍 45×90) (例 左:柱脚 右:柱頭)
⊗	たすき掛筋違い (4.00倍 45×90)
---	構造用合板 (2.70倍) (t=9 9材 EXハイバ)
△	床点検口
⊗	天井点検口
⊗	換気扇
⊗	熱交換換気扇VLR-70

※ 照明は、全室LED照明とし、
居室においては調光制御
非居室は人感センサー採用とする


アドバンスシリーズ			
スマートデザイン (外部)			
凡例			
1	コンセント	1ヶ所	
2	コンセント	2ヶ所	
3	コンセント	3ヶ所	
1ET	コンセント1ヶ所接地ターミナル付		
2ET	コンセント2ヶ所接地ターミナル付		
WP	コンセント 防水型		
	エアコン用コンセント		
	200V用コンセント		
WP	防雨入線プレート		
	スイッチ		
3	3路スイッチ		
4	4路スイッチ		
	直結電源		
TV	テレビ取出口		
TEL	電話取出口 (テレホンガイド)		
LAN	LAN取出口 (テレホンガイド)		
R	壁照明		
WH	リモコン(給湯関係・ルフロ)		
	メーター		
t	分電盤		
	チャイム		

※ACコンセント天井付け
※TVアンテナ工事
※スイッチはFL+1100、コンセントはFL+200

訂正	浜岡一級総合設計事務所 一級建築士事務所 静岡県知事登録第 (10)2441 号 一級建築士 大臣登録第 365879 号 西原利昌	PG HOUSE ピージーハウス	株式会社 LIFEFUND InDesign office 一級建築士事務所 事務所登録 (2)第7595号 一級建築士登録 第179770号 鈴木 達男 〒432-8023 静岡県浜松市中央区鴨江3丁目70番23号	年月日 2025.9.14 縮尺 1/50	件名 小長井祐希様邸 新築工事 図名 1階電気配線図	設計 酒井	IC	工事 青島	図番 7-1
----	--	---------------------	--	--------------------------------	-------------------------------------	----------	----	----------	-----------

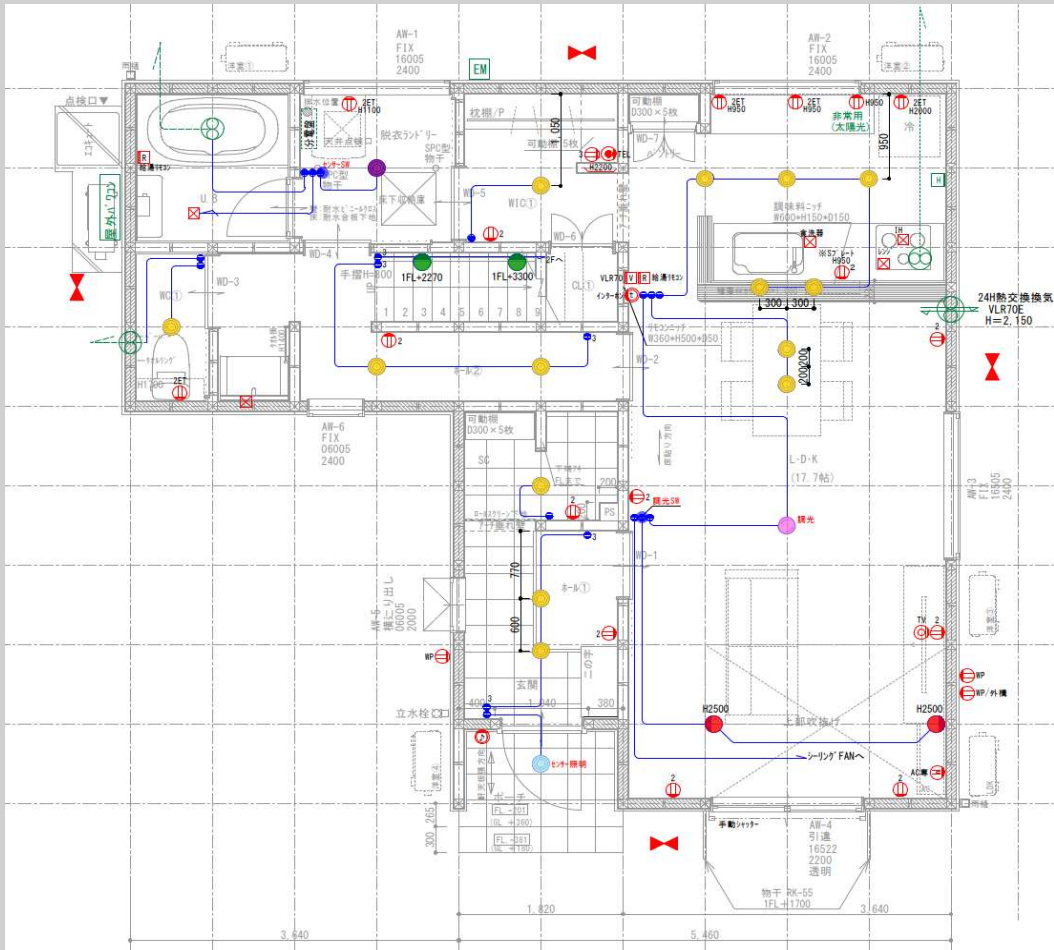

1階

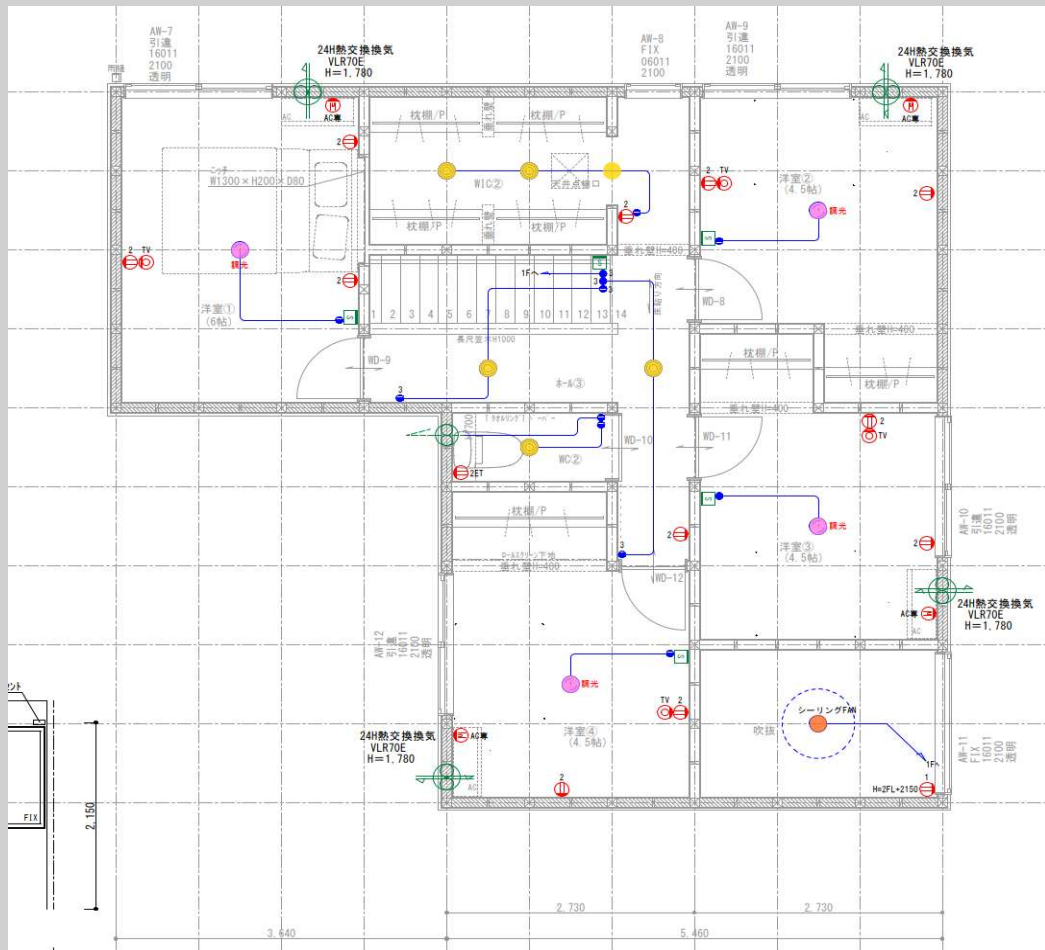

2階

ドアホン：VL-SE31XL

(Panasonic)




内部SW：アドバンス

マットホワイト



外部：スマートデザインシリーズ

初付

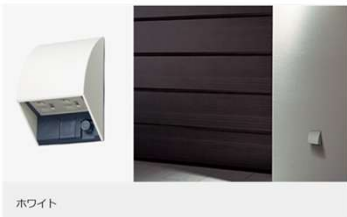

ポーチ灯

×1

センサー付きダウンドライ

DDL_4496YW

基本照明ダウンドライ

×20

DDL_6102YW

脱衣ランドリー

×1

ダウンドライ

DDL_6102AW

LDK、洋室①②③④

×5

シーリングライト

DCL_40507

吹抜

×2

スポットライト

DSL_5529FWG

階段

×2

階段灯

DBK_41544Y

吹抜

×1

センサー-SW

DP_40332

脱衣ランドリー

×1

センサー-SW

DP_40334

LDK

×1

調光SW

WTA_57583WK



決定図

PG House


小長井祐希様

邸新築工事

Lighting Plan

2025.9.14

(図面 7-3)

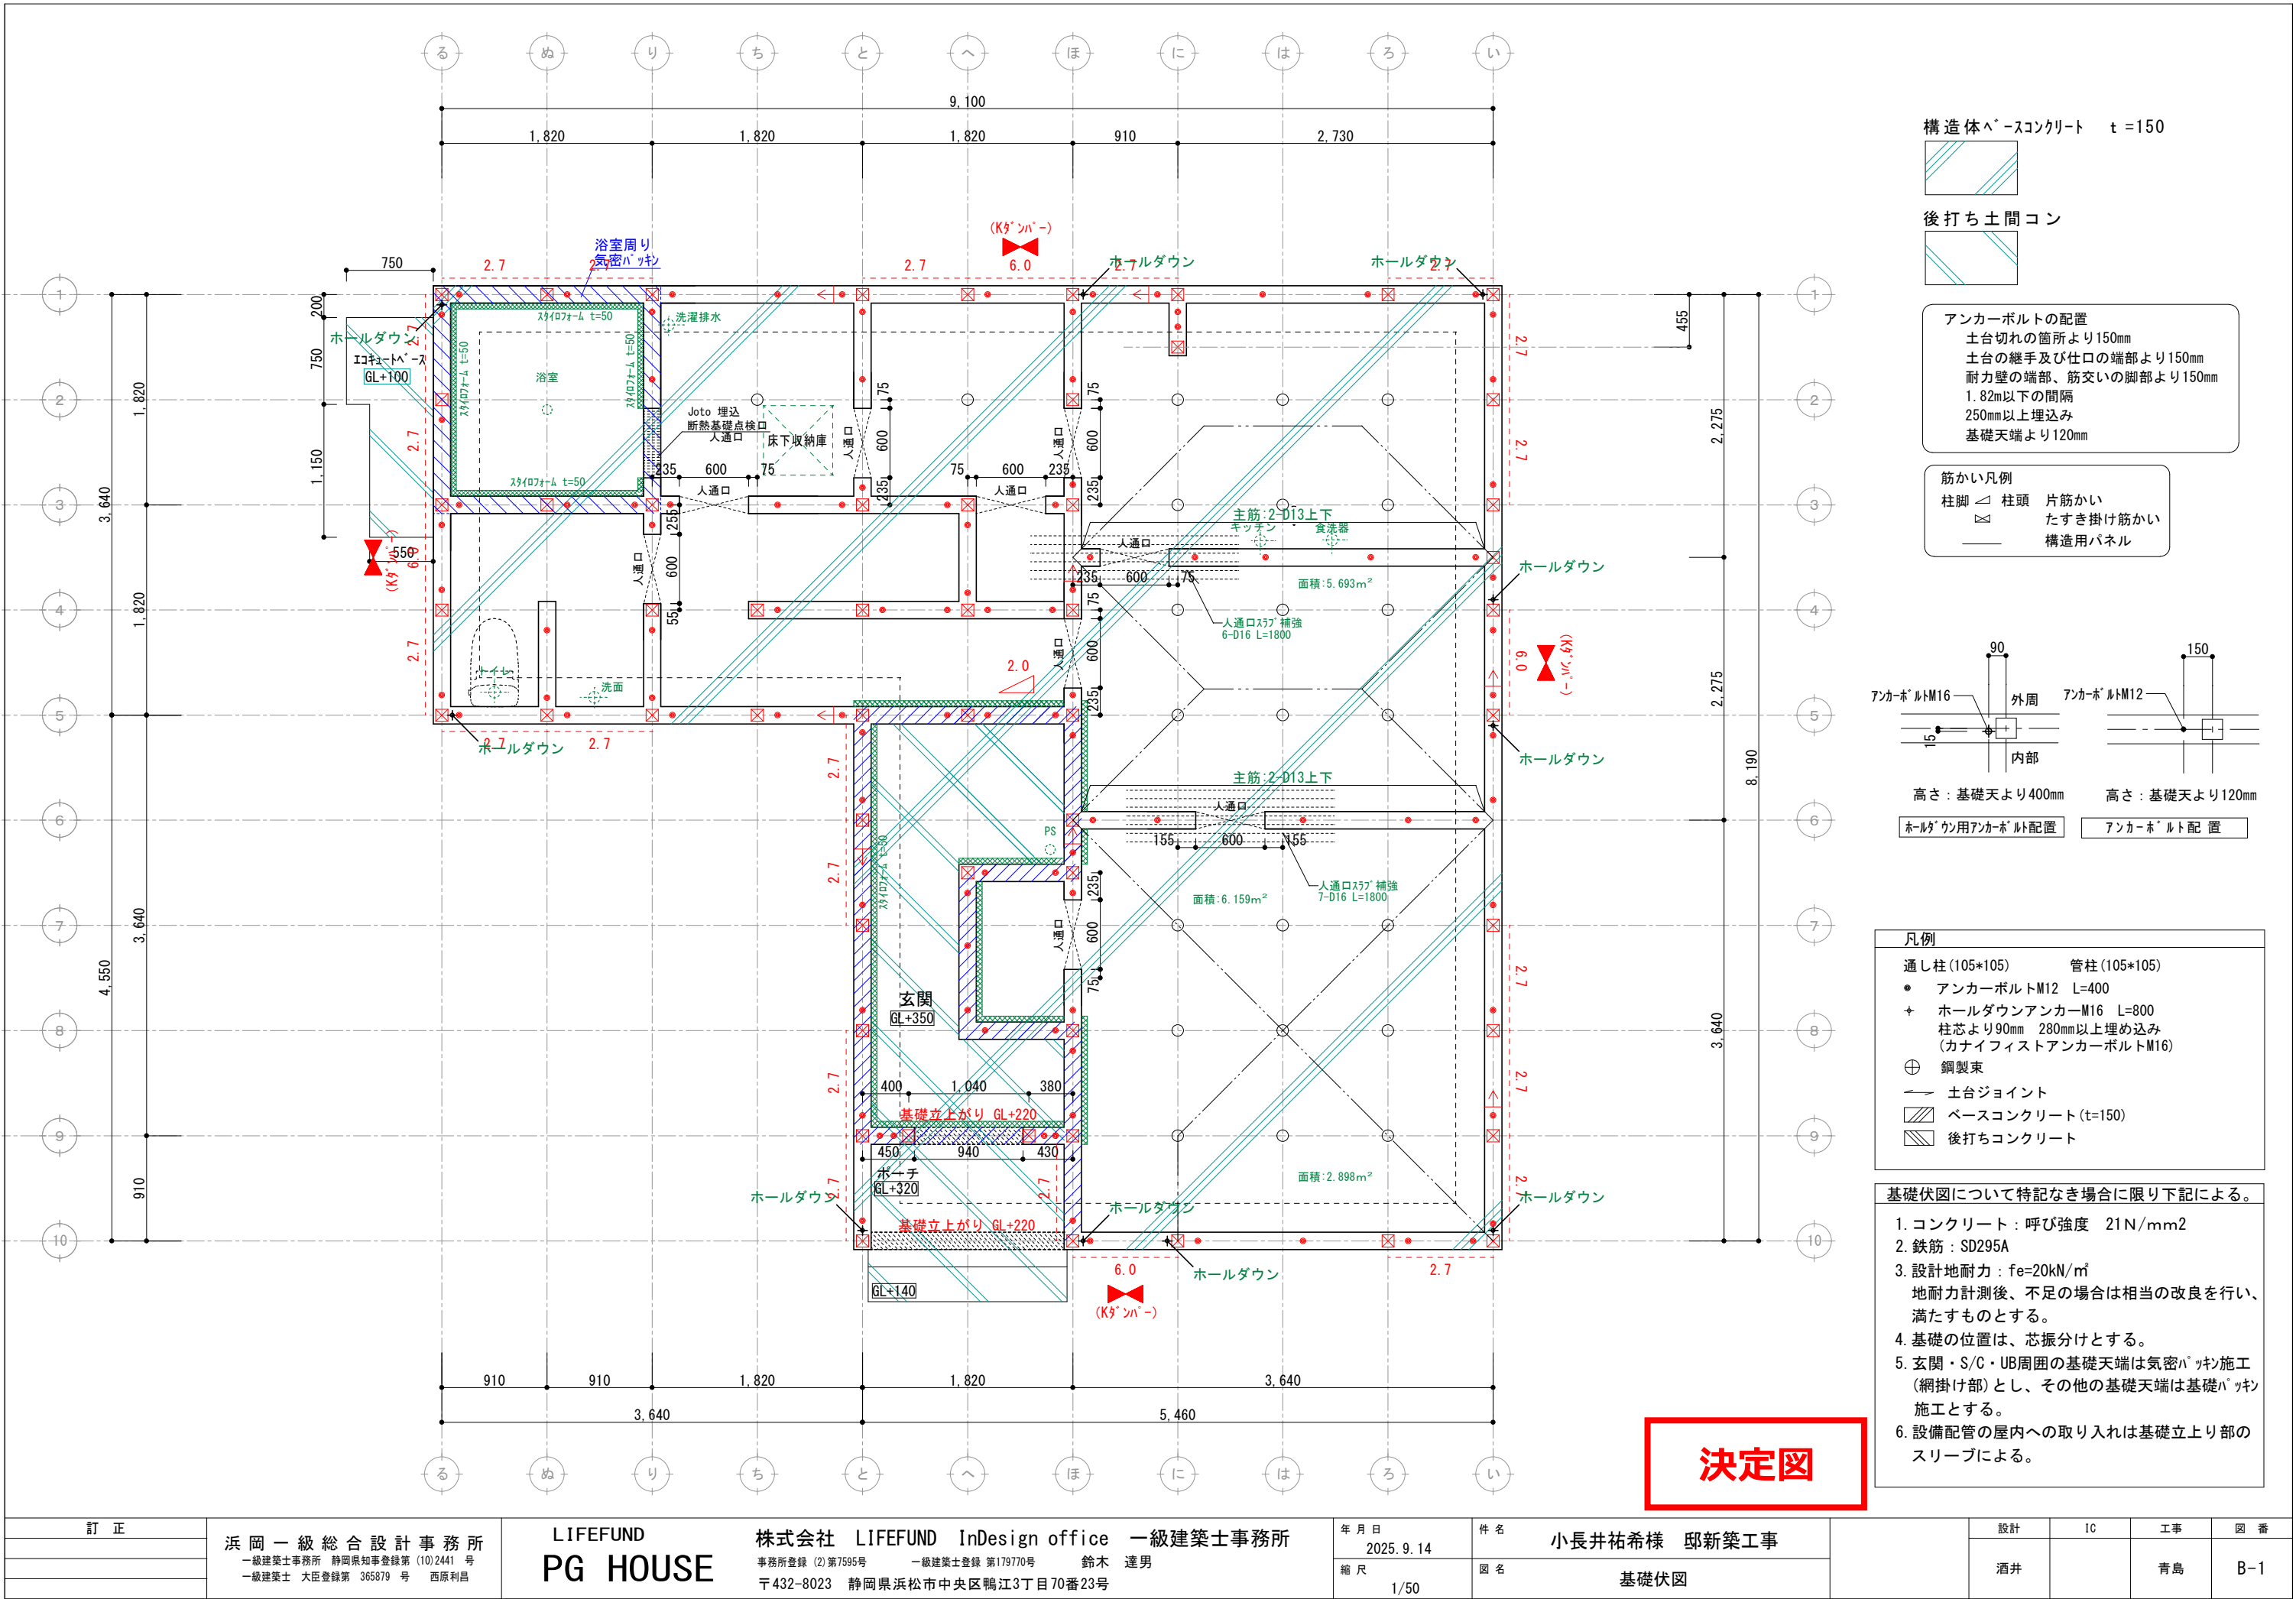


構造体ベースコンクリート t=150

後打ち土間コン









アンカーボルトの配置
土台切れの箇所より150mm
土台の継手及び仕口の端部より150mm
耐力壁の端部、筋交いの脚部より150mm
1.82m以下の間隔
250mm以上埋込み
基礎天端より120mm

筋かい凡例
柱脚 柱頭 筋かい
たすき掛け筋かい
構造用パネル

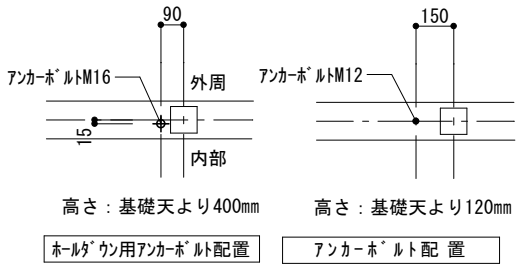

凡例	
通し柱 (105*105)	管柱 (105*105)
● アンカーボルト M12 L=400	
✦ ホールダウンアンカー M16 L=800	
柱芯より90mm 280mm以上埋め込み (カナダファイストアンカーボルト M16)	
⊕ 鋼製束	
→ 土台ジョイント	
▨ ベースコンクリート (t=150)	
▨ 後打ちコンクリート	

- 基礎伏図について特記なき場合に限り下記による。
1. コンクリート：呼び強度 21N/mm²
 2. 鉄筋：SD295A
 3. 設計地耐力：f_e=20kN/m²
地耐力計測後、不足の場合は相当の改良を行い、満たすものとする。
 4. 基礎の位置は、芯振分けとする。
 5. 玄関・S/C・UB周囲の基礎天端は気密パッキン施工（網掛け部）とし、その他の基礎天端は基礎パッキン施工とする。
 6. 設備配管の屋内への取り入れは基礎立上り部のスリーブによる。

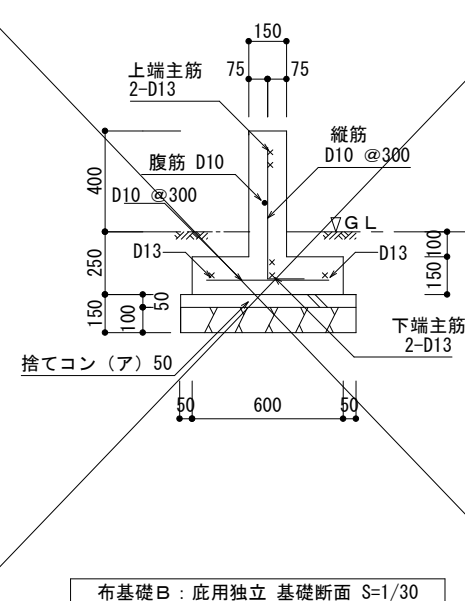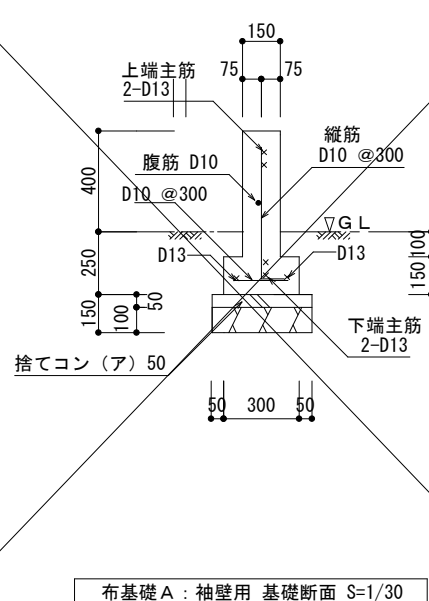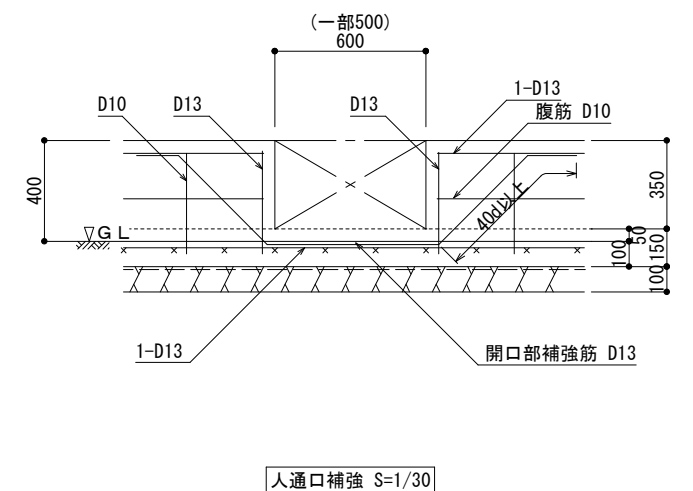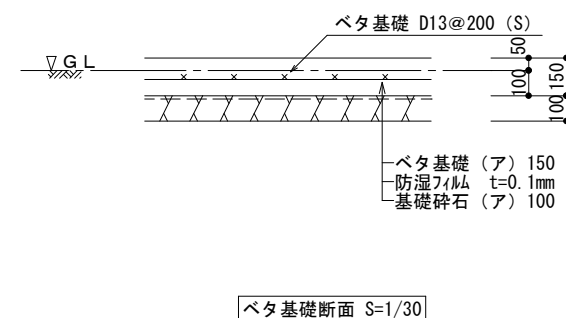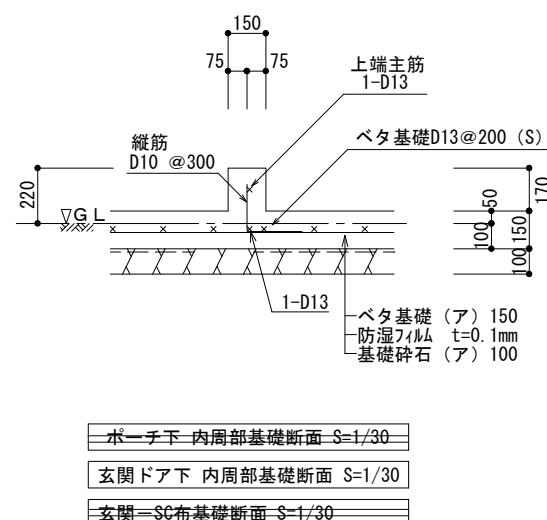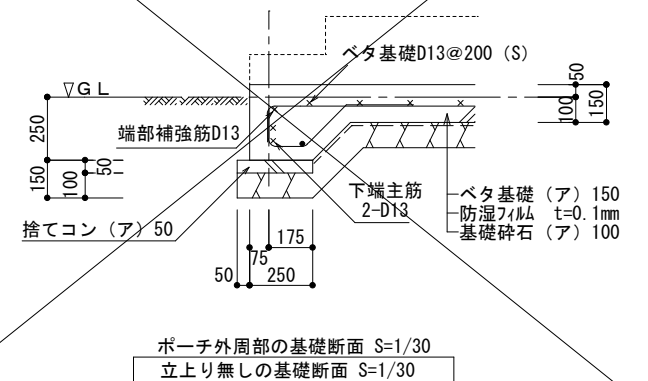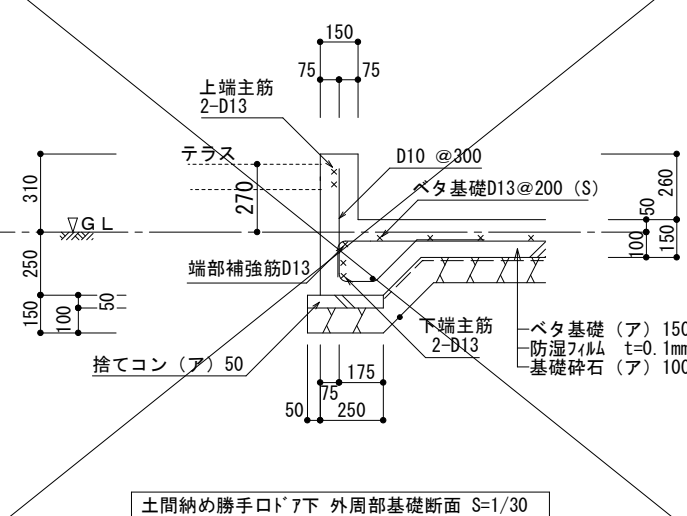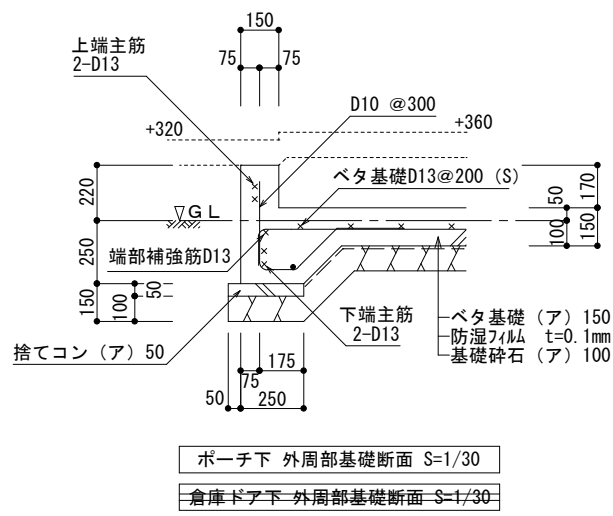

基礎の寸法 及び 配筋の検証方法	基礎立上り配筋は、 (財)日本住宅・木材技術 センター発行のスパン表 (増補版)による。 ベタ基礎スラブ配筋は、 まもりすまい保険設計施工 基準同解説のベタ基礎配筋表 による。具体的な寸法・配 筋は基礎詳細図参照。
---------------------------------	--


鉄筋断面表記

・ D10を示す。


× ・ ・ D13を示す。

※使用しない断面は

決定図

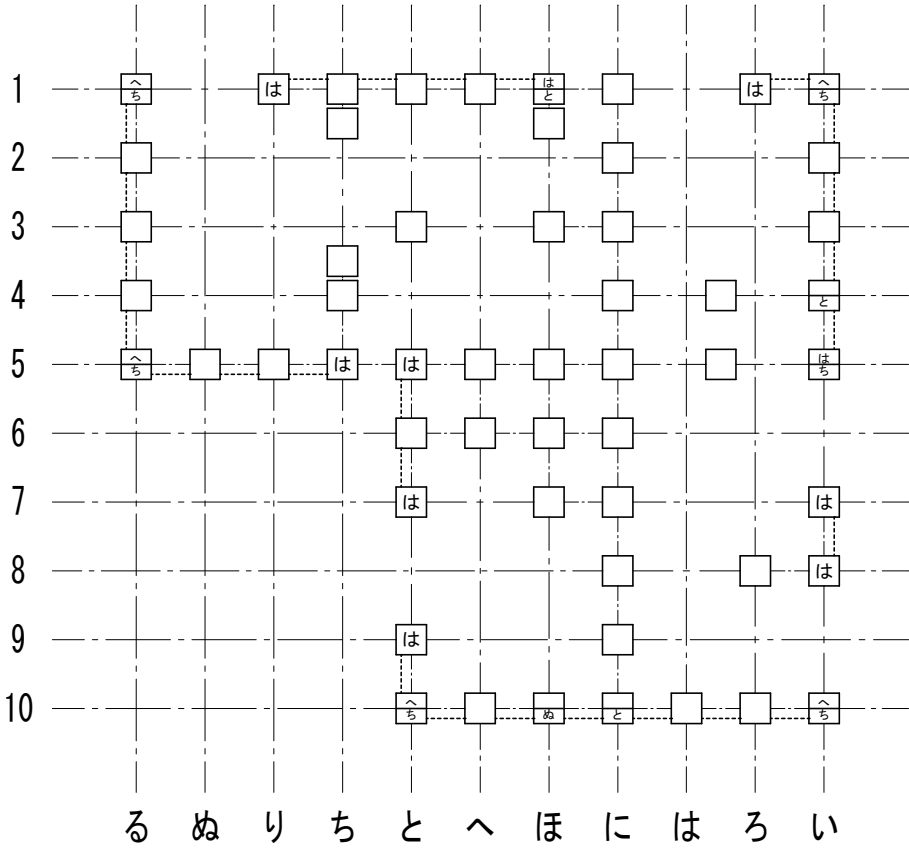

2階柱壁伏図

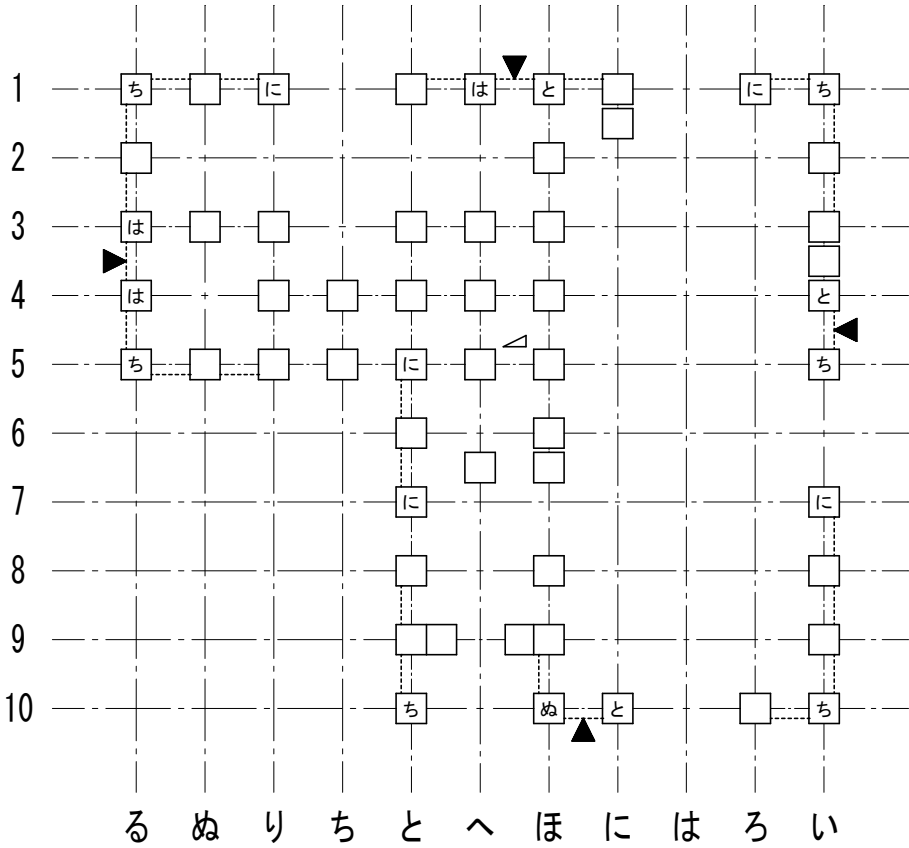

1階柱壁伏図

接合部凡例				*接合部凡例はユーザ設定されたものです。	
記号	仕様（カナイ金物）		N	倍率	
SBCP	スリムビルドコーナー75, チビクリCK(化粧柱の場合)		0.00	1.00	
SBCP	スリムビルドコーナー75, チビクリCK(化粧柱の場合)		0.65	1.00	
SBCP	は	スリムビルドコーナー75	1.00	1.00	
ARCG	に	アレントコーナー合板用	1.40	2.20	
ARCG	ほ	アレントコーナー合板用	1.60	2.20	
ARCG	へ	アレントコーナー合板用	1.80	2.20	
HD15	と	ブレイブホールダウン B-HD15	2.80	3.60	
HD20	ち	ブレイブホールダウン B-HD20	3.70	4.70	
HD25	り	ブレイブホールダウン B-HD25	4.70	4.80	
HD30	ぬ	ブレイブホールダウン B-HD30	5.60	7.20	
J1	る	腰掛け蟻若しくは大入れ蟻掛け+羽子板ボルト、短冊金物		1.90	
J2	を	腰掛け蟻若しくは大入れ蟻掛け+羽子板ボルト、短冊金物×2		3.00	

※表示なき金物は「は」とする。

梁継手・仕口用

梁継手・仕口用

接合部凡例				*接合部凡例はユーザ設定されたものです。	
記号	仕様（タナカ金物）		N	倍率	
FCP	フックコーナー, チビクリCK(化粧柱の場合)		0.00	1.00	
FCP	フックコーナー, チビクリCK(化粧柱の場合)		0.65	1.00	
FCP	は	フックコーナー	1.00	1.00	
CCP	に	シナコーナー	1.40	2.20	
CCP	ほ	シナコーナー	1.60	2.20	
CCP	へ	シナコーナー	1.80	2.20	
HD15	と	ビス止めホールダウンU HD15	2.80	3.60	
HD20	ち	ビス止めホールダウンU HD20	3.70	4.70	
HD25	り	ビス止めホールダウンU HD25	4.70	4.80	
HD30	ぬ	ビス止めホールダウンU HD15×2 (HD35)	5.60	7.20	
J1	る	腰掛け蟻若しくは大入れ蟻掛け+羽子板ボルト、短冊金物		1.90	
J2	を	腰掛け蟻若しくは大入れ蟻掛け+羽子板ボルト、短冊金物×2		3.00	

※表示なき金物は「は」とする。

梁継手・仕口用


梁継手・仕口用

筋かいの種類に応じた筋かいの端部の接合部の仕様		
	筋かいの種類	接合部の仕様（構造方法）
イ	鉄筋φ9	柱又は横架材を貫通し、三角座金を介してナット締め、又は鋼板添え板を用い鋼板を柱及び横架材にCN90, 8本平打ち
ロ	筋かい:15×90	柱・横架材を欠き込み、柱・横架材双方に対してN65, 5本平打ち
ハ	筋かい:30×90	鋼板添え板t=1.6mmを筋かいに対してボルトφ12及びCN65, 3本平打ち、柱に対してCN65, 3本平打ち、横架材に対してCN65, 4本平打ち。筋かいプレートBP同等品
ニ	筋かい:45×90	鋼板添え板t=2.3mmを筋かいに対してボルトφ12及びスクリュー釘φ4.5L50, 7本平打ち、柱及び横架材に対してスクリュー釘φ4.5L50, 5本平打ち。筋かいプレートBP-2同等品
ホ	筋かい:90×90	柱又は横架材にボルトφ12mmを用いて一面剪断接合

胴差と通し柱の接合部の仕様		
	胴差と通し柱の条件	仕口
T1	通し柱の片側に胴差が来る場合	胴差を柱にかたぎ大入れ短ほぞ差しの上、羽子板ボルト、かね折り金物又は同等以上の仕口
T2	通し柱の両側に胴差が来る場合	胴差を柱にかたぎ大入れ短ほぞ差しの上、短冊金物又は、同等以上の仕口で胴差相互を緊結
T3	通し柱と胴差の接合部の近くに90×90以上の筋かいが来る場合(通し柱が建物の出隅にあるか、筋かい壁が外壁と直交して接する場合)	胴差を通し柱に、15KN用引き寄せ金物を水平に用いて緊結

決定図

3ヶ所702 指示書 1F

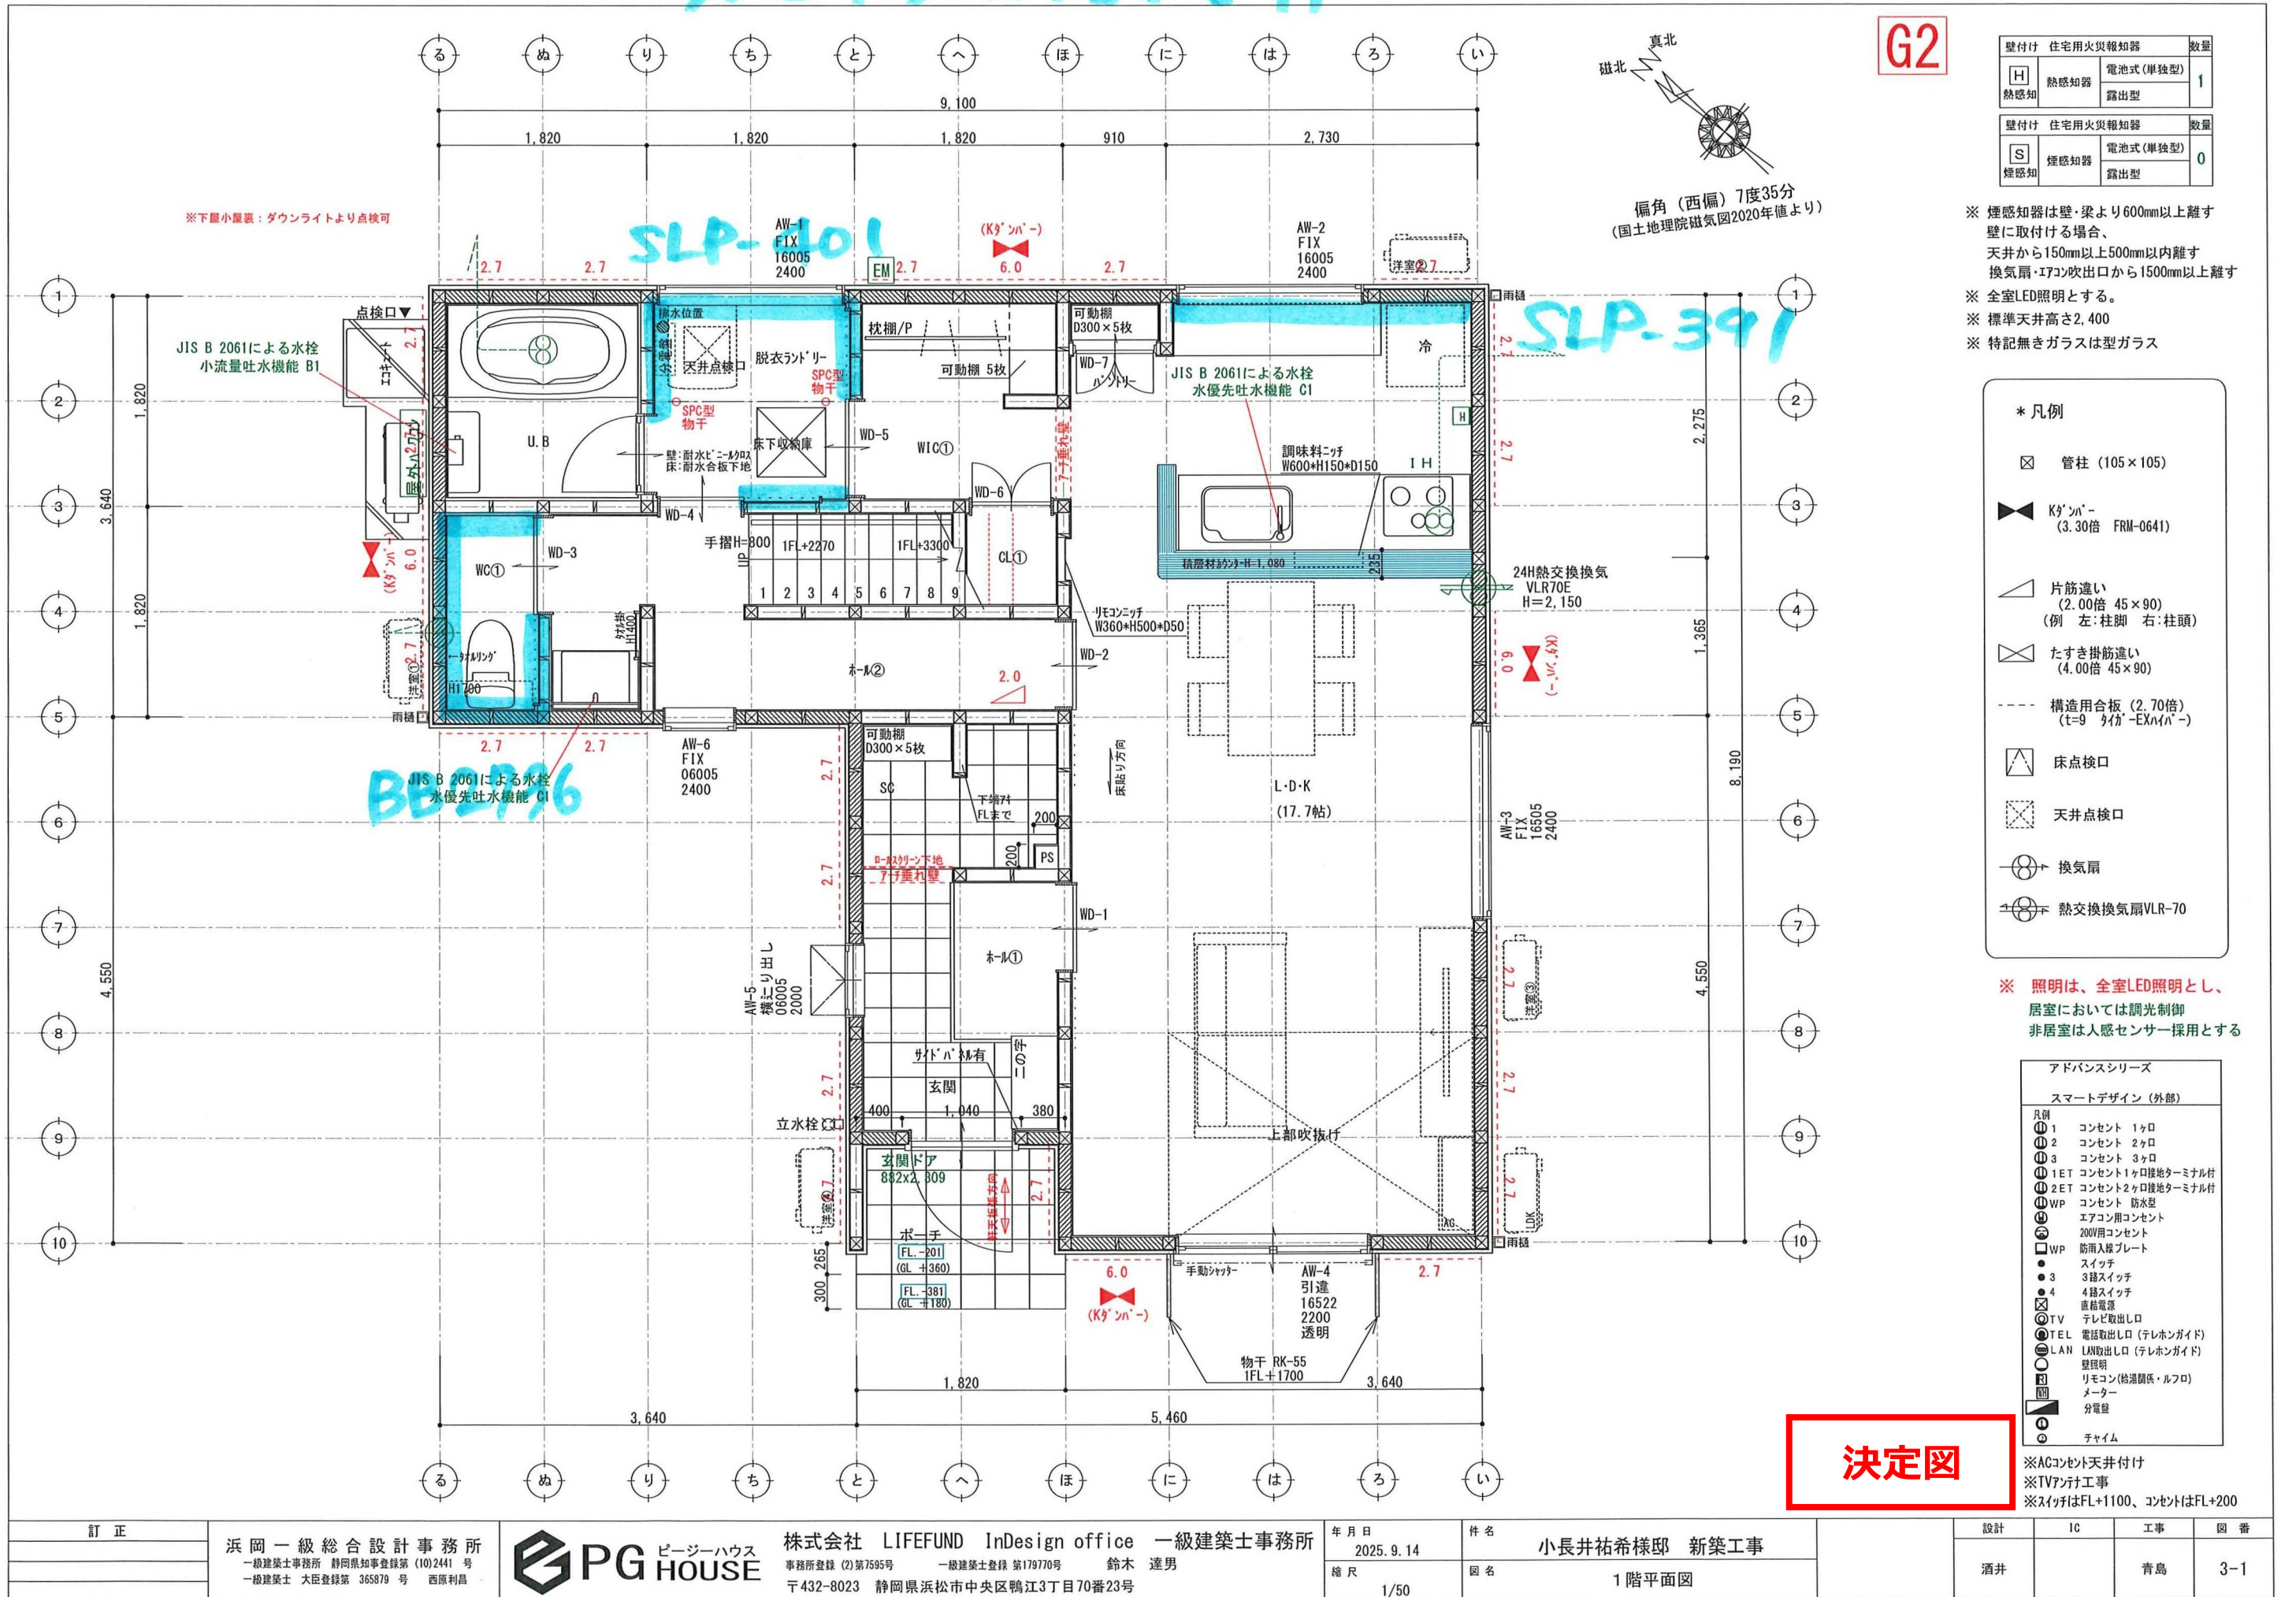

G2

壁付け 住宅用火災報知器			数量
[H] 熱感知	熱感知器	電池式(単独型)	1
		露出型	
壁付け 住宅用火災報知器			数量
[S] 煙感知	煙感知器	電池式(単独型)	0
		露出型	

※ 煙感知器は壁・梁より600mm以上離す
壁に取付ける場合、
天井から150mm以上500mm以内離す
換気扇・エアコン吹出口から1500mm以上離す
※ 全室LED照明とする。
※ 標準天井高さ2,400
※ 特記無きガラスは型ガラス

* 凡例

- 管柱 (105×105)
- K'ンバー (3.30倍 FRM-0641)
- 片筋違い (2.00倍 45×90)
(例 左:柱脚 右:柱頭)
- たすき掛筋違い (4.00倍 45×90)
- 構造用合板 (2.70倍)
(t=9 4'4" -EXN/A-N-)
- 床点検口
- 天井点検口
- 換気扇
- 熱交換換気扇VLR-70

※ 照明は、全室LED照明とし、
居室においては調光制御
非居室は人感センサー採用とする


アドバンスシリーズ		
スマートデザイン (外部)		
凡例	1	コンセント 1ヶ所
①	2	コンセント 2ヶ所
②	3	コンセント 3ヶ所
③	1ET	コンセント1ヶ所接地ターミナル付
④	2ET	コンセント2ヶ所接地ターミナル付
⑤	WP	コンセント 防水型
⑥	WP	エアコン用コンセント
⑦	WP	200V用コンセント
⑧	WP	防雨入換プレート
⑨	●	スイッチ
⑩	●	3路スイッチ
⑪	●	4路スイッチ
⑫	⊗	直結電源
⑬	⊗	テレビ取出口
⑭	⊗	TEL 電話取出口 (テレホンガイド)
⑮	⊗	LAN LAN取出口 (テレホンガイド)
⑯	⊗	照明
⑰	⊗	リモコン (格調調度・ルフロ)
⑱	⊗	メーター
⑲	⊗	分電盤
⑳	⊗	チャイム

※ACコンセント天井付け
※TVアンテナ工事
※スイッチはFL+1100、コンセントはFL+200

決定図

3次元CAD表示書 2F

G2

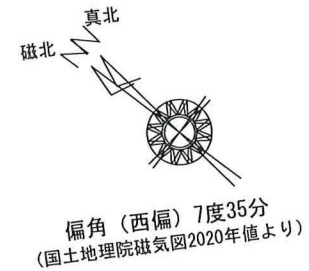

壁付け 住宅用火災報知器			数量
[H]	熱感知器	電池式(単独型)	0
	熱感知器	露出型	0
壁付け 住宅用火災報知器			数量
[S]	煙感知器	電池式(単独型)	4
	煙感知器	露出型	0

- ※ 煙感知器は壁・梁より600mm以上離す壁に取付ける場合、天井から150mm以上500mm以内離す換気扇・エアコン吹出口から1500mm以上離す
- ※ 全室LED照明とする。
- ※ 標準天井高さ2,400
- ※ 特記無きガラスは型ガラス

* 凡例

- 管柱 (105×105)
- K'ンバー (3.30倍 FRM-0641)
- 片筋違い (2.00倍 45×90) (例 左:柱脚 右:柱頭)
- たすき掛筋違い (4.00倍 45×90)
- 構造用合板 (2.70倍) (t=9 9分 EXN/A-)
- 床点検口
- 天井点検口
- 換気扇
- 熱交換換気扇VLR-70

※ 照明は、全室LED照明とし、居室においては調光制御非居室は人感センサー採用とする

アドバンスシリーズ		
スマートデザイン (外部)		
凡例	1	コンセント 1ヶ口
②	2	コンセント 2ヶ口
③	3	コンセント 3ヶ口
④	4	コンセント 4ヶ口
⑤	5	コンセント 5ヶ口
⑥	6	コンセント 6ヶ口
⑦	7	コンセント 7ヶ口
⑧	8	コンセント 8ヶ口
⑨	9	コンセント 9ヶ口
⑩	10	コンセント 10ヶ口
⑪	11	コンセント 11ヶ口
⑫	12	コンセント 12ヶ口
⑬	13	コンセント 13ヶ口
⑭	14	コンセント 14ヶ口
⑮	15	コンセント 15ヶ口
⑯	16	コンセント 16ヶ口
⑰	17	コンセント 17ヶ口
⑱	18	コンセント 18ヶ口
⑲	19	コンセント 19ヶ口
⑳	20	コンセント 20ヶ口
㉑	21	コンセント 21ヶ口
㉒	22	コンセント 22ヶ口
㉓	23	コンセント 23ヶ口
㉔	24	コンセント 24ヶ口
㉕	25	コンセント 25ヶ口
㉖	26	コンセント 26ヶ口
㉗	27	コンセント 27ヶ口
㉘	28	コンセント 28ヶ口
㉙	29	コンセント 29ヶ口
㉚	30	コンセント 30ヶ口
㉛	31	コンセント 31ヶ口
㉜	32	コンセント 32ヶ口
㉝	33	コンセント 33ヶ口
㉞	34	コンセント 34ヶ口
㉟	35	コンセント 35ヶ口
㊱	36	コンセント 36ヶ口
㊲	37	コンセント 37ヶ口
㊳	38	コンセント 38ヶ口
㊴	39	コンセント 39ヶ口
㊵	40	コンセント 40ヶ口
㊶	41	コンセント 41ヶ口
㊷	42	コンセント 42ヶ口
㊸	43	コンセント 43ヶ口
㊹	44	コンセント 44ヶ口
㊺	45	コンセント 45ヶ口
㊻	46	コンセント 46ヶ口
㊼	47	コンセント 47ヶ口
㊽	48	コンセント 48ヶ口
㊾	49	コンセント 49ヶ口
㊿	50	コンセント 50ヶ口
㊿	51	コンセント 51ヶ口
㊿	52	コンセント 52ヶ口
㊿	100	コンセント 100ヶ口

※ACコンセント天井付け
※TVアンテナ工事
※スイッチはFL+1100、コンセントはFL+200

決定図

