


3ヶ所702 指示書 1F

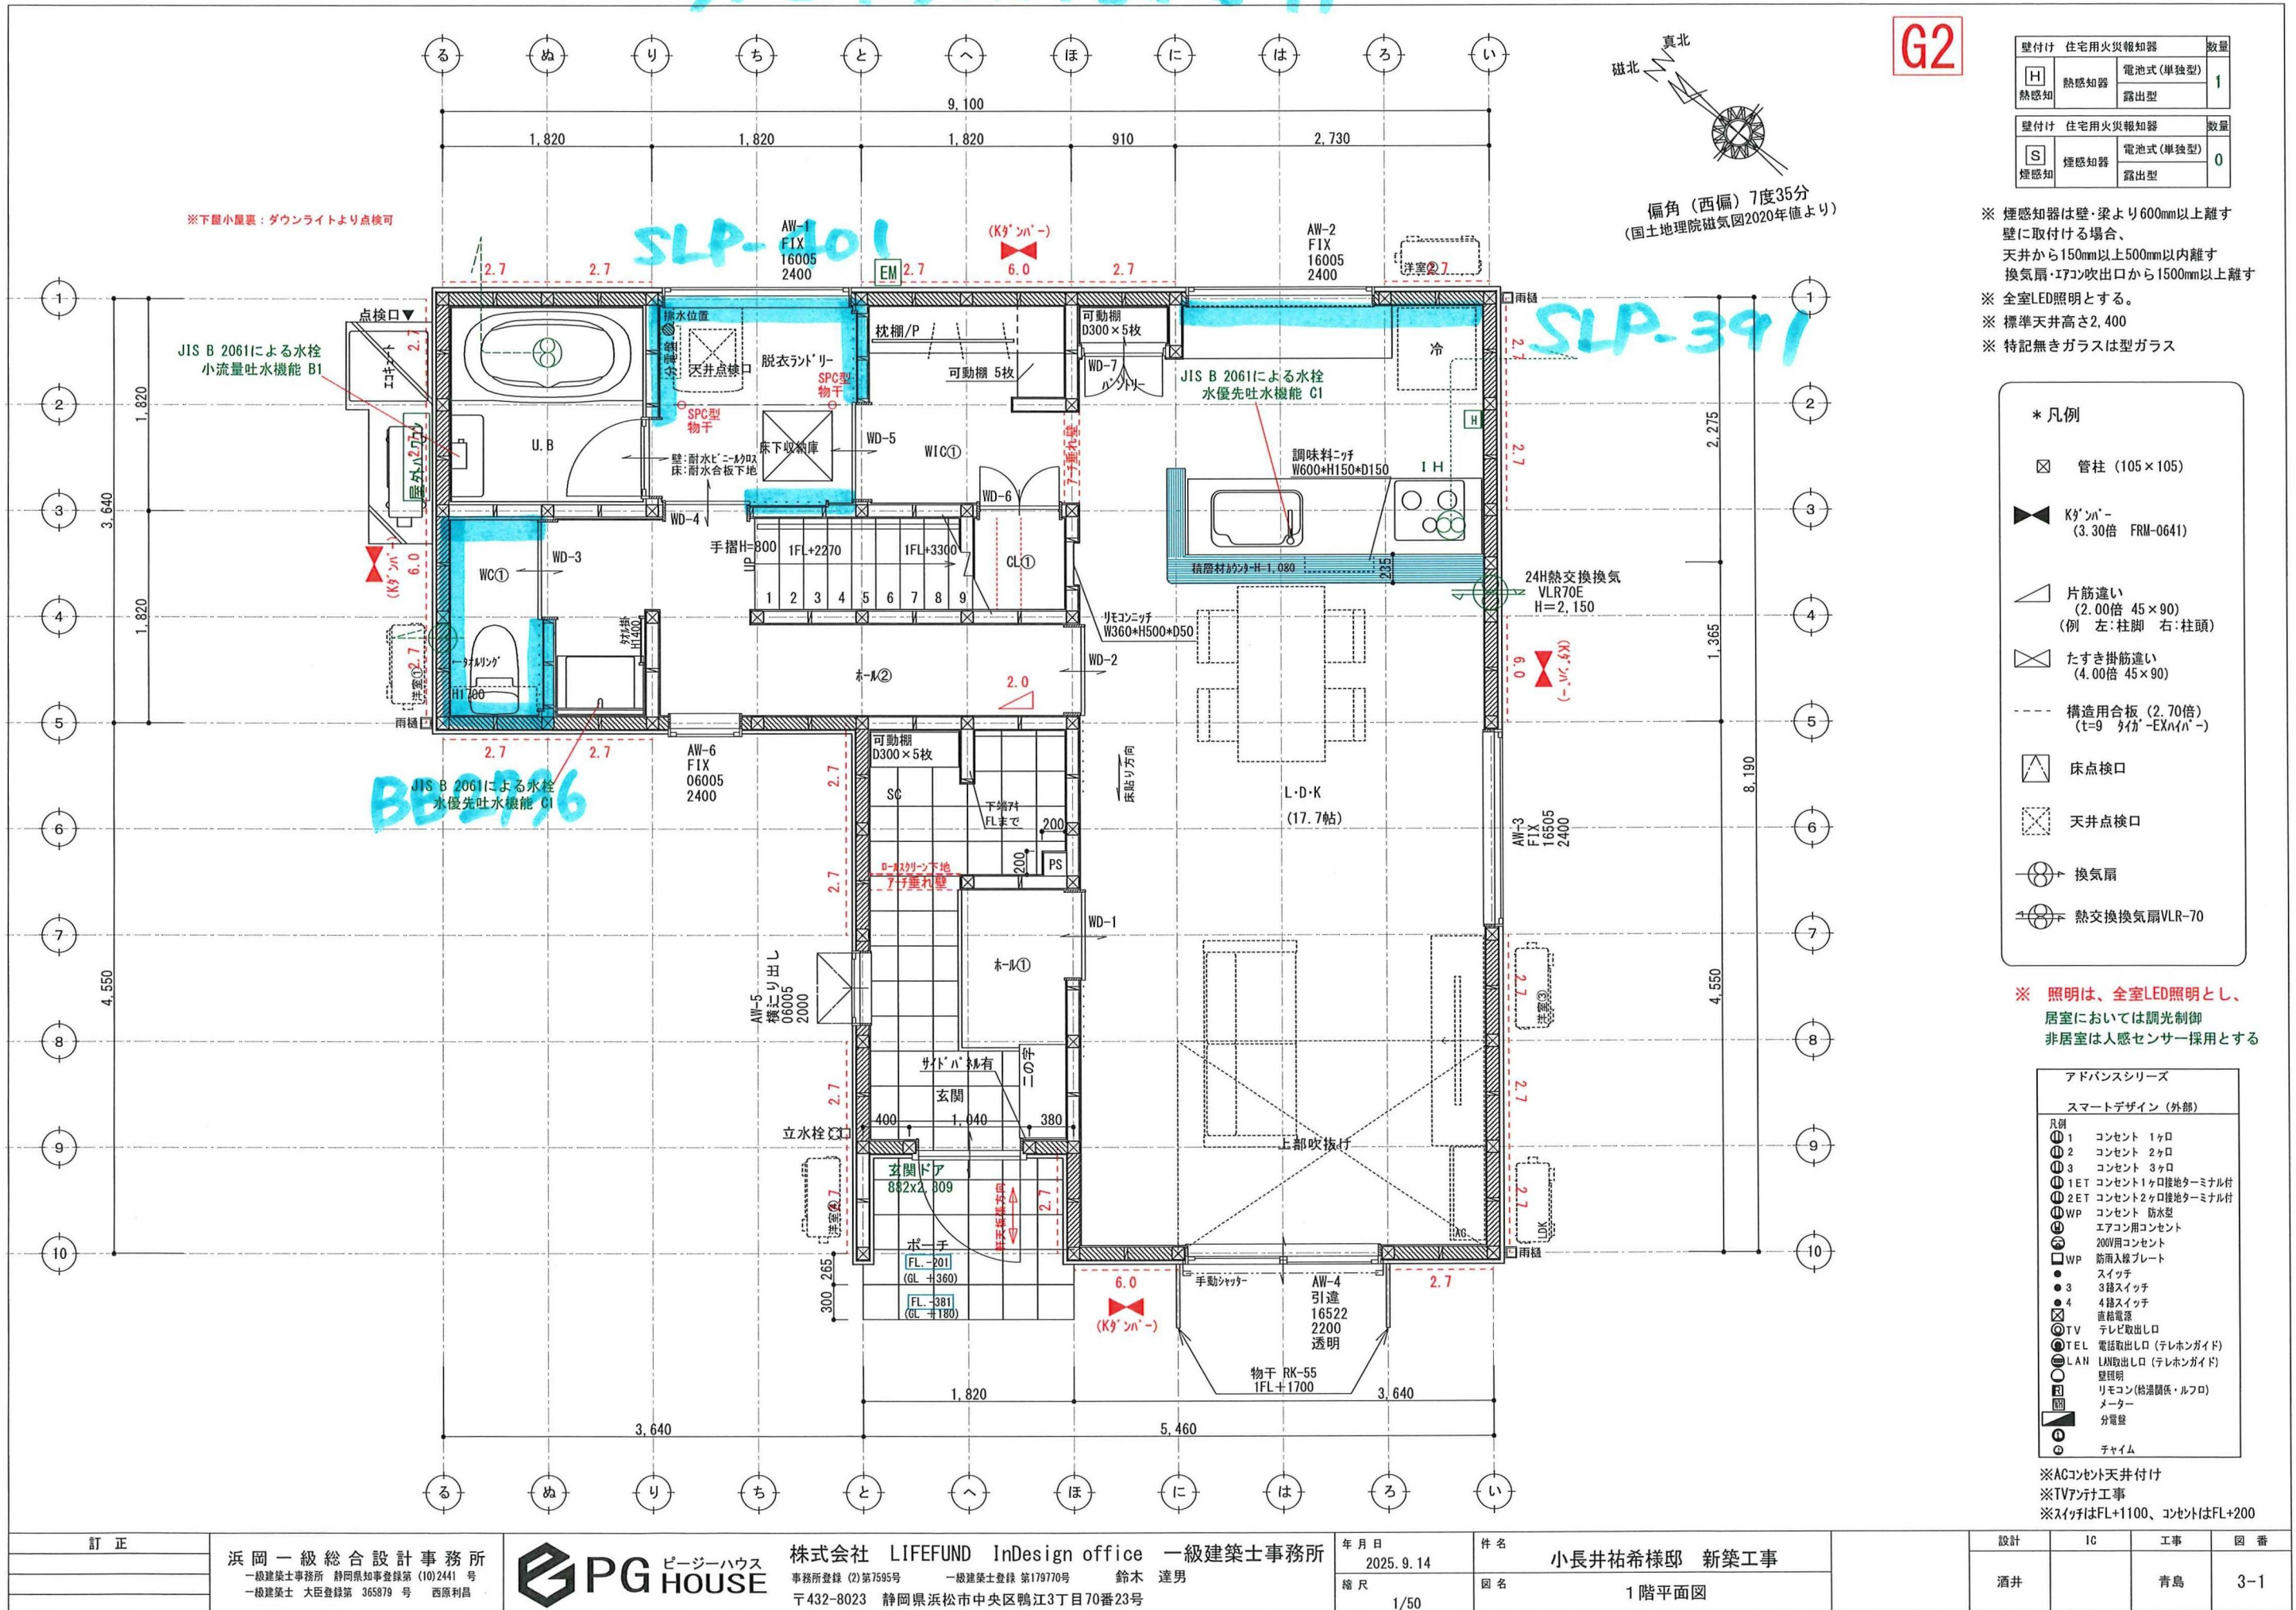

G2

壁付け 住宅用火災報知器			数量
[H] 熱感知	熱感知器	電池式(単独型)	1
		露出型	
壁付け 住宅用火災報知器			数量
[S] 煙感知	煙感知器	電池式(単独型)	0
		露出型	

※ 煙感知器は壁・梁より600mm以上離す
壁に取付ける場合、
天井から150mm以上500mm以内離す
換気扇・エアコン吹出口から1500mm以上離す

※ 全室LED照明とする。

※ 標準天井高さ2,400

※ 特記無きガラスは型ガラス

* 凡例

☒ 管柱 (105×105)

◀▶ K'ンバー
(3.30倍 FRM-0641)

△ 片筋違い
(2.00倍 45×90)
(例 左:柱脚 右:柱頭)

⊠ たすき掛筋違い
(4.00倍 45×90)

--- 構造用合板 (2.70倍)
(t=9 4インチ EXN/A-N)

△ 床点検口

⊠ 天井点検口

⊕ 換気扇

⊕ 熱交換換気扇VLR-70


※ 照明は、全室LED照明とし、
居室においては調光制御
非居室は人感センサー採用とする

アドバンスシリーズ		
スマートデザイン (外部)		
凡例	① 1	コンセント 1ヶ所
	② 2	コンセント 2ヶ所
	③ 3	コンセント 3ヶ所
	①ET	コンセント1ヶ所接地ターミナル付
	②ET	コンセント2ヶ所接地ターミナル付
	①WP	コンセント 防水型
	②WP	エアコン用コンセント
	③WP	200V用コンセント
	④WP	防雨入換プレート
	①	スイッチ
	③	3路スイッチ
	④	4路スイッチ
	①	直結電源
	①TV	テレビ取出口
	①TEL	電話取出口 (テレホンガイド)
	①LAN	LAN取出口 (テレホンガイド)
	①	壁照明
	①	リモコン (格調調度・ルフロ)
	①	メーター
	①	分電盤
	①	チャイム

※ACコンセント天井付け
※TVアンテナ工事
※スイッチはFL+1100、コンセントはFL+200

3次元CAD表示書 2F

G2

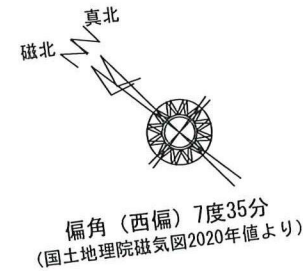

壁付け 住宅用火災報知器			数量
[H]	熱感知器	電池式(単独型)	0
	熱感知器	露出型	0
壁付け 住宅用火災報知器			数量
[S]	煙感知器	電池式(単独型)	4
	煙感知器	露出型	0

- ※ 煙感知器は壁・梁より600mm以上離す壁に取付ける場合、天井から150mm以上500mm以内離す換気扇・エアコン吹出口から1500mm以上離す
- ※ 全室LED照明とする。
- ※ 標準天井高さ2,400
- ※ 特記無きガラスは型ガラス

- * 凡例
- 管柱 (105×105)
 - K'ンパ (3.30倍 FRM-0641)
 - 片筋違い (2.00倍 45×90) (例 左:柱脚 右:柱頭)
 - たすき掛筋違い (4.00倍 45×90)
 - 構造用合板 (2.70倍) (t=9 9分 EXN/A-)
 - 床点検口
 - 天井点検口
 - 換気扇
 - 熱交換換気扇VLR-70

- ※ 照明は、全室LED照明とし、居室においては調光制御非居室は人感センサー採用とする

アドバンスシリーズ		
スマートデザイン (外部)		
凡例	1	コンセント 1ヶ口
②	2	コンセント 2ヶ口
③	3	コンセント 3ヶ口
④ET	コンセント1ヶ口接地ターミナル付	
⑤ET	コンセント2ヶ口接地ターミナル付	
⑥WP	コンセント 防水型	
⑦	エアコン用コンセント	
⑧	200V用コンセント	
⑨WP	防雨入線プレート	
⑩	スイッチ	
⑪	3線スイッチ	
⑫	4線スイッチ	
⑬	直結電源	
⑭TV	テレビ取出口	
⑮TEL	電話取出口 (テレホンガイド)	
⑯LAN	LAN取出口 (テレホンガイド)	
⑰	照明	
⑱	リモコン (給湯関係・ルフロ)	
⑲	メーター	
⑳	分電盤	
㉑	チャイム	

- ※ACコンセント天井付け
- ※TVアンテナ工事
- ※スイッチはFL+1100、コンセントはFL+200

決定図

