



面

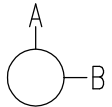

A面

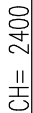

面

[illegible]

【ご注意】

- 記載のキャビネット寸法は扉前面までの呼び寸法です。キャビネット本体の寸法・扉厚等は商品ガイドの巻末資料をご確認ください。

特記事項 扉色 VK5:グレージュスタック 取手 [M]スリム取手（ブラック）	物件名	太田悠斗 様邸	案件No.	図面名	担当	図面	図番 : 株式会社 LIXIL
			A2506DDDD0ENN9M	レイアウト図	栗野 友仁		
	仕様	ES21	見積No.	縮尺	日付		
			M25067881610-005-3	1/30	2025.08.23		



特記事項
扉色 VK5:グレージュスタッコ
取手 [M]スリム取手（ブラック）



物件名	太田悠斗 様邸
仕様	E S 2 1

案件No.	図面名	担当	図面
A2506DDDD0ENN9M	納まり図	葉野 友仁	
見積No.	縮尺	日付	
M25067881610-005-3	1/30	2025.08.23	

図番 :
 株式会社 LIXIL


B面

B面

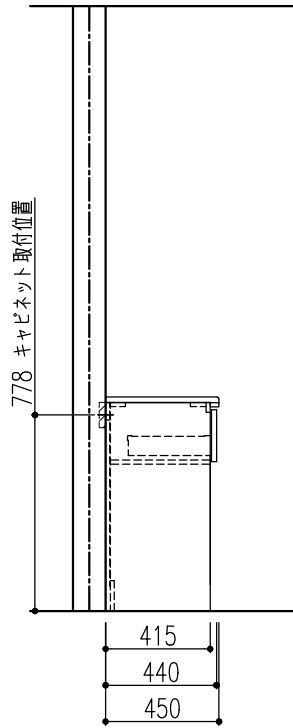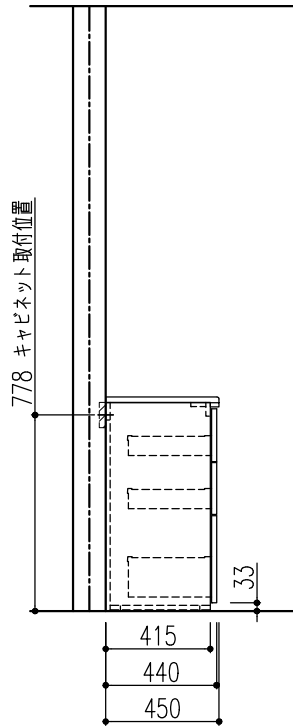

特記事項 扉色 VK5:グレージュスタック 取手 [M]スリム取手（ブラック）	物件名	太田悠斗 様邸	案件No.	図面名	担当	図面	図番
	仕様	E S 2 1	A2506DDD0ENN9M	納まり図	栗野 友仁		株式会社 LIXIL
			見積No.	縮尺	日付		
			M25067881610-005-3	1/30	2025.08.23		

■ 床の不陸に関して

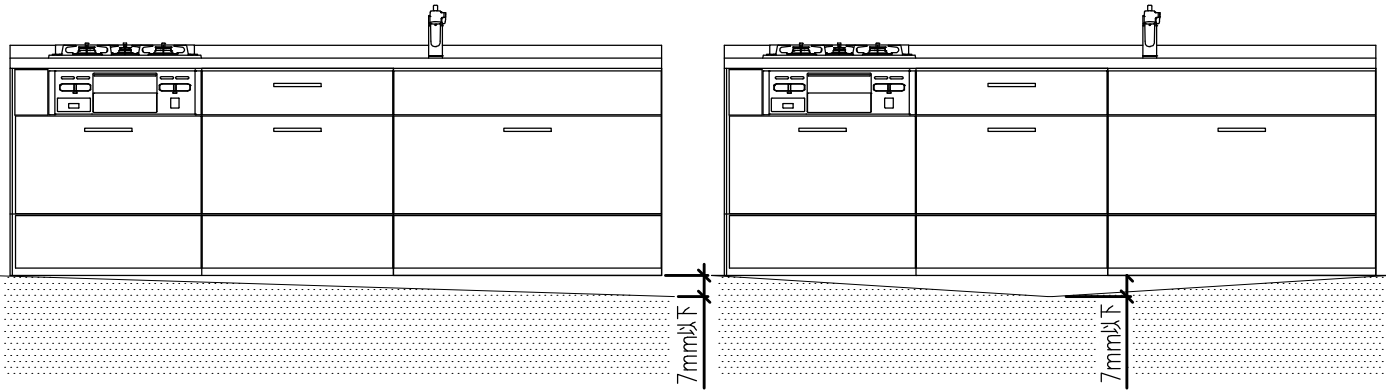

床の不陸は、7 m m 以下に抑えるようにしてください。不陸が大きい場合は、現場責任者に床の修正を依頼してください。
※キャビネット取付時には不陸調整スペーサー等で水平になるように設置してください。

	特記事項 扉色 VK5:グレージュスタック 取手 [M]スリム取手（ブラック）	物件名	太田悠斗 様邸	案件No.	図面名	担当	図面	図番
				A2506DDD0ENN9M	機能図	栗野 友仁		株式会社 LIXIL
				見積No.	縮尺	日付		
				M25067881610-005-3		2025.08.23		
		仕様	ES 2 1					

■ キッチン取付者さま向け 動画コンテンツ ■
商品取付けの注意点を2次元コードでご視聴いただけます。
取付日より前に、是非ご確認ください。

1 ページ目

■ キッチン取付者さま向け 動画コンテンツ ■
商品取付けの注意点を2次元コードでご視聴いただけます。
取付日より前に、是非ご確認ください。

1 ページ目

■ キッチン取付者さま向け 動画コンテンツ ■
商品取付けの注意点を2次元コードでご視聴いただけます。
取付日より前に、是非ご確認ください。

1 ページ目

荷扱い・搬入


荷扱い・搬入



作成日：2024年10月01日

荷扱い・搬入

荷扱い・搬入

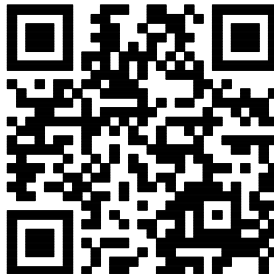


作成日：2024年10月01日



荷扱い・搬入


荷扱い・搬入

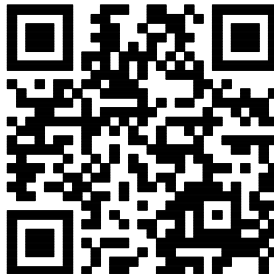

作成日：2024年10月01日

カウンター開梱搬入「養生ツール」


カウンター開梱搬入 「養生ツール」のご紹介

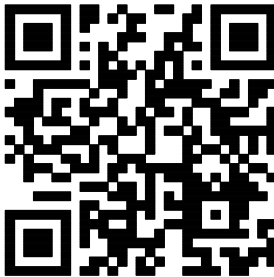

作成日：2024年10月01日

カウンター開梱搬入「養生ツール」

カウンター開梱搬入 「養生ツール」のご紹介

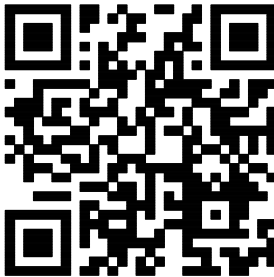


作成日：2024年10月01日




カウンター開梱搬入「養生ツール」

カウンター開梱搬入 「養生ツール」のご紹介


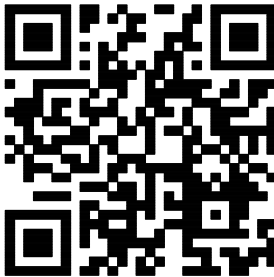


作成日：2024年10月01日


不陸の確認と調整

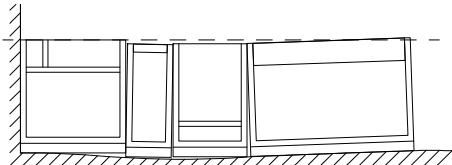

作成日：2024年02月07日

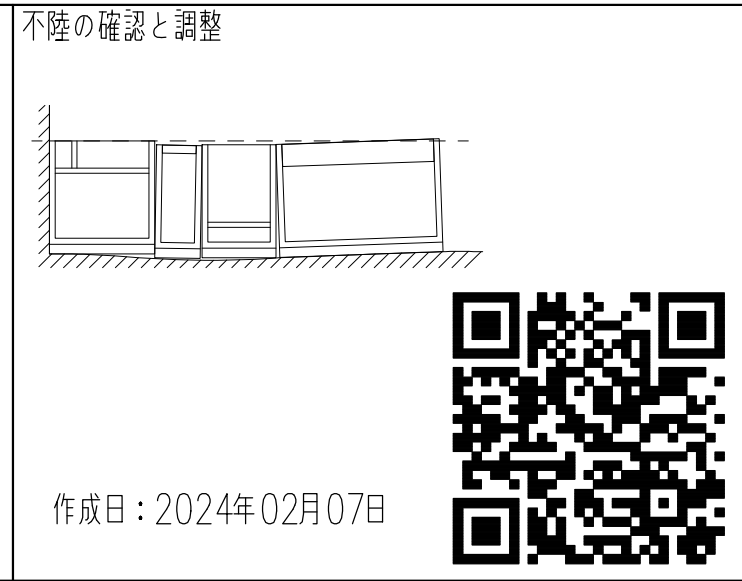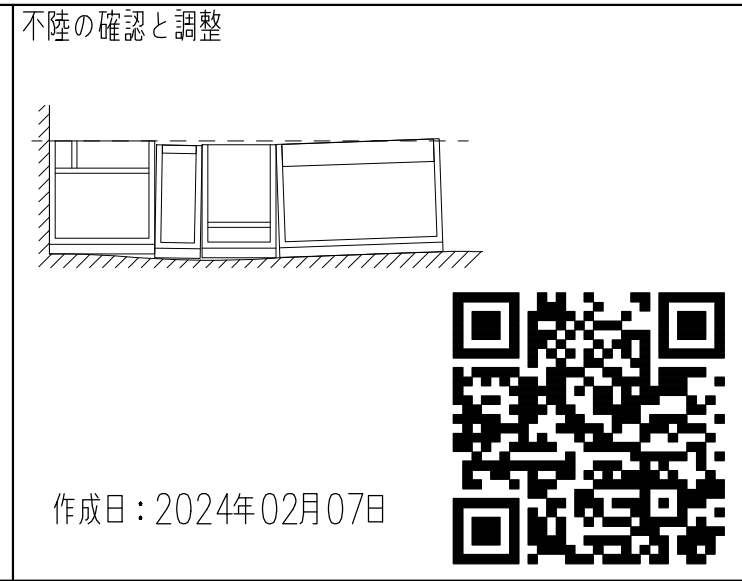

不陸の確認と調整

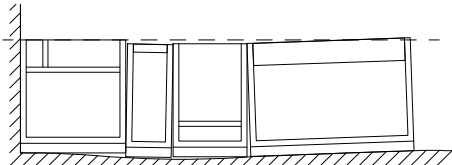

作成日：2024年02月07日

マグネット キッチンパネル

マグネット キッチンパネル 「取付・設置」ポイント



作成日：2024年03月06日

マグネット キッチンパネル

マグネット キッチンパネル 「取付・設置」ポイント



作成日：2024年03月06日




マグネット キッチンパネル

マグネット キッチンパネル 「取付・設置」ポイント



作成日：2024年03月06日


人造大理石カウンターL型キッチン

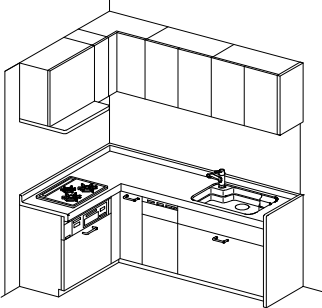

作成日：2024年02月07日




人造大理石カウンターL型キッチン

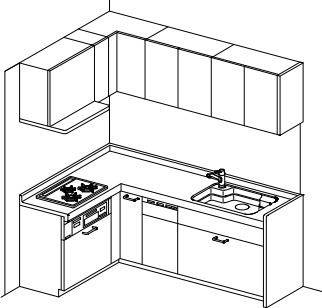



作成日：2024年02月07日




センターキッチン（ペニンシュラ型）

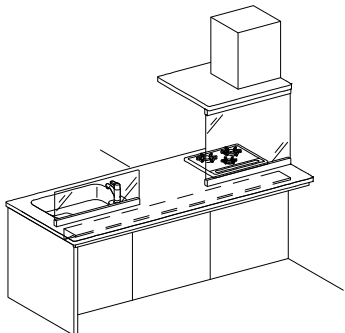

作成日：2024年02月07日

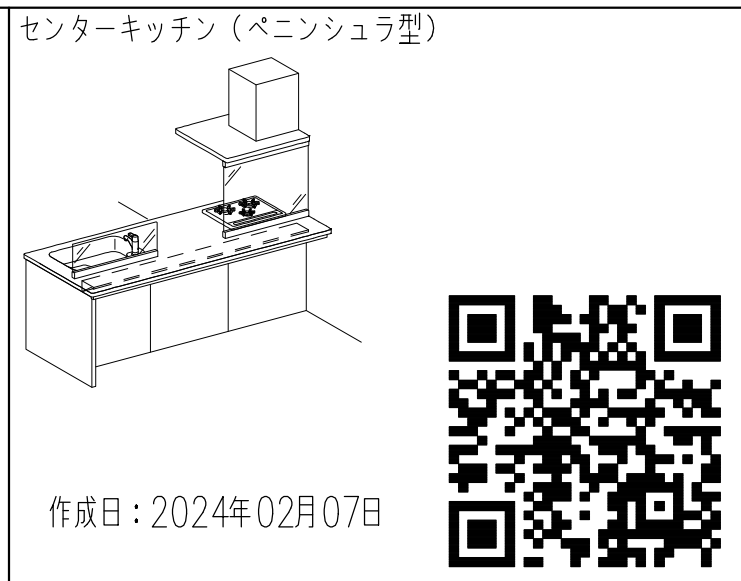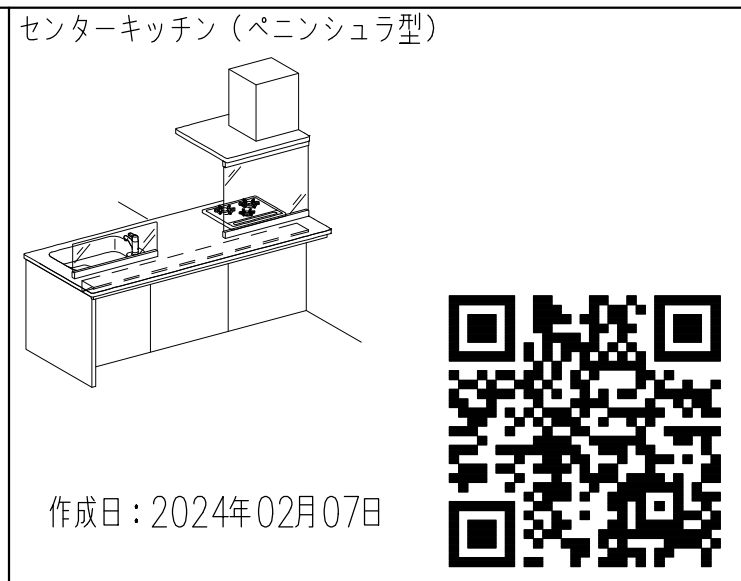

センターキッチン（ペニンシュラ型）





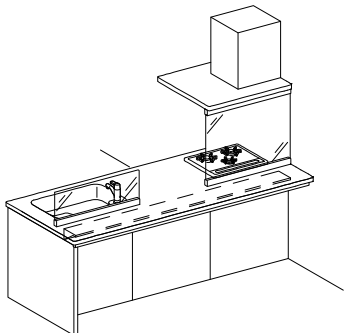


作成日：2024年02月07日

[illegible]

■ キッチン取付者さま向け 動画コンテンツ ■

商品取付けの注意点を2次元コードでご視聴いただけます。
取付日より前に、是非ご確認ください。

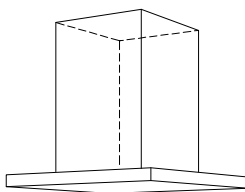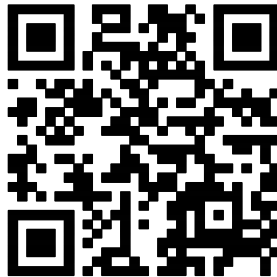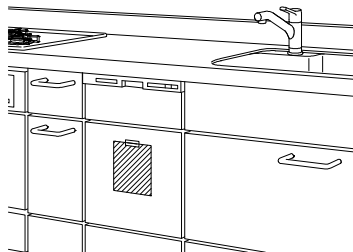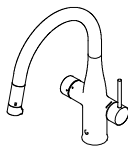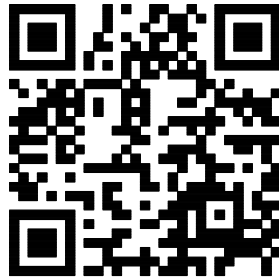センターフード型レンジフード (天吊りフード)  作成日：2024年06月03日 		I H加熱機器関連 I H加熱機器 仕切り板 作成日：2024年02月07日 		食器洗い乾燥機  作成日：2024年02月07日 		ミネラル浄水栓 Greentap  作成日：2024年06月03日 			
	特記事項 扉色 VK5:グレージュスタック 取手 [M]スリム取手 (ブラック)	物件名 仕様	太田悠斗 様邸		案件No.	図面名	担当	図面	図番
					A2506DDD0ENN9M	機能図	栗野 友仁		株式会社 LIXIL
			ES21		見積No.	縮尺	日付		
					M25067881610-005-3		2025.08.23		