

壁付け 住宅用火災報知器			数量
 熱感知	熱感知器	電池式(単独型)	4
		露出型	
壁付け 住宅用火災報知器			数量
 煙感知	煙感知器	電池式(単独型)	4
		露出型	

- ※ 煙感知器は壁・梁より600mm以上離す
壁に取付ける場合、
天井から150mm以上500mm以内離す
換気扇・エアコン吹出口から1500mm以上離す
- ※ 全室LED照明とする。
- ※ 標準天井高さ2,400
- ※ 特記無きガラスは型ガラス

* 凡例

-  管柱 (105×105)
 K $\frac{1}{2}$ " $\frac{1}{2}$ " $\frac{1}{2}$ "
 (3.30倍 FRM-0641)
 片筋違
 (2.00倍 45×90)
 (例 左:柱脚 右:柱頭)
 たすき掛筋違
 (4.00倍 45×90)
 - - - 構造用合板 (2.70倍)
 (t=9 $\frac{1}{2}$ " $\frac{1}{2}$ " $\frac{1}{2}$ "-EX $\frac{1}{2}$ " $\frac{1}{2}$ " $\frac{1}{2}$ "-)
 床点検口
 天井点検口
 換気扇
 熱交換換気扇VLR-70


アドバンスシリーズ

スマートデザイン（外部）

- 1 コンセント 1ヶロ
- 2 コンセント 2ヶロ
- 3 コンセント 3ヶロ
- 1 E T コンセント1ヶロ接地ターミナル
- 2 E T コンセント2ヶロ接地ターミナル
- WP コンセント 防水型
- ア エア用コンセント
- 200V用コンセント
- WP 防雨入線プレート
- スイッチ
- 3 路スイッチ
- 4 路スイッチ
- ⊗ 直結電源
- TV テレビ取出しロ
- TEL 電話取出しロ (テレホンガイド)
- LAN 取出口 (テレホンガイド)
- 壁照明
- リモ (給湯関係・ルフロ)
- メーウ
- 分電盤
- チャイム

※ACコンセント天井付け
※TVアンテナ工事
※スイッチはFL+1100、コンセントはFL+200

決定図

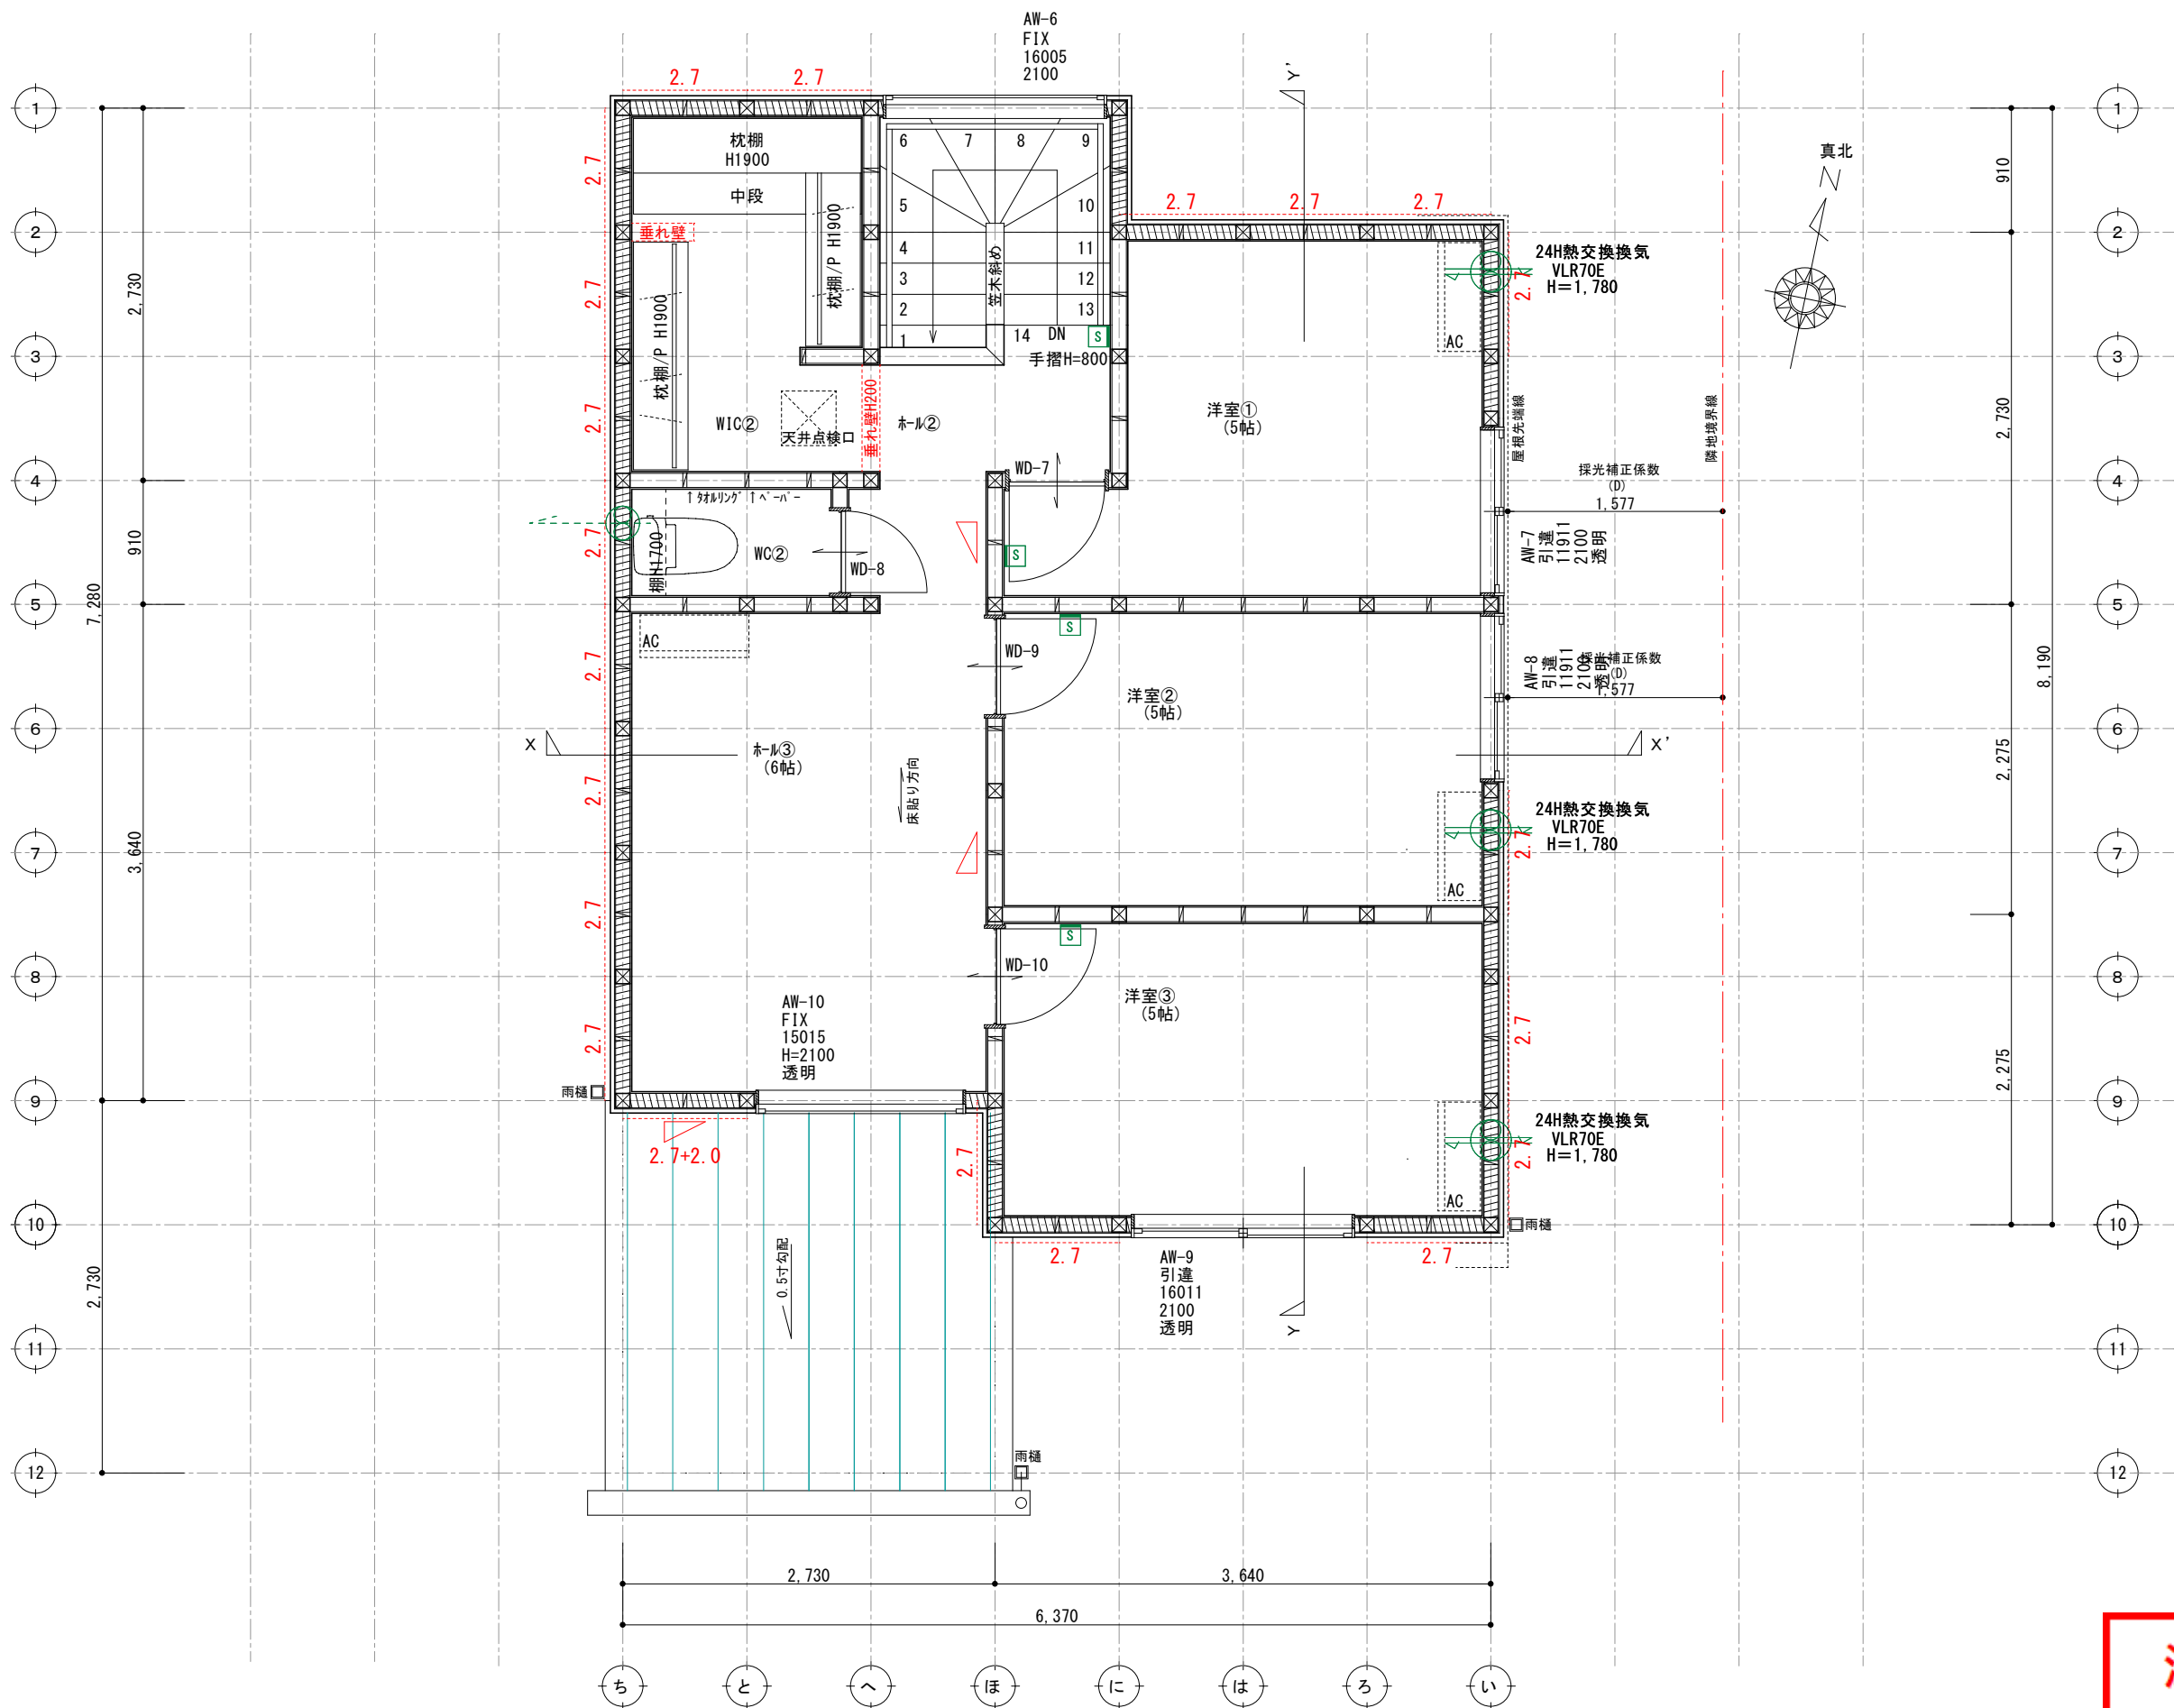

訂 正

浜岡一級総合設計事務所
一級建築士事務所 静岡県知事登録第 (10)2441 号
一級建築士 大臣登録第 365879 号 西原利昌



株式会社 LIFEFUND InDesign office 一級建築士事務所
事務所登録 (2) 第7595号 一級建築士登録 第179770号 鈴木 達男
〒432-8023 静岡県浜松市中央区鵜江3丁目70番23号

年 月 日
2025. 8. 30

縮 尺
1/50

件名	太田悠斗様邸 新築工事
図名	2階平面図

設計	IC	工事	図 番
酒井		青島	3-2