

37セントクロス指示書

G1

壁付付		住宅用火災報知器		変
H 熱感知	熱感知器	電池式(単独型)	露出型	
壁付付		住宅用火災報知器		変
S 煙感知	煙感知器	電池式(単独型)	露出型	


- ※ 煙感知器は壁・梁より600mm以上離す壁に取付ける場合、天井から150mm以上500mm以内離す換気扇・エアコン吹出口から1500mm以上離す
- ※ 全室LED照明とする。
- ※ 標準天井高さ2,400
- ※ 特記無きガラスは型ガラス

* 凡例

- ☒ 管柱 (105×105)
- ◀▶ K'ンパ (3.30倍 FRM-0641)
- △ 片筋違い (2.00倍 45×90) (例 左:柱脚 右:柱頭)
- ⊠ たすき掛筋違い (4.00倍 45×90)
- 構造用合板 (2.70倍) (t=9 94kg-EXN(17))
- ◀ 床点検口
- ⊠ 天井点検口
- ⊕ 換気扇
- ⊕ 熱交換換気扇VLR-70

アドバンスシリーズ	
スマートデザイン (外部)	
凡例	
①	コンセント 1ヶ口
②	コンセント 2ヶ口
③	コンセント 3ヶ口
①ET	コンセント1ヶ口接地ターミナル付
②ET	コンセント2ヶ口接地ターミナル付
WP	コンセント 防水型
WP	エアコン用コンセント
WP	200V用コンセント
WP	防雨入線プレート
●	スイッチ
●	3路スイッチ
●	4路スイッチ
⊠	直結電線
⊠TV	テレビ取出口
⊠TEL	電話取出口 (テレホンガイド)
⊠LAN	LAN取出口 (テレホンガイド)
⊠	壁掛型
⊠	リモコン (給湯関係・ルフロ)
⊠	メーカー
⊠	分電盤
⊠	チャイム

- ※ACコンセント天井付け
- ※TVアンテナ工事
- ※スイッチはFL+1100、コンセントはFL+200

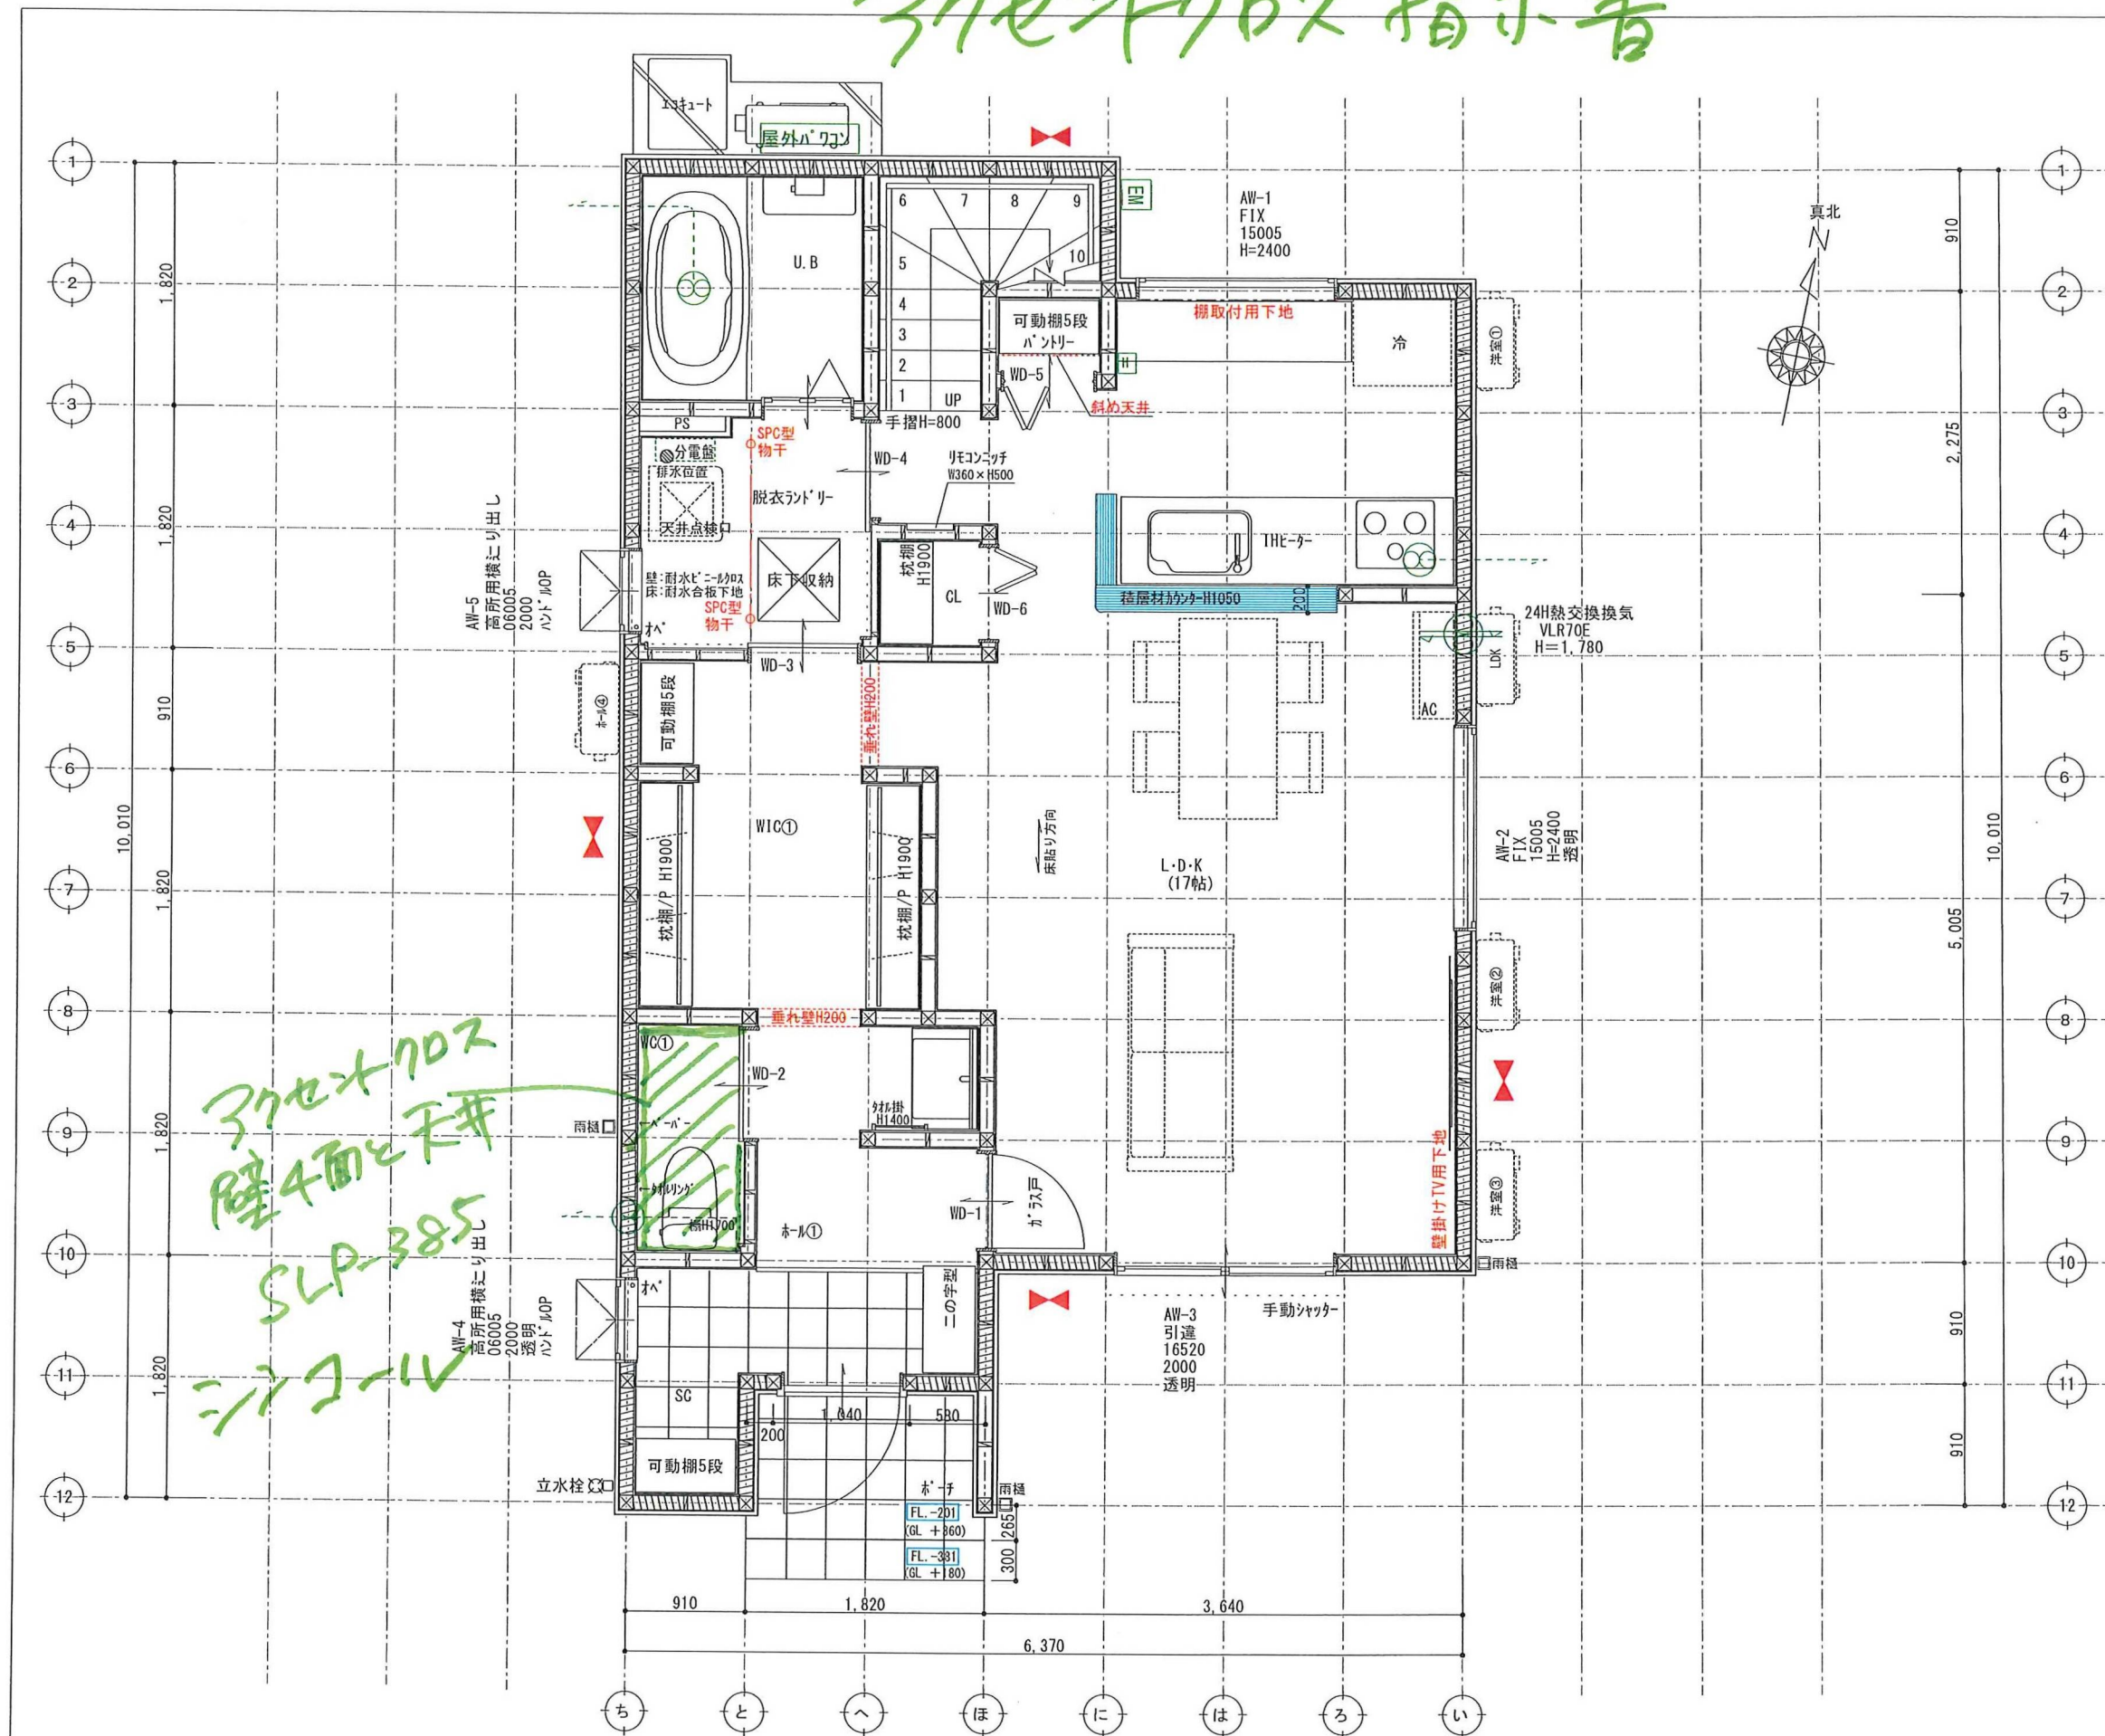

37セントクロス
壁4面と天井
SLP-385
シンコー

G1

壁付け 住宅用火災報知器			数量
H 熱感知	熱感知器	電池式(単独型)	
		露出型	
壁付け 住宅用火災報知器			数量
S 煙感知	煙感知器	電池式(単独型)	4
		露出型	

※ 煙感知器は壁・梁より600mm以上離す
壁に取付ける場合、
天井から150mm以上500mm以内離す
換気扇・エアコン吹出口から1500mm以上離す
※ 全室LED照明とする。
※ 標準天井高さ2,400
※ 特記無きガラスは型ガラス

* 凡例

- ☒ 管柱 (105×105)
- ≡ K' 'n' - (3.30倍 FRM-0641)
- △ 片筋違い (2.00倍 45×90)
(例 左:柱脚 右:柱頭)
- ⊗ たすき掛筋違い (4.00倍 45×90)
- 構造用合板 (2.70倍)
(t=9 タイガ EXハイパー)
- △ 床点検口
- ⊗ 天井点検口
- ⊗ 換気扇
- ⊗ 熱交換換気扇VLR-70

アドバンスシリーズ	
スマートデザイン (外装)	
凡例	
①	コンセント 1ヶ口
②	コンセント 2ヶ口
③	コンセント 3ヶ口
①ET	コンセント1ヶ口接地ターミナル付
②ET	コンセント2ヶ口接地ターミナル付
WP	コンセント 防水型
④	エアコン用コンセント
⑤	200V用コンセント
WP	防雨入換プレート
●	スイッチ
● 3	3路スイッチ
● 4	4路スイッチ
⊗	直結電源
TV	テレビ取出口
TEL	電話取出口 (テレホンガイド)
LAN	LAN取出口 (テレホンガイド)
⊗	壁照明
⊗	リモコン (松浦園氏・ルフロ)
⊗	メーター
⊗	分電盤
⊗	チャイム

※ACコンセント天井付け
※TVアンテナ工事
※スイッチはFL+1100、コンセントはFL+200



37セ+702
壁1面SLP-386
シ21-11