


内 部 仕 上 表 （壁下地:石膏ボード12.5mm/天井下地:9.5mm）※脱衣室:床合板特類 下地									
階		床	巾木	壁	品番	廻 縁	天 井	品番	特記事項
1F	ポーチ	LIXILパセオ300/PSO-FIO 1							
	玄関	LIXILパセオ300/PSO-FIO 1	ライン巾木(W)	ビニルクロス	SLP-252	突付	ビニルクロス	SLP-252	
	ホール①	イタ銘木フロアースティックt12 ナラ桎3P	ライン巾木(W)	ビニルクロス	SLP-252	突付	ビニルクロス	SLP-252	
	WC①	フロアタイルt2.3 サンゲツIS-2073	H40ソフト巾木W97	ビニルクロス	SLP-252	突付	ビニルクロス	SLP-252	アクセントクロス SLP-385
	LDK	イタ銘木フロアースティックt12 ナラ桎3P	ライン巾木(W)	ビニルクロス	SLP-252	突付	ビニルクロス	SLP-252	
	WIC①	イタ銘木フロアースティックt12 ナラ桎3P	ライン巾木(W)	ビニルクロス	SLP-252	突付	ビニルクロス	SLP-252	
	脱衣ランドリー	フロアタイルt2.3 サンゲツIS-2070	H40ソフト巾木W97	ビニルクロス	SLP-252	突付	ビニルクロス	SLP-252	
2F									
	洋室①	イタ銘木フロアースティックt12 ナラ桎3P	ライン巾木(W)	ビニルクロス	SLP-252	突付	ビニルクロス	SLP-252	
	洋室②	イタ銘木フロアースティックt12 ナラ桎3P	ライン巾木(W)	ビニルクロス	SLP-252	突付	ビニルクロス	SLP-252	
	洋室③	イタ銘木フロアースティックt12 ナラ桎3P	ライン巾木(W)	ビニルクロス	SLP-252	突付	ビニルクロス	SLP-252	アクセントクロス SLP-386
	ファミリースペース	イタ銘木フロアースティックt12 ナラ桎3P	ライン巾木(W)	ビニルクロス	SLP-252	突付	ビニルクロス	SLP-252	
	WC②	フロアタイルt2.3 サンゲツIS-2073	H40ソフト巾木W97	ビニルクロス	SLP-252	突付	ビニルクロス	SLP-252	
	WIC②	イタ銘木フロアースティックt12 ナラ桎3P	ライン巾木(W)	ビニルクロス	SLP-252	突付	ビニルクロス	SLP-252	
	ホール③	イタ銘木フロアースティックt12 ナラ桎3P	ライン巾木(W)	ビニルクロス	SLP-252	突付	ビニルクロス	SLP-252	
物入・収納・CL etc		※接続する部屋と同仕様とする							

上 框 ※	■ LIXILラシッサS 上框のみ30×150 色: クリエペール
階 段	■ LIXIL KA 階段 ササラ: プレシャスホワイト
KA階段で対応できない場合、オプション	段板 : クリエペール 蹴込板: プレシャスホワイト
ラウンド手摺: クリエペール	手摺金物 プレシャスホワイト
にてラシッサS階段	上段框: クリエペール 長尺笠木156: LIXIL プレシャスホワイト
窓 枠	■ LIXIL スマート10 色 プレシャスホワイト
	※浴室ドア枠 フクビ3方枠 [ホワイト]
キッチン笠木	■ ゴム集成カウンター(オスモカラー) 色 30627ロアーグリアmatt
カウンター	形状 L型(ジョイント加工) t=30
天井点検口	■ 天井アルミ点検口枠 450角 TAN45BW フクビ化学工業
	ミルキーホワイト
床下収納庫	■ 高気密型床下点検口断熱型 SPF-R6060 城東テクノ 収納付
	(脱衣室) ライトグレー(LG)
トイレ棚	■ 1,2階トイレ D250 アートランバー棚(シェルホワイト)
室内物干し金物	■ 川口技研SPC型1セット
LDK-カウンター	■ ゴム集成カウンター(オスモカラ 色 30627ロアーグリアmatt
	t=25
下足入	■ LIXILラシッサS 色 プレシャスホワイト
プッシュタイプ	サイズ: W800 D400 形状: 二の字型


支給品	■ 無し
備考	※付框は(30×150)プレシャスホワイト 可動棚アートランバー色 シェルホワイト 棚受金物類は全てホワイト

内 部 建 具 表								
LIXIL		建具色：プレシャスホワイト		枠色 ： 扉同色		※その他、下記特記による		
ラシッサS(標準)		把手 ： スクエアL (シャインニッケル) 丁番 固定枠(156) 外付戸当り ガイドピン床色合せ 引戸のみ上吊Wソフトモーション						
階	No	室名	形式	枠外W サイズ	デザイン	枠色	特記事項	
				枠外H サイズ	建具色	把手		
1	1	LDK	片開き戸	—	RAA	—	ラフィスに変更	
	WD			2400	—	—	プレシャスホワイト	
	2	WC①	片引き戸	—	LAA	—	明り窓・表示錠	
	WD			2000	—	—		
	3	脱衣ランドリー	片引き戸	—	LAA	—	明り窓・表示錠	
	WD			2000	—	—		
	4	脱衣ランドリー	片引き戸	—	LAA	—	明り窓・表示錠	
	WD			2000	—	—		
	5	パントリー	折れ戸	—	LAA	—	角型Lタテ取付	
	WD			2000	—	—		
	6	CL	折れ戸	—	LAA	—	角型Lタテ取付	
	WD			2000	—	—		
2	7	洋室①	片開き戸	—	LAA	—		
	WD			2000	—	—		
	8	WC②	片開き戸	—	LAA	—	明り窓・表示錠	
	WD			2000	—	—		
	9	洋室②	片開き戸	—	LAA	—		
	WD			2000	—	—		
	10	洋室③	片開き戸	—	LAA	—		
	WD			2000	—	—		

		浜 岡 一 級 総 合 設 計 事 務 所			株式会社 LIFEFUND InDesign office 一級建築士事務所		年 月 日	件名		太田悠斗 様邸 新築工事			設計	IC	工務	図 番
		一級建築士事務所 静岡県知事登録第 (10)2441 号			事務所登録 (2) 第7595号 一級建築士登録 第179770号 鈴木 達男		2025/8/30	図面		仕上表 2			酒井		青島	1-2
		一級建築士 大臣登録第 365879 号 西原利昌			〒432-8023 静岡県浜松市中央区鴨江3丁目70番23号		縮尺									

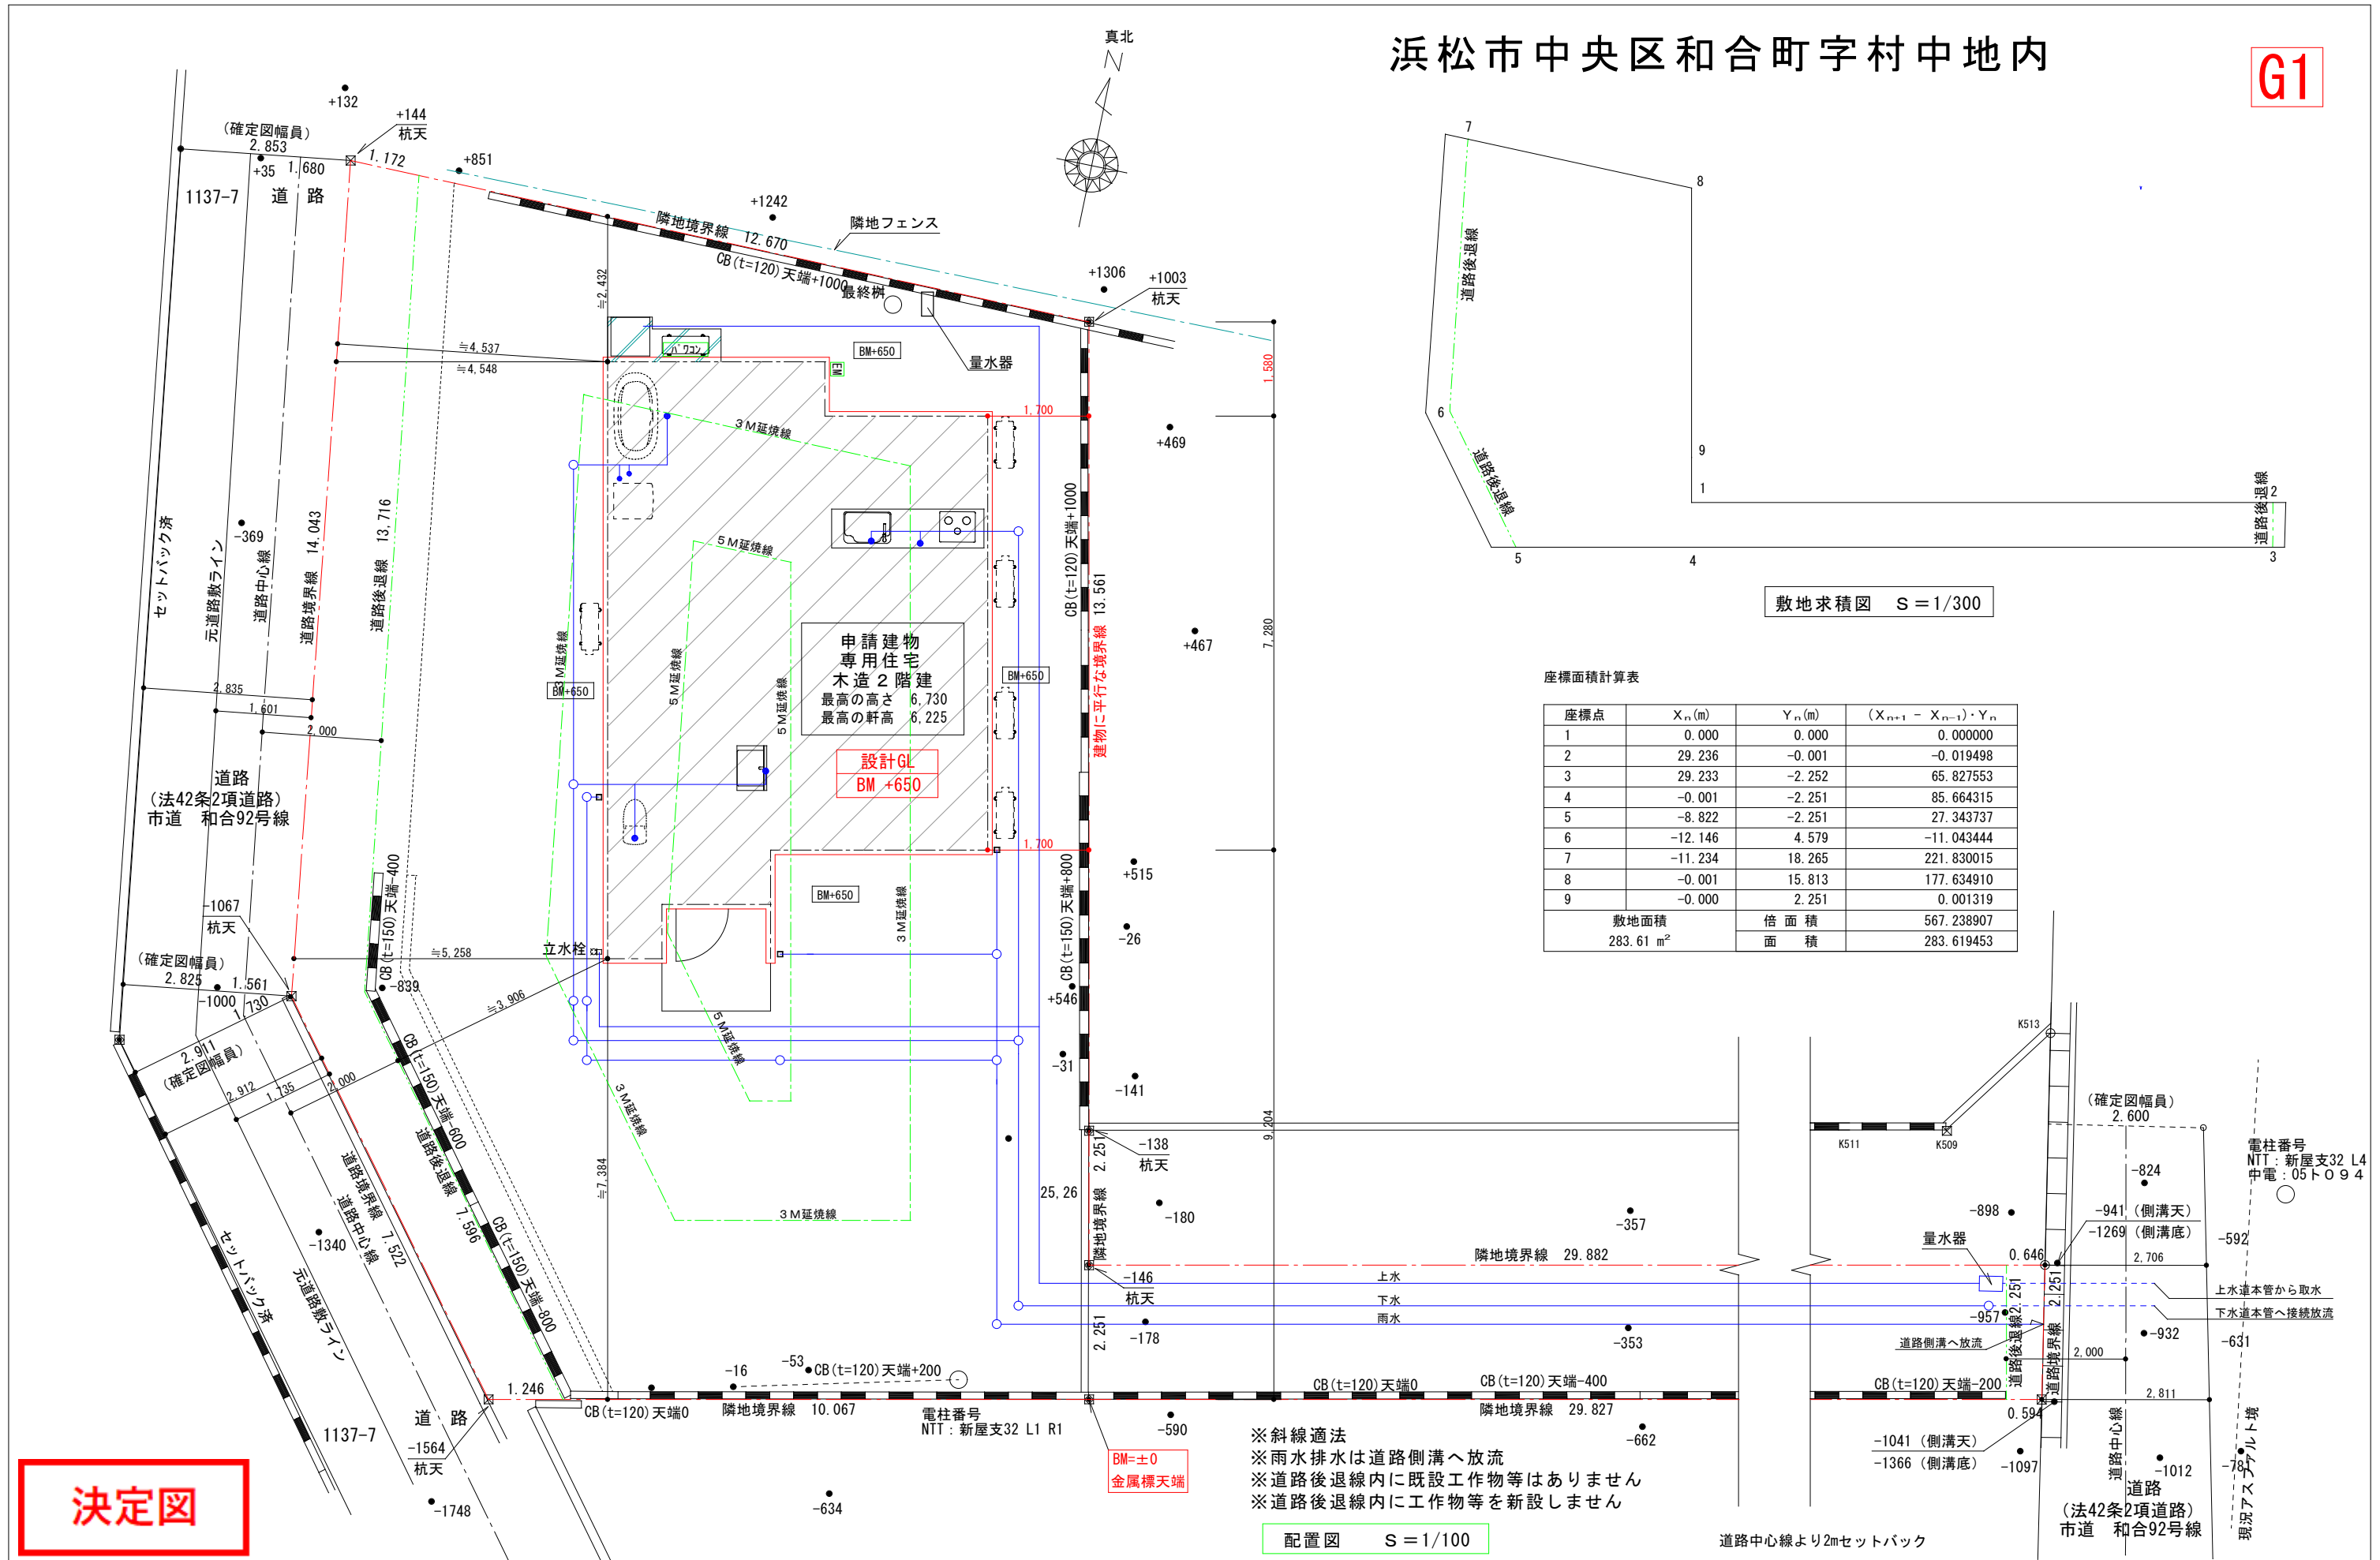


決定図

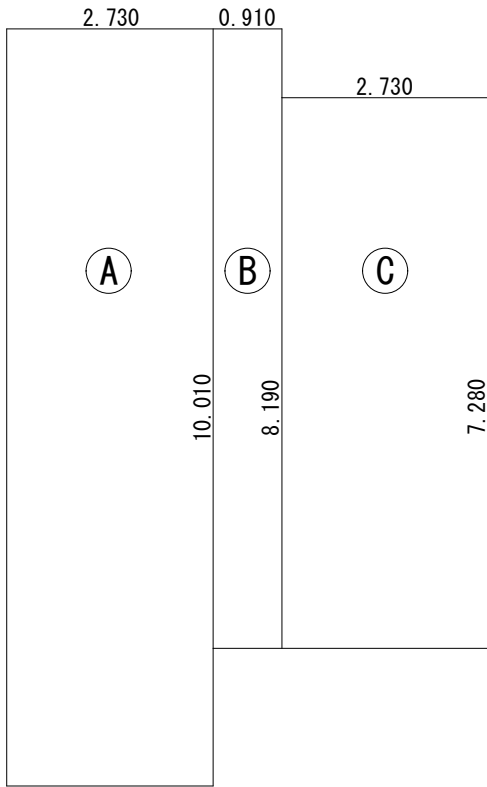

建築面積求積図 S=1/100

建築面積求積表


番号	計算式	(m)	面積 (㎡)
㊦	2.730 × 10.010		27.3273
㊧	0.910 × 8.190		7.4529
㊨	2.730 × 7.280		19.8744
合計			54.6546 54.65 (16.5坪)

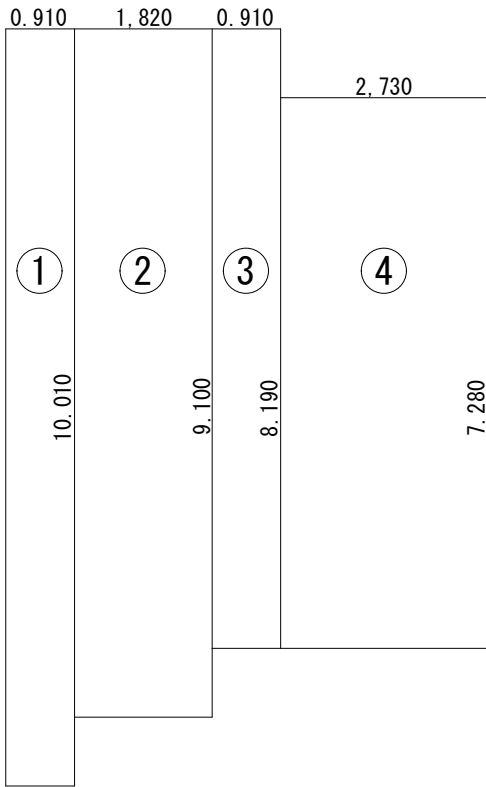

1階床面積図 S=1/100

1階床面積求積表

番号	計算式	(m)	面積 (㎡)
①	0.910 × 10.010		9.1091
②	1.820 × 9.100		16.5620
③	0.910 × 8.190		7.4529
④	2.730 × 7.280		19.8744
合計			52.9984 52.99 (16.0坪)

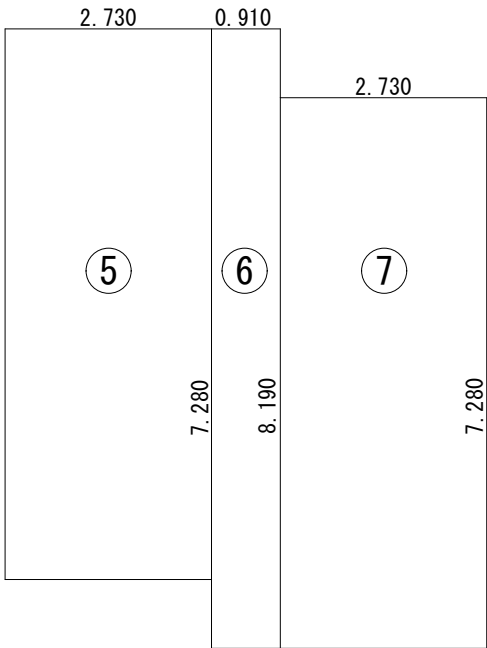

2階床面積図 S=1/100

2階床面積求積表

番号	計算式	(m)	面積 (㎡)
⑤	2.730 × 7.280		19.8744
⑥	0.910 × 8.190		7.4529
⑦	2.730 × 7.280		19.8744
合計			47.2017 47.20 (14.2坪)

延べ床面積表

	番号	(m)	面積 (㎡)
1階床面積	① ② ③ ④		52.99
2階床面積	⑤ ⑥ ⑦		47.20
合計			100.20 (30.3坪)

決定図

G1

壁付け 住宅用火災報知器			数量
H	熱感知器	電池式(単独型)	1
	熱感知器	露出型	
壁付け 住宅用火災報知器			数量
S	煙感知器	電池式(単独型)	
	煙感知器	露出型	

※ 煙感知器は壁・梁より600mm以上離す
壁に取付ける場合、
天井から150mm以上500mm以内離す
換気扇・エアコン吹出口から1500mm以上離す
※ 全室LED照明とする。
※ 標準天井高さ2,400
※ 特記無きガラスは型ガラス

* 凡例

- 管柱 (105×105)
- Kタ'ンパ' (3.30倍 FRM-0641)
- 片筋違い (2.00倍 45×90)
(例 左:柱脚 右:柱頭)
- たすき掛筋違い (4.00倍 45×90)
- 構造用合板 (2.70倍)
(t=9 9材 -EXハイパ-)
- 床点検口
- 天井点検口
- 換気扇
- 熱交換換気扇VLR-70

決定図

※照明設備：全ての照明設備機器において全てLED照明を使用している

訂正	浜岡一級総合設計事務所 一級建築士事務所 静岡県知事登録第 (10)2441 号 一級建築士 大臣登録第 365879 号 西原利昌	PG HOUSE ピージーハウス	株式会社 LIFEFUND InDesign office 一級建築士事務所 事務所登録 (2) 第7595号 一級建築士登録 第179770号 鈴木 達男 〒432-8023 静岡県浜松市中央区鴨江3丁目70番23号	年月日 2025. 8. 30	件名 太田悠斗様邸 新築工事	設計 酒井	IC	工事 青島	図番 3-1
				縮尺 1/50	図名 1階平面図				

G1

壁付け 住宅用火災報知器			数量
[H] 熱感知	熱感知器	電池式(単独型)	
	露出型		
壁付け 住宅用火災報知器			数量
[S] 煙感知	煙感知器	電池式(単独型)	4
	露出型		

※ 煙感知器は壁・梁より600mm以上離す
壁に取付ける場合、
天井から150mm以上500mm以内離す
換気扇・エアコン吹出口から1500mm以上離す
※ 全室LED照明とする。
※ 標準天井高さ2,400
※ 特記無きガラスは型ガラス

* 凡例

- 管柱 (105×105)
- Kダクト (3.30倍 FRM-0641)
- 片筋違い (2.00倍 45×90)
(例 左:柱脚 右:柱頭)
- たすき掛筋違い (4.00倍 45×90)
- 構造用合板 (2.70倍)
(t=9 材種-EXハイバ-)
- 床点検口
- 天井点検口
- 換気扇
- 熱交換換気扇VLR-70


アドバンスシリーズ

スマートデザイン (外部)

- 凡例
- 1 コンセント 1ヶロ
- 2 コンセント 2ヶロ
- 3 コンセント 3ヶロ
- 1ET コンセント1ヶロ接地ターミナル付
- 2ET コンセント2ヶロ接地ターミナル付
- WP コンセント 防水型
- エアコン用コンセント
- 200V用コンセント
- WP 防雨入線プレート
- スイッチ
- 3 3路スイッチ
- 4 4路スイッチ
- 直接電源
- TV テレビ取出口
- TEL 電話取出口 (テレホンガイド)
- LAN LAN取出口 (テレホンガイド)
- 壁照明
- リモコン (給湯関係・ルフロ)
- メーター
- 分電盤
- チャイム

※ACコンセント天井付け
※TVアンテナ工事
※スイッチはFL+1100、コンセントはFL+200



決定図

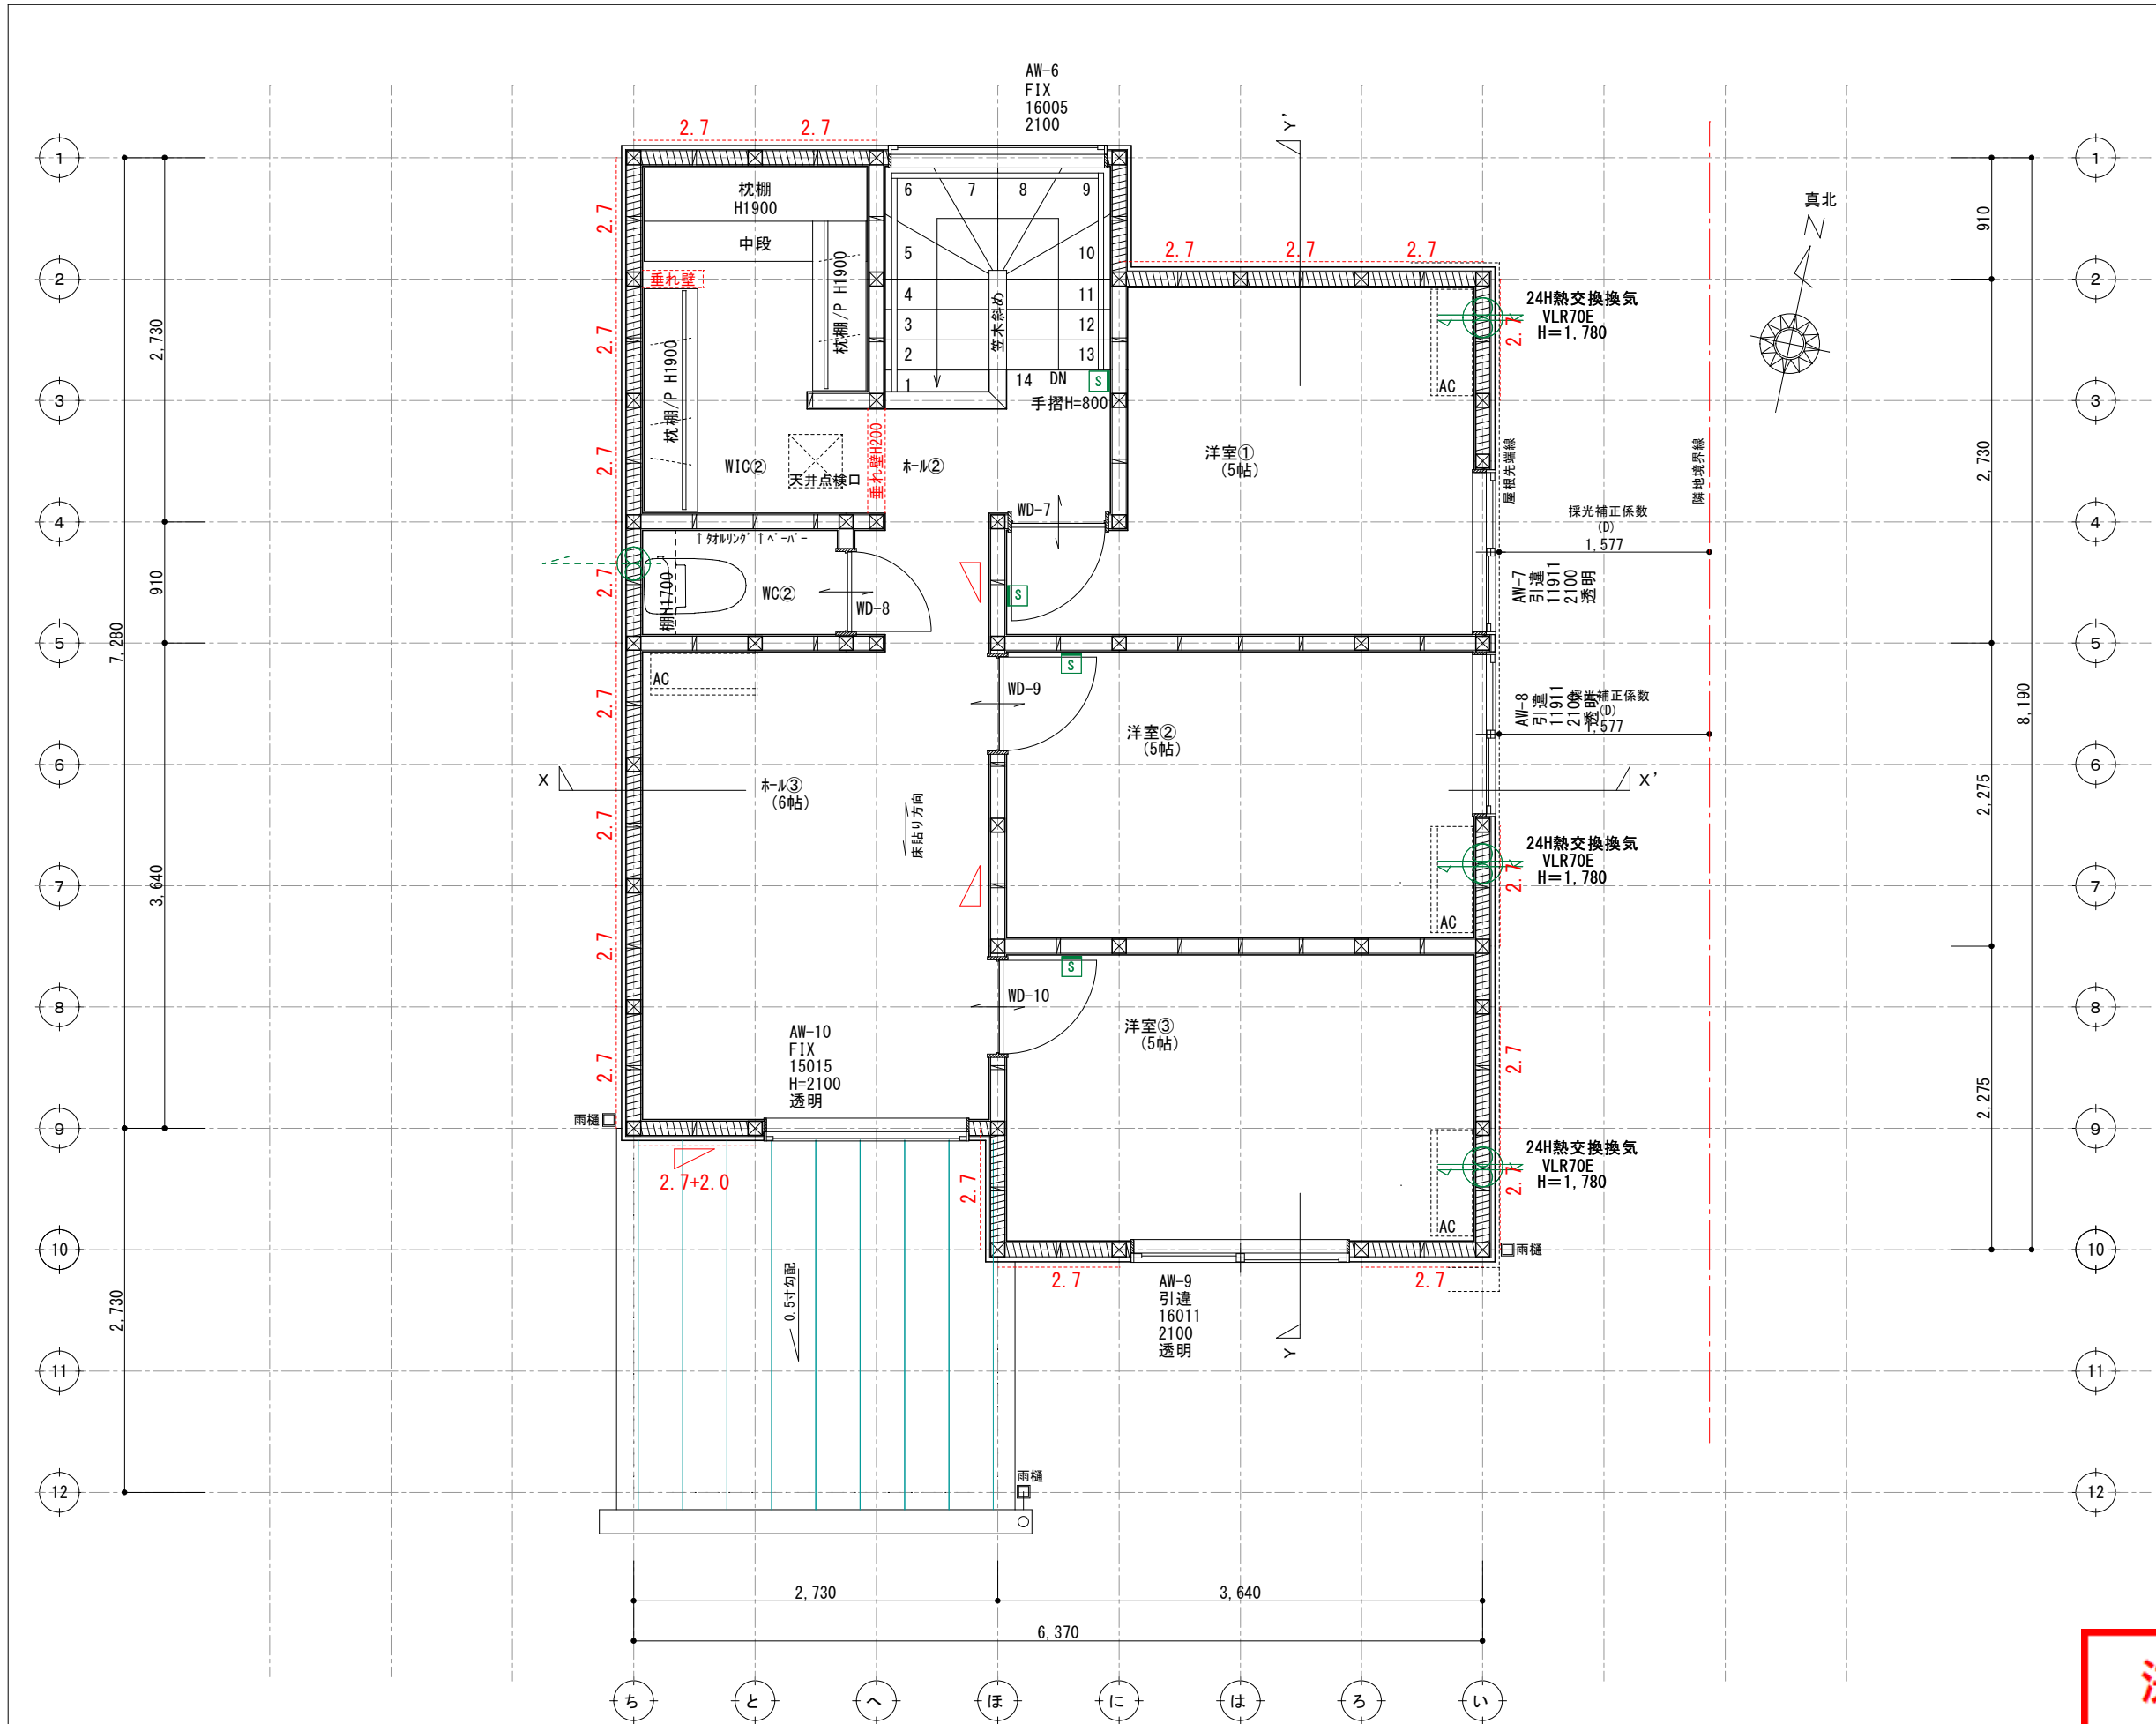

太陽光あり



訂 正	浜 岡 一 級 総 合 設 計 事 務 所 一級建築士事務所 静岡県知事登録第 (10)2441 号 一級建築士 大臣登録第 365879 号 西原利昌	 PG HOUSE ピーjee-ハウス	株式会社 LIFEFUND InDesign office 一級建築士事務所 事務所登録 (2) 第7595号 一級建築士登録 第179770号 鈴木 達男 〒432-8023 静岡県浜松市中央区鴨江3丁目70番23号	年 月 日	件 名		設計	IC	工事	図 番
2025. 8. 30				太田悠斗様邸 新築工事						
縮 尺				図 名						
1/100		屋根伏図		酒井		青島	3-3			

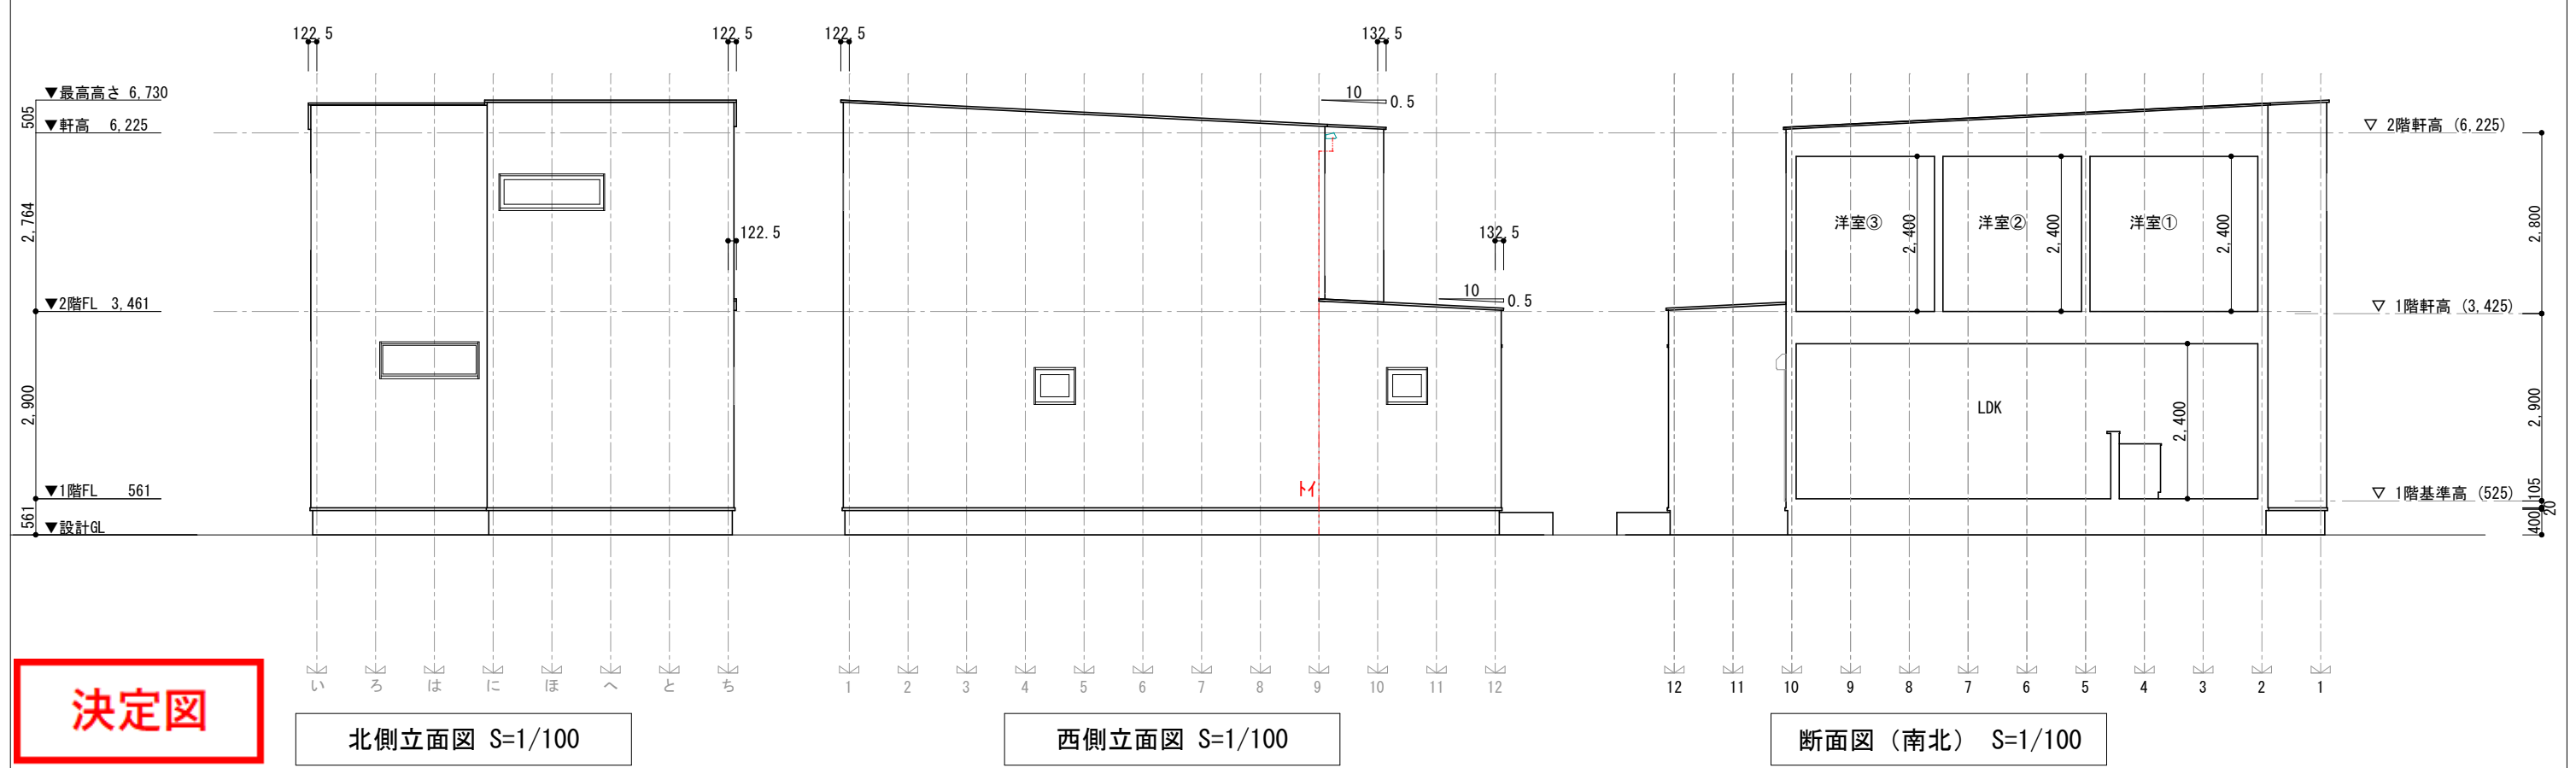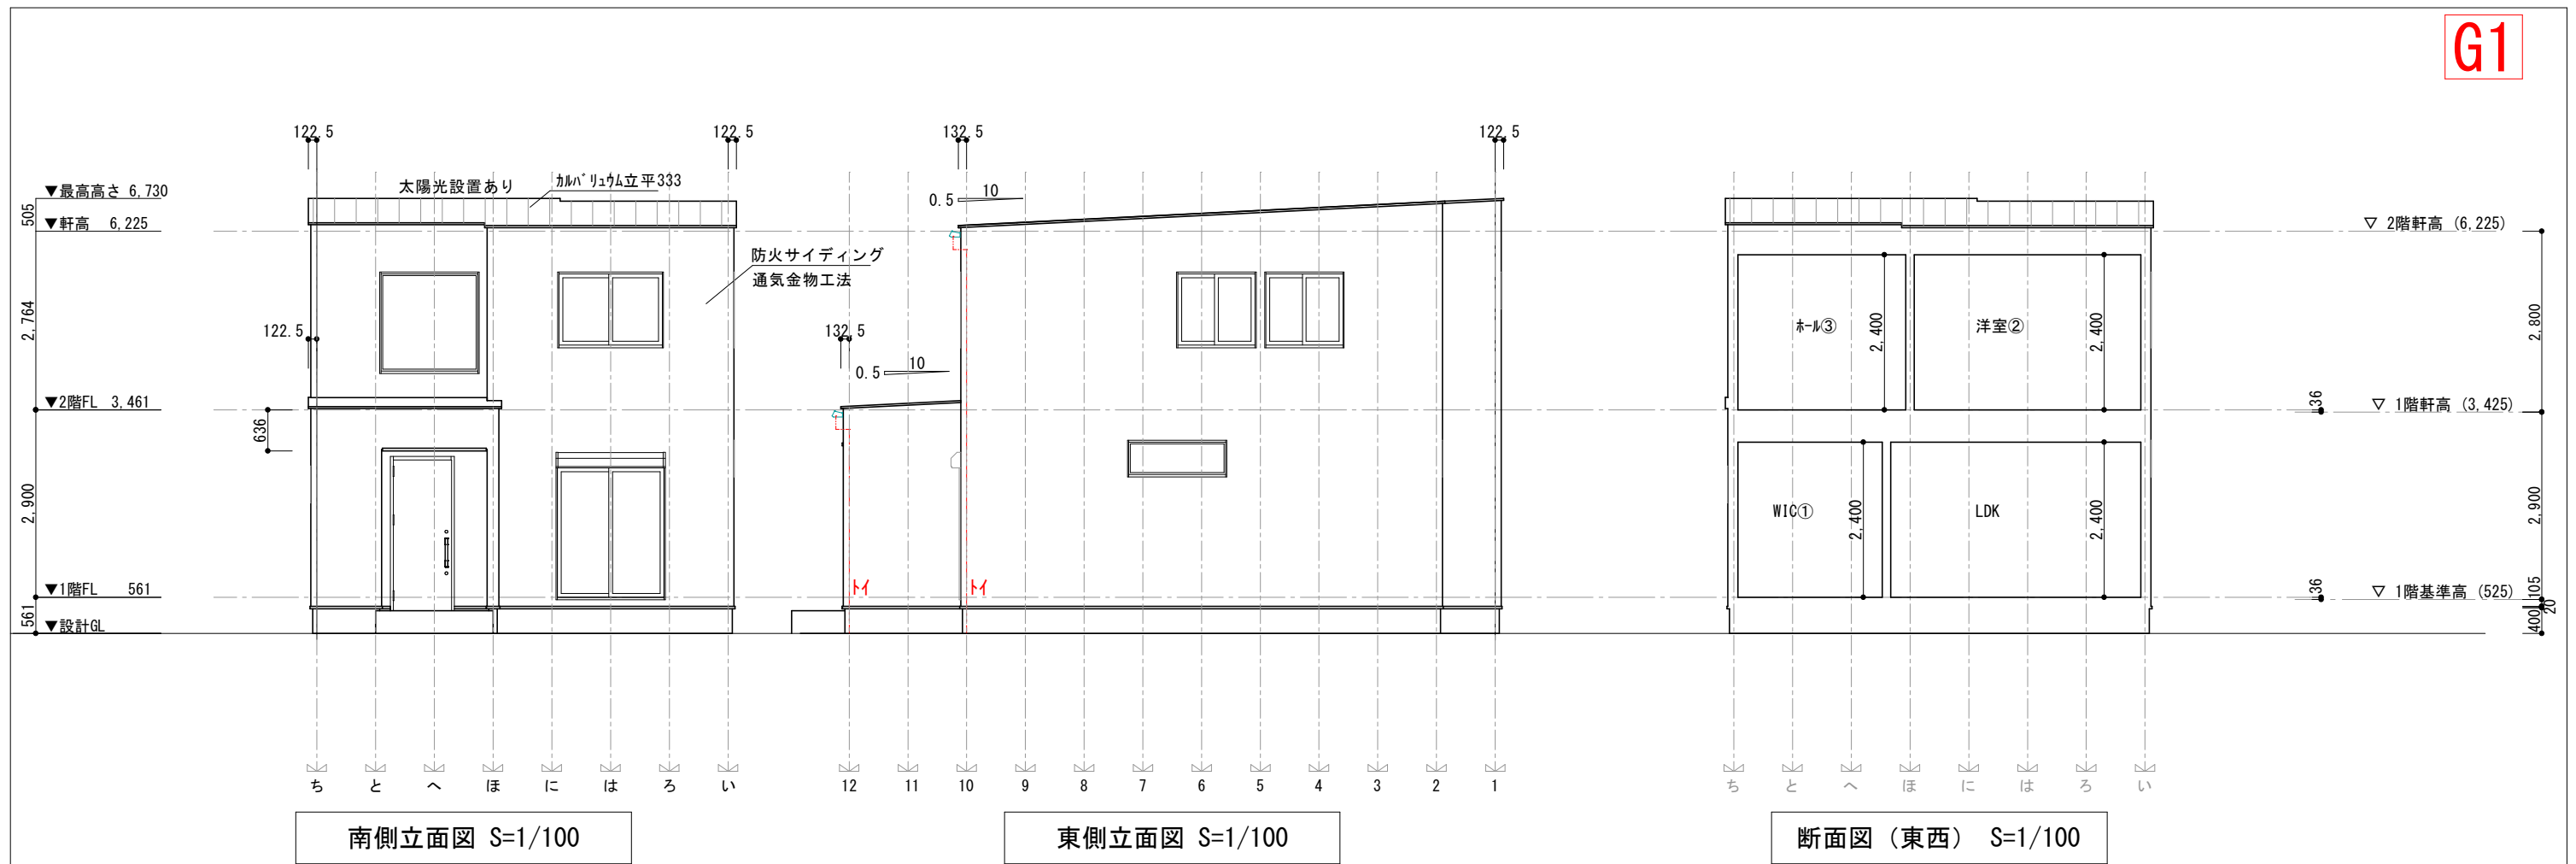


決定図

訂正	浜岡一級総合設計事務所 一級建築士事務所 静岡県知事登録第 (10)2441 号 一級建築士 大臣登録第 365879 号 西原利昌	PG HOUSE ピージーハウス	株式会社 LIFEFUND InDesign office 一級建築士事務所 事務所登録 (2) 第7595号 一級建築士登録 第179770号 鈴木 達男 〒432-8023 静岡県浜松市中央区鴨江3丁目70番23号	年月日 2025. 8. 30 縮尺 1/100	件名 太田悠斗様邸 新築工事 図名 立面図	設計 酒井	IC	工事 青島	図番 4
----	--	---------------------	---	-----------------------------------	--------------------------------	----------	----	----------	---------


太陽光パネル有

G 1

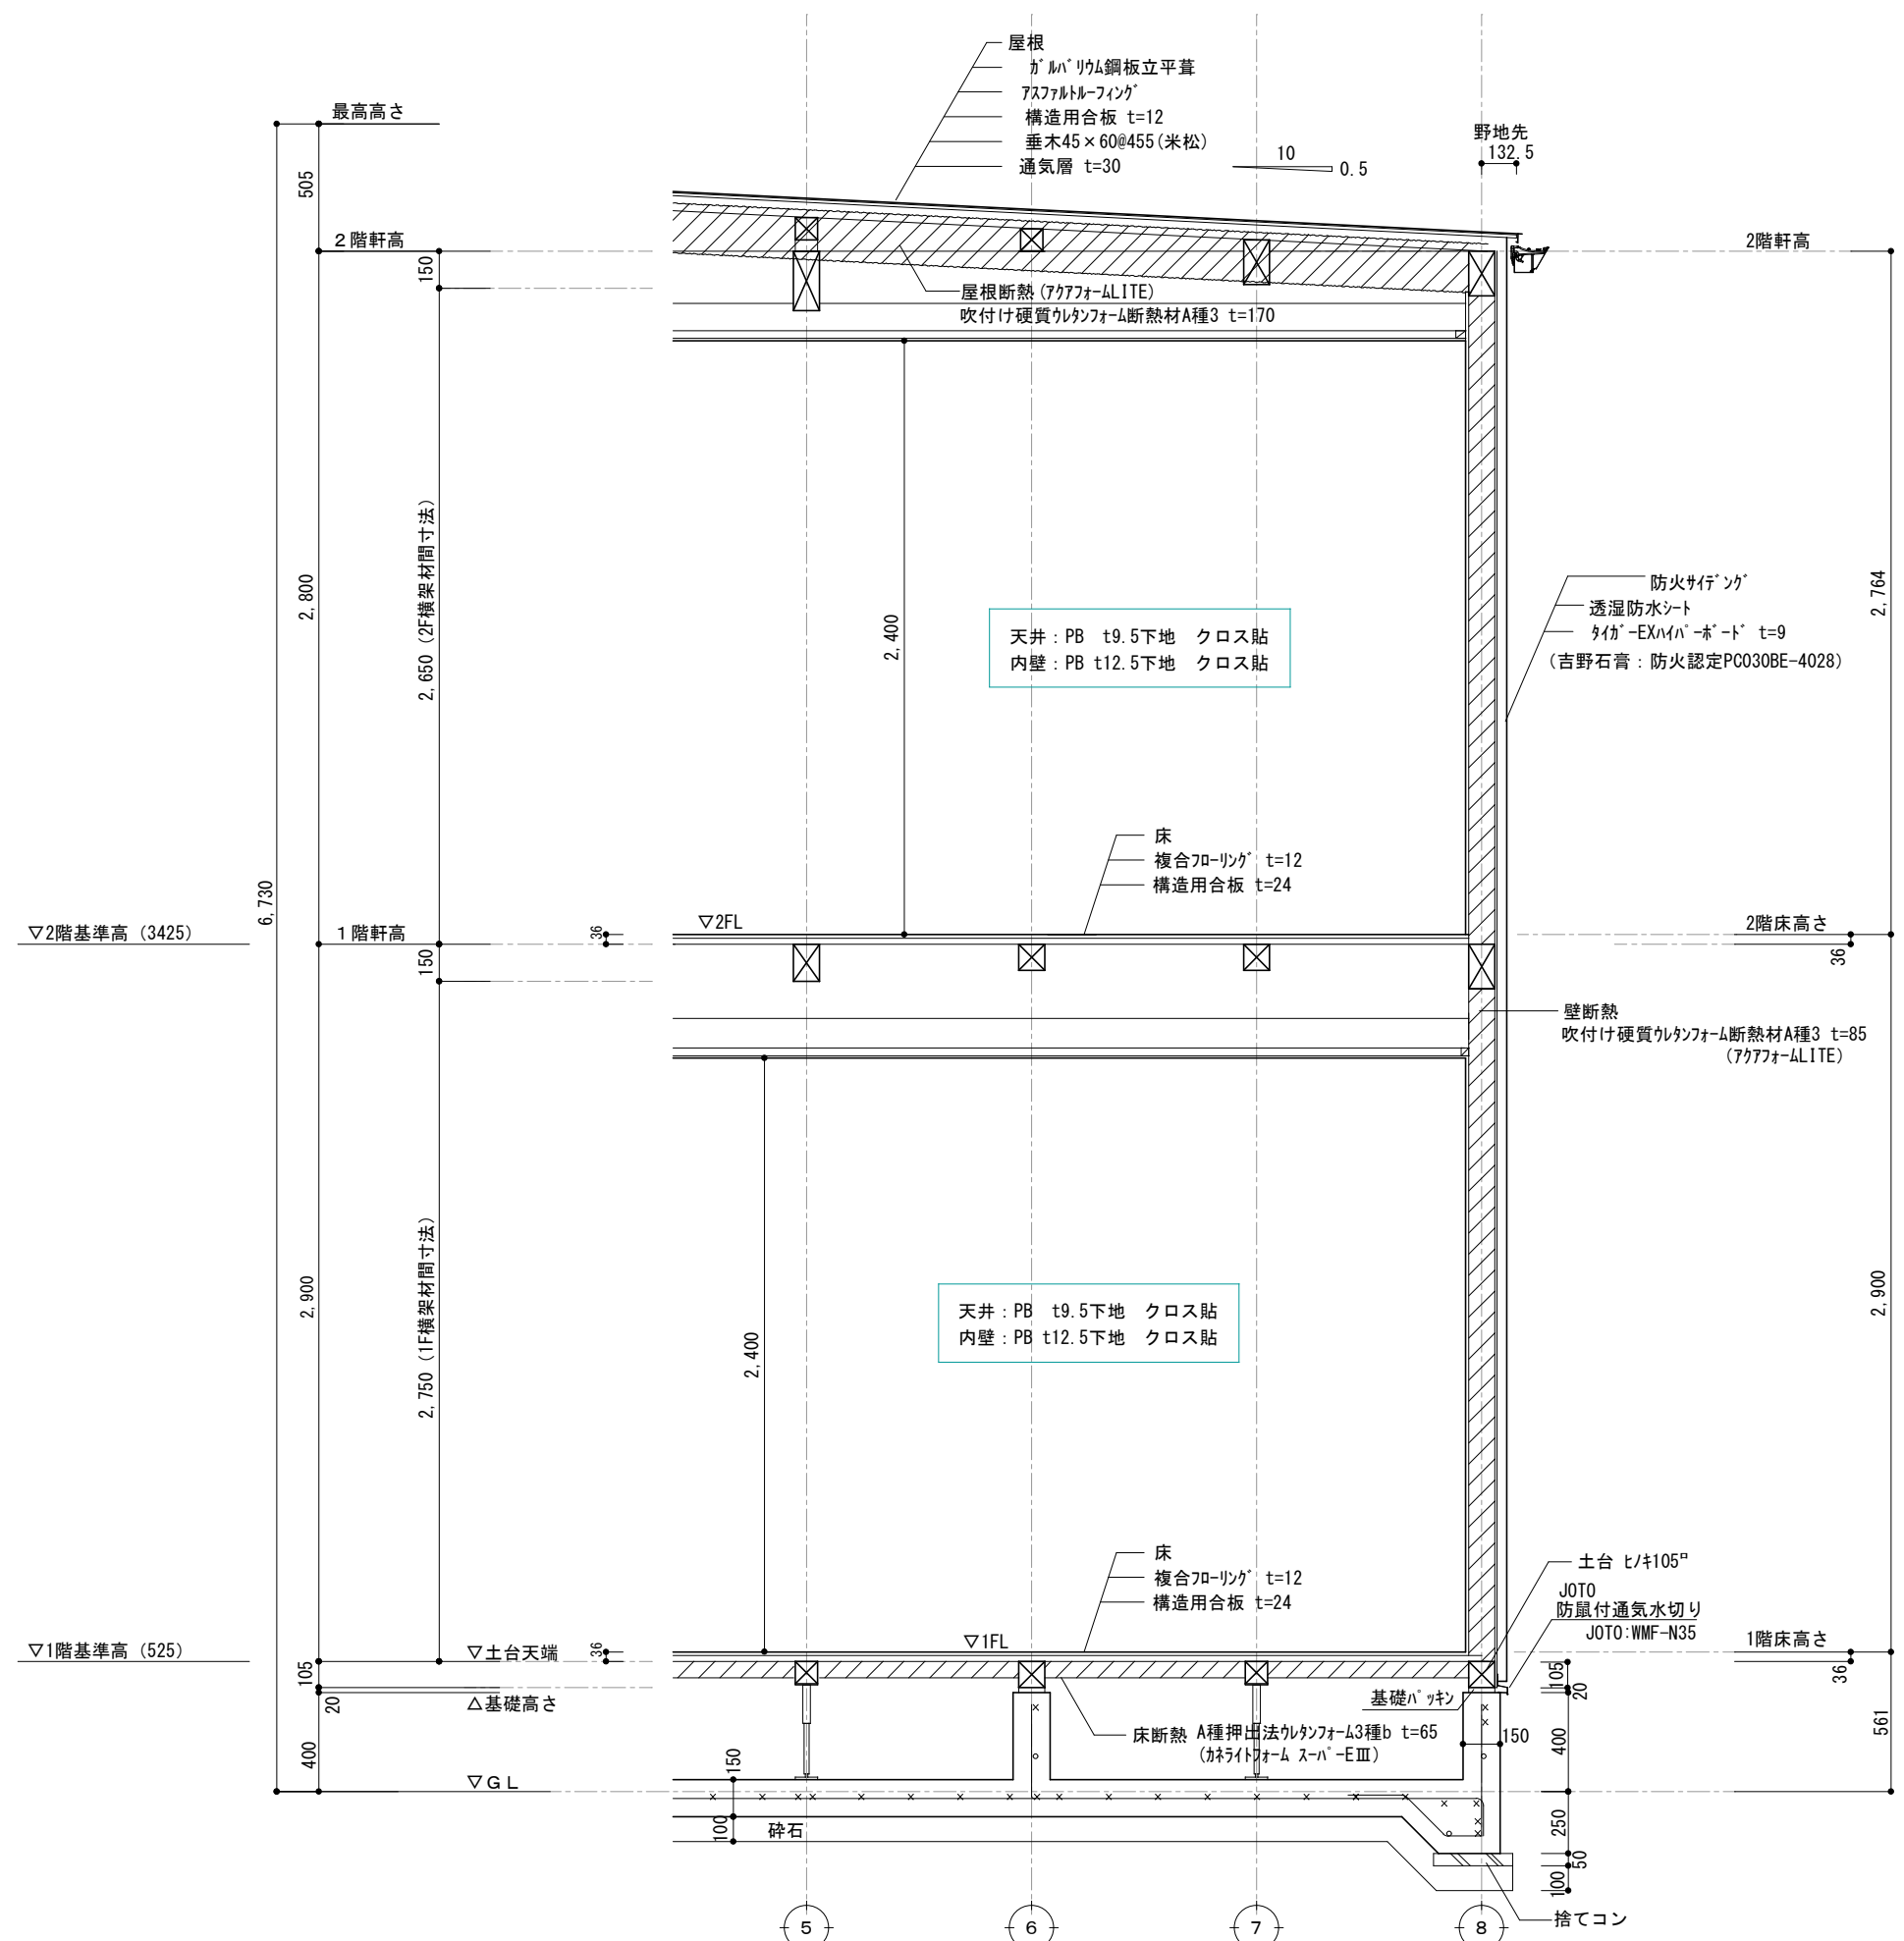


決定図


訂 正	浜 岡 一 級 総 合 設 計 事 務 所 一級建築士事務所 静岡県知事登録第 (10) 2441 号 一級建築士 大臣登録第 365879 号 西原利昌		株式会社 LIFEFUND InDesign office 一級建築士事務所 事務所登録 (2) 第7595号 一級建築士登録 第179770号 鈴木 達男 〒432-8023 静岡県浜松市中央区鴨江3丁目70番23号	年 月 日	件 名		設計	IC	工事	図 番
				2025. 8. 30	太田悠斗様 邸新築工事					
				縮 尺	図 名					
				1/30	矩計図		酒井		青島	A-5

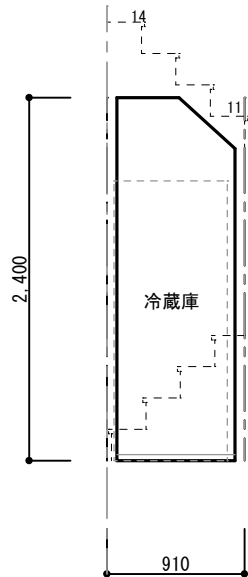


パントリー 西面

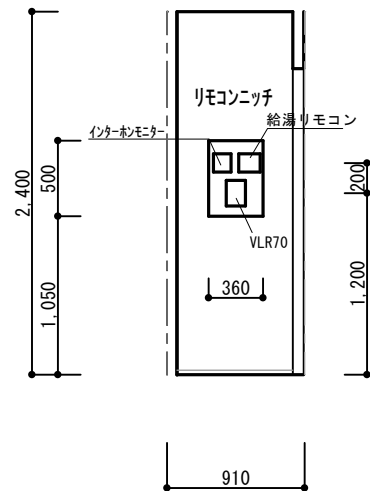

LDK 南面

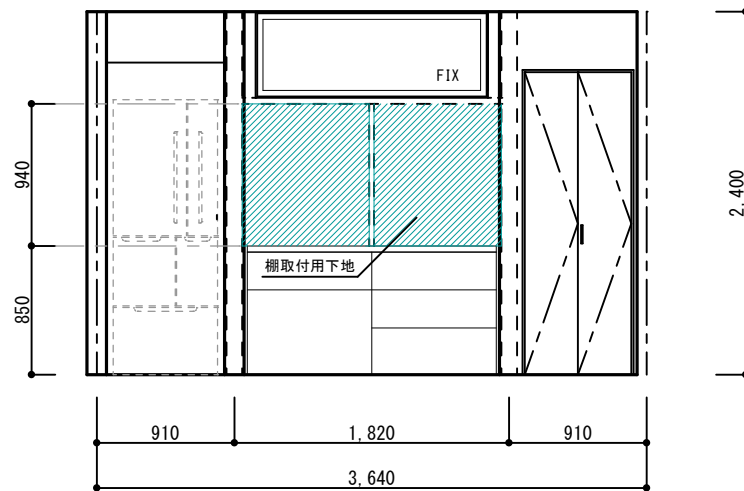

キッチン 北面

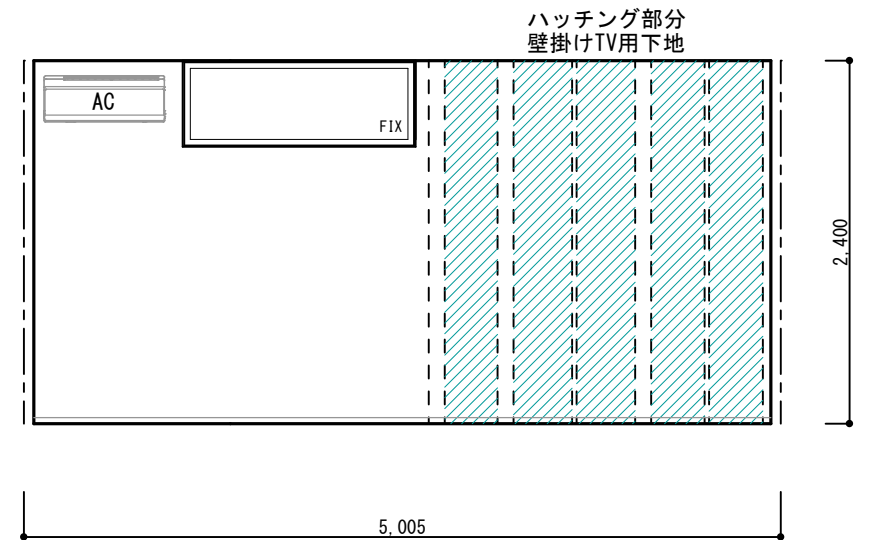

LDK 東面

決定図

訂正	浜岡一級総合設計事務所 一級建築士事務所 静岡県知事登録第 (10)2441 号 一級建築士 大臣登録第 365879 号 西原利昌	LIFEFUND PG HOUSE	株式会社 LIFEFUND InDesign office 一級建築士事務所 事務所登録 (2) 第7595号 一級建築士登録 第179770号 鈴木 達男 〒432-8023 静岡県浜松市中央区鴨江3丁目70番23号	年月日 2025.8.30	件名 太田悠斗様 新築工事		設計	IC	工事	図番
				縮尺 1/50	図名 展開図-1		酒井		青島	6-1

G1

壁付け 住宅用火災報知器			数量
H 熱感知	熱感知器	電池式(単独型)	1
		露出型	

壁付け 住宅用火災報知器			数量
S 煙感知	煙感知器	電池式(単独型)	
		露出型	

※ 煙感知器は壁・梁より600mm以上離す
壁に取付ける場合、
天井から150mm以上500mm以内離す
換気扇・エアコン吹出口から1500mm以上離す
※ 全室LED照明とする。
※ 標準天井高さ2,400
※ 特記無きガラスは型ガラス

* 凡例


- ☒ 管柱 (105×105)
- ◀▶ Kダクト (3.30倍 FRM-0641)
- △ 片筋違い (2.00倍 45×90)
(例 左:柱脚 右:柱頭)
- ⊠ たすき掛筋違い (4.00倍 45×90)
- 構造用合板 (2.70倍)
(t=9 9材 EXハイバ)
- ◻ 床点検口
- ⊠ 天井点検口
- ⊗ 換気扇
- ⊗ 熱交換換気扇VLR-70

アドバンスシリーズ	
スマートデザイン (外部)	
凡例	
①	コンセント 1ヶロ
②	コンセント 2ヶロ
③	コンセント 3ヶロ
①ET	コンセント1ヶロ接地ターミナル付
②ET	コンセント2ヶロ接地ターミナル付
WP	コンセント 防水型
⊗	エアコン用コンセント
⊗	200V用コンセント
WP	防雨入線プレート
⊗	スイッチ
③	3路スイッチ
④	4路スイッチ
⊗	直結電源
⊗TV	テレビ取出口
⊗TEL	電話取出口 (テレホンガイド)
⊗LAN	LAN取出口 (テレホンガイド)
⊗	壁照明
⊗	リモコン (給湯関係・ルフロ)
⊗	メーター
⊗	分電盤
⊗	チャイム

※ACコンセント天井付け
※TVアンテナ工事
※スイッチはFL+1100、コンセントはFL+200

決定図

※照明設備：全ての照明設備機器において全てLED照明を使用している

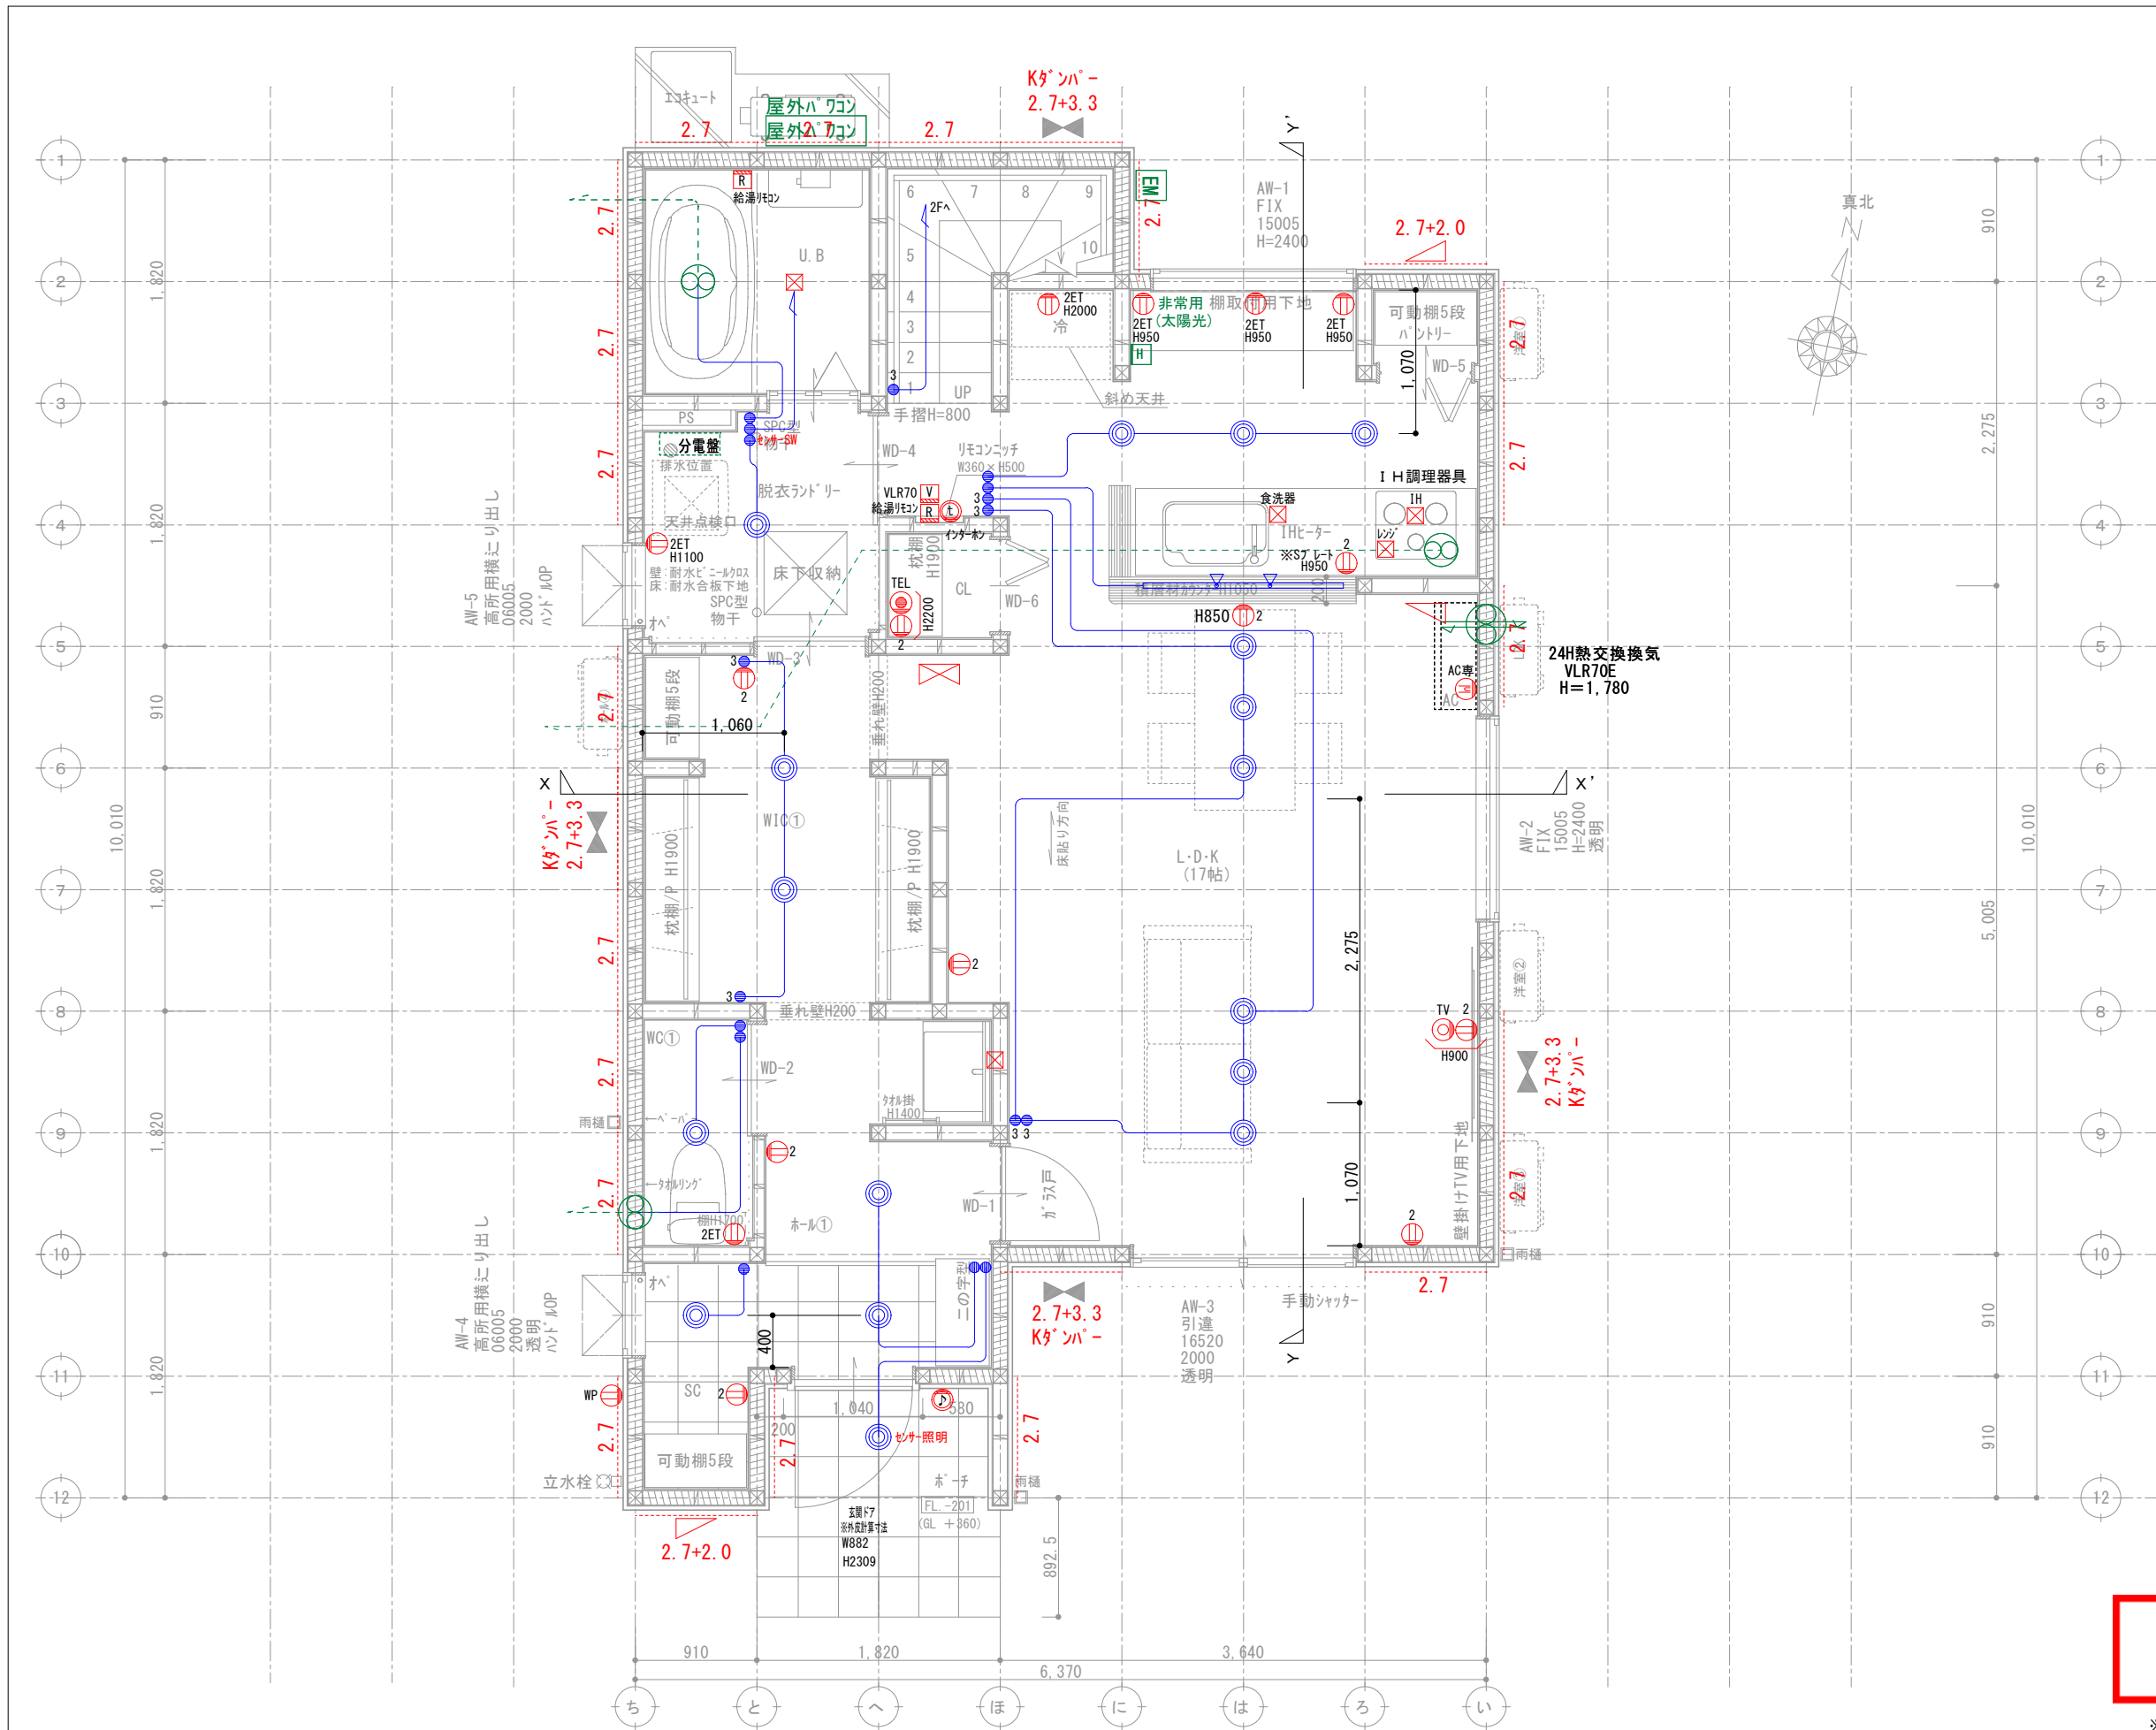

G1

壁付け 住宅用火災報知器			数量
H 熱感知	熱感知器	電池式(単独型)	
	露出型		
壁付け 住宅用火災報知器			数量
S 煙感知	煙感知器	電池式(単独型)	4
	露出型		

※ 煙感知器は壁・梁より600mm以上離す
壁に取付ける場合、
天井から150mm以上500mm以内離す
換気扇・エアコン吹出口から1500mm以上離す
※ 全室LED照明とする。
※ 標準天井高さ2,400
※ 特記無きガラスは型ガラス


* 凡例


- ☒ 管柱 (105×105)
- ◀▶ Kダクト (3.30倍 FRM-0641)
- △ 片筋違い (2.00倍 45×90)
(例 左:柱脚 右:柱頭)
- ◻ たすき掛筋違い (4.00倍 45×90)
- 構造用合板 (2.70倍)
(t=9 3イタ EXハイバ)
- ◻ 床点検口
- ◻ 天井点検口
- ↻ 換気扇
- ↻ 熱交換換気扇VLR-70

アドバンスシリーズ	
スマートデザイン (外部)	
凡例	
1	コンセント 1ヶロ
2	コンセント 2ヶロ
3	コンセント 3ヶロ
1ET	コンセント1ヶロ接地ターミナル付
2ET	コンセント2ヶロ接地ターミナル付
WP	コンセント 防水型
	エアコン用コンセント
	200V用コンセント
WP	防雨入線プレート
	スイッチ
3	3路スイッチ
4	4路スイッチ
	直結電源
TV	テレビ取出口
TEL	電話取出口 (テレホンガイド)
LAN	LAN取出口 (テレホンガイド)
	壁照明
R	リモコン (給湯関係・ルフロ)
WH	メーター
t	分電盤
チ	チャイム


※ACコンセント天井付け
※TVアンテナ工事
※スイッチはFL+1100、コンセントはFL+200

決定図

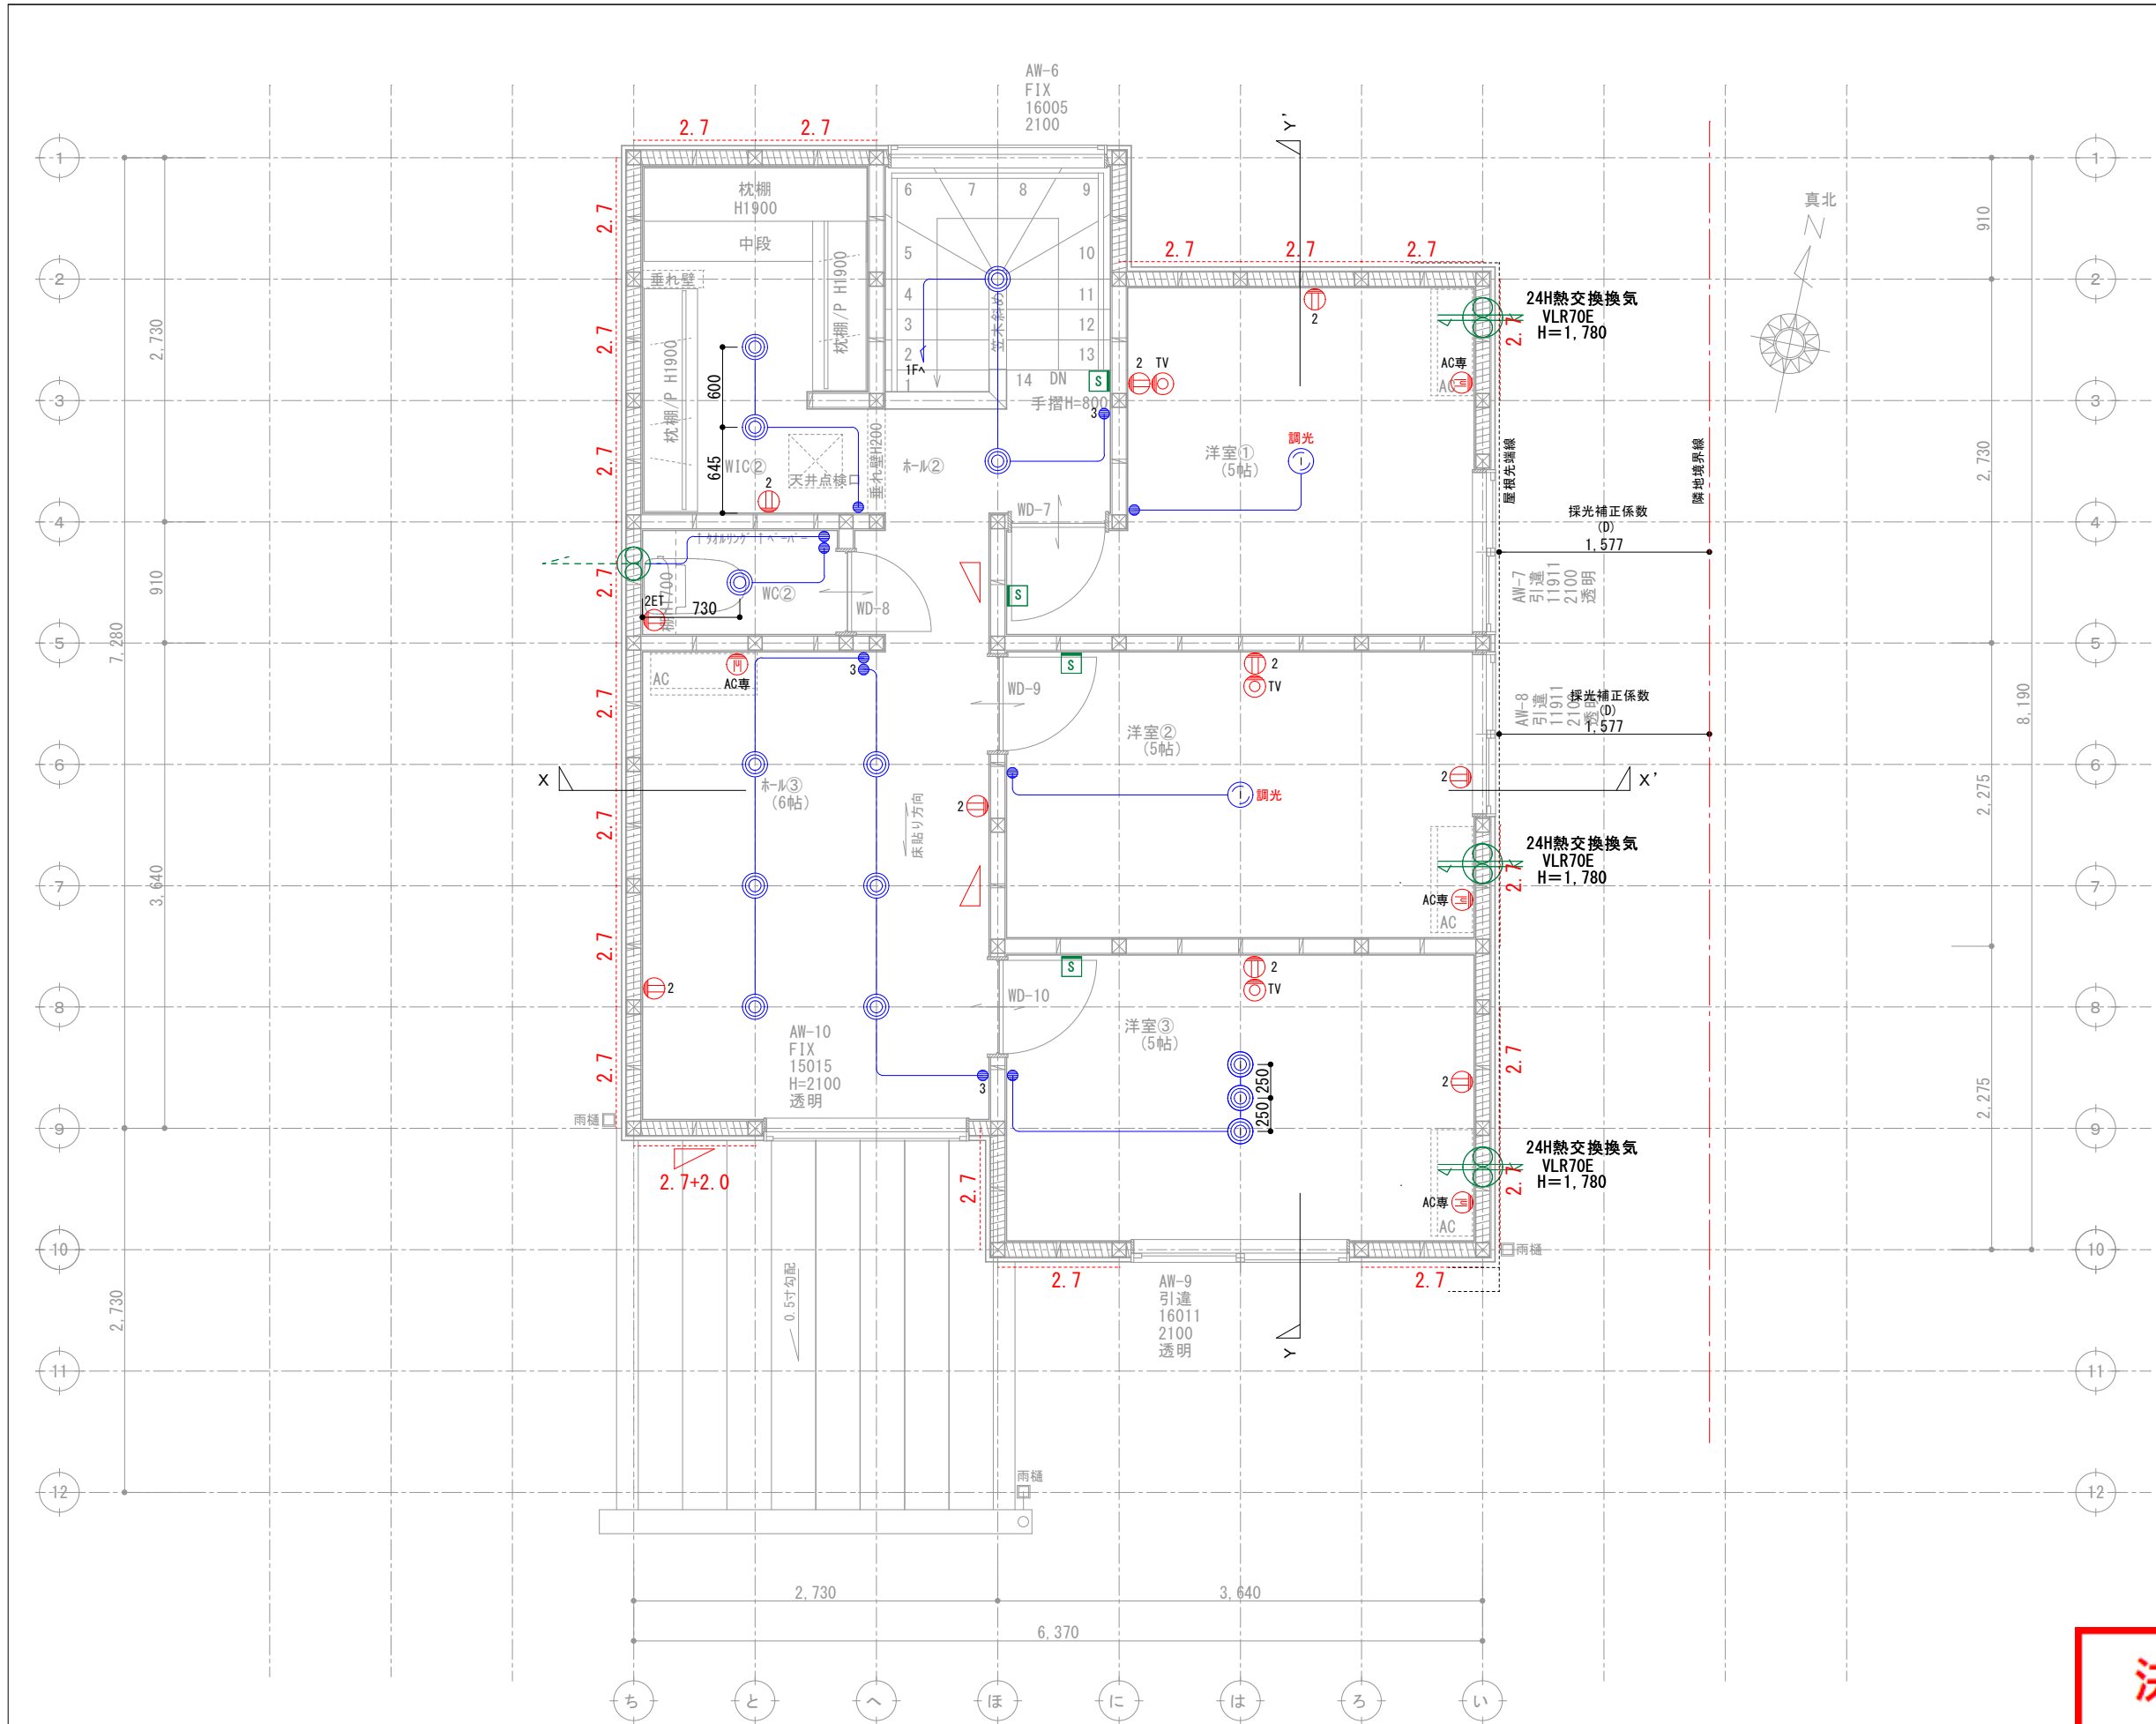

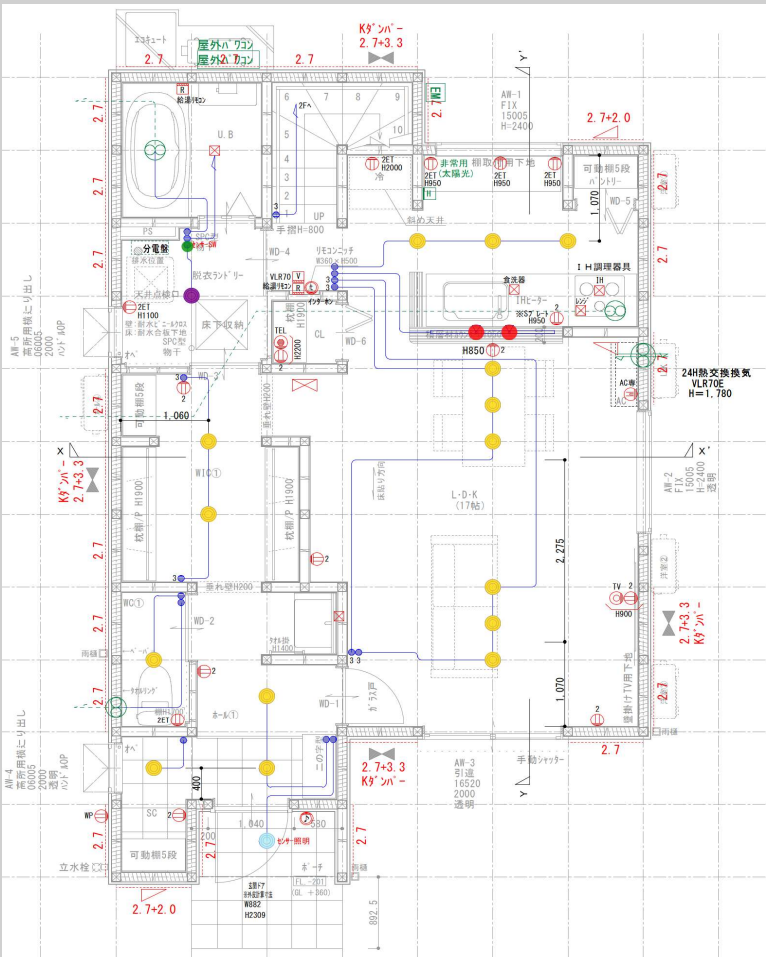

1階

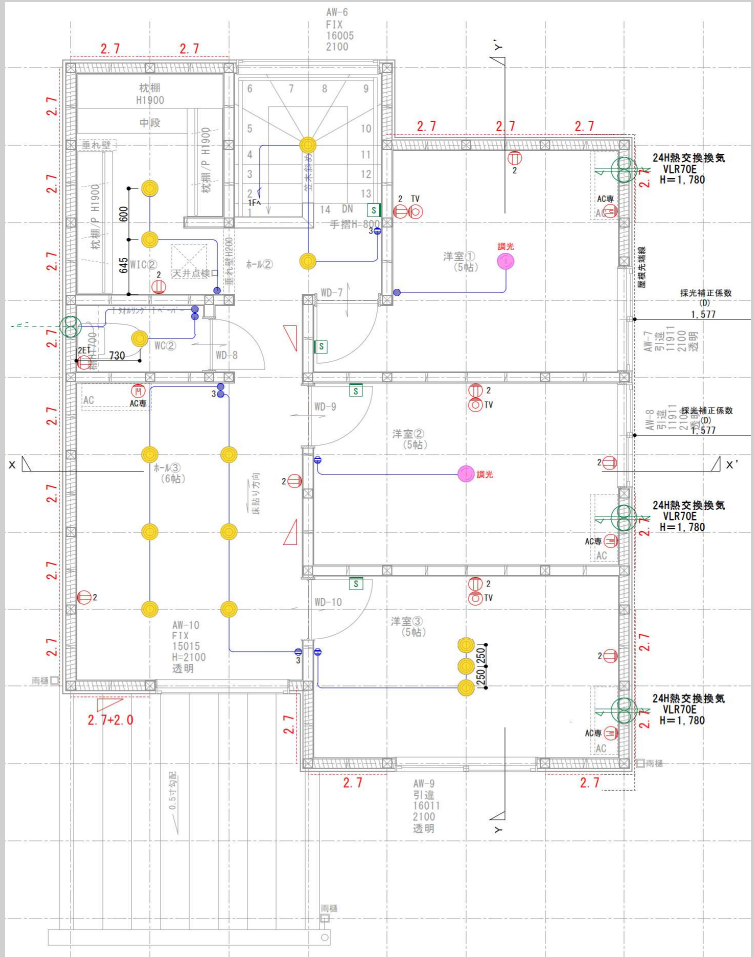

2階

ドアホン：VL-SE31XL
(Panasonic)



内部SW：アドバンス
マットホワイト



ポーチ灯

● × 1

センサー付きダウライト

DDL_4497YB

基本照明ダウライト

● × 29

DDL_6102YW

● × 1

ダウライト

DDL_6102AW

● × 5

シーリングライト

DCL_40507

● × 1

レール照明

DP_02915W

● × 1

センサーSW

WTA_14119W



高気密S₈形 | 人感センサー | 連動ON/OFFタイプII

DDL-4497 YB
電球色 / 2700K・Ra83

定格光束 消費電力 照度センサー消費電力
425lm 7.7W 55.1lm/W

¥18,800-(税抜) (LED内蔵)

LED 7.7W
白熱灯60W相当

- アルミダイカスト 黒塗装
- アクリル 乳白(マット)
- 径φ111 埋込穴φ100 埋込深80mm 0.5kg
- 14VA
- 点灯角度調節機能付(暗・明・切)
- 点灯保持時間(1分3分)
- ※8hタイマー設定時1分固定
- 低照度センサー付
- AC100V
- 光源寿命50,000時間
- 取付可能天井厚5~25mm
- 調光器併用不可
- 【調光器別について】
LED60VAまで
電球形蛍光灯
10W形・15W形・25W形3灯まで
蛍光灯インバータイプ60Wまで
白熱灯60Wまで

非調光
60°
0.1m
照度範囲
80
LED内蔵
不可
防雨形
温度保護
機能付
強制
ON
埋込穴
100



COBタイプ | 高気密S₈形

DDL-6102 YW
電球色 / 2700K・Ra83

定格光束 消費電力 照度センサー消費電力
440lm 4.6W 95.6lm/W

¥3,600-(税抜) (LED内蔵)

LED 4.6W
白熱灯60W相当

- 銅板 白塗装
- アクリル 乳白(マット)
- 径φ116 埋込穴φ100 埋込深70mm 0.3kg
- 5VA
- 広配光(ベール付)
- AC100V
- 光源寿命60,000時間
- 取付可能天井厚5~25mm
- 調光器併用不可

LED内蔵
不可
防雨形
温度保護
機能付
埋込穴
100
70
55°
準耐火



COBタイプ | 高気密S₈形

DDL-6102 AW
温白色 / 3500K・Ra83

定格光束 消費電力 照度センサー消費電力
470lm 4.6W 102.1lm/W

¥3,600-(税抜) (LED内蔵)

LED 4.6W
白熱灯60W相当

- 銅板 白塗装
- アクリル 乳白(マット)
- 径φ116 埋込穴φ100 埋込深70mm 0.3kg
- 5VA
- 広配光(ベール付)
- AC100V
- 光源寿命60,000時間
- 取付可能天井厚5~25mm
- 調光器併用不可

LED内蔵
不可
防雨形
温度保護
機能付
埋込穴
100
70
55°
準耐火



タイマー付リモコン付レス | 調色調光タイプ

DCL-40507
昼光色 / 6500K・Ra83 ~ 電球色 / 2700K・Ra83

LED 29.5W
消費電力 3699lm 29.5W 125.3lm/W

¥22,000-(税抜) (LED内蔵)

- アクリル 乳白(マット)
- 径φ110 高さ129mm 1.0kg
- アルミスリット付(全灯・半灯・点灯・電燈灯)
- ※調光器の調色調光対応
- 調光機能付(50%~100%)
- 充電式リチウム電池
- AC100V
- 光源寿命40,000時間
- 消費電力省エネ設計
- 調光器併用不可
- シーンコントロールは使用できません。

クリック操作式
カラー温度調整
55°

調色調光タイプ
可能
DP-40091
可能
DP-40638



フィードインボックス・エンドキャップセット

ダクトレール1.5m用
DP-02915 W
¥8,800(税抜)

- アルミ型材 白アルマイト
- ※33 ダクト長1500 全長1603 高19mm
- 2P 15A 125V
- フィードインボックス・エンドキャップ1個付



3線 / 4線式

WTA14119W


壁取付 熱線センサー付自動スイッチ(銀器)
(検知後連続動作時間 約10秒~30分可変形)
(明るさセンサー・手動スイッチ付) (マットホワイト)

3A 100V AC

プレート別売

照明器具
施主支給

外部：スマートデザインシリーズ
ブラック

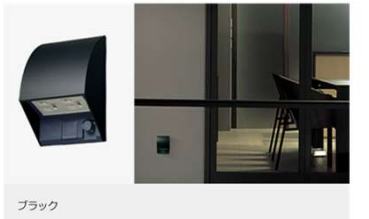

決定図


PG House

太田悠斗様 邸新築工事

Lighting Plan

2025.08.30

(図面 7-3)

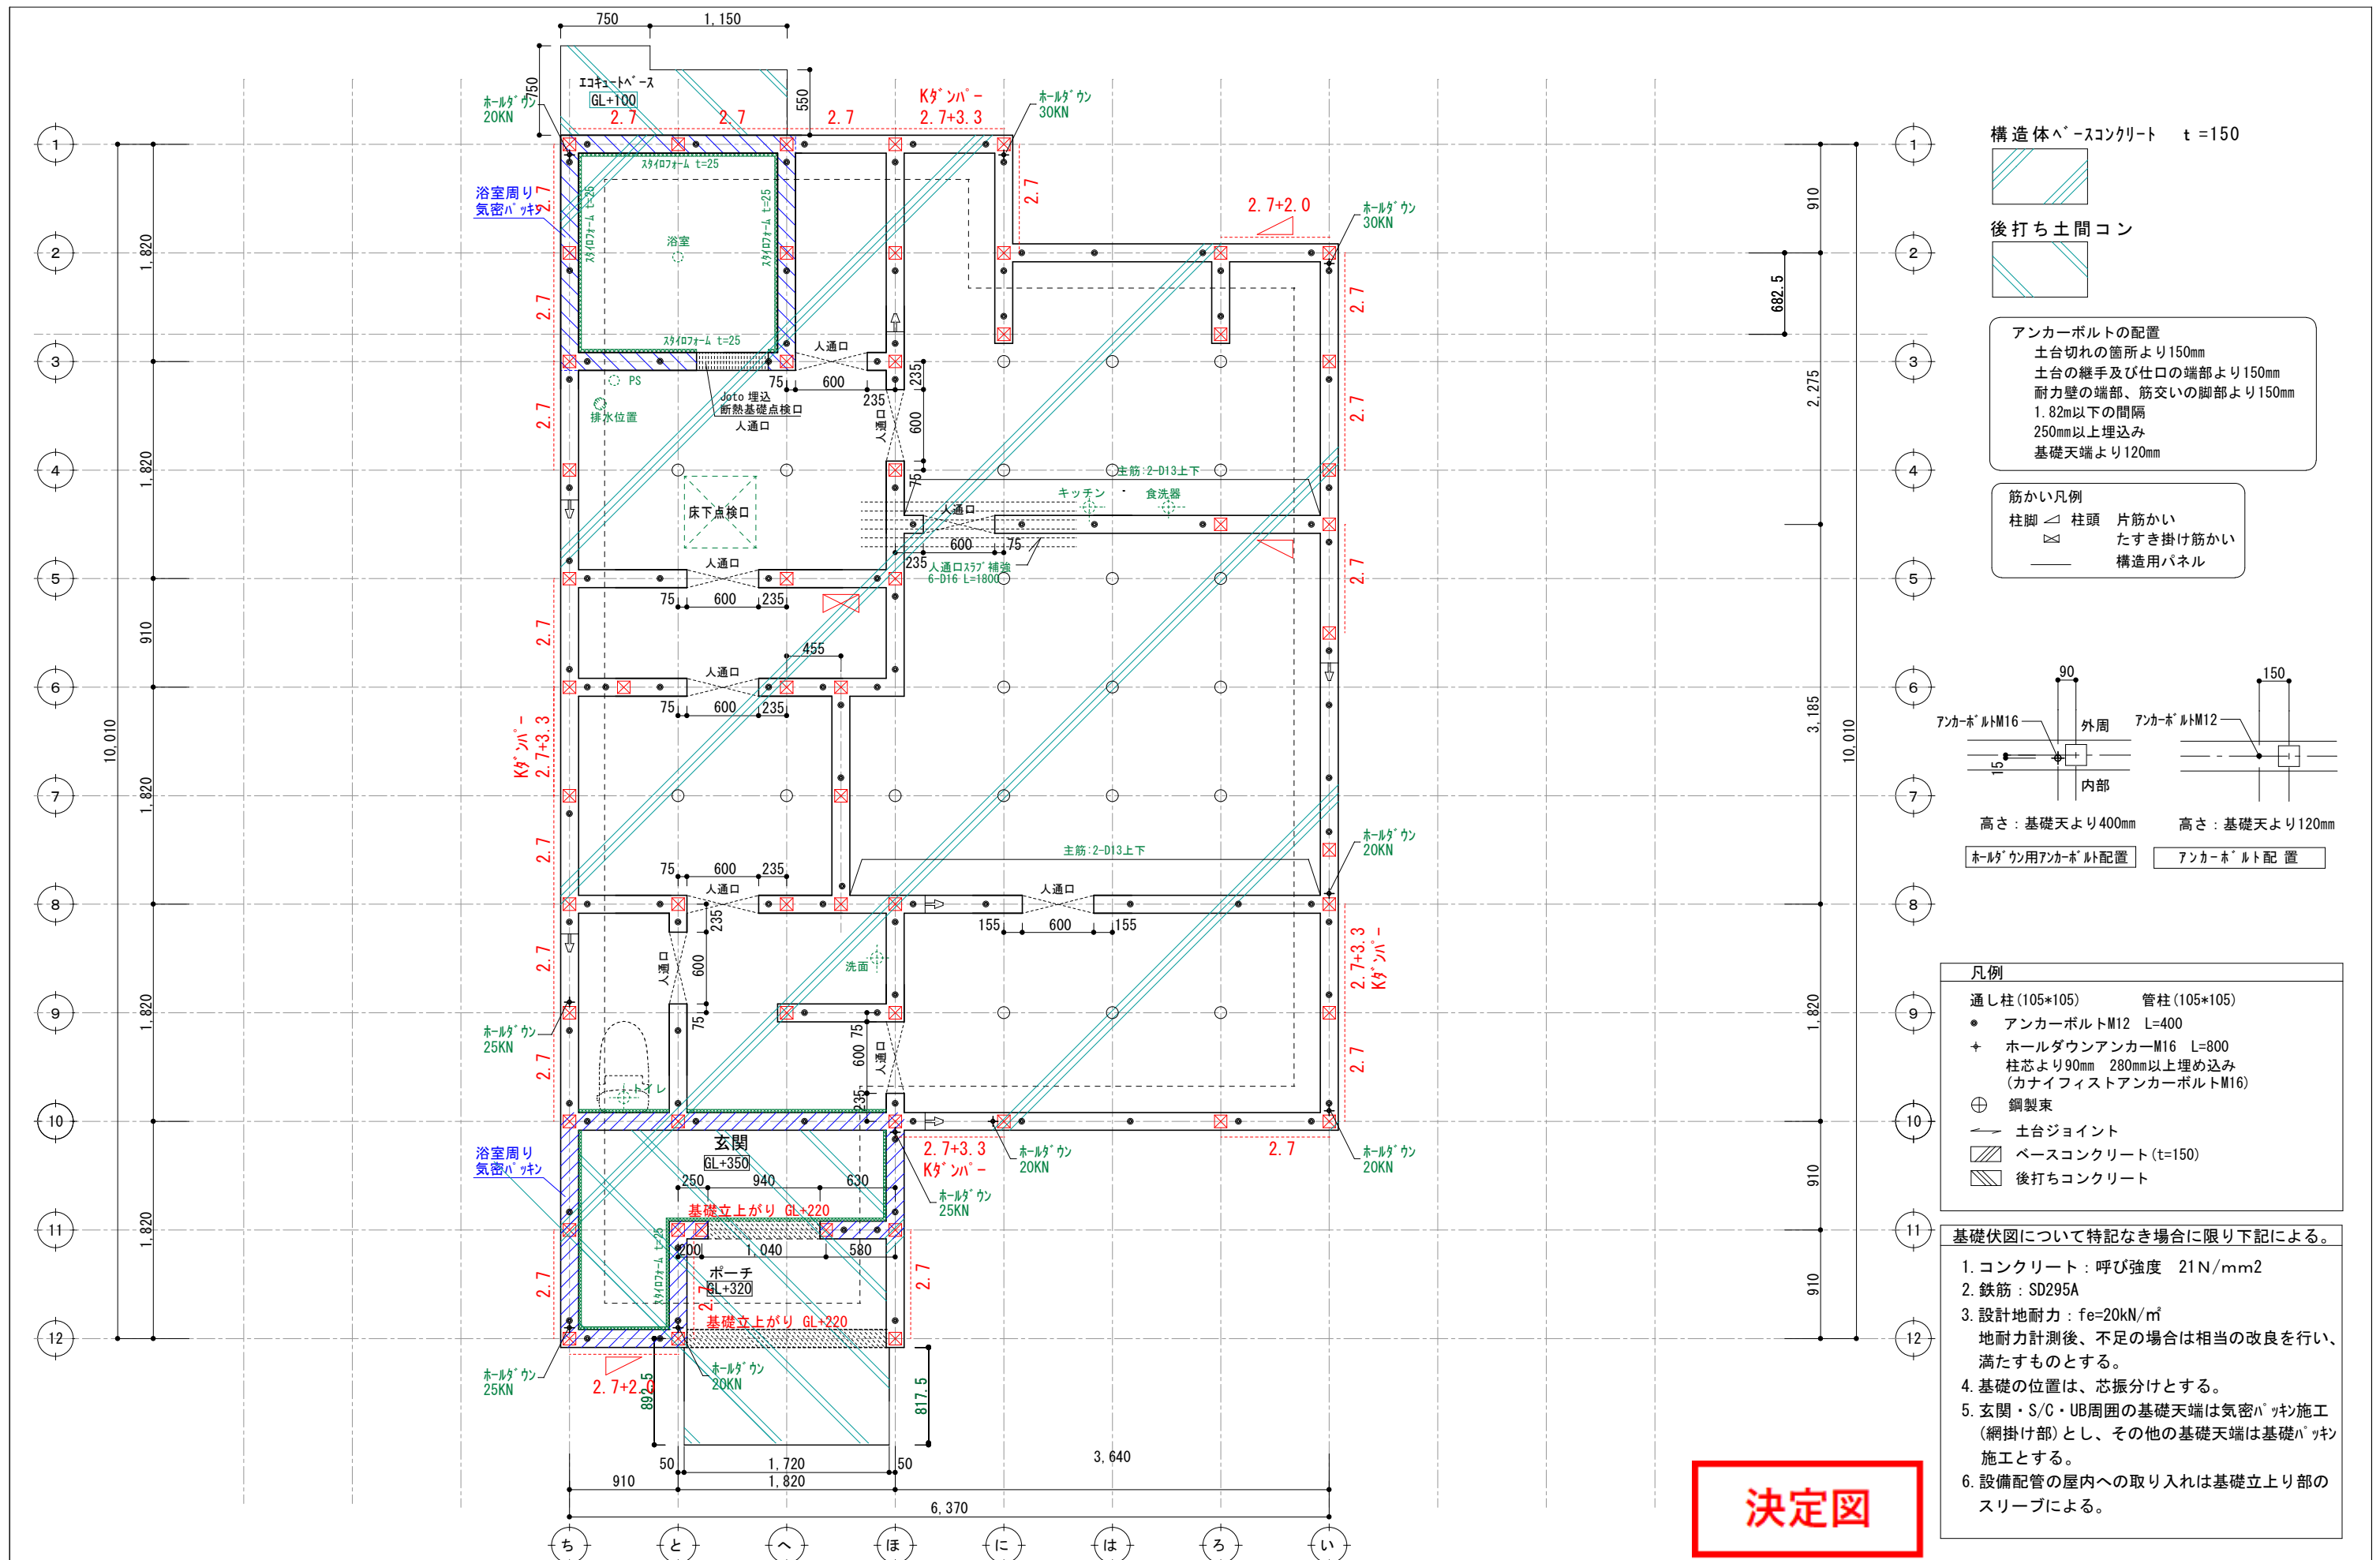


構造体ベースコンクリート t=150

後打ち土間コン







アンカーボルトの配置
土台切れの箇所より150mm
土台の継手及び仕口の端部より150mm
耐力壁の端部、筋交いの脚部より150mm
1.82m以下の間隔
250mm以上埋込み
基礎天端より120mm

筋かい凡例
柱脚 柱頭 片筋かい
たすき掛け筋かい
構造用パネル

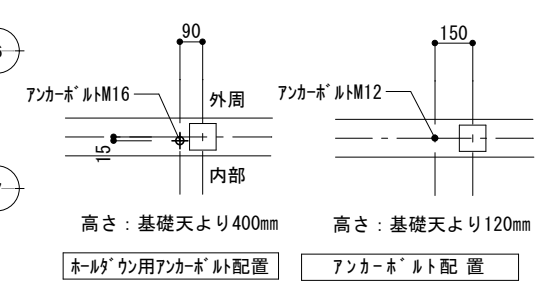

- 凡例
- 通し柱 (105*105) 管柱 (105*105)
 - アンカーボルトM12 L=400
 - + ホールダウンアンカーM16 L=800
柱芯より90mm 280mm以上埋め込み
(カナイフリストアンカーボルトM16)
 - ⊕ 鋼製束
 - 土台ジョイント
 - ベースコンクリート (t=150)
 - 後打ちコンクリート

- 基礎伏図について特記なき場合に限り下記による。
1. コンクリート：呼び強度 21N/mm²
 2. 鉄筋：SD295A
 3. 設計地耐力：fe=20kN/m²
地耐力計測後、不足の場合は相当の改良を行い、満たすものとする。
 4. 基礎の位置は、芯振分けとする。
 5. 玄関・S/C・UB周囲の基礎天端は気密パッキン施工（網掛け部）とし、その他の基礎天端は基礎パッキン施工とする。
 6. 設備配管の屋内への取り入れは基礎立上り部のスリーブによる。

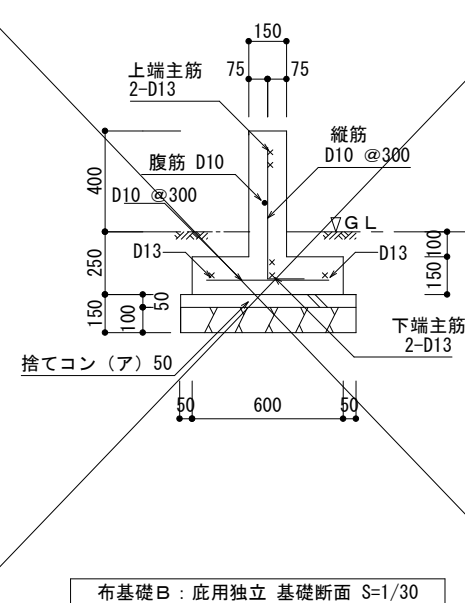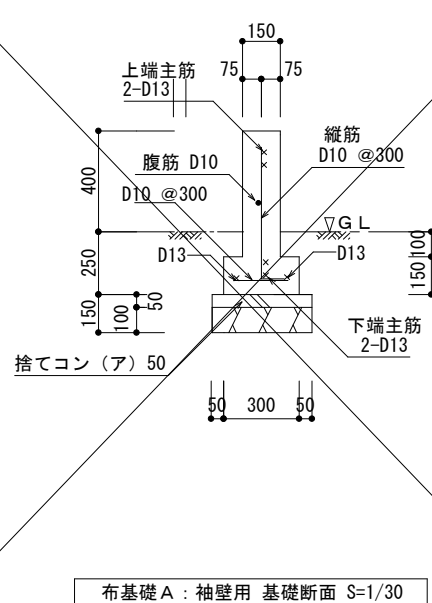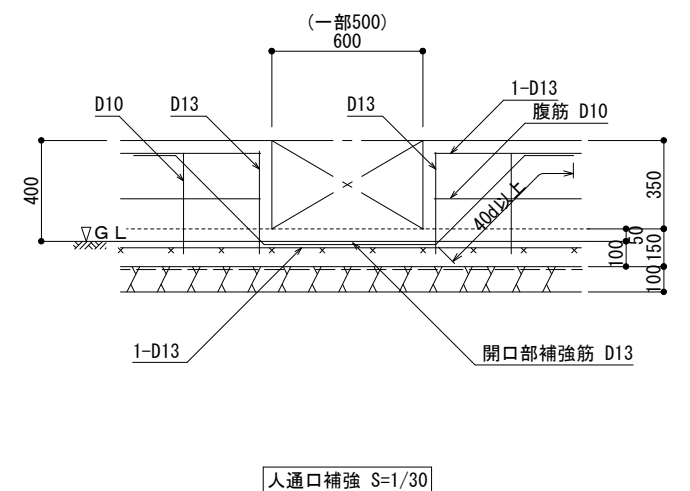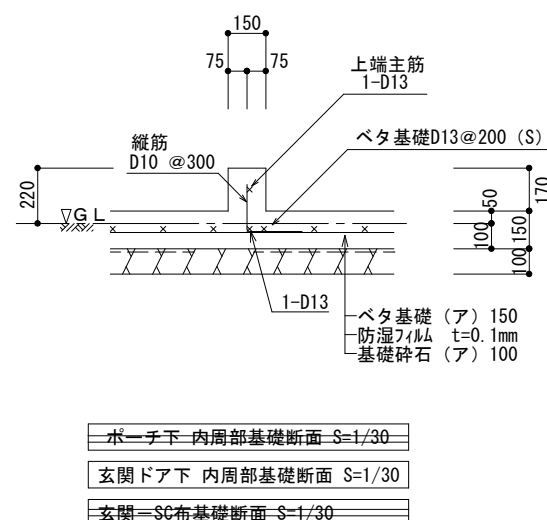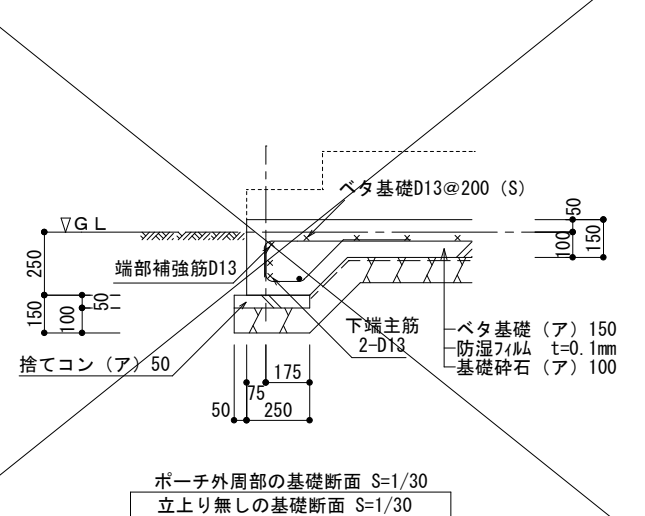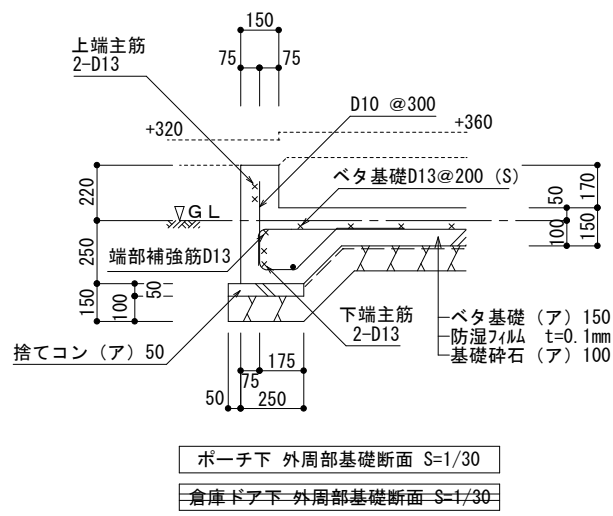


基礎の寸法 及び 配筋の検定方法	基礎立上り配筋は、 (財)日本住宅・木材技術 センター発行のスパン表 (増補版)による。 ベタ基礎スラブ配筋は、 まもりすまい保険設計施工 基準同解説のベタ基礎配筋表 による。具体的な寸法・配 筋は基礎詳細図参照。
---------------------------------------	--


- ・ D10を示す。
- × ・ D13を示す。

※使用しない断面は

決定図

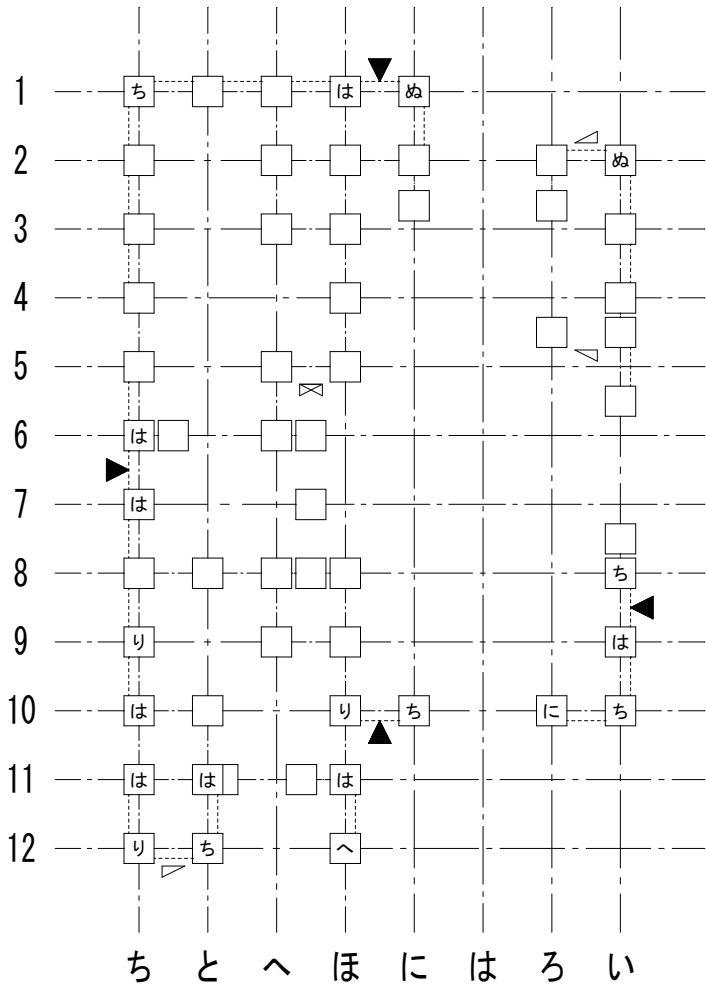

1階柱壁伏図

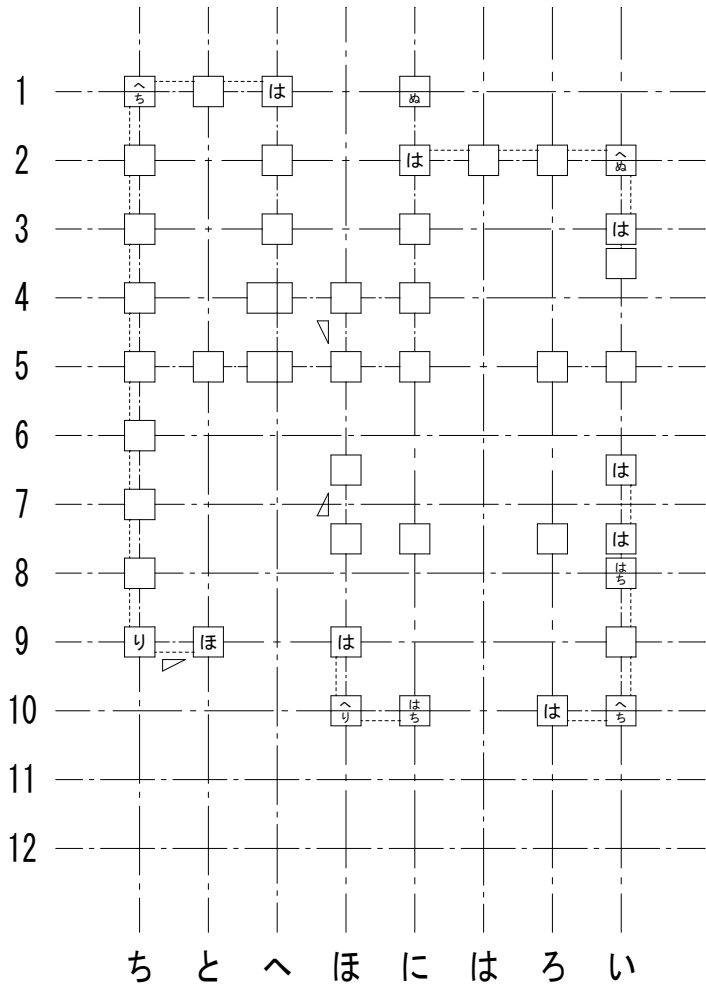

2階柱壁伏図

接合部凡例

*接合部凡例はユーザ設定されたものです。

記号	仕様（カナイ金物）	N	倍率
SBCP	スリムビルドコーナー75, チビクリCK (化粧柱の場合)	0.00	1.00
SBCP	スリムビルドコーナー75, チビクリCK (化粧柱の場合)	0.65	1.00
SBCP	は スリムビルドコーナー75	1.00	1.00
ARCG	に アレントコーナー合板用	1.40	2.20
ARCG	ほ アレントコーナー合板用	1.60	2.20
ARCG	へ アレントコーナー合板用	1.80	2.20
HD15	と ブレイブホールダウン B-HD15	2.80	3.60
HD20	ち ブレイブホールダウン B-HD20	3.70	4.70
HD25	り ブレイブホールダウン B-HD25	4.70	4.80
HD30	ぬ ブレイブホールダウン B-HD30	5.60	7.20
J1	る 腰掛け蟻若しくは大入れ蟻掛け+羽子板 [※] ルト, 短冊金物		1.90
J2	を 腰掛け蟻若しくは大入れ蟻掛け+羽子板 [※] ルト, 短冊金物×2		3.00

※表示なき金物は「は」とする。

梁継手・仕口用
梁継手・仕口用

接合部凡例

*接合部凡例はユーザ設定されたものです。

記号	仕様（タナカ金物）	N	倍率
FCP	フックコーナー, チビクリCK (化粧柱の場合)	0.00	1.00
FCP	フックコーナー, チビクリCK (化粧柱の場合)	0.65	1.00
FCP	は フックコーナー	1.00	1.00
CCP	に シナコーナー	1.40	2.20
CCP	ほ シナコーナー	1.60	2.20
CCP	へ シナコーナー	1.80	2.20
HD15	と ビス止めホールダウンU HD15	2.80	3.60
HD20	ち ビス止めホールダウンU HD20	3.70	4.70
HD25	り ビス止めホールダウンU HD25	4.70	4.80
HD30	ぬ ビス止めホールダウンU HD15×2 (HD35)	5.60	7.20
J1	る 腰掛け蟻若しくは大入れ蟻掛け+羽子板 [※] ルト, 短冊金物		1.90
J2	を 腰掛け蟻若しくは大入れ蟻掛け+羽子板 [※] ルト, 短冊金物×2		3.00

※表示なき金物は「は」とする。

梁継手・仕口用
梁継手・仕口用

筋かいの種類に応じた筋かいの端部の接合部の仕様		
	筋かいの種類	接合部の仕様（構造方法）
イ	鉄筋φ9	柱又は横架材を貫通し、三角座金を介してナット締め、又は鋼板添え板を用い鋼板を柱及び横架材にCN90, 8本平打ち
ロ	筋かい:15×90	柱・横架材を欠き込み、柱・横架材双方に対してN65, 5本平打ち
ハ	筋かい:30×90	鋼板添え板t=1.6mmを筋かいに対してボルトφ12及びCN65, 3本平打ち、柱に対してCN65, 3本平打ち、横架材に対してCN65, 4本平打ち。筋かいプレートBP同等品
ニ	筋かい:45×90	鋼板添え板t=2.3mmを筋かいに対してボルトφ12及びスクリュー釘φ4.5L50, 7本平打ち、柱及び横架材に対してスクリュー釘φ4.5L50, 5本平打ち。筋かいプレートBP-2同等品
ホ	筋かい:90×90	柱又は横架材にボルトφ12mmを用いて一面剪断接合

胴差と通し柱の接合部の仕様		
	胴差と通し柱の条件	仕口
T1	通し柱の片側に胴差が来る場合	胴差を柱にかたぎ大入れ短ほぞ差しの上、羽子板ボルト、かね折り金物又は同等以上の仕口
T2	通し柱の両側に胴差が来る場合	胴差を柱にかたぎ大入れ短ほぞ差しの上、短冊金物又は、同等以上の仕口で胴差相互を緊結
T3	通し柱と胴差の接合部の近くに90×90以上の筋かいが来る場合（通し柱が建物の出隅にあるか、筋かい壁が外壁と直交して接する場合）	胴差を通し柱に、15KN用引き寄せ金物を水平に用いて緊結

決定図

37セントクロス指示書

G1

壁付け 住宅用火災報知器			数量
H	熱感知器	電池式(単独型)	1
	露出型		
壁付け 住宅用火災報知器			数量
S	煙感知器	電池式(単独型)	
	露出型		


- ※ 煙感知器は壁・梁より600mm以上離す壁に取付ける場合、天井から150mm以上500mm以内離す換気扇・エアコン吹出口から1500mm以上離す
- ※ 全室LED照明とする。
- ※ 標準天井高さ2,400
- ※ 特記無きガラスは型ガラス

* 凡例

- ☒ 管柱 (105×105)
- ◀▶ K'ンパ (3.30倍 FRM-0641)
- △ 片筋違い (2.00倍 45×90)
(例 左:柱脚 右:柱頭)
- ⊠ たすき掛筋違い (4.00倍 45×90)
- 構造用合板 (2.70倍)
(t=9 タイガ EXN(ハ))
- ◀ 床点検口
- ⊠ 天井点検口
- ⊕ 換気扇
- ⊕ 熱交換換気扇VLR-70

アドバンスシリーズ	
スマートデザイン (外部)	
凡例	
①	コンセント 1ヶ口
②	コンセント 2ヶ口
③	コンセント 3ヶ口
①ET	コンセント1ヶ口接地ターミナル付
②ET	コンセント2ヶ口接地ターミナル付
WP	コンセント 防水型
WP	エアコン用コンセント
WP	200V用コンセント
WP	防雨入線プレート
●	スイッチ
●3	3路スイッチ
●4	4路スイッチ
⊠	直結電線
⊠TV	テレビ取出口
⊠TEL	電話取出口 (テレホンガイド)
⊠LAN	LAN取出口 (テレホンガイド)
⊠	壁掛型
⊠	リモコン (給湯関係・ルフロ)
⊠	メーカー
⊠	分電盤
⊠	チャイム

- ※ACコンセント天井付け
- ※TVアンテナ工事
- ※スイッチはFL+1100、コンセントはFL+200

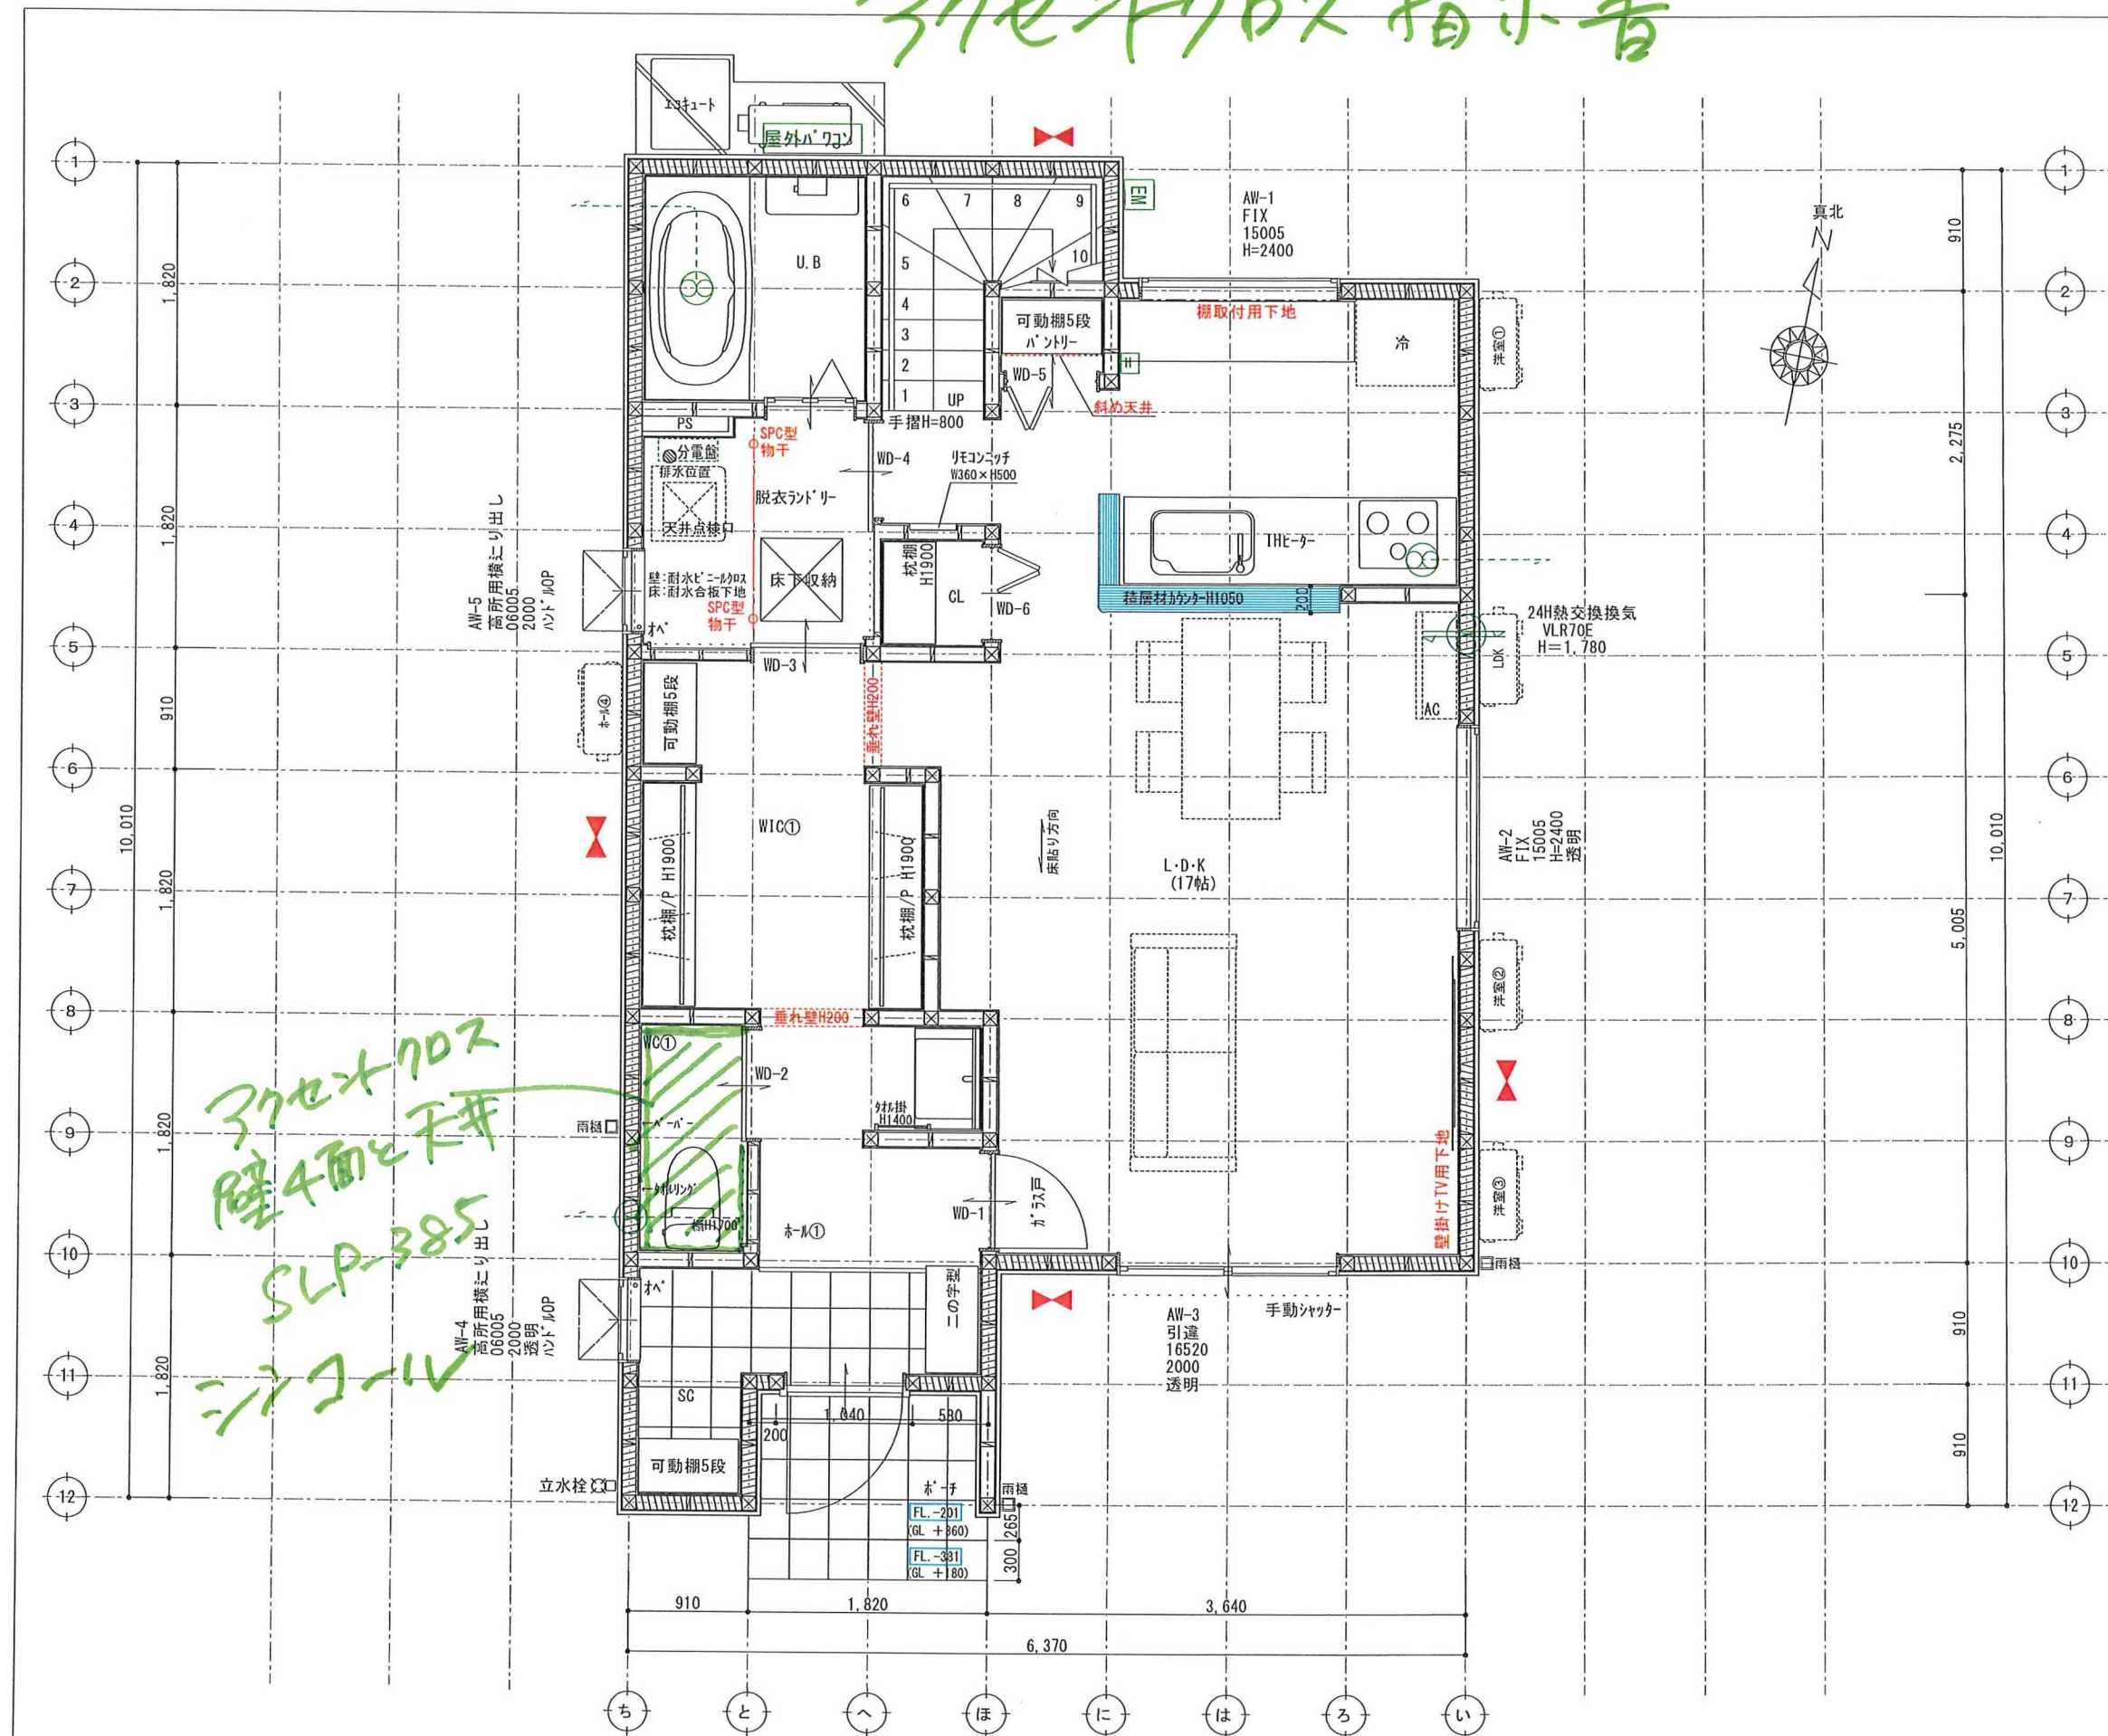

37セントクロス
壁4面と天井
SLP-385
シンコー

G1

壁付け 住宅用火災報知器			数量
H 熱感知	熱感知器	電池式(単独型)	
		露出型	
壁付け 住宅用火災報知器			数量
S 煙感知	煙感知器	電池式(単独型)	4
		露出型	

※ 煙感知器は壁・梁より600mm以上離す
壁に取付ける場合、
天井から150mm以上500mm以内離す
換気扇・エアコン吹出口から1500mm以上離す
※ 全室LED照明とする。
※ 標準天井高さ2,400
※ 特記無きガラスは型ガラス

* 凡例

- ☒ 管柱 (105×105)
- ≡ K' 'n' - (3.30倍 FRM-0641)
- △ 片筋違い (2.00倍 45×90)
(例 左:柱脚 右:柱頭)
- ⊗ たすき掛筋違い (4.00倍 45×90)
- - - 構造用合板 (2.70倍)
(t=9 タイガ EXハイパー)
- △ 床点検口
- ⊗ 天井点検口
- ⊗ 換気扇
- ⊗ 熱交換換気扇VLR-70

アドバンスシリーズ	
スマートデザイン (外装)	
凡例	
①	コンセント 1ヶ口
②	コンセント 2ヶ口
③	コンセント 3ヶ口
①ET	コンセント1ヶ口接地ターミナル付
②ET	コンセント2ヶ口接地ターミナル付
WP	コンセント 防水型
⊗	エアコン用コンセント
⊗	200V用コンセント
WP	防雨入換プレート
●	スイッチ
● 3	3路スイッチ
● 4	4路スイッチ
⊗	直結電源
TV	テレビ取出口
TEL	電話取出口 (テレホンガイド)
LIN	LIN取出口 (テレホンガイド)
⊗	壁照明
⊗	リモコン (松浦園氏・ルフロ)
⊗	メーター
⊗	分電盤
⊗	チャイム

※ACコンセント天井付け
※TVアンテナ工事
※スイッチはFL+1100、コンセントはFL+200

